




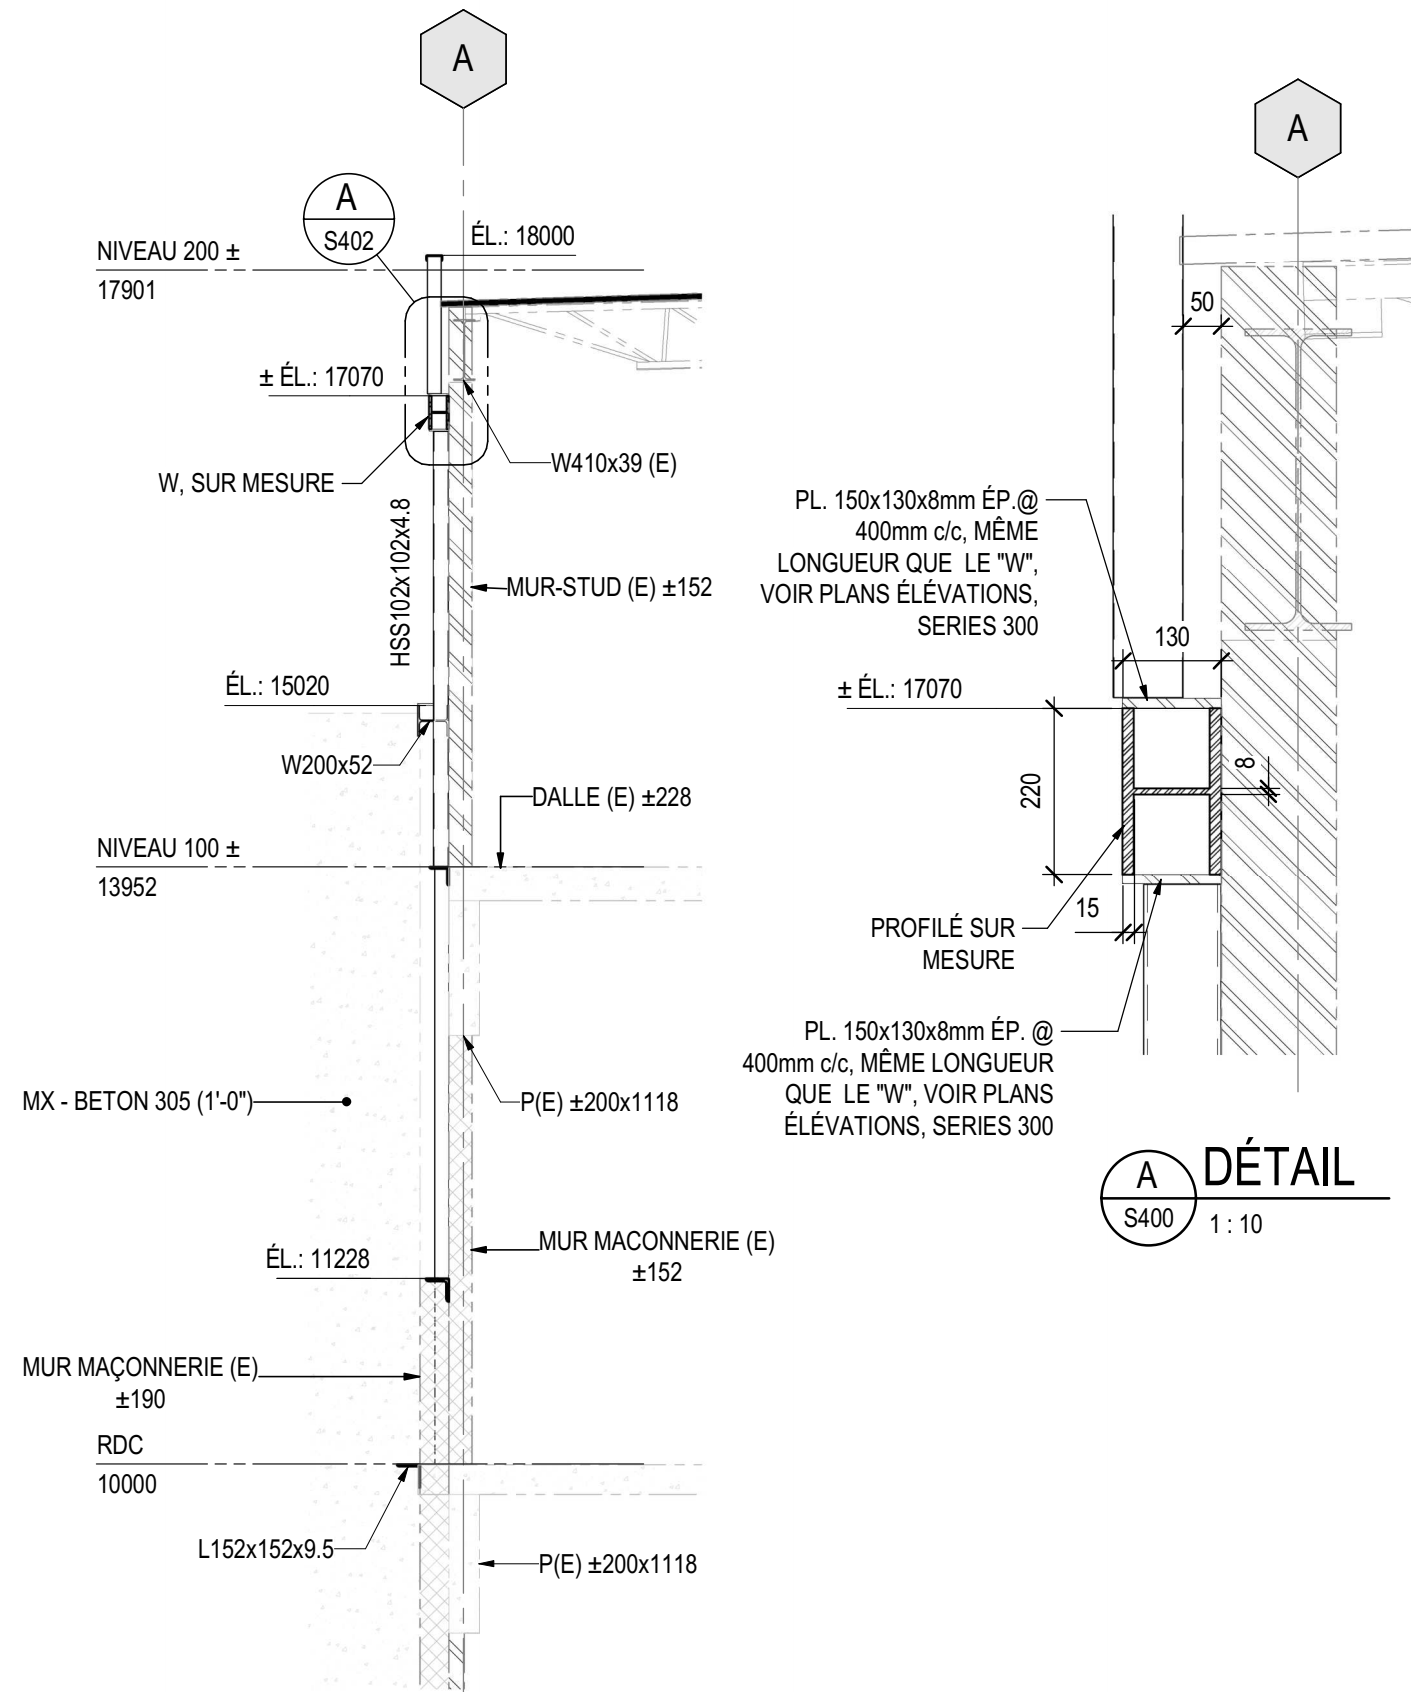


26 COUPE
S201 1 : 50

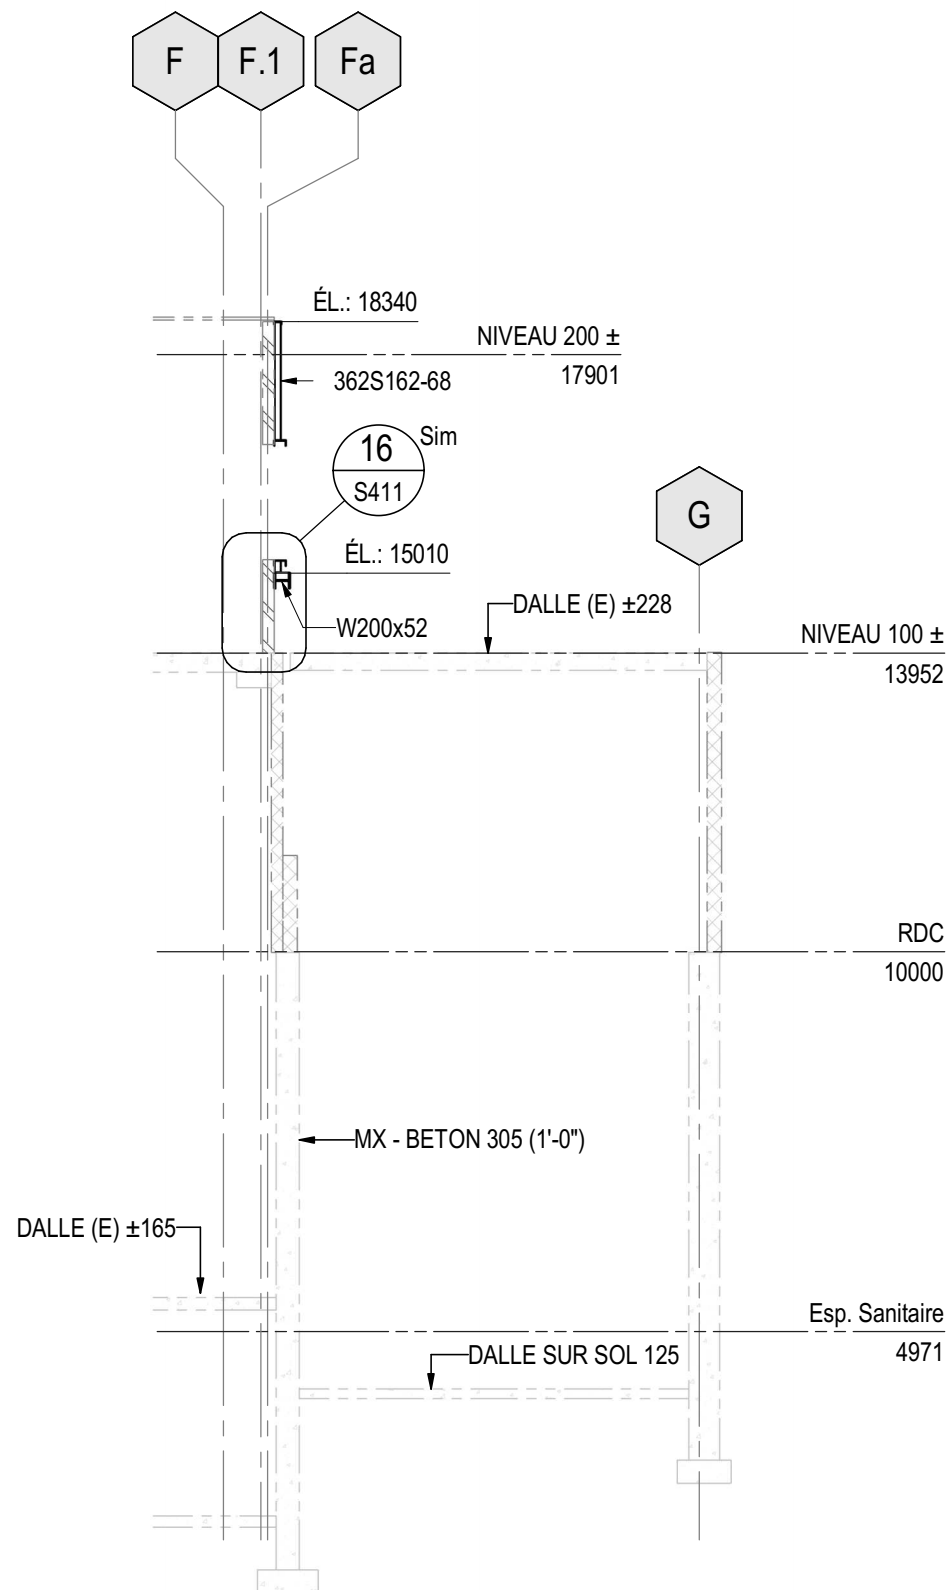


34 COUPE SAUT-DE-LOUP
S201 1 : 100

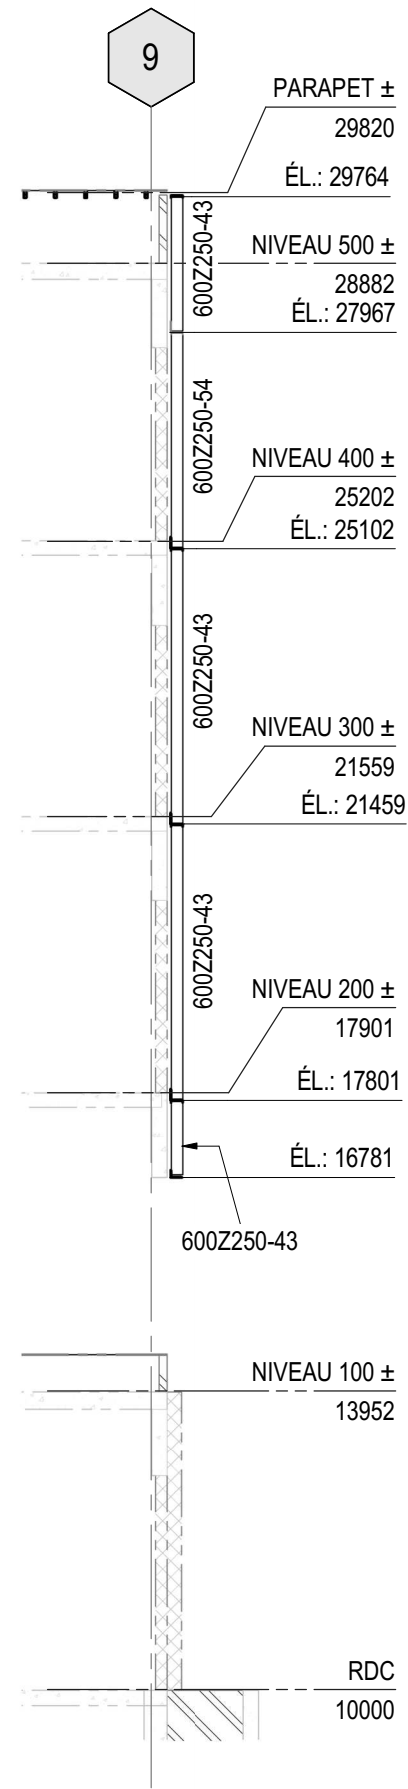


27 COUPE
S201 1 : 100

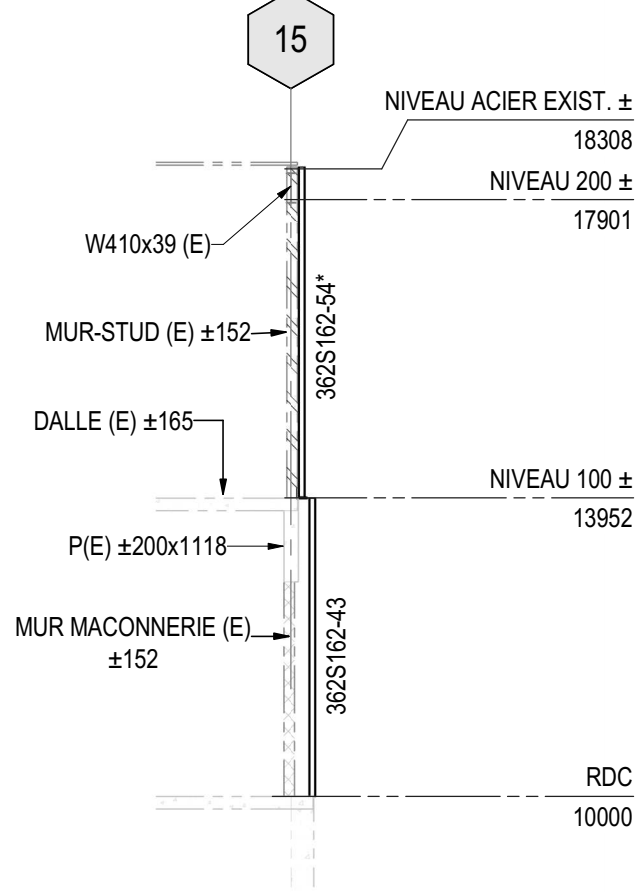


28 COUPE
S302 1 : 100

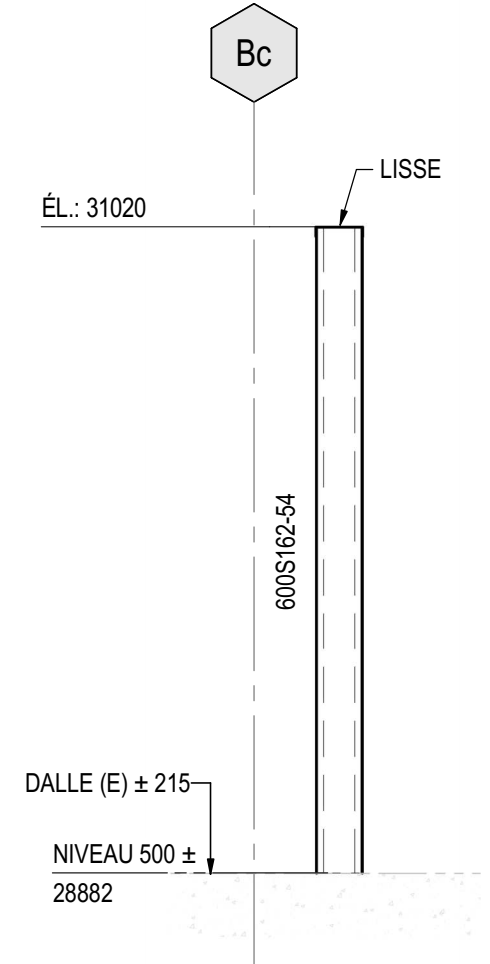


30 COUPE
S303 1 : 25

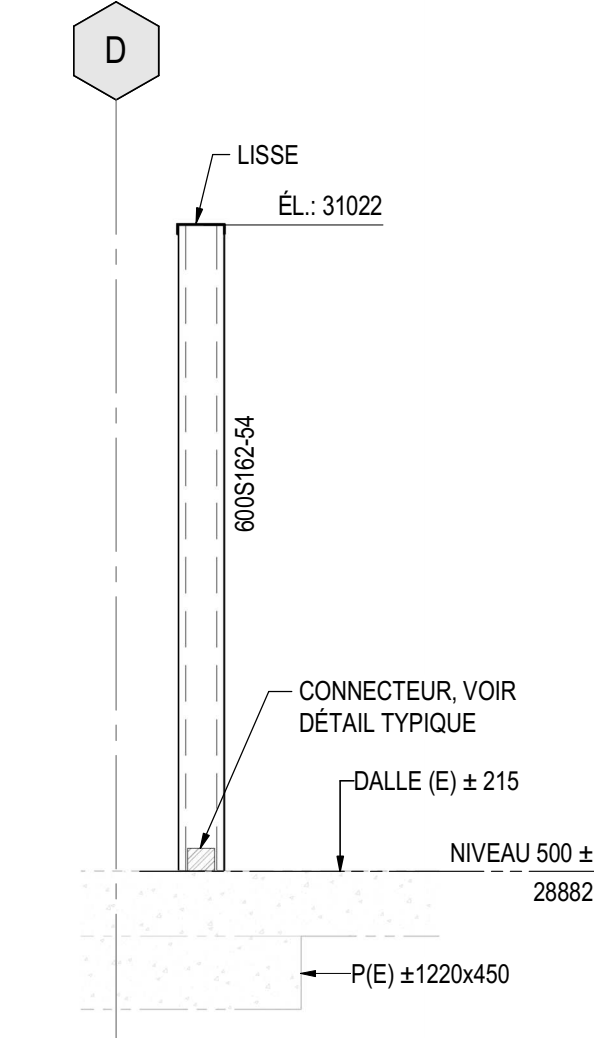

31 COUPE
S300 1 : 25

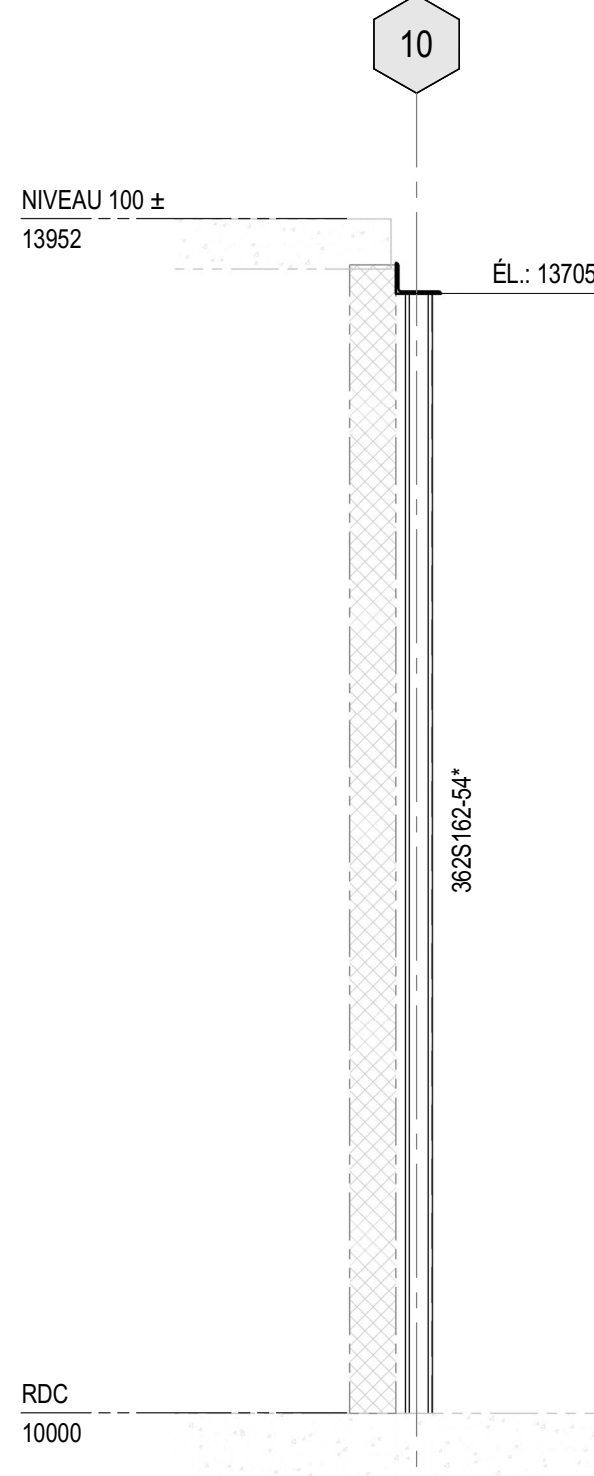

32 COUPE
S201 1 : 25

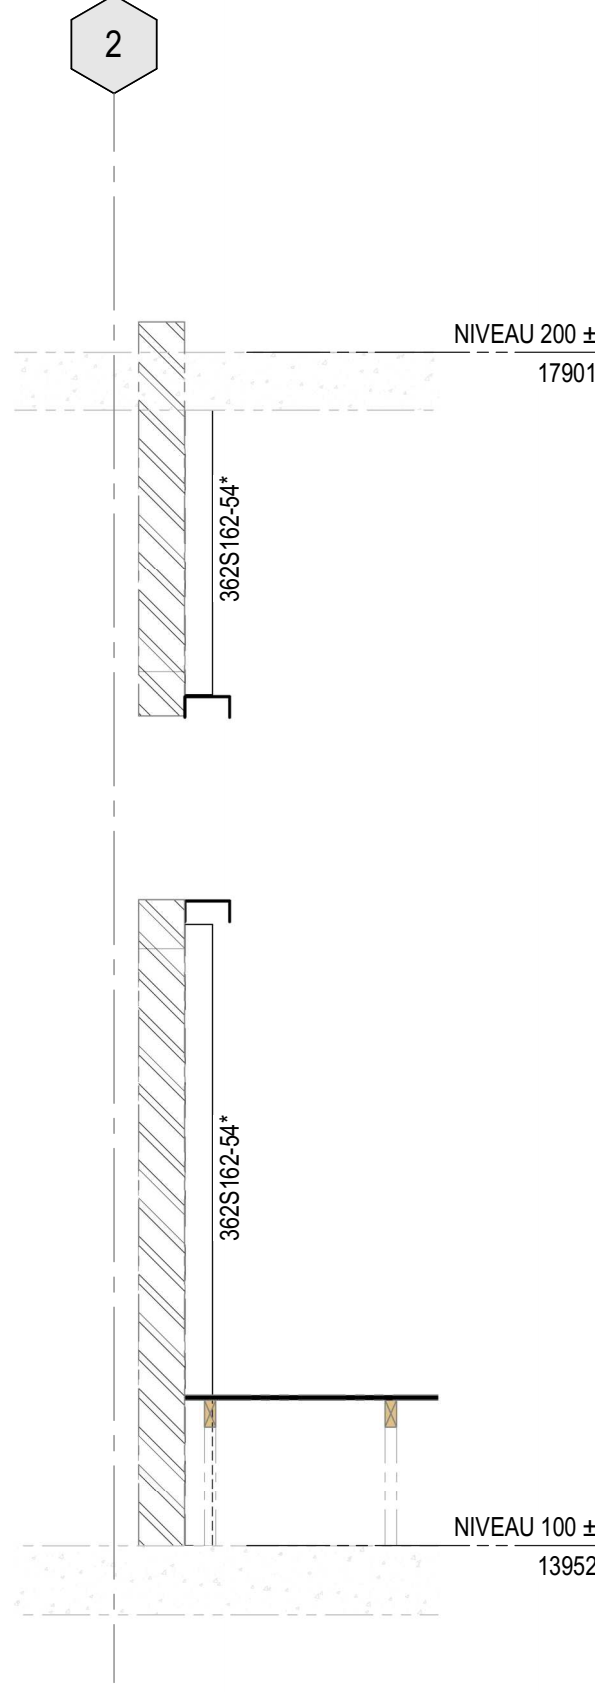

33 COUPE
S202 1 : 25

CE DOCUMENT NE DOIT PAS ÊTRE UTILISÉ
À DES FINS DE CONSTRUCTION

ARCHITECTURE:



MÉCANIQUE:



RÉVISIONS:

REV	DATE	DESCRIPTION	PAR
0	2026-09-04	DÉFINITIFS POUR SOUMISSION	JLB

SCEAU:



AVERTISSEMENT: CE DRESSIN EST LA PROPRIÉTÉ INTELLECTUELLE DE WSP CANADA INC. AUCUNE RÉVISION, REPRODUCTION OU TOUT AUTRE USAGE N'EST PERMIS SANS L'AUTORISATION ÉCRITE DE WSP CANADA INC. L'ENTREPRENEUR DOIT VÉRIFIER TOUTES LES DIMENSIONS AUX PLANS ET FAIRE LOCALISER TOUTES LES SERVICES D'UTILITÉS PUBLIQUES ET RAPPORTER TOUTES ERREURS OU OMISSIONS AVANT DE COMMENCER LES TRAVAUX.

ÉCHELLE ORIGINALE: Comme indiqué	DATE: 2026-09-04
PRÉPARÉ PAR: Approuvateur Concepteur NATHAN SCHMITT, ing. PRT	SI CETTE BARRE NE MESURE PAS 25 mm, AJUSTER VOTRE ÉCHELLE DE TRAÇAGE.
VÉRIFIÉ PAR: Vérificateur	25mm
DESSINÉ PAR: Auteur	

DISCIPLINE: STRUCTURE



WSP Canada Inc.
1135 Boulevard Lebourgneuf
Ville de Québec, Québec, G2K 0M5
T +1 418-623-2254 | www.wsp.com

NO PROJET: CA0062562.5541

CLIENT:



RÉF. CLIENT: R874-24 / 24-108

PROJET:

HÔPITAL DE CHANDLER
(RÉFECTION DE L'ENVELOPPE)

TITRE:



COUPES DE MURS

NUMÉRO DU FEUILLET:

S402

REV:

0

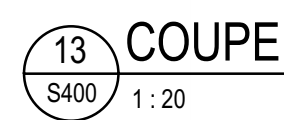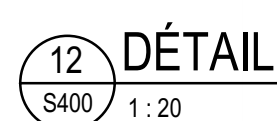

ARCHITECTURE:



MÉCANIQUE:



RÉVISIONS:

0	2026-09-04	DÉFINITIFS POUR SOUMISSION	JLB
REV	DATE	DESCRIPTION	PAR

SCEAU:



AVERTISSEMENT: CE DESSIN EST LA PROPRIÉTÉ INTELLECTUELLE DE WSP CANADA INC. AUCUNE RÉVISION, REPRODUCTION OU TOUT AUTRE USAGE N'EST PERMIS SANS L'AUTORISATION ÉCRITE DE WSP CANADA INC. L'ENTREPRENEUR DEVRA VÉRIFIER TOUTES LES DIMENSIONS AUX PLANS ET FAIRE LOCALISER TOUS LES SERVICES D'UTILITÉS PUBLIQUES ET RAPPORTER TOUTES ERREURS OU OMISSIONS AVANT DE COMMENCER LES TRAVAUX.

ÉCHELLE ORIGINALE:

1:2

PRÉPARÉ PAR:

JOANIE ROBILLARD, ing.
CHARLOTTE ALLARD, CPI
NATHAN SCHMITT, ing. PRT

VÉRIFIÉ PAR:
JEAN-LUC BOUFFARD, ing.

DESSINÉ PAR:
GLORIA GILDA SIMIREA, tech

SI CETTE BARRE NE
MESURE PAS 25 mm,
AJUSTER VOTRE ÉCHELLE
DE TRAÇAGE.



25mm

DISCIPLINE:

STRUCTURE



1135 Boulevard Lebourgneuf
Ville de Québec, Québec, G2K 0M5
+1 418-623-2254 | www.wsp.com

NO PROJET: CA0062562.5541

CLIENT:



RÉF. CLIENT: R674-24 / 24-108

PROJET:

HÔPITAL DE CHANDLER
(RÉFECTION DE L'ENVELOPPE)

TITRE:


COUPES ET DÉTAILS

NUMÉRO DU FEUILLET:


S410

REV.

0

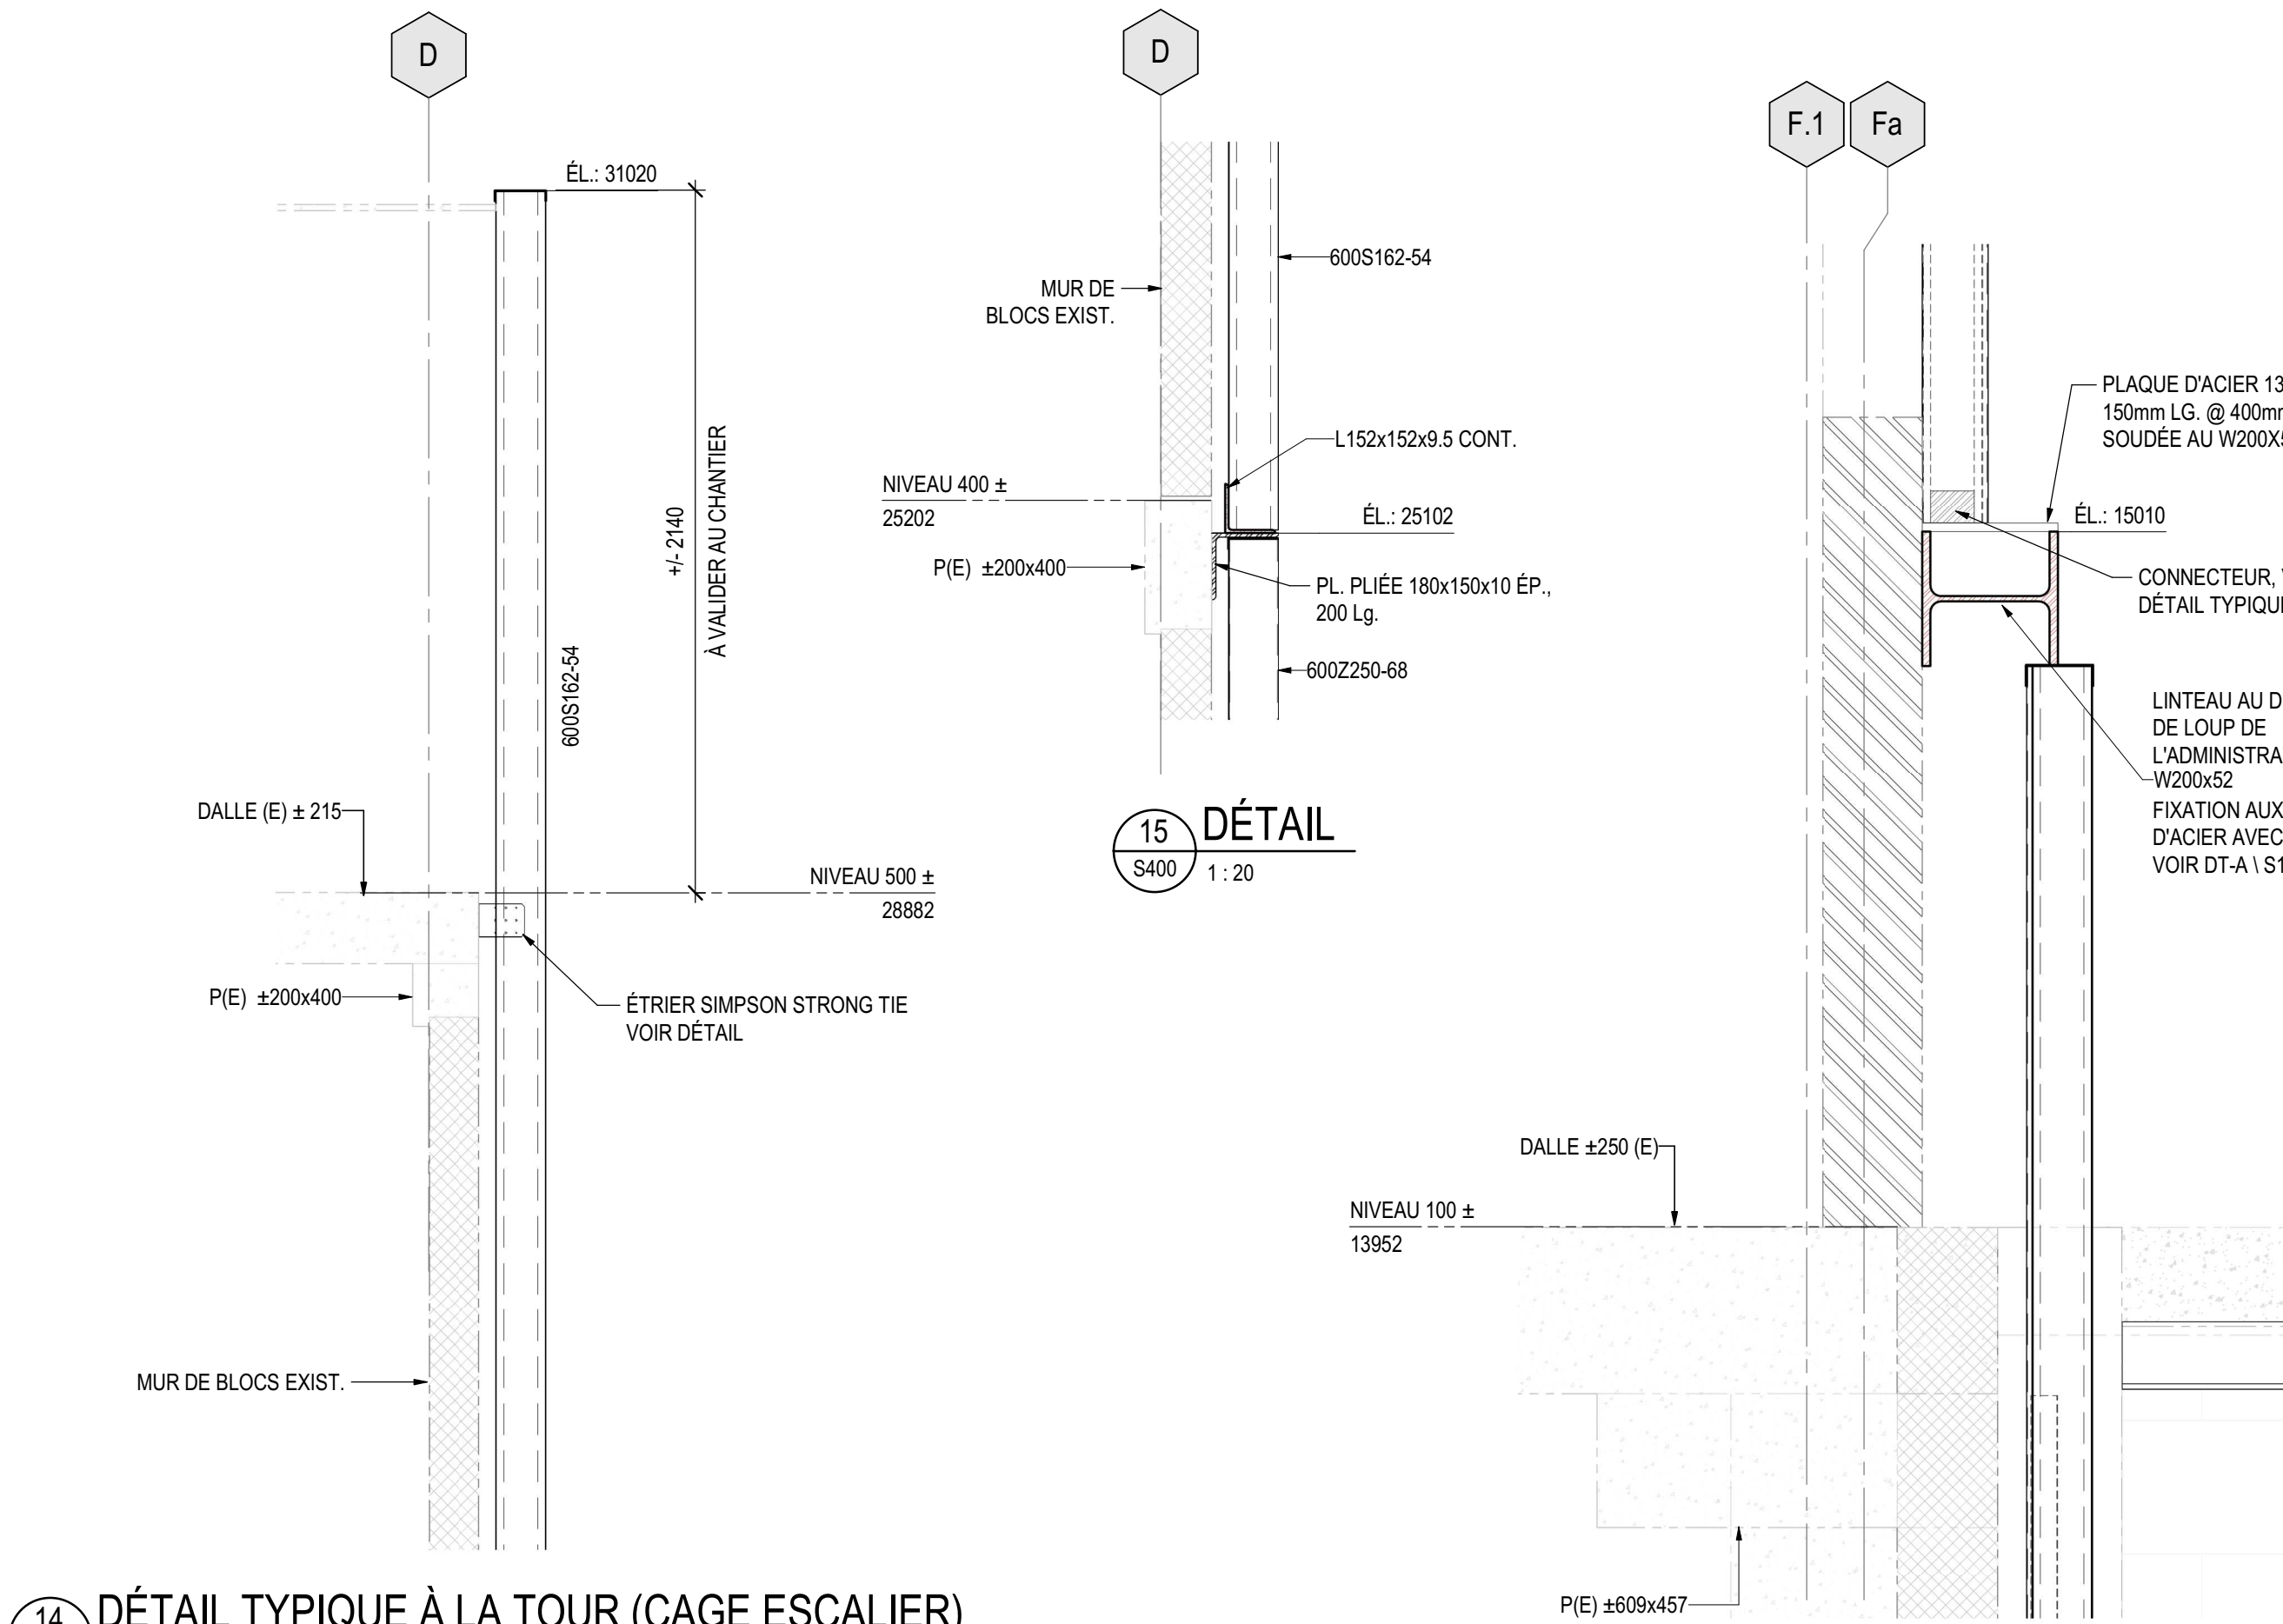


14 DÉTAIL TYPIQUE À LA TOUR (CAGE ESCALIER)
S400 1:20

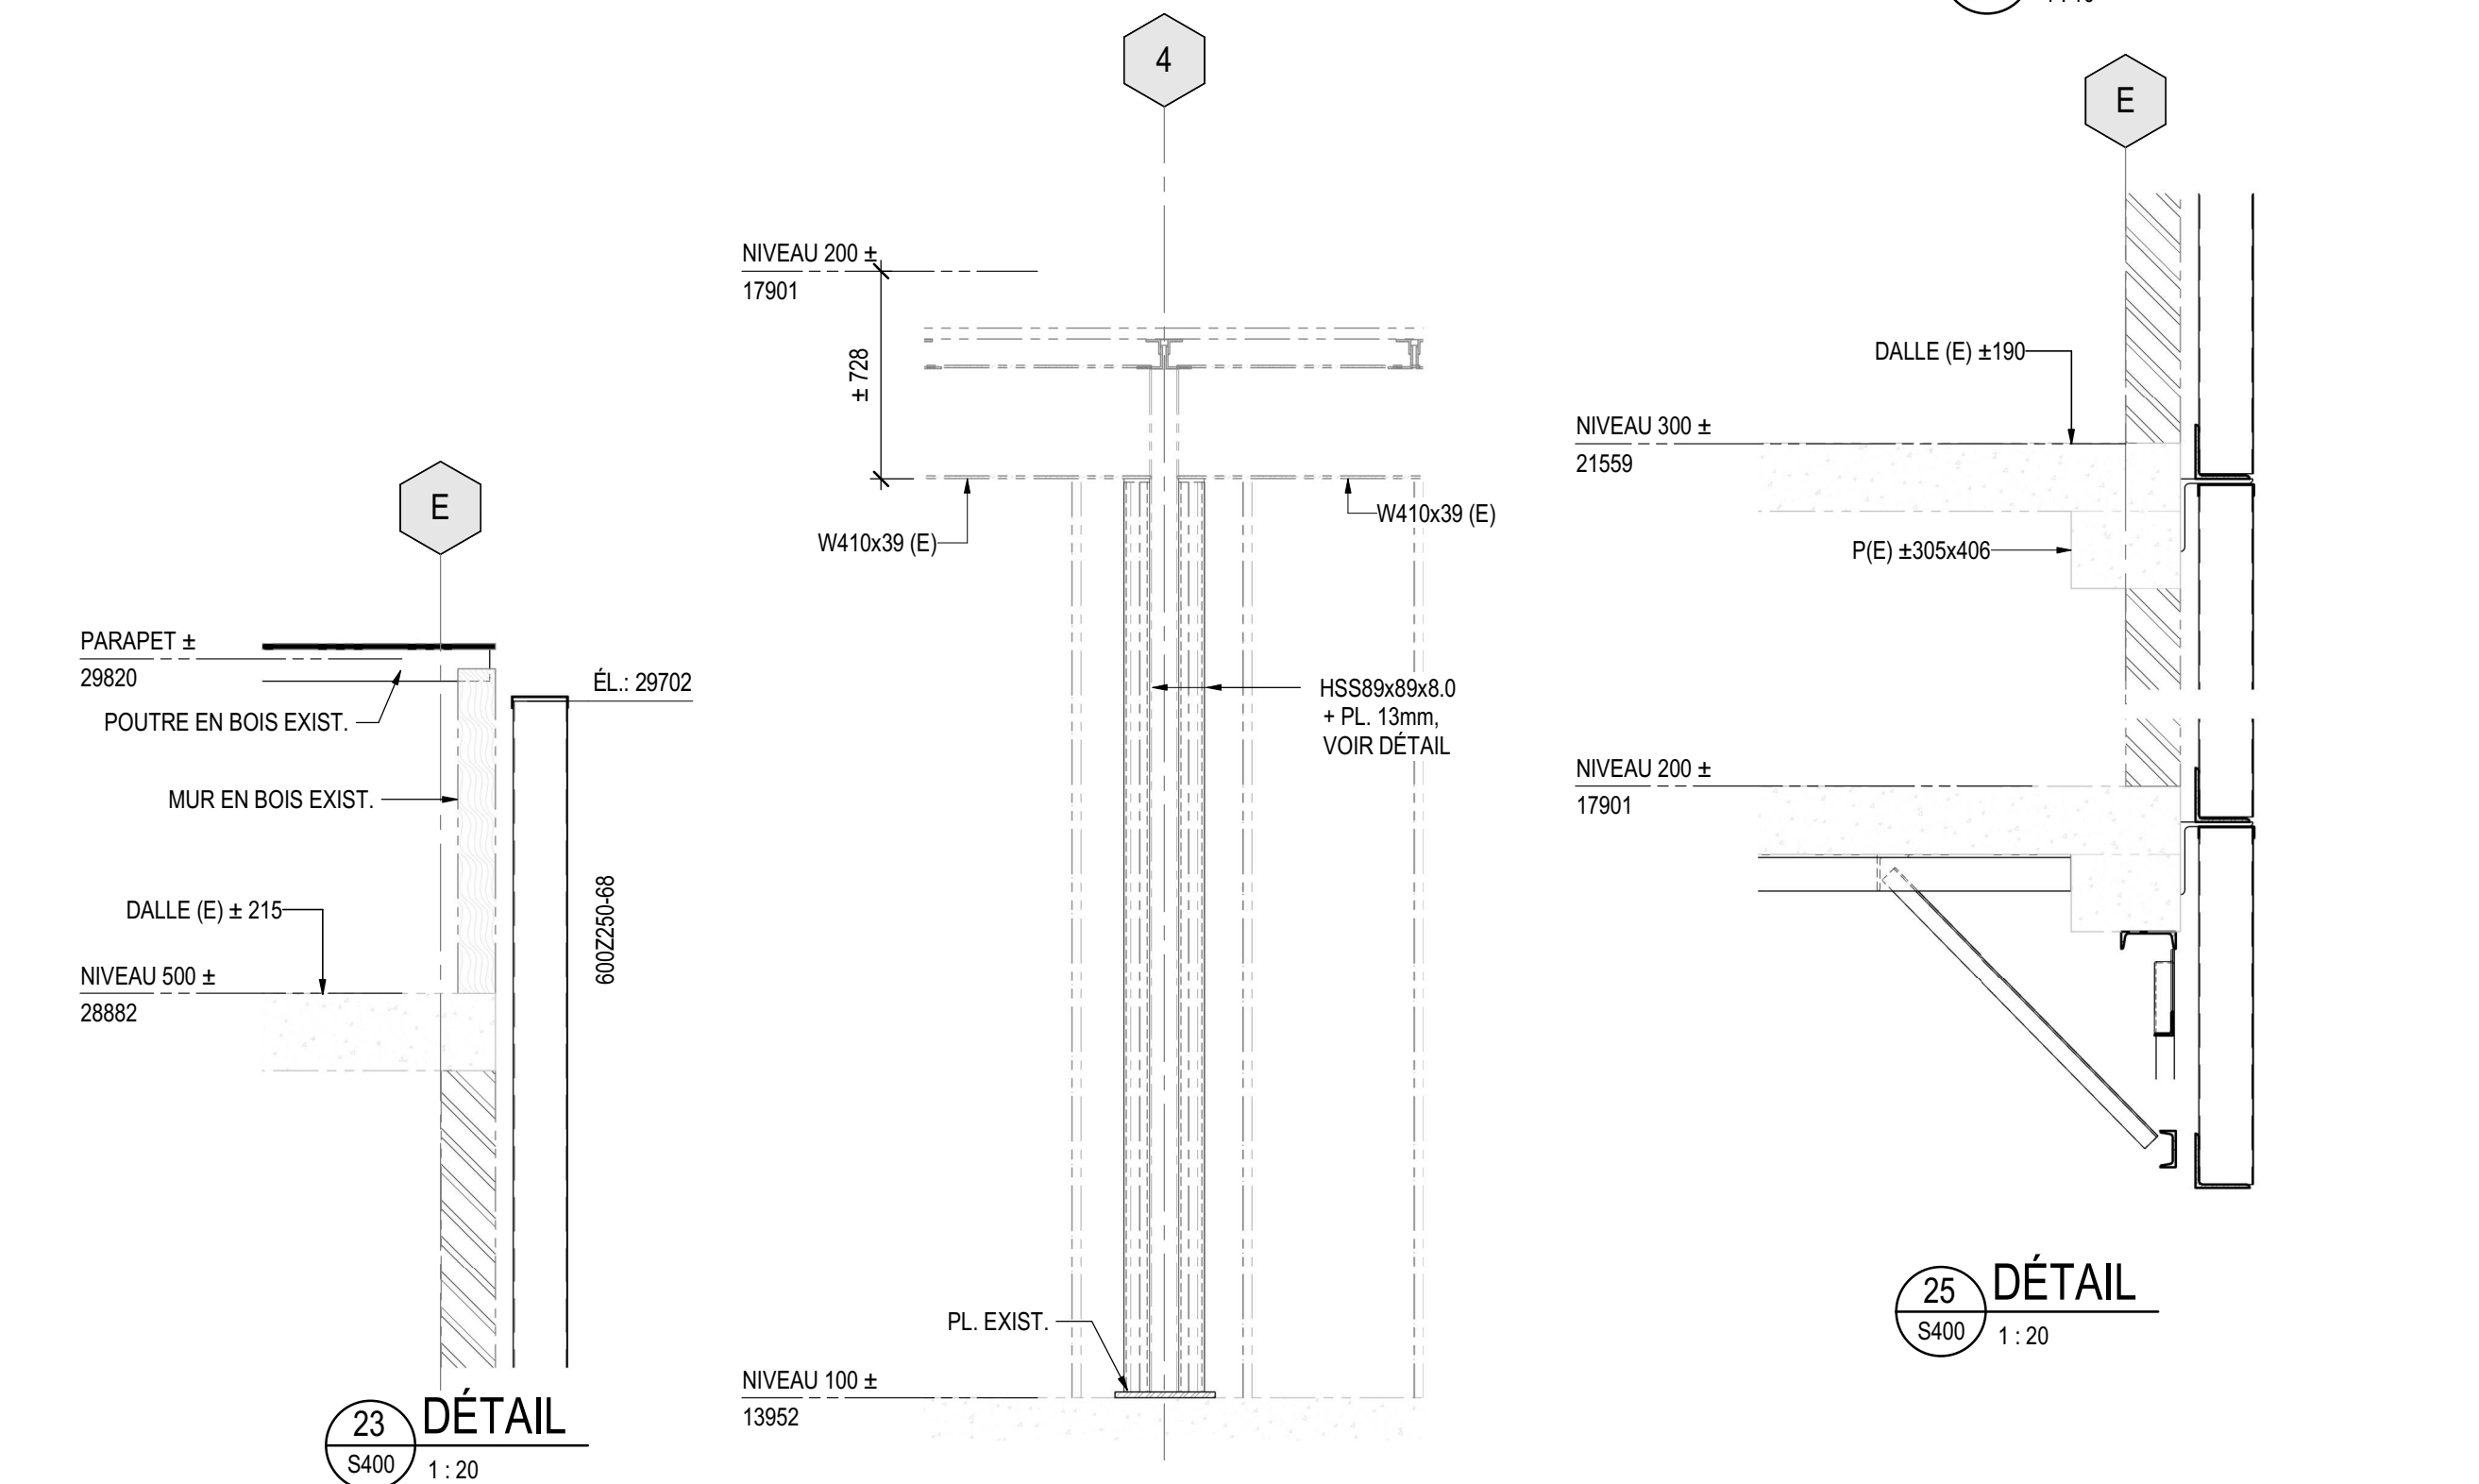


15 DÉTAIL
S400 1:20

23 DÉTAIL
S400 1:20


24 COUPE
S411 1:25

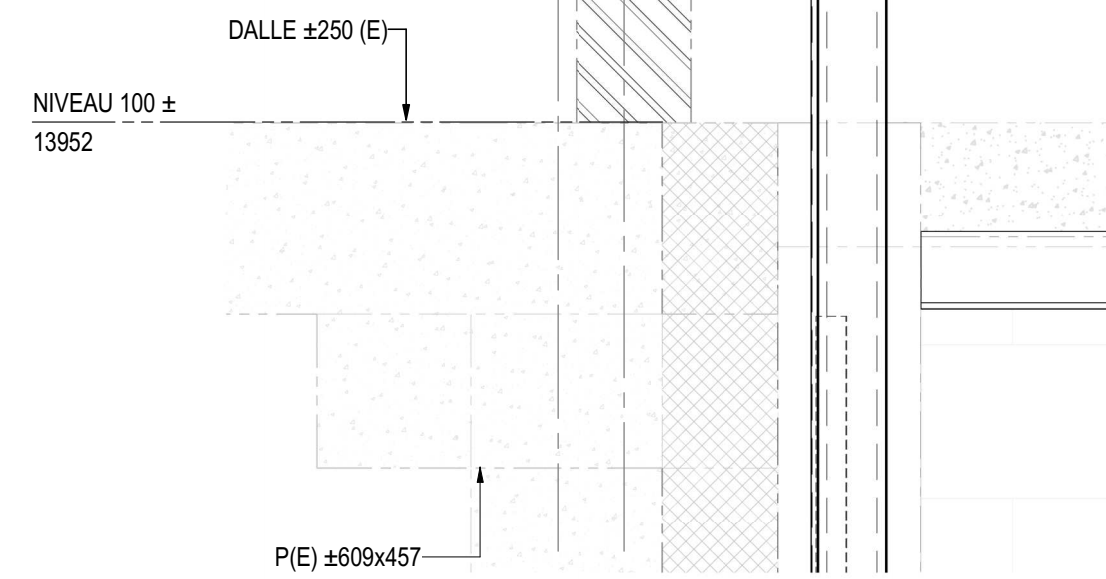


16 DÉTAIL
S401 1:10

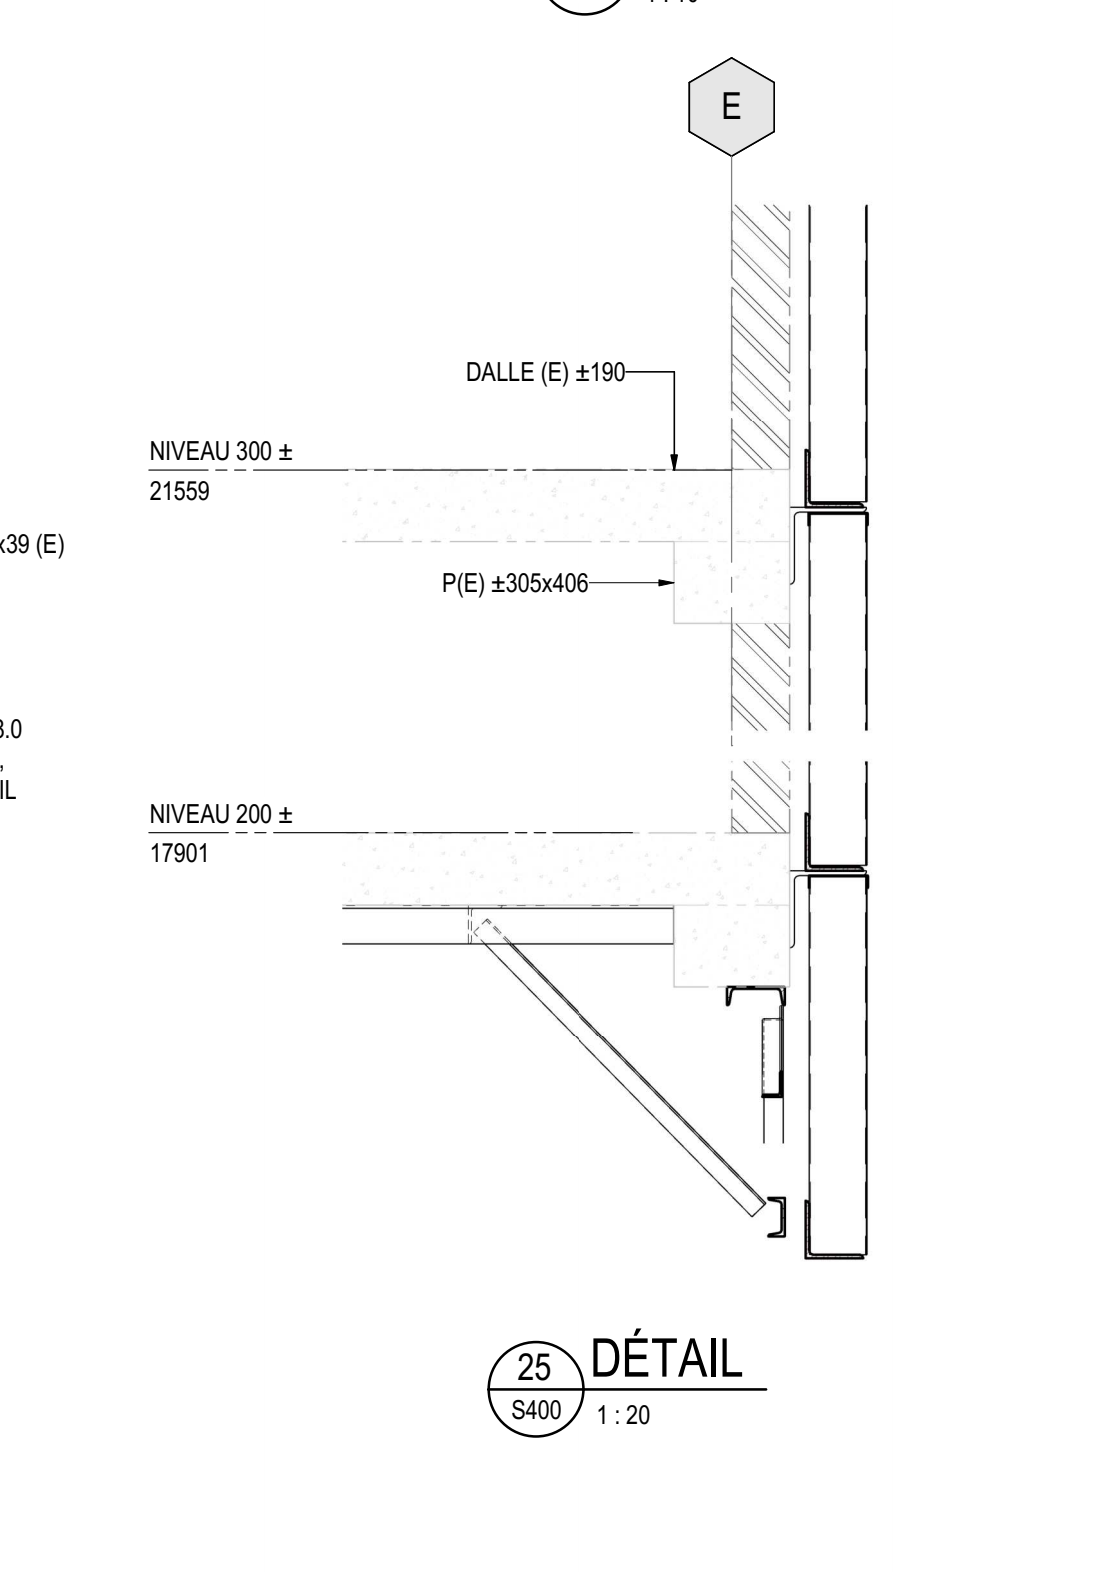


17 COUPE
S400 1:20

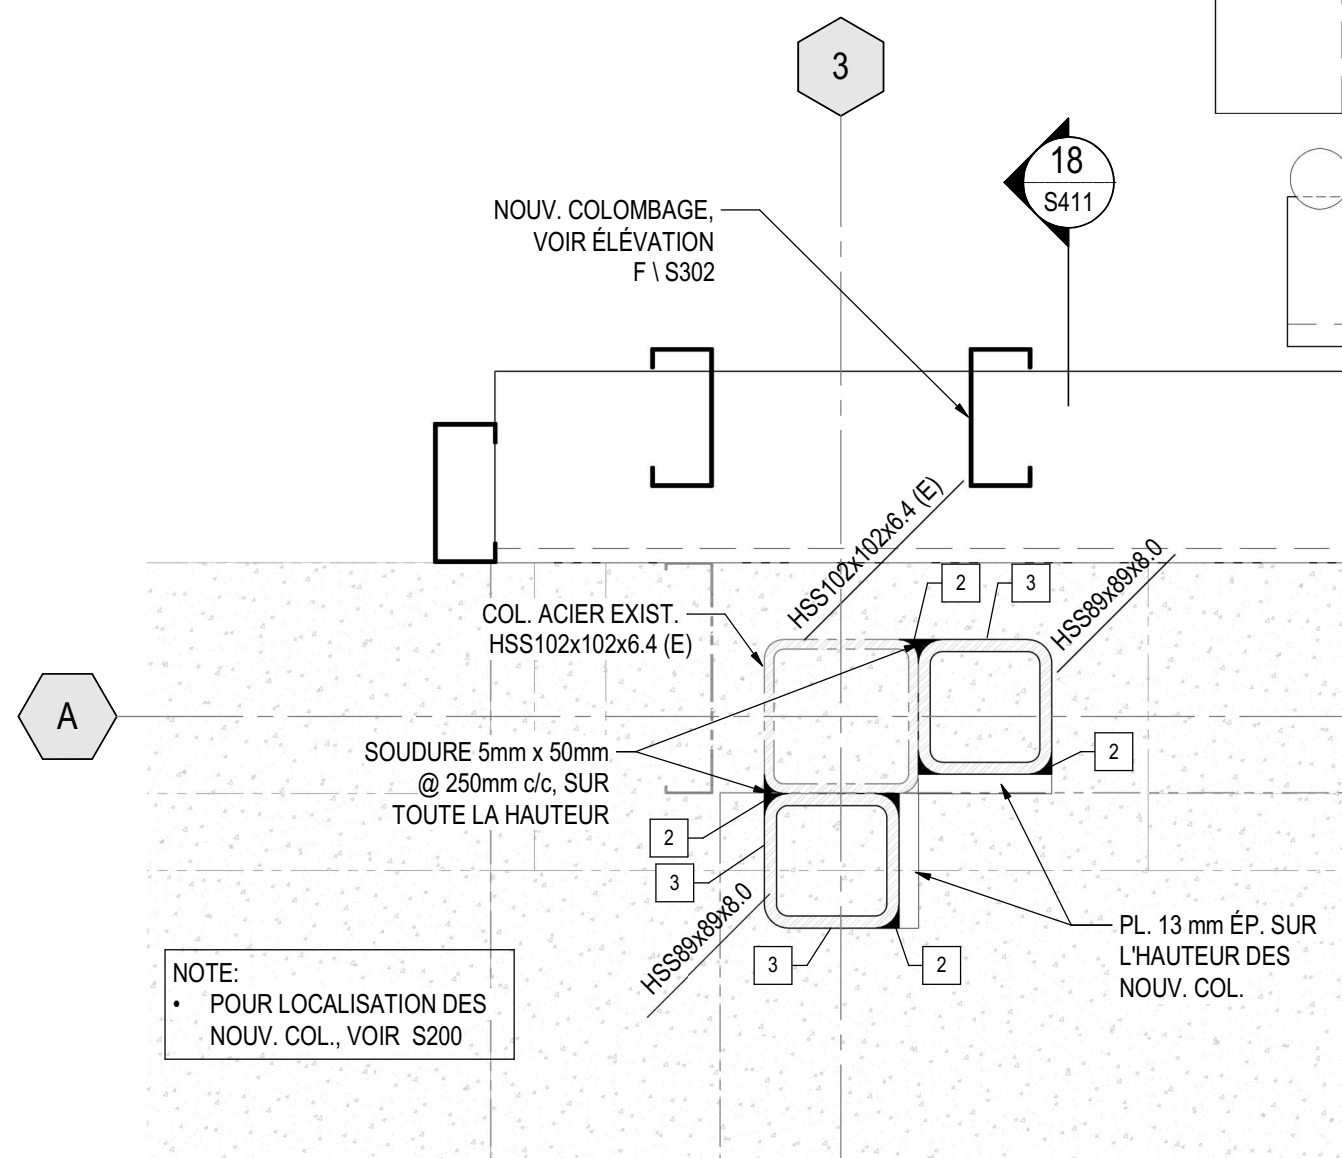


18 COUPE
S411 1:25

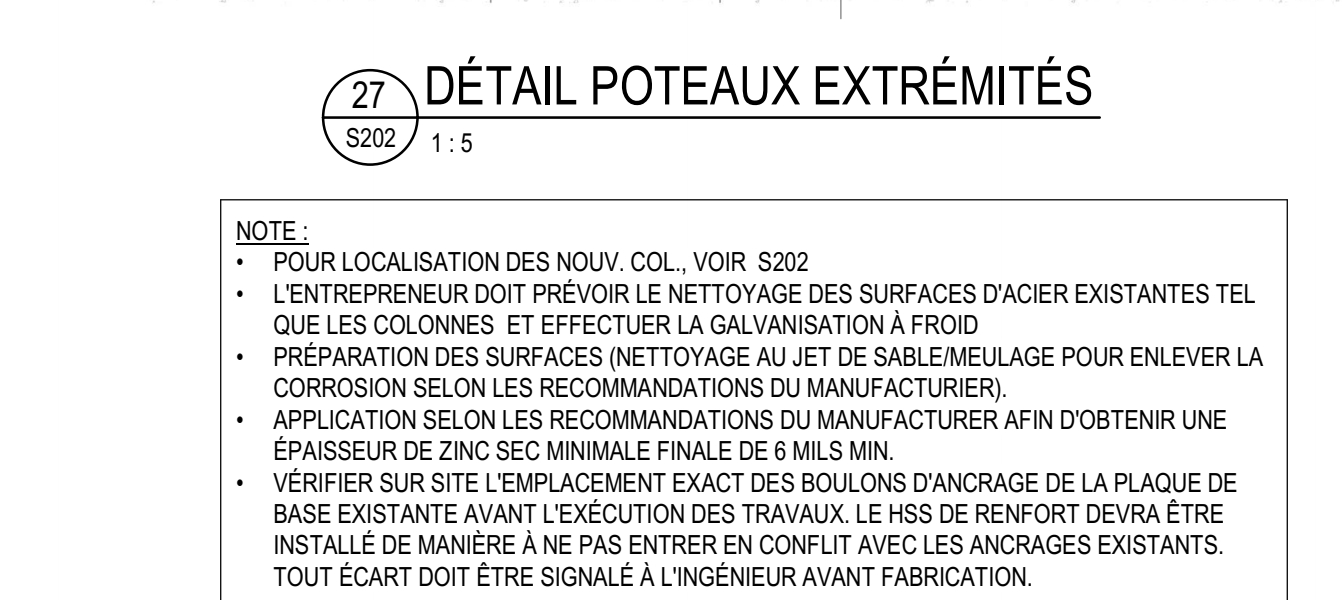

19 DÉTAIL
S400 1:20

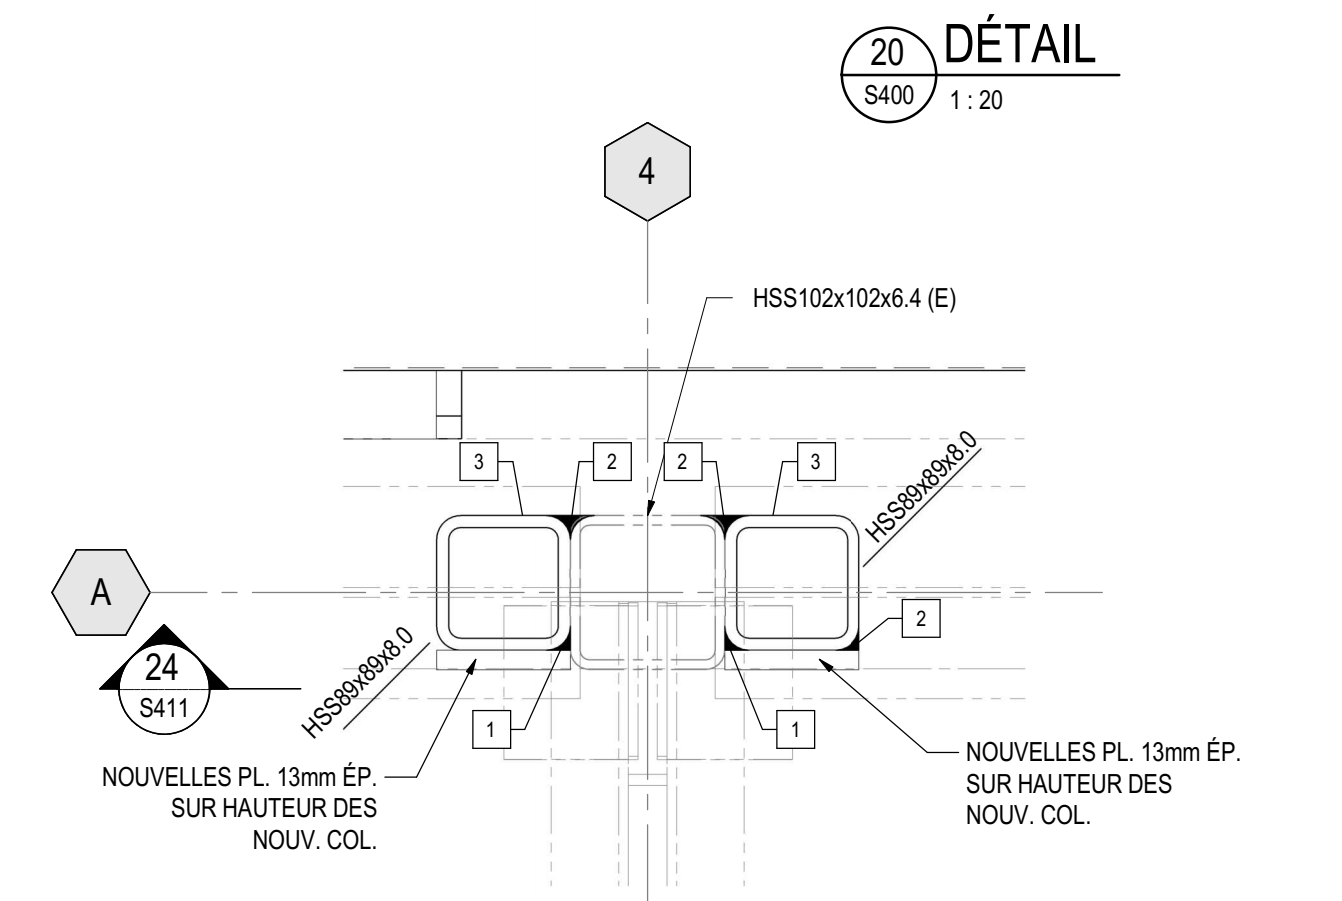

20 DÉTAIL
S400 1:20

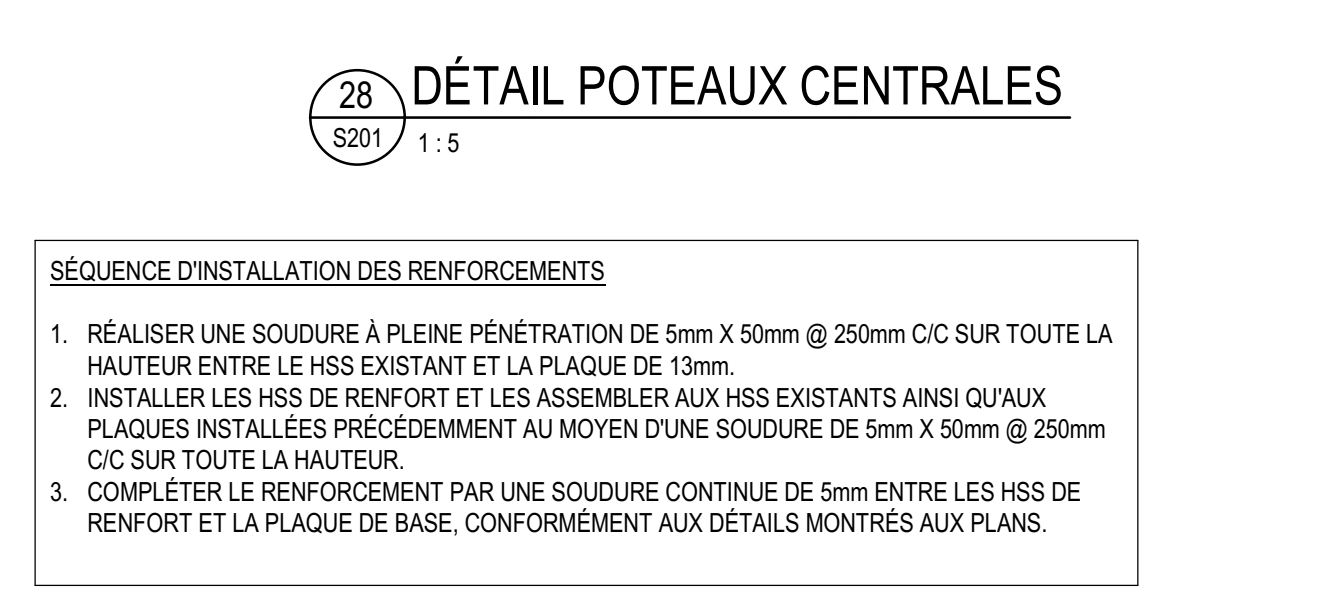

21 DÉTAIL
S401 1:5

NOTE:
• POUR LOCALISATION DES NOUV. COL., VOIR S202
• L'ENTREPRENEUR DOIT PRÉVOIR LE NETTOYAGE DES SURFACES D'ACIER EXISTANTES TEL QUE LES COLONNES ET EFFECTUER LA GALVANISATION À FROID
• PRÉPARATION DES SURFACES (NETTOYAGE AU JET DE SABLE/MEULAGE POUR ENLEVER LA CORROSION SELON LES RECOMMANDATIONS DU MANUFACTURIER)
• APPLICATION SELON LES RECOMMANDATIONS DU MANUFACTURIER AFIN D'OBTENIR UNE ÉPAISSEUR DE ZINC SEC MINIMALE FINALE DE 6 MILS MIN.
• VÉRIFIER SUR SITE L'EMPLACEMENT EXACT DES BOULONS D'ANCRAGE DE LA PLAQUE DE BASE EXISTANTE AVANT L'EXÉCUTION DES TRAVAUX. LE HSS DE RENFORT DEVRA ÊTRE INSTALLÉ DE MANIÈRE À NE PAS ENTRER EN CONFLIT AVEC LES ANCRAGES EXISTANTS. TOUT ÉCART DOIT ÊTRE SIGNALÉ À L'INGÉNIEUR AVANT FABRICATION.

SÉQUENCE D'INSTALLATION DES RENFORCEMENTS
1. RÉALISER UNE SOUDURE À PLEINE PÉNÉTRATION DE 5mm X 50mm @ 250mm C/C SUR TOUTE LA HAUTEUR ENTRE LE HSS EXISTANT ET LA PLAQUE DE 13mm.
2. INSTALLER LES HSS DE RENFORT ET LES ASSEMBLER AUX HSS EXISTANTS AINSI QU'aux PLAQUES INSTALLÉES PRÉCÉDEMMENT AU MOYEN D'UNE SOUDURE DE 5mm X 50mm @ 250mm C/C SUR TOUTE LA HAUTEUR.
3. COMPLÉTER LE RENFORCEMENT PAR UNE SOUDURE CONTINUE DE 5mm ENTRE LES HSS DE RENFORT ET LA PLAQUE DE BASE, CONFORMÉMENT AUX DÉTAILS MONTRÉS AUX PLANS.

CE DOCUMENT NE DOIT PAS ÊTRE UTILISÉ
À DES FINS DE CONSTRUCTION

ARCHITECTURE:

GLCRM **GLCRM+PROULXSAVARD**
CONSORTIUM D'ARCHITECTES

MÉCANIQUE:

wsp

RÉVISIONS:			
REV	DATE	DESCRIPTION	PAR
0	2026-09-04	DÉFINITIFS POUR SOUMISSION	JLB

SCEAU:

Jean-Luc Bouffard
5015089

AVERTISSEMENT:
CE Dessin est la propriété intellectuelle de WSP Canada Inc. Aucune réimpression, reproduction ou tout autre usage n'est permis sans l'autorisation écrite de WSP Canada Inc. L'entrepreneur devra vérifier toutes les dimensions aux plans et faire localiser tous les services d'utilités publiques et rapporter toutes erreurs ou omissions avant de commencer les travaux.

ÉCHELLE ORIGINALE:
Comme indiqué

DATE:
2026-09-04

PRÉPARÉ PAR:
JOANIE ROBILLARD, ing.
CHARLOTTE ALLARD, CPI
NATHAN SCHMITT, ing. PRT

VÉRIFIÉ PAR:
JEAN-LUC BOUFFARD, ing.

DESSINÉ PAR:
GLORIA GILDA SIMIREA, tech.

SI CETTE BARRE NE MESURE PAS 25 mm, AJUSTER VOTRE ÉCHELLE DE TRAÇAGE.

DISCIPLINE:
STRUCTURE

wsp

WSP Canada Inc.
1135 Boulevard Lebourgneuf
Ville de Québec, Québec, G2K 0M5
T +1 418-623-2254 | www.wsp.com

NO PROJET: CA0062562.5541

CLIENT:

Santé Québec

RÉF. CLIENT: R874-24 / 24-108

PROJET:




**HÔPITAL DE CHANDLER
(RÉFECTION DE L'ENVELOPPE)**

TITRE:

Coupes et détails

NUMÉRO DU FEUILLET: **S411**

REV: **0**

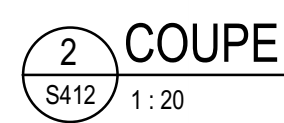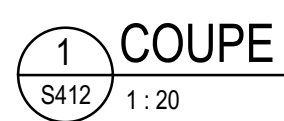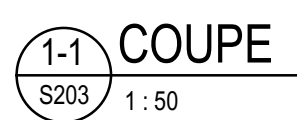

WS |

[illegible]

ÉCHELLE ORIGINALE: Comme indiqué	DATE: 2026-09-04
PRÉPARE PAR: JOANIE ROBILLARD, ing. CHARLOTTE ALLARD, CPI NATHAN SCHMITT, ing. PRT	SI CETTE BARRE NE MESURE PAS 25 mm AJUSTER VOTRE ÉCHELLE DE TRACAGE.
VÉRIFIER PAR: JEAN-LUC BOUFFARD, ing.	
DESSINÉ PAR: GLORIA GILDA SIMIREA, tech.	25mm

DISCIPLINE:	STRUCTURE
-------------	-----------

WSP Canada Inc.
1135 Boulevard Lebourgneuf
Ville de Québec, Québec, G2K 0M5
T +1 418-623-2254 | www.wsp.com

NO PROJET: CA0062562.5541

CLIENT:



RÉF. CLIENT: R674-24 / 24-108

PROJET:

HÔPITAL DE CHANDLER
(RÉFECTION DE L'ENVELOPPE)

TITRE:

ÉLEVATIONS, COUPES ET
DÉTAILS CHARPANTE
SUPPORT

NUMÉRO DU FEUILLET:

S412

REV.

CE DOCUMENT NE DOIT PAS ÊTRE UTILISÉ
À DES FINS DE CONSTRUCTION