


Autodesk Docs/Reflexion Enr Hôpital Chandler/CA0062562_5541_STR_P26.rvt
2026-09-04 11:13:46

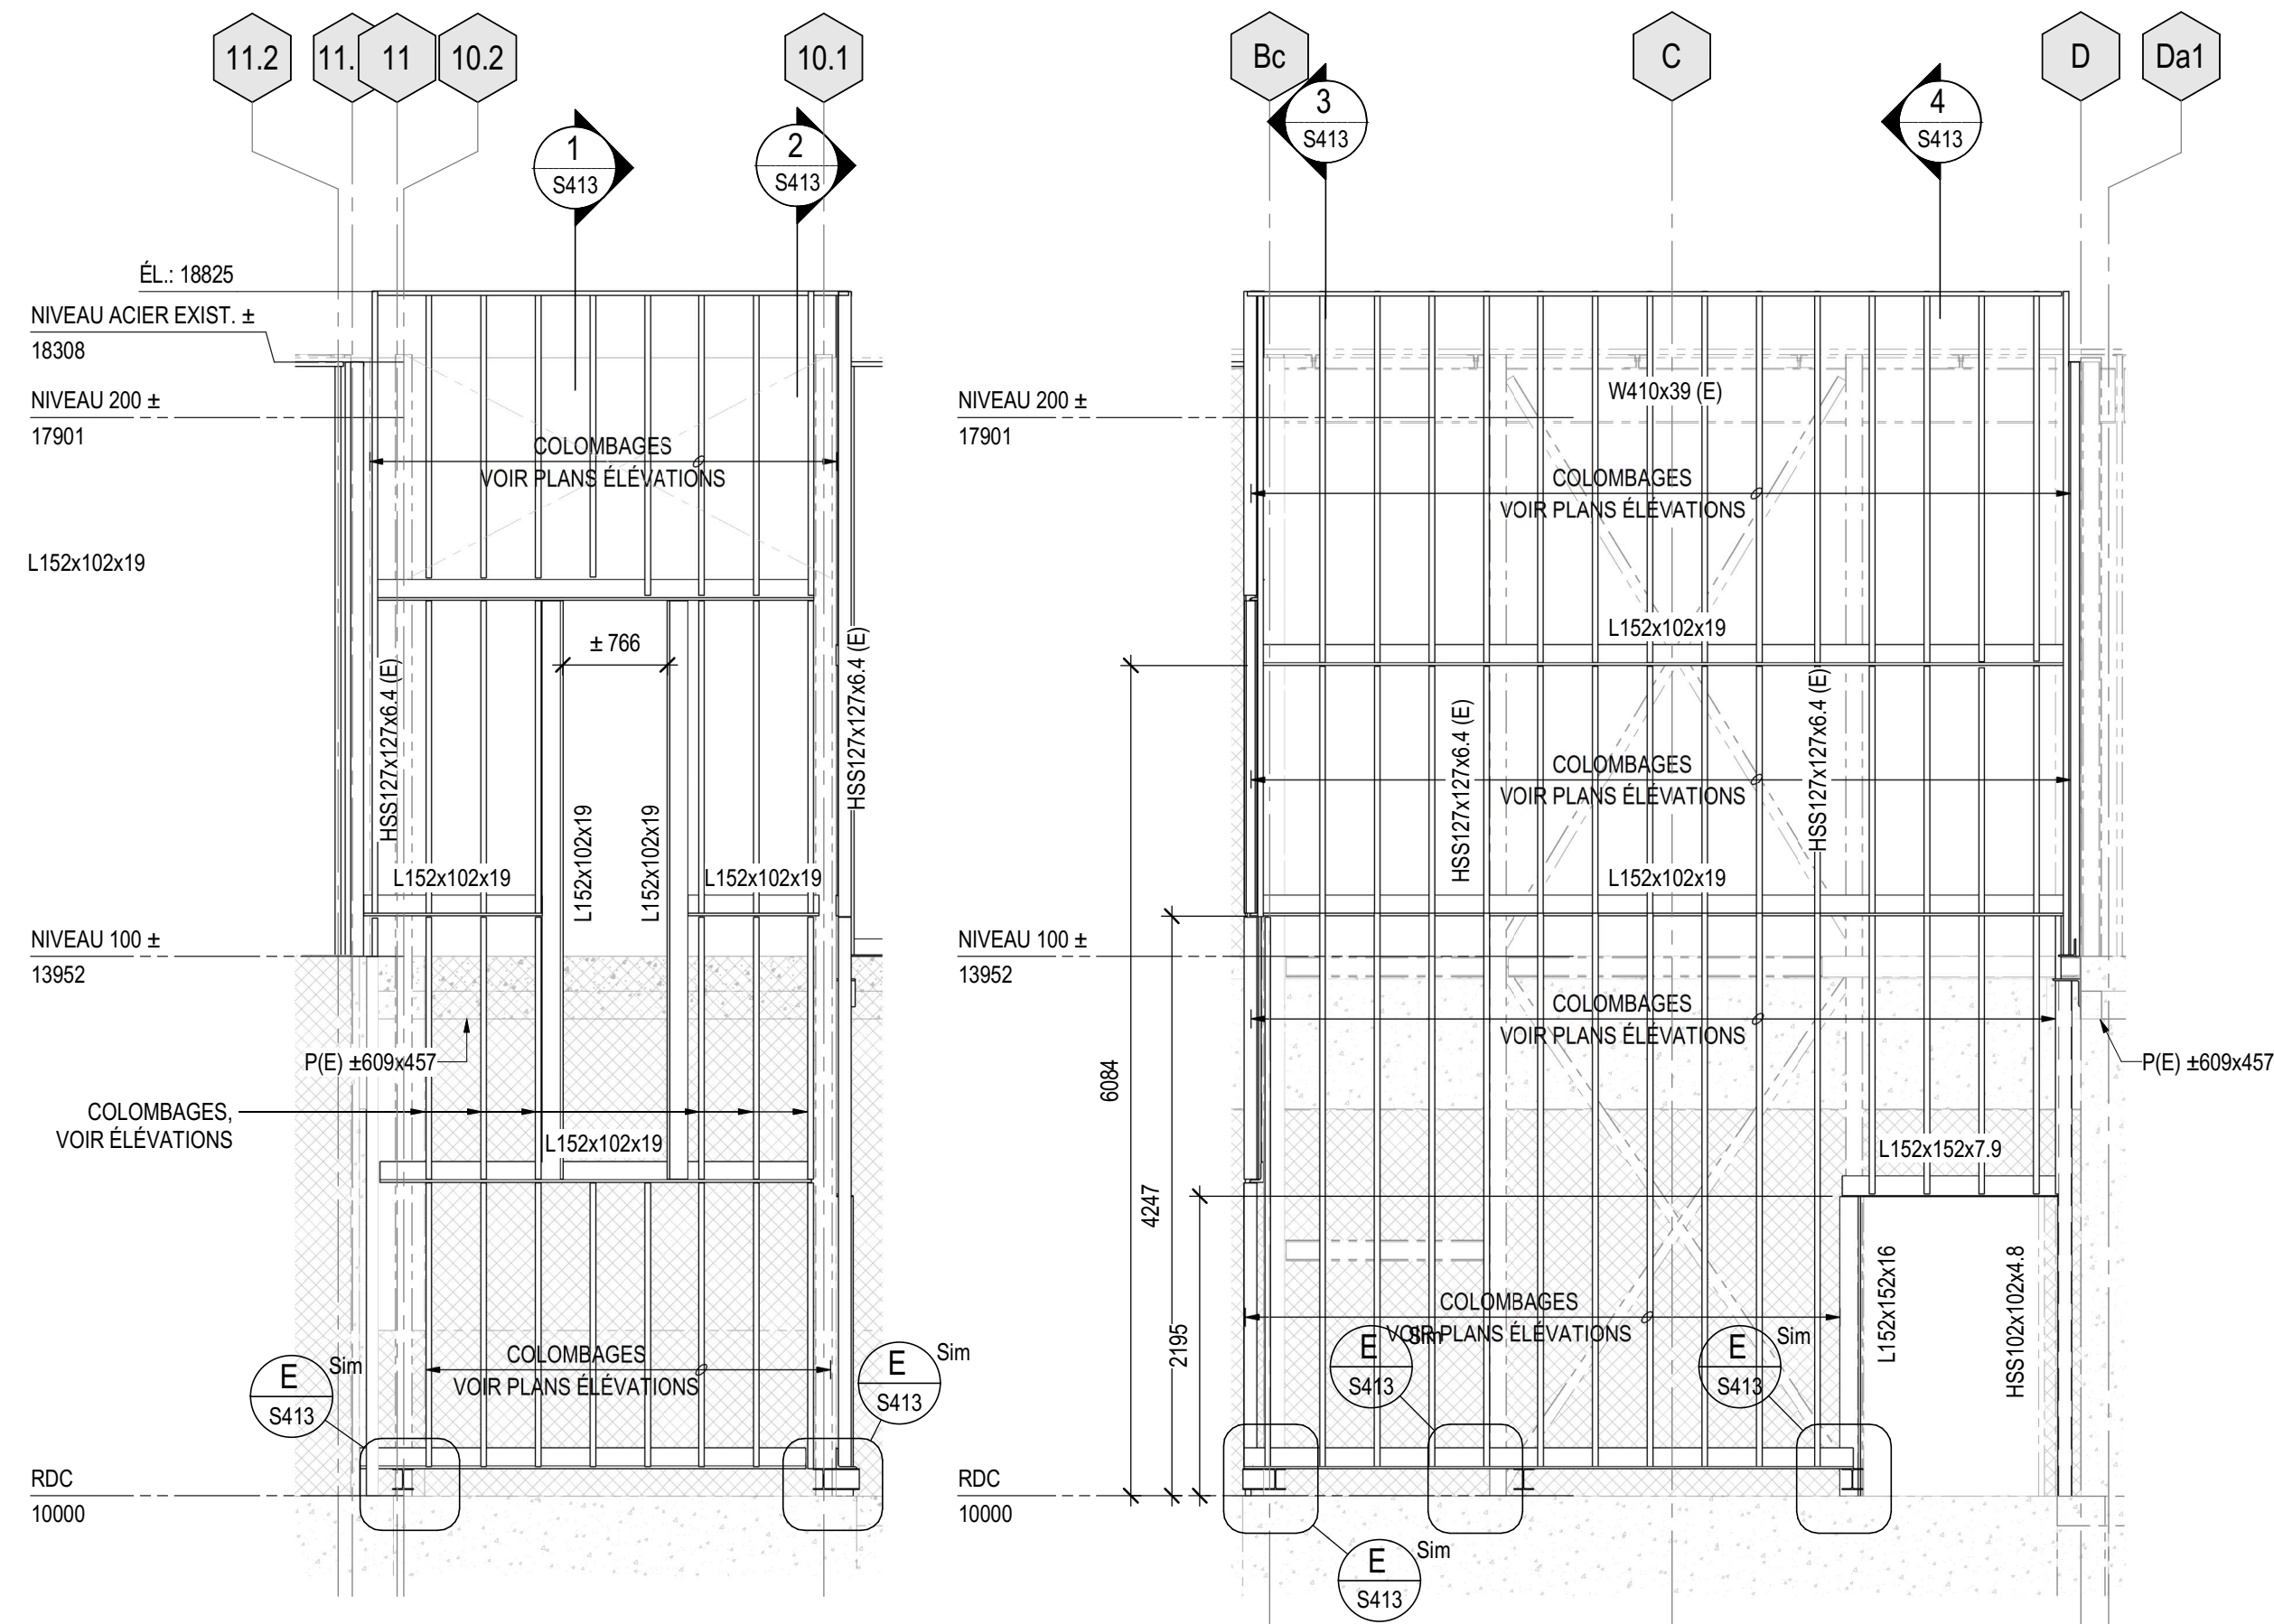

A ÉLEVATION ESCALIER #6
S302 1:50


B ÉLEVATION ESCALIER #6
S303 1:50

1 COUPE ESCALIER #6
S413 1:50

2 COUPE ESCALIER #6
S413 1:50


3 COUPE ESCALIER #6
S413 1:50

4 COUPE ESCALIER #6
S413 1:50

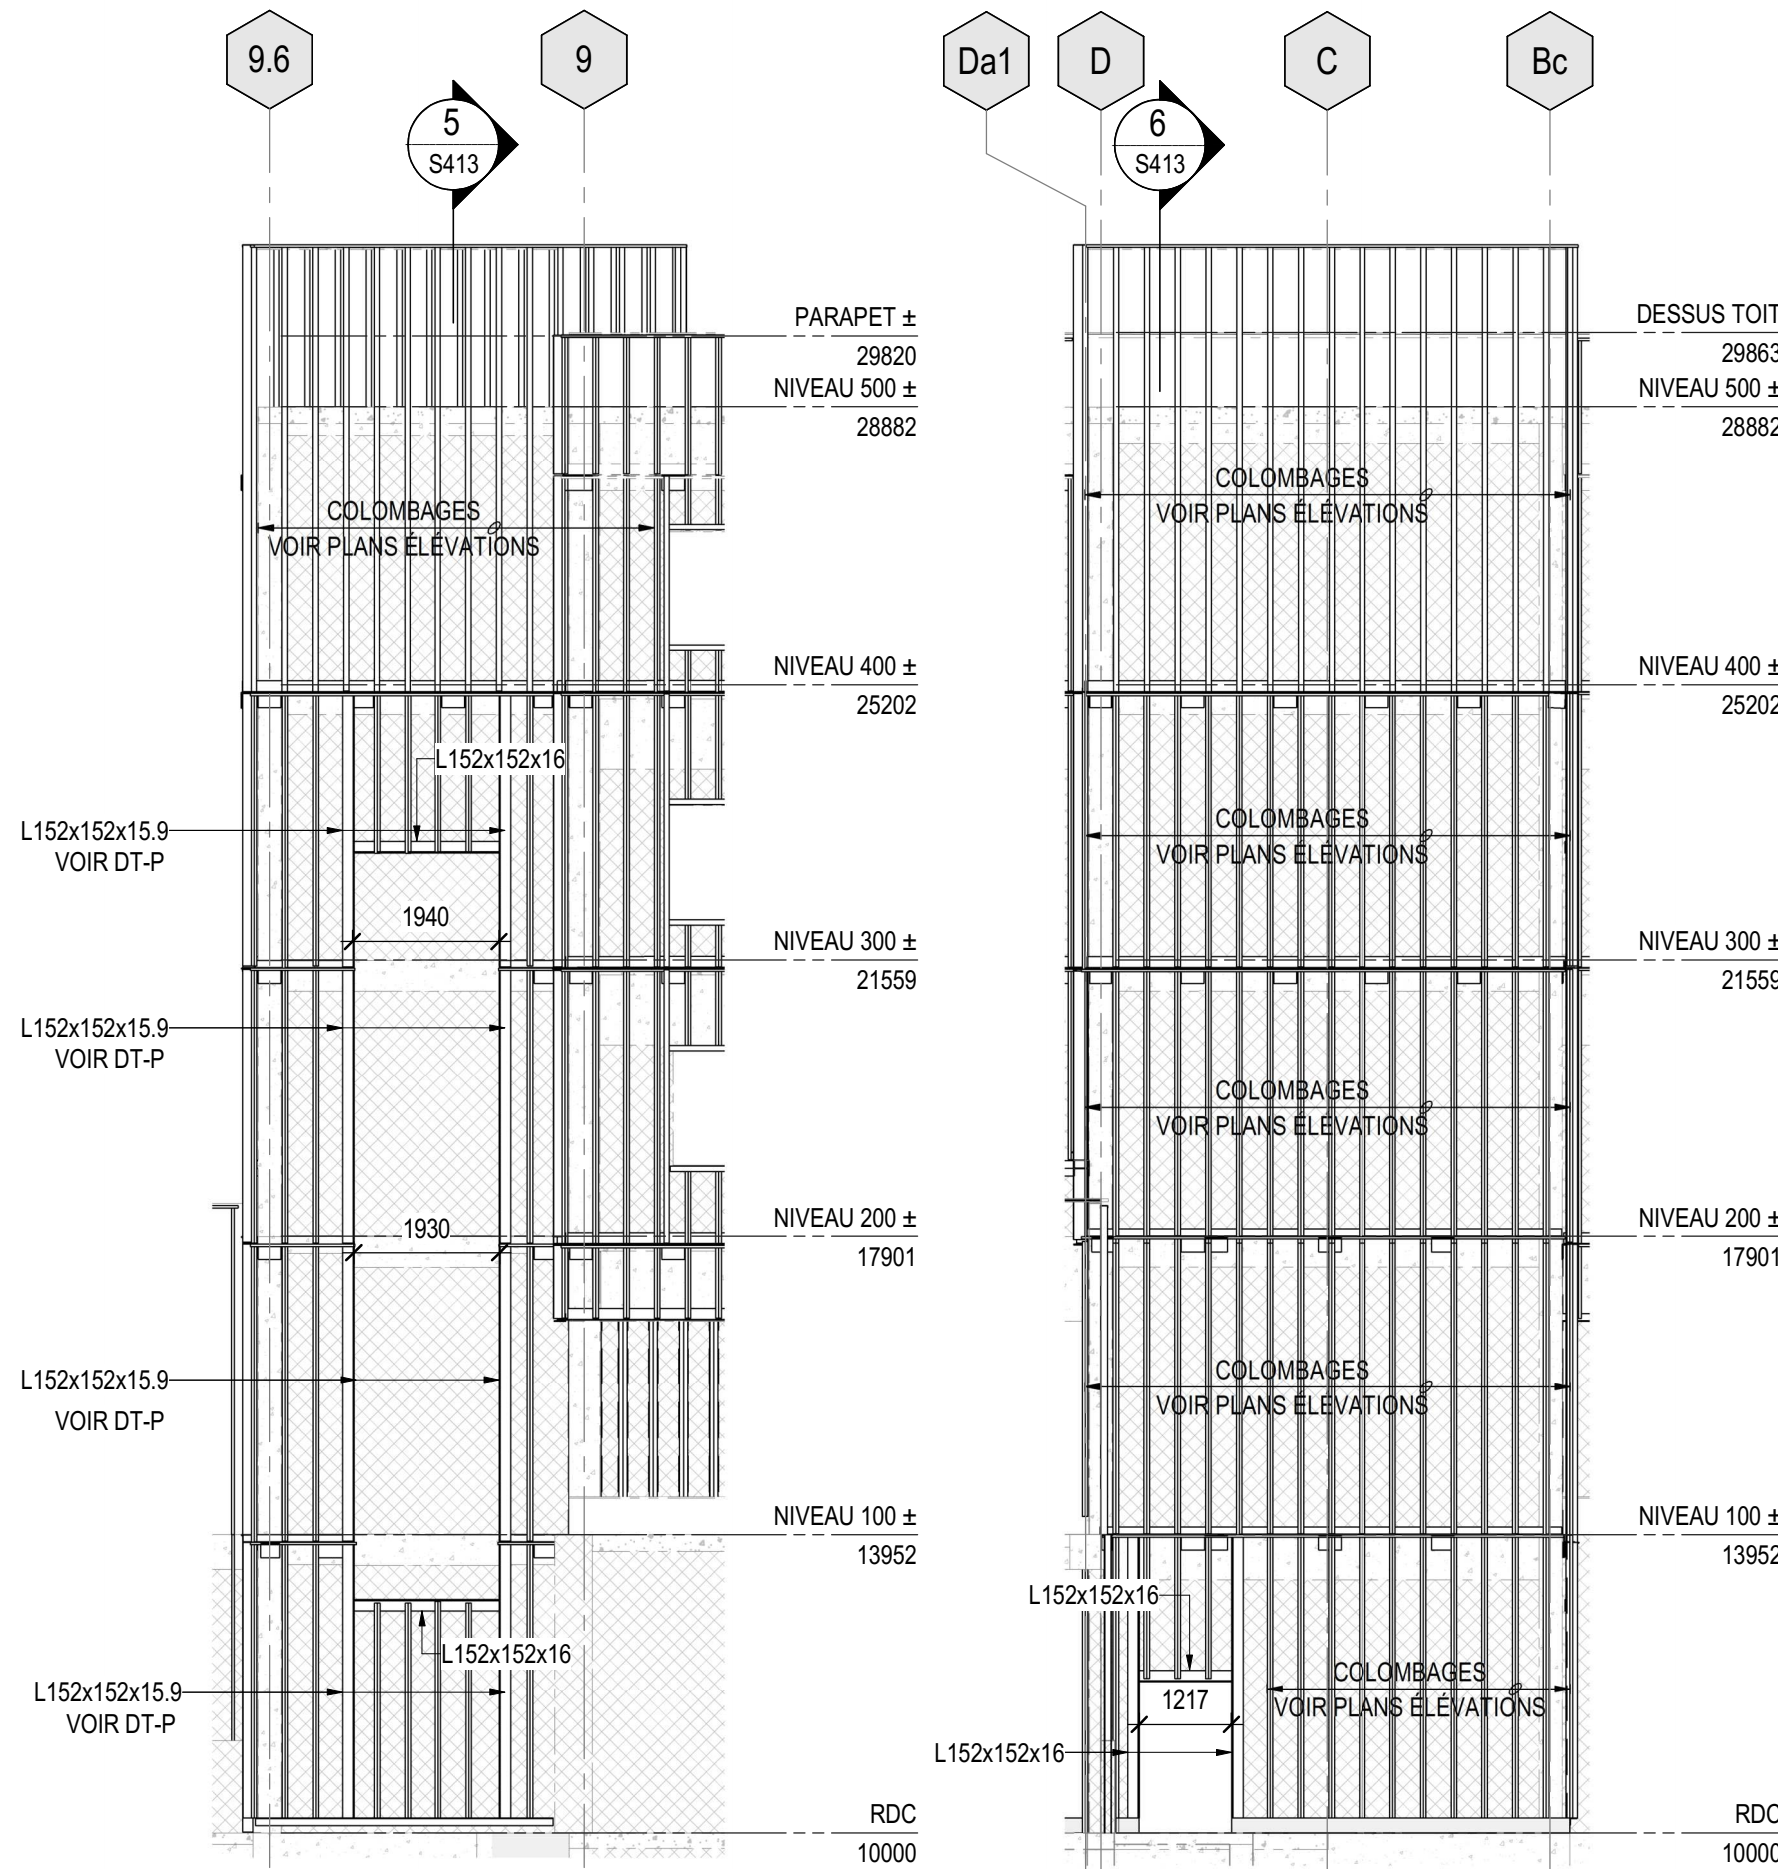


C ÉLEVATION ESCALIER #3
S302 1:100

D ÉLEVATION ESCALIER #3
S303 1:100

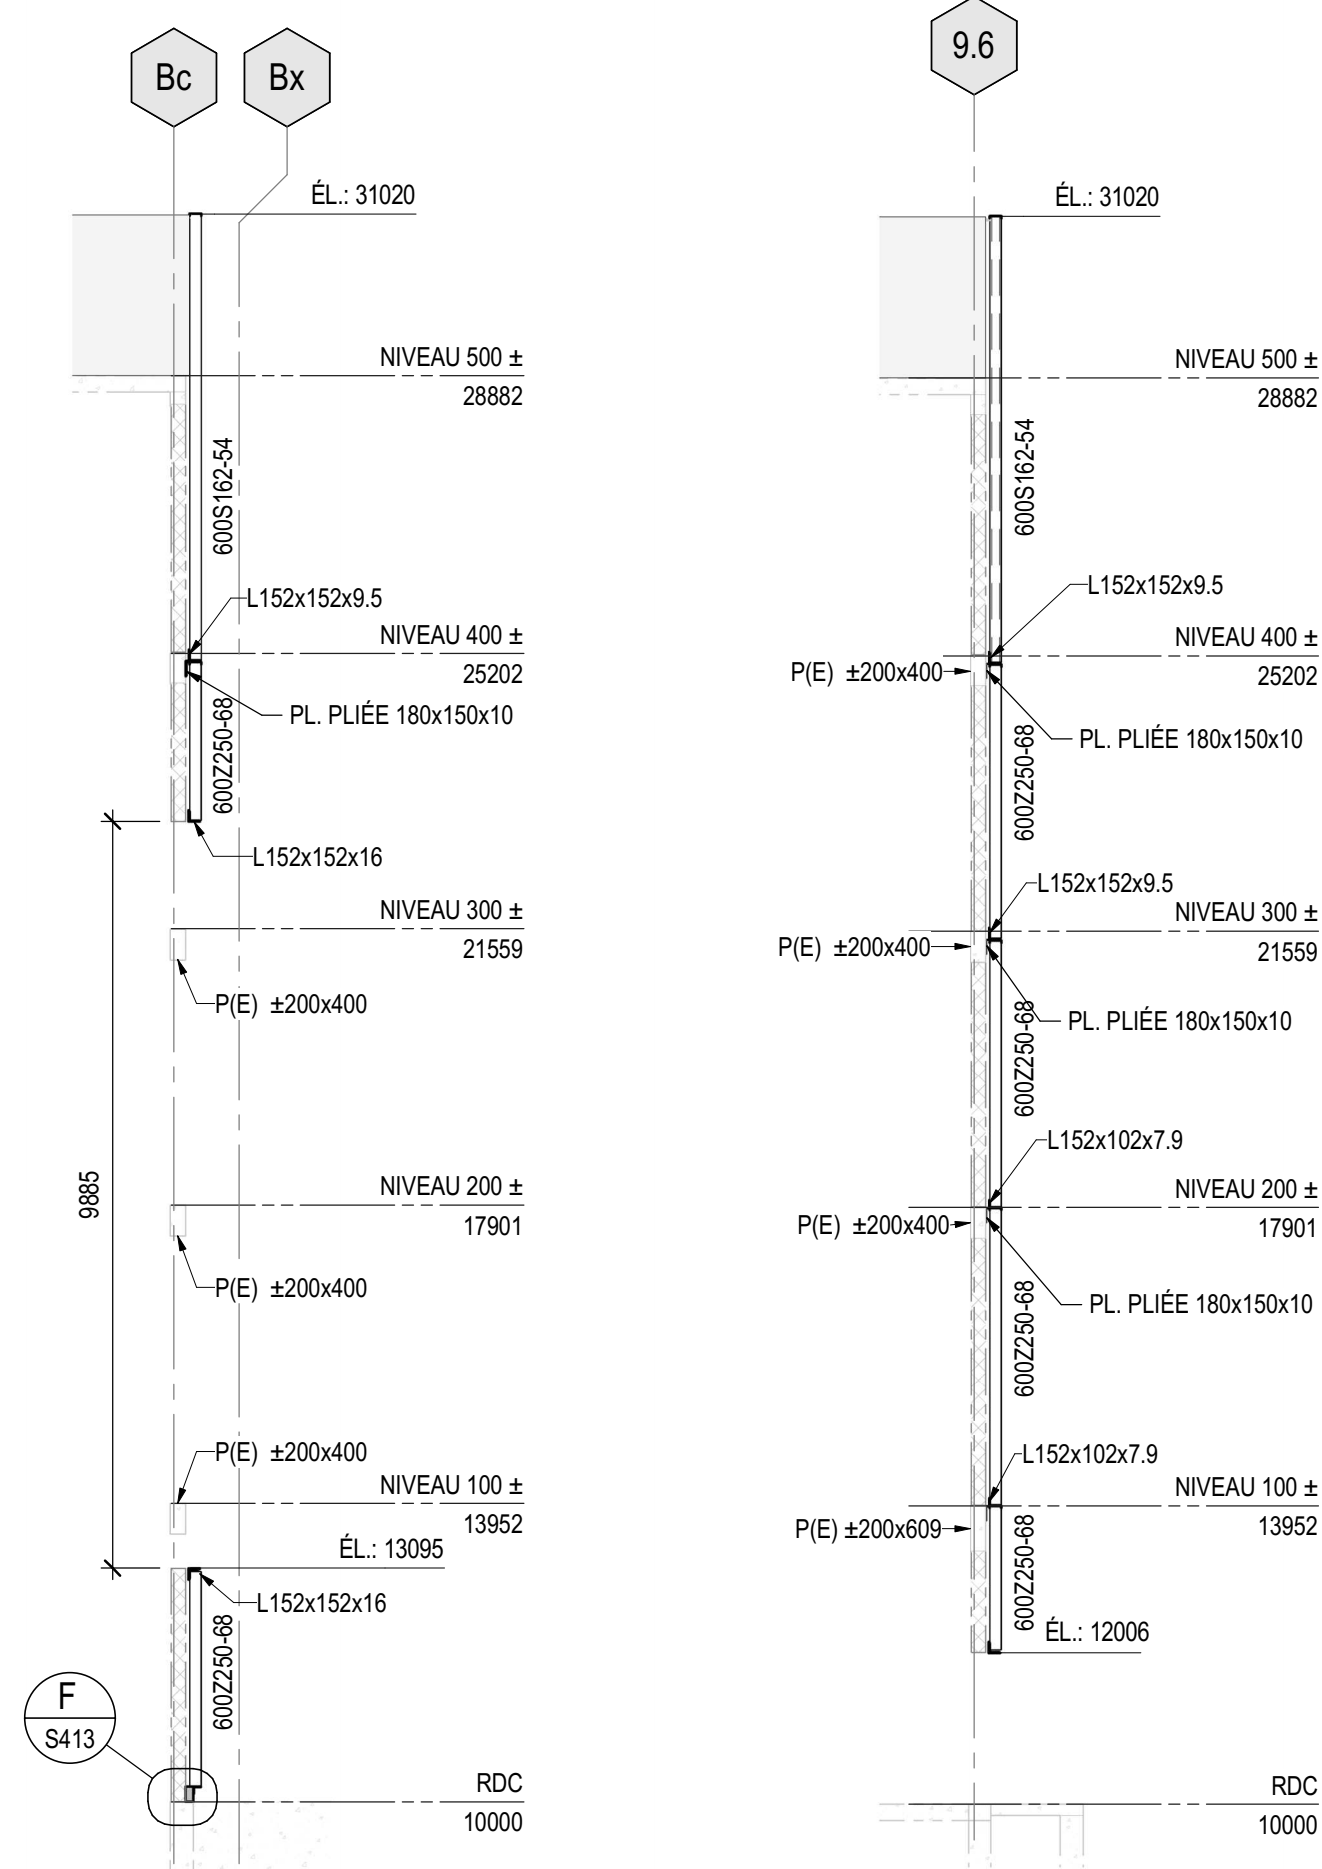


5 COUPE ESCALIER #3
S413 1:100

6 COUPE ESCALIER #3
S413 1:100

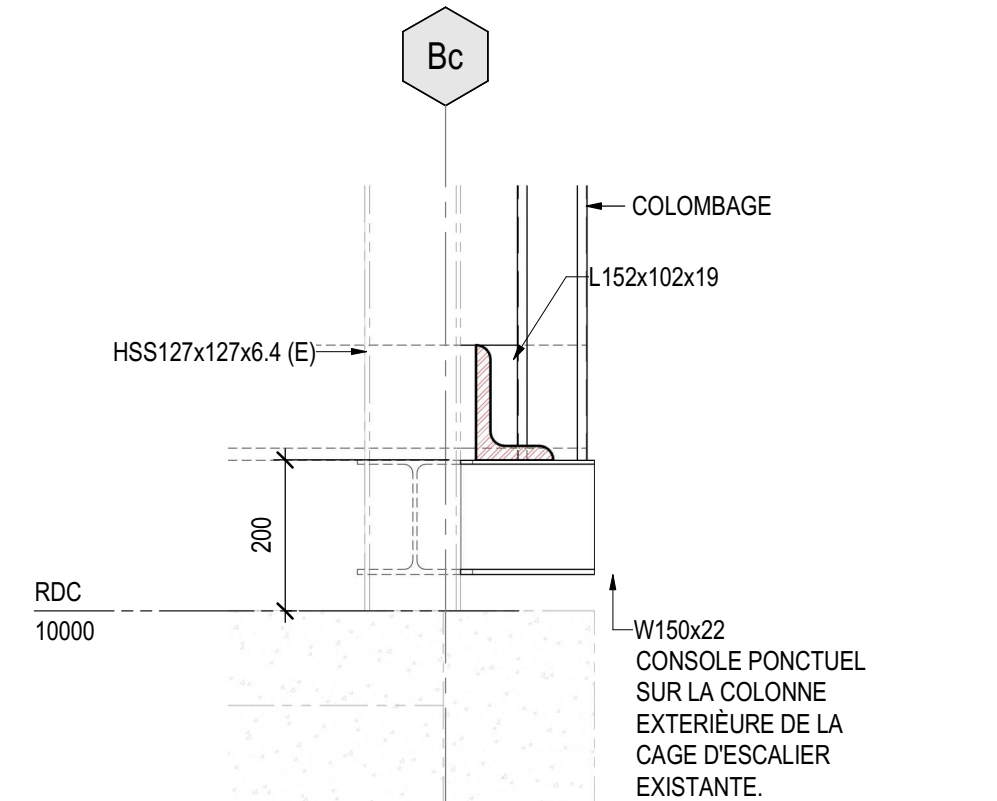

E DÉTAIL CONNEXION À LA BASE D'ESCALIER #6
S413 1:10

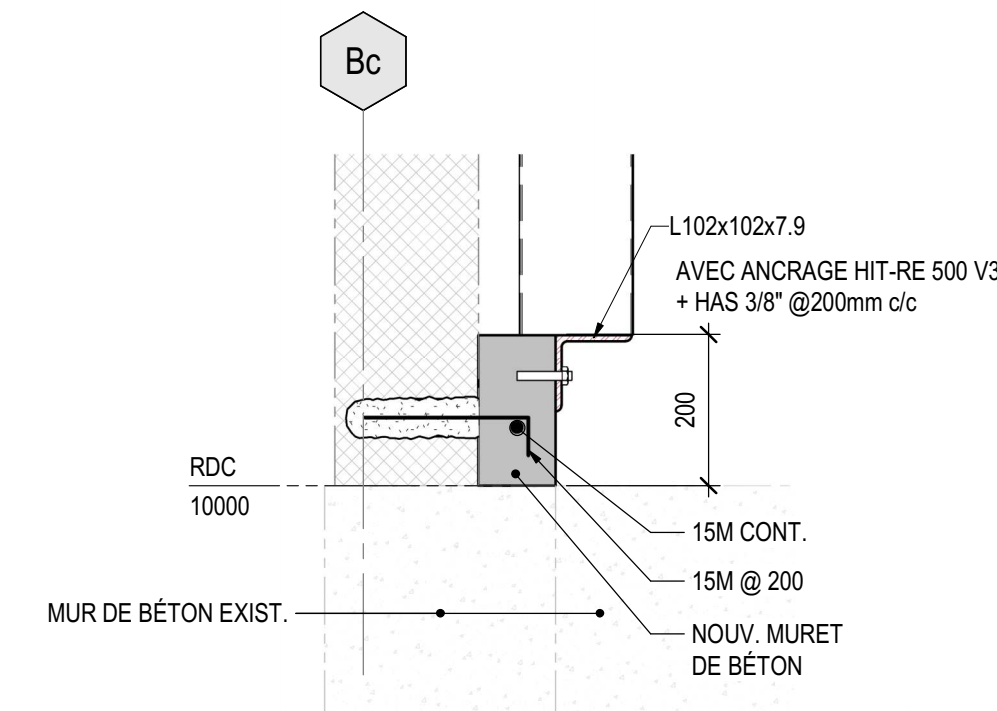

F DÉTAIL À LA BASE D'ESCALIER #3
S413 1:10

CE DOCUMENT NE DOIT PAS ÊTRE UTILISÉ
À DES FINS DE CONSTRUCTION

ARCHITECTURE:




MÉCANIQUE:



RÉVISIONS:

REV	DATE	DESCRIPTION	PAR
0	2026-09-04	DÉFINITIFS POUR SOUMISSION	JLB

SCEAU:

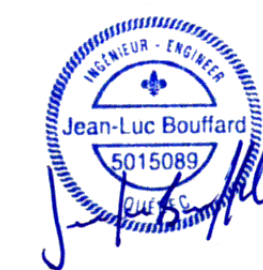

AVERTISSEMENT: CE DESIGN EST LA PROPRIÉTÉ INTELLECTUELLE DE WSP CANADA INC. AUCUNE RÉVISION, REPRODUCTION OU TOUT AUTRE USAGE N'EST PERMIS SANS L'AUTORISATION ÉCRITE DE WSP CANADA INC. L'UTILISATEUR DOIT VÉRIFIER TOUTES LES DIMENSIONS AUX PLANS ET FAIRE LOCALISER TOUTES LES SERVICES D'UTILITÉS PUBLIQUES ET RAPPORTER TOUTES ERREURS OU OMISSIONS AVANT DE COMMENCER LES TRAVAUX.

ÉCHELLE ORIGINALE: Comme indiqué	DATE: 2026-09-04
PRÉPARÉ PAR: JOANIE ROBILLARD, ing. CHARLOTTE ALLARD, CPI NATHAN SCHMITT, ing. PRT	SI CETTE BARRE NE MESURE PAS 25 mm, AJUSTER VOTRE ÉCHELLE DE TRACÉ.
VÉRIFIÉ PAR: JEAN-LUC BOUFFARD, ing.	
DESSINÉ PAR: GLORIA GILDA SIMIREA, tech.	

DISCIPLINE: STRUCTURE



WSP Canada Inc.
1135 Boulevard Lebourgneuf
Ville de Québec, Québec, G2K 0M5
T +1 418-623-2254 | www.wsp.com

NO PROJET: CA0062562.5541

CLIENT:



RÉF. CLIENT: R674-24 / 24-108

PROJET:

HÔPITAL DE CHANDLER
(RÉFECTION DE L'ENVELOPPE)

TITRE:


ÉLEVATIONS, COUPES ET
DÉTAILS ESCALIERS

NUMÉRO DU FEUILLET:

S413

REV:

0

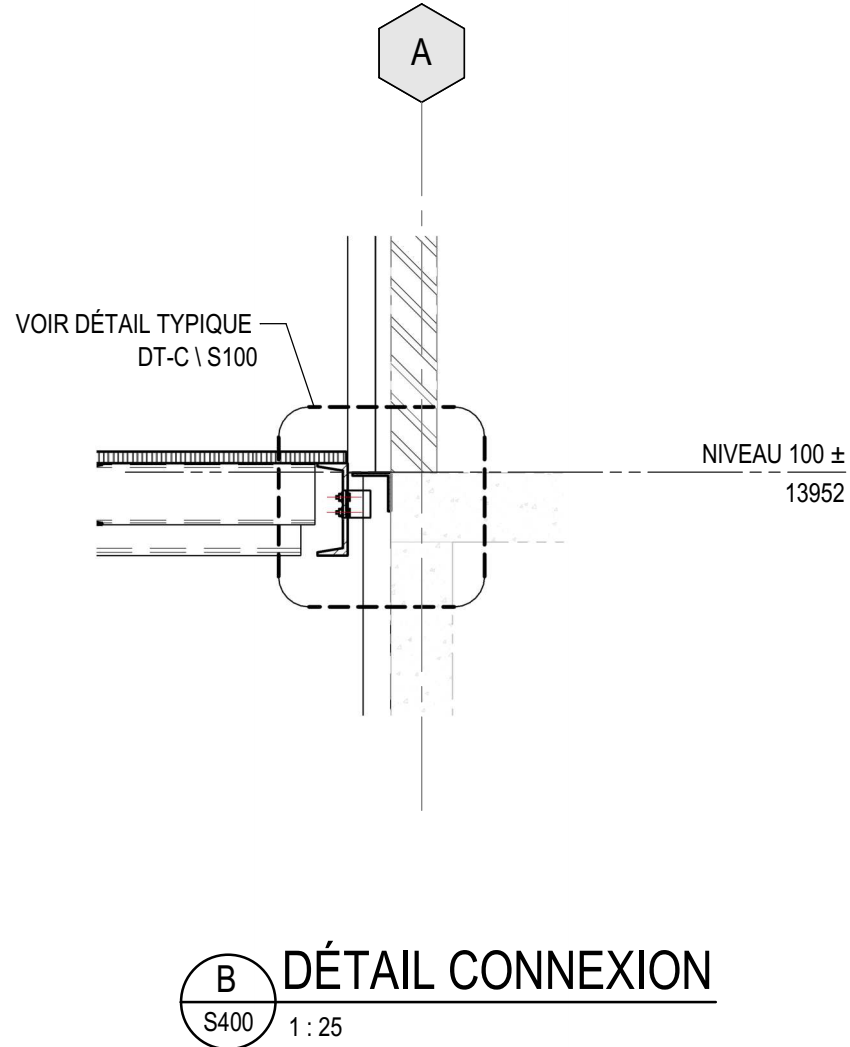

ARCHITECTURE:



MECANIQUE:



REVISIONS:			
REV	DATE	DESCRIPTION	PAR
0	2026-09-04	DÉFINITIFS POUR SOUMISSION	JLB

SCEAU:

AVERTISSEMENT: DROIT D'AUTEUR:
CE DESSIN EST LA PROPRIÉTÉ INTELLECTUELLE DE WSP CANADA INC. AUCUNE RÉVISION,
REPRODUCTION OU TOUT AUTRE USAGE N'EST PERMIS SANS L'AUTORISATION ÉCRITE DE WSP CANADA
INC. L'ENTREPRENEUR DEVRA VÉRIFIER TOUTES LES DIMENSIONS AUX PLANS ET FAIRE LOCALISER TOUTES
LES SERVICES D'UTILITÉS PUBLIQUES ET RAPPORTER TOUTES ERREURS OU OMISSIONS AVANT DE

ÉCHELLE ORIGINALE: Comme indiqué	DATE: 2026-09-04
PRÉPARÉ PAR: JOANIE ROBILLARD, ing. CHARLOTTE ALLARD, CPI NATHAN SCHMITT, ing. PRT	SI CETTE BARRE NE MESURE PAS 25 mm, AJUSTER VOTRE ÉCHELLE DE TRAÇAGE.
VÉRIFIÉ PAR: JEAN-LUC BOUFFARD, ing.	
DESSINÉ PAR: GLORIA GILDA SIMIREA, tech.	25mm

DISCIPLINE: STRUCTURE

wsp
WSP Canada Inc.
1135 Boulevard Lebourgneuf
Ville de Québec, Québec, G2K 0M5
T +1 418-623-2254 | www.wsp.com

NO PROJCT: CA0062562.5541

CLIENT: _____



RÉF. CLIENT: R674-24 / 24-108

PROJET: _____

HÔPITAL DE CHANDLER
(RÉFECTION DE L'ENVELOPPE)

TITRE: _____

ÉLÉVATIONS, COUPES ET DÉTAILS ESCALIERS

NUMÉRO DU FEUILLET:	REV.
---------------------	------

S414	0
------	---