

- NOTES
- 61) NOUVEL APPAREIL DE CHAUFFAGE, VOIR DOCUMENTS D'INGÉNÉRIE.
- 62) TOLE EN ACIER GALVANISÉ 1,994mm ép. INSTALLÉE EN SURFACE DU PARAPET AVANT L'INSTALLATION DES NOUVELLES MEMBRANES DU PARAPET.
- 63) NOUVELLE PERSIENNE DE 950 X 400mm. VOIR DÉTAIL 24 DE LA FEUILLE 455.
- 64) NOUVELLE PORTE ISOLÉE ET CADRE EN ACIER ISOLÉ AVEC BRIS THERMIQUE, PEINT, 762 X 1800mm.
- 65) NOUVEAU PARAPET ET ZONE DE RECONSTRUCTION DE TOITURE, VOIR DÉTAIL 4 SUR LA FEUILLE 306.
- 66) APPRÊTER, PLÂTRER ET PEINDRE LE MUR D'UN COIN À L'AUTRE. PRÉVOIR LE REMPLACEMENT DE LA CIMASE SUR TOUTE LA LARGEUR DU MUR EXTÉRIEUR.
- 67) APPRÊTER, PLÂTRER ET PEINDRE LE MUR D'UN COIN À L'AUTRE. LA FINITION DU MUR EXISTANT EST À REPROFILER DE LAÇON À OBTENIR UNE SURFACE LISSE AVANT LES TRAVAUX DE PEINTURE. PRÉVOIR LE RETRAIT DES MOULURES VERTICALES AVANT DE PRÉPARER LA SURFACE.

- NOTES
- 55) NOUVEL AÉRATEUR D'ENTRETOIT. PRÉVOIR UNE NOUVELLE BASE EN CONTREPLAQUÉ 19mm TYPE EXTERIEUR RECOUVERTE DU SYSTÈME DE MEMBRANE ELASTOMÈRE. DIMENSIONS SELON LE TYPE. VOIR LEGENDE. PRÉVOIR ÉGALEMENT DE MODIFIER ET/OU RAGRÉER L'OUVERTURE DANS LE PONTAGE DE BOIS. LORSQUE INSTALLÉ DANS UNE OUVERTURE EXISTANTE, VOIR DÉTAIL 1 SUR LA FEUILLE 306.
- 56) NOUVELLE PORTE ISOLÉE ET CADRE EN ACIER ISOLÉ AVEC BRIS THERMIQUE, PEINT, 864 X 1880mm.
- 57) PRÉVOIR UN SCELLANT COUPE-FEU À LA TÊTE ET À LA BASE DE LA NOUVELLE CLOISON ET LA CLOISON EXISTANTE.
- 58) TUILES DE PLAFOND SUSPENDU À RÉINSTALLER. PRÉVOIR DE REMPLACER DES TUILES AU BESOIN.
- 59) OUVERTURE À OBTURER AVEC DES MATÉRIAUX TEL QUE L'EXISTANT APRÈS LES TRAVAUX DE STRUCTURE.
- 60) TUILE EXISTANTE COMPRENANT UN GICLEUR À CONSERVER ET À PROTÉGER PENDANT LES TRAVAUX.

- NOTES
- 49) NOUVELLE CLOISON CONSTRUIRE SOUS LA RETOMBÉE DE PLAFOND EXISTANTE À L'AIDE DE COLOMBAGE MÉTALLIQUE 92mm ET D'UN GYPSE 16mm TYPE X DE CHAQUE CÔTÉ. PRÉVOIR D'ENLEVER LES MOULURES SUR LA RETOMBÉE EXISTANTE.
- 50) TUILES DE PLAFOND SUSPENDU À RETIRER TEMPORAIREMENT POUR LES TRAVAUX DE MÉCANIQUE DANS L'ENTREPLAFOND ET À RÉINSTALLER.
- 51) NOUVEAU REVÊTEMENT DE PLANCHER DE VINYLE ET PLINTHE DE VINYLE TEL QUE L'EXISTANT À INSTALLER DANS LE LOCAL.
- 52) PEINDRE LE LOCAL AU COMPLET. COULEUR TEL QUE L'EXISTANT.
- 53) NOUVELLE PLINTHE DE VINYLE DES DEUX CÔTÉS DE LA CLOISON TEL QUE L'EXISTANT.
- 54) PROFIL DU NOUVEAU CAPOTIN DE VENTILATION.


- NOTES
- 42) NOUVEAU PARAPET INTRAMURAL, VOIR DÉTAIL EN COUPE TYPE DE LA SÉRIE DE FEUILLES 400.
- 43) FENÊTRE EXISTANTE À OBTURER, VOIR DÉTAIL #1 DE LA PAGE 504.
- 44) PRÉVOIR DE RAGRÉER AVEC DU GYPSE D'ÉPAISSEUR REQUISSE LES MURS ET LES CLOISONS TOUCHÉS PAR LA DÉMOLITION DES CLOISONS EXISTANTES. TIRER LES JOINTS ET PLÂTRER.
- 45) TUILES DE PLAFOND SUSPENDU À RETIRER TEMPORAIREMENT PENDANT LES TRAVAUX ET À RÉINSTALLER À LA FIN DES TRAVAUX.
- 46) NOUVEAU SOLIN SUR LE PARAPET EXISTANT, VOIR DÉTAILS DE LA SÉRIE DE FEUILLES 400.
- 47) ÉVENT DÉPLACÉ, VOIR DOCUMENTS D'INGÉNÉRIE.
- 48) NOUVEAU CONDUIT ET NOUVELLES PERSIENNES, VOIR DOCUMENTS D'INGÉNÉRIE.

- NOTES
- 34) OBTURER UNE PARTIE DE L'OUVERTURE AU-DESSUS DE LA NOUVELLE PORTE PROJETÉE, VOIR LE DÉTAIL #14 SUR LA FEUILLE 607.
- 35) NOUVELLE PORTE ISOLÉE ET CADRE EN ACIER ISOLÉ AVEC BRIS THERMIQUE, PEINT, 1015 X 2135mm.
- 36) NOUVEAU VOLET COUPE-FEU, VOIR DÉTAILS DE LA SÉRIE DE FEUILLES 500.
- 37) APPRÊTER, PLÂTRER ET PEINDRE LE MUR D'UN COIN À L'AUTRE.
- 38) TOLE EN ACIER GALVANISÉ 1,994mm ép. INSTALLÉE EN SURFACE DU PARAPET AVANT L'INSTALLATION DES NOUVELLES MEMBRANES DU PARAPET.
- 39) TOILE AMOVIBLE EXISTANTE À RÉINSTALLER.
- 40) INSTALLER UN TAPIS DE CAOUTCHOUC SOUS L'ESCALIER DE 1525 X 1525mm.
- 41) GARDE-CORPS EXISTANT À CONSERVER ET À PROTÉGER LORS DES TRAVAUX.

- NOTES
- 28) PARAPET EXISTANT À CONSERVER ET À PROTÉGER PENDANT LES TRAVAUX.
- 29) NOUVELLE PERSIENNE, VOIR DOCUMENT D'INGÉNÉRIE.
- 30) PRÉVOIR DE BOUCHER DE FAÇON ÉTANCHE TOUTS LES PERCEMENTS DU SYSTÈME DE TOITURE EXISTANT APRÈS LE RETRAIT DU GARDE-CORPS ET DES COMPOSANTES DU PALIER SUPÉRIEUR DE L'ESCALIER.
- 31) AÉRATEUR D'ENTRETOIT EXISTANT À RÉINSTALLER. PRÉVOIR UNE NOUVELLE BASE EN CONTREPLAQUÉ 19mm TYPE EXTERIEUR RECOUVERTE DU SYSTÈME DE MEMBRANE ELASTOMÈRE. DIMENSIONS TEL QUE L'EXISTANT. PRÉVOIR ÉGALEMENT DE MODIFIER L'OUVERTURE DANS LE PONTAGE DE BOIS LORSQUE INSTALLÉ DANS UNE OUVERTURE EXISTANTE, VOIR DÉTAIL 2 SUR LA FEUILLE 305.
- 32) ZONE DE RECONSTRUCTION DE TOITURE. CHEVAUCHER LA NOUVELLE MEMBRANE DE FINITION DE 300mm SUR CELLE EXISTANTE. DÉGRANULER LA MEMBRANE EXISTANTE AU PRÉALABLE.
- 33) NOUVEL ESCALIER. VOIR DÉTAILS DE LA SÉRIE DE FEUILLES 700.

- NOTES
- 19) NOUVEAU PARAPET, VOIR DÉTAILS DE LA SÉRIE DE FEUILLES 400.
- 20) BASE MEMBRANÉE EN TOITURE EXISTANTE POUR SORTIE DE CONDUITS.
- 21) BASE MEMBRANÉE EN TOITURE EXISTANTE.
- 22) TRAPPE D'ACCÈS AU TOIT EXISTANTE.
- 23) COL DE CYGNE EXISTANT, VOIR DOCUMENTS D'INGÉNÉRIE.
- 24) OUVERTURE EXISTANTE À OBTURER, VOIR DÉTAIL #2 DE LA SÉRIE DE FEUILLES 500.
- 25) GARGOUILLE EXISTANTE À NETTOYER.
- 26) MURET PARAPET EXISTANT À CONSERVER.
- 27) NOUVEAU MURET PARAPET À CONSTRUIRE TEL QUE L'EXISTANT.

- NOTES
- 1) APPAREIL D'ÉLECTRO-MÉCANIQUE ET SUPPORT EXISTANT, VOIR DOCUMENTS D'INGÉNÉRIE. PRÉVOIR UN FOND DE VISSAGE EN ACIER GALVANISÉ 1,6mm D'ÉPAISSEUR DE DIMENSIONS REQUISES DERRIÈRE LE REVÊTEMENT.
- 2) CONDUIT EXISTANT, VOIR DOCUMENTS D'INGÉNÉRIE.
- 3) PERSIENNE DE VENTILATION EXISTANTE RÉINSTALLÉE, VOIR DOCUMENTS D'INGÉNÉRIE. LA PERSIENNE DOIT ÊTRE REPEINT, AVANT SON INSTALLATION, DE LA MEME COULEUR QUE LE REVÊTEMENT DANS LEQUEL ELLE SÉRA INSTALLÉE, VOIR ÉLEVATIONS POUR LE TYPE DE REVÊTEMENT DANS LEQUEL ELLE SÉRA INSTALLÉE.
- 4) GARDE-CORPS EXISTANT, À RÉINSTALLER. VOIR LES MODIFICATIONS PRÉVUES SUR LES FEUILLES DE LA SÉRIE 700.
- 5) ÉCHELLE EXISTANTE À RÉINSTALLÉE. VOIR LES MODIFICATIONS PRÉVUS SUR LES FEUILLES DE LA SÉRIE 700.
- 6) COUSSIN GONFLABLE D'ÉTANCHÉITÉ POUR QUAI D'EMBARQUEMENT EXISTANT À RÉINSTALLER. PRÉVOIR FOND DE VISSAGE DE DIMENSIONS REQUISES, VOIR DÉTAIL #6 DE LA SÉRIE 600.
- 7) SORTIE OU ENTRÉE DE VENTILATION EXISTANTE, VOIR DOCUMENTS D'INGÉNÉRIE.
- 8) ESCALIER EN ACIER EXISTANT À RÉINSTALLER SUR UN TAPIS DE CAOUTCHOUC. FIXER MÉCANIQUEMENT L'ESCALIER AUX BARRES EN «Z» DU MUR À TRAVERS LE REVÊTEMENT.
- 9) SECTION DE GARDE-CORPS EXISTANTE, MODIFIÉE ET RÉINSTALLÉE. VOIR SÉRIE 700 POUR LES INTERVENTIONS SUR LE GARDE-CORPS.
- 10) CONDUIT DE VENTILATION EXISTANT, VOIR DOCUMENTS D'INGÉNÉRIE.
- 11) PLATEFORME ET GARDE-CORPS EN ACIER EXISTANT À RÉINSTALLER.
- 12) ZONE DE RECONSTRUCTION DE TOITURE, SUITE AUX TRAVAUX STRUCTURAUX, VOIR DÉTAILS DE LA SÉRIE DE FEUILLES 400. CHEVAUCHER LA NOUVELLE MEMBRANE DE FINITION DE 305mm SUR CELLE EXISTANTE. DÉGRANULER LA MEMBRANE EXISTANTE AU PRÉALABLE.
- 13) PROFIL DU PORTE-A-FEAUX EXISTANT AU-DESSUS.
- 14) PROFIL DU DÉBORD DE TOIT EXISTANT AU-DESSUS.
- 15) ÉVENT EXISTANT, VOIR DOCUMENTS D'INGÉNÉRIE.
- 16) AÉRATEUR D'ENTRETOIT EXISTANT.
- 17) TRAPPE D'ACCÈS À L'ENTRETOIT EXISTANTE À CONSERVER.
- 18) DRAIN DE TOITURE EXISTANT, VOIR DOCUMENTS D'INGÉNÉRIE.

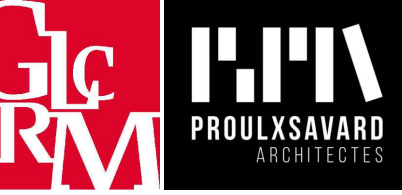


GLCRM | Proulx Savard |

GLCRM:
138 Avenue de la Cathédrale,
Bureau 201
Rimouski, QC, G5L 5H7
(418) 722-7655

2406, Ch. des Quatres-Bourgeois,
Bureau 100
Québec, QC G1V 1W5
(418) 647-1700

Proulx Savard Architectes:
75, boul. Arthur-Buies Ouest,
Rimouski, QC G5L 5C2
(418) 723-5543

ARCHITECTURE

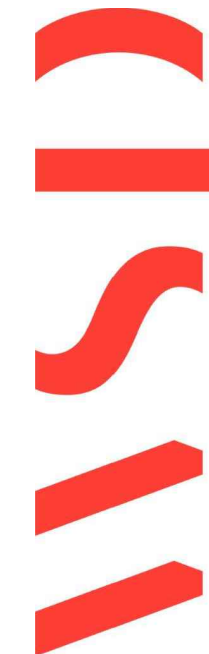

CONSULTANTS



DOSSIER No.	DESIGNATEUR (S)	DATE	DATE	RÉVISIONS
24-1087 / 687-24	D.B. A.C.	SEPTEMBRE 2024		
PROJET HÔPITAL DE CHANDLER, Chandler (Redaction de l'enveloppe)	ÉCHELLE INDIQUÉE	05	2024-09-04	DÉFINITIVES POUR SOUMISSION
		06	2024-08-21	DÉFINITIVES 100% POUR APPROBATION
		03	2024-08-03	DÉFINITIVES 80% POUR APPROBATION
		02	2024-05-14	DÉFINITIVES 40% POUR APPROBATION
PROPRIÉTAIRE Santé Québec		01	2024-02-27	PRÉLIMINAIRES 20% POUR APPROBATION
		No		


NE DOIT PAS SERVIR À L'EXÉCUTION

Le présent document est émis pour la seule fin identifiée. Son contenu est protégé par les droits d'auteur et toute reproduction ou modification, partielle ou totale, est interdite sans l'autorisation écrite de gagnon, letellier, cyr, ricard, mathieu, proulx, savard consortium d'architectes.

104

LISTE DES LOCAUX

301	CHAMBRE 2 LITS
302	CHAMBRE 2 LITS
303	CHAMBRE 2 LITS
304	CHAMBRE 2 LITS
305	CHAMBRE 2 LITS
306	CHAMBRE 1 LIT
307	CHAMBRE À PRESSION NÉGATIVE
308	CHAMBRE 2 LITS
309	CHAMBRE 1 LIT
310	CHAMBRE 2 LITS
311	CHAMBRE 2 LITS
315	CHAMBRE 1 LIT
316	CHAMBRE 1 LIT
317	CHAMBRE 1 LIT
318	CHAMBRE 1 LIT
319	CHAMBRE 1 LIT
320	BAIN ADAPTE
321	BUREAU
322	CHAMBRE 1 LIT
323	CHAMBRE 1 LIT
324	CHAMBRE 1 LIT
325	CHAMBRE D'ISOLEMENT
326	CHAMBRE 2 LITS
321A	TOILETTE
331	SALON GÉR.
331-A	BUREAU
332	SOINS INTENSIFS
332-A	CHAMBRE
332-B	CHAMBRE
332-C	CHAMBRE
332-D	RÉSERVE
332-D1	TOILETTE
332-H	CHAMBRE
337	SÉJOUR PSYCHIATRIE
338	DÉPÔT
339	DÉPÔT

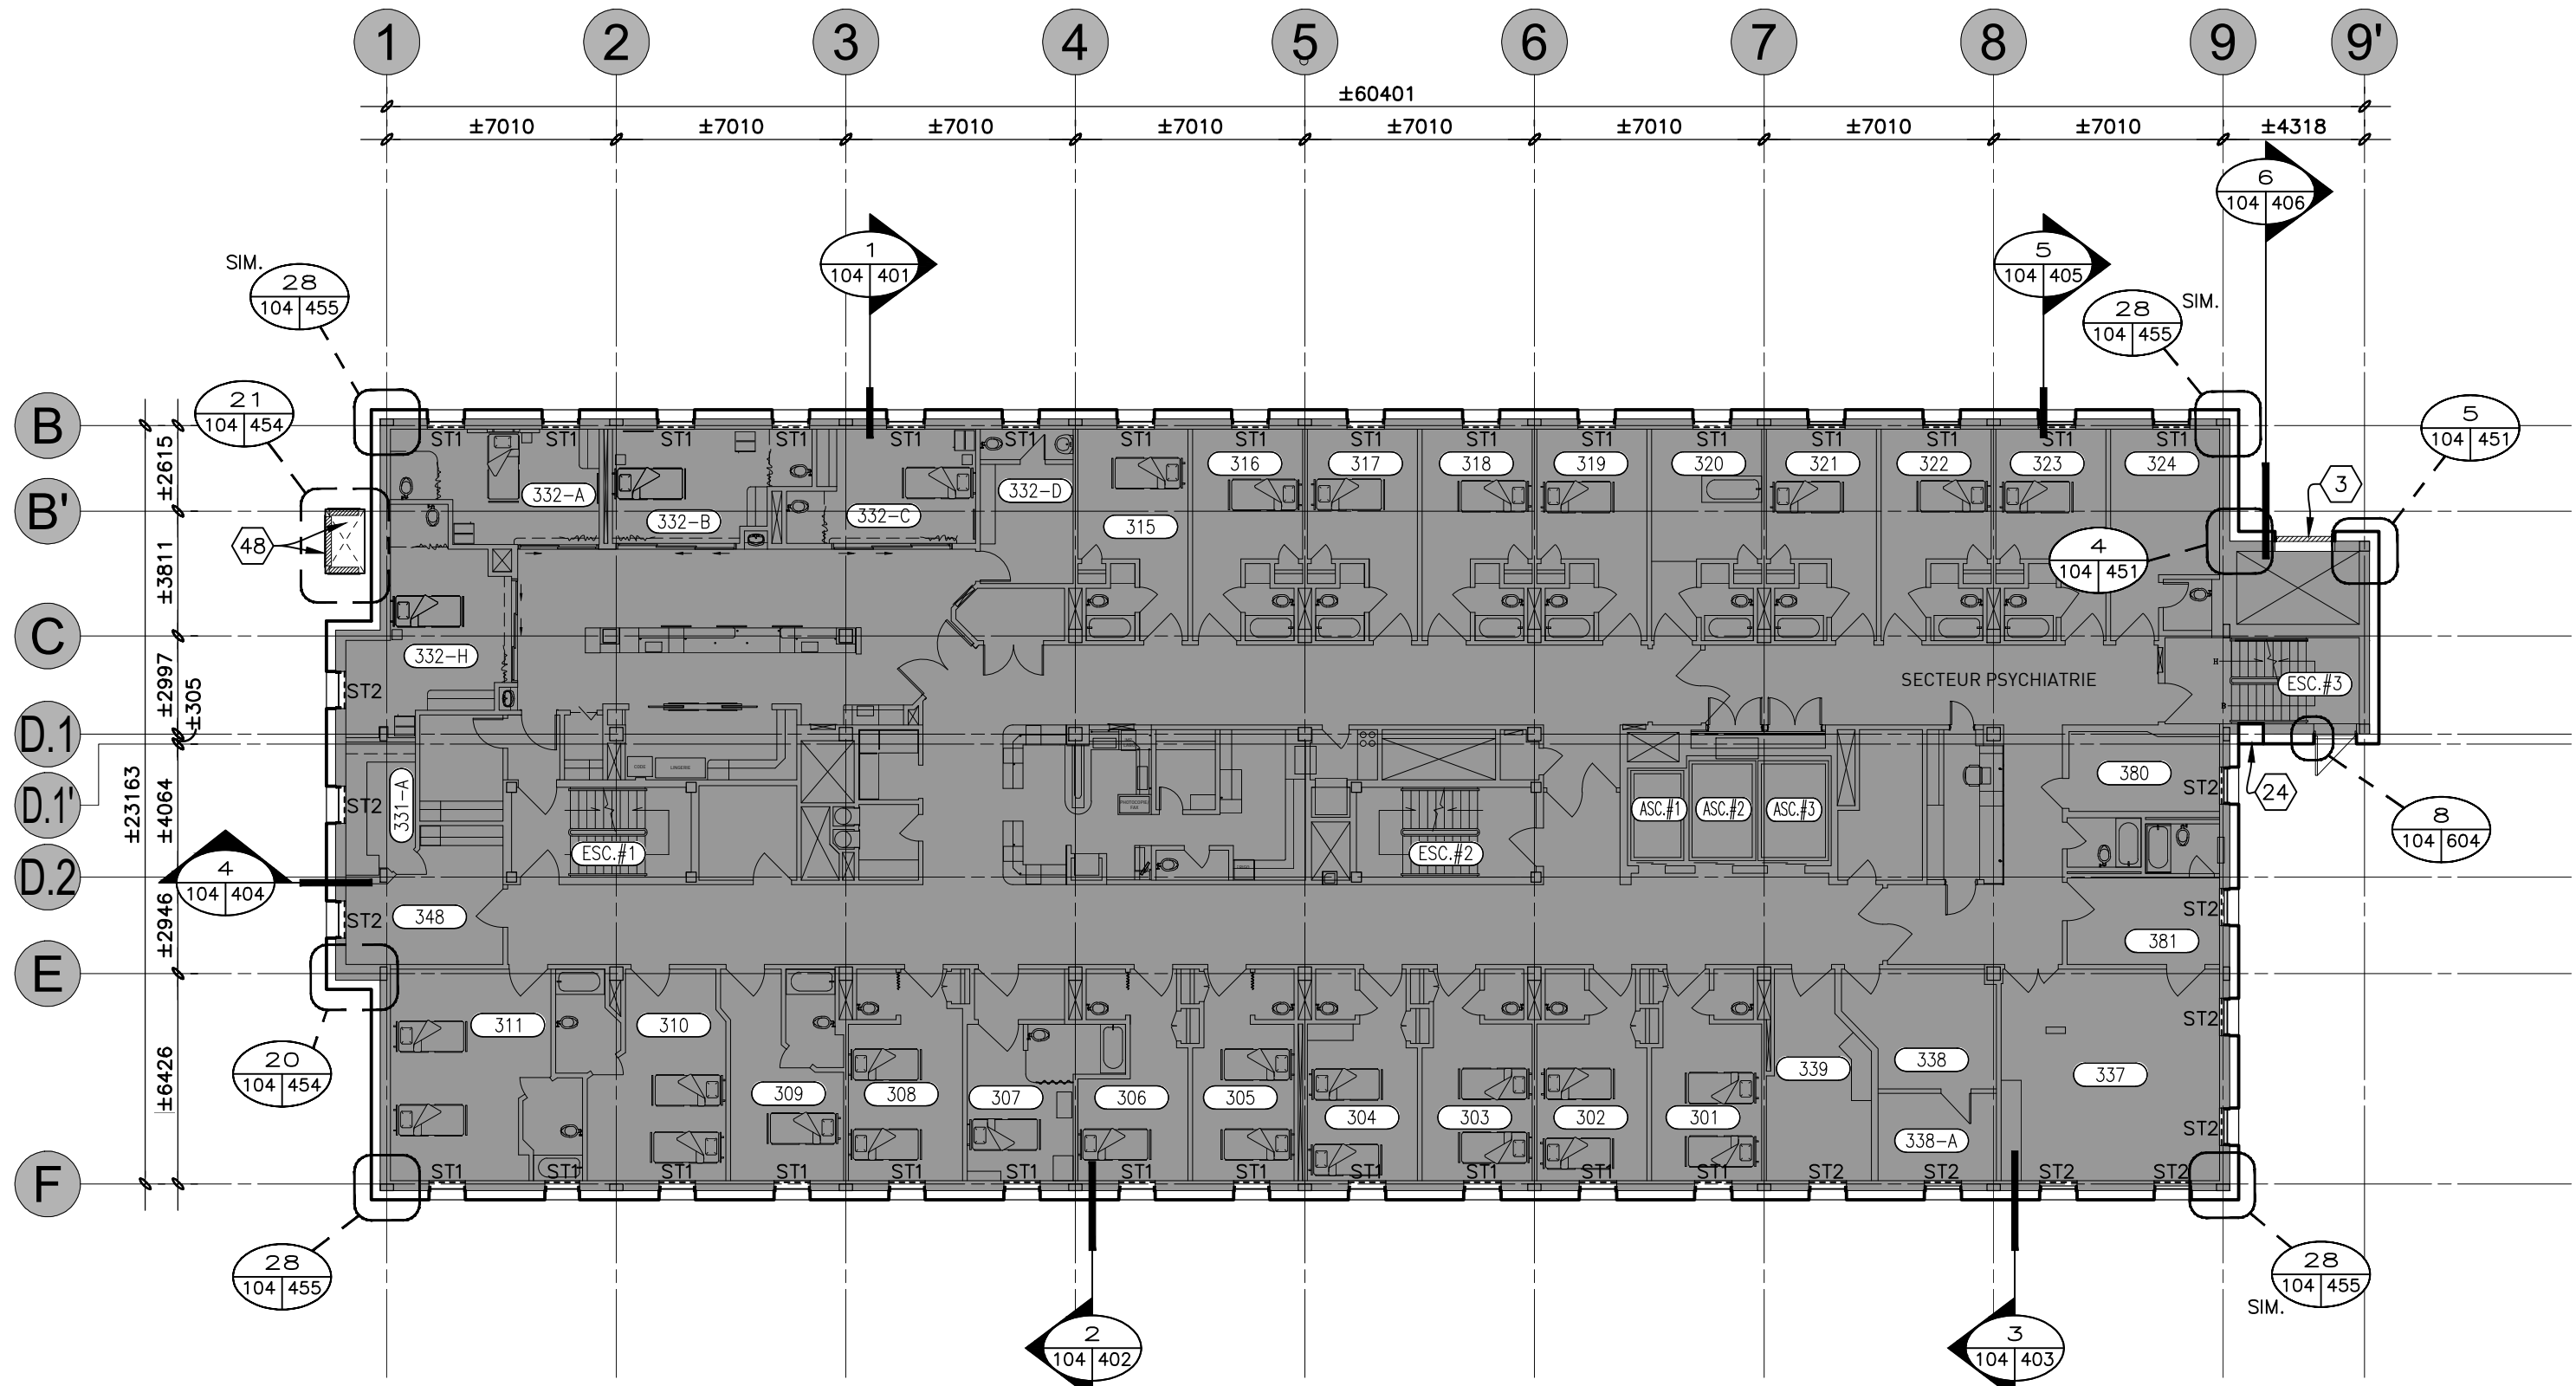


PLAN DU NIVEAU 300 - CONSTRUCTION

1:200mm






LISTE DES LOCAUX

401	CHAMBRE 2 LITS
402	CHAMBRE 2 LITS
403	CHAMBRE 2 LITS
404	CHAMBRE 2 LITS
405	CHAMBRE 2 LITS
406	CHAMBRE 2 LITS
407	CHAMBRE 2 LITS
408	CHAMBRE 2 LITS
409	CHAMBRE 2 LITS
410a	SOINS PAL.
410b	SOINS PAL.
411	CHAMBRE 2 LITS
412	CHAMBRE 2 LITS
414	CHAMBRE 1 LIT
415	CHAMBRE 1 LIT
416	CHAMBRE 1 LIT
417	CHAMBRE 1 LIT
418	CHAMBRE 2 LITS
419	CHAMBRE 2 LITS
420	CHAMBRE 2 LITS
421	CHAMBRE 2 LITS
422	CHAMBRE 2 LITS
423	CHAMBRE 1 LIT
423-A	CHAMBRE 1 LIT
431	FUMOIR
432	SALON FAMILLE
434	SALLE COMMUNAUTAIRE
436	BUREAU
437	SAS
438	CHAMBRE 2 LITS
439	SALLE COMMUNAUTAIRE
439-A	CUISINE COMMUNE

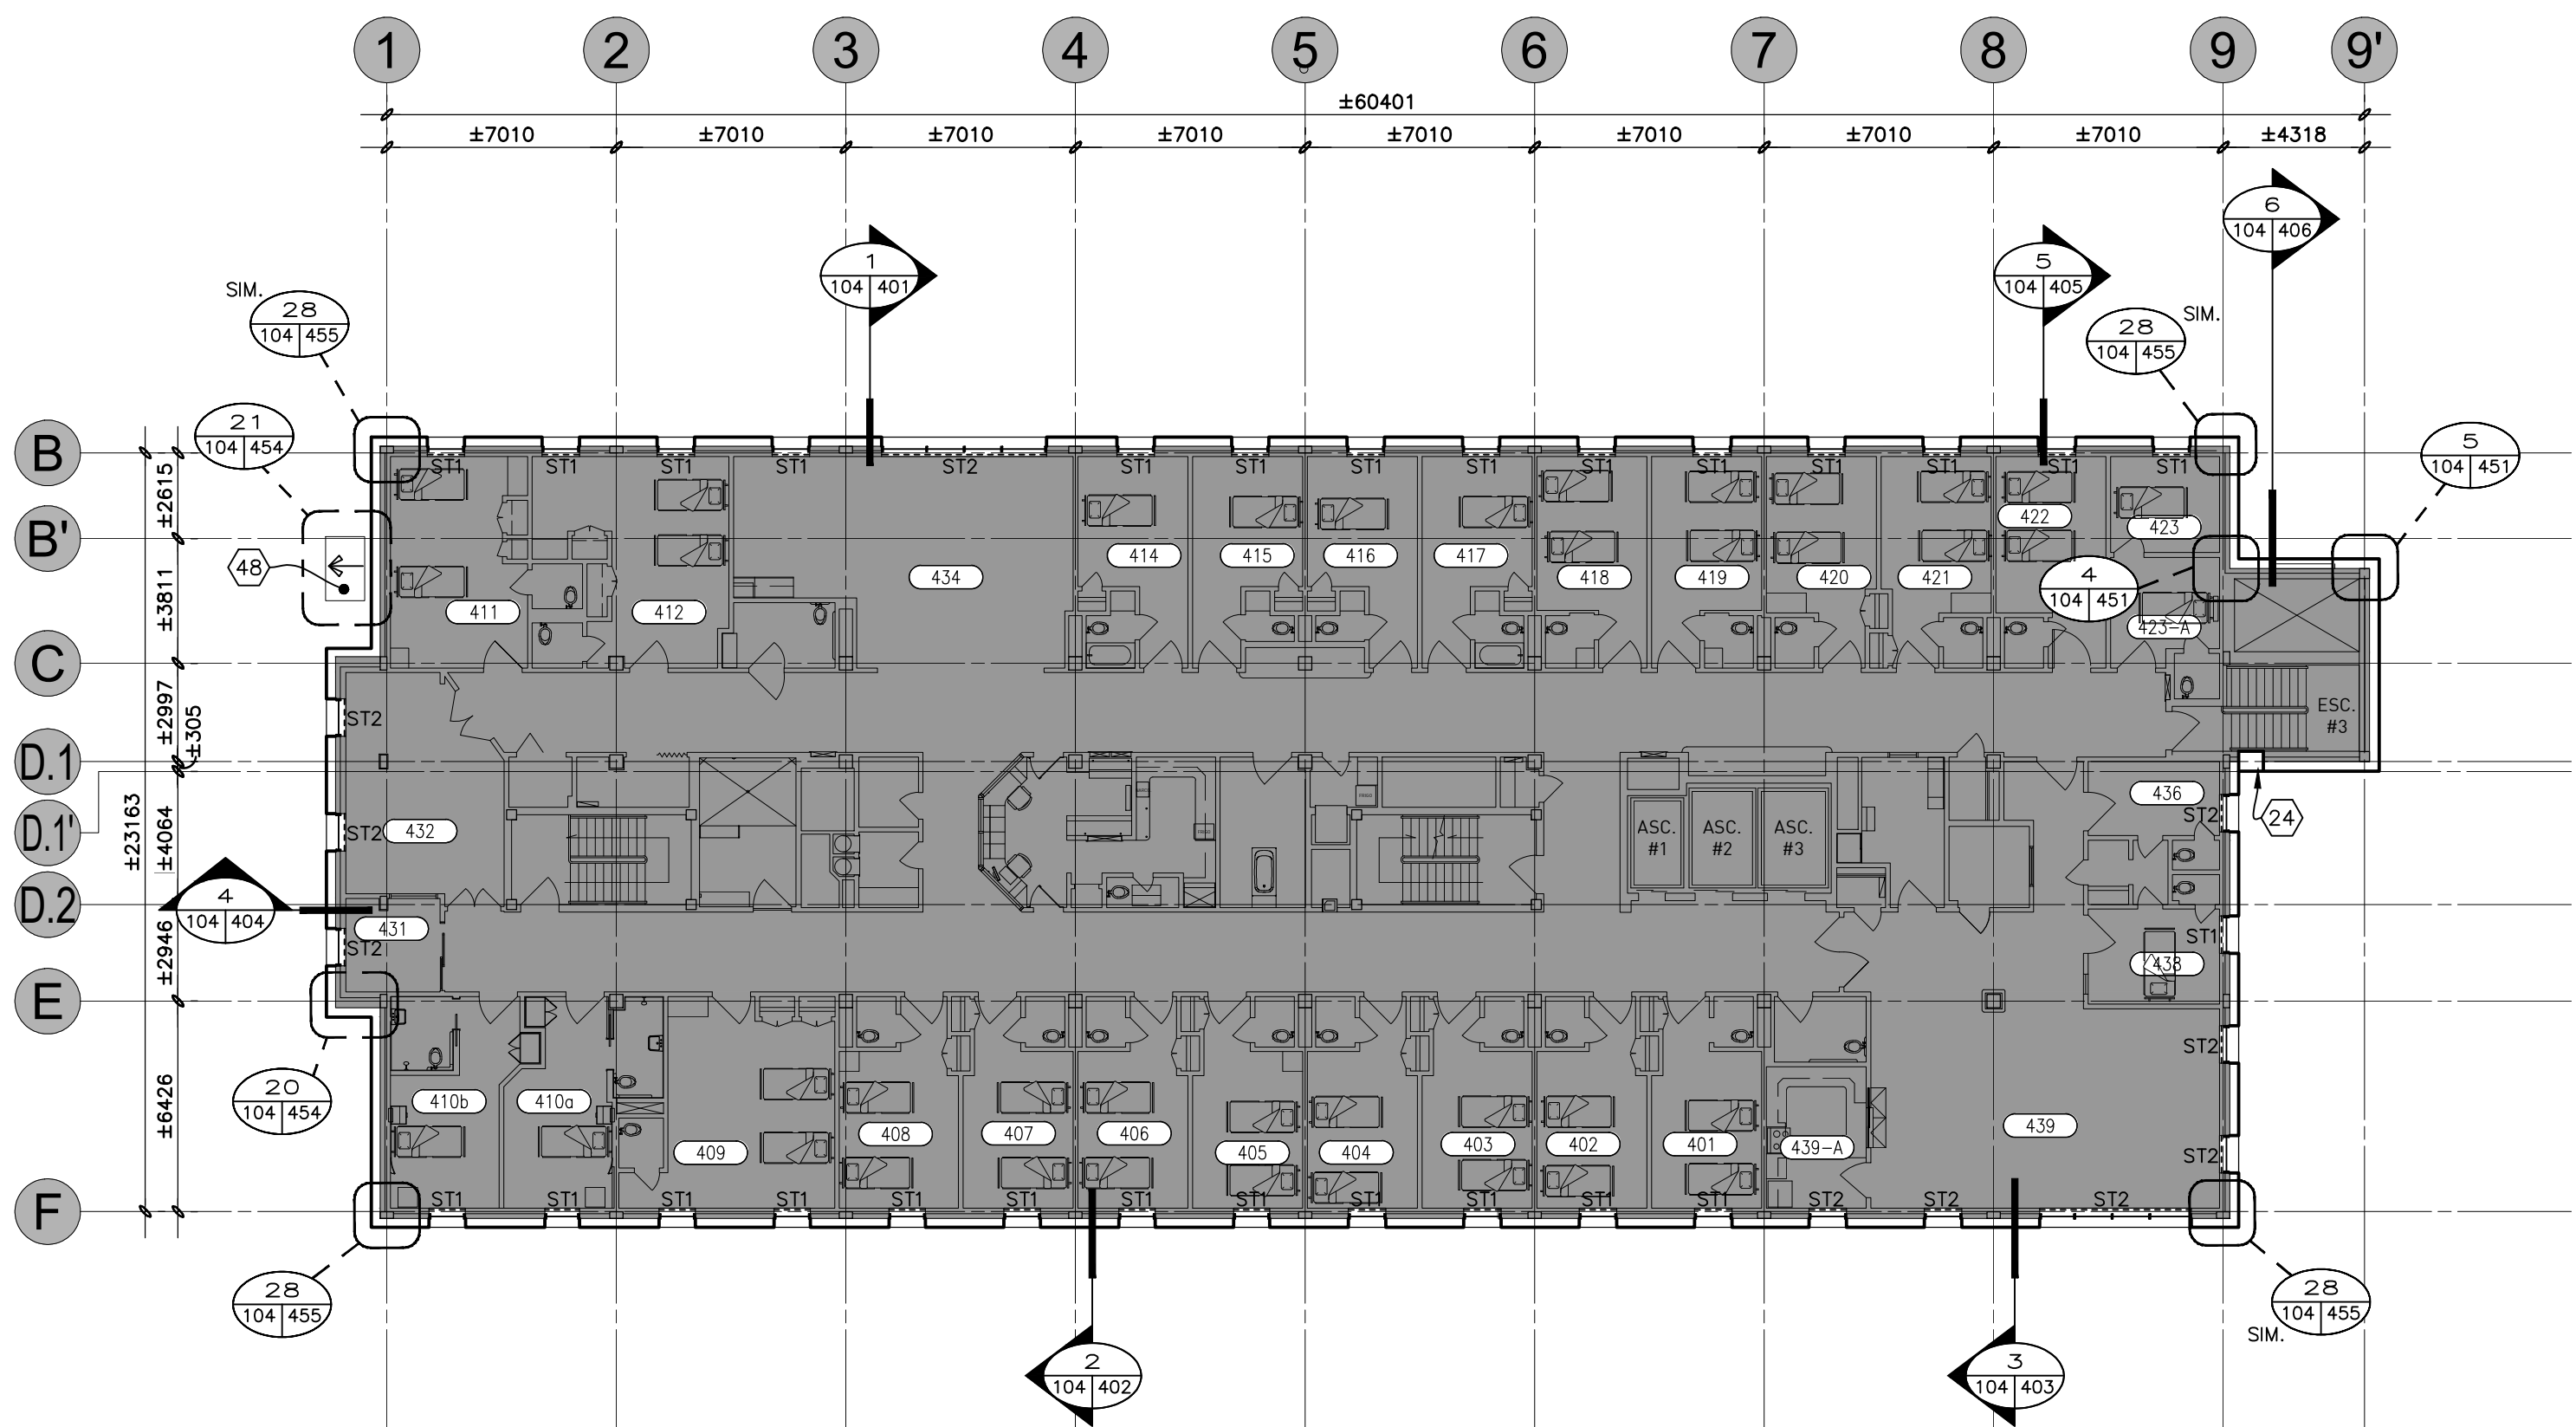

PLAN DU NIVEAU 400 - CONSTRUCTION

1:200mm

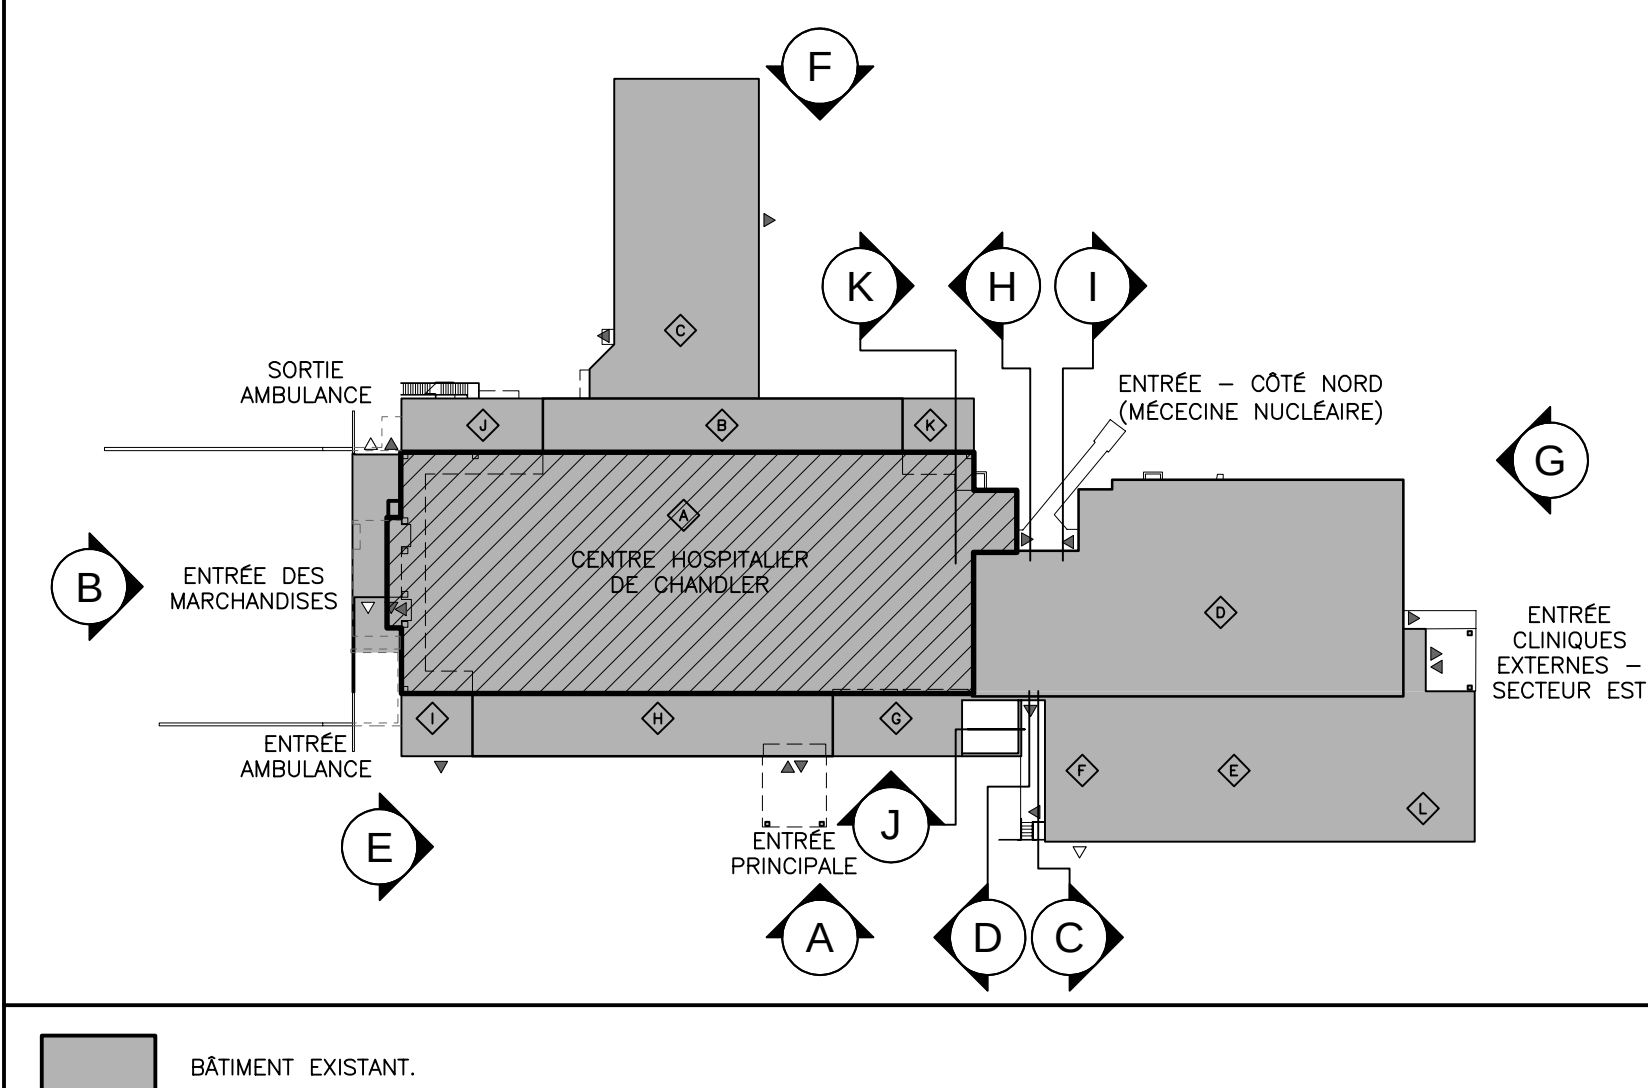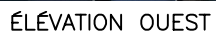
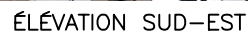
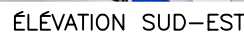
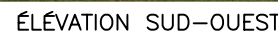


41 ZONE DE DÉMOLITION DE LA MAÇONNERIE ±3 BRIQUES DE HAUT SUR ±3 BRIQUES DE LARGEUR POUR PERMETTRE LES TRAVAUX DE STRUCTURE.

- 1 TOILE AMOVIBLE EXISTANTE A DEMONTER ET ENTREPOSER POUR REINSTALLATION FUTURE.
- 2 APPAREIL D'ELECTRO-MECANIQUE ET SUPPORT EXISTANT, VOIR DOCUMENTS D'INGENIERIE.
- 3 LUMINAIRE EXISTANT, VOIR DOCUMENTS D'INGENIERIE.
- 4 CONDUIT EXISTANT, VOIR DOCUMENTS D'INGENIERIE.
- 5 PERSIENNE A DEMENTELER ET ENTREPOSER PENDANT LES TRAVAUX POUR REINSTALLATION FUTURE, VOIR DOCUMENTS D'INGENIERIE.
- 6 GARDE-CORPS EXISTANT A DEMONTER ET ENTREPOSER POUR REINSTALLATION FUTURE, VOIR LES MODIFICATIONS PREVUES SUR LES FEUILLES DE LA SERIE 700.
- 7 LECTEUR DE CARTE/PUCE EXISTANT A ENLEVER, VOIR INGENIEUR.
- 8 PRISE ELECTRIQUE EXISTANTE, VOIR DOCUMENTS D'INGENIERIE.
- 9 ECHELLE EXISTANTE A DEMONTER ET ENTREPOSER POUR REINSTALLATION FUTURE, VOIR LA SERIE DE FEUILLES 700 POUR LES INTERVENTIONS A FAIRE SUR LES ECHELLES AVANT LEUR REINSTALLATION.
- 10 CAMERA EXISTANTE A DEMONTER ET ENTREPOSER POUR REINSTALLATION FUTURE, VOIR DOCUMENTS D'INGENIERIE.
- 11 AFFICHAGE EXISTANT A RETIRER ET ENTREPOSER POUR REINSTALLATION FUTURE.
- 12 COUSSIN GONFLABLE D'ETANCHEITE POUR QUAU D'EMBARQUEMENT A DEMONTER ET ENTREPOSER POUR REINSTALLATION FUTURE.
- 13 MAT DE DRAPEAU EN ENLEVER INCLUANT SON ANCRAGE ET A REMETTRE A L'ETABLISSEMENT/PROPRIETAIRE.
- 14 LETRAGE RETROECLAIRE A DEMONTER ET ENTREPOSER POUR REINSTALLATION FUTURE, VOIR DOCUMENTS D'INGENIERIE POUR LE RACCORDEMENT ELECTRIQUE. PRENDRE LES MESURES DES ESPACEMENTS DES LETTRES AVANT DE LES DEMONTER AFIN DE POUVOIR LES REINSTALLER A LA MEME FACON.
- 15 GRILLE DE VENTILATION EXISTANTE POUR L'ESCALIER, A DEMONTER ET ENTREPOSER POUR REINSTALLATION FUTURE.
- 16 PARATONNERRE ET CABLAGE DE MISE A LA TERRE EXISTANT A DEMOLIR, VOIR DOCUMENTS D'INGENIERIE.
- 17 ESCALIER EN ALUMINIUM EXISTANT A RETIRER ET ENTREPOSER POUR REINSTALLATION FUTURE.
- 18 AERATEUR POUR PAREMENT DE MAÇONNERIE EXISTANT A DEMOLIR.
- 19 SECTION DE GARDE-CORPS A COUPER, VOIR LES INTERVENTION SUR LES FEUILLES DE LA SERIE 700.
- 20 FILET EXISTANT A CONSERVER.
- 21 APPAREIL DE COMMUNICATION EXISTANT, VOIR DOCUMENTS D'INGENIERIE.
- 22 BOITE DE JONCTION ET FILAGE EXISTANT, VOIR DOCUMENTS D'INGENIERIE.
- 23 GARGOUILLE EXISTANTE A DEMOLIR, VOIR DETAIL #1 SUR LA FEUILLE 306.
- 24 CONDUIT DE VENTILATION EXISTANT A DEMOLIR, VOIR DOCUMENTS D'INGENIERIE.
- 25 PLATEFORME ET GARDE-CORPS EN ACIER EXISTANT A DEMONTER ET ENTREPOSER POUR REINSTALLATION FUTURE.
- 26 SORTIE D'ARROSAGE EXTERIEUR EXISTANTE, VOIR DOCUMENTS D'INGENIERIE.
- 27 DETECTEUR DE PRESENCE EXISTANT A DEMONTER ET ENTREPOSER POUR REINSTALLATION FUTURE, VOIR DOCUMENTS D'INGENIERIE.
- 28 GARDE-CORPS EXISTANT A CONSERVER EN PLACE ET A PROTEGER PENDANT LES TRAVAUX.
- 29 COMPOSITION ISOLEE SUR LA COLONNE EXISTANTE A DEMOLIR, VOIR LE DETAIL #52 DE LA PAGE 420 ET LE DETAIL #25 DE LA PAGE 455.
- 30 TRAPPE D'ACCES MURALE EXISTANTE A CONSERVER.
- 31 PERSIENNE EXISTANTE A DEMOLIR, VOIR DOCUMENTS D'INGENIERIE.
- 32 PAREMENT DE MAÇONNERIE EXISTANT A ENLEVER TEMPORAIREMENT ET ENTREPOSER POUR REINSTALLATION FUTURE.
- 33 SECTION DE MUR A DEMOLIR A PARTIR DU DESSOUS DE LA FENETRE EXISTANTE JUSQU'AU PLANCHER. SE REFERER A LA VUE EN PLAN ET AU DETAIL EN PLAN DE LA SERIE DE FEUILLES 600 POUR LA LARGEUR DE LA NOUVELLE OUVERTURE.
- 34 PAREMENT DE TOILE EXISTANT A DEMOLIR.
- 35 ESCALIER EXISTANT A DEMOLIR.
- 36 SUPPORTS DE L'ESCALIER A DEMONTER SOIGNEUSEMENT DE LA FACADE DE BRIQUE AFIN D'EVITER D'ABIMER LA BRIQUE EXISTANTE A CONSERVER, FAIRE TOUTES LES REPARATIONS REQUISE AU PAREMENT DE BRIQUE SUITE AU RETRAIT DES SUPPORTS.
- 37 CLAPET (EVENT) EXISTANT A DEMOLIR, VOIR DOCUMENTS D'INGENIERIE.
- 38 PERSIENNE EXISTANTE A DEMOLIR, VOIR DOCUMENTS D'INGENIERIE, VOIR DETAIL SIMILAIRE #2 DE LA FEUILLE 302.
- 39 GARDE-CORPS EXISTANT A DEMOLIR.
- 40 PORTE ET CADRE EXISTANTS A DEMOLIR.

	PAREMENT EXISTANT À DÉMOLIR.
	PAREMENT DE TÔLE EXISTANT À DÉMOLIR.
	PAREMENT DE BRIQUE EXISTANT À DÉMOLIR.
	PAREMENT DE BRIQUE EXISTANT À CONSERVER.
	EXISTANT À CONSERVER.


Le présent document est émis pour la seule fin identifiée. Son contenu est protégé par les droits d'auteur et toute reproduction ou modification, partielle ou totale, est interdite sans l'autorisation écrite de gagnon, letellier, cyr, ricard, mathieu, proulx, savard consortium d'architectes.

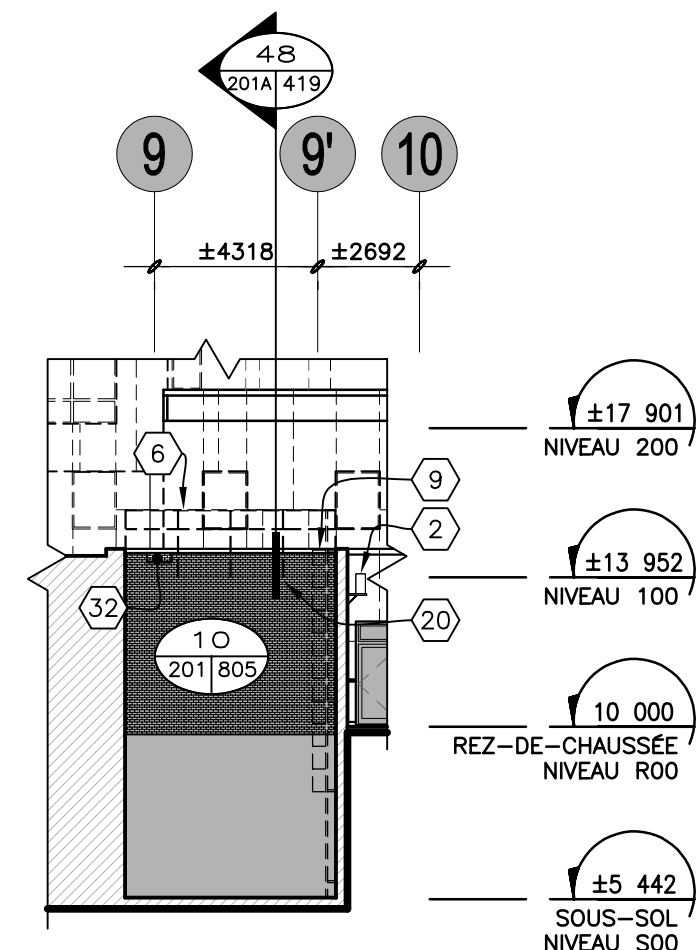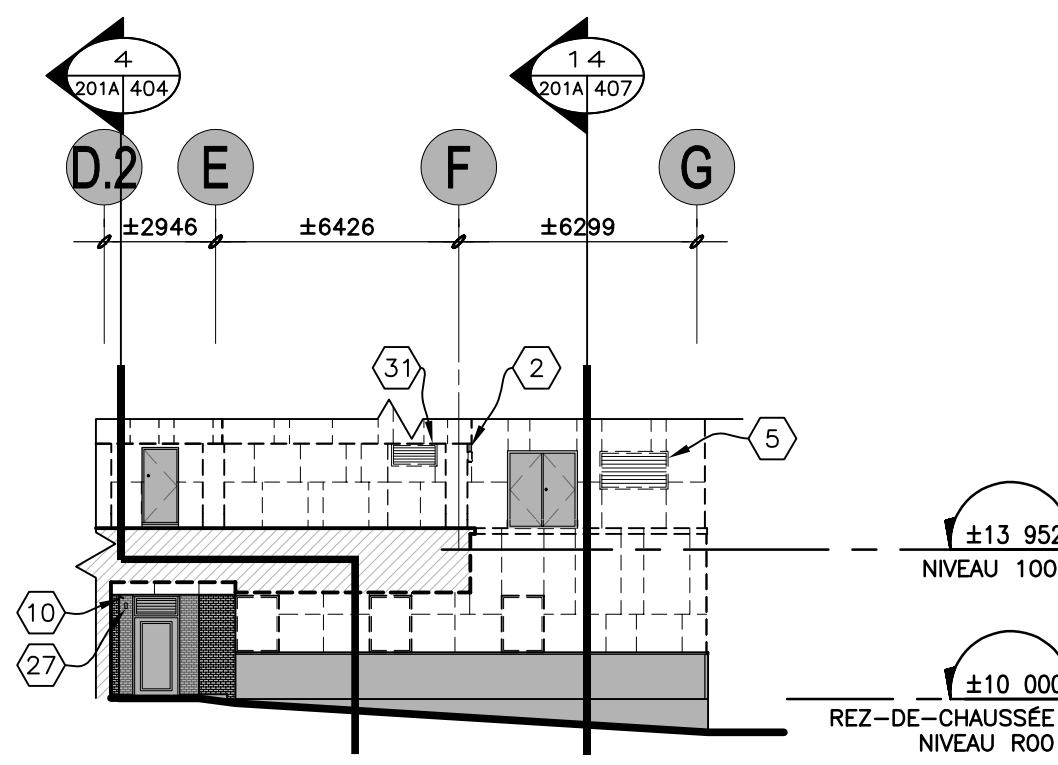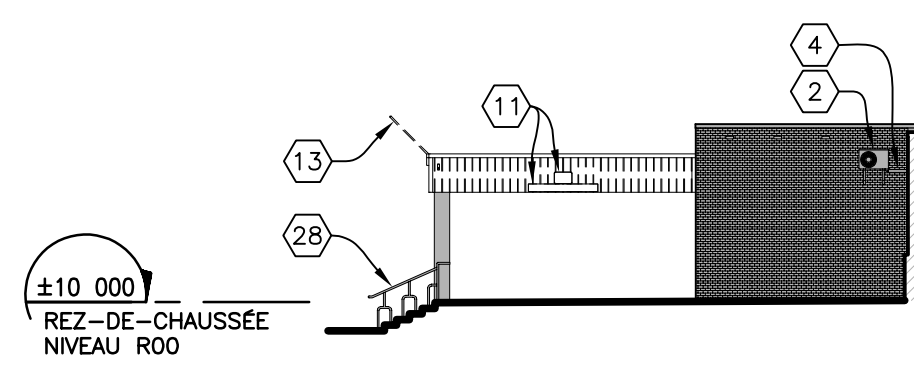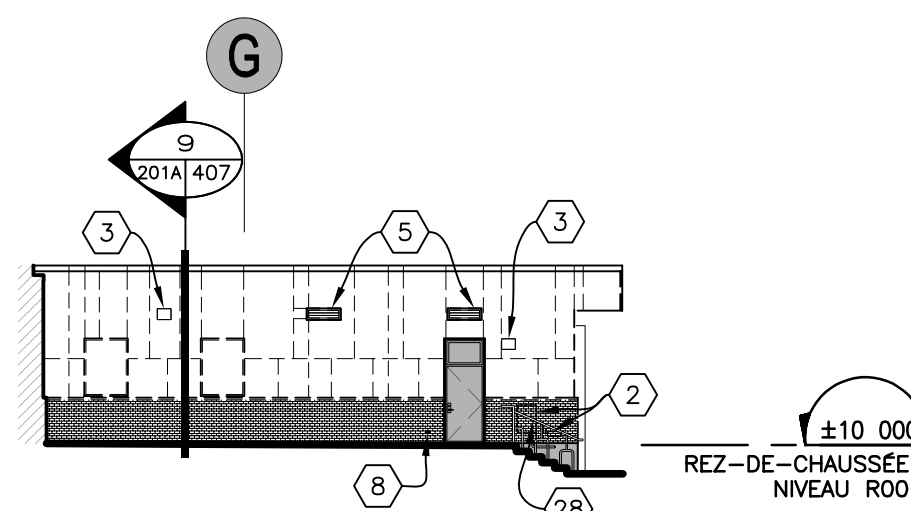

NOTES

- 41 ZONE DE DÉMOLITION DE LA MAÇONNERIE ±3 BRIQUES DE HAUT SUR ±3 BRIQUES DE LARGEUR POUR PERMETTRE LES TRAVAUX DE STRUCTURE.

LÉGENDE

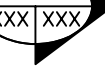- | | |
|---|-----------------------|
|  | NOTE DESCRIPTIVE. |
|  | NIVEAU. |
|  | COUPE DE MUR. |
|  | DÉTAIL TYPE. |
|  | AXE. EXISTANT. |
|  | NOUVEL AXE. |
|  | EXISTANT À CONSERVER. |
| ----- JOINT D'EXPANSION À CONSERVER | |

LÉGENDE DES ZONES

- | | |
|---|--|
| A | TOUR CHAMBRES (NIVEAU 200,300 ET 400)
(1974). |
| B | LABORATOIRE (NIVEAU 100)(1990). |
| C | ARCHIVES (REZ-DE-CHAUSSÉE)(2001). |
| D | ADMINISTRATIVE (NIVEAU 100) (2005) ET
CLINIQUE EXTERNES (REZ-DE-CHAUSSÉE)
(1974) |
| E | ONCOLOGIE (REZ-DE-CHAUSSÉE) (1974). |
| F | IRM (REZ-DE-CHAUSSÉE) (2007) |
| G | BASILAIRE SUD-EST(1974) |
| H | CLINIQUE CHIRURGIE D'UN JOUR
(NIVEAU 100) (2005)ET URGENCE
(REZ-DE-CHAUSSÉE) |
| I | BASILAIRE SUD-OUEST (1974) |
| J | BASILAIRE NORD-OUEST (1974) |
| K | BASILAIRE NORD-EST (1974) |
| L | ONCOLOGIE (REZ-DE-CHAUSSÉE) (2023) |

NOTES

- (1) TOILE AMOVIBLE EXISTANTE À DÉMONTÉR ET ENTREPOSER POUR REINSTALLATION FUTURE.
- (2) APPAREIL D'ÉLECTRO-MÉCANIQUE ET SUPPORT EXISTANT, VOIR DOCUMENTS D'INGÉNIERIE.
- (3) LUMINAIRE EXISTANT, VOIR DOCUMENTS D'INGÉNIERIE.
- (4) CONDUIT EXISTANT, VOIR DOCUMENTS D'INGÉNIERIE.
- (5) PERSIENNE À DÉMONTÉLER ET ENTREPOSER PENDANT LES TRAVAUX POUR REINSTALLATION FUTURE, VOIR DOCUMENTS D'INGÉNIERIE.
- (6) GARDE-CORPS EXISTANT À DÉMONTÉR ET ENTREPOSER POUR REINSTALLATION FUTURE, VOIR LES MODIFICATIONS PRÉVUES SUR LES FEUILLES DE LA SÉRIE 700.
- (7) LECTEUR DE CARTE/PUCE EXISTANT À ENLEVER. VOIR INGÉNIEUR.
- (8) PRISE ÉLECTRIQUE EXISTANTE, VOIR DOCUMENTS D'INGÉNIERIE.
- (9) ECHELLE EXISTANTE À DÉMONTÉR ET ENTREPOSER POUR REINSTALLATION FUTURE, VOIR LA SÉRIE DE FEUILLES 700 POUR LES INTERVENTIONS À FAIRE SUR LES ECHELLES AVANT LEUR REINSTALLATION.
- (10) CAMÉRA EXISTANTE À DÉMONTÉR ET ENTREPOSER POUR REINSTALLATION FUTURE, VOIR DOCUMENTS D'INGÉNIERIE.
- (11) AFFICHAGE EXISTANT À RETIRER ET ENTREPOSER POUR REINSTALLATION FUTURE.
- (12) COUSSIN GONFLABLE D'ÉTANCHÉITÉ POUR QUIA D'EMBARQUEMENT À DÉMONTÉR ET ENTREPOSER POUR REINSTALLATION FUTURE.
- (13) MAT DE DRAPEAU À ENLEVER INCLUANT SON ANCRAGE ET À REMETTRE À L'ÉTABLISSEMENT/PROPRIÉTAIRE.
- (14) LETRAGE RÉTROÉCLAIRÉ À DÉMONTÉR ET ENTREPOSER POUR REINSTALLATION FUTURE, VOIR DOCUMENTS D'INGÉNIERIE POUR LE RACCORDÉMENT ÉLECTRIQUE. PRENDRE LES MESURES DES ESPACEMENTS DES LETTRES AVANT DE LES DÉMONTÉLER AFIN DE POUVOIR LES REINSTALLER À LA MÊME FAÇON.
- (15) GRILLE DE VENTILATION EXISTANTE POUR L'ENTRÉE D'AIR À DÉMONTÉR ET ENTREPOSER POUR REINSTALLATION FUTURE.
- (16) PARATONNERRE ET CÂBLAGE DE MISE À LA TERRE EXISTANT À DÉMÔLER, VOIR DOCUMENTS D'INGÉNIERIE.
- (17) ESCALIER EN ALUMINIUM EXISTANT À RETIRER ET ENTREPOSER POUR REINSTALLATION FUTURE.
- (18) AÉRATEUR POUR PAREMENT DE MAÇONNERIE EXISTANT À DÉMÔLER.
- (19) SECTION DE GARDE-CORPS À COUPER, VOIR LES INTERVENTIONS SUR LES FEUILLES DE LA SÉRIE 700.
- (20) FILET EXISTANT À CONSERVER.
- (21) APPAREIL DE COMMUNICATION EXISTANT, VOIR DOCUMENTS D'INGÉNIERIE.
- (22) BOÎTE DE JONCTION ET FILAGE EXISTANT, VOIR DOCUMENTS D'INGÉNIERIE.
- (23) GARGOUILLE EXISTANTE À DÉMÔLER, VOIR DÉTAIL #1 SUR LA FEUILLE 306.
- (24) CONDUIT DE VENTILATION EXISTANT À DÉMÔLER, VOIR DOCUMENTS D'INGÉNIERIE.
- (25) PLATEFORME ET GARDE-CORPS EN ACIER EXISTANT À DÉMONTÉR ET ENTREPOSER POUR REINSTALLATION FUTURE.
- (26) SORTIE D'ARROSAGE EXTÉRIEUR EXISTANTE, VOIR DOCUMENTS D'INGÉNIERIE.
- (27) DÉTECTEUR DE PRÉSENCE EXISTANT À DÉMONTÉR ET ENTREPOSER POUR REINSTALLATION FUTURE, VOIR DOCUMENTS D'INGÉNIERIE.
- (28) GARDE-CORPS EXISTANT À CONSERVER EN PLACE ET À PROTÉGER PENDANT LES TRAVAUX.
- (29) COMPOSITION ISOLÉE SUR LA COLONNE EXISTANTE À DÉMÔLER, VOIR LE DÉTAIL #52 DE LA PAGE 420 ET LE DÉTAIL #25 DE LA PAGE 455.
- (30) TRAPPE D'ACCÈS MURALE EXISTANTE À CONSERVER.
- (31) PERSIENNE EXISTANTE À DÉMÔLER, VOIR DOCUMENTS D'INGÉNIERIE.
- (32) PAREMENT DE MAÇONNERIE EXISTANT À ENLEVER TEMPORAIREMENT ET ENTREPOSER POUR REINSTALLATION FUTURE.
- (33) SECTION DE MUR À DÉMÔLER À PARTIR DU DESSOUS DE LA FENÊTRE EXISTANTE JUSQU'AU PLANCHER. SE RÉFÉRER À LA VUE EN PLAN ET AU DÉTAIL EN PLAN DE LA SÉRIE DE FEUILLES 600 POUR LA LARGEUR DE LA NOUVELLE OUVERTURE.
- (34) PAREMENT DE TOILE EXISTANT À DÉMÔLER.
- (35) ESCALIER EXISTANT À DÉMÔLER.
- (36) SUPPORTS DE L'ESCALIER À DÉMONTÉR SOIGNEUSEMENT DE LA FASCE DE BROU ET À ÉVITER D'ARRACHER LA BRIQUE EXISTANTE À CONSERVER. FAIRE TOUTES LES RÉPARATIONS REQUISE AU PAREMENT DE BRIQUE SUITE AU RETRAIT DES SUPPORTS.
- (37) CLAPET (ÉVENT) EXISTANT À DÉMÔLER, VOIR DOCUMENTS D'INGÉNIERIE.
- (38) PERSIENNE EXISTANTE À DÉMÔLER, VOIR DOCUMENTS D'INGÉNIERIE, VOIR DÉTAIL SIMILAIRE #2 DE LA FEUILLE 306.
- (39) GARDE-CORPS EXISTANT À DÉMÔLER.
- (40) PORTE ET CADRE EXISTANTS À DÉMÔLER.

LÉGENDE DES
-PAREMENTS -
DÉMOLITION

- | | |
|---|--|
|  | PAREMENT EXISTANT À DÉMOLIR. |
|  | PAREMENT DE TÔLE EXISTANT À DÉMOLIR. |
|  | PAREMENT DE BRIQUE EXISTANT À DÉMOLIR. |
|  | PAREMENT DE BRIQUE EXISTANT À CONSERVER. |
|  | EXISTANT À CONSERVER. |

NE DOIT PAS SERVIR À L'EXÉCUTION

Le présent document est émis pour la seule fin identifiée. Son contenu est protégé par les droits d'auteur et toute reproduction ou modification, partielle ou totale, est interdite sans l'autorisation écrite de gagnon, letellier, cyr, ricard, mathieu, proulx, savard consortium d'architectes.




GLCRM | Proulx Savard

GLCRM:
128, Avenue de la Cathédrale,
Bureau 201
Rimouski, QC, G5L 5H7
(418) 722-7655



2406, Ch. des Quatres-Bourgeois,
Bureau 100
Québec, QC, G1V 1W5
(418) 647-1700

Proulx Savard Architectes:
75, boul. Arthur-Buies Ouest,
Rimouski QC G5L 5C2
(418) 723-5543

ARCHITECTURE

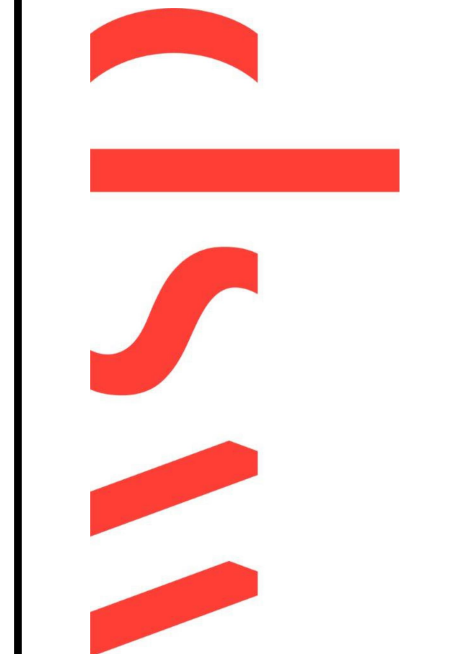

CONSULTANTS

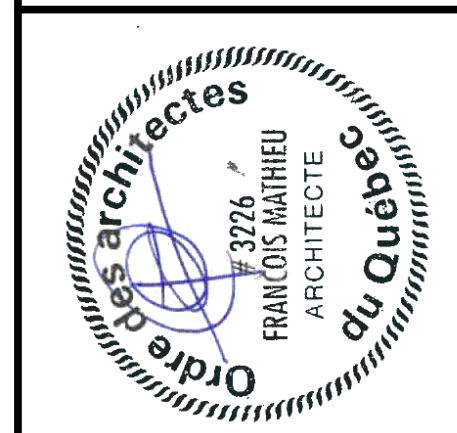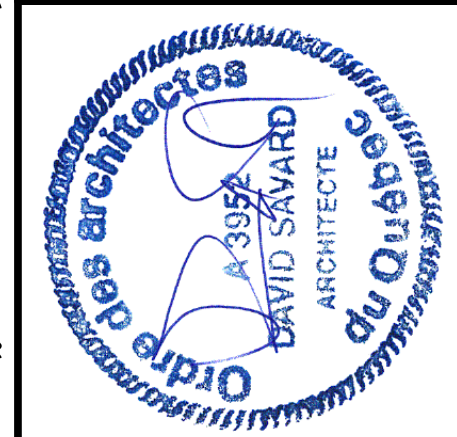

DESSINATEUR(S)	DOSSIER No.	
D.B., A.B., A.C., J.L.	24-108 / R657-24	
ECHELLE	DATE	
INNOUÉE	SEPTEMBRE 2026	
		DEFINITIFS POUR SOUMISSION
05	2024-09-04	DEFINITIFS 100% POUR APPROBATION
04	2024-08-21	DEFINITIFS 80% POUR APPROBATION
03	2024-08-03	DEFINITIFS 60% POUR APPROBATION
02	2024-05-14	DEFINITIFS 40% POUR APPROBATION
01	2024-02-27	PRELIMINAIRES 30% POUR APPROBATION
		REVISIONS
		DATE

PROJET	HÔPITAL DE CHANDLER, Chandler (Réfection de l'enveloppe)
PROPRIÉTAIRE	 Santé Québec



201-A



ELEVATION NORD




ELEVATION NORD



ELEVATION NORD PARTIELLE



ELEVATION EST

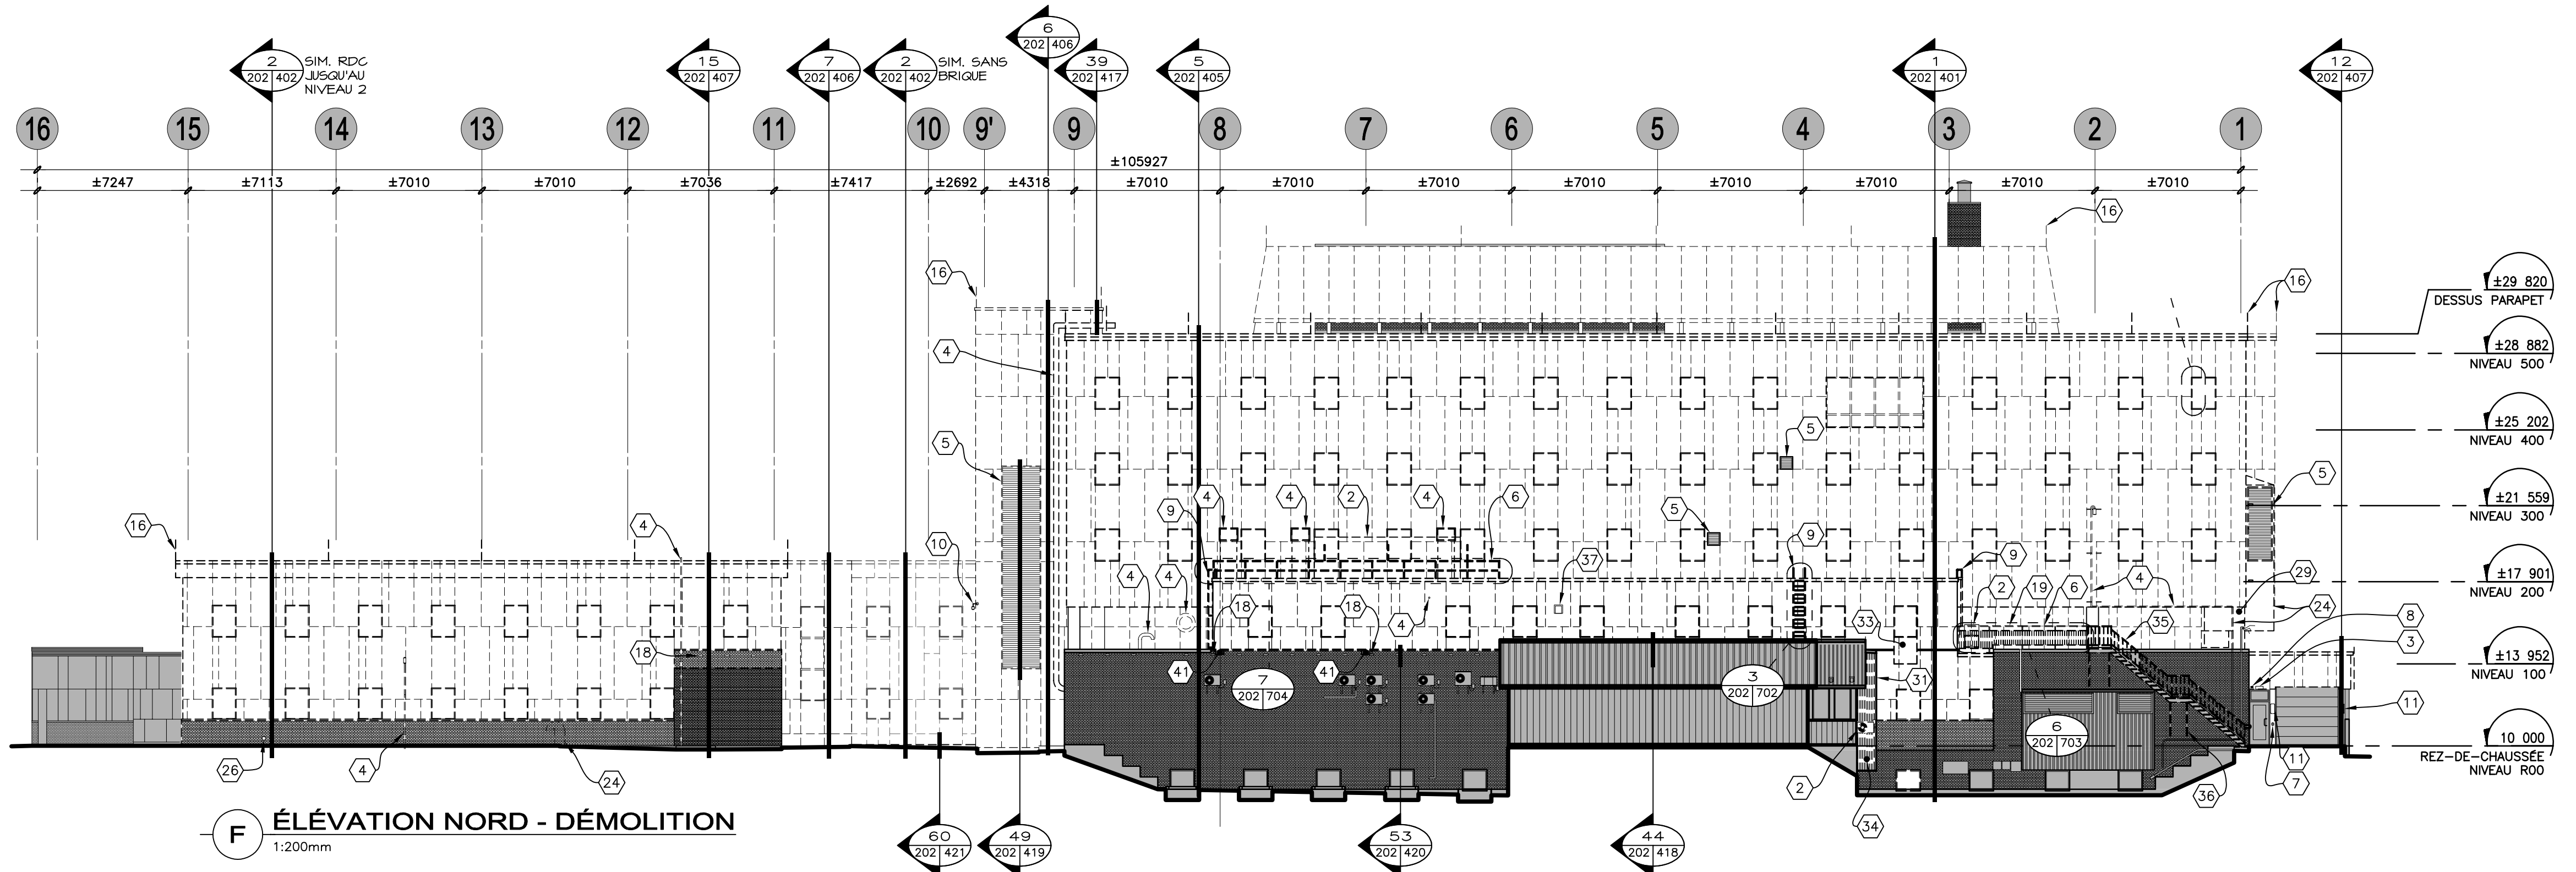

NOTES

- (41) ZONE DE DÉMOLITION DE LA MAÇONNERIE ±3 BRIQUES DE HAUT SUR ±3 BRIQUES DE LARGEUR POUR PERMETTRE LES TRAVAUX DE STRUCTURE.

NOTES

- 1 TOILE AMOVIBLE EXISTANTE À DÉMONTER ET ENTREPOSER POUR RÉINSTALLATION FUTURE.
- 2 APPAREIL D'ÉLECTRO-MÉCANIQUE ET SUPPORT EXISTANT, VOIR DOCUMENTS D'INGÉNÉRIE.
- 3 LUMINAIRE EXISTANT, VOIR DOCUMENTS D'INGÉNÉRIE.
- 4 CONDUIT EXISTANT, VOIR DOCUMENTS D'INGÉNÉRIE.
- 5 PERSIENNE À DÉMONTÉLER ET ENTREPOSER PENDANT LES TRAVAUX POUR RÉINSTALLATION FUTURE, VOIR DOCUMENTS D'INGÉNÉRIE.
- 6 GARDE-CORPS EXISTANT À DÉMONTER ET ENTREPOSER POUR RÉINSTALLATION FUTURE, VOIR LES MODIFICATIONS PRÉVUES SUR LES FEUILLES DE LA SÉRIE 700.
- 7 LECTEUR DE CARTE/PUCE EXISTANT À ENLEVER, VOIR INGÉNIEUR.
- 8 PRISE ÉLECTRIQUE EXISTANTE, VOIR DOCUMENTS D'INGÉNÉRIE.
- 9 ÉCHELLE EXISTANTE À DÉMONTER ET ENTREPOSER POUR RÉINSTALLATION FUTURE, VOIR LA SÉRIE DE FEUILLES 700 POUR LES INTERVENTIONS À FAIRE SUR LES ÉCHELLES AVANT LEUR RÉINSTALLATION.
- 10 CAMERA EXISTANTE À DÉMONTER ET ENTREPOSER POUR RÉINSTALLATION FUTURE, VOIR DOCUMENTS D'INGÉNÉRIE.
- 11 AFFICHAGE EXISTANT À RETIRER ET ENTREPOSER POUR RÉINSTALLATION FUTURE.
- 12 COUSSIN GONFLABLE D'ÉTANCHÉITÉ POUR QUAI D'EMBARQUEMENT À DÉMONTER ET ENTREPOSER POUR RÉINSTALLATION FUTURE.
- 13 MAT DE DRAPEAU À ENLEVER INCLUANT SON ANCRAGE ET À REMETTRE À L'ÉTABLISSEMENT/PROPRIÉTAIRE.
- 14 LETTRAGE RÉTROÉCLAIRÉ À DÉMONTER ET ENTREPOSER POUR RÉINSTALLATION FUTURE, VOIR DOCUMENTS D'INGÉNÉRIE POUR LE RACCORDEMENT ÉLECTRIQUE. PRENDRE LES MESURES DES ESPACEMENTS DES LETTRES AVANT DE LES DÉMONTER AFIN DE POUVOIR LES REINSTALLÉES DE LA MÊME FAÇON.
- 15 GRILLE DE VENTILATION EXISTANTE POUR L'ENTREPLAFOND, À DÉMONTER ET ENTREPOSER POUR RÉINSTALLATION FUTURE.
- 16 PARATONNERRE ET CÂBLAGE DE MISE À LA TERRE EXISTANT À DÉMOLIR, VOIR DOCUMENTS D'INGÉNÉRIE.
- 17 ESCALIER EN ALUMINIUM EXISTANT À RETIRER ET ENTREPOSER POUR RÉINSTALLATION FUTURE.
- 18 AÉRATEUR POUR PAREMENT DE MAÇONNERIE EXISTANT À DÉMOLIR.
- 19 SECTION DE GARDE-CORPS À COUPER, VOIR LES INTERVENTIONS SUR LES FEUILLES DE LA SÉRIE 700.
- 20 FILET EXISTANT À CONSERVER.
- 21 APPAREIL DE COMMUNICATION EXISTANT, VOIR DOCUMENTS D'INGÉNÉRIE.
- 22 BOÎTE DE JONCTION ET FILAGE EXISTANT, VOIR DOCUMENTS D'INGÉNÉRIE.
- 23 GARGOUILLE EXISTANTE À DÉMOLIR, VOIR DÉTAIL #1 SUR LA FEUILLE 306.
- 24 CONDUIT DE VENTILATION EXISTANT À DÉMOLIR, VOIR DOCUMENTS D'INGÉNÉRIE.
- 25 PLATEFORME ET GARDE-CORPS EN ACIER EXISTANT À DÉMONTER ET ENTREPOSER POUR RÉINSTALLATION FUTURE.
- 26 SORTIE D'ARROSAGE EXTERIEUR EXISTANTE, VOIR DOCUMENTS D'INGÉNÉRIE.
- 27 DÉTECTEUR DE PRÉSENCE EXISTANT À DÉMONTER ET ENTREPOSER POUR RÉINSTALLATION FUTURE, VOIR DOCUMENTS D'INGÉNÉRIE.
- 28 GARDE-CORPS EXISTANT À CONSERVER EN PLACE ET À PROTÉGER PENDANT LES TRAVAUX.
- 29 COMPOSITION ISOLÉE SUR LA COLONNE EXISTANTE À DÉMOLIR, VOIR LE DÉTAIL #52 DE LA PAGE 420 ET LE DÉTAIL #25 DE LA PAGE 455.
- 30 TRAPPE D'ACCÈS MURALE EXISTANTE À CONSERVER.
- 31 PERSIENNE EXISTANTE À DÉMOLIR, VOIR DOCUMENTS D'INGÉNÉRIE.
- 32 PAREMENT DE MAÇONNERIE EXISTANT À ENLEVER TEMPORAIREMENT ET ENTREPOSER POUR RÉINSTALLATION FUTURE.
- 33 SECTION DE MUR À DÉMOLIR À PARTIR DU DESSOUS DE LA FENÊTRE EXISTANTE JUSQU'AU PLANCHER, SE RÉFÉRER À LA VUE EN PLAN ET AU DÉTAIL EN PLAN DE LA SÉRIE DE FEUILLES 600 POUR LA LARGEUR DE LA NOUVELLE OUVERTURE.
- 34 PAREMENT DE TÔLE EXISTANT À DÉMOLIR.
- 35 ESCALIER EXISTANT À DÉMOLIR.
- 36 SUPPORTS DE L'ESCALIER À DÉMONTER SOIGNEUSEMENT DE LA FAÇON DE BRIQUE AFIN D'ÉVITER D'ABIMER LA BRIQUE EXISTANTE À CONSERVER, FAIRE TOUTES LES RÉPARATIONS REQUISE AU PAREMENT DE BRIQUE SUITE AU RETRAIT DES SUPPORTS.
- 37 CLAPET (ÉVENT) EXISTANT À DÉMOLIR, VOIR DOCUMENTS D'INGÉNÉRIE.
- 38 PERSIENNE EXISTANTE À DÉMOLIR, VOIR DOCUMENTS D'INGÉNÉRIE, VOIR DÉTAIL SIMILAIRE #2 DE LA FEUILLE 502.
- 39 GARDE-CORPS EXISTANT À DÉMOLIR.
- 40 PORTE ET CADRE EXISTANTS À DÉMOLIR.

LÉGENDE

- (X) NOTE DESCRIPTIVE.
- XXXXX NIVEAU.
- (X) COUPE DE MUR.
- (X) DÉTAIL TYPE.
- (X) AXE EXISTANT.
- (NS) NOUVEL AXE.
- EXISTANT À CONSERVER.
- JOINT D'EXPANSION À CONSERVER.

LÉGENDE DES ZONES

- A TOUR CHAMBRES (NIVEAU 200,300 ET 400) (1974).
- B LABORATOIRE (NIVEAU 100)(1990).
- C ARCHIVES (REZ-DE-CHAUSSEE)(2001).
- D ADMINISTRATIVE (NIVEAU 100) (2005) ET CLINIQUES EXTERNES (REZ-DE-CHAUSSEE) (1974)
- E ONCOLOGIE (REZ-DE-CHAUSSEE) (1974).
- F IRM (REZ-DE-CHAUSSEE) (2007)
- G BASILAIRES SUD-EST(1974)
- H CLINIQUE CHIRURGIE D'UN JOUR (NIVEAU 100) (2005)ET URGENCE (REZ-DE-CHAUSSEE)
- I BASILAIRES SUD-OUEST (1974)
- J BASILAIRES NORD-OUEST (1974)
- K BASILAIRES NORD-EST (1974)
- L ONCOLOGIE (REZ-DE-CHAUSSEE) (2023)

LÉGENDE DES PAREMENTS - DÉMOLITION


- PAREMENT EXISTANT À DÉMOLIR.
- PAREMENT DE TÔLE EXISTANT À DÉMOLIR.
- PAREMENT DE BRIQUE EXISTANT À DÉMOLIR.
- PAREMENT DE BRIQUE EXISTANT À CONSERVER.
- EXISTANT À CONSERVER.

NE DOIT PAS SERVIR À L'EXÉCUTION

Le présent document est émis pour la seule fin identifiée. Son contenu est protégé par les droits d'auteur et toute reproduction ou modification, partielle ou totale, est interdite sans l'autorisation écrite de gagnon, letellier, cyr, ricard, mathieu, proulx, savard consortium d'architectes.




ELEVATION NORD-OUEST

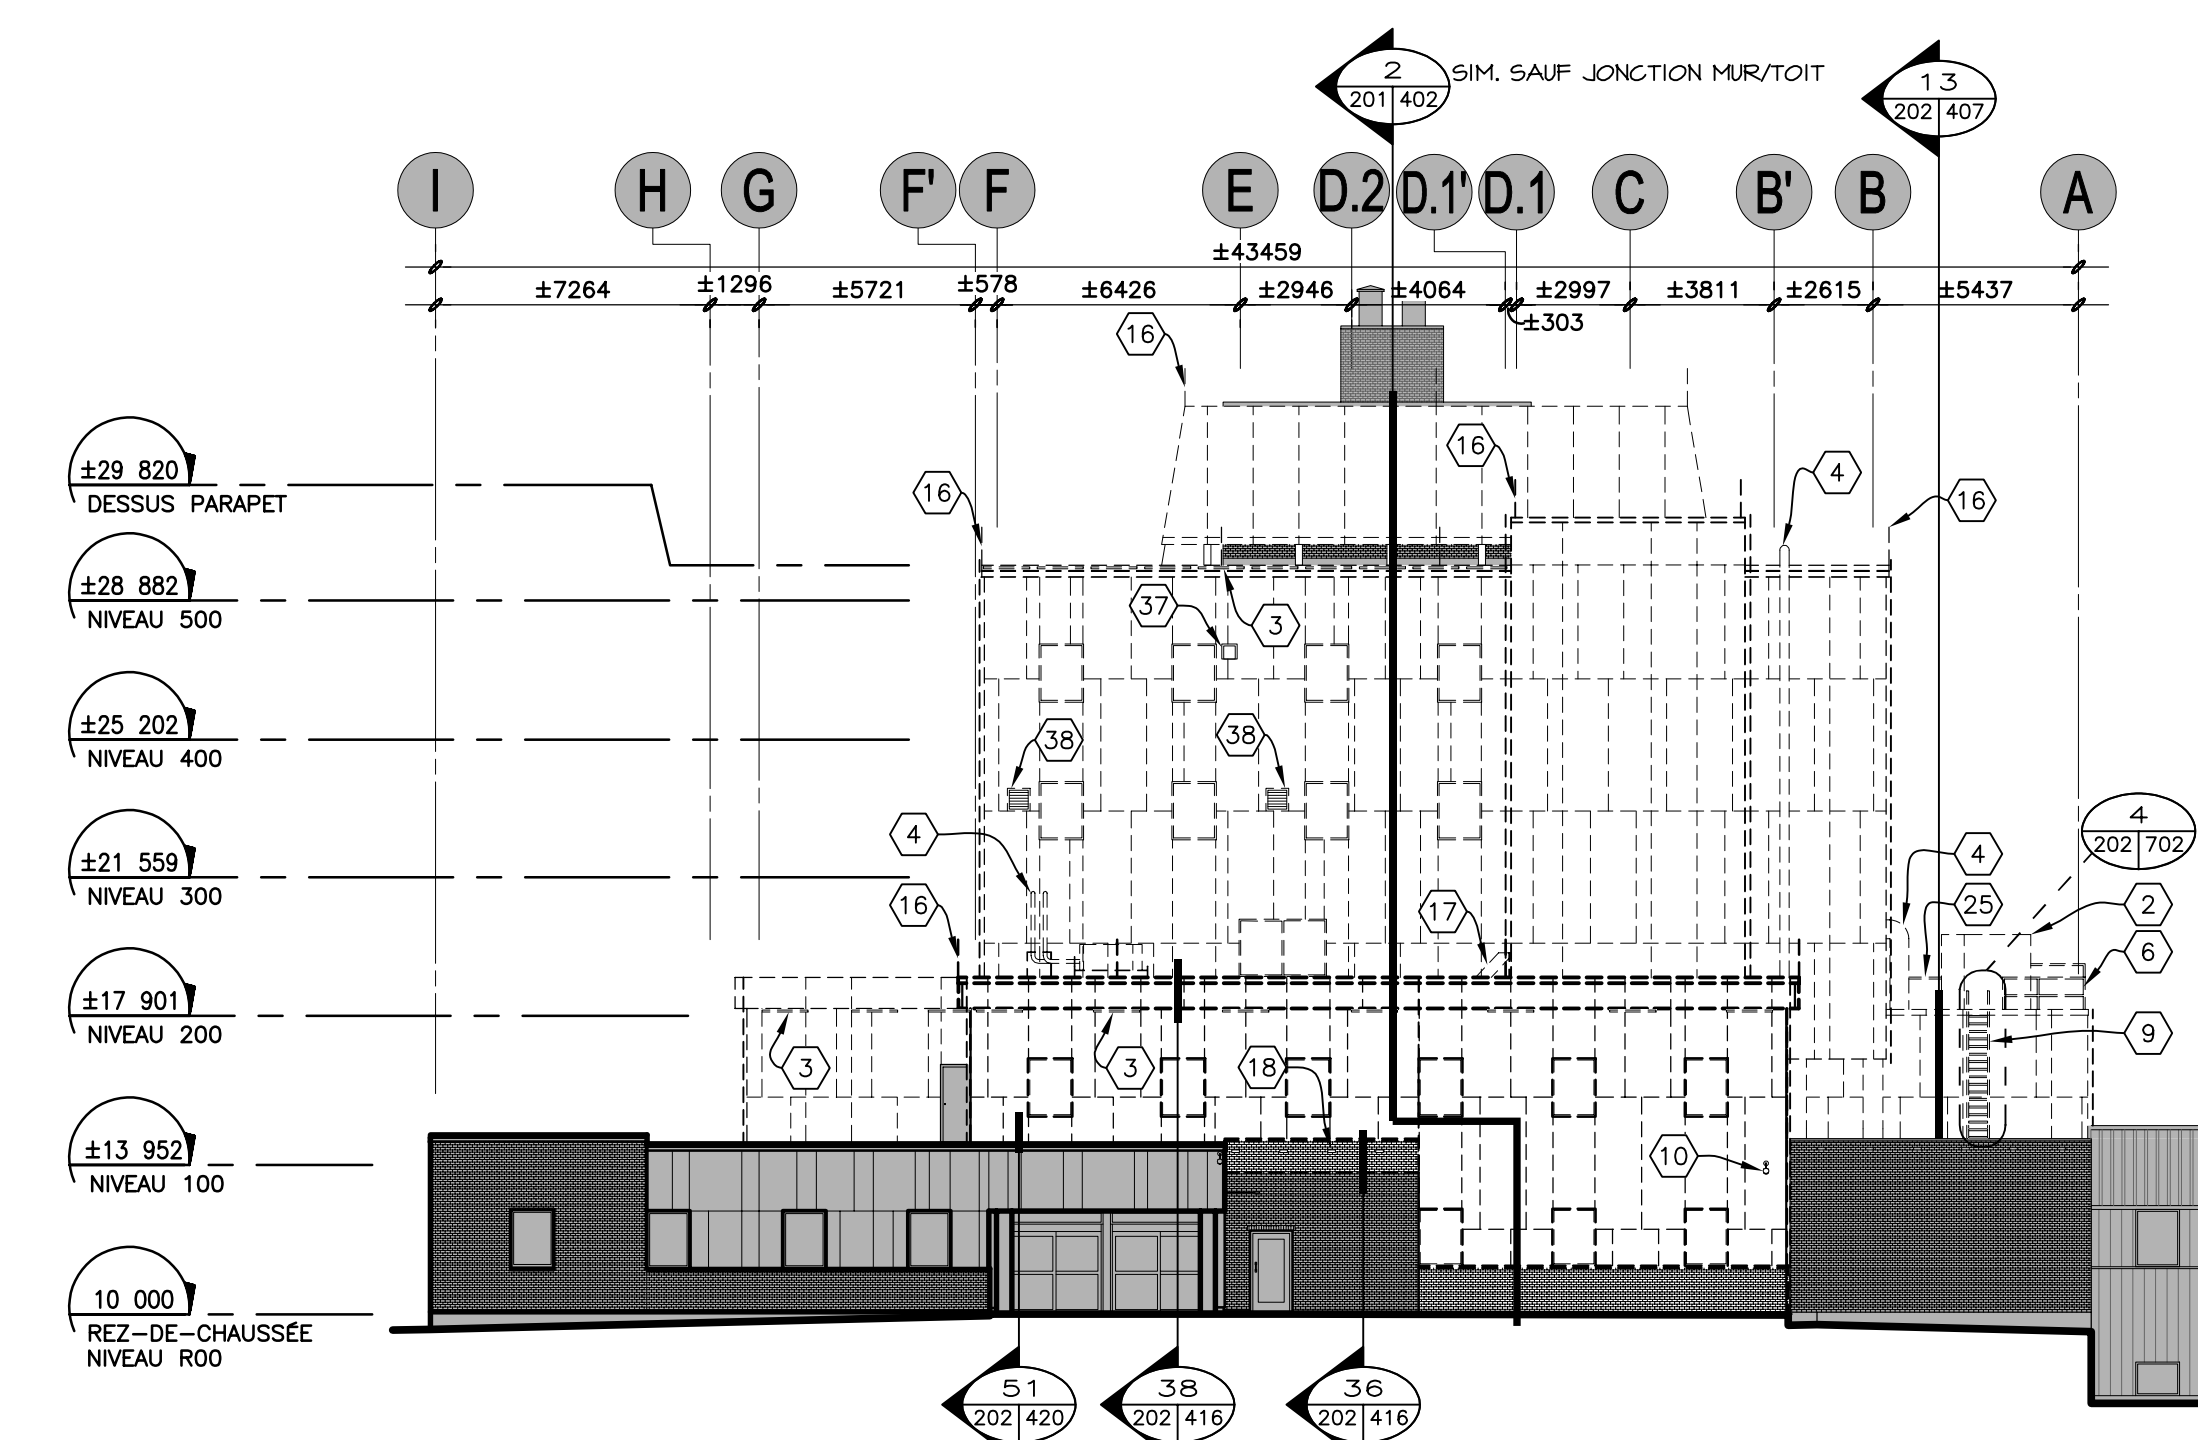

ÉLEVATION EST - DÉMOLITION

1:200mm

PLAN CLÉ

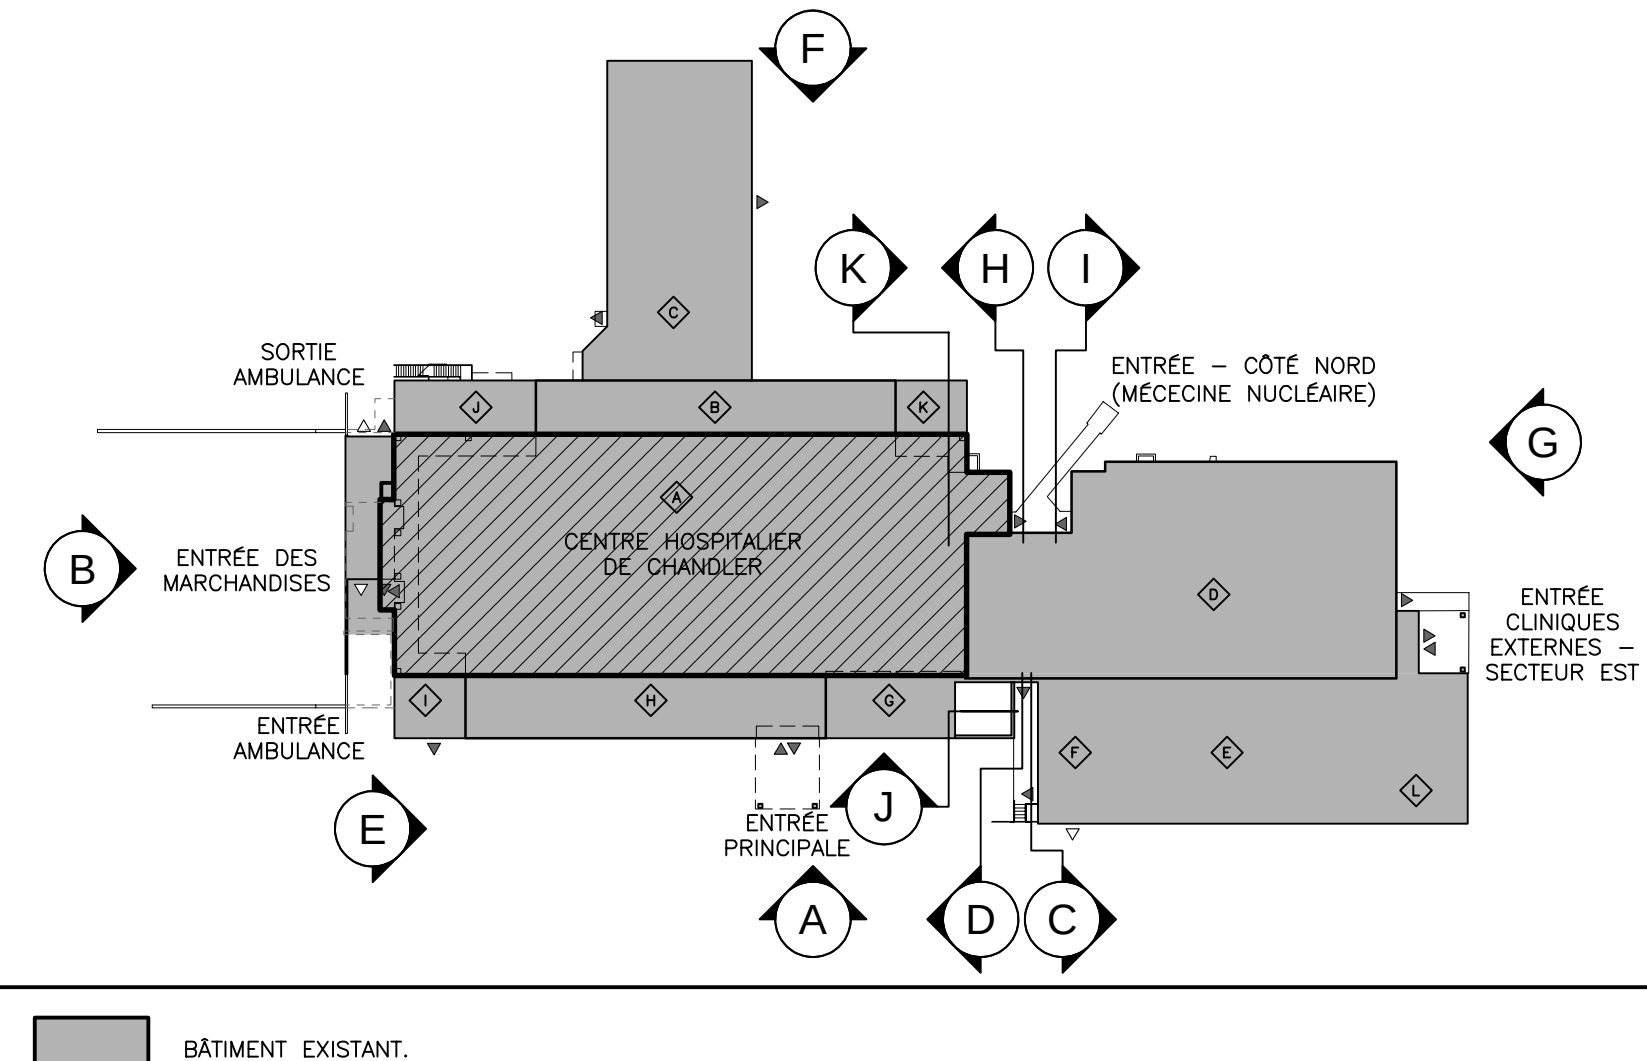


GLCRM | Proulx Savard |

GLCRM:
128, Avenue de la Cathédrale,
Bureau 201
Rimouski, QC, G5L 5H7
(418) 722-7655



2406, Ch. des Quatres-Bourgeois,
Bureau 100
Québec, QC, G1V 1W5
(418) 647-1700

Proulx Savard Architectes:
75, boul. Arthur-Buies Ouest,
Rimouski QC G5L 5C2
(418) 723-5543

ARCHITECTURE

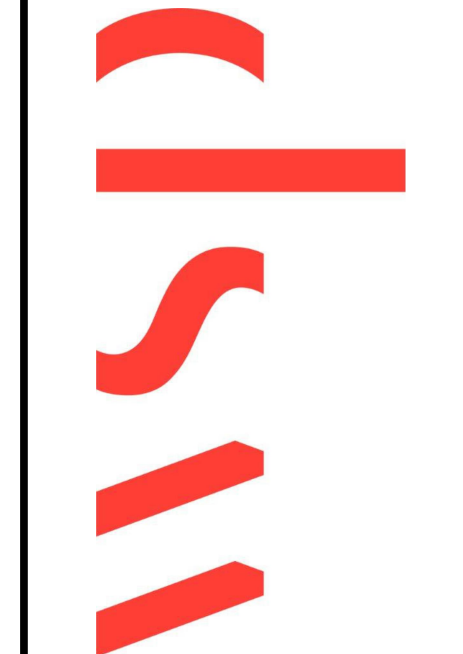


CONSULTANTS

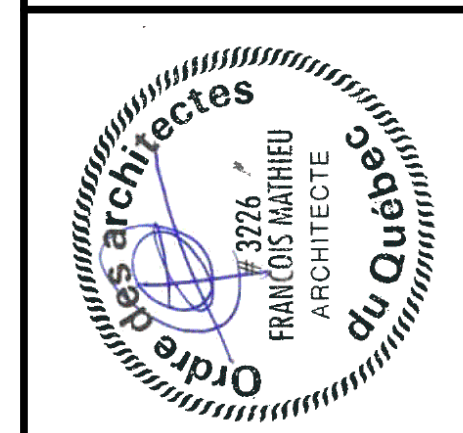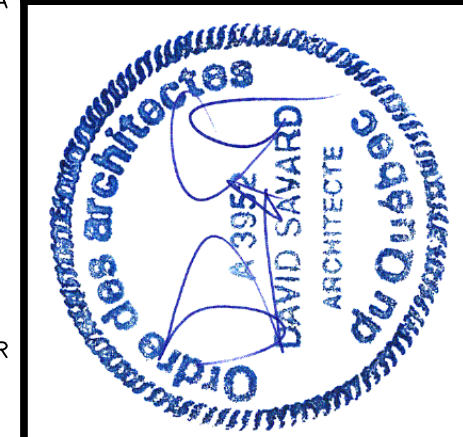


DOSSIER No.		DATE		REVISIONS	
24-108 / R657-24		SEPTEMBRE 2026			
DESIGNATEUR(S)		ÉCHELLE		INDIQUÉE	
D.B. A.B. A.C. J.L.					
PROJET		DATE		DATE	
HÔPITAL DE CHANDLER, Chandler (Réfection de l'enveloppe)		05	2026-09-04	DEFINITIFS POUR SOUMISSION	
		06	2026-08-21	DEFINITIFS 100% POUR APPROBATION	
		03	2026-08-03	DEFINITIFS 80% POUR APPROBATION	
		02	2026-05-14	DEFINITIFS 40% POUR APPROBATION	
		01	2026-02-27	PRELIMINAIRES 30% POUR APPROBATION	
				REVISIONS	


DESIGNÉ	PROJET	PROPRIÉTAIRE
D.B. A.B. A.C. J.L.	HÔPITAL DE CHANDLER, Chandler (Réfection de l'enveloppe)	Santé Québec

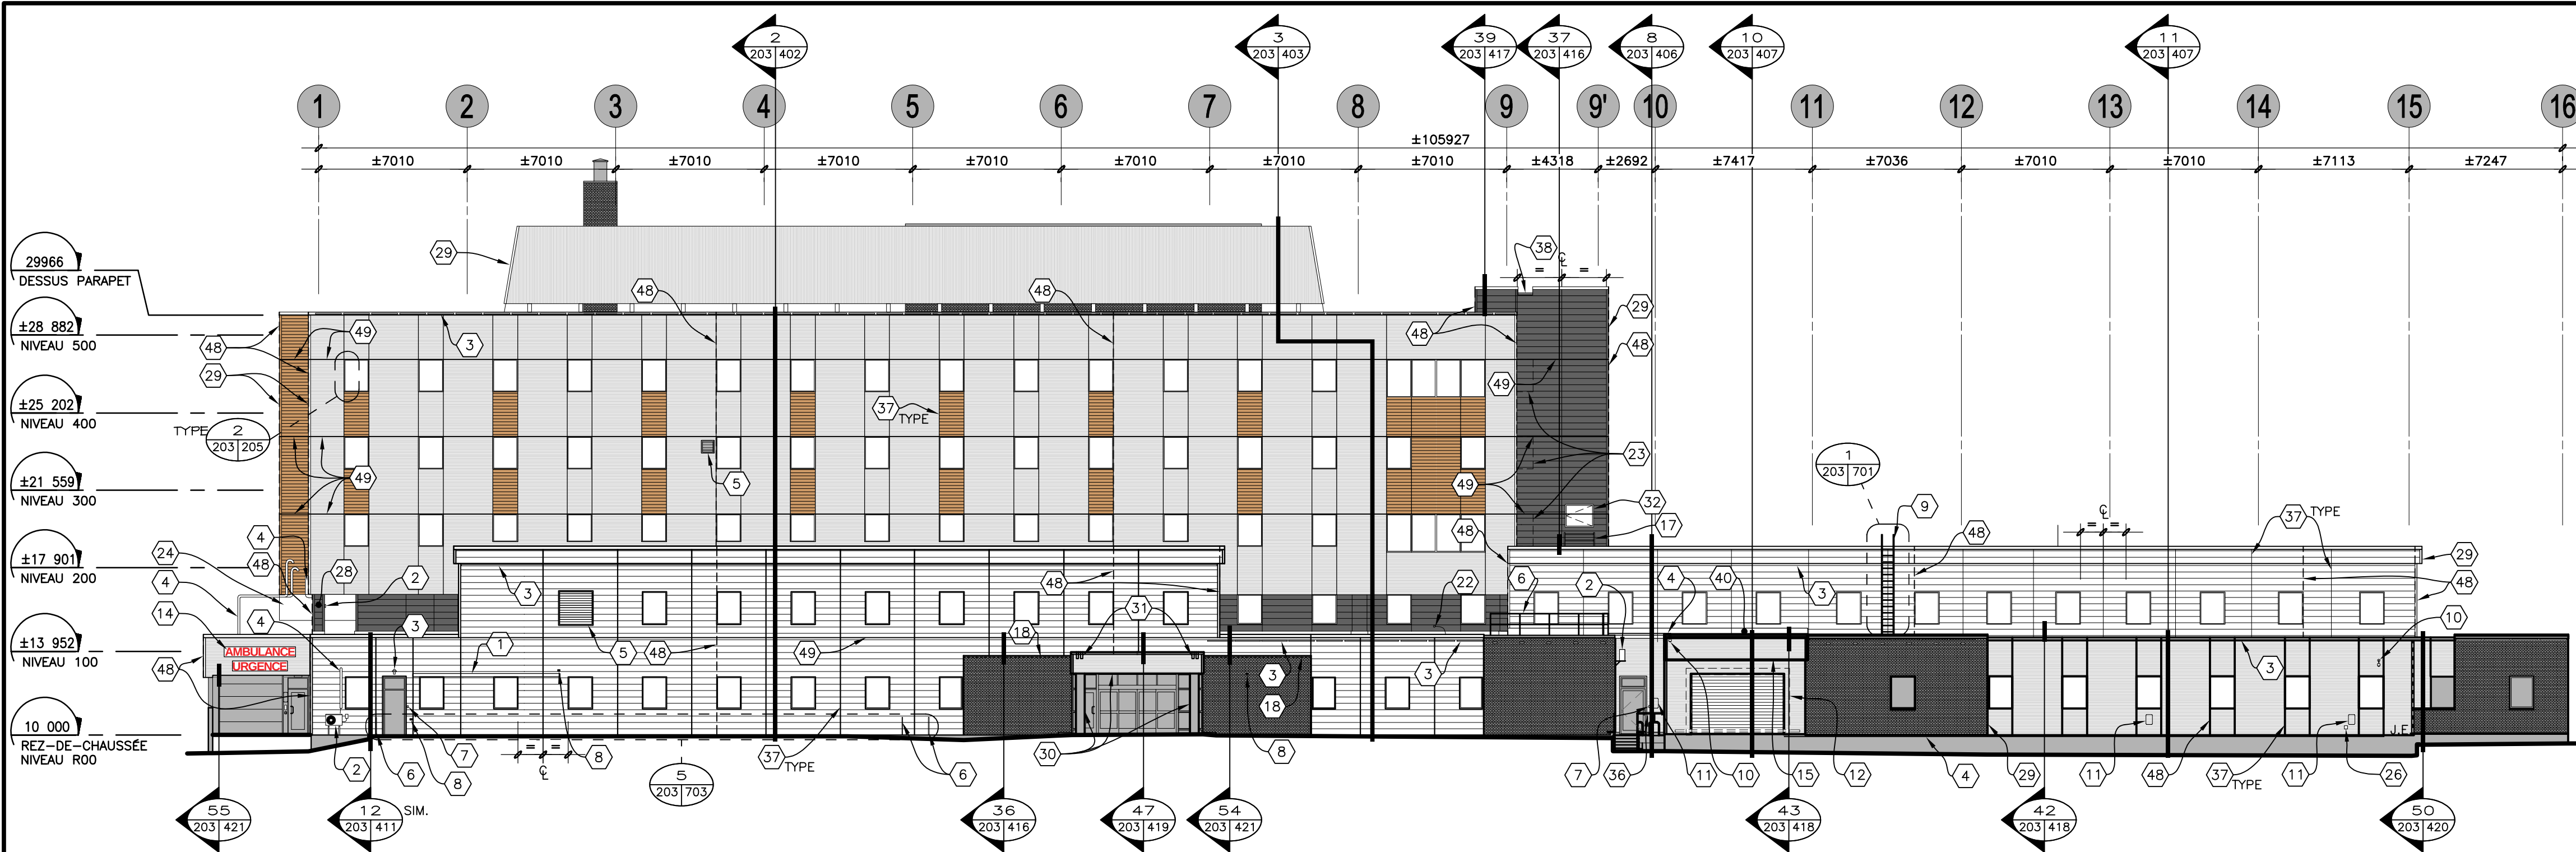

A ÉLEVATION SUD - CONSTRUCTION
1:200mm

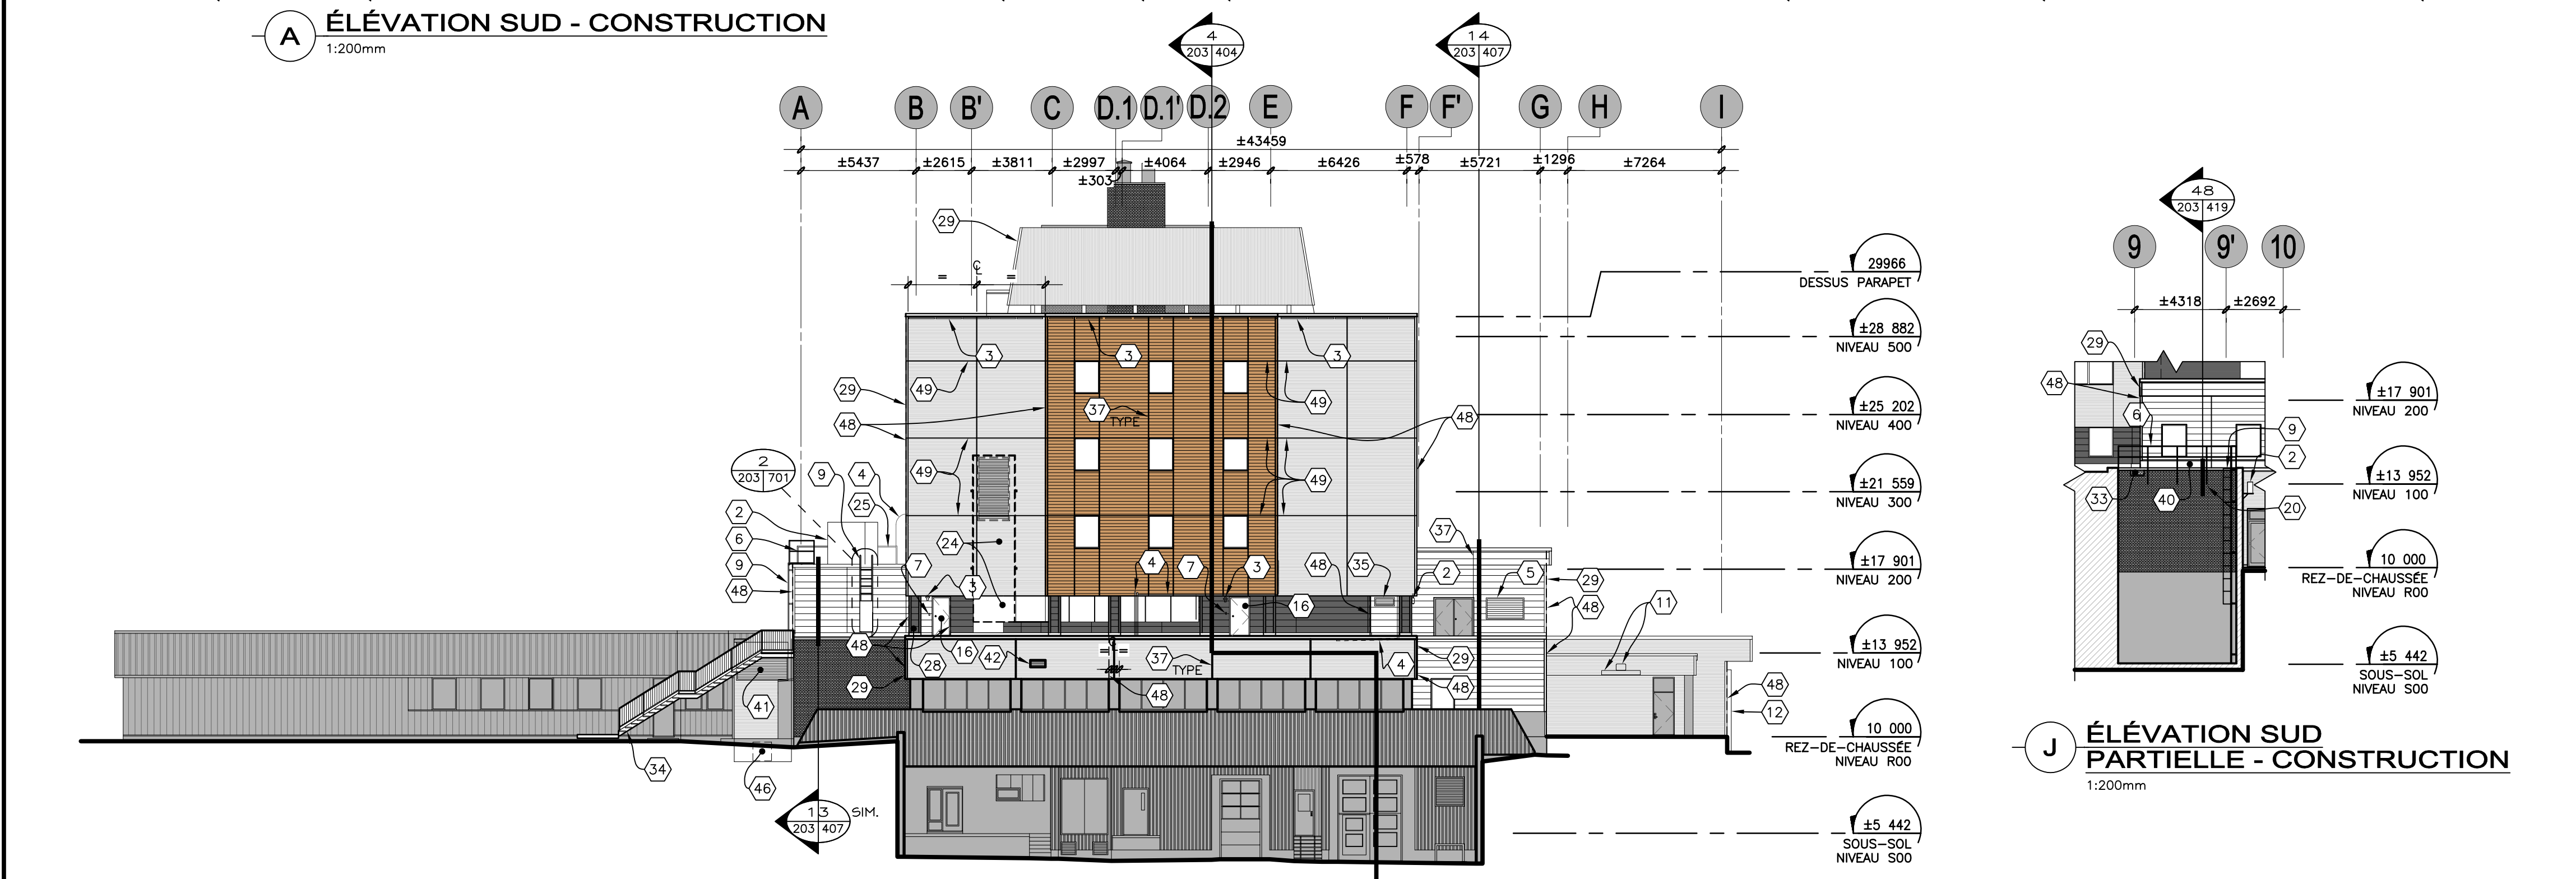

B ÉLEVATION OUEST - CONSTRUCTION
1:200mm

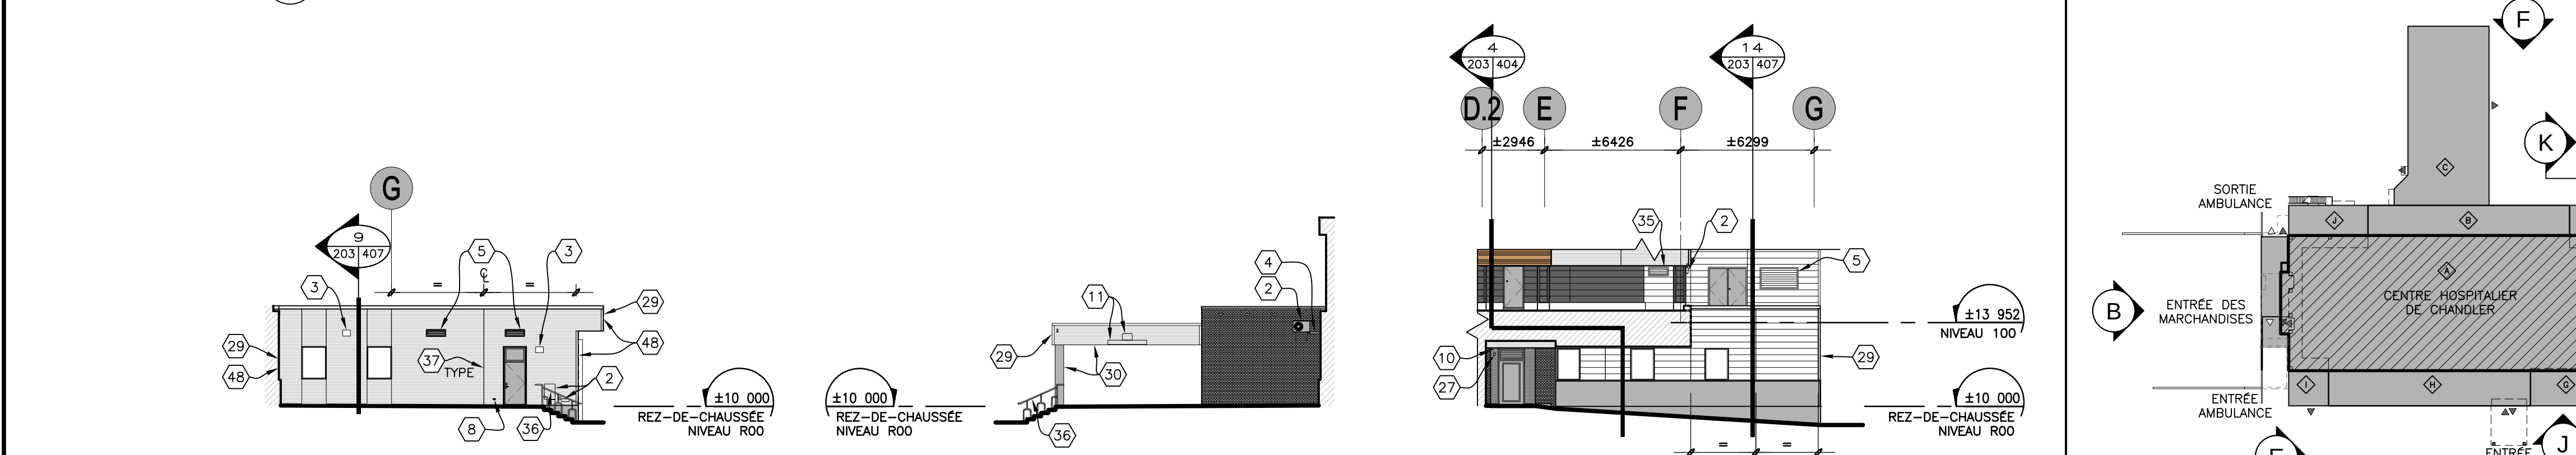


C ÉLEVATION OUEST PARTIELLE - CONSTRUCTION
1:200mm




D ÉLEVATION EST PARTIELLE - CONSTRUCTION
1:200mm



E ÉLEVATION OUEST PARTIELLE - CONSTRUCTION
1:200mm

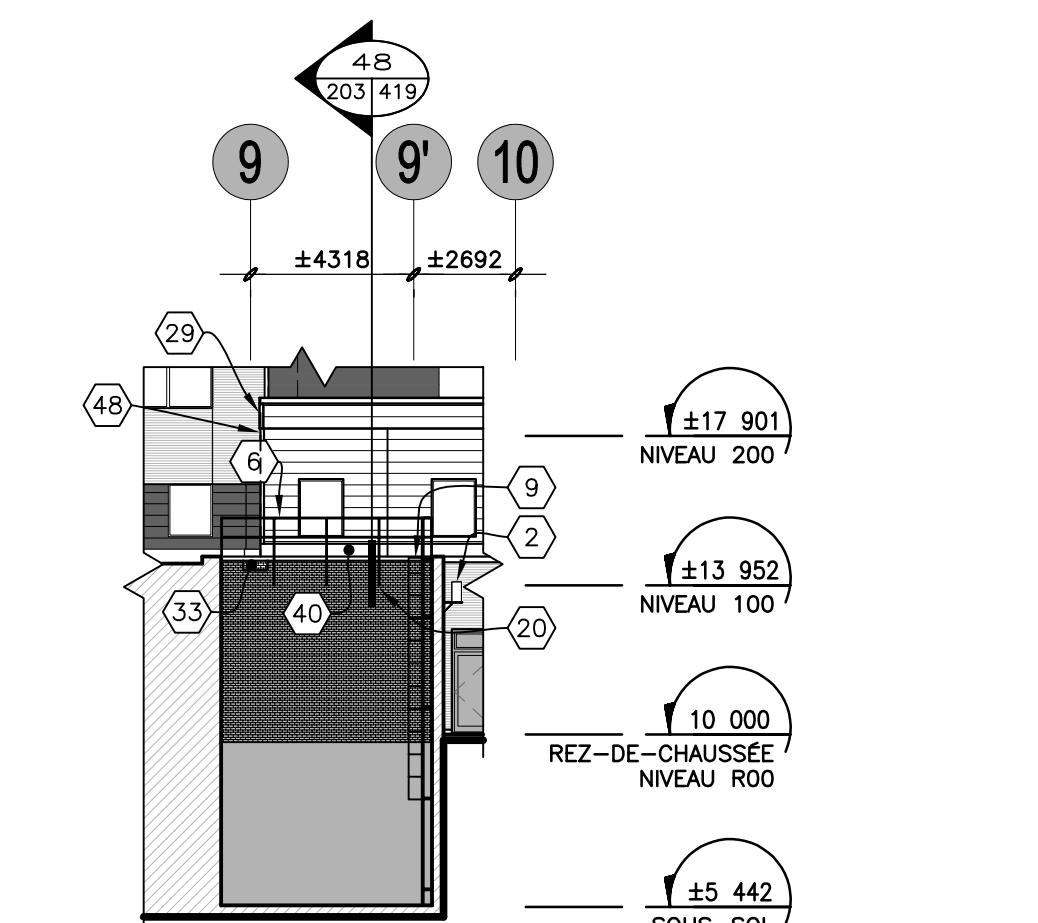

J ÉLEVATION SUD PARTIELLE - CONSTRUCTION
1:200mm

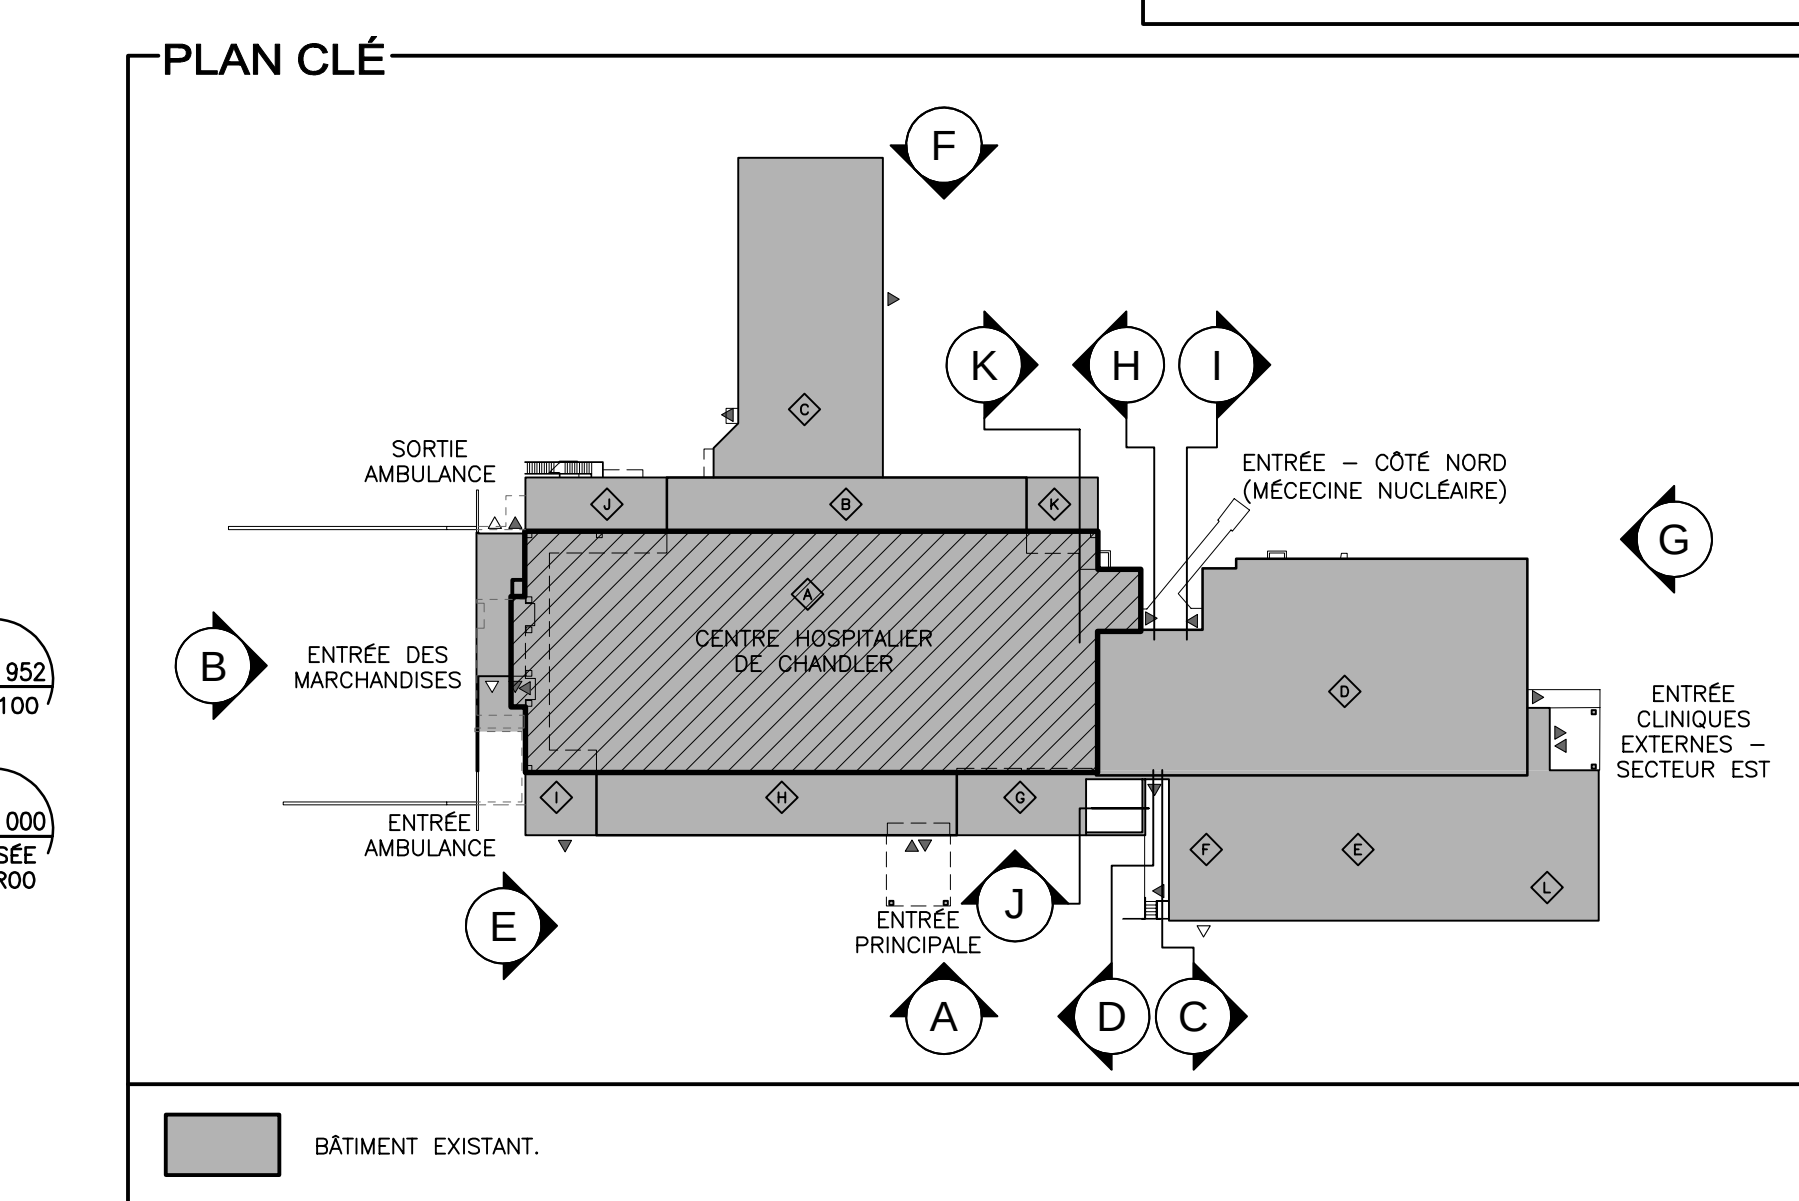

PLAN CLÉ

- ### NOTES
- TOILE AMOVIBLE EXISTANTE À REINSTALLER.
 - APPAREIL D'ÉLECTRO-MÉCANIQUE ET SUPPORT EXISTANT, VOIR DOCUMENTS D'INGÉNIERIE.
 - LUMINAIRE EXISTANT, VOIR DOCUMENTS D'INGÉNIERIE. VOIR DÉTAIL #8 À LA FEUILLE 205.
 - CONDUIT EXISTANT, VOIR DOCUMENTS D'INGÉNIERIE.
 - PERSIENNE DE VENTILATION EXISTANTE REINSTALLÉE, VOIR DOCUMENTS D'INGÉNIERIE. LA PERSIENNE DOIT ÊTRE REPEINT, AVANT SON INSTALLATION, DE LA MÊME COULEUR QUE LE REVÊTEMENT DANS LEQUEL ELLE SERA INSTALLÉE. VOIR ÉLEVATIONS POUR LE TYPE DE REVÊTEMENT DANS LEQUEL ELLE SERA INSTALLÉE.
 - GARDE-CORPS EXISTANT À REINSTALLER, VOIR FEUILLES DE LA SÉRIE 700 POUR LES TRAVAUX À EXÉCUTER SUR LE GARDE-CORPS AVANT SA REINSTALLATION.
 - LECTEUR DE CARTE/PUCE EXISTANT À REINSTALLER. VOIR INGÉNIEUR. VOIR DÉTAIL #4 À LA FEUILLE 205.
 - PRISE ÉLECTRIQUE EXISTANTE, VOIR DOCUMENTS D'INGÉNIERIE. VOIR DÉTAIL #4 À LA FEUILLE 205.
 - ÉCHELLE EXISTANTE À REINSTALLER, VOIR LES FEUILLES DE LA SÉRIE 700 POUR LES TRAVAUX À EXÉCUTER SUR L'ÉCHELLE AVANT SA REINSTALLATION.
 - CAMERA EXISTANTE À REINSTALLER, VOIR DOCUMENTS D'INGÉNIERIE. VOIR DÉTAIL #3 À LA FEUILLE 205.
 - AFFICHAGE EXISTANT À REINSTALLER.
 - COUSSIN GONFLABLE D'ÉTANCHÉITÉ POUR QUAI D'EMBARQUEMENT À REINSTALLER. VOIR DÉTAIL #6 SUR LA FEUILLE 603.
 - PERSIENNE DE VENTILATION EXISTANTE À REINSTALLER.
 - LETTRAGE RÉTROÉCLAIRÉ EXISTANT À REINSTALLER AU MÊME ENDROIT ET AVEC LES MÊMES ESPACEMENTS QUE L'EXISTANT. VOIR LES DOCUMENTS D'INGÉNIERIE POUR LE RACCORDEMENT ÉLECTRIQUE. VOIR DÉTAIL D'INTÉGRATION #9 SUR LA FEUILLE 205. LA STRUCTURE DU LETTRAGE DOIT ÊTRE REPEINT AVANT D'ÊTRE REINSTALLÉES.
 - GRILLE DE VENTILATION EXISTANTE POUR L'ENTREPLAFOND À REINSTALLÉE.
 - NOUVELLE PORTE ISOLÉ ET CADRE EN ACIER ISOLÉ AVEC BRIS THERMIQUE. PEINT.
 - ESCALIER EN ACIER EXISTANT À REINSTALLER SUR UN PANNEAU DE CAOUTCHOUC.
 - CRÉER DES ÉVÈNEMENTS À MAÇONNERIE DANS L'AVANT DERNIER RANG DE BRIQUES DU MUR EXISTANT, EN ÉVITANT LE JOINT DE MORTIER VERTICAL À TOUS LES 3 BRIQUES.
 - SECTION DE GARDE-CORPS À MODIFIER. VOIR LES INTERVENTIONS À LA SÉRIE DE FEUILLES 700.
 - FILET EXISTANT À CONSERVER.
 - APPAREIL DE COMMUNICATION EXISTANT, VOIR DOCUMENTS D'INGÉNIERIE.
 - BOÎTE DE JONCTION ET FILAGE EXISTANT, VOIR DOCUMENTS D'INGÉNIERIE.
 - OUVERTURE EXISTANTE À OBTURER, VOIR DÉTAIL SIMILAIRE #2 DE LA FEUILLE 502.
 - NOUVEAU CONDUIT DE VENTILATION, VOIR DOCUMENTS D'INGÉNIERIE.
 - PLATEFORME ET GARDE-CORPS EN ACIER EXISTANT À REINSTALLER, VOIR LES FEUILLES DE LA SÉRIE 700 POUR LES TRAVAUX À EXÉCUTER SUR LA PLATEFORME ET LE GARDE-CORPS AVANT LEUR REINSTALLATION.
 - SORTIE D'ARROSAGE EXTERIEUR EXISTANTE, VOIR DOCUMENTS D'INGÉNIERIE. VOIR DÉTAIL #3 À LA FEUILLE 205.
 - DÉTECTEUR DE PRÉSENCE EXISTANT À REINSTALLER, VOIR DOCUMENTS D'INGÉNIERIE.

- ### NOTES
- TOILE AMOVIBLE EXISTANTE À REINSTALLER.
 - APPAREIL D'ÉLECTRO-MÉCANIQUE ET SUPPORT EXISTANT, VOIR DOCUMENTS D'INGÉNIERIE.
 - LUMINAIRE EXISTANT, VOIR DOCUMENTS D'INGÉNIERIE. VOIR DÉTAIL #8 À LA FEUILLE 205.
 - CONDUIT EXISTANT, VOIR DOCUMENTS D'INGÉNIERIE.
 - PERSIENNE DE VENTILATION EXISTANTE REINSTALLÉE, VOIR DOCUMENTS D'INGÉNIERIE. LA PERSIENNE DOIT ÊTRE REPEINT, AVANT SON INSTALLATION, DE LA MÊME COULEUR QUE LE REVÊTEMENT DANS LEQUEL ELLE SERA INSTALLÉE. VOIR ÉLEVATIONS POUR LE TYPE DE REVÊTEMENT DANS LEQUEL ELLE SERA INSTALLÉE.
 - GARDE-CORPS EXISTANT À REINSTALLER, VOIR FEUILLES DE LA SÉRIE 700 POUR LES TRAVAUX À EXÉCUTER SUR LE GARDE-CORPS AVANT SA REINSTALLATION.
 - LECTEUR DE CARTE/PUCE EXISTANT À REINSTALLER. VOIR INGÉNIEUR. VOIR DÉTAIL #4 À LA FEUILLE 205.
 - PRISE ÉLECTRIQUE EXISTANTE, VOIR DOCUMENTS D'INGÉNIERIE. VOIR DÉTAIL #4 À LA FEUILLE 205.
 - ÉCHELLE EXISTANTE À REINSTALLER, VOIR LES FEUILLES DE LA SÉRIE 700 POUR LES TRAVAUX À EXÉCUTER SUR L'ÉCHELLE AVANT SA REINSTALLATION.
 - CAMERA EXISTANTE À REINSTALLER, VOIR DOCUMENTS D'INGÉNIERIE. VOIR DÉTAIL #3 À LA FEUILLE 205.
 - AFFICHAGE EXISTANT À REINSTALLER.
 - COUSSIN GONFLABLE D'ÉTANCHÉITÉ POUR QUAI D'EMBARQUEMENT À REINSTALLER. VOIR DÉTAIL #6 SUR LA FEUILLE 603.
 - PERSIENNE DE VENTILATION EXISTANTE À REINSTALLER.
 - LETTRAGE RÉTROÉCLAIRÉ EXISTANT À REINSTALLER AU MÊME ENDROIT ET AVEC LES MÊMES ESPACEMENTS QUE L'EXISTANT. VOIR LES DOCUMENTS D'INGÉNIERIE POUR LE RACCORDEMENT ÉLECTRIQUE. VOIR DÉTAIL D'INTÉGRATION #9 SUR LA FEUILLE 205. LA STRUCTURE DU LETTRAGE DOIT ÊTRE REPEINT AVANT D'ÊTRE REINSTALLÉES.
 - GRILLE DE VENTILATION EXISTANTE POUR L'ENTREPLAFOND À REINSTALLÉE.
 - NOUVELLE PORTE ISOLÉ ET CADRE EN ACIER ISOLÉ AVEC BRIS THERMIQUE. PEINT.
 - ESCALIER EN ACIER EXISTANT À REINSTALLER SUR UN PANNEAU DE CAOUTCHOUC.
 - CRÉER DES ÉVÈNEMENTS À MAÇONNERIE DANS L'AVANT DERNIER RANG DE BRIQUES DU MUR EXISTANT, EN ÉVITANT LE JOINT DE MORTIER VERTICAL À TOUS LES 3 BRIQUES.
 - SECTION DE GARDE-CORPS À MODIFIER. VOIR LES INTERVENTIONS À LA SÉRIE DE FEUILLES 700.
 - FILET EXISTANT À CONSERVER.
 - APPAREIL DE COMMUNICATION EXISTANT, VOIR DOCUMENTS D'INGÉNIERIE.
 - BOÎTE DE JONCTION ET FILAGE EXISTANT, VOIR DOCUMENTS D'INGÉNIERIE.
 - OUVERTURE EXISTANTE À OBTURER, VOIR DÉTAIL SIMILAIRE #2 DE LA FEUILLE 502.
 - NOUVEAU CONDUIT DE VENTILATION, VOIR DOCUMENTS D'INGÉNIERIE.
 - PLATEFORME ET GARDE-CORPS EN ACIER EXISTANT À REINSTALLER, VOIR LES FEUILLES DE LA SÉRIE 700 POUR LES TRAVAUX À EXÉCUTER SUR LA PLATEFORME ET LE GARDE-CORPS AVANT LEUR REINSTALLATION.
 - SORTIE D'ARROSAGE EXTERIEUR EXISTANTE, VOIR DOCUMENTS D'INGÉNIERIE. VOIR DÉTAIL #3 À LA FEUILLE 205.
 - DÉTECTEUR DE PRÉSENCE EXISTANT À REINSTALLER, VOIR DOCUMENTS D'INGÉNIERIE.

- ### LÉGENDE DES ZONES
- A TOUR CHAMBRES (NIVEAU 200,300 ET 400) (1974).
 - B LABORATOIRE (NIVEAU 100)(1990).
 - C ARCHIVES (REZ-DE-CHAUSÉE)(2001).
 - D ADMINISTRATIVE (NIVEAU 100) (2005) ET CLINIQUES EXTERNES (REZ-DE-CHAUSÉE) (1974)
 - E ONCOLOGIE (REZ-DE-CHAUSÉE) (1974).
 - F IRM (REZ-DE-CHAUSÉE) (2007)
 - G BASILAIRE SUD-EST(1974)
 - H CLINIQUE CHIRURGIE D'UN JOUR (NIVEAU 100) (2005)ET URGENCE (REZ-DE-CHAUSÉE)
 - I BASILAIRE SUD-OUEST (1974)
 - J BASILAIRE NORD-OUEST (1974)
 - K BASILAIRE NORD-EST (1974)
 - L ONCOLOGIE (REZ-DE-CHAUSÉE) (2023)

- ### LÉGENDE DES PAREMENTS
- PAREMENT D'ACIER CORRUGUÉ 22mm, TYPE 1. COULEUR BLANC CAMBRIDGE.
 - PAREMENT D'ACIER CORRUGUÉ 22mm, TYPE 2. COULEUR BLANC CAMBRIDGE.
 - PAREMENT DE DÉCLIN D'ALUMINIUM TYPE 3. COULEUR HICORY NATUREL.
 - PAREMENT D'ACIER AD300 SR TYPE 4. COULEUR GRIS RÉGENT.
 - PAREMENT D'ACIER AD300 SR TYPE 5. COULEUR GRIS CHARGON.
- ### LÉGENDE
- (X) NOTE DESCRIPTIVE.
 - (XXXX) NIVEAU.
 - (X/XXX) COUPE DE MUR.
 - (XXX/XXX) DÉTAIL TYPE.
 - (X) AXE EXISTANT.
 - (NS) NOUVEL AXE.
 - EXISTANT À CONSERVER.
 - JOINT D'EXPANSION À CONSERVER.

NE DOIT PAS SERVIR À L'EXÉCUTION

Le présent document est émis pour la seule fin identifiée. Son contenu est protégé par les droits d'auteur et toute reproduction ou modification, partielle ou totale, est interdite sans l'autorisation écrite de gagnon, letellier, cyr, ricard, mathieu, prouls, savard consortium d'architectes.

GLCRM | Proulx Savard |

GLCRM:
128, Avenue de la Cathédrale,
Bureau 201
Rimouski, QC, G5L 5H7
(418) 722-7655

2406, Ch. des Quatres-Bourgeois,
Bureau 100
Québec, QC, G1V 1W5
(418) 647-1700

Proulx Savard Architectes:
75, boul. Arthur-Buies Ouest,
Rimouski QC G5L 5C2
(418) 723-5543

ARCHITECTURE

CONSULTANTS

DOSSIER No.: 24-107 / 1687-24
DATE: SEPTEMBRE 2024
DESIGN: ELEVATIONS CONSTRUCTION
PROJET: HÔPITAL DE CHANDLER, (Réfection de l'enveloppe)
PROPRIÉTAIRE: Santé Québec

No	DATE	REVISIONS
05	2024-09-04	DÉFINITIVES POUR SOUMISSION
04	2024-08-21	DÉFINITIVES 100% POUR APPROBATION
03	2024-08-03	DÉFINITIVES 80% POUR APPROBATION
02	2024-05-14	DÉFINITIVES 60% POUR APPROBATION
01	2024-02-27	PRÉLIMINAIRES 30% POUR APPROBATION

203