




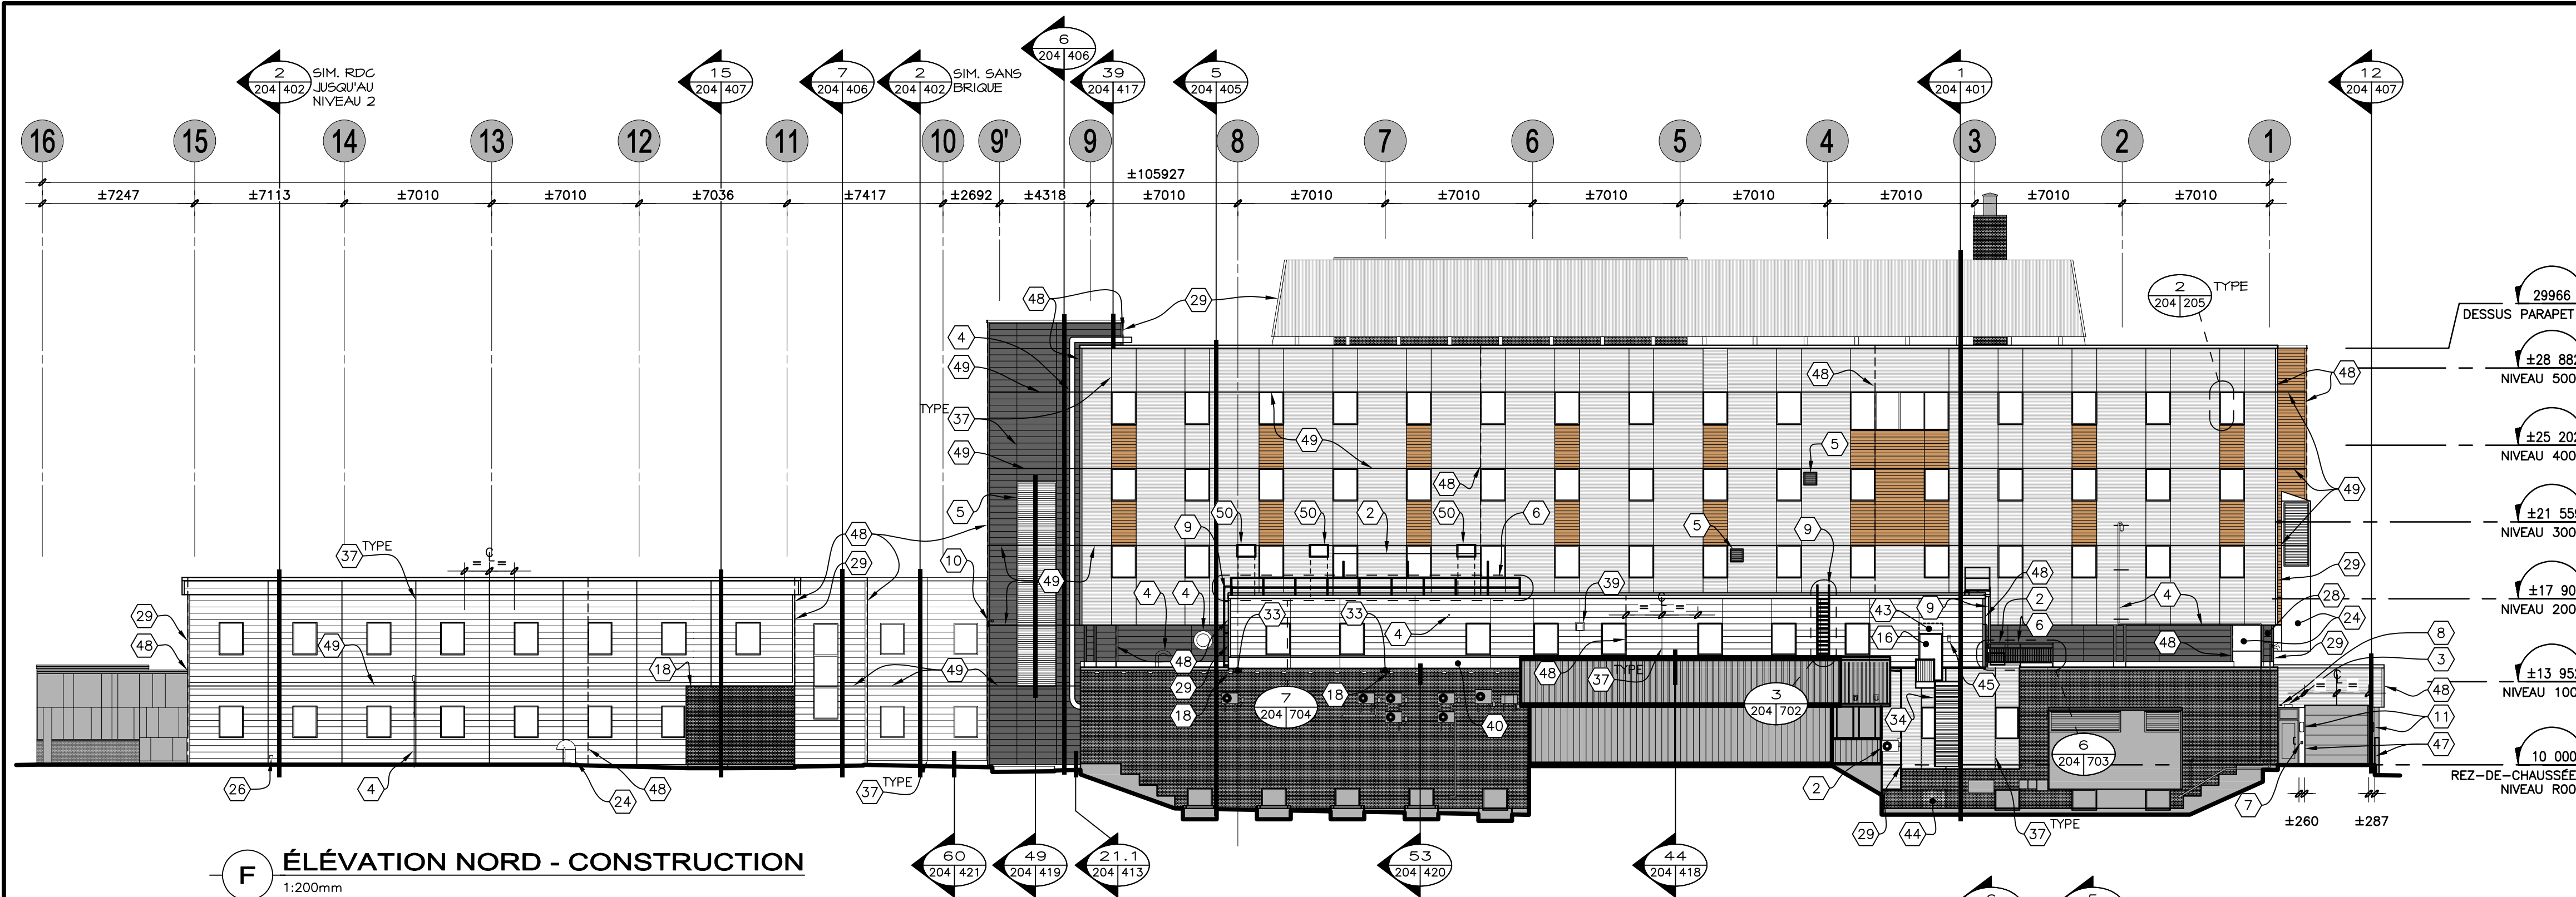

F ÉLEVATION NORD - CONSTRUCTION
1:200mm

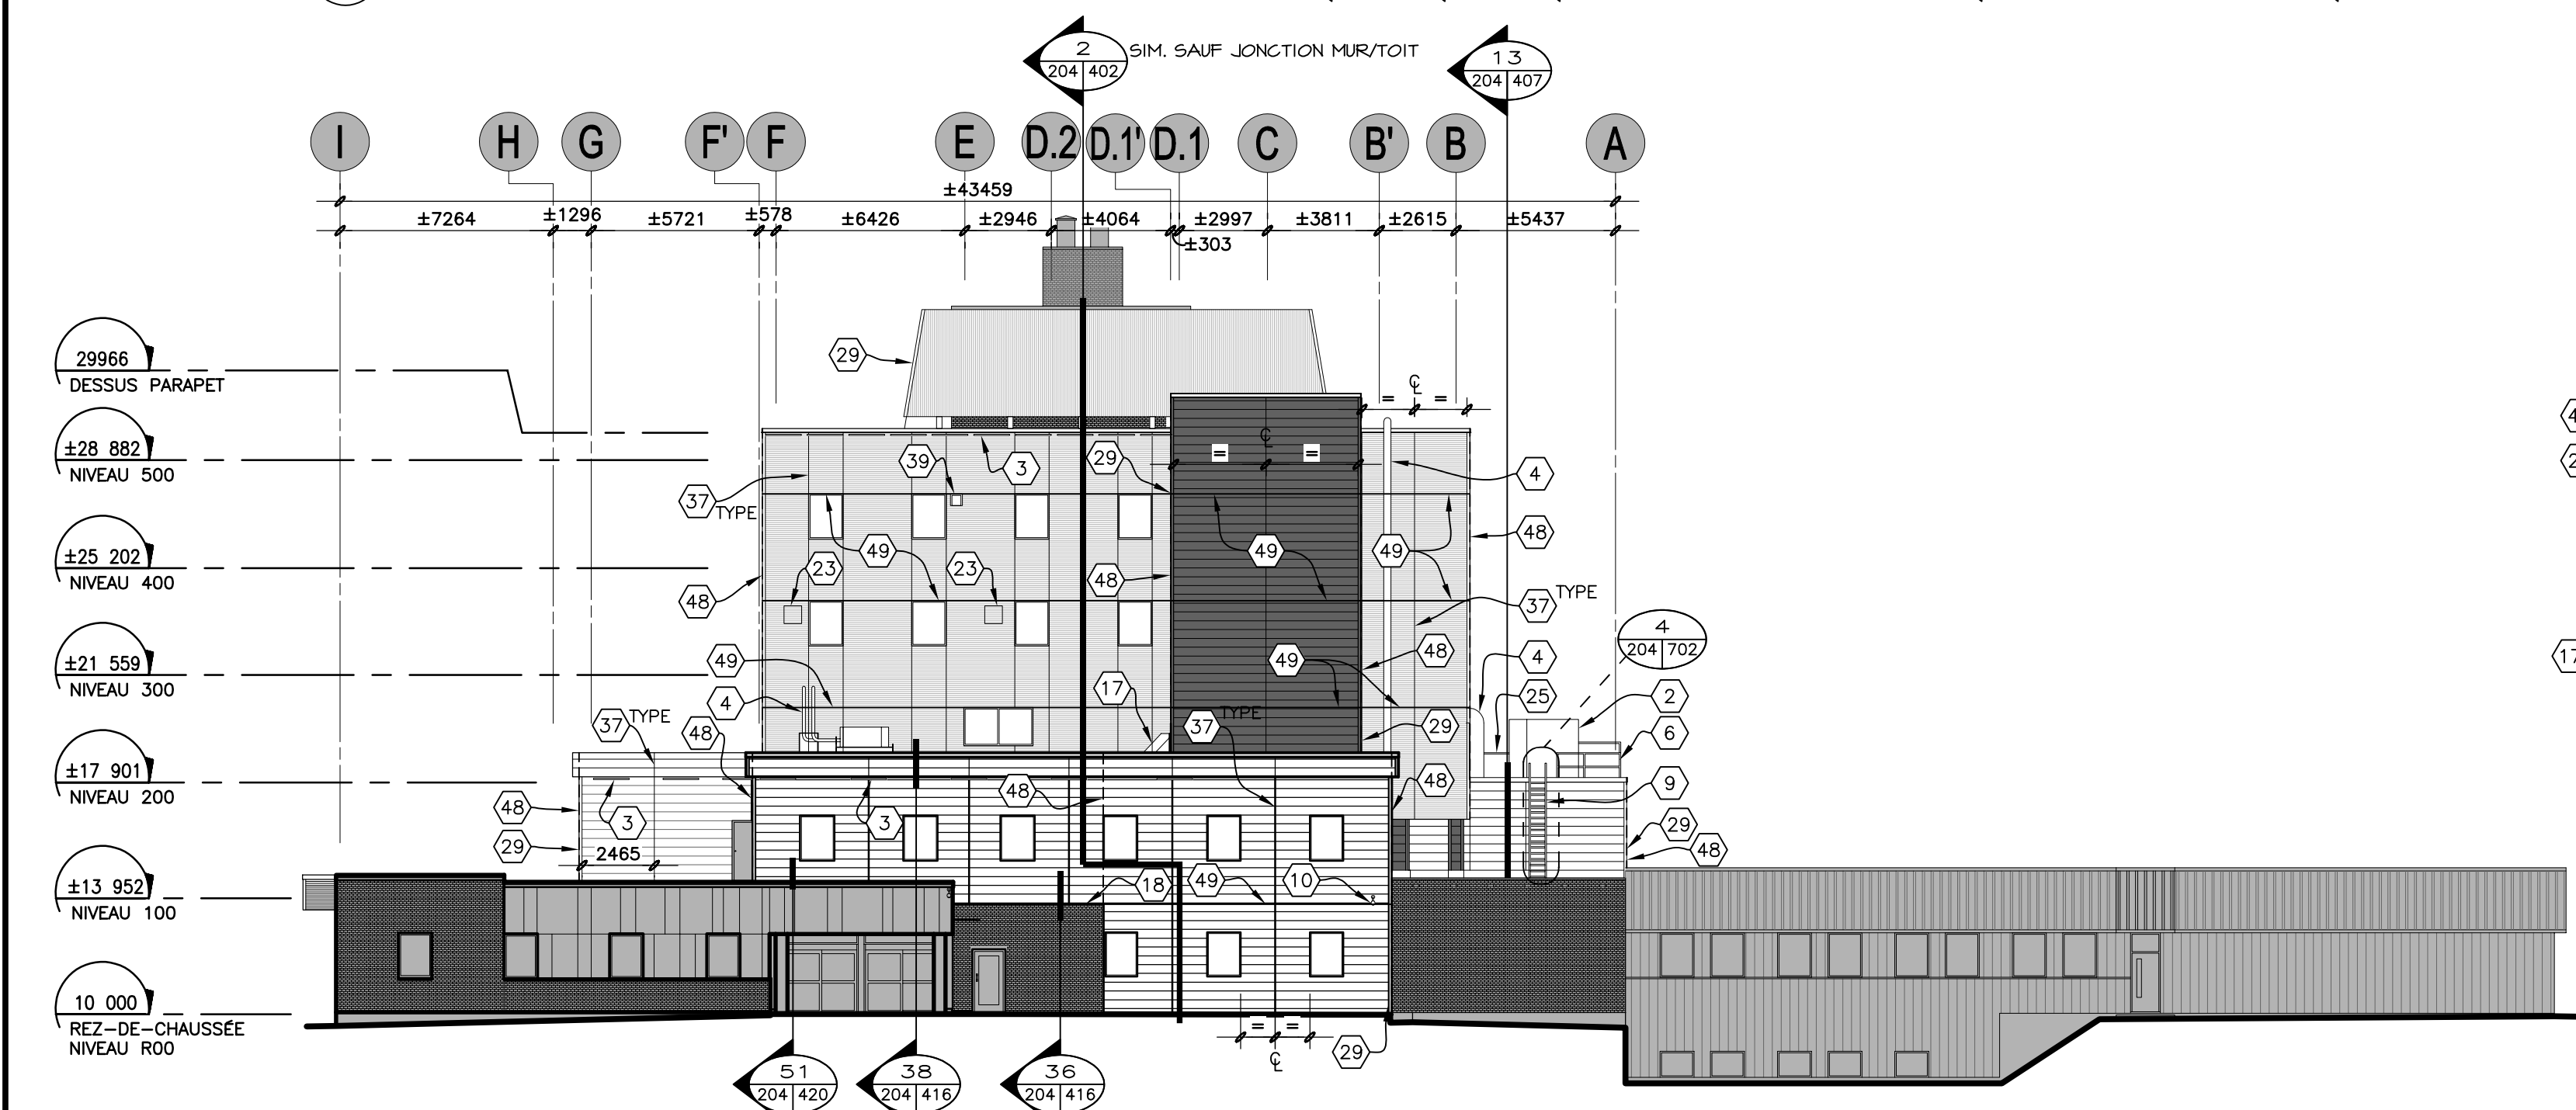

G ÉLEVATION EST - CONSTRUCTION
1:200mm

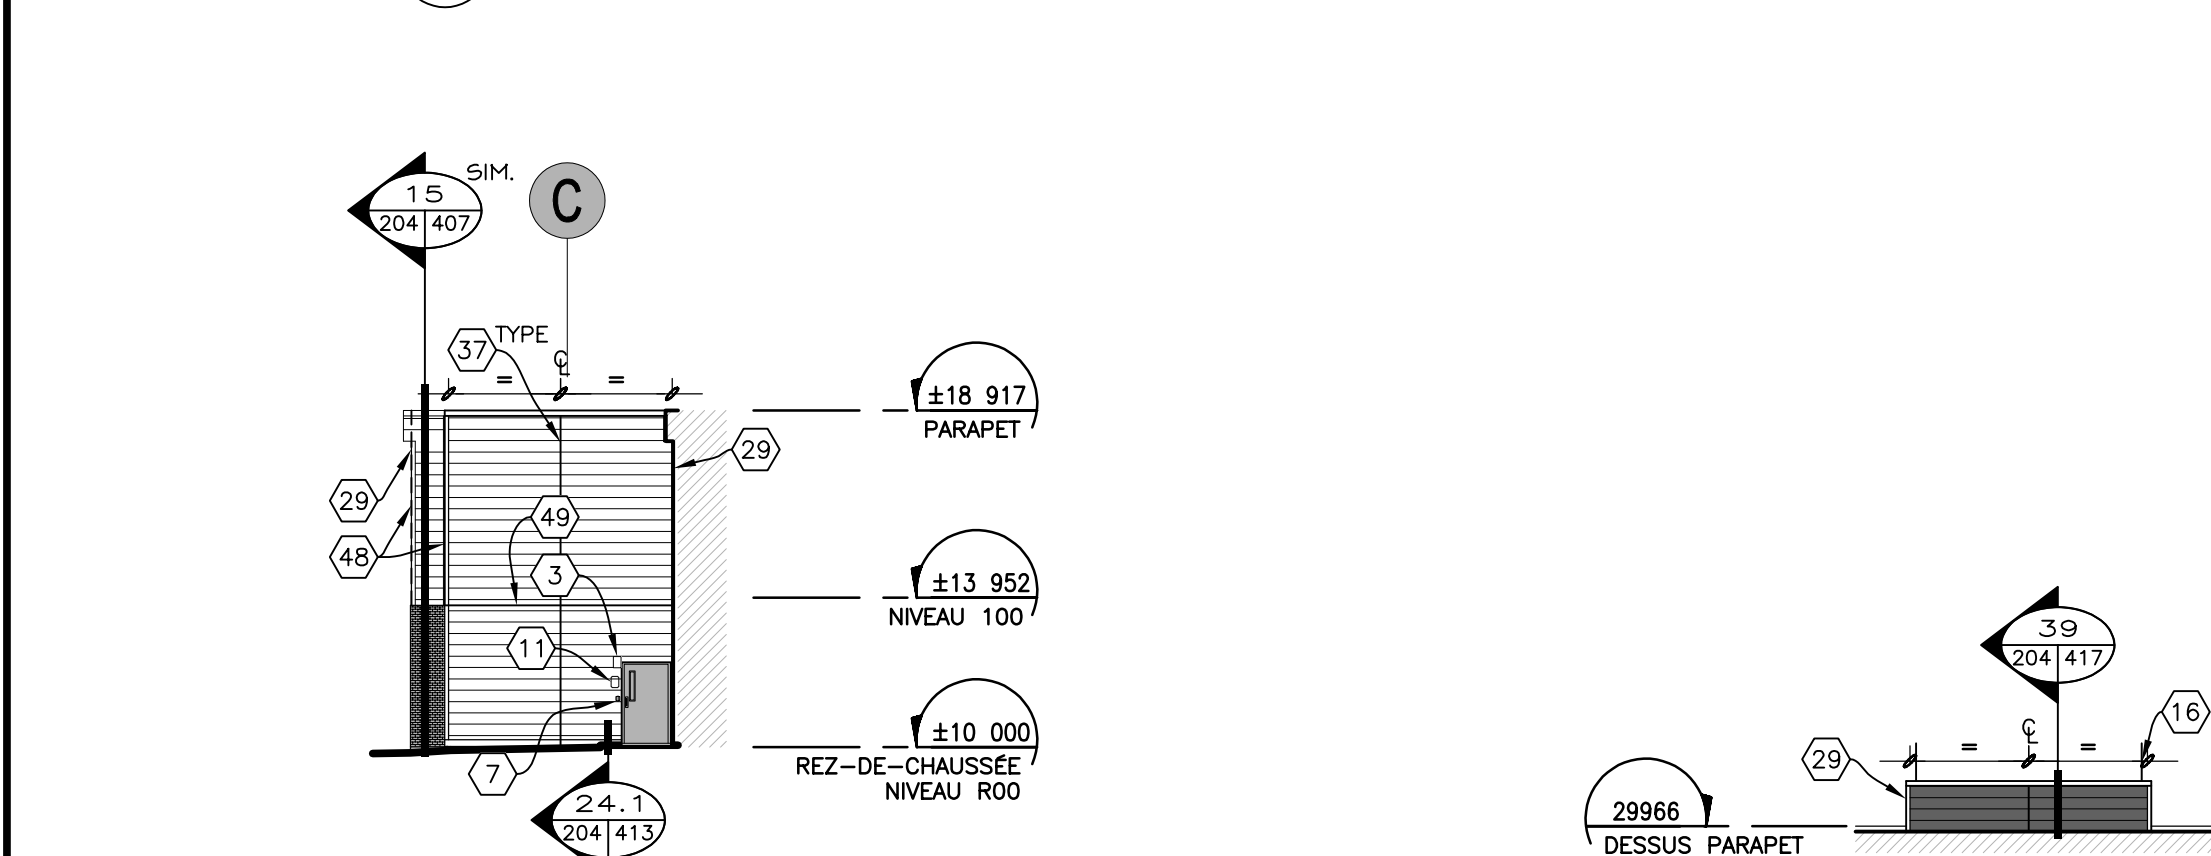


I ÉLEVATION OUEST PARTIELLE - CONSTRUCTION
1:200mm


K ÉLEVATION OUEST PARTIELLE - CONSTRUCTION
1:200mm



ÉLEVATION MARQUISE ENTRÉE PRINCIPALE

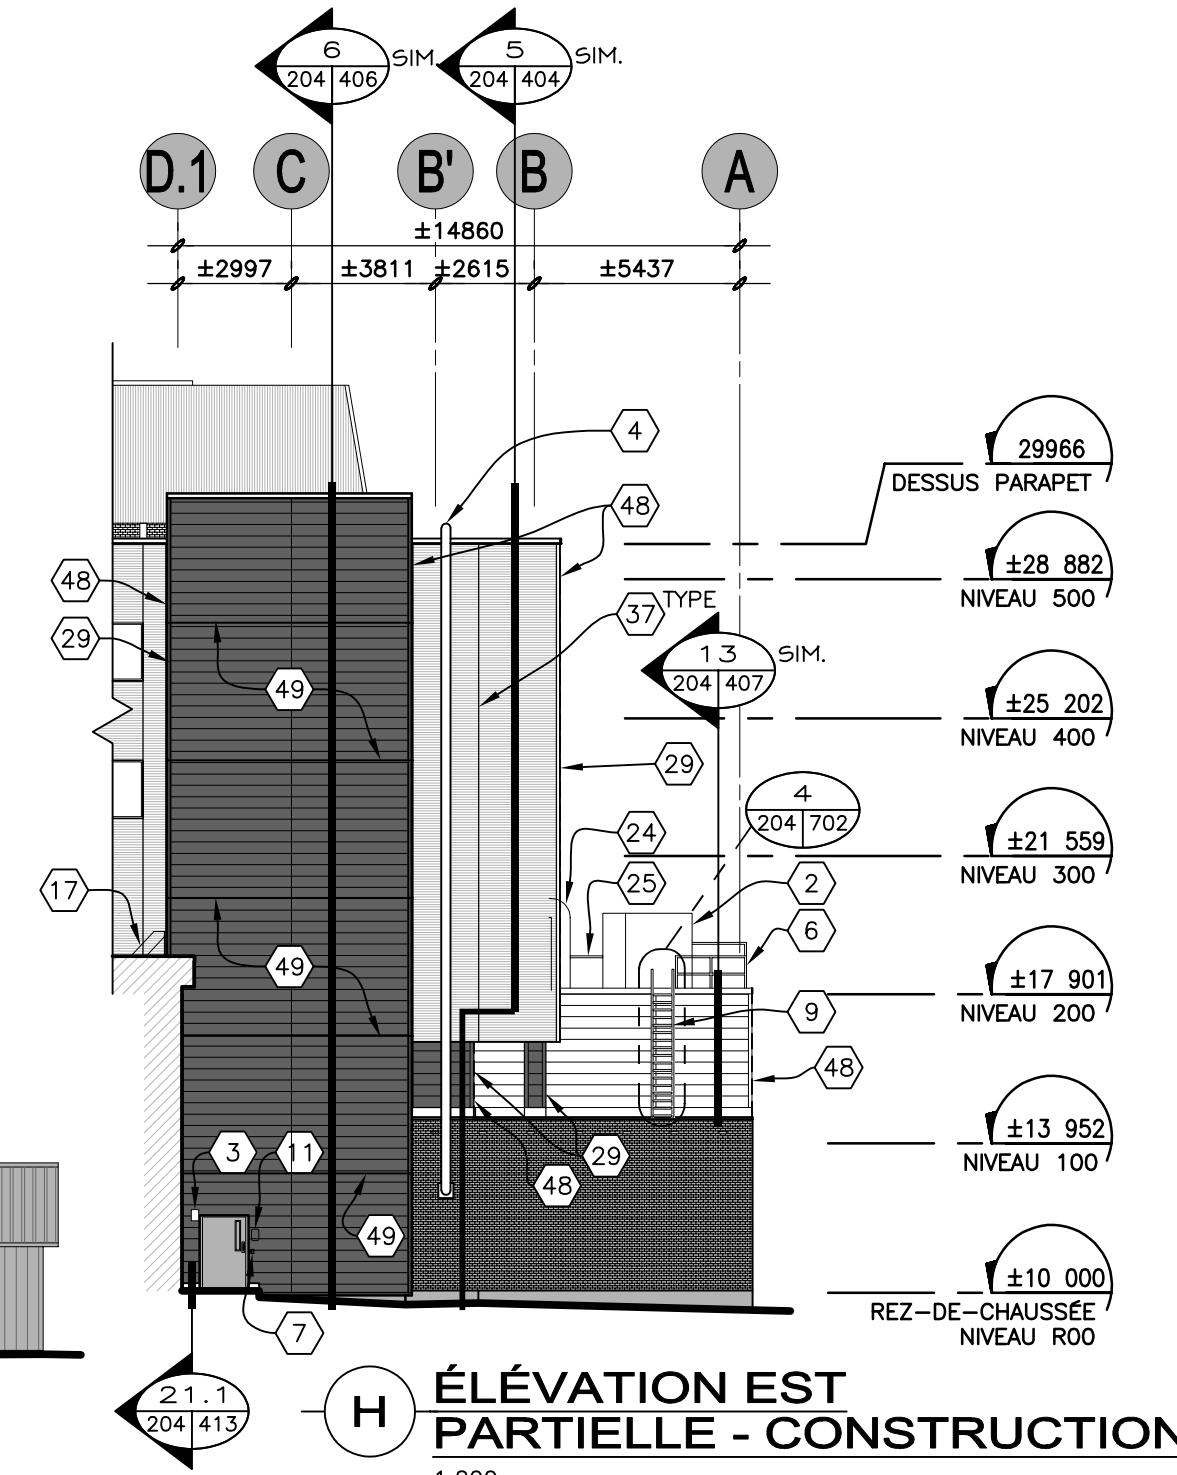

H ÉLEVATION EST PARTIELLE - CONSTRUCTION
1:200mm

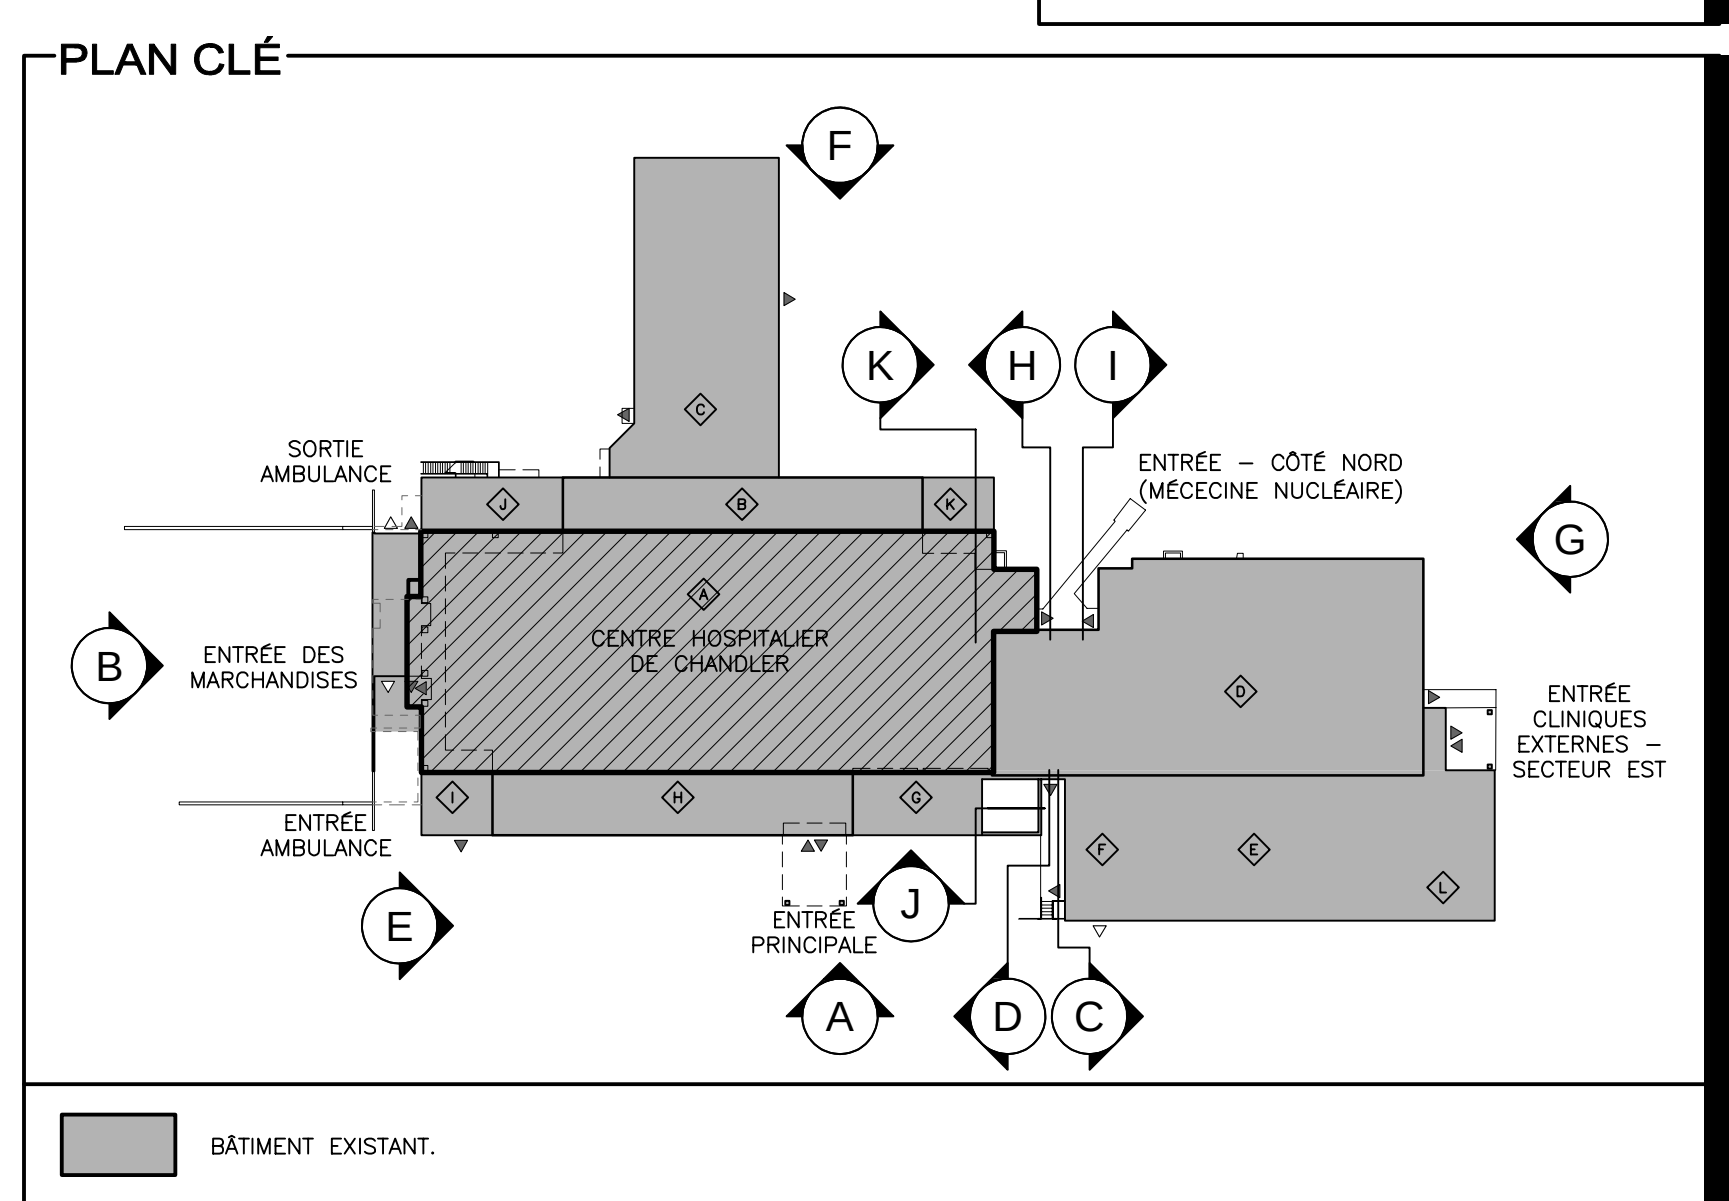

- ### NOTES
- NOUVELLE COMPOSITION ISOLÉE SUR LA COLONNE EXISTANTE, VOIR LE DÉTAIL #52 DE LA PAGE 420 ET LE DÉTAIL #25 DE LA PAGE 455.
 - MOULURE DE COIN, VOIR FEUILLE 205 POUR LE PROFIL.
 - GARGOUILLE EXISTANTE À NETTOYER.
 - TRAPPE D'ACCÈS MURALE EXISTANTE À CONSERVER.
 - PARÈMENT DE MAÇONNERIE DE BRIQUES EXISTANT À REINSTALLER, CRÉER DES ÉVÈNEMENTS DANS LES JOINTS DE L'AVANT-DERNIÈRE BRIQUE, À TOUTES LES 3 BRIQUES.
 - NOUVEL ESCALIER D'ISSUE, VOIR DÉTAILS DE LA FEUILLE 705.
 - NOUVELLE PERSIENNE DE 950 X 400mm, VOIR DÉTAIL 24 À LA FEUILLE 455.
 - GARDE-CORPS EXISTANT À CONSERVER EN PLACE ET À PROTÉGER PENDANT LES TRAVAUX.
 - MOULURE VERTICALE DE TRANSITION, VOIR FEUILLE 205.
 - NOUVELLE GARGOUILLE, VOIR DÉTAIL #1 SUR LA FEUILLE 306.
 - NOUVEAU CLAPET (ÉVÈN), VOIR DOCUMENTS D'INGÉNIERIE, VOIR DÉTAIL #12 À LA FEUILLE 205.
 - SOLIN EN ACIER ÉMAILLÉ, CAL 24, JOINTS AGRAFES. VOIR DÉTAIL #53 DE LA FEUILLE 420.
 - NOUVELLE PERSIENNE DE 2440 X 1800mm, VOIR DÉTAIL #61 À LA FEUILLE 422.
 - PERSIENNE EXISTANTE NON-PEINTE À REINSTALLER.
 - OBTURER UNE PARTIE DE L'OUVERTURE AU-DESSUS DE LA NOUVELLE PORTE PROJETÉE, VOIR LE DÉTAIL #14 SUR LA FEUILLE 607.
 - OUVERTURE EXISTANTE À OBTURER, VOIR DÉTAIL #22 DE LA FEUILLE 512.
 - NOUVEAU LUMINAIRE, VOIR DOCUMENTS D'INGÉNIERIE, VOIR DÉTAIL #8 À LA FEUILLE 205.
 - NOUVELLE TRAPPE D'ACCÈS, VOIR DÉTAIL #61 DE LA FEUILLE 422.
 - PLAQUE D'ACIER, VOIR DÉTAIL #7 À LA FEUILLE 604.
 - COMPARTIMENTATION VERTICALE DE L'ENVELOPPE.
 - SOLIN D'ÉGOUTTEMENT EN ACIER ÉMAILLÉ, VOIR LES DÉTAILS TYPE SUR LA FEUILLE 415.
 - CONDUIT EXISTANT, VOIR DOCUMENTS D'INGÉNIERIE, VOIR DÉTAIL #10 À LA FEUILLE 205.

- ### LÉGENDE DES ZONES
- A TOUR CHAMBRES (NIVEAU 200,300 ET 400) (1974).
 - B LABORATOIRE (NIVEAU 100)(1990).
 - C ARCHIVES (REZ-DE-CHAUSSEE)(2001).
 - D ADMINISTRATIVE (NIVEAU 100) (2005) ET CLINIQUES EXTERNES (REZ-DE-CHAUSSEE) (1974)
 - E ONCOLOGIE (REZ-DE-CHAUSSEE) (1974).
 - F IRM (REZ-DE-CHAUSSEE) (2007)
 - G BASILAIRE SUD-EST(1974)
 - H CLINIQUE CHIRURGIE D'UN JOUR (NIVEAU 100) (2005)ET URGENCE (REZ-DE-CHAUSSEE)
 - I BASILAIRE SUD-OUEST (1974)
 - J BASILAIRE NORD-OUEST (1974)
 - K BASILAIRE NORD-EST (1974)
 - L ONCOLOGIE (REZ-DE-CHAUSSEE) (2023)

- ### NOTES
- TOILE AMOVIBLE EXISTANTE À REINSTALLER.
 - APPAREIL D'ÉLECTRO-MÉCANIQUE ET SUPPORT EXISTANT, VOIR DOCUMENTS D'INGÉNIERIE.
 - LUMINAIRE EXISTANT, VOIR DOCUMENTS D'INGÉNIERIE. VOIR DÉTAIL #8 À LA FEUILLE 205.
 - CONDUIT EXISTANT, VOIR DOCUMENTS D'INGÉNIERIE.
 - PERSIENNE DE VENTILATION EXISTANTE REINSTALLÉE, VOIR DOCUMENTS D'INGÉNIERIE. LA PERSIENNE DOIT ÊTRE REPEINT, AVANT SON INSTALLATION, DE LA MÊME COULEUR QUE LE REVÊTEMENT DANS LEQUEL ELLE SERA INSTALLÉE.
 - GARDE-CORPS EXISTANT À REINSTALLER, VOIR FEUILLES DE LA SÉRIE 700 POUR LES TRAVAUX À EXÉCUTER SUR LE GARDE-CORPS AVANT SA REINSTALLATION.
 - LECTEUR DE CARTE/PUCE EXISTANT À REINSTALLER, VOIR INGÉNIEUR, VOIR DÉTAIL #4 À LA FEUILLE 205.
 - PRISE ÉLECTRIQUE EXISTANTE, VOIR DOCUMENTS D'INGÉNIERIE, VOIR DÉTAIL #4 À LA FEUILLE 205.
 - ÉCHELLE EXISTANTE À REINSTALLER, VOIR LES FEUILLES DE LA SÉRIE 700 POUR LES TRAVAUX À EXÉCUTER SUR L'ÉCHELLE AVANT SA REINSTALLATION.
 - CAMERA EXISTANTE À REINSTALLER, VOIR DOCUMENTS D'INGÉNIERIE, VOIR DÉTAIL #8 À LA FEUILLE 205.
 - AFFICHAGE EXISTANT À REINSTALLER.
 - COUSSIN GONFLABLE D'ÉTANCHÉITÉ POUR QUAI D'EMBARQUEMENT À REINSTALLER, VOIR DÉTAIL #6 SUR LA FEUILLE 603.
 - PERSIENNE DE VENTILATION EXISTANTE À REINSTALLER.
 - LETTRAGE RÉTROÉCLAIRÉ EXISTANT À REINSTALLER AU MÊME ENDROIT ET AVEC LES MÊMES ESPACEMENTS QUE L'EXISTANT, VOIR LES DOCUMENTS D'INGÉNIERIE POUR LE RACCORDEMENT ÉLECTRIQUE, VOIR DÉTAIL D'INTÉGRATION #9 SUR LA FEUILLE 205. LA STRUCTURE DU LETTRAGE DOIT ÊTRE REPEINT AVANT D'ÊTRE REINSTALLÉES.
 - GRILLE DE VENTILATION EXISTANTE POUR L'ENTREPLAFOND À REINSTALLÉE.
 - NOUVELLE PORTE ISOLÉ ET CADRE EN ACIER ISOLÉ AVEC BRIS THERMIQUE. PEINT.
 - ESCALIER EN ACIER EXISTANT À REINSTALLER SUR UN PANNEAU DE CAOUTCHOUC.
 - CRÉER DES ÉVÈNEMENTS À MAÇONNERIE DANS L'AVANT DERNIER RANG DE BRIQUES DU MUR EXISTANT, EN ÉVITANT LE JOINT DE MORTIER VERTICAL À TOUTES LES 3 BRIQUES.
 - SECTION DE GARDE-CORPS À MODIFIER, VOIR LES INTERVENTIONS À LA SÉRIE DE FEUILLES 700.
 - FILET EXISTANT À CONSERVER.
 - APPAREIL DE COMMUNICATION EXISTANT, VOIR DOCUMENTS D'INGÉNIERIE.
 - BOÎTE DE JONCTION ET FILAGE EXISTANT, VOIR DOCUMENTS D'INGÉNIERIE.
 - OUVERTURE EXISTANTE À OBTURER, VOIR DÉTAIL SIMILAIRE #2 DE LA FEUILLE 502.
 - NOUVEAU CONDUIT DE VENTILATION, VOIR DOCUMENTS D'INGÉNIERIE.
 - PLATEFORME ET GARDE-CORPS EN ACIER EXISTANT À REINSTALLER, VOIR LES FEUILLES DE LA SÉRIE 700 POUR LES TRAVAUX À EXÉCUTER SUR LA PLATEFORME ET LE GARDE-CORPS AVANT LEUR REINSTALLATION.
 - SORTIE D'ARROSAGE EXTÉRIEUR EXISTANTE, VOIR DOCUMENTS D'INGÉNIERIE, VOIR DÉTAIL #3 À LA FEUILLE 205.
 - DÉTECTEUR DE PRÉSENCE EXISTANT À REINSTALLER, VOIR DOCUMENTS D'INGÉNIERIE.

- ### LÉGENDE DES PAREMENTS
- PAREMENT D'ACIER CORRUGUÉ 22mm, TYPE 1. COULEUR BLANC CAMBRIDGE.
 - PAREMENT D'ACIER CORRUGUÉ 22mm, TYPE 2. COULEUR BLANC CAMBRIDGE.
 - PAREMENT DE DÉCLIN D'ALUMINIUM TYPE 3. COULEUR HICHOXY NATUREL.
 - PAREMENT D'ACIER AD300 SR TYPE 4. COULEUR GRIS RÉGENT.
 - PAREMENT D'ACIER AD300 SR TYPE 5. COULEUR GRIS CHARBON.

- ### LÉGENDE
- NOTE DESCRIPTIVE.
 - NIVEAU.
 - COUPE DE MUR.
 - DÉTAIL TYPE.
 - AXE EXISTANT.
 - NOUVEL AXE.
 - EXISTANT À CONSERVER.
 - JOINT D'EXPANSION À CONSERVER.

NE DOIT PAS SERVIR À L'EXÉCUTION

Le présent document est émis pour la seule fin identifiée. Son contenu est protégé par les droits d'auteur et toute reproduction ou modification, partielle ou totale, est interdite sans l'autorisation écrite de gagnon, letellier, cyr, ricard, mathieu, prouls, savard consortium d'architectes.

GLCRM | Proulx Savard |

GLCRM:
128, Avenue de la Cathédrale,
Bureau 201
Rimouski, QC, G5L 5H7
(418) 722-7655

2406, Ch. des Quatres-Bourgeois,
Bureau 100
Québec, QC, G1V 1W5
(418) 647-1700

Proulx Savard Architectes:
75, boul. Arthur-Buies Ouest,
Rimouski, QC G5L 5C2
(418) 723-5543

ARCHITECTURE

CONSULTANTS

DOSSIER No.	DATE	REVISIONS
24-107 / 1637-24	SEPTEMBRE 2024	

DESIGNATEUR (S)	DATE	REVISIONS
D.B. A.B. A.C. J.L.		

PROJET	PROPRIÉTAIRE
HÔPITAL DE CHANDLER, Chandler (Réfection de l'enveloppe)	Santé Québec

204

CONDITION REVÊTEMENT DE TYPE 1 CONDITION REVÊTEMENT DE TYPE 4

12 **DÉTAIL TYPE CLAPET (ÉVENT)**

203-204 205 1:10mm

10 DÉTAIL TYPE - CONDUIT MÉCANIQUE
203-204 205 1:10mm

7 DÉTAIL TYPE TRAPPE POUR SOFFITE
203-204 | 205 1:10mm

3 DÉTAIL TYPE ROBINET EXTÉRIEUR
203-204 | 205 1:10mm

3 DÉTAIL TYPE ROBINET EXTÉRIEUR
203-204 | 205 1:10mm

7 DÉTAIL TYPE TRAPPE POUR SOFFITE
203-204 | 205 1:10mm

11 DÉTAIL TYPE - PERCEMENT MÉTAUX-OUVRÉS

9 DÉTAIL ENSEIGNE LUMINEUSE
203-204 205 1:10mm

6 DÉTAIL PERSIENNE EN SOFFITE

2 ÉLEVATION TYPE - ALIGNEMENT MOULURES
203-204 205 1:20mm

DÉTAIL TYPE - SOLIN
1:5mm TÊTE DES OUVERTURES

MOULURE DE COIN
EXTÉRIEUR

MOULURE DE COIN
INTÉRIEUR

MOULURE DE TRANSITION
VERTICALE

SOLIN DE PARAPET
PÉRIMÉTRIQUE

SOLIN D'ALLÈGE
D'OUVERTURE

REVÊTEMENTS TYPES 1
ET 3

PROFILÉS D'ALUMINIUM TYPES

PROFILÉS D'ACIER TYPES

MOULURE D'EXTRÉMITÉ DE REVÊTEMENT

MOULURE DE JAMBAGE
D'OUVERTURE

MOULURE DE HAUT DE REVÊTEMENT TYPES 4 ET 5

MOULURE DE JONCTION
BAS DE MUR ET SOFFITE

SOLIN DE BAS DE
REVÊTEMENT SUR
FONDATION

MOULURE DE TÊTE
D'OUVERTURE

NOTES

- 1 AGRAFE CONTINUE EN ACIER GALVANISÉ CAL. 22.
- 2 NOUVEAU MOULURE EN ACIER ÉMAILLÉ CAL. 22, COULEUR AU CHOIX DE L'ARCHITECTE. VOIR LES DÉTAILS TYPES.
- 3 SOLIN EN ACIER ÉMAILLÉ, CAL.22, JOINTS AGRAFÉS.
- 4 ROBINET EXTÉRIEUR EXISTANT, VOIR DOCUMENTS D'INGÉNIEURIE.
- 5 MEMBRANE DE TYPE-1.
- 6 SCELLANT CONTINUE AU POURTOUR DE L'OUVRETURE.
- 7 CONDUIT EXISTANT POUR LE ROBINET EXTÉRIEUR. VOIR DOCUMENTS D'INGÉNIEURIE.
- 8 PRISE ÉLECTRIQUE OU LECTEUR DE CARTE. VOIR DOCUMENTS D'INGÉNIEURIE.
- 9 FILAGE EXISTANT, VOIR DOCUMENTS D'INGÉNIEURIE.
- 10 REMPLIR L'ESPACE D'ISOLANT DE FIBRE DE ROCHE.
- 11 SCELLANT SUR BOUDIN COMPRESSIBLE.
- 12 PLAQUE DE FIXATION EN ACIER GALVANISÉ 3mm D'ÉPAISSEUR DES DIMENSIONS APPROPRIÉES.
- 13 NOUVELLE BOTE DE JONCTION, VOIR DOCUMENTS D'INGÉNIEURIE.
- 14 NOUVEAU RACCORD, VOIR DOCUMENTS D'INGÉNIEURIE.
- 15 NOUVEAU FILAGE, VOIR DOCUMENTS D'INGÉNIEURIE.
- 16 OUVERTURE DE 300 X 300mm À FAIRE DANS LE MUR EXISTANT POUR L'INSTALLATION DE LA NOUVELLE TRAPPE D'ACCÈS.
- 17 NOUVELLE TRAPPE D'ACCÈS, VOIR LES PLANS DE SOFFITES POUR LE TYPE DE TRAPPE À UTILISER.
- 18 LUMINAIRE OU CAMÉRA EXISTANTS REINSTALLÉ, VOIR DOCUMENTS D'INGÉNIEURIE.
- 19 NOUVEAU CONDUIT, VOIR DOCUMENTS D'INGÉNIEURIE.
- 20 L EN ACIER GALVANISÉ 30 X 30mm.
- 21 BARRE EN "Z" VERTICALE 19mm INSTALLÉE DE CHAQUE CÔTÉ DU SUPPORT MÉTALLIQUE POUR FIXATION DE LA TÔLE DE FINITION.
- 22 SCELLANT DE FINITION, AU POURTOUR DE L'ÉLÉMENT, DE LA MÊME COULEUR QUE LE REVÊTEMENT ADJACENT.
- 23 SUPPORT MÉTALLIQUE, VOIR FEUILLES DE LA SÉRIE 700. COORDONNER L'EMPLACEMENT DE LA TÔLE DE FINITION ET DES MOULURES EN FONCTION DE L'EMPLACEMENT DES SUPPORTS MÉTALLIQUES.
- 24 TÔLE DE FINITION PLIÉE EN ACIER ÉMAILLÉ CAL.20, DE MÊME COULEUR QUE LE REVÊTEMENT ADJACENT.
- 25 CONDUIT EXISTANT À CONSERVER, VOIR DOCUMENTS D'INGÉNIEURIE.
- 26 EXTENSION DE CONDUIT, VOIR DOCUMENTS D'INGÉNIEURIE.
- 27 TÔLE D'ÉTANCHÉITE EN ACIER GALVANISÉ 100X100mm, CAL. 22.
- 28 ASSEMBLAGE DE COLOMBAGES SUR TOUT LE PÉRIMÈTRE DE L'OUVRETURE, VOIR DOCUMENTS D'INGÉNIEURIE.
- 29 ISOLANT SEMI-RIGIDE DE FIBRE DE ROCHE, 152mm D'ÉPAISSEUR.
- 30 MOUSTIQUEAIRE.
- 31 RUBAN AUTOCOLLANT.
- 32 SCELLANT D'ÉTANCHÉITE AU BITUME AU POURTOUR DU CONDUIT.
- 33 BARRE EN "Z" OU EN "J" EN ACIER GALVANISÉ CAL.18.
- 34 CONTRAPLAQUE TYPE EXTÉRIEUR 19mm D'ÉPAISSEUR RECROUVERTE D'UNE MEMBRANE DE TYPE 1.
- 35 PLAGE EN "L" EN ACIER GALVANISÉ 38X38mm CAL.18.
- 36 PLAGE EN "J" EN ACIER GALVANISÉ 75X75X38mm CAL.16.
- 37 PERSIENNE EXISTANTE REINSTALLÉE, À PEINDRE, VOIR DOCUMENTS D'INGÉNIEURIE POUR LE RACCORDEMENT AU CONDUIT EXISTANT.
- 38 NOUVEAU VENTILATION EXISTANT, VOIR DOCUMENTS D'INGÉNIEURIE.
- 39 LETTRAGE LUMINEUX EXISTANT REINSTALLÉ SUR LE SUPPORT MÉTALLIQUE, VOIR DOCUMENTS D'INGÉNIEURIE POUR LE RACCORDEMENT ÉLECTRIQUE.
- 40 SUPPORT MÉTALLIQUE EXISTANT DU LETTRAGE REINSTALLÉ AU MÊME EMBLEMENT. REPRISE LES SUPPORTS AVANT L'INSTALLATION.
- 41 NOUVEAU CLAPET (EVENT), VOIR DOCUMENTS D'INGÉNIEURIE.

NOTE GÉNÉRALE :
L'ENSEMBLE DES MOULURES ET SOLINS DOIVENT ÊTRE DE LA MÊME COULEUR QUE LE REVÊTEMENT ADJACENT, SAUF INDICATION CONTRAIRE AUX DESSINS.

NE DOIT PAS SERVIR À L'EXÉCUTION

Le présent document est émis pour la seule fin identifiée. Son contenu est protégé par les droits d'auteur et toute reproduction ou modification, partielle ou totale, est interdite sans l'autorisation écrite de gagnon, letellier, cyr, ricard, mathieu, proulx, savard consortium d'architectes.




GLCRM | Proulx Savard

GLCRM:
128, Avenue de la Cathédrale,
Bureau 201
Rimouski, QC, G5L 5H7
(418) 722-7655



2406, Ch. des Quatres-Bourgeois,
Bureau 100
Québec, QC, G1V 1W5
(418) 647-1700

Proulx Savard Architectes:
75, boul. Arthur-Buies Ouest,
Rimouski QC G5L 5C2
(418) 723-5543

ARCHITECTURE

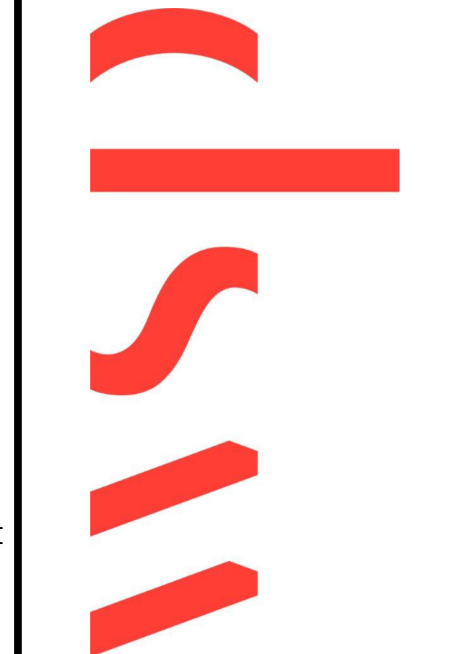

CONSULTANTS

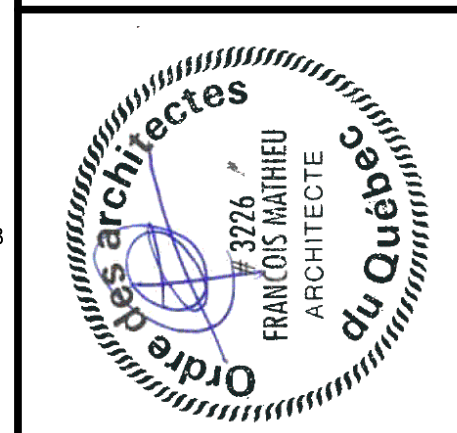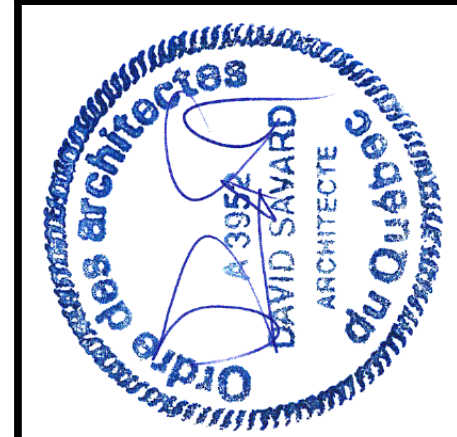[illegible]



ATTACHE CÂBLE PARATONNERRE



PHOTO RÉFÉRENCE #1



PHOTO RÉFÉRENCE #2



PHOTO RÉFÉRENCE #3

NOTES

- 32 AÉRATEUR D'ENTRETOIT À DÉMOLIR.
33 SECTION DU SYSTÈME DE TOITURE EXISTANT À DÉMOLIR POUR L'INSTALLATION DES VENTILATEURS D'ENTRETOIT. DIMENSIONS SELON LE TYPE, VOIR LÉGENDE ET PLAN DE CONSTRUCTION À LA PAGE 302. PRÉVOIR DE DÉGRANULER LA MEMBRANE DE ±305mm, VOIR DÉTAIL 2 SUR LA FEUILLE 305.
34 TRAPPE D'ACCÈS À L'ENTRETOIT ET BASE DE TOIT À DÉMOLIR, MODIFIER L'OUVERTURE POUR L'INSTALLATION D'UN VENTILATEUR D'ENTRETOIT, DIMENSIONS SELON LE TYPE, VOIR LÉGENDE ET PLAN DE CONSTRUCTION À LA PAGE 302.

NOTES

- 1 PARAPET EXISTANT À DÉMOLIR. COUPER LA MEMBRURE SUPÉRIEURE DES FERMES DE TOIT, VOIR DÉTAILS EN COUPE TYPES DE LA SÉRIE DE FEUILLES 400.
2 SECTION DU SYSTÈME DE TOITURE EXISTANT À DÉMOLIR, VOIR DÉTAILS DES SÉRIES DE FEUILLES 300 ET 400. PRÉVOIR DE DÉGRANULER LA MEMBRANE DE FINITION EXISTANTE SUR ±305mm.
3 TRAPPE D'ACCÈS À L'ENTRETOIT EXISTANTE À DÉMOLIR.
4 SÉPARATION COUPE-FEU EN GYPSE EXISTANTE À CONSERVER.
5 SYSTÈME DE PARATONNERRE À DÉMOLIR (POTEAUX ET CÂBLES), PRÉVOIR D'ENLEVER LES ATTACHES QUI FIXE LES FILS, VOIR LA PHOTO DE RÉFÉRENCE. BOUCHER TOUS LES TROUS CRÉER PAR LE RETRAIT DES FIXATIONS DANS LA TOITURE EXISTANTE CONSERVÉE.
6 REVÊTEMENT MURAL SUR L'ÉCRAN ARCHITECTURALE À DÉMOLIR, VOIR COUPES DE LA SÉRIE DE FEUILLES 400.
7 CONDUIT DE VENTILATION EXISTANT, VOIR DOCUMENTS D'INGÉNIERIE.
8 CONDUIT EXISTANT, VOIR DOCUMENTS D'INGÉNIERIE.
9 APPAREIL D'ÉLECTRO-MÉCANIQUE ET SUPPORT EXISTANT, VOIR DOCUMENTS D'INGÉNIERIE.
10 ESCALIER EN ACIER EXISTANT À RETIRER ET ENTREPOSER POUR REINSTALLATION FUTURE.
11 GARGOUILLE EXISTANT À DÉMOLIR, VOIR DÉTAIL TYPE 3 À LA FEUILLE 306.
12 SECTION DU SYSTÈME DE TOITURE EXISTANTE À DÉMOLIR POUR LES TRAVAUX DE STRUCTURE, SUR ±610mm DE LARGEUR LE LONG DU MUR, VOIR DÉTAILS DE SÉRIE DE FEUILLES 400. PRÉVOIR DE DÉGRANULER LA MEMBRANE DE FINITION EXISTANTE SUR ±305mm.
13 AÉRATEUR D'ENTRETOIT EXISTANT À CONSERVER.
14 DRAIN EXISTANT, VOIR DOCUMENTS D'INGÉNIERIE.
15 EVENT EXISTANT, VOIR DOCUMENTS D'INGÉNIERIE.
16 COL DE CYGNE POUR CONDUIT FLEXIBLE À DÉMOLIR, VOIR DOCUMENTS D'INGÉNIERIE.
17 TAPIS DE CAOUTCHOUC À RETIRER TEMPORAIREMENT.
18 BOÎTE À MASTIC ET ANCRAGE DES HAUBANS À DÉMOLIR.
19 SYSTÈME DE CÂBLE CHAUFFANT À DÉSINSTALLER ET ENTREPOSER PENDANT LES TRAVAUX, VOIR DOCUMENTS D'INGÉNIERIE.
20 VENTILATEUR EXTRACTEUR D'AIR MÉCANIQUE EXISTANT, VOIR DOCUMENTS D'INGÉNIERIE.
21 TRAPPE D'ACCÈS EXISTANTE ET BASE DE TOIT À DÉMOLIR.
22 SÉPARATEUR DE BASSIN EXISTANT À CONSERVER.
23 UNITÉ DE VENTILATION, VOIR DOCUMENTS D'INGÉNIERIE.
24 BASE POUR LE PASSAGE DE CONDUITS EXISTANTS À CONSERVER.
25 BASE DE BOIS AVEC SUPPORT EXISTANTS À CONSERVER.
26 SECTION DU SYSTÈME DE TOITURE EXISTANT À DÉMOLIR 915 X 915mm POUR AVOIR ACCÈS À LA COMPARTIMENTATION EXISTANTE. PRÉVOIR DE DÉGRANULER LA MEMBRANE DE ±305mm, VOIR DÉTAIL 1 SUR LA FEUILLE 306.
27 FASCIA À DÉMOLIR. COUPER LE SOLIN ET LE BÂTI DE BOIS SUR LE DESSUS DU PARAPET, VOIR DÉTAILS EN COUPE TYPES DE LA SÉRIE DE FEUILLES 400.
28 FASCIA À DÉMOLIR. SOLIN DE PARAPET À COUPER, VOIR DÉTAILS EN COUPE TYPES DE LA SÉRIE DE FEUILLES 400.
29 PARAPET DE BRIQUE À DÉMOLIR. COUPER LA MEMBRURE SUPÉRIEURE DES FERMES DE TOIT, VOIR DÉTAILS EN COUPE TYPES DE LA SÉRIE DE FEUILLES 400.
30 SOLIN À COUPER, VOIR DÉTAILS EN COUPE TYPES DE LA SÉRIE DE FEUILLES 400.
31 EVENT À DÉPLACER, VOIR DOCUMENTS D'INGÉNIERIE.




GLCRM | Proulx Savard |

GLCRM:
128, Avenue de la Cathédrale,
Bureau 201
Rimouski, QC, G5L 5H7
(418) 722-7655


2406, Ch. des Quatres-Bourgeois,
Bureau 100
Dorval, QC, H9V 1W5
(418) 647-1700

Proulx Savard Architectes:
75, boul. Arthur-Buies Ouest,
Rimouski QC G5L 5C2
(418) 722-5543

ARCHITECTURE

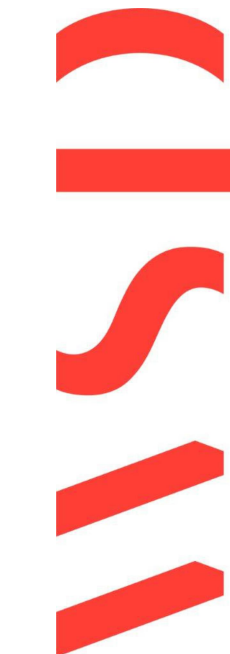

CONSULTANTS

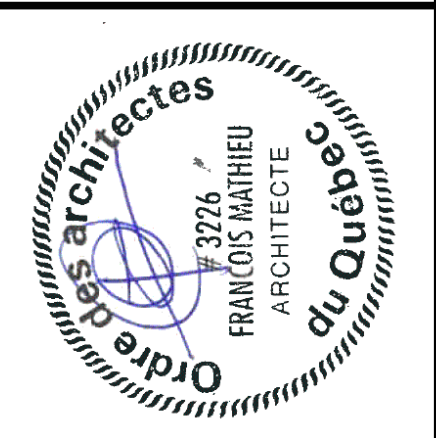

LÉGENDE

- (X) NOTE DESCRIPTIVE.
(X) AXE EXISTANT.
(NS) NOUVEL AXE.
EXISTANT À CONSERVER.
----- FASCIA OU SOLIN À DÉMOLIR.
===== PARAPET À DÉMOLIR.
(X/XXX/XXX) COUPE DE MUR.
(X/XXX/XXX) DÉTAIL TYPE.
----- ZONE DE DÉMOLITION DE TOITURE.
----- ZONE DE RECONSTRUCTION DE TOITURE.
----- NOUVEAU PARAPET.
----- NOUVELLE PORTE.
----- NOUVELLE COMPARTIMENTATION DANS L'ENTRETOIT.
----- COMPARTIMENTATION EXISTANTE DANS L'ENTRETOIT À COMPLÉTER.

TYPE DE VENTILATEUR D'ENTRETOIT
TYPE A: CABANON DE VENTILATION 813X813
TYPE B: CABANON DE VENTILATION 660X660
TYPE C: VENTILATEUR 450X450
TYPE D: VENTILATEUR EXISTANT

NE DOIT PAS SERVIR À L'EXÉCUTION

Le présent document est émis pour la seule fin identifiée. Son contenu est protégé par les droits d'auteur et toute reproduction ou modification, partielle ou totale, est interdite sans l'autorisation écrite de gagnon, letellier, cyr, ricard, mathieu, proulx, savard consortium d'architectes.

BESIGN PLAN DES TOITURES DÉMOLITION	DOSSIER No. 24-107 / 1657-24		DATE SEPTEMBRE 2026		REVISIONS
	DESIGNATEUR(S) D.B., A.C., J.L.	ÉCHELLE	INDIQUÉE		
PROJET HÔPITAL DE CHANDLER, Chandler (Réfection de l'enveloppe)	05	2024-09-04	DÉFINITIVES POUR SOUMISSION		
	06	2024-08-21	DÉFINITIVES 100% POUR APPROBATION		
	03	2024-08-03	DÉFINITIVES 80% POUR APPROBATION		
	02	2024-05-14	DÉFINITIVES 40% POUR APPROBATION		
	01	2024-02-27	PRÉLIMINAIRES 20% POUR APPROBATION		
PROPRIÉTAIRE Santé Québec	No	DATE			

NOTES

- (26) BASE POUR LE PASSAGE DE CONDUIT ÉLECTRIQUE EXISTANTE À CONSERVER.
- (27) UNITÉ DE VENTILATION, VOIR DOCUMENTS D'INGÉNÉRIE.
- (28) NOUVEAU SOLIN SUR LE PARAPET EXISTANT, VOIR DÉTAILS DE LA SÉRIE DE FEUILLES 400.
- (29) INSTALLER UN TAPIS DE CAOUTCHOUC SOUS L'ESCALIER DE 1525 X 1525mm.
- (30) NOUVEAU BÂTI ISOLÉ SUR LE PARAPET EXISTANT ET NOUVELLES MEMBRANES, VOIR DÉTAILS EN COUPE TYPES DE LA SÉRIE DE FEUILLES 400.
- (31) PROLONGEMENT DU PARAPET EXISTANT ET NOUVEAU CAPAGE DE TOLE, VOIR DÉTAILS EN COUPE TYPES DE LA SÉRIE DE FEUILLES 400.
- (32) NOUVEAU PARAPET INTRAMURAL, VOIR DÉTAILS EN COUPE TYPES DE LA SÉRIE DE FEUILLES 400.
- (33) ÉVENT DÉPLACÉ, VOIR DOCUMENTS D'INGÉNÉRIE.

NOTES

- (1) NOUVEAU PARAPET, VOIR DÉTAILS DE LA SÉRIE DE FEUILLES 400.
- (2) REPRISSE DU SYSTÈME DE TOITURE, VOIR DÉTAILS DE LA SÉRIE DE FEUILLES 400.
- (3) NOUVELLE TRAPPE D'ACCÈS INCOMBUSTIBLE À L'ENTRETOIT DE 1120mm X 520mm DE HAUTEUR.
- (4) NOUVELLE COMPARTIMENTATION DANS L'ENTRETOIT EN PANNEAU DE GYPSE TYPE "X" 13mm FIXÉ SUR UN CÔTÉ D'UNE FERMÉ DE TÔIT SUR TOUTE LA HAUTEUR, SCÉLER AU POURTOUR À L'AIDE DE SCÉLLANT IGNIFUGE. RETIRER L'URÉTHANE SUR LA LARGEUR REQUISSE POUR RÉALISER LA SÉPARATION COUPE-FEU. VOIR DÉTAIL #4 À LA PAGE 305.
- (5) NOUVEAU VENTILATEUR D'ENTRETOIT, PRÉVOIR UNE NOUVELLE BASE EN CONTREPLAQUÉ 19mm TYPE EXTERIEUR RECOUVERTE DU SYSTÈME DE MEMBRANE ELASTOMÈRE, DIMENSION SELON LE TYPE, VOIR LÉGENDE, MODIFIER ET/OU RAGRÉER L'OUVERTURE DANS LE PONTAGE DE BOIS, VOIR DÉTAIL 1 SUR LA FEUILLE 306.
- (6) NOUVEAU REVÊTEMENT MURAL SUR L'ÉCRAN ARCHITECTURALE, VOIR COUPES DE LA SÉRIE DE FEUILLES 400.
- (7) CONDUIT DE VENTILATION EXISTANT, VOIR DOCUMENTS D'INGÉNÉRIE.
- (8) CONDUIT EXISTANT, VOIR DOCUMENTS D'INGÉNÉRIE.
- (9) APPAREIL D'ÉLECTRO-MÉCANIQUE ET SUPPORT EXISTANT, VOIR DOCUMENTS D'INGÉNÉRIE.
- (10) ESCALIER EN ACIER EXISTANT À REINSTALLÉ, FIXER LES AILETTES DE L'ESCALIER DANS LES BARRES Z DU MUR, VOIR DÉTAILS DE LA SÉRIE DE FEUILLES 700.
- (11) NOUVELLE GARGOUILLE, VOIR DÉTAIL #3 À LA PAGE 306.
- (12) CHEVAUCHER LA NOUVELLE MEMBRANE DE FINITION DE 305mm SUR CELLE EXISTANTE, DÉGRANULER LA MEMBRANE EXISTANTE AU PRÉALABLE.
- (13) AÉRATEUR D'ENTRETOIT EXISTANT À CONSERVER.
- (14) DRAIN EXISTANT, VOIR DOCUMENTS D'INGÉNÉRIE.
- (15) ÉVENT EXISTANT, VOIR DOCUMENTS D'INGÉNÉRIE.
- (16) NOUVEAU VENTILATEUR D'ENTRETOIT, PRÉVOIR UNE NOUVELLE BASE EN CONTREPLAQUÉ 19mm TYPE EXTERIEUR RECOUVERTE DU SYSTÈME DE MEMBRANE ELASTOMÈRE, VOIR DÉTAIL TYPE 2 DE LA FEUILLE 305, DIMENSIONS SELON LE TYPE, VOIR LÉGENDE.
- (17) NOUVELLE PORTE D'ACCÈS EN CONTREPLAQUÉ DANS L'ENTRETOIT DE ±800 X ± 500mm, AVEC CHARNIERE À RESSORT ET SERRURE FONCTION PASSAGE. PORTE : CONTREPLAQUÉ 19mm, FOURRURE DE 19 X 64mm AU PÉRIMÈTRE DE LA PORTE. JAMBAGE ET TÊTE DE LA PORTE : PRÉVOIR 38 X 64mm POUR FERMER L'OUVERTURE.
- (18) REPRISSE DU SYSTÈME DE TOITURE SUITE AUX TRAVAUX DE STRUCTURE, VOIR DÉTAILS DE LA SÉRIE DE FEUILLES 400.
- (19) SÉPARATION COUPE-FEU EN GYPSE TYPE "X" 13mm EXISTANTE À COMPLÉTER. LE GYPSE DOIT ÊTRE CONTINU DE LA DALLE DE BÉTON JUSQU'AU CONTREPLAQUÉ. SCÉLER AU POURTOUR DE CHACUN DES ÉLÉMENTS DE STRUCTURE À L'AIDE DE SCÉLLANT IGNIFUGE. RETIRER L'URÉTHANE SUR LA DALLE POUR INSTALLER LA SÉPARATION COUPE-FEU. INSTALLER UNE PIÈCE DE BOIS 38mm VIS-À-VIS LES JOINTS NON APPUYÉS DES PANNEAUX.
- (20) TAPIS DE CAOUTCHOUC À REINSTALLER.
- (21) SYSTÈME DE CÂBLE CHAUFFANT À REINSTALLER, VOIR DOCUMENTS D'INGÉNÉRIE.
- (22) BASE DE BOIS AVEC SUPPORT EXISTANTS À CONSERVER.
- (23) VENTILATEUR EXTRACTEUR D'AIR MÉCANIQUE EXISTANT, VOIR DOCUMENTS D'INGÉNÉRIE.
- (24) ABROGÉ
- (25) SÉPARATEUR DE BASSIN EXISTANT À CONSERVER.

LÉGENDE

- (X) NOTE DESCRIPTIVE.
- (X) AXE EXISTANT.
- (NS) NOUVEL AXE.
- EXISTANT À CONSERVER.
- FASCIA OU SOLIN À DÉMOLIR.
- ===== PARAPET À DÉMOLIR.
- (X/XXX/XXX) COUPE DE MUR.
- (X/XXX/XXX) DÉTAIL TYPE.
- ZONE DE DÉMOLITION DE TOITURE.
- ZONE DE RECONSTRUCTION DE TOITURE.
- NOUVEAU PARAPET.
- NOUVELLE PORTE.
- NOUVELLE COMPARTIMENTATION DANS L'ENTRETOIT.
- COMPARTIMENTATION EXISTANTE DANS L'ENTRETOIT À COMPLÉTER.
- TYPE DE VENTILATEUR D'ENTRETOIT
- TYPE A: CABANON DE VENTILATION 813X813
- TYPE B: CABANON DE VENTILATION 660X660
- TYPE C: VENTILATEUR 450X450
- TYPE D: VENTILATEUR EXISTANT

NE DOIT PAS SERVIR À L'EXÉCUTION

Le présent document est émis pour la seule fin identifiée. Son contenu est protégé par les droits d'auteur et toute reproduction ou modification, partielle ou totale, est interdite sans l'autorisation écrite de gagnon, letellier, cyr, ricard, mathieu, proulx, savard consortium d'architectes.




GLCRM | Proulx Savard |

GLCRM:
178, Avenue de la Cathédrale,
Bureau 201
Rimouski, QC, G5L 5H7
(418) 722-7655


2406, Ch. des Quatre-Bourgeois,
Bureau 100
Québec, QC, G1V 1W5
(418) 647-1700

Proulx Savard Architectes:
75, boul. Arthur-Buies Ouest,
Rimouski, QC G5L 5C2
(418) 723-5543

ARCHITECTURE

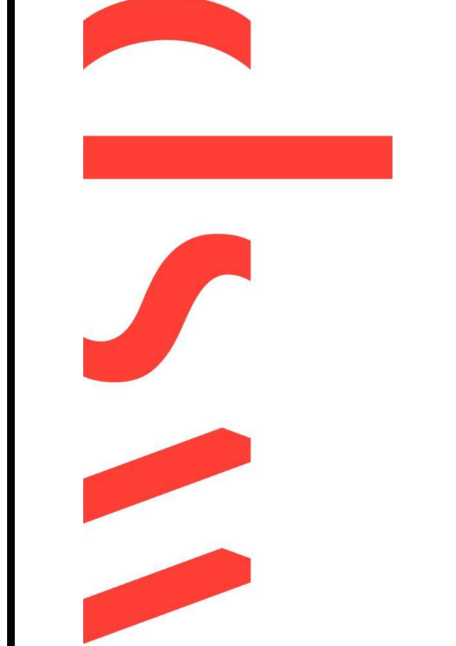


CONSULTANTS

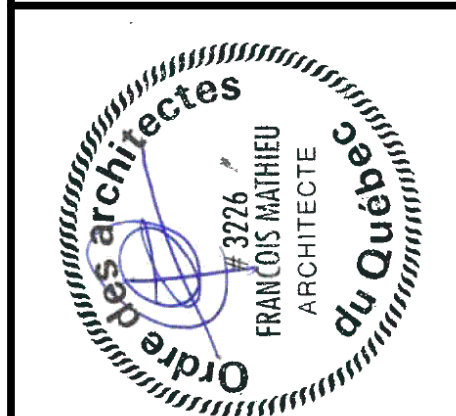


DOSSIER No.	DATE	DESIGNATEUR (S)	DB, A.C. J.L.	ÉCHELLE	INDICÉE	DATE	No	RÉVISIONS
24-107 / 1657-24	SEPTEMBRE 2024							
PROJET	HÔPITAL DE CHANDLER, Chandler (Réfection de l'enveloppe)	PROPRIÉTAIRE	Santé Québec	05	2024-09-04	04	03	02
PROJET	HÔPITAL DE CHANDLER, Chandler (Réfection de l'enveloppe)	PROPRIÉTAIRE	Santé Québec	06	2024-08-21	05	04	03
PROJET	HÔPITAL DE CHANDLER, Chandler (Réfection de l'enveloppe)	PROPRIÉTAIRE	Santé Québec	07	2024-05-14	06	05	04
PROJET	HÔPITAL DE CHANDLER, Chandler (Réfection de l'enveloppe)	PROPRIÉTAIRE	Santé Québec	08	2024-02-27	07	06	05

302

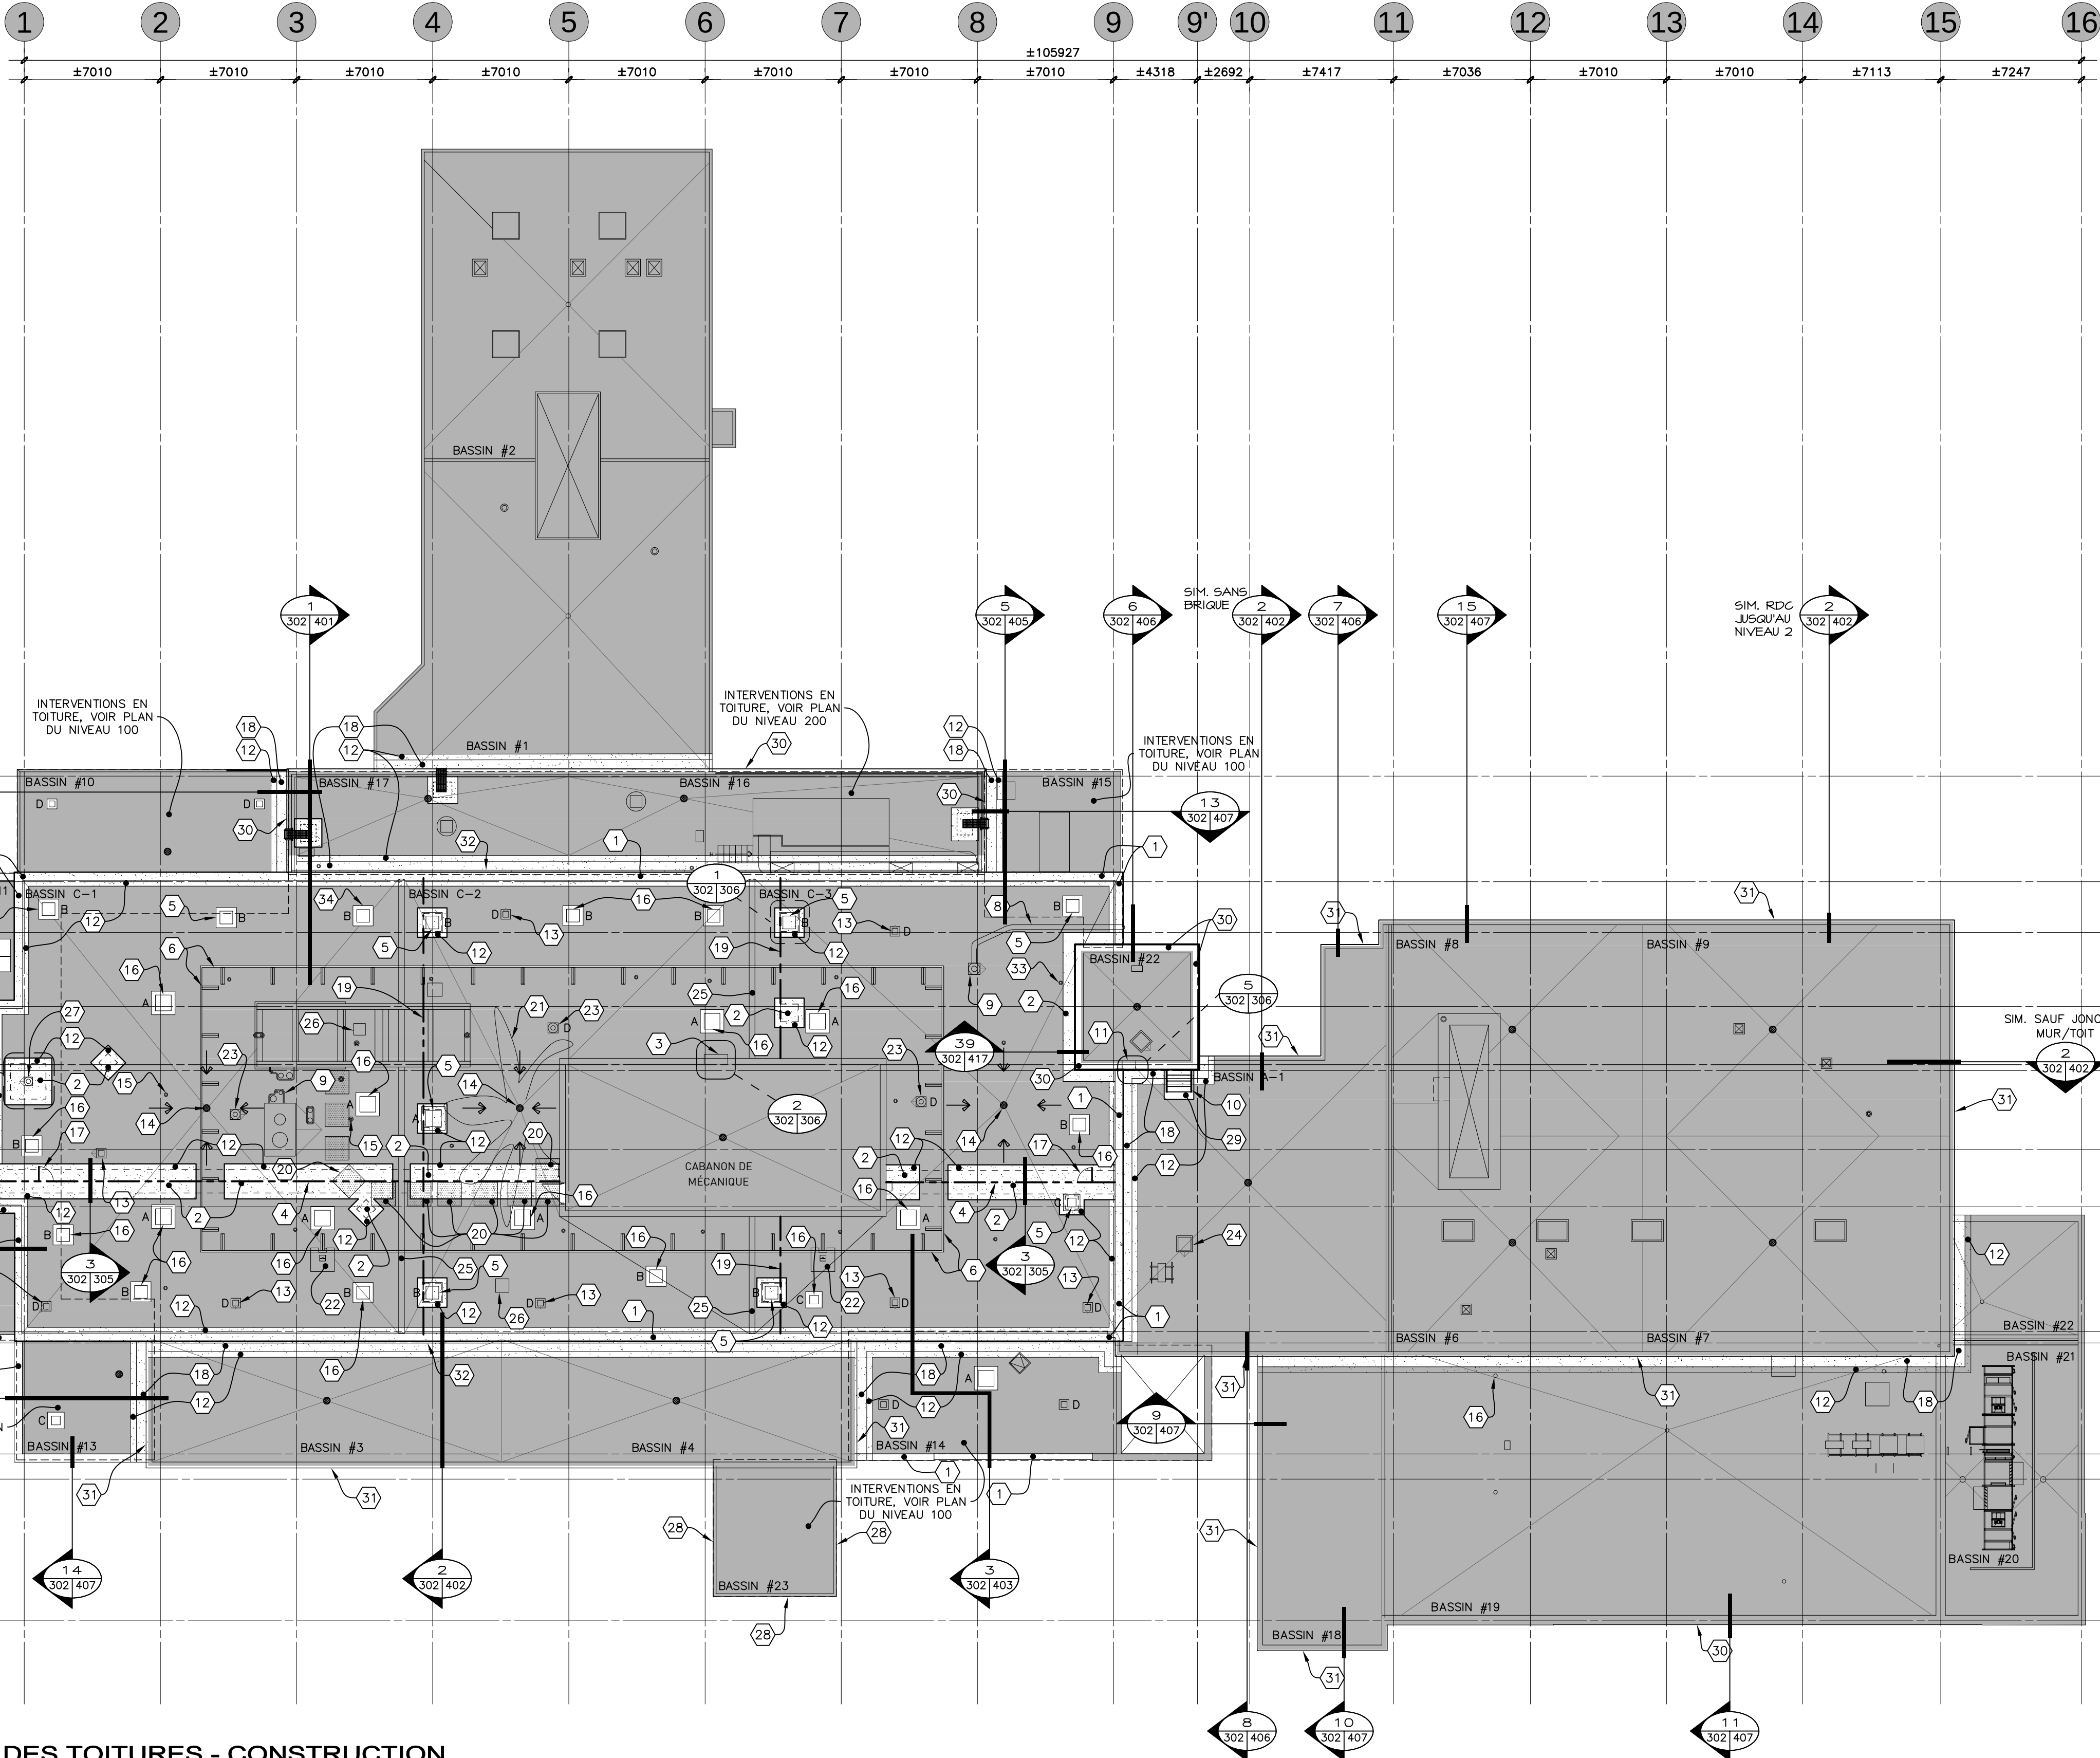


PLAN DES TOITURES - CONSTRUCTION

1:200mm

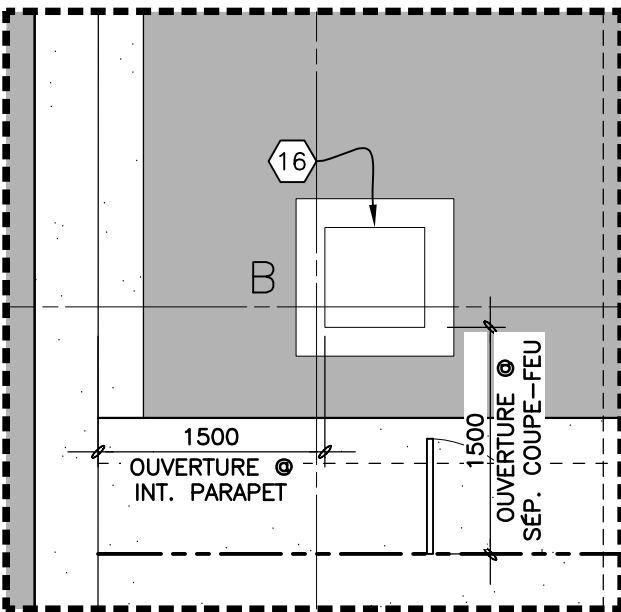


POSITION TYPE VENTILATEUR

1:50mm

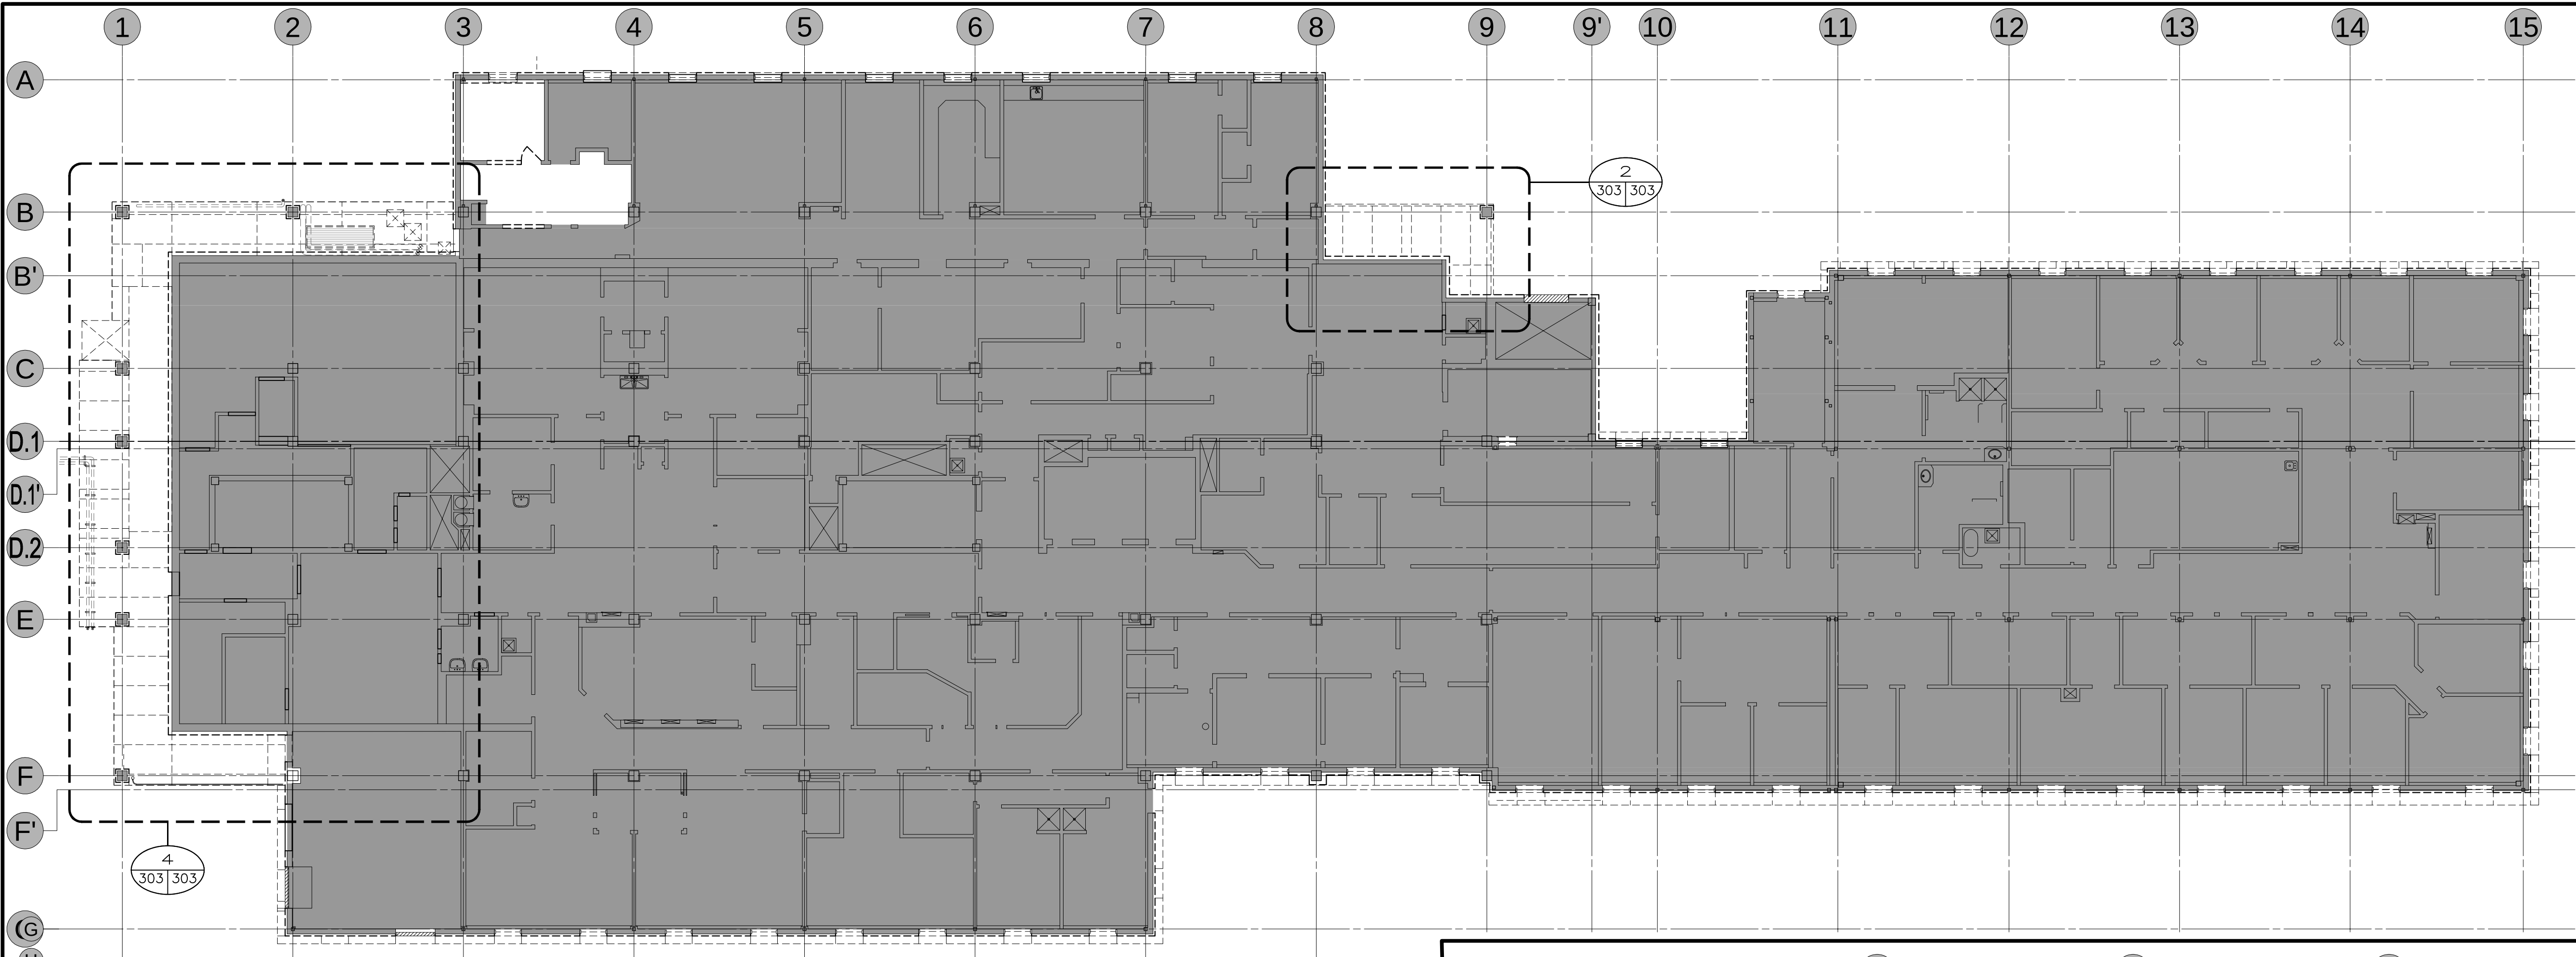


PLAN DES SOFFITES DU NIVEAU 100 DÉMOLITION

1:150mm

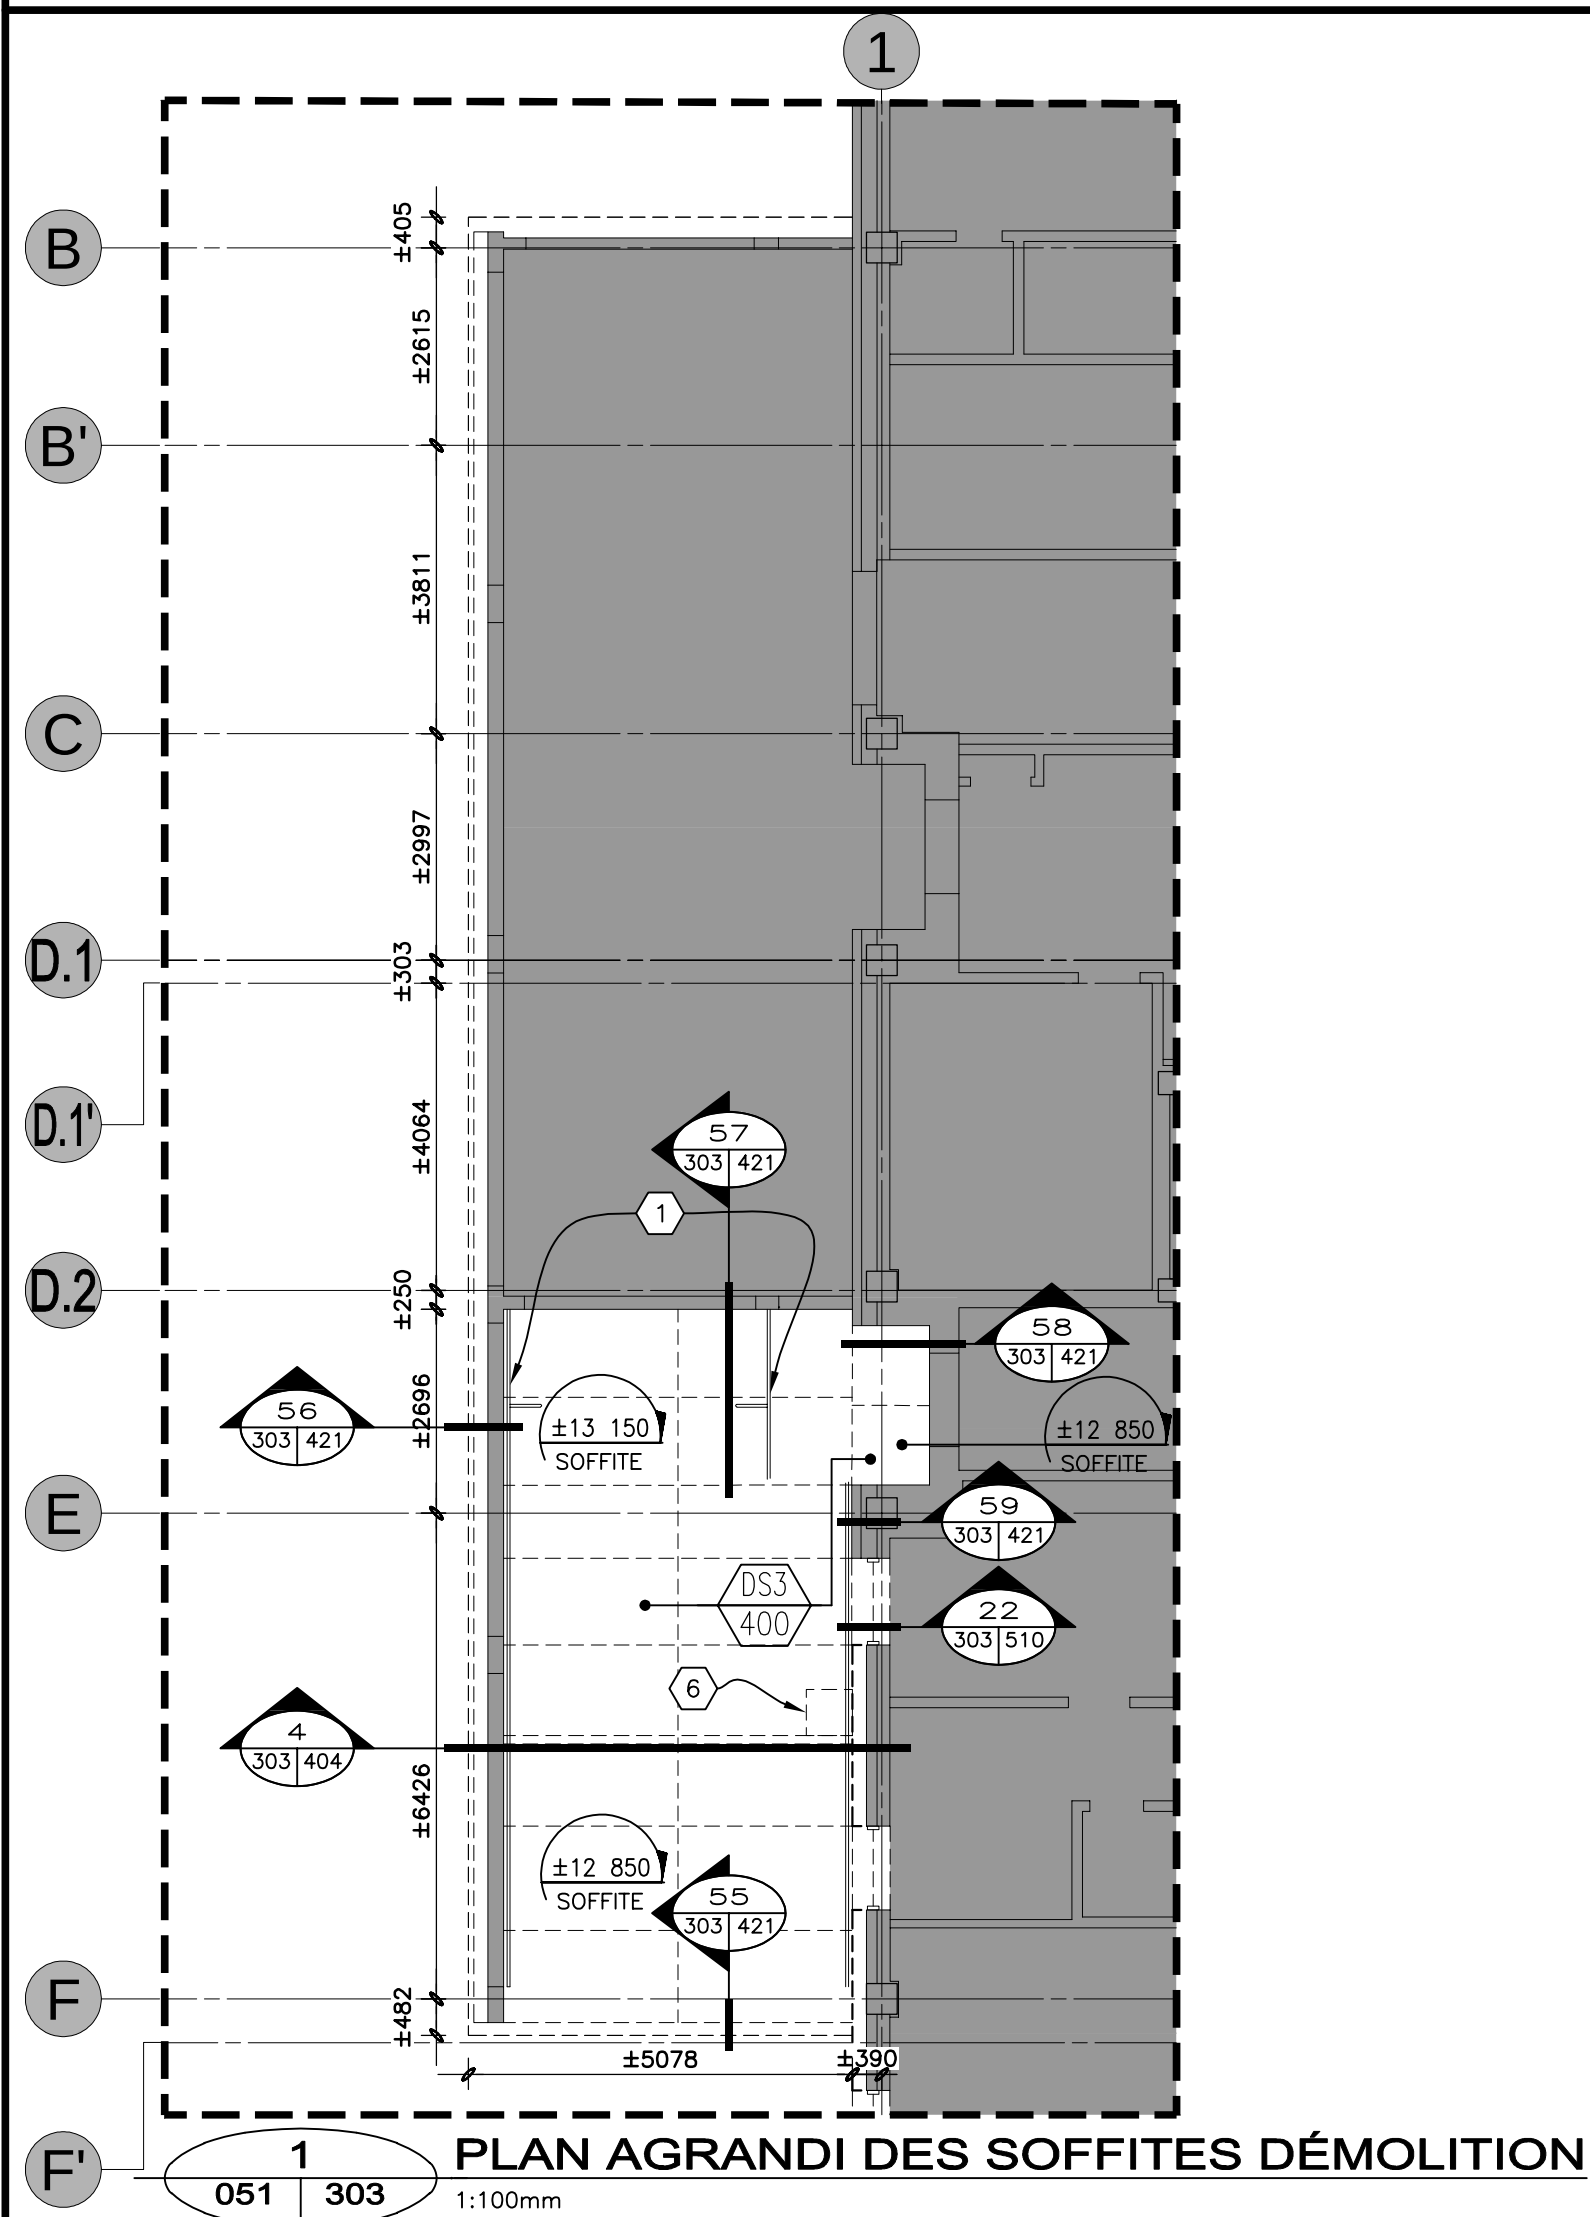


PLAN AGRANDI DES SOFFITES DÉMOLITION

1:100mm

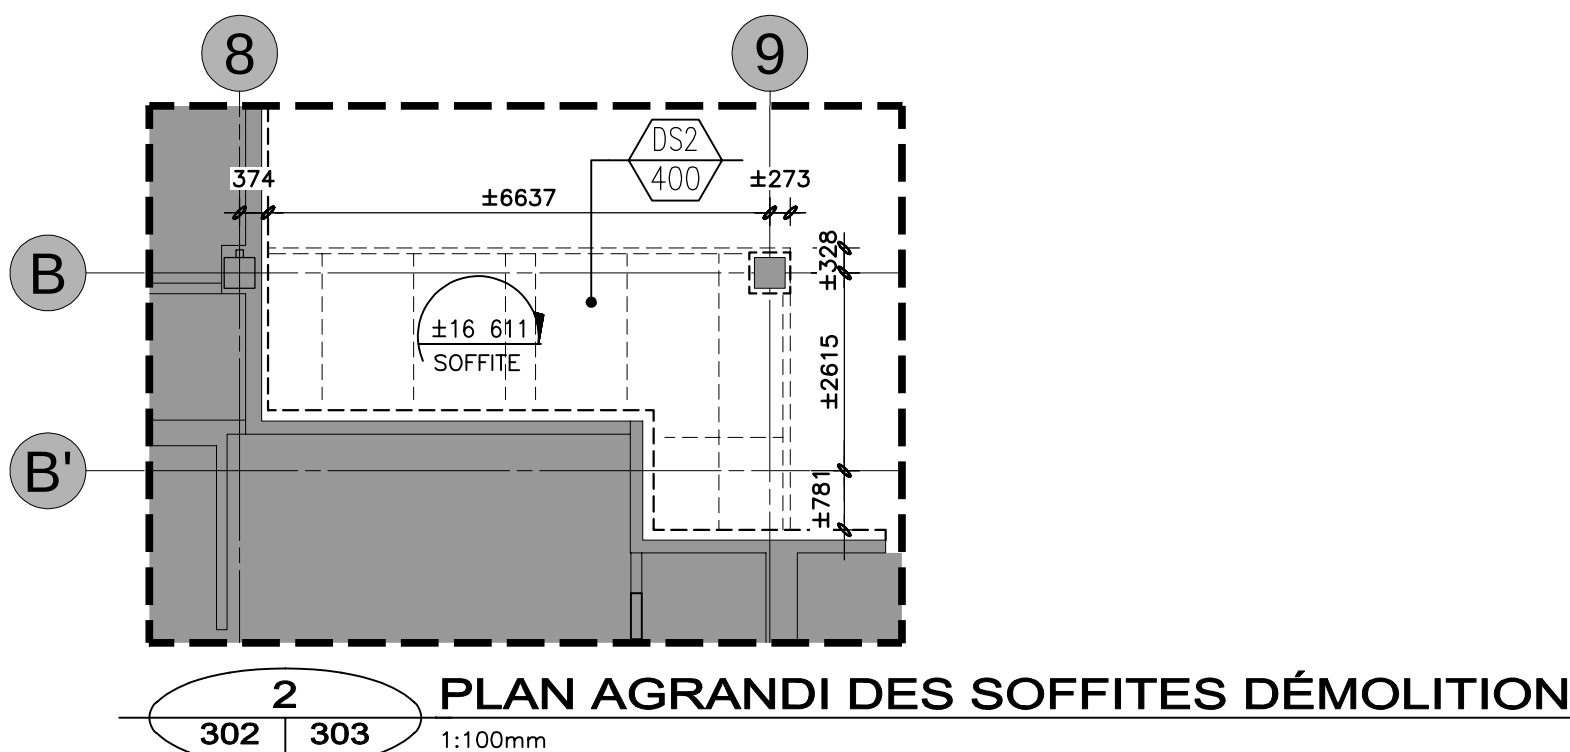


PLAN AGRANDI DES SOFFITES DÉMOLITION

1:100mm

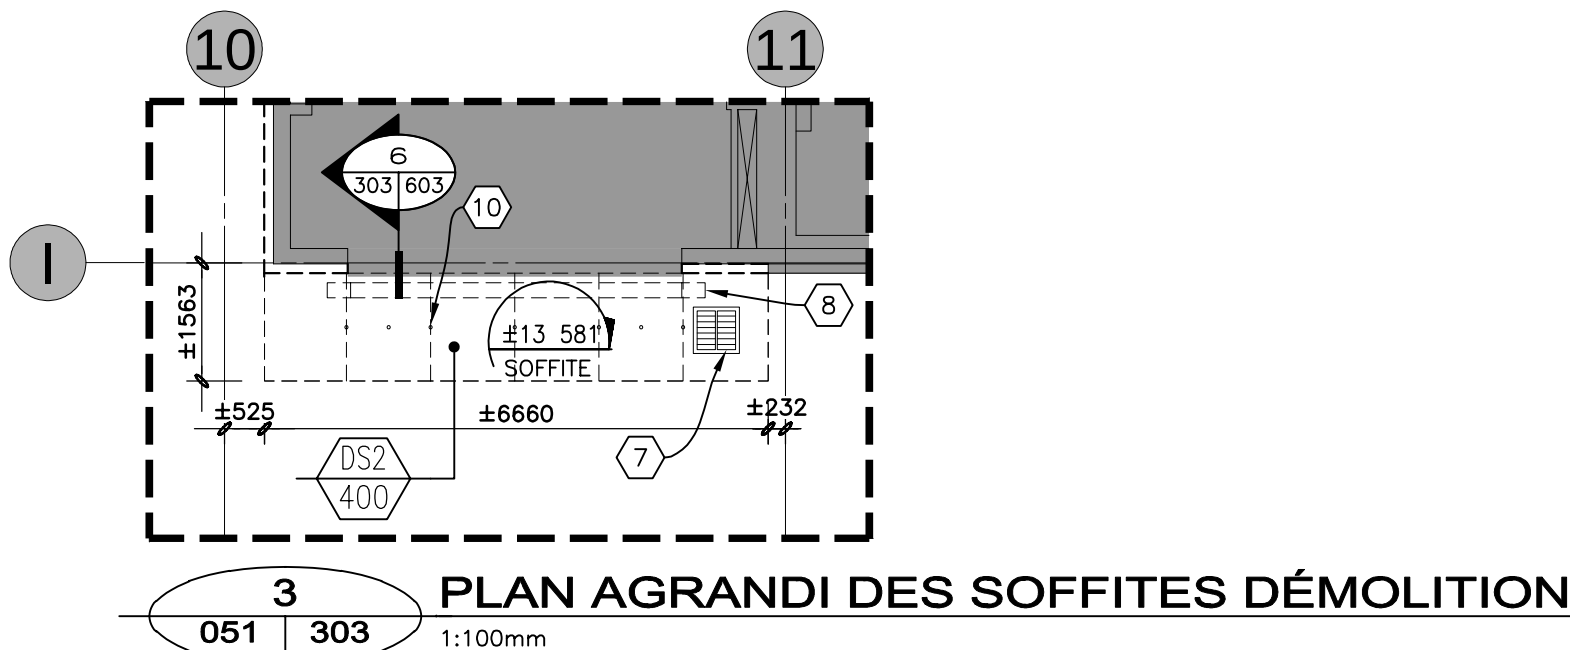


PLAN AGRANDI DES SOFFITES DÉMOLITION

1:100mm

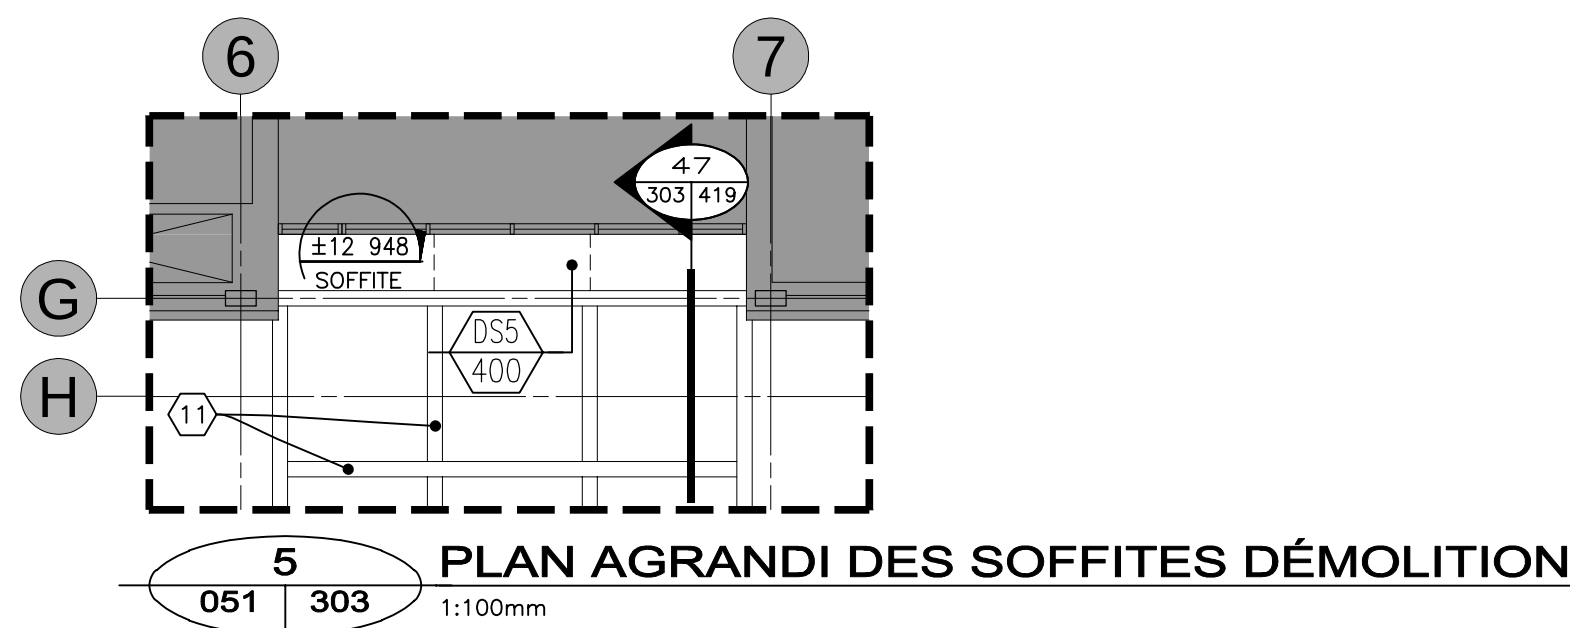

PLAN AGRANDI DES SOFFITES DÉMOLITION

1:100mm

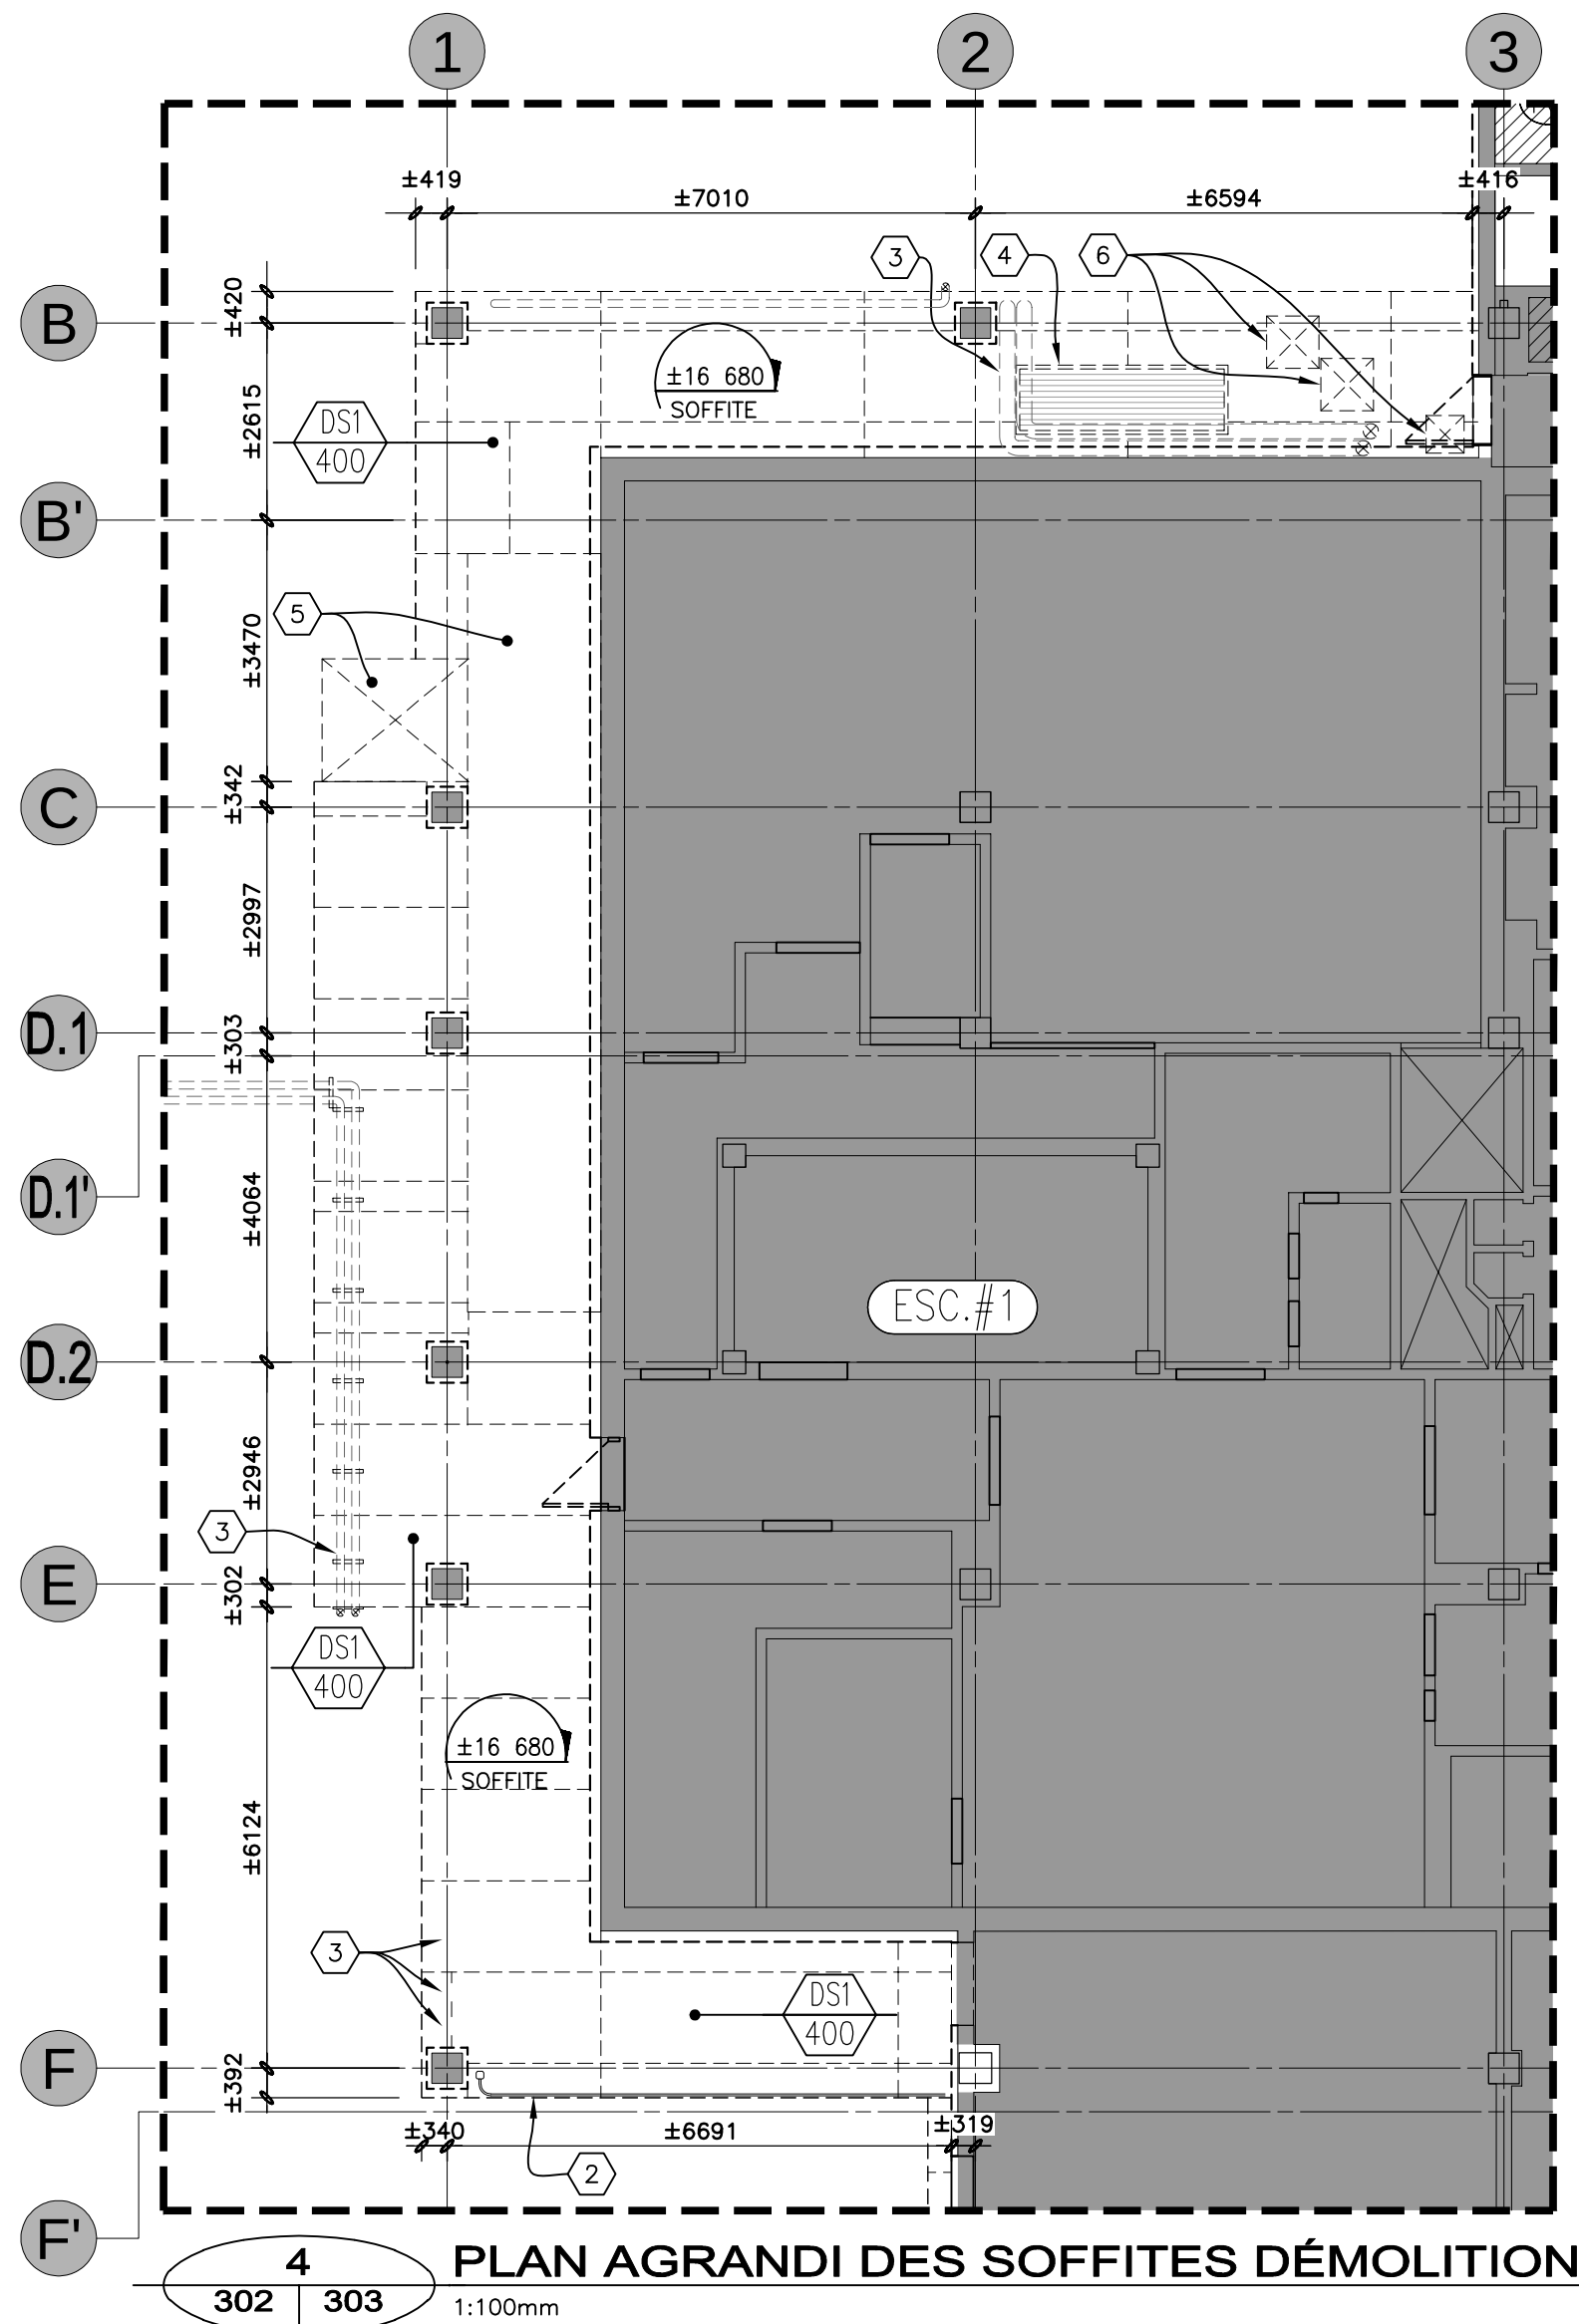

PLAN AGRANDI DES SOFFITES DÉMOLITION

1:100mm

NOTES

- 1 LIGNE DE GICLEURS EXISTANTE, VOIR DOCUMENTS D'INGÉNIERIE.
- 2 APPAREIL D'ELECTRO-MÉCANIQUE ET SUPPORT EXISTANT, VOIR DOCUMENTS D'INGÉNIERIE.
- 3 CONDUIT EXISTANT, VOIR DOCUMENTS D'INGÉNIERIE.
- 4 PERSIENNE DE VENTILATION EXISTANTE À ENLEVER TEMPORAIREMENT, VOIR DOCUMENTS D'INGÉNIERIE.
- 5 CONDUIT DE VENTILATION EXISTANT À DÉMOLIR, VOIR DOCUMENTS D'INGÉNIERIE.
- 6 TRAPPE ACCÈS EXISTANTE À DÉMOLIR.
- 7 GRILLE DE VENTILATION POUR L'ENTREPLAFOND EXISTANTE À DÉMONTÉ ET ENTREPOSER POUR RÉINSTALLATION FUTURE.
- 8 CONDUIT POUR COUSSIN D'ÉTANCHÉITÉ GONFLABLE POUR QUAI D'EMBARQUEMENT, VOIR DOCUMENTS D'INGÉNIERIE.
- 9 POUTRES, DALLES ET COLONNES EXISTANTES EN BÉTON À GRATTER ET À PEINDRE.
- 10 SUPPORT POUR COUSSIN D'ÉTANCHÉITÉ GONFLABLE À ENLEVER TEMPORAIREMENT ET ENTREPOSER POUR RÉINSTALLATION FUTURE.
- 11 POUTRE EXISTANTE EN BÉTON À NETTOYER.

LÉGENDE

- (X) NOTE DESCRIPTIVE.
- (X) AXE EXISTANT.
- (NS) NOUVEL AXE.
- (XXX) NUMÉRO DE LOCAUX.
- EXISTANT À CONSERVER.
- MUR OU CLOISON À DÉMOLIR.
- TRAVAUX DE DÉMOLITION SUR LE MUR EXISTANT, VOIR LES COMPOSITIONS, COUPES DE MUR TYPES ET DÉTAILS TYPES POUR LES COMPOSANTES À DÉMOLIR.
- (X) COUPE DE MUR.
- (X) DÉTAIL TYPE.
- FENÊTRE EXISTANTE OU MUR-RIDEAU À CONSERVER.
- FENÊTRE EXISTANTE OU MUR-RIDEAU À DÉMOLIR, VOIR LES COUPES DE MURS ET DÉTAILS TYPES DE FENÊTRE POUR LA SÉQUENCE DE TRAVAIL.
- NOUVEAU MUR OU NOUVELLE CLOISON À CONSTRUIRE.
- NOUVELLES COMPOSANTES DE MUR À CONSTRUIRE, DÉTAILS TYPES.
- NOUVELLE FENÊTRE OU NOUVEAU MUR-RIDEAU, VOIR COUPES DEMUR, DÉTAILS TYPES ET ÉLEVATIONS TYPE DE FENÊTRES.
- NIVEAU.
- REFERENCE DE COMPOSITION.
- SOFFITE À DÉMOLIR.

NE DOIT PAS SERVIR À L'EXÉCUTION

Le présent document est émis pour la seule fin identifiée. Son contenu est protégé par les droits d'auteur et toute reproduction ou modification, partielle ou totale, est interdite sans l'autorisation écrite de gagnon, letellier, cyr, ricard, mathieu, proulx, savard consortium d'architectes.




GLCRM | Proulx Savard |

GLCRM:
128, Avenue de la Cathédrale,
Bureau 201
Rimouski, QC, G5L 5H7
(418) 722-7455



2406, Ch. des Quatres-Bourgeois,
Bureau 100
Québec, QC, G1V 1W5
(418) 647-1700

Proulx Savard Architectes:
75, boul. Arthur-Buies Ouest,
Rimouski QC G5L 5C2
(418) 723-5543

ARCHITECTURE

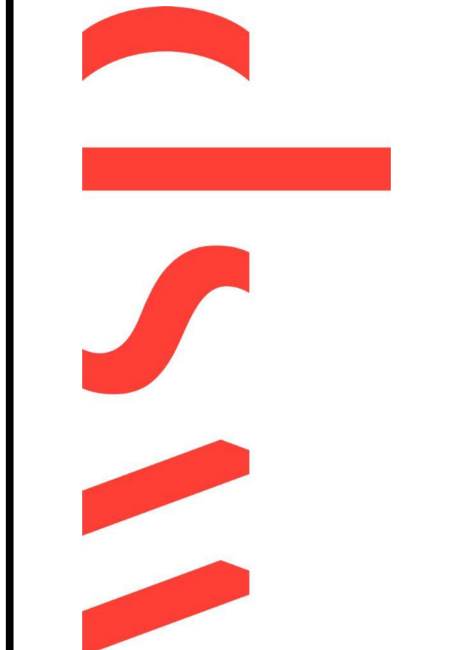

CONSULTANTS

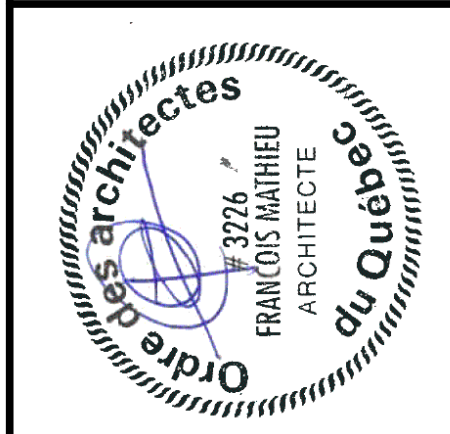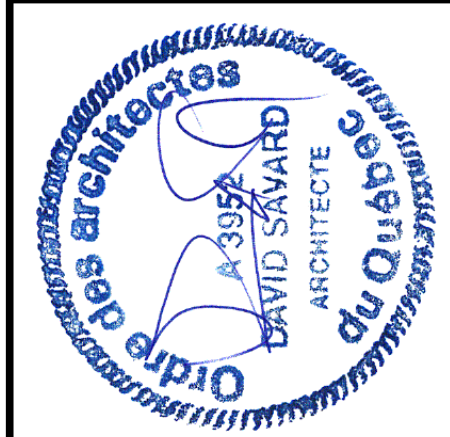

DESIGNATEUR (S) D.S., A.C.	DOSSIER N° 24-102 1637-24	DATE SEPTEMBRE 2024	ÉCHELLE INDIQUÉE	DÉSIGNÉES POUR SOUMISSION DÉSIGNÉES 100% POUR APPROBATION DÉSIGNÉES 80% POUR APPROBATION DÉSIGNÉES 40% POUR APPROBATION PRÉLIMINAIRES 20% POUR APPROBATION	RÉVISIONS	DATE	No
DESIGN	PLAN DES SOFFITES DÉMOLITION			05 2024-09-24 04 2024-08-21 03 2024-08-03 02 2024-05-14 01 2024-02-27			
PROJET	HÔPITAL DE CHANDLER, Chandler (Réfection de l'enveloppe)						
PROPRIÉTAIRE	Santé Québec						

303