


Le présent document est émis pour la seule fin identifiée. Son contenu est protégé par les droits d'auteur et toute reproduction ou modification, partielle ou totale, est interdite sans l'autorisation écrite de gagnon, letellier, cyr, ricard, mathieu, proulx, savard consortium d'architectes.




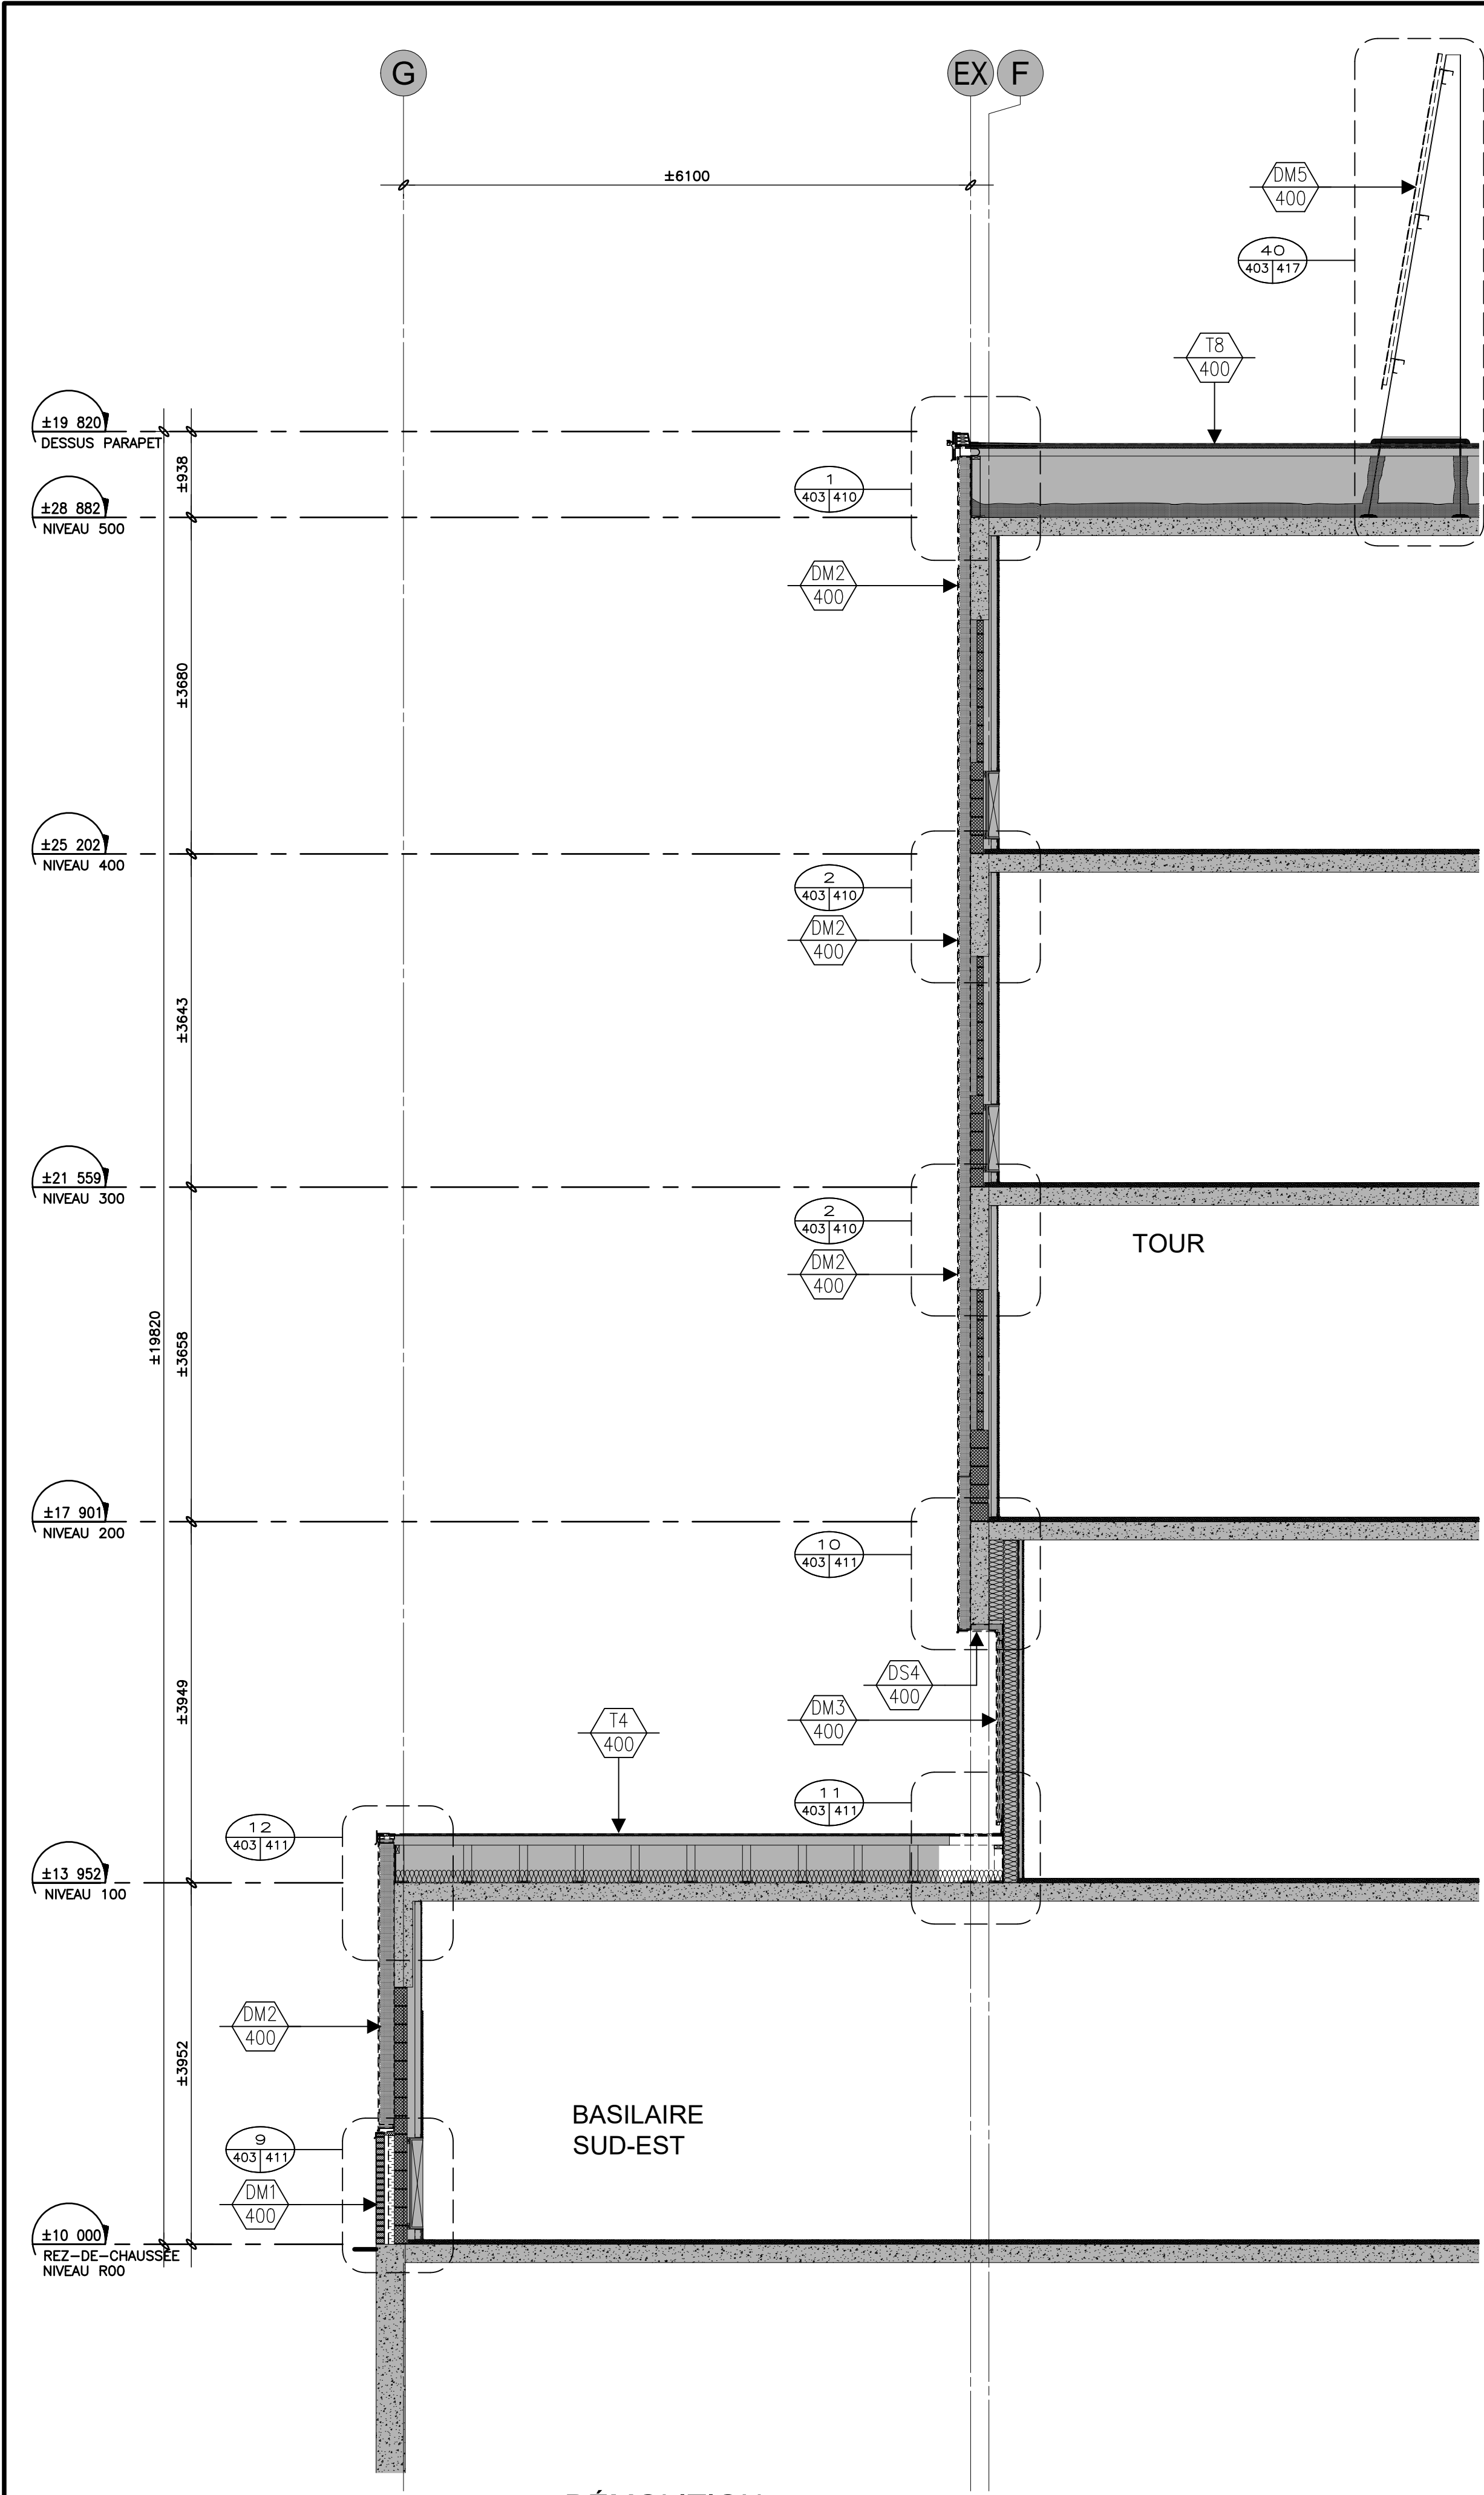

DÉMOLITION

3 COUPE DE MUR TYPE
403 1:50mm (TOUR ET BASILAIRE SUD-EST)

051,052,053,054,101,102,103,104,201,203

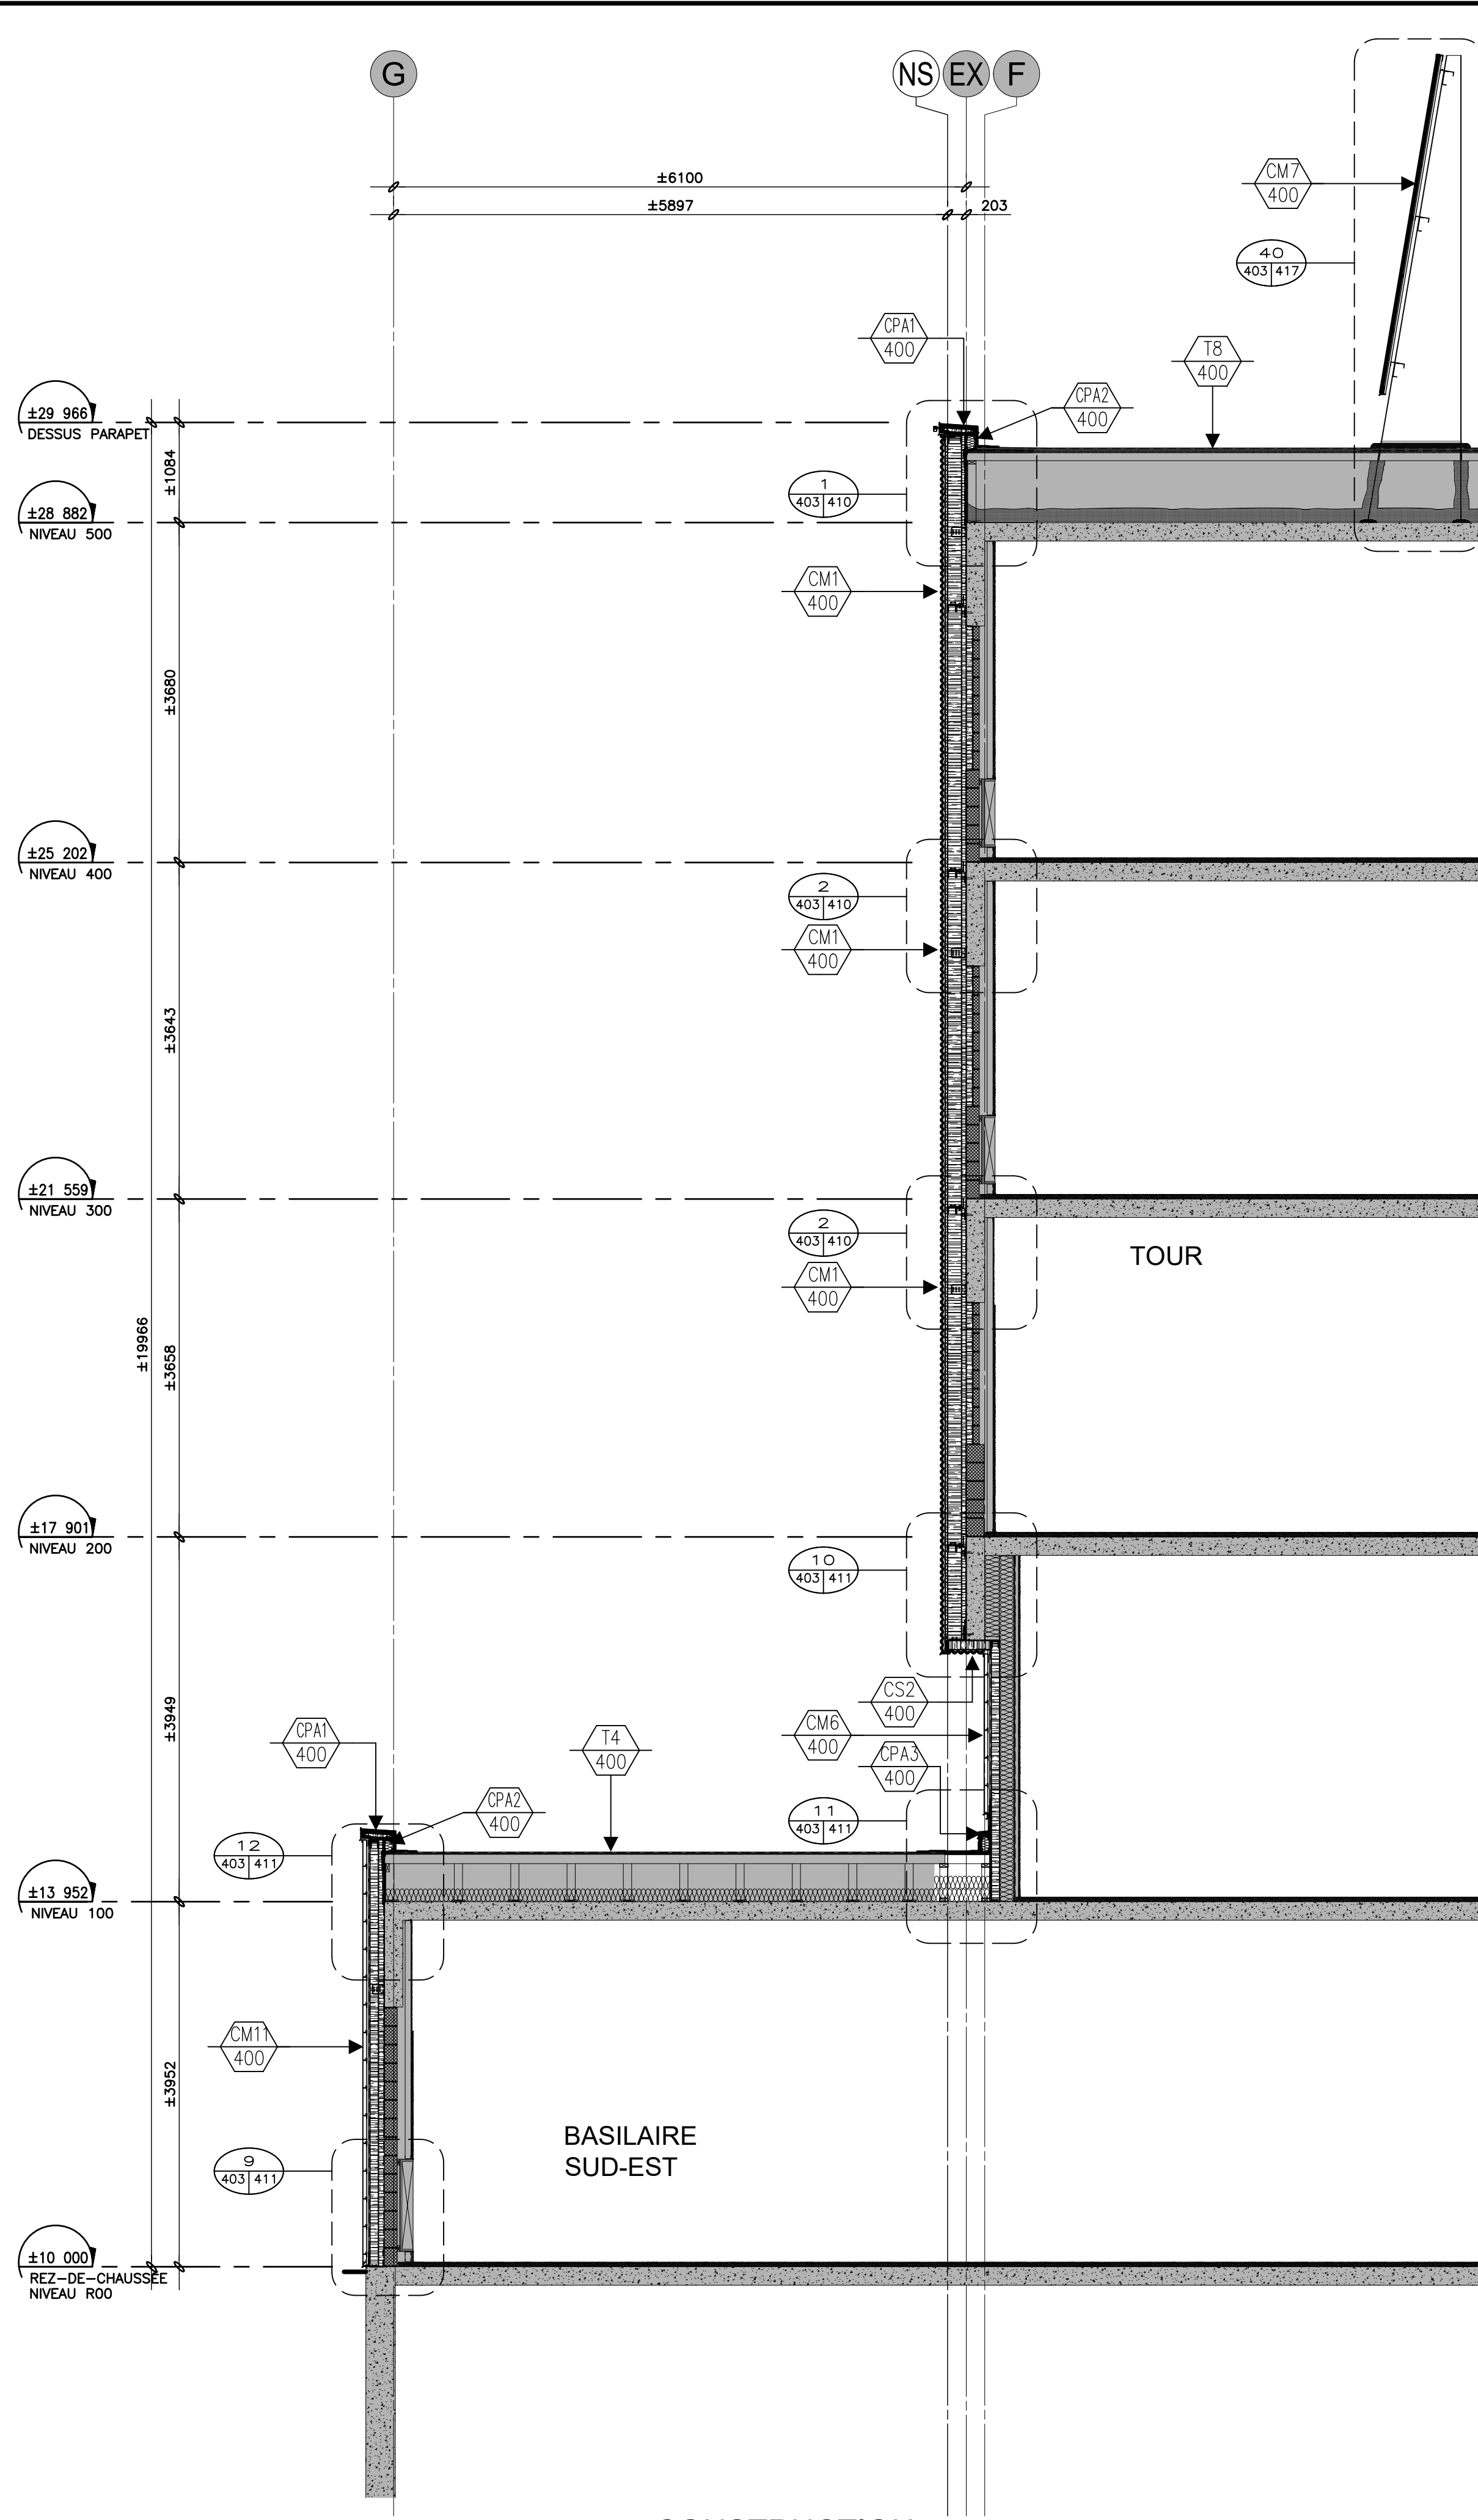

CONSTRUCTION

NOTES

GLCRM

PROULXSAVARD

ARCHITECTES

GLCRM | Proulx Savard |

GLCRM:
128, Avenue de la Cathédrale,
Bureau 201
Rimouski, QC, G5L 5H7
(418) 722-7655

2406, Ch. des Quatres-Bourgeois,
Bureau 100
Québec, QC, G1V 1W5
(418) 647-1700

Proulx Savard Architectes:
75, boul. Arthur-Buies Ouest,
Rimouski QC G5L 5C2
(418) 723-5543

ARCHITECTURE

IS

CONSULTANTS

Ordre des architectes
A-3998
DAVID SAVARD
ARCHITECTE
du Québec

Ordre des architectes
A-3726
FRANÇOIS MATHIEU
ARCHITECTE
du Québec

DESIGNATEUR (S)	DOSSIER No.	DATE	RÉVISIONS				
			No	DATE			
DESIGN COUPE DE MUR TYPE DÉMOLITION ET CONSTRUCTION	24-1087 / 6857-24	SEPTEMBRE 2024	05	2024-09-04	DÉFINITIVES POUR SOUMISSION		
			06	2024-08-21	DÉFINITIVES 100% POUR APPROBATION		
			03	2024-08-03	DÉFINITIVES 80% POUR APPROBATION		
			02	2024-05-14	DÉFINITIVES 60% POUR APPROBATION		
			01	2024-02-27	DÉFINITIVES 50% POUR APPROBATION		

PROJET
HÔPITAL DE CHANDLER,
Chandler
(Réfection de l'enveloppe)

PROPRIÉTAIRE
Santé Québec

NE DOIT PAS SERVIR À L'EXÉCUTION

Le présent document est émis pour la seule fin identifiée. Son contenu est protégé par les droits d'auteur et toute reproduction ou modification, partielle ou totale, est interdite sans l'autorisation écrite de gagnon, letellier, cyr, ricard, mathieu, proulx, savard consortium d'architectes.

LÉGENDE

EXISTANT À CONSERVER.

ÉLÉMENT À DÉMOLIR.

X

AXE EXISTANT

EX

EXTÉRIEUR DE LA STRUCTURE DE BÉTON EXISTANTE DE LA TOUR.

NS

NOUVEL AXE: FACE EXTÉRIEURE DES BARRES Z ET COLOMBAGES DE LA TOUR. VOIR STRUCTURE.
(*) VOIR NOTE GÉNÉRAL PAGE 400.


403



051,052,053,054,101,102,103,104,201,201A,203,204,303,304



Le présent document est émis pour la seule fin identifiée. Son contenu est protégé par les droits d'auteur et toute reproduction ou modification, partielle ou totale, est interdite sans l'autorisation écrite de gagnon, letellier, cyr, ricard, mathieu, proulx, savard consortium d'architectes.


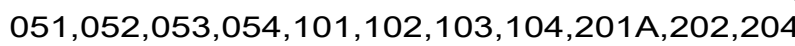


1:50mm (TOUR ET BASILAIRE NORD-EST)



Le présent document est émis pour la seule fin identifiée. Son contenu est protégé par les droits d'auteur et toute reproduction ou modification, partielle ou totale, est interdite sans l'autorisation écrite de gagnon, letellier, cyr, ricard, mathieu, proulx, savard consortium d'architectes.



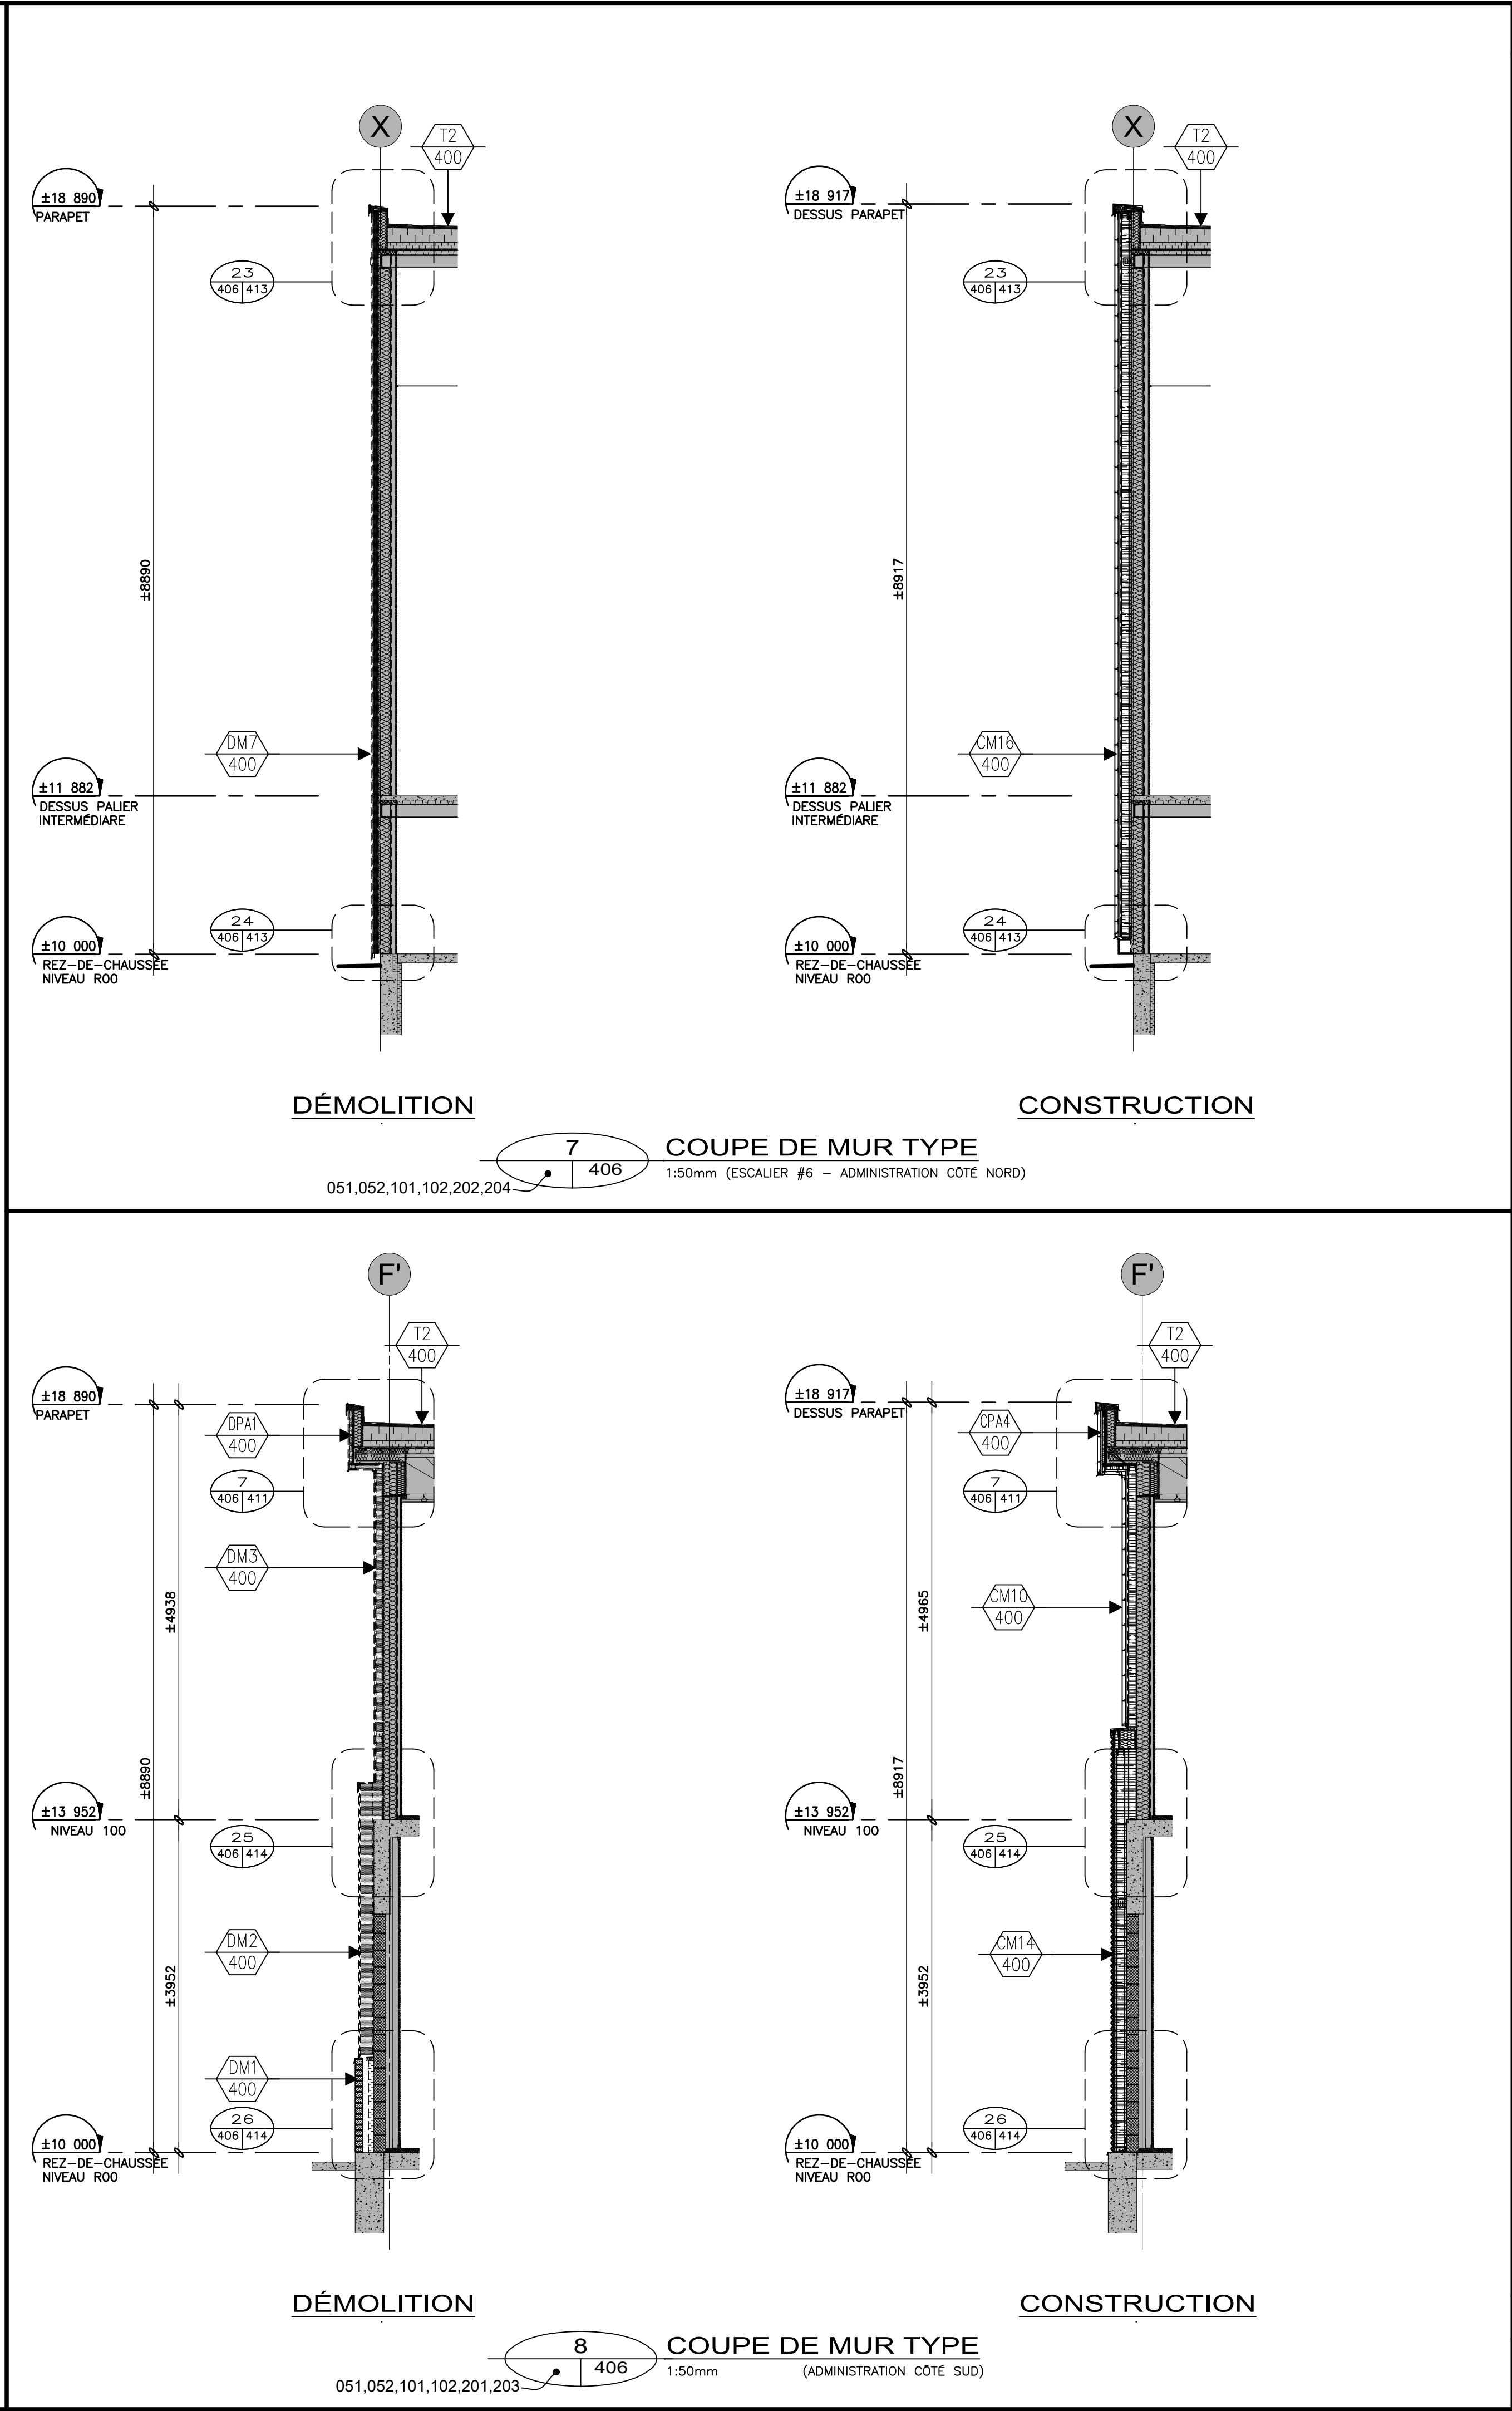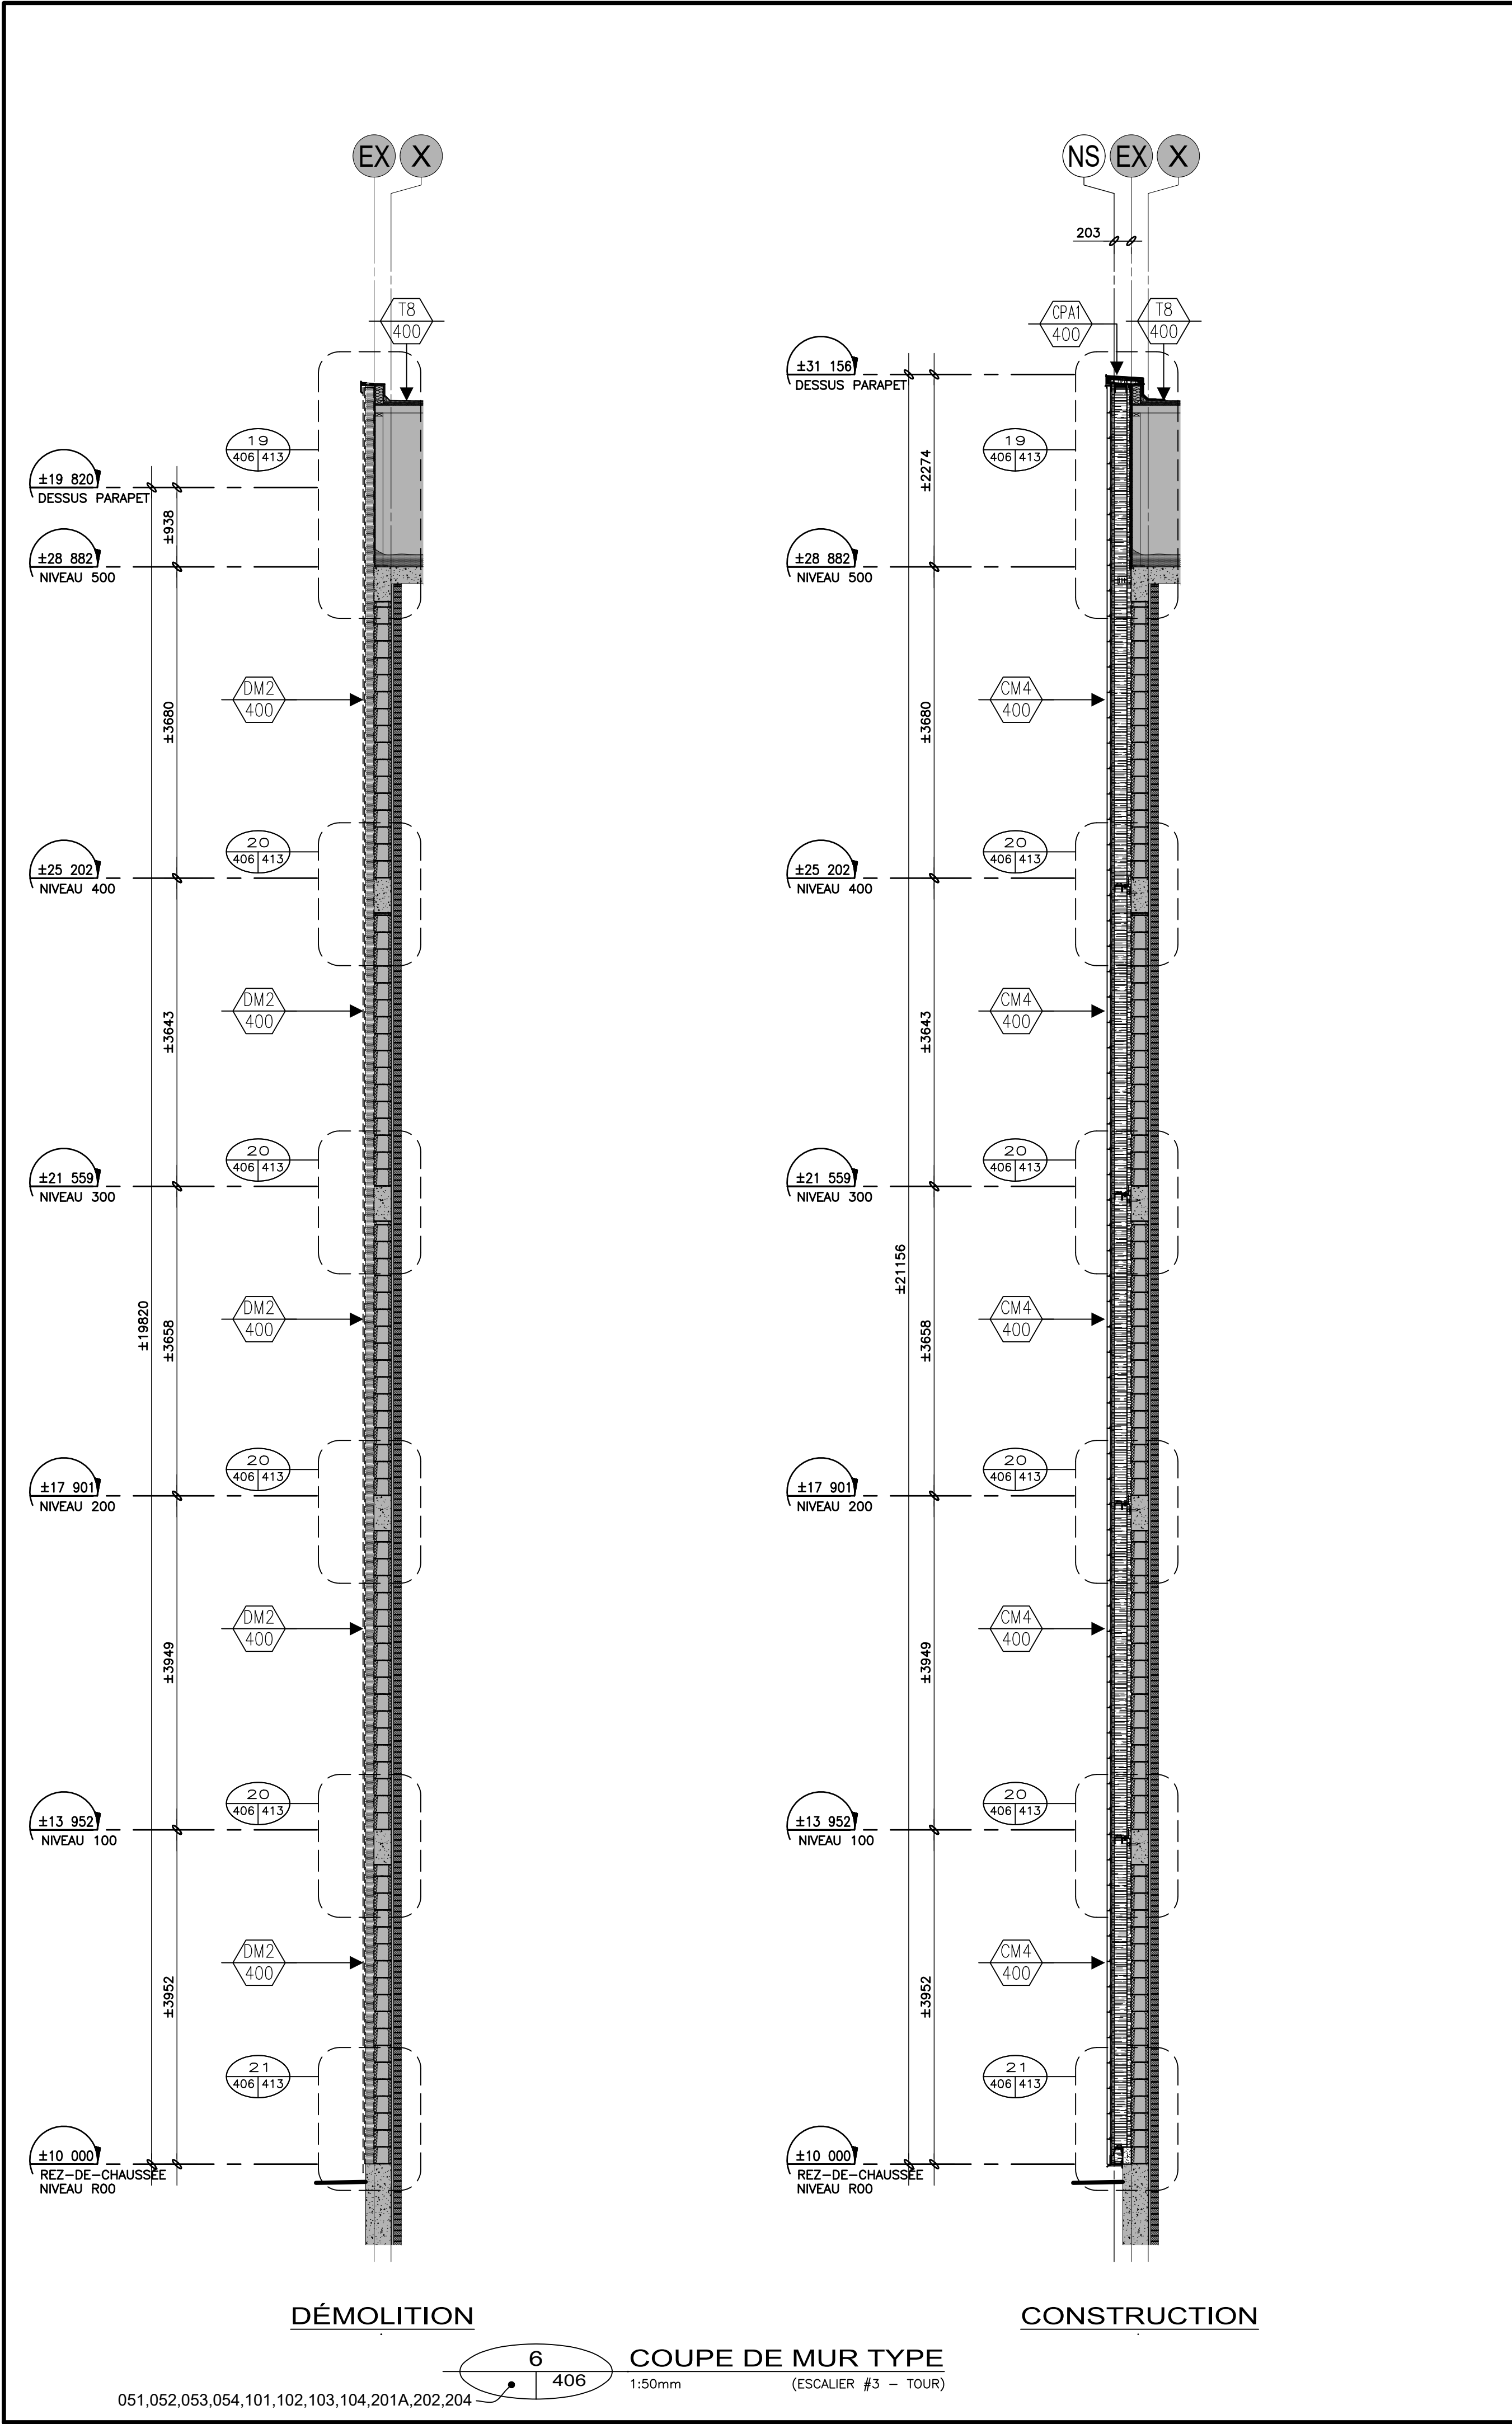

NOTES

Le présent document est émis par la seule fin identifiée. Son contenu est protégé par les droits d'auteur et toute reproduction ou modification, partielle ou totale, est interdite sans l'autorisation écrite de gagnon, letellier, cyr, ricard, mathieu, proulx, savard consortium d'architectes.

NE DOIT PAS SERVIR À L'EXÉCUTION

Le présent document est émis par la seule fin identifiée. Son contenu est protégé par les droits d'auteur et toute reproduction ou modification, partielle ou totale, est interdite sans l'autorisation écrite de gagnon, letellier, cyr, ricard, mathieu, proulx, savard consortium d'architectes.

GLCRM | Proulx Savard |

GLCRM:
128, Avenue de la Cathédrale,
Bureau 201
Rimouski, QC, G5L 5H7
(418) 722-7655

2406, Ch. des Quatres-Bourgeois,
Bureau 100
Québec, QC, G1V 1W5
(418) 647-1700

Proulx Savard Architectes:
75, boul. Arthur-Buies Ouest,
Rimouski QC G5L 5C2
(418) 723-5543

ARCHITECTURE

CONSULTANTS

Ordre des architectes du Québec

Ordre des architectes du Québec

DESSINATEUR (S)	DOSSIER No.	DATE	REVISIONS
DB AL	24-1087 / 687-24	SEPTEMBRE 2024	
ÉCHELLE			
INDIQUÉE			
	05	2024-09-04	DÉFINITIVES POUR SOUMISSION
	06	2024-08-21	DÉFINITIVES 100% POUR APPROBATION
	03	2024-08-03	DÉFINITIVES 80% POUR APPROBATION
	02	2024-05-14	DÉFINITIVES 40% POUR APPROBATION
	01	2024-02-27	PRÉLIMINAIRES 20% POUR APPROBATION
No	DATE		

DESIGN
COUPE DE MUR TYPE
DÉMOLITION ET CONSTRUCTION

PROJET
HÔPITAL DE CHANDLER,
Chandler
(Redaction de l'enveloppe)

PROPRIÉTAIRE
Santé Québec

406