
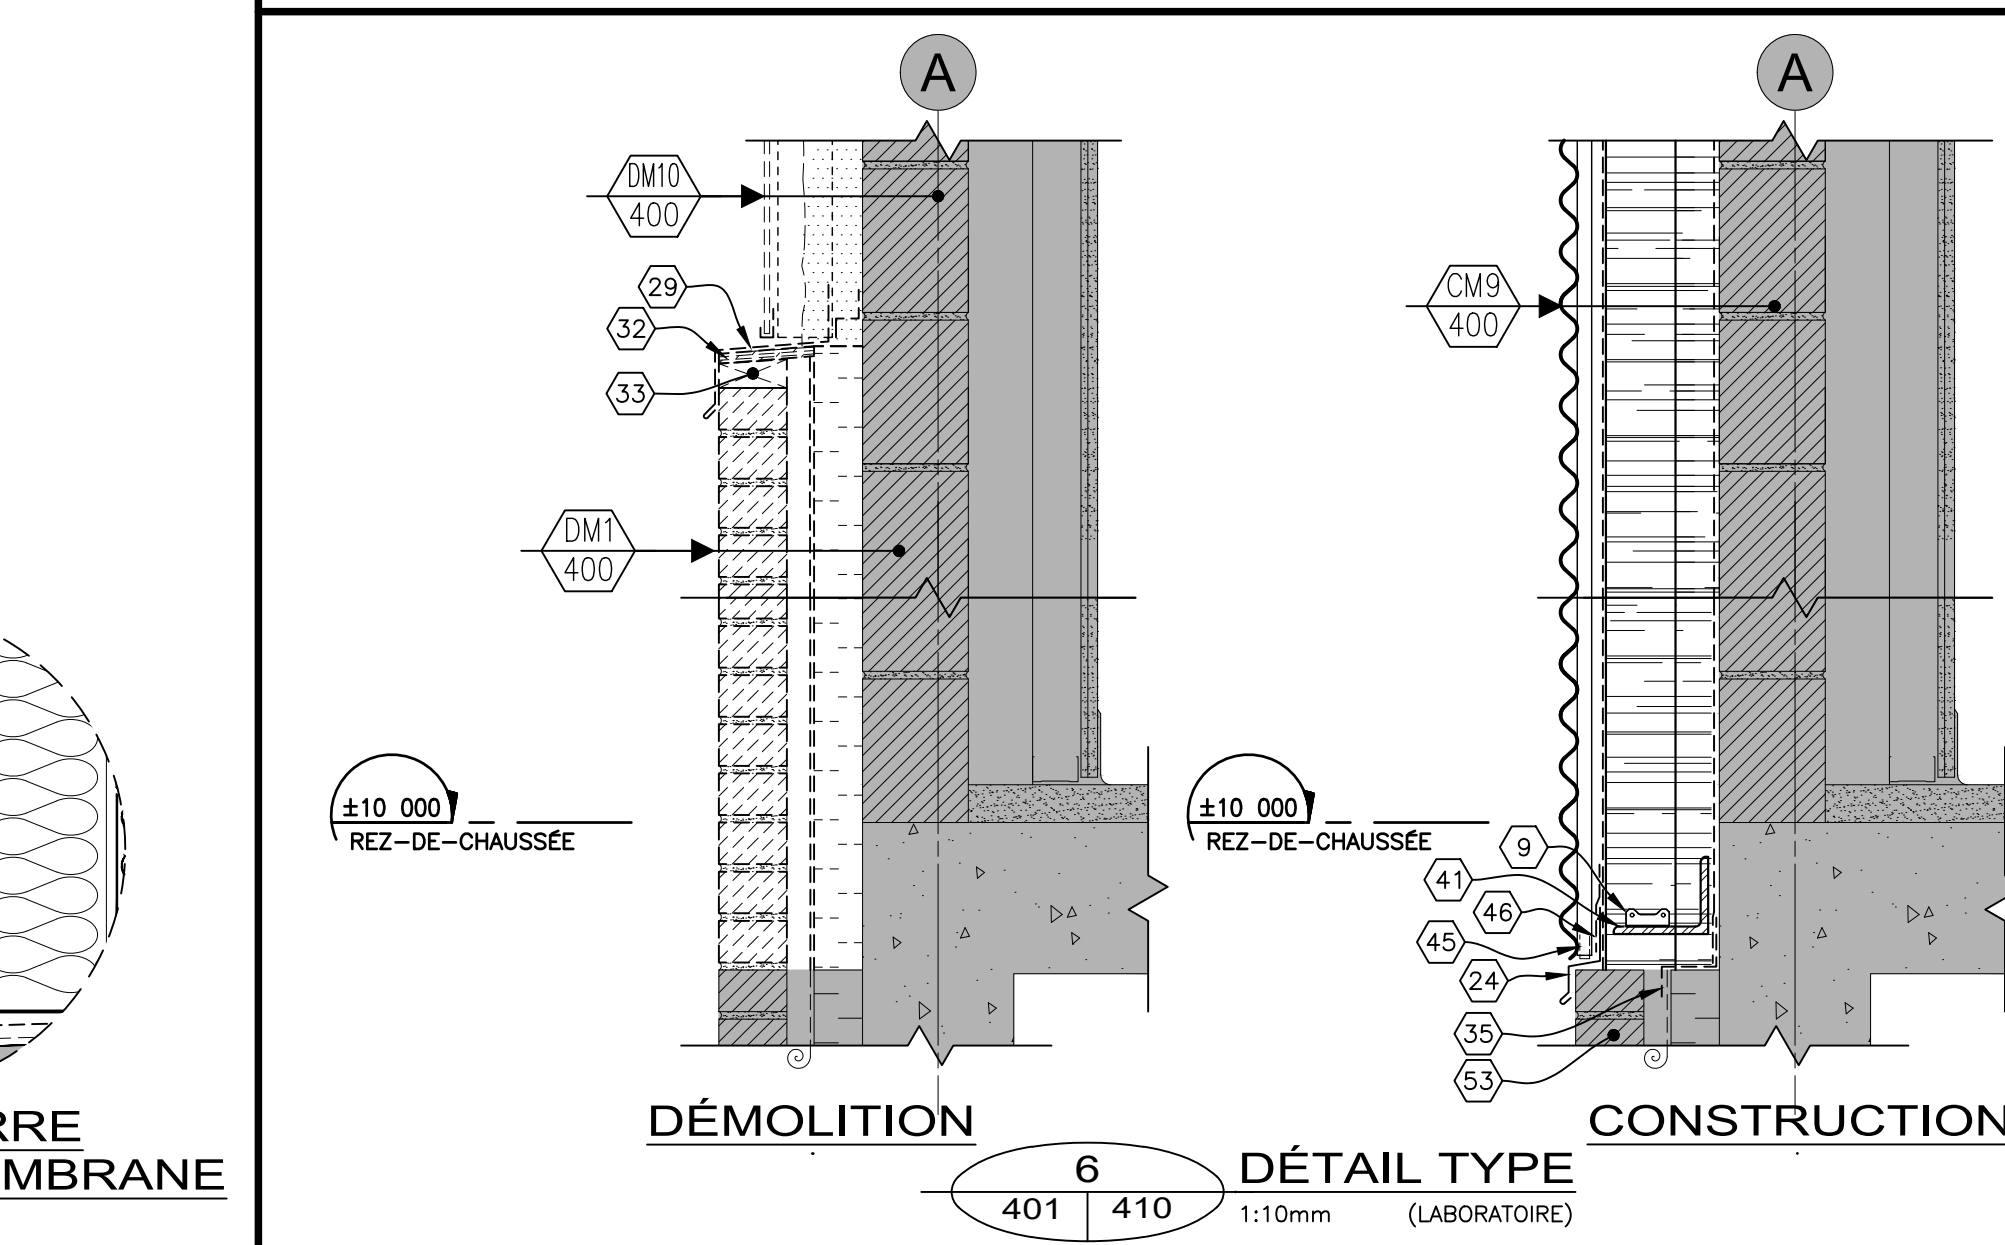
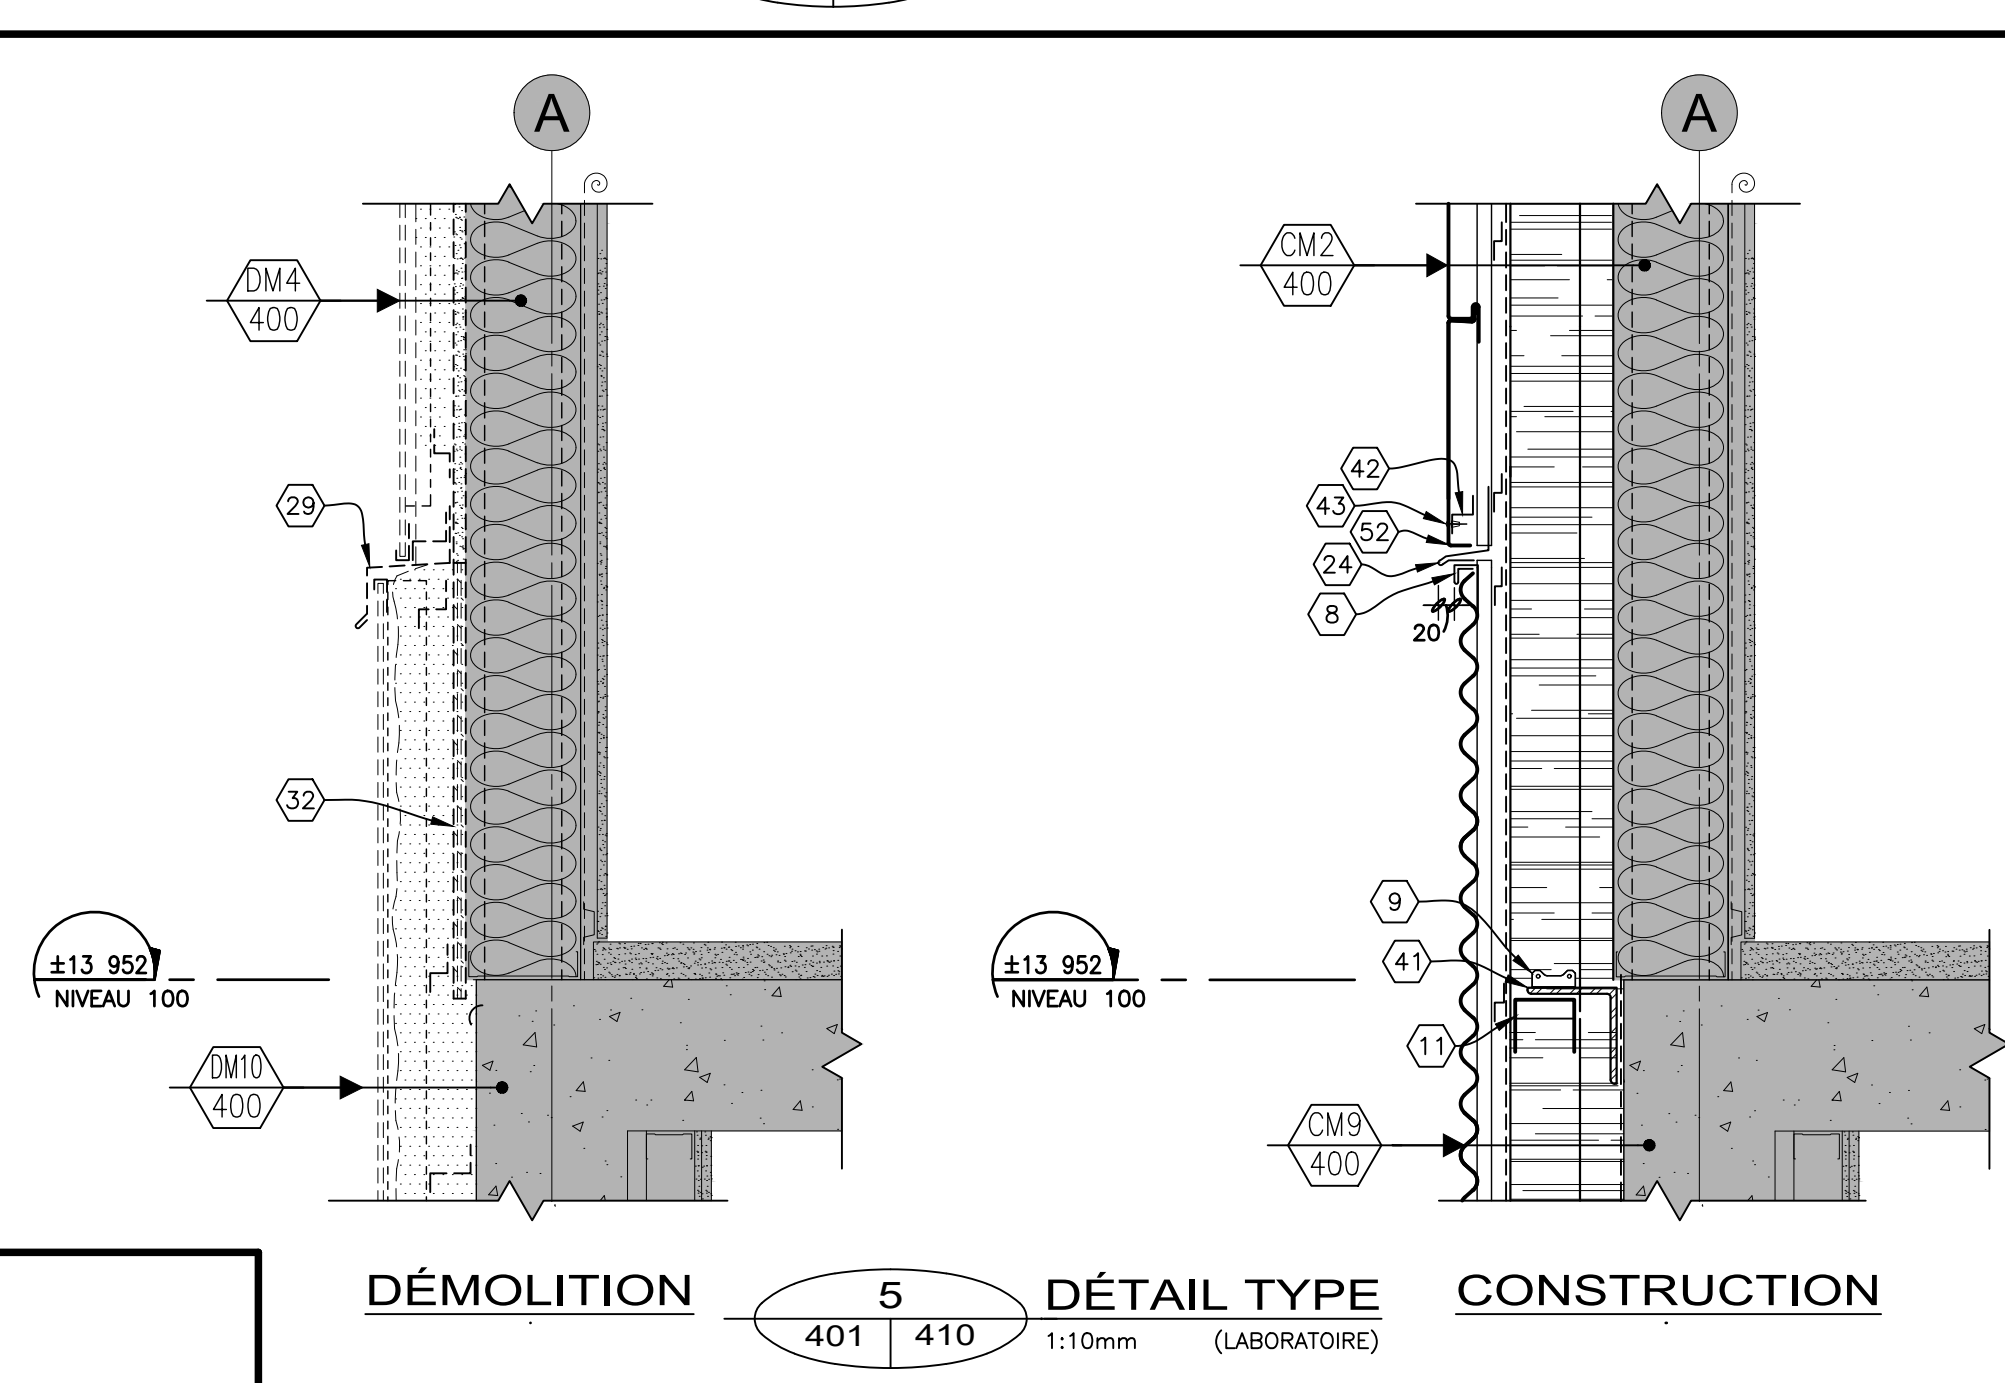
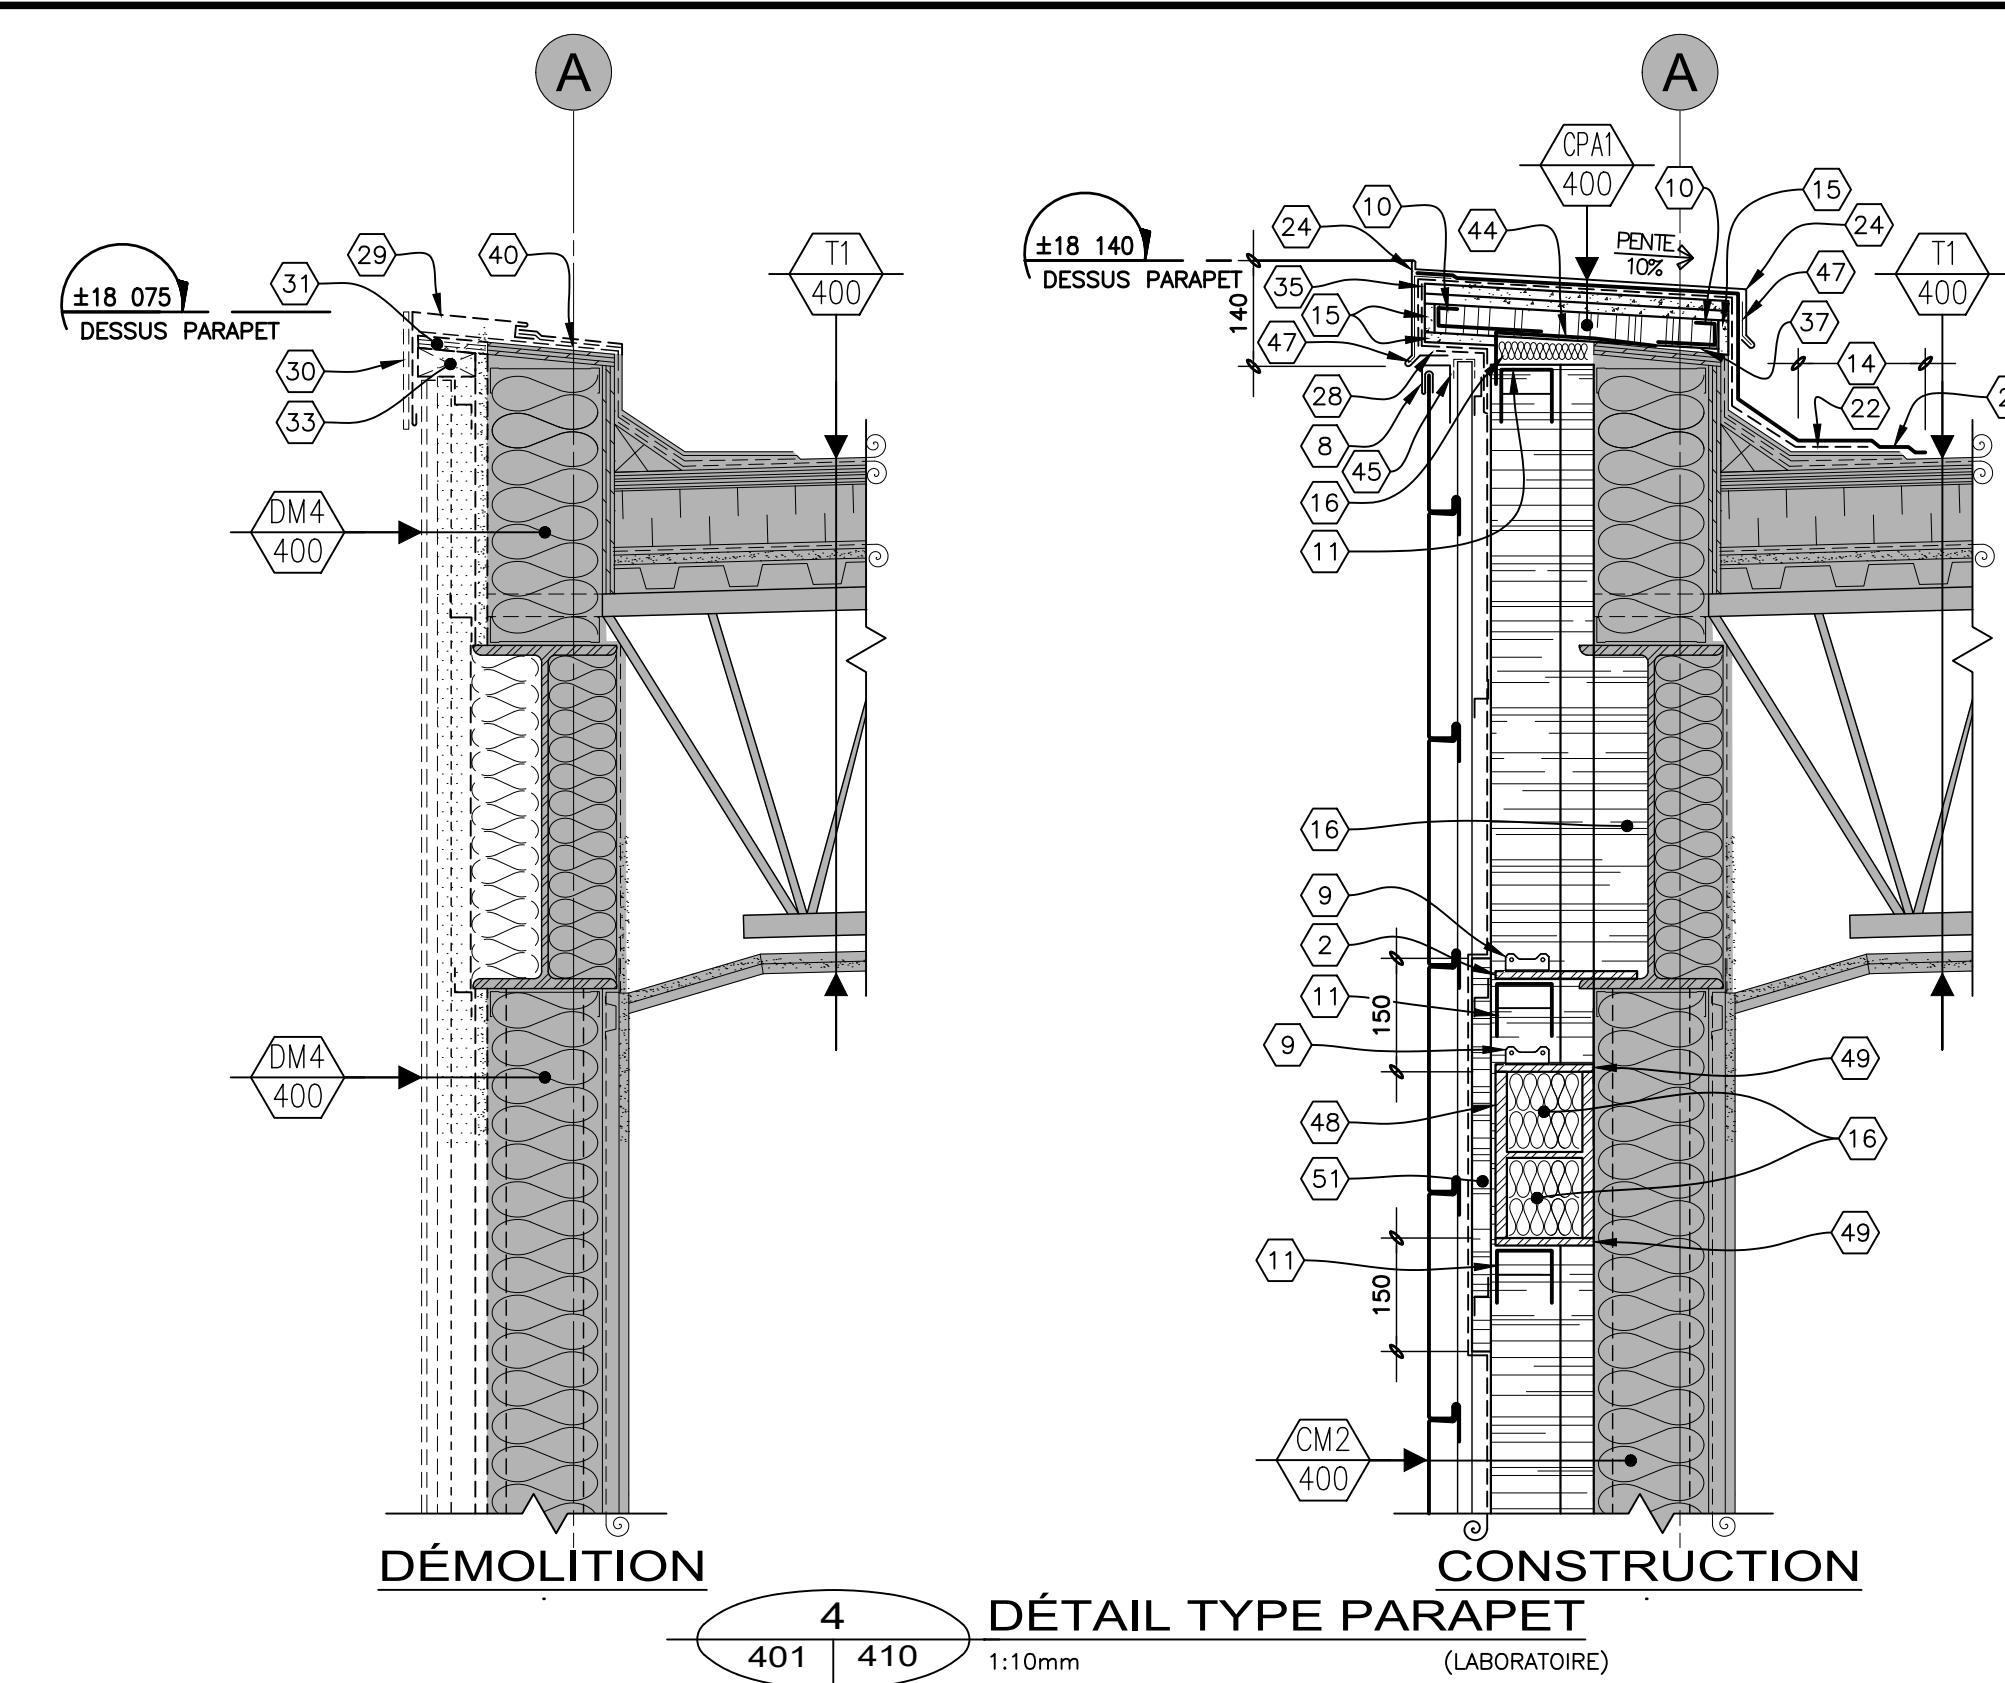
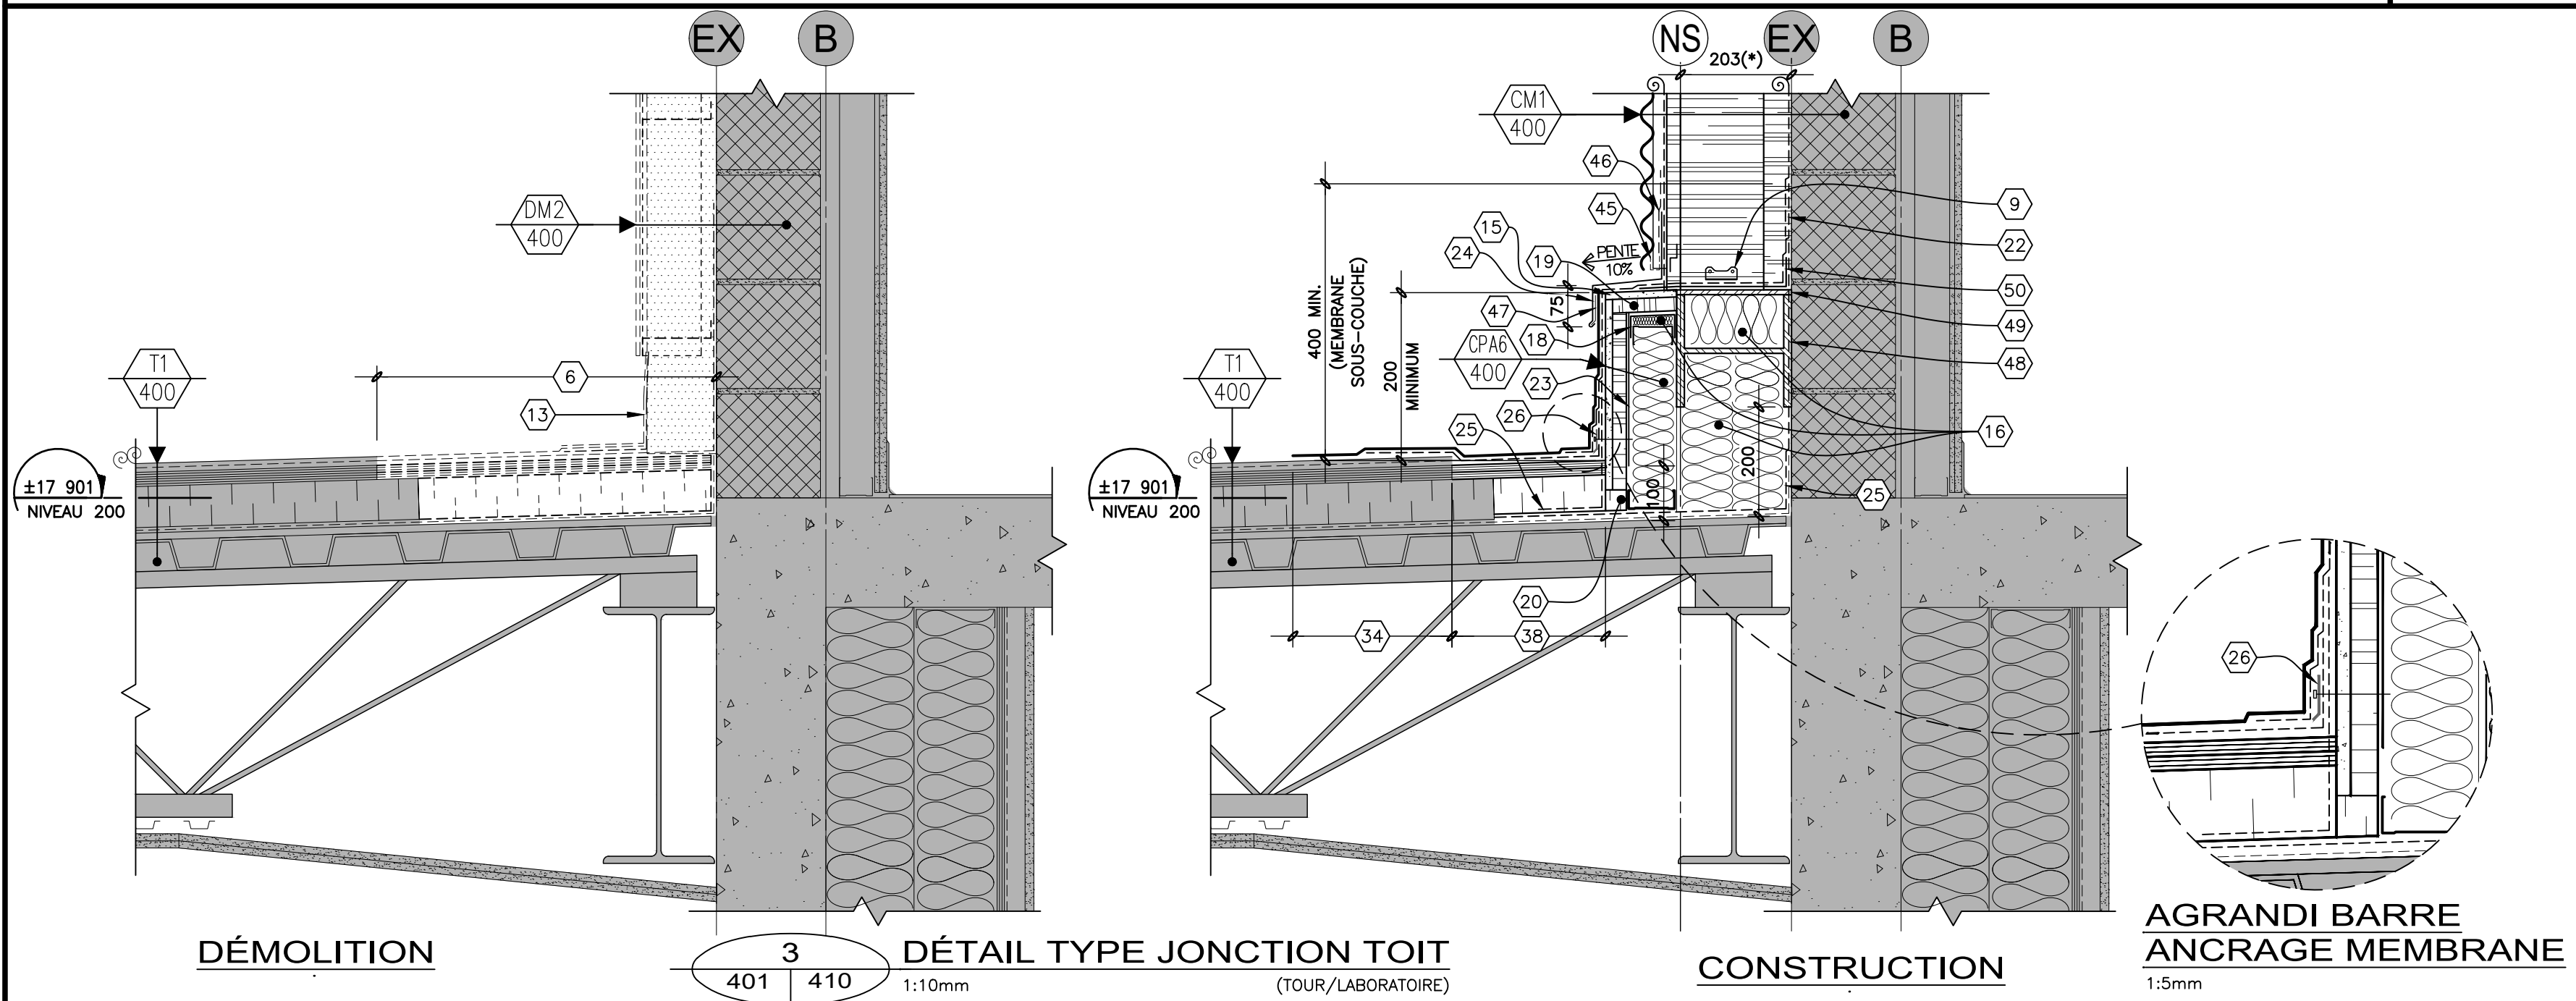
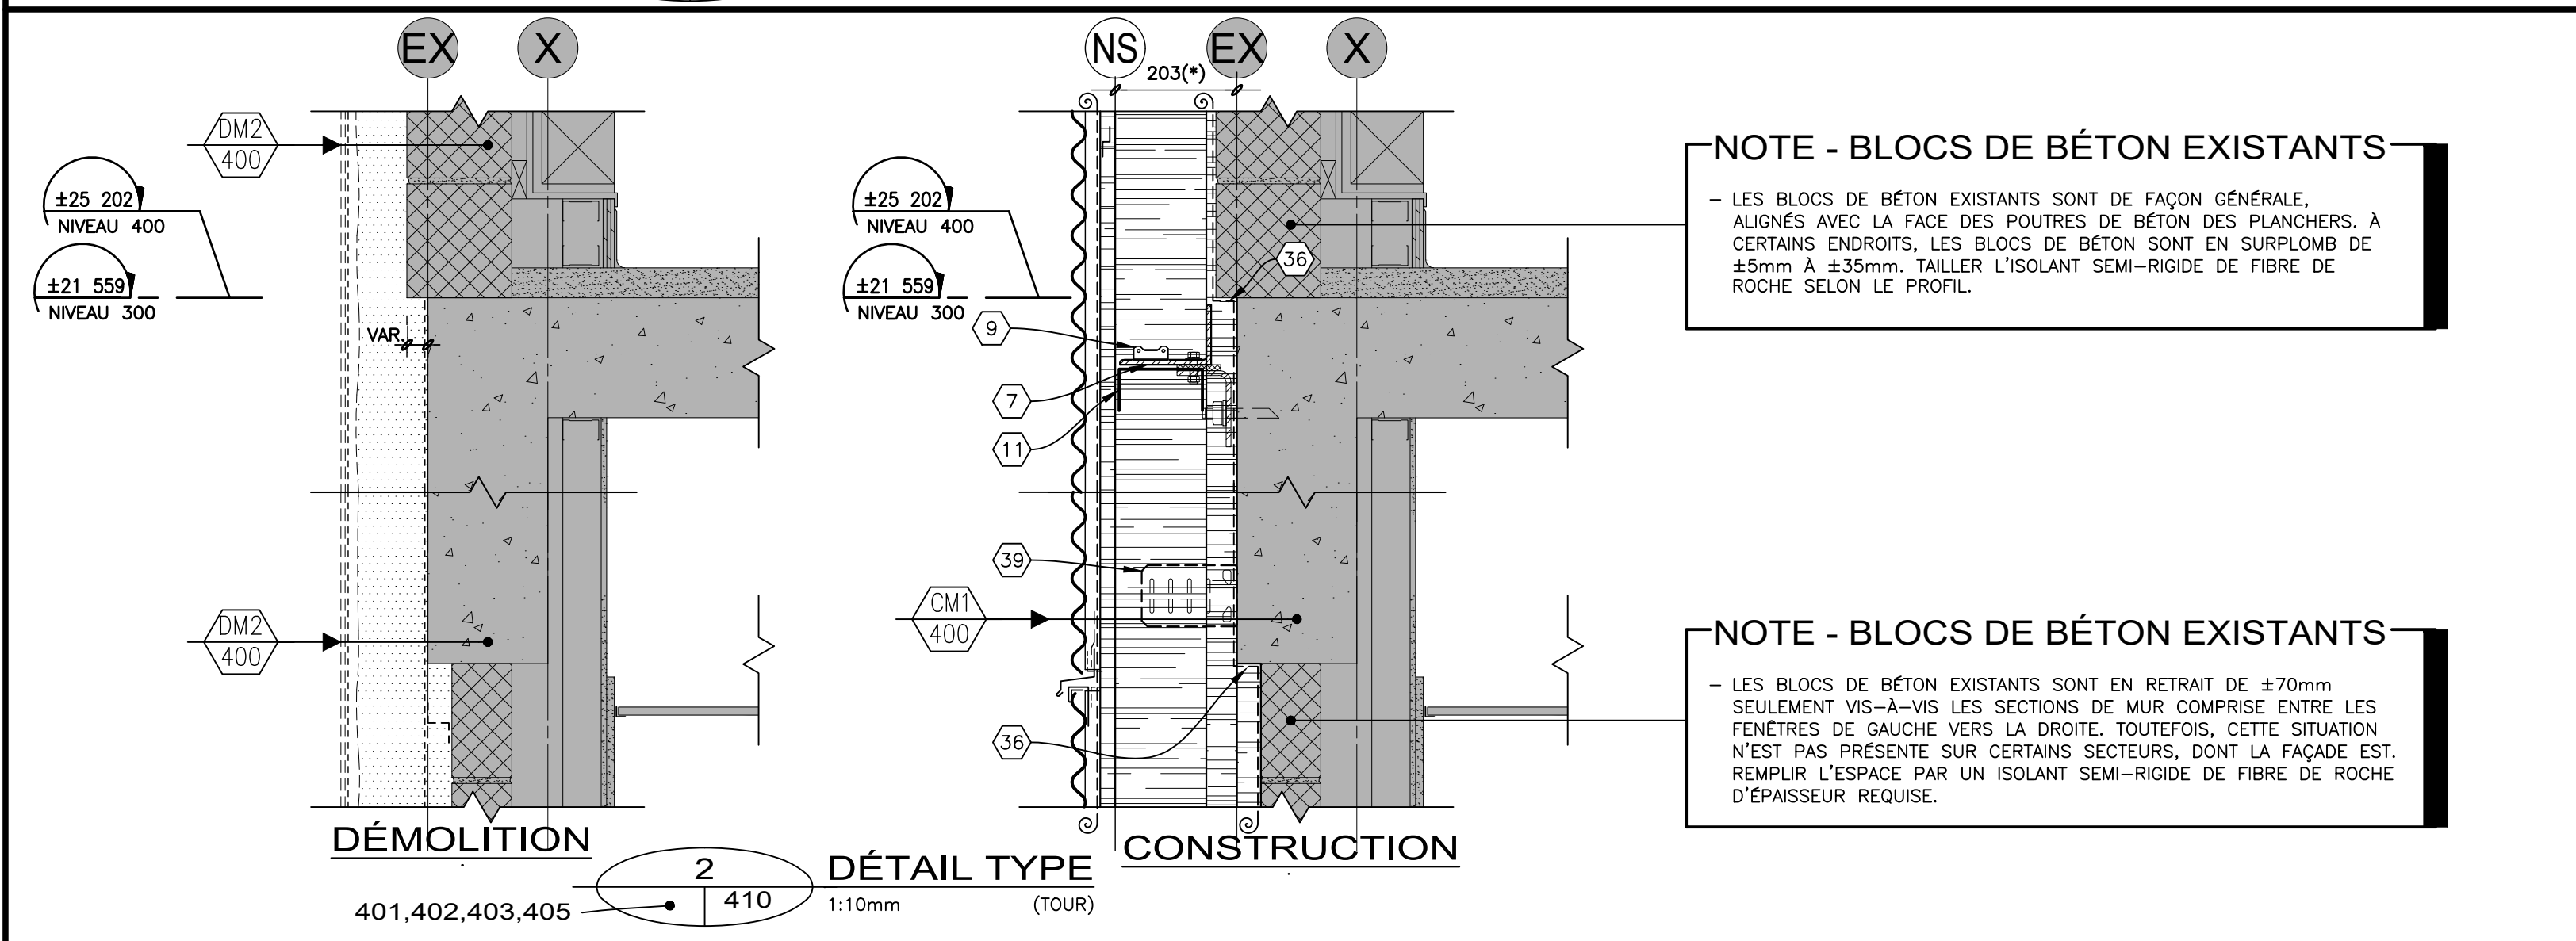


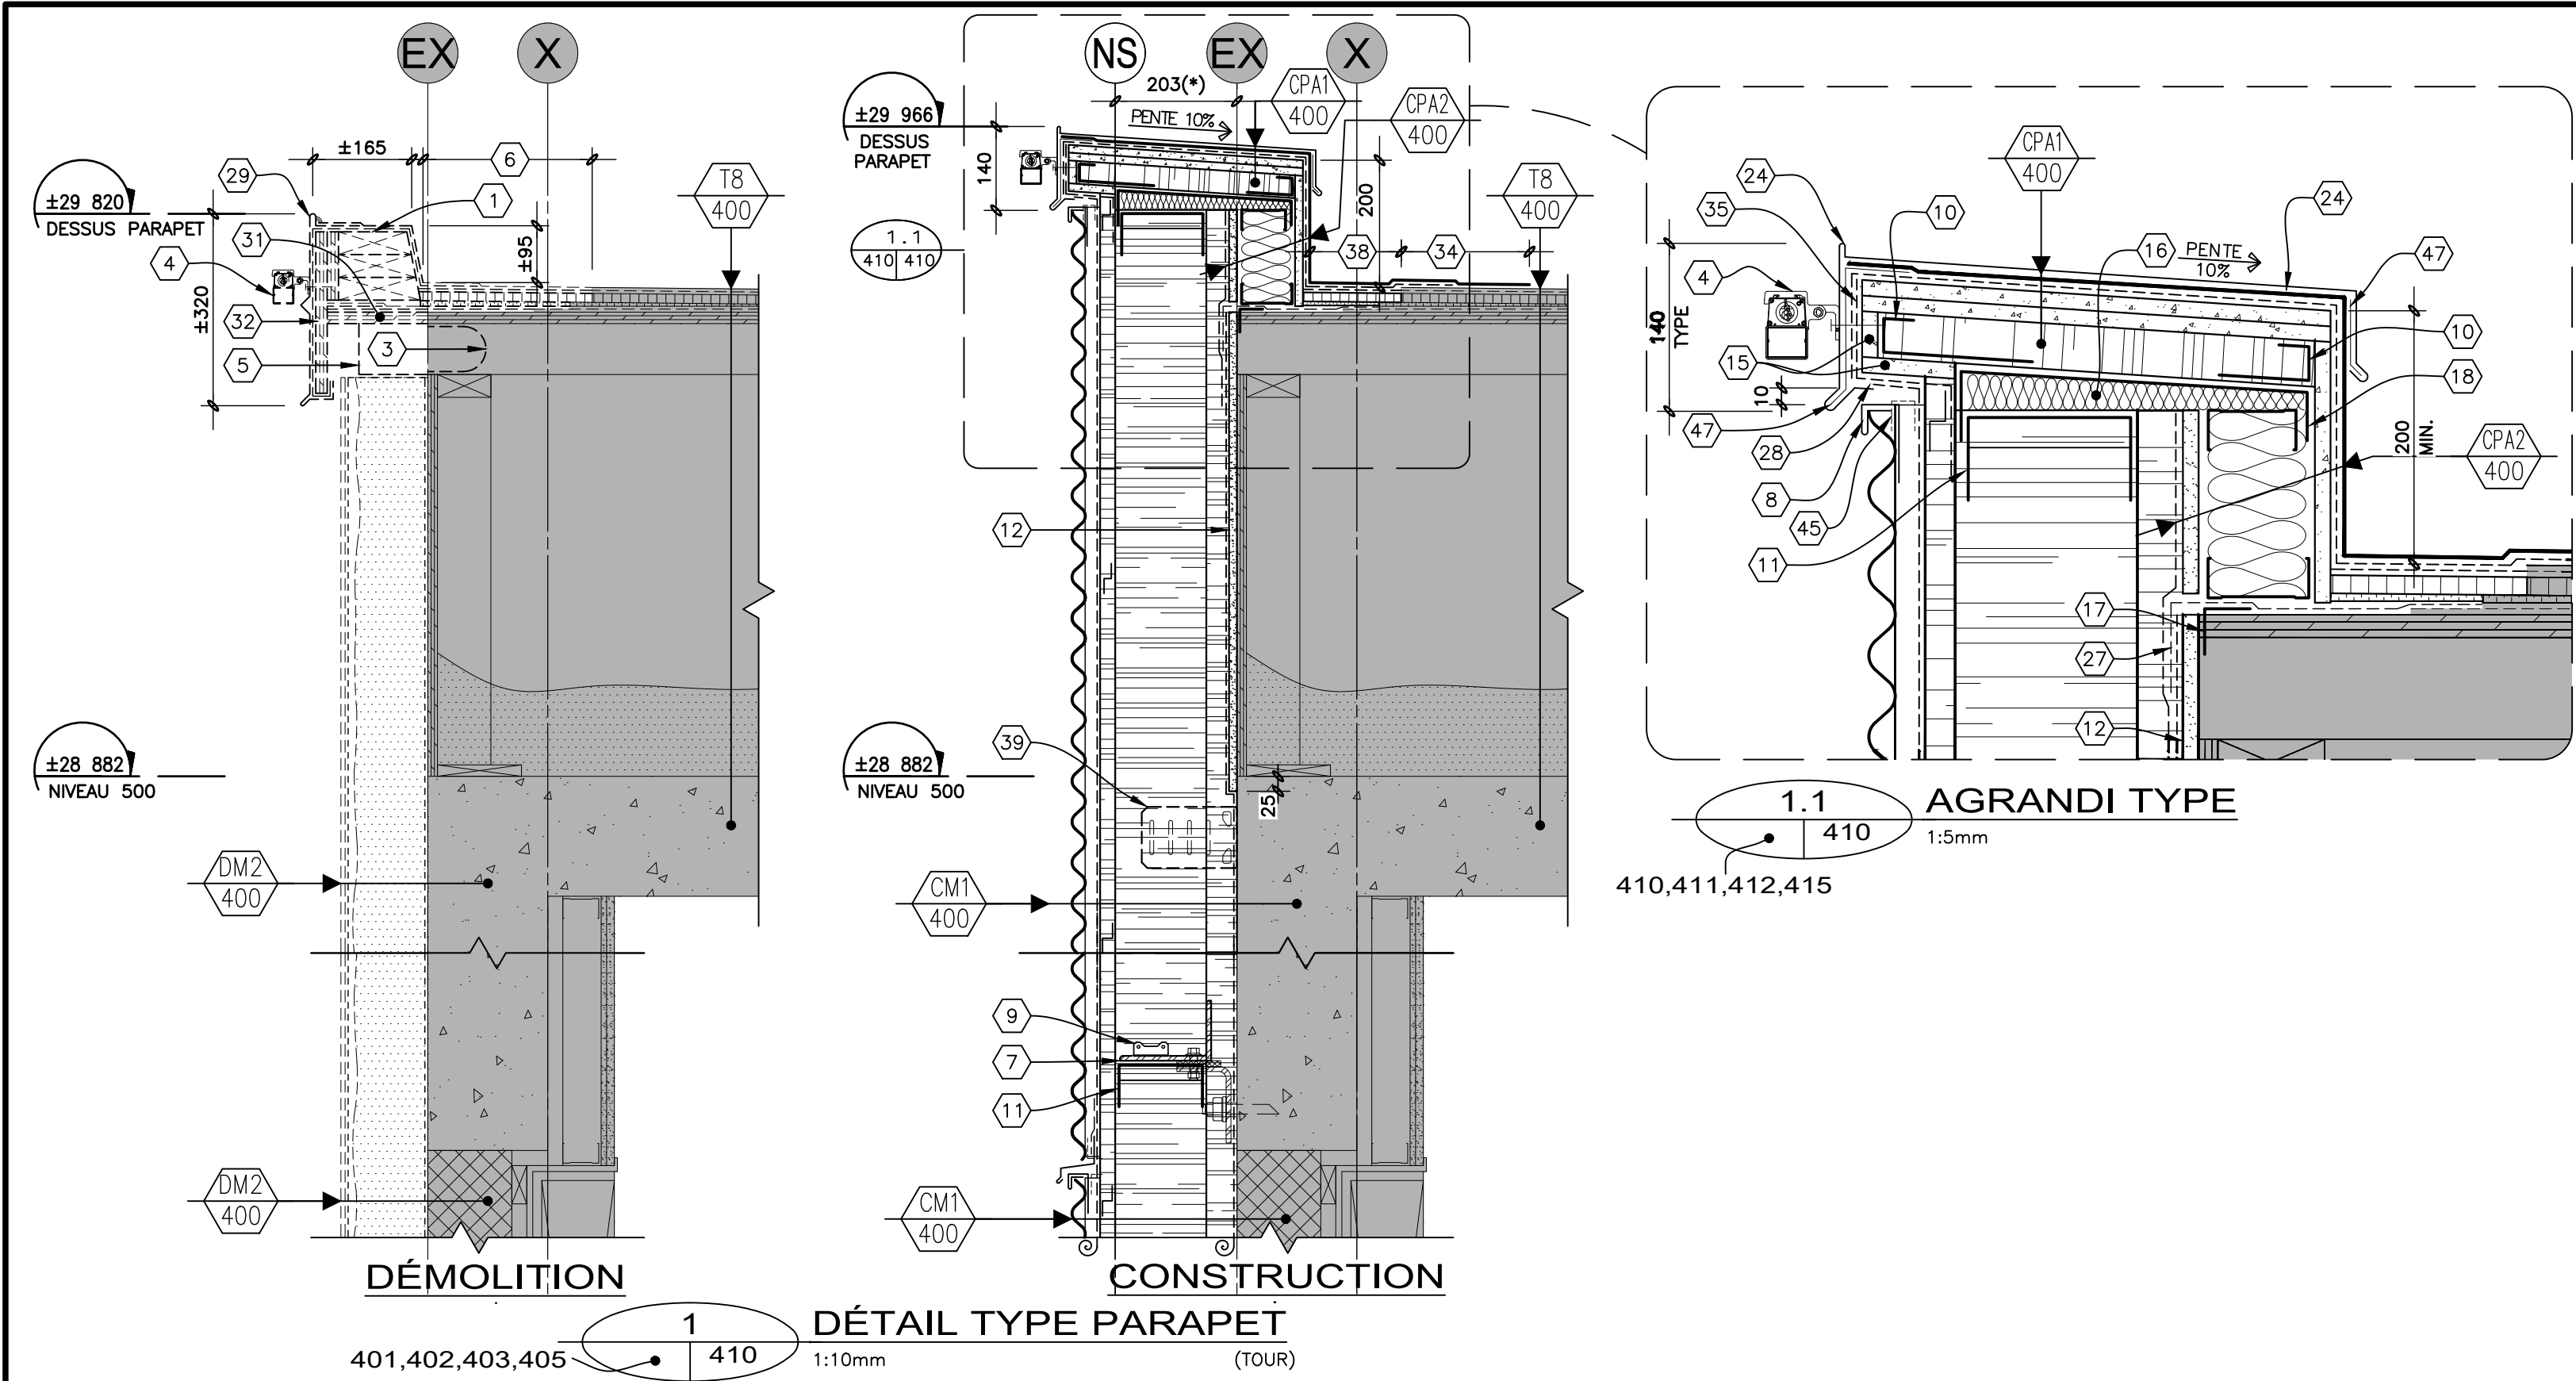

NOTES

- PARAPET PÉRIMÉTRIQUE EN PIÈCE DE BOIS 38mmX140mm RECOUVERT D'UNE MEMBRANE DE BITUME MODIFIÉ EXISTANT À DÉMOLIR.
- PLAQUE D'ACIER CONTINUE, VOIR STRUCTURE.
- FILTRE MÉDIA EXISTANT À ENLEVER.
- APPAREIL D'ÉCLAIRAGE CONTINUE SUR LA FAÇADE PRINCIPALE (SUD), EST ET OUEST DE LA TOUR À ENLEVER ET À RÉINSTALLER, VOIR INGÉNIEUR.
- MEMBRURE EXISTANTE DE 38mmX89mm À COUPER, VOIR STRUCTURE.
- OUVERTURE À FAIRE DANS LA TOITURE EXISTANTE SUR ±600mm POUR LA CONSTRUCTION DU NOUVEAU PARAPET. VOIR COMPOSITION DE TOIT SUR LE DÉTAIL.
- CORNIÈRE CONTINUE ET CONSOLE, VOIR STRUCTURE.
- MOULURE EN "J" EN ACIER ÉMAILLÉ, CAL.24.
- CONNECTEUR À CHAQUE COLOMBAGES OU BARRE "Z" SELON LE CAS, VOIR STRUCTURE.
- PLIAGE DE TÔLE EN "J", CAL.18 EN ACIER GALVANISÉ.
- LISSE DE DÉFLEXION, VOIR STRUCTURE.
- PANNEAU DE MAT DE FIBRE DE VERRE 16mm D'ÉPAISSEUR, TYPE X.
- REMONTEE DE MEMBRANES ET SUPPORT À DÉMOLIR.
- CHEVAUCHER LA NOUVELLE MEMBRANE SUR LES MEMBRANES DE LA TOITURE EXISTANTE SUR MINIMUM 150mm. DÉGRANULER LA MEMBRANE EXISTANTE AU PRÉALABLE.
- PANNEAU DE CIMENT 13mm.
- REMPLEIR L'ESPACE D'ISOLANT DE FIBRE DE ROCHE.
- PLIAGE EN ACIER GALVANISÉ CAL.16 CONTINUE.
- PLIAGE DE TÔLE EN "U", CAL.16 EN ACIER GALVANISÉ.
- ISOLANT RIGIDE DE FIBRE DE ROCHE 25mm.
- ISOLANT SEMI-RIGIDE DE FIBRE DE ROCHE DE 38mm D'ÉPAISSEUR.
- MEMBRANE DE FINITION GRANULÉE.
- MEMBRANE SOUS-COUCHE.
- TÔLE D'APPUI EN ACIER GALVANISÉ CAL.18.
- SOLIN EN ACIER ÉMAILLÉ, CAL.24 (JOINT AGRAFÉS).
- MEMBRANE AUTOCOLLANTE PARE-VAPEUR.
- BARRE D'ANCRAGE DE LA MEMBRANE.
- MEMBRANE AUTOCOLLANTE. CHEVAUCHER D'AU MOINS 25mm LA MEMBRANE DU MUR ET LA MEMBRANE EXISTANTE DE LA TOITURE.
- SCELLER LA MEMBRANE PARE-INTÉMPIRIES SUR LE PARAPET AVEC UN RUBAN AUTOCOLLANT.
- SOLIN EXISTANT À DÉMOLIR.
- PANNEAU DE POLYMERES RENFORCÉ DE FIBRES DE VERRE 7mm D'ÉPAISSEUR À DÉMOLIR.
- CONTREPLAQUÉ À PLUS EXISTANT À COUPER.
- CONTREPLAQUÉ À PLUS EXISTANT À DÉMOLIR.
- PIÈCE DE BOIS EXISTANTE À DÉMOLIR.
- CHEVAUCHER LA NOUVELLE MEMBRANE SUR LES MEMBRANES DE LA TOITURE EXISTANTE SUR MINIMUM 300mm. DÉGRANULER LA MEMBRANE EXISTANTE AU PRÉALABLE.
- MEMBRANE AUTOCOLLANTE.
- MEMBRANES DE RENFORT, VOIR NOTES "CONDITIONS EXISTANTES MUR DE FOND EN BLOCS ET BÉTON" PAGE 400.
- CALE D'AJUSTEMENT EN ACIER GALVANISÉ D'ÉPAISSEUR REQUISE.
- RAGRÉER LA TOITURE TEL QUE L'EXISTANT, VOIR COMPOSITION SUR LE DÉTAIL.
- ETRIER, VOIR STRUCTURE.
- DÉMOLIR LES MEMBRANES EXISTANTES SUR LE DESSUS DU PARAPET.
- CORNIÈRE, VOIR STRUCTURE.
- PLIAGE DE TÔLE EN ACIER GALVANISÉ, CAL.22.
- RIVET EN ACIER INOXYDABLE.
- PLIAGE DE TÔLE, CAL.18 EN ACIER GALVANISÉ, FIXÉ SUR LE DESSUS DU PARAPET EXISTANT.
- MOUSTQUAIRE.
- SCELLER LA MEMBRANE PARE-INTÉMPIRIES SUR LE SOLIN AVEC UN RUBAN AUTOCOLLANT.
- AGRAFE EN ACIER GALVANISÉ, CAL.24 CONTINUE.
- POUTRE D'ACIER, VOIR STRUCTURE.
- PLAQUE D'ACIER PONCTUELLE, VOIR STRUCTURE.
- TÔLE PLIÉE CONTINUE EN ACIER GALVANISÉ, CAL. 18.
- ISOLANT SEMI-RIGIDE DE FIBRE DE ROCHE 25mm D'ÉPAISSEUR VIS-À-VIS DE LA POUTRE D'ACIER.
- BOUT DU PANNEAU REPLIÉ VERS L'INTÉRIEUR.
- CRÉER DES ÉVÉNEMENTS À MAÇONNERIE DANS L'AVANT DERNIER RANG DE BRIQUES DU MUR EXISTANT, EN ÉVIDANT LE JOINT DE MORTIER VERTICAL À TOUS LES 3 BRIQUES.

LÉGENDE

- EXISTANT À CONSERVER.
- ÉLÉMENT À DÉMOLIR.
- AXE EXISTANT
- EXTÉRIEUR DE LA STRUCTURE DE BÉTON EXISTANTE DE LA TOUR
- NOUVEL AXE: FACE EXTÉRIÈURE DES BARRES Z ET COLOMBAGES DE LA TOUR. VOIR STRUCTURE.
- (*) VOIR NOTE GÉNÉRAL PAGE 400.

NE DOIT PAS SERVIR À L'EXÉCUTION

Le présent document est émis pour la seule fin identifiée. Son contenu est protégé par les droits d'auteur et toute reproduction ou modification, partielle ou totale, est interdite sans l'autorisation écrite de gagnon, letellier, cyr, ricard, mathieu, proulx, savard consortium d'architectes.

GLCRM | Proulx Savard |

GLCRM:
128, Avenue de la Cathédrale,
Bureau 201
Rimouski, QC, G5L 5H7
(418) 722-7655

2406, Ch. des Quatres-Bourgeois,
Bureau 100
Québec, QC, G1V 1W5
(418) 647-1700

Proulx Savard Architectes:
75, boul. Arthur-Buies Ouest,
Rimouski QC G5L 5C2
(418) 723-5543

ARCHITECTURE

CONSULTANTS

Ordre des architectes du Québec
A-3996
DAVID SAVARD
ARCHITECTE












































Ordre des architectes du Québec
3726
FRANÇOIS MATHIEU
ARCHITECTE


DESSINATEUR (S)	DOSSIER No.	DATE	RÉVISIONS			
			No	DATE	REVISIONS	REVISIONS
DB: M.P.A.L.	24-187 / 687-24	SEPTEMBRE 2024	05	2024-09-04	DÉFINITIVES POUR SOUMISSION	
ÉCHELLE	INDIQUÉE	04	04	2024-08-21	DÉFINITIVES 100% POUR APPROBATION	
			03	2024-08-03	DÉFINITIVES 80% POUR APPROBATION	
			02	2024-05-14	DÉFINITIVES 40% POUR APPROBATION	
PROJET	HÔPITAL DE CHANDLER, Chandler (Réfection de l'enveloppe)	01	01	2024-02-27	PRÉLIMINAIRES 50% POUR APPROBATION	
			No	DATE	REVISIONS	REVISIONS

COUPE DE MUR TYPE DÉMOLITION ET CONSTRUCTION

PROPRIÉTAIRE: **Santé Québec**

410

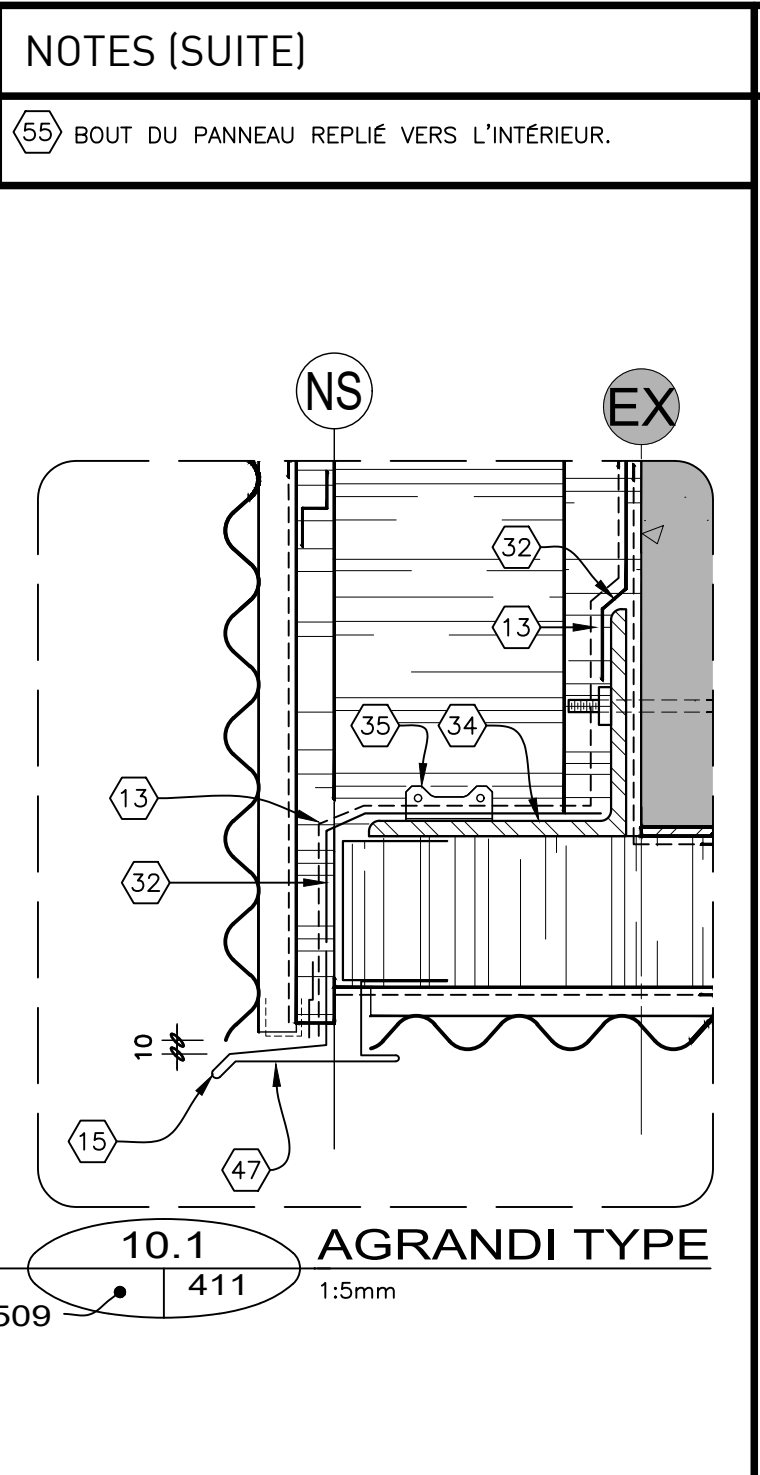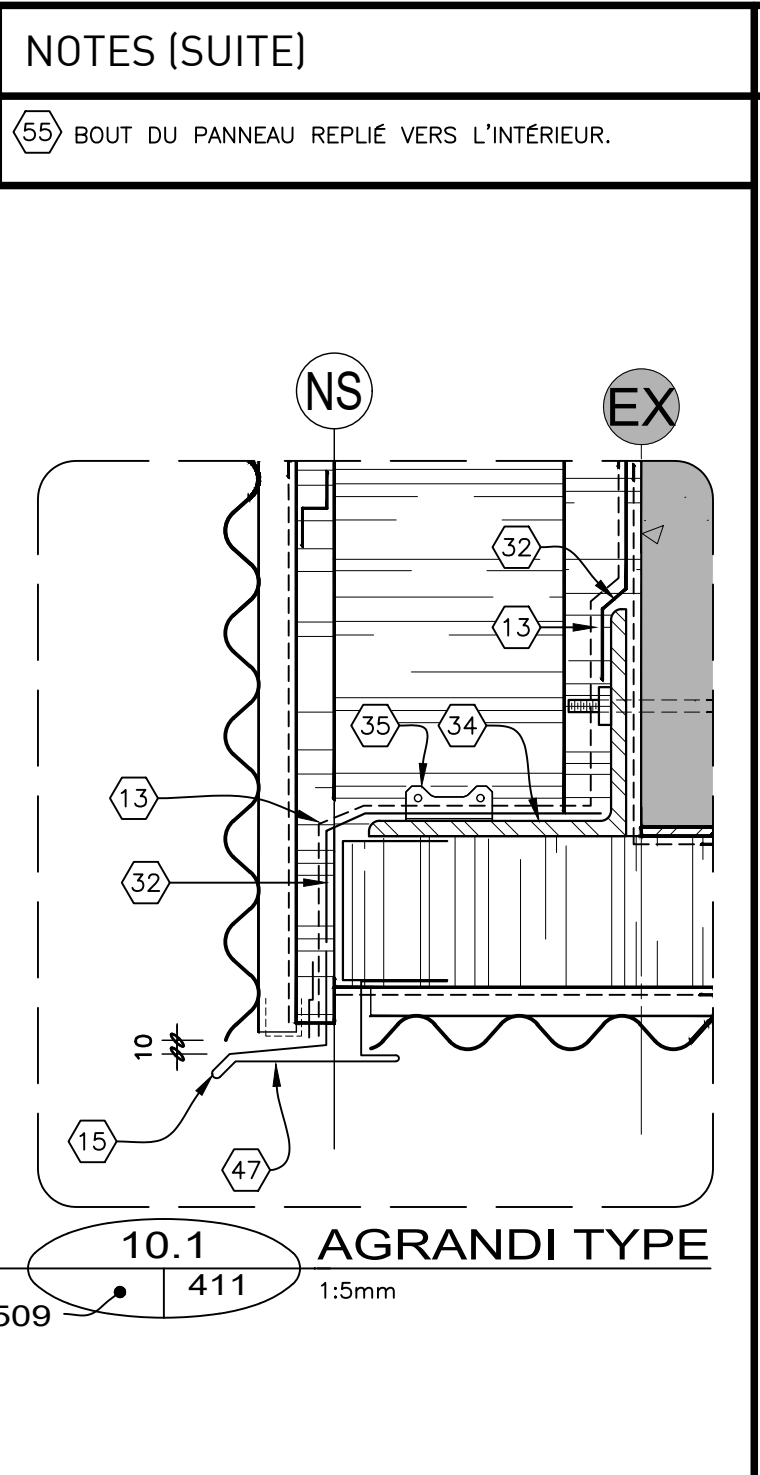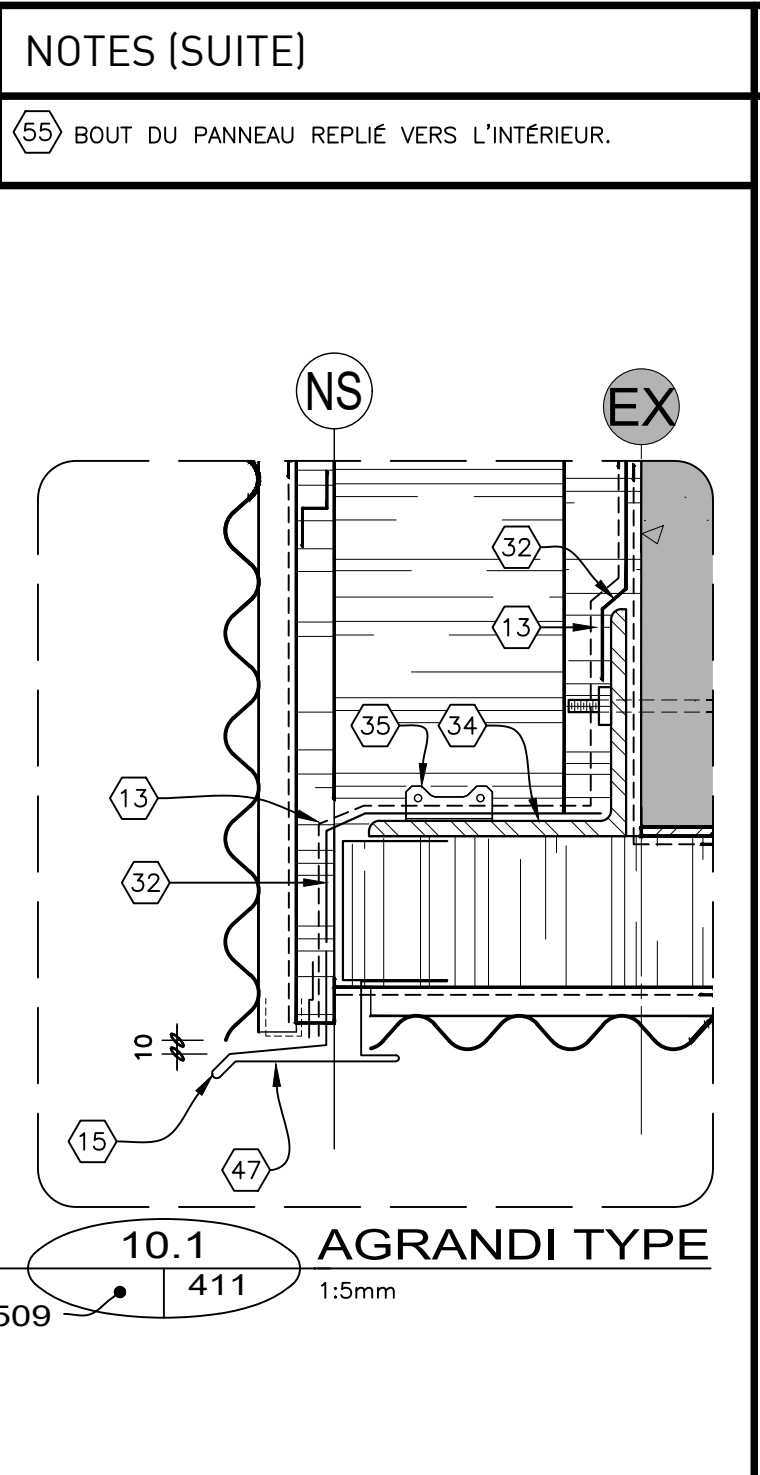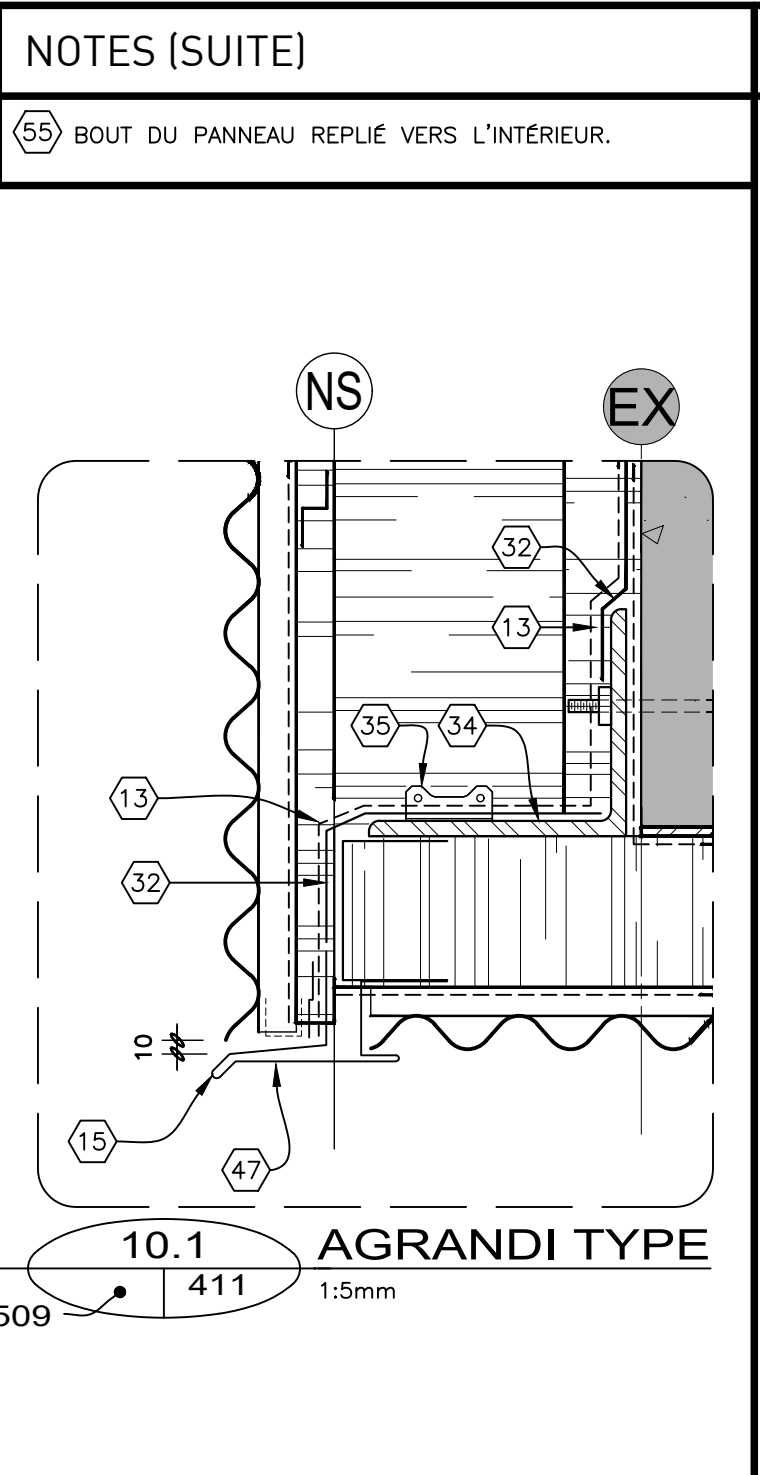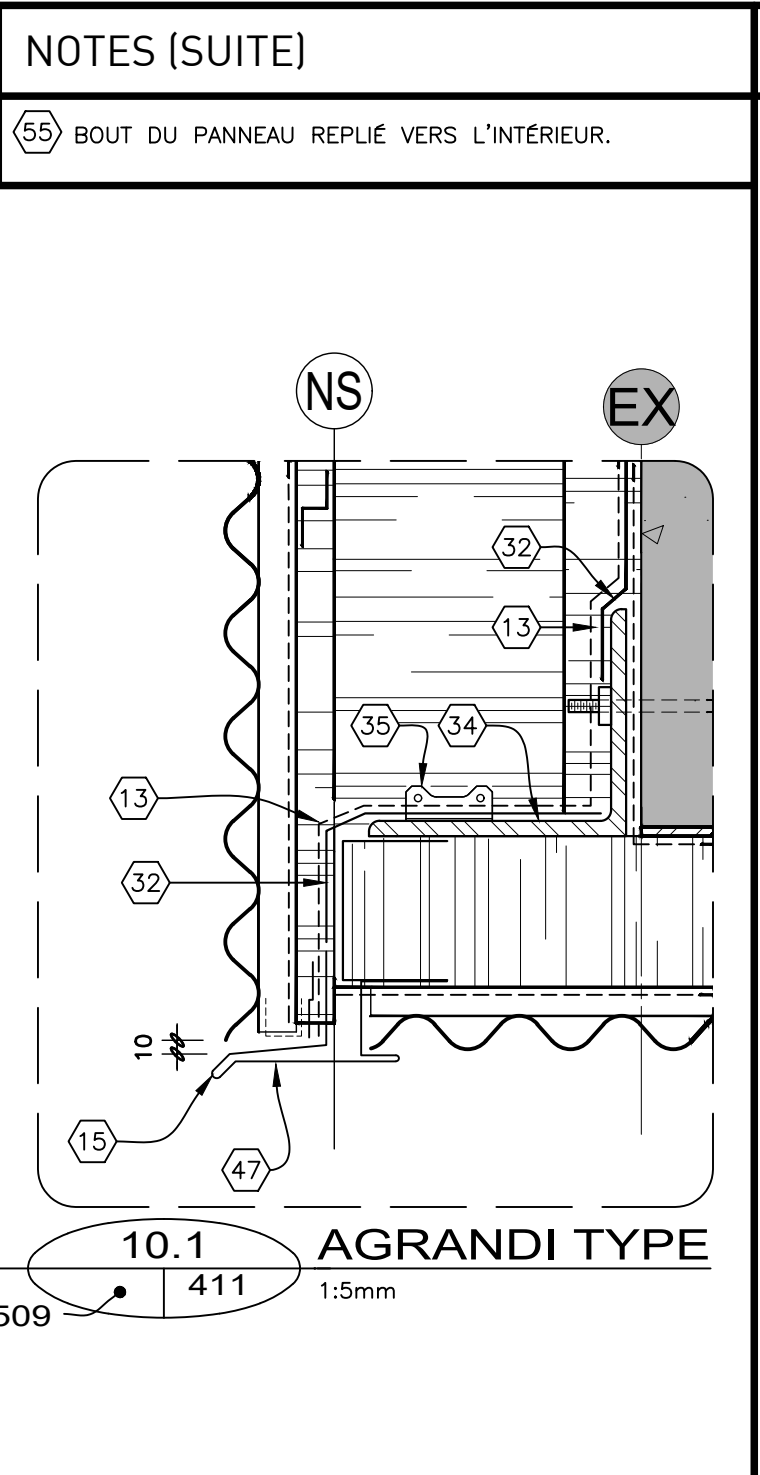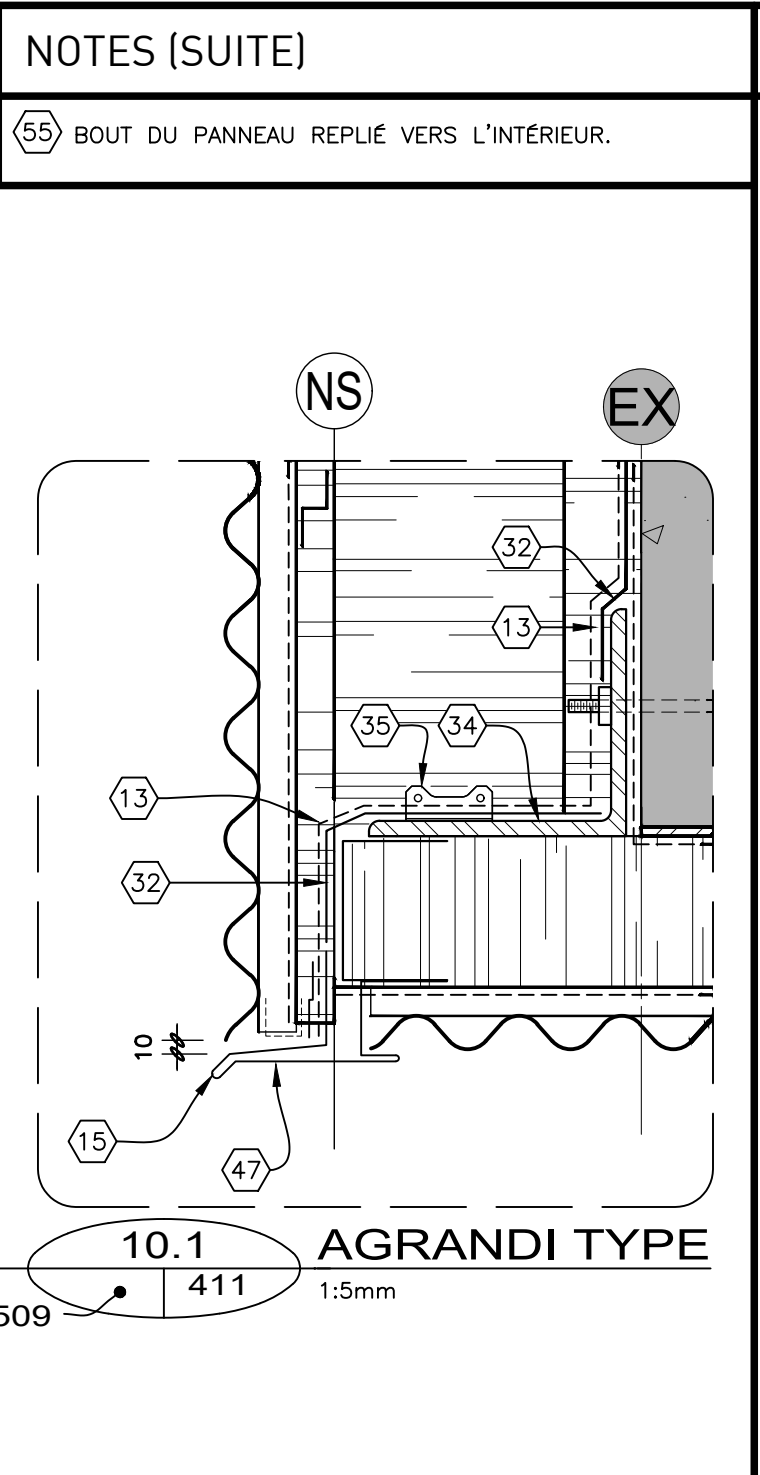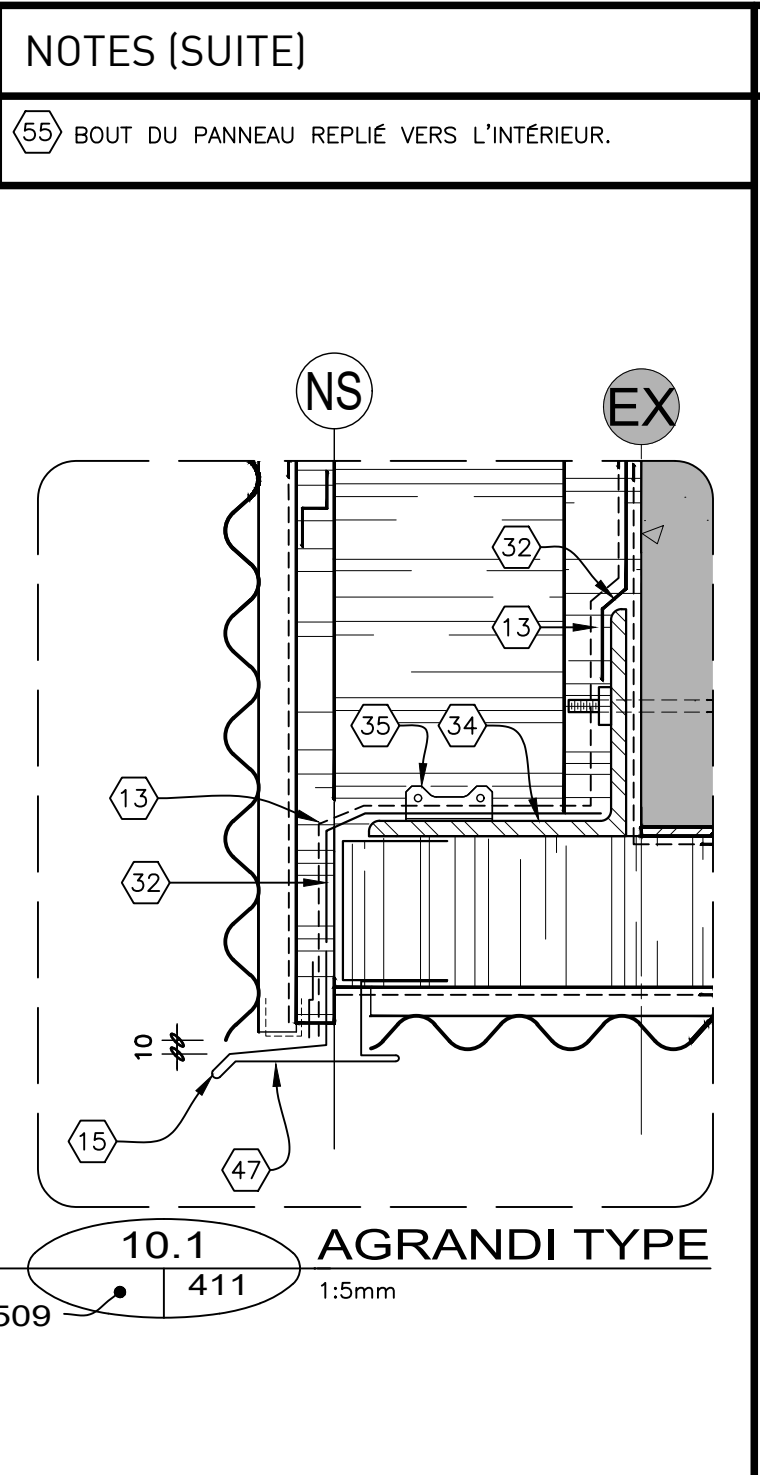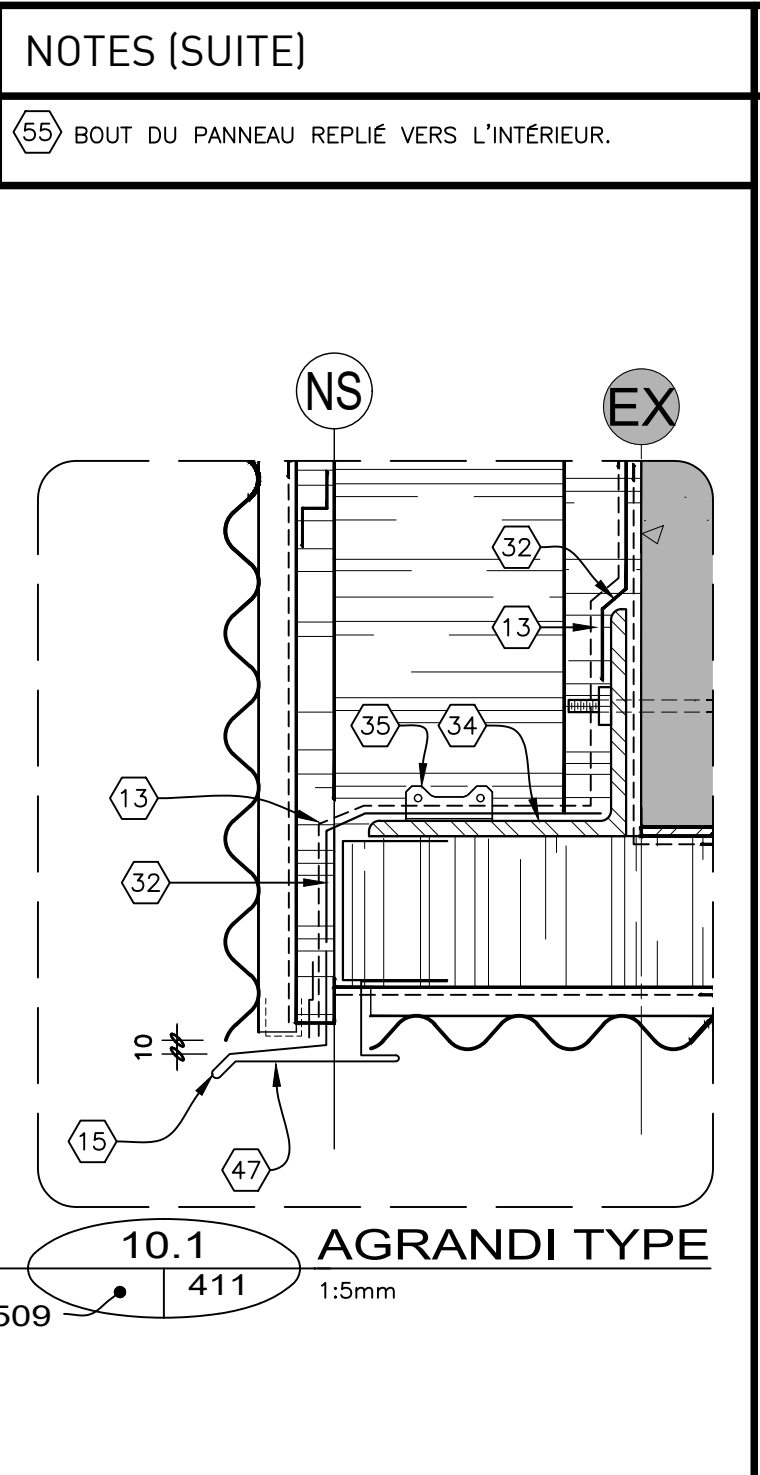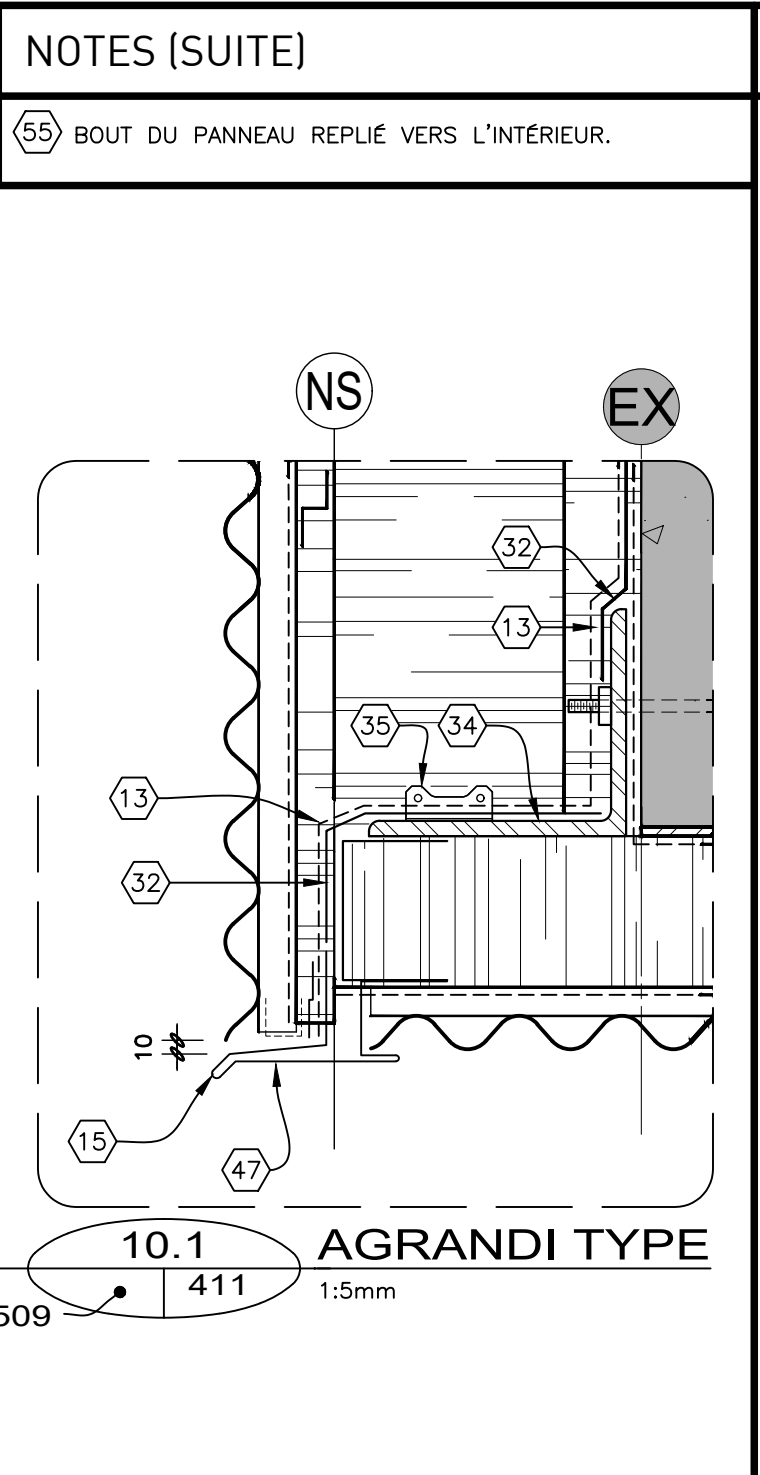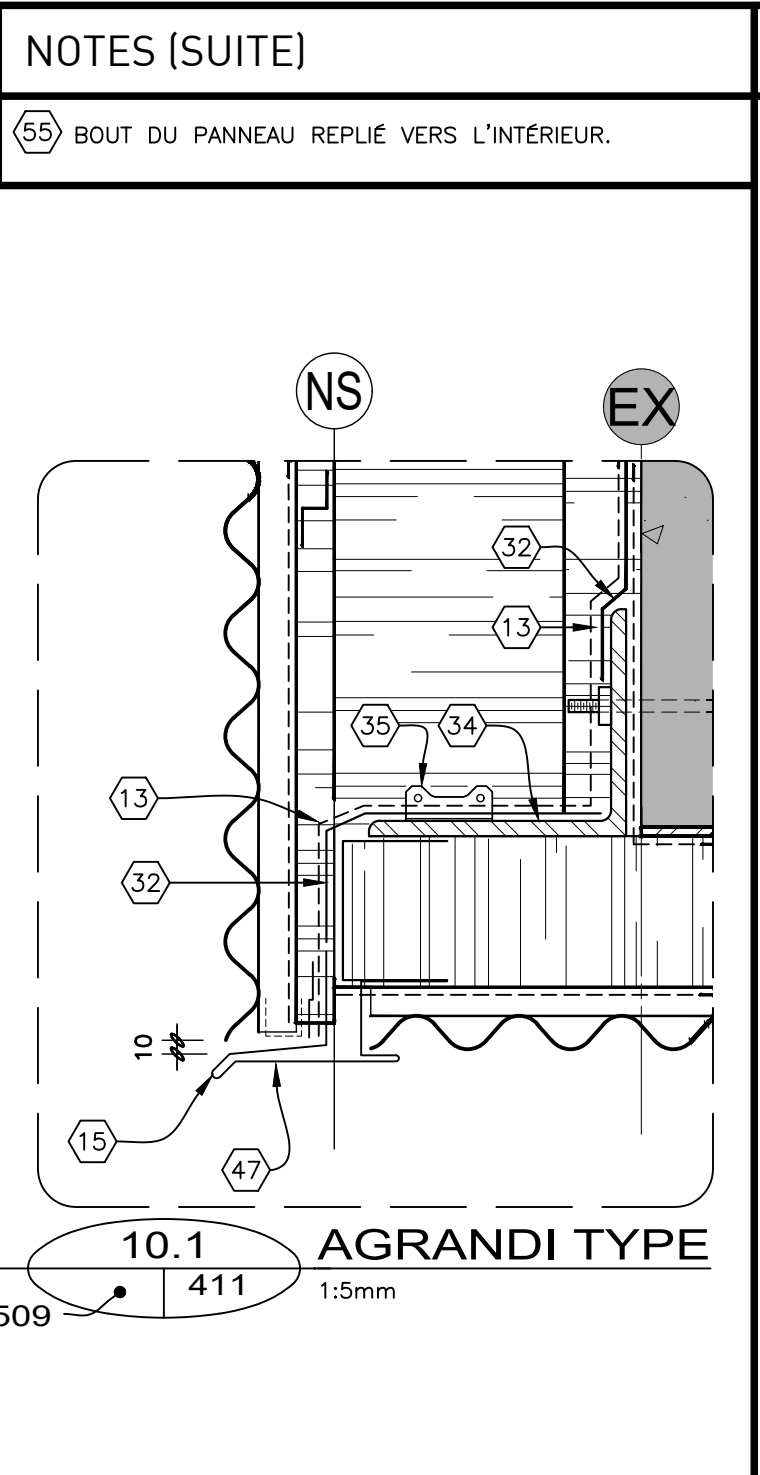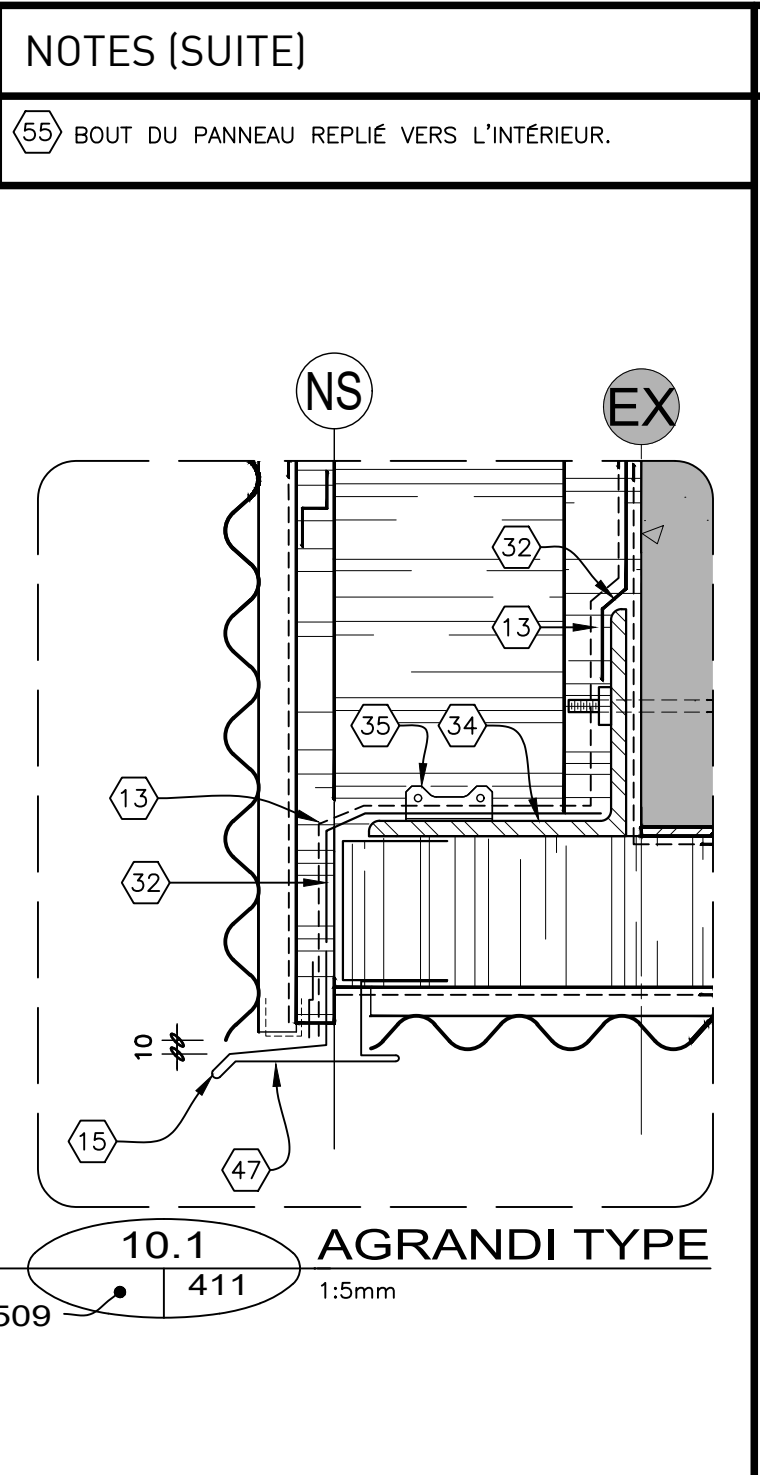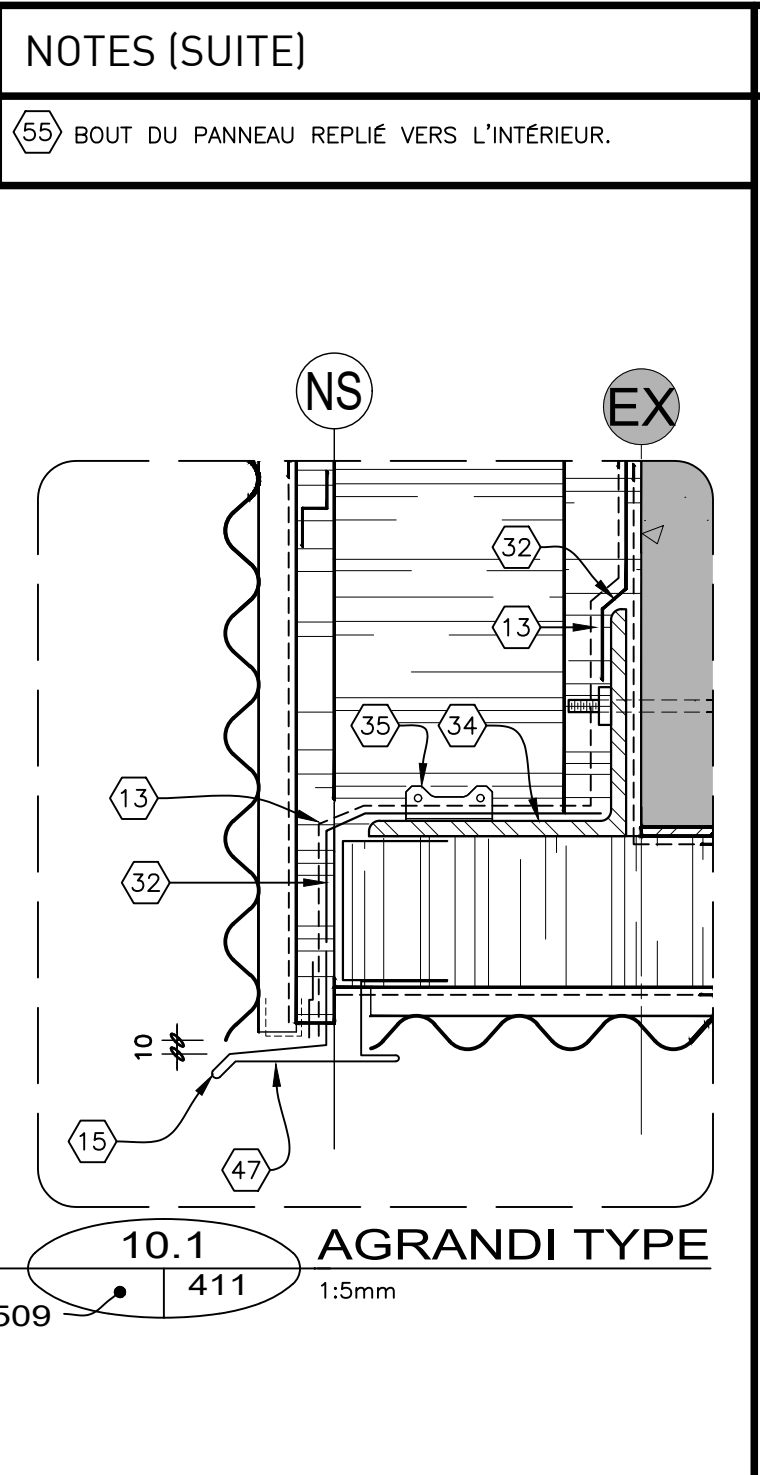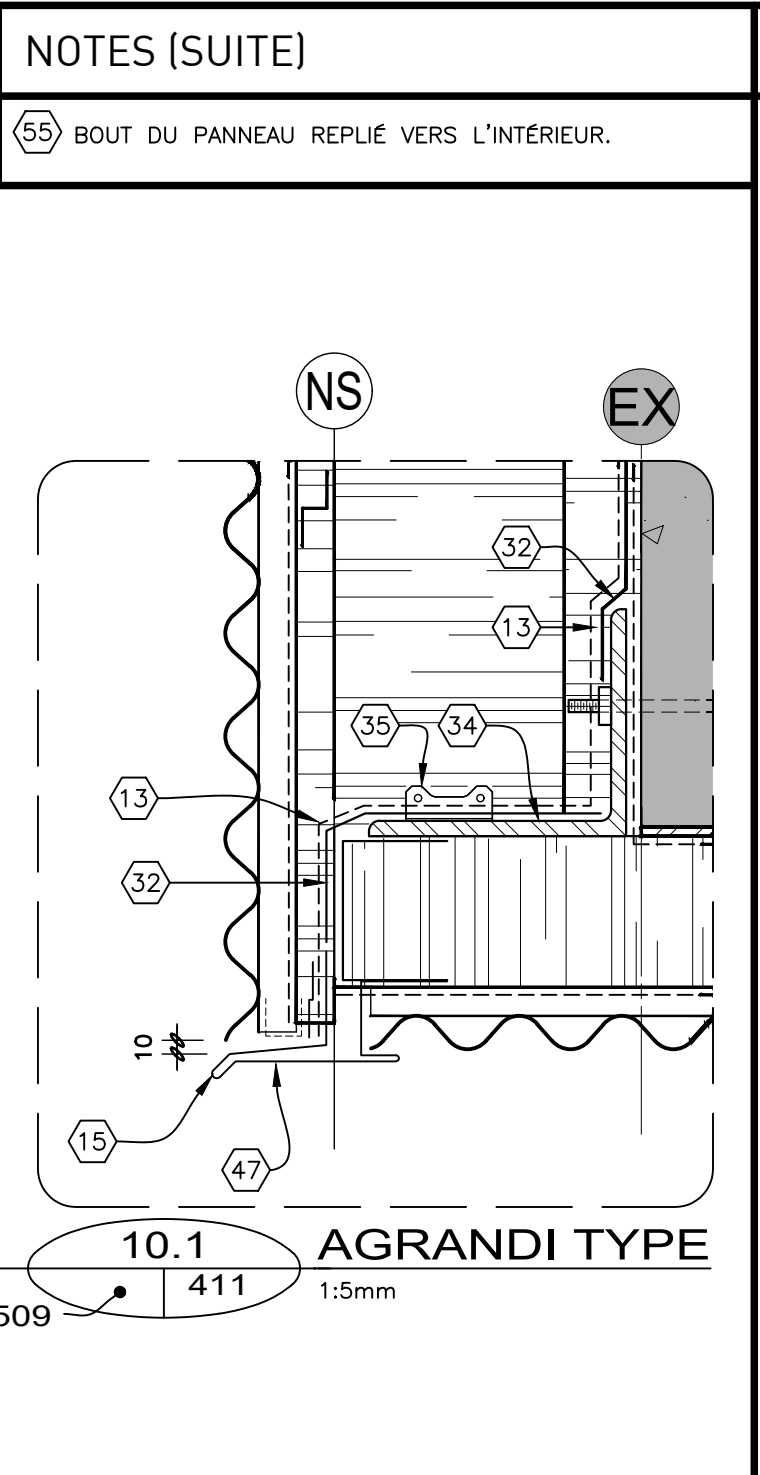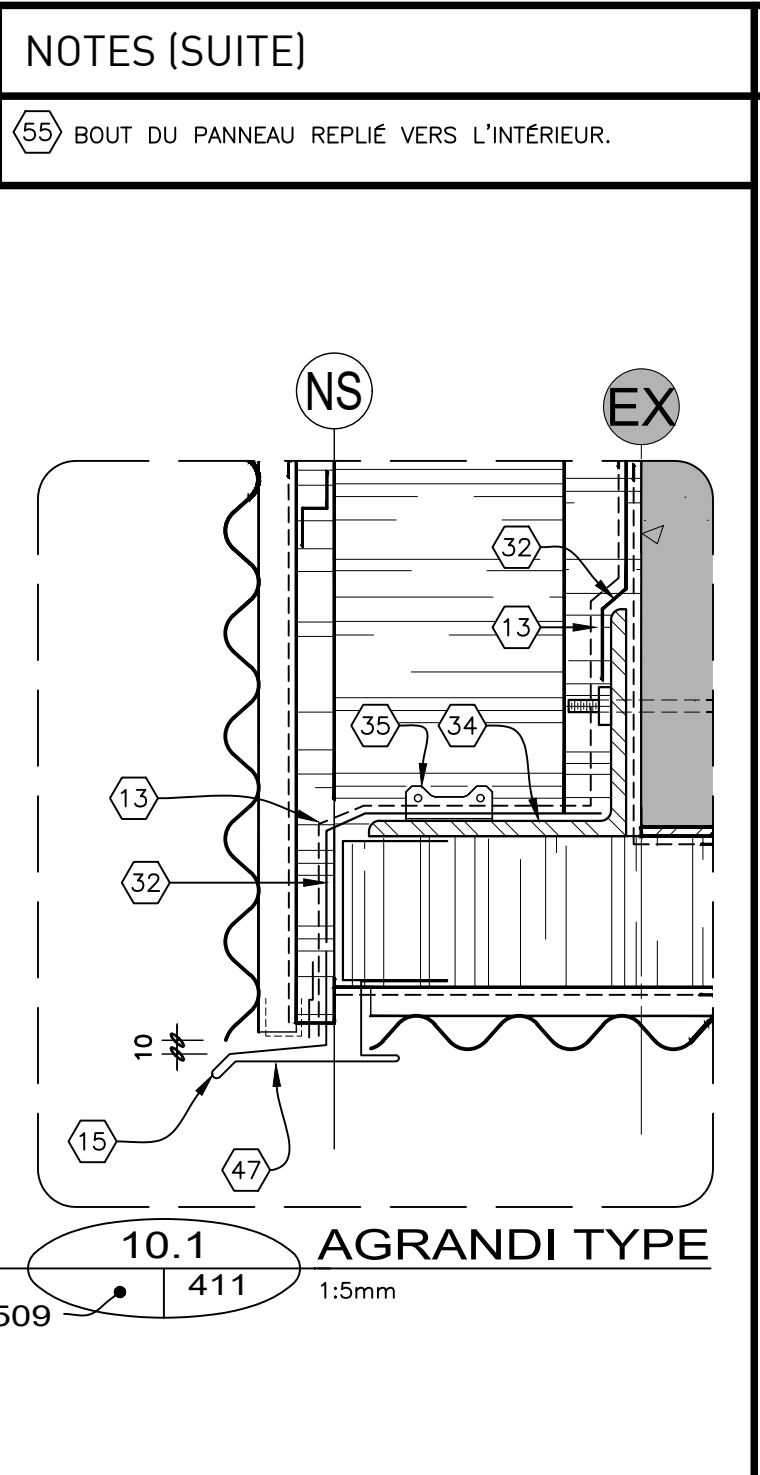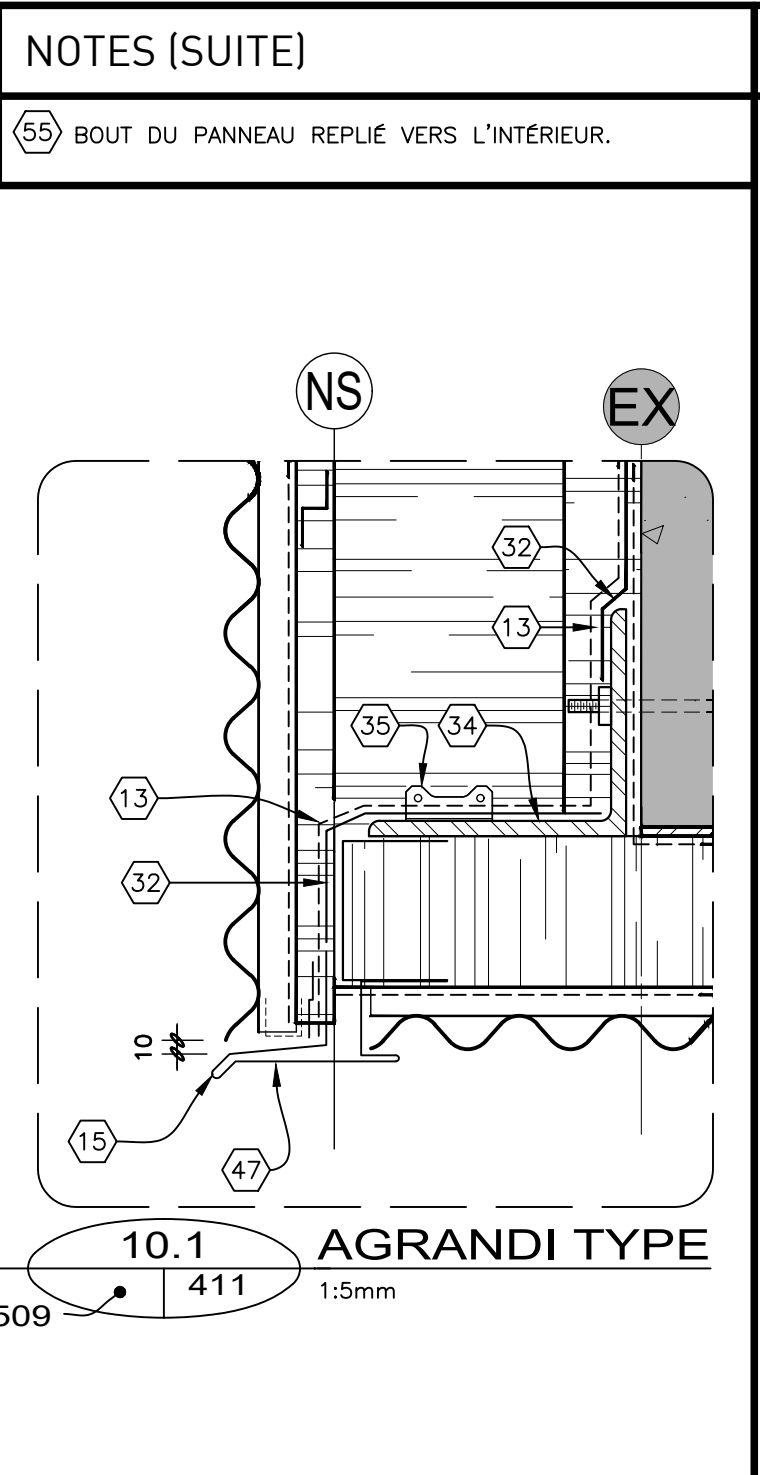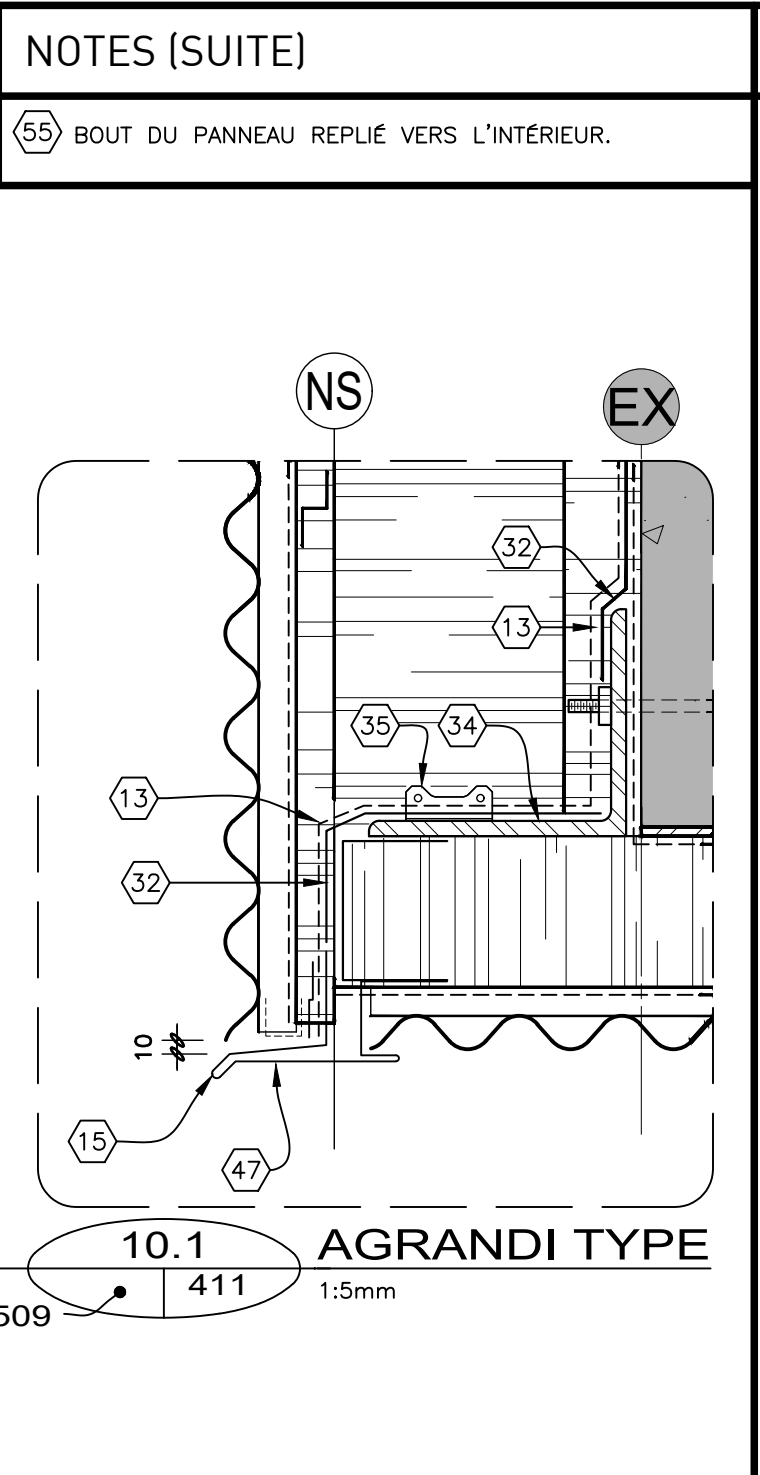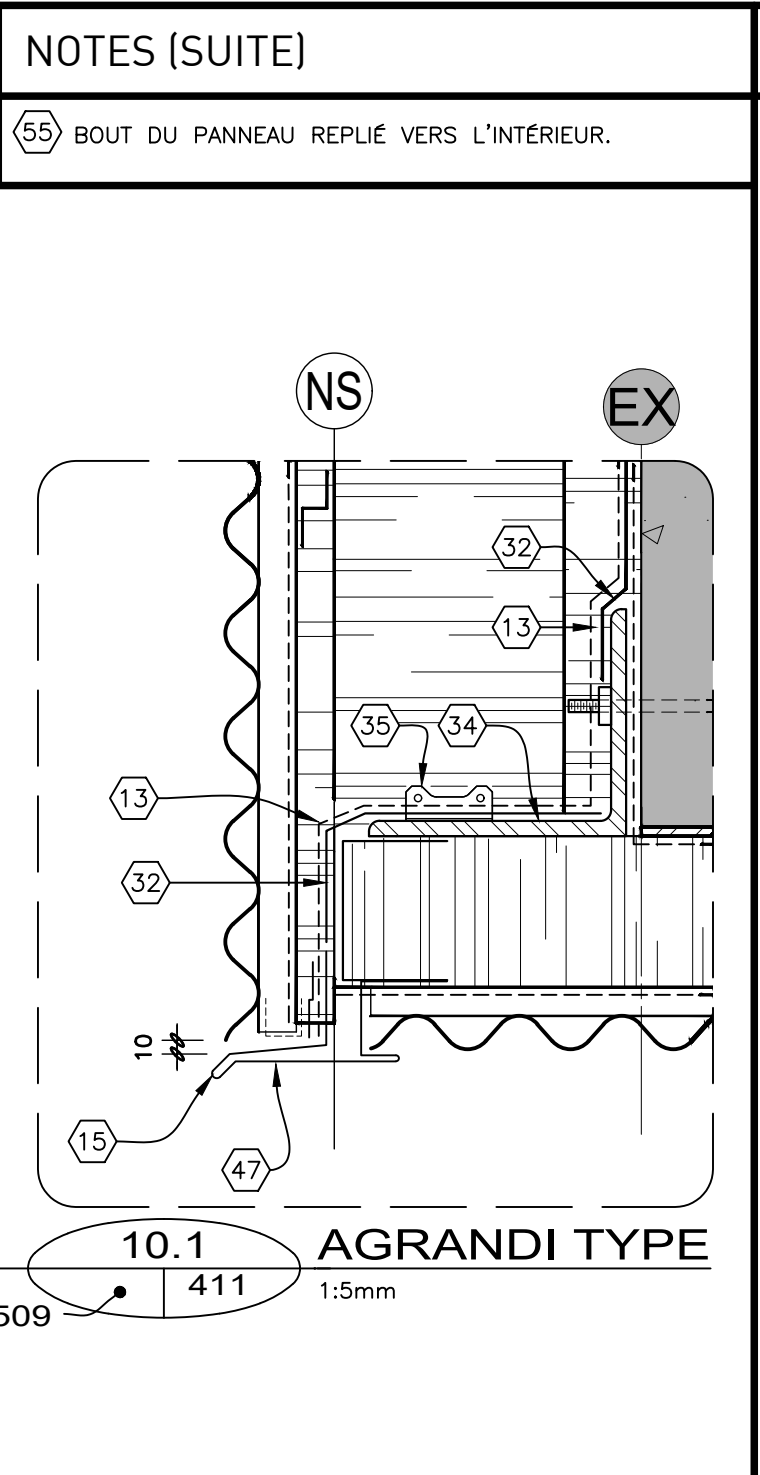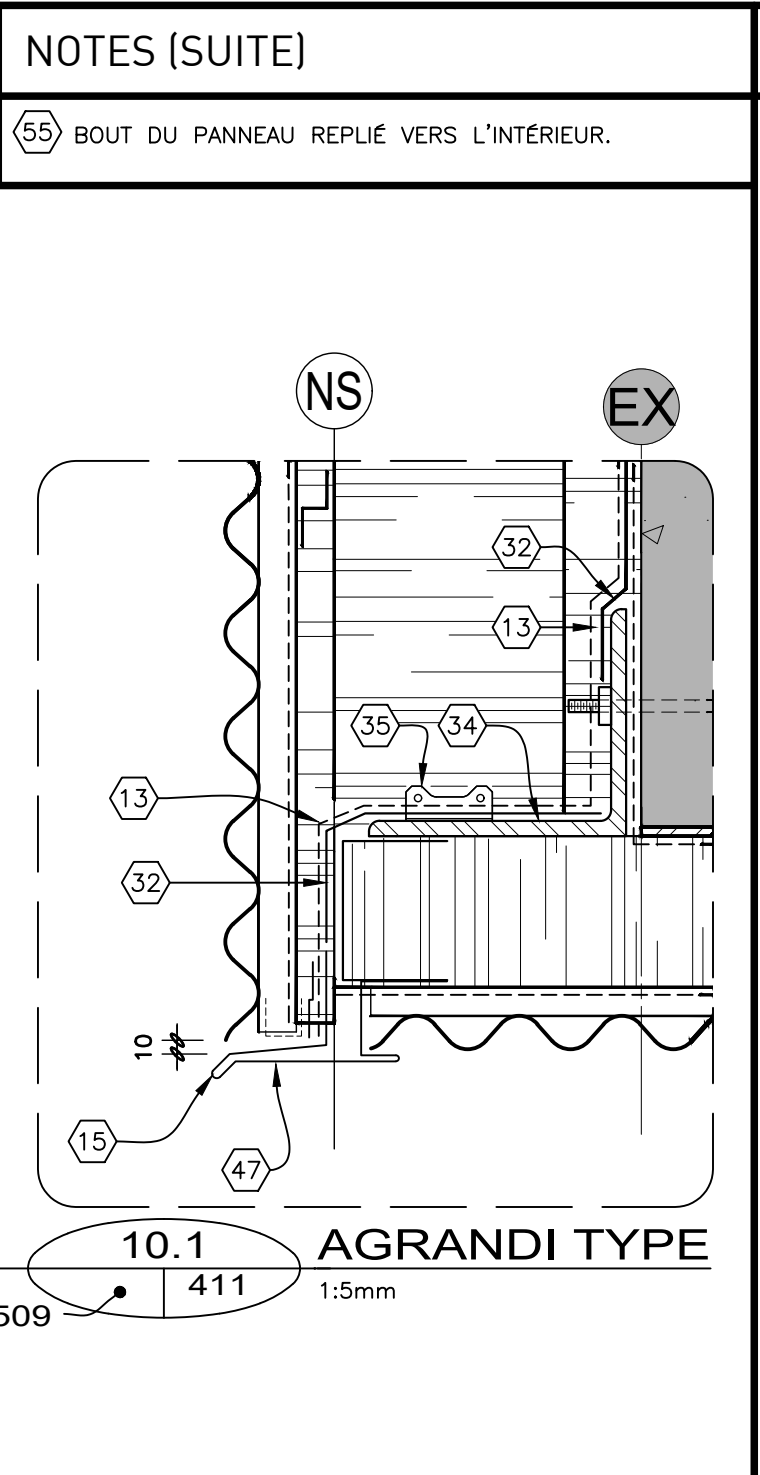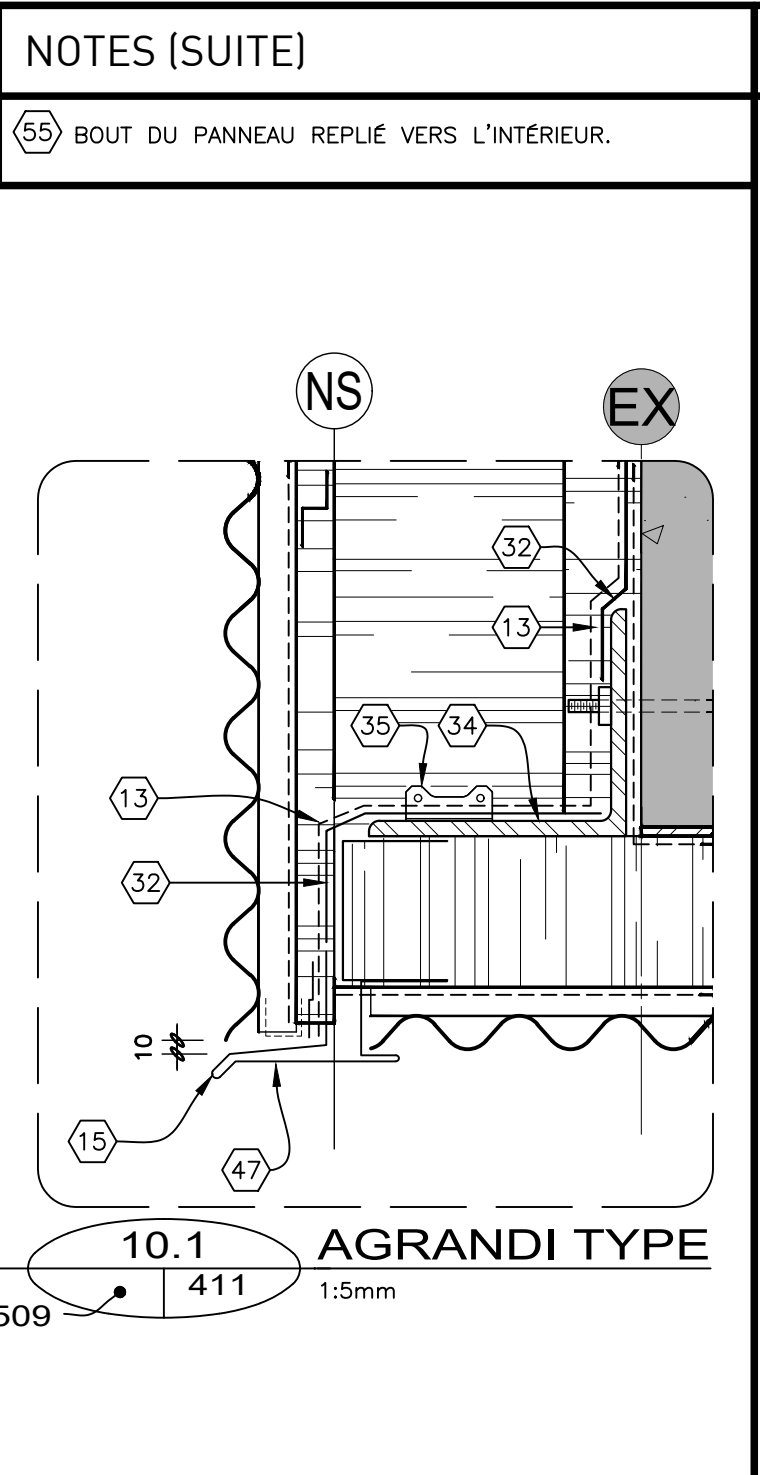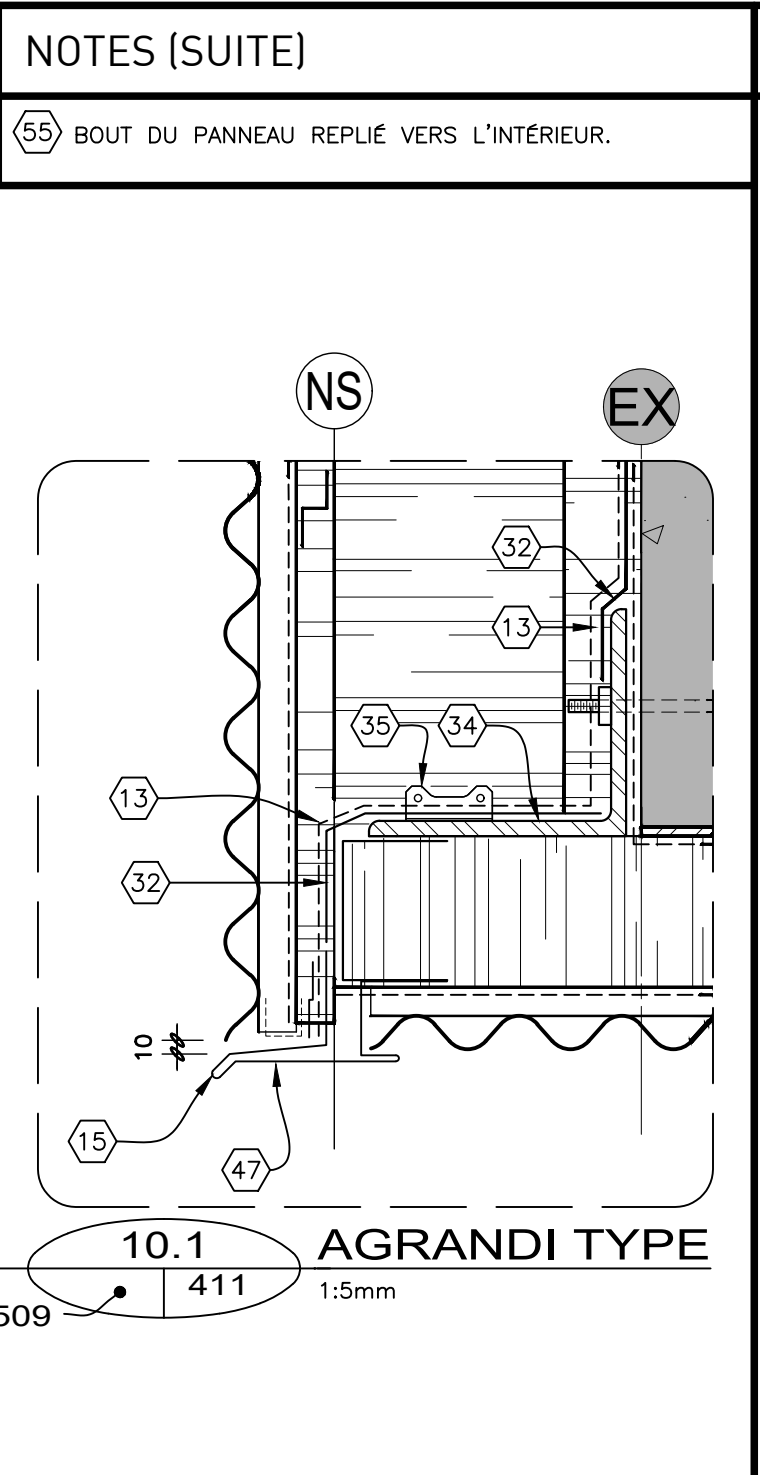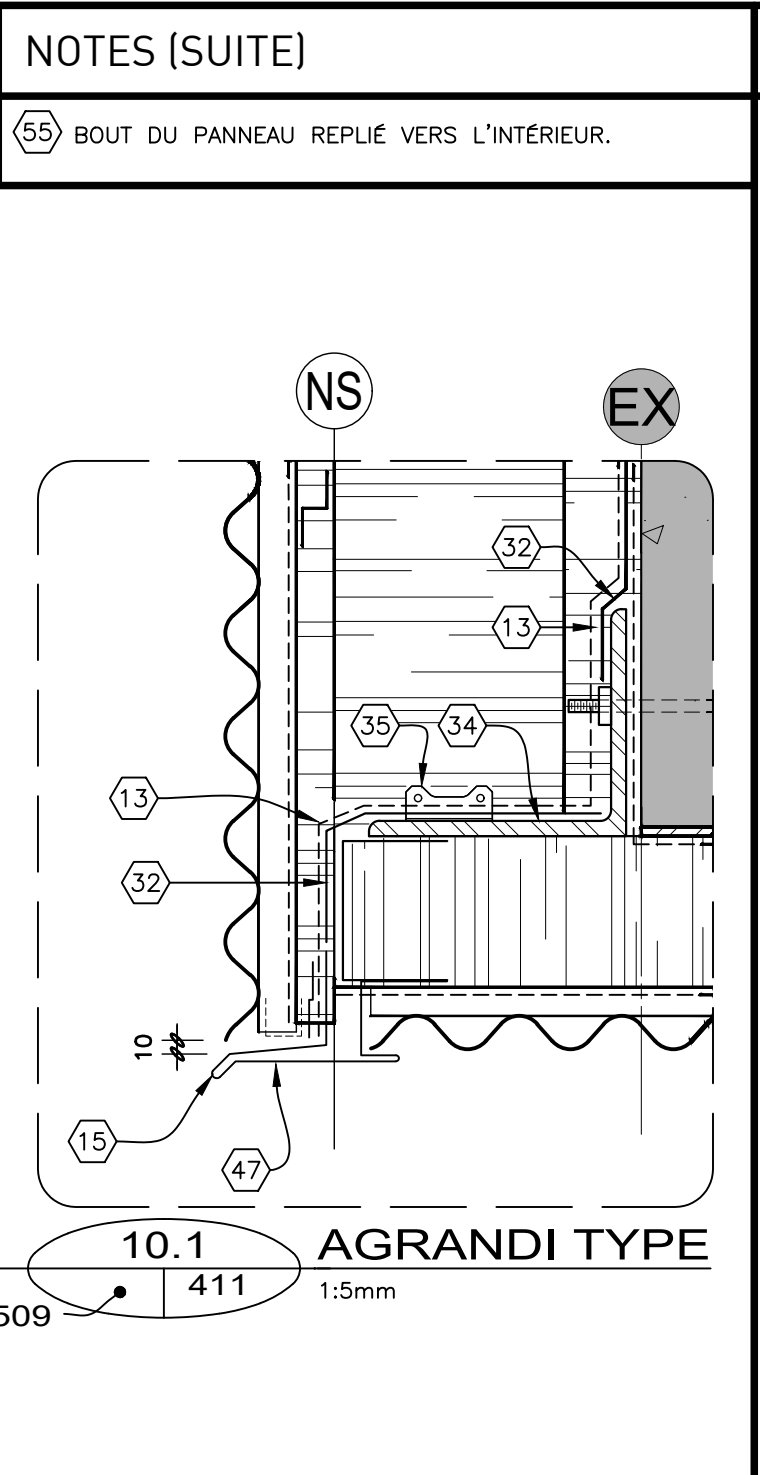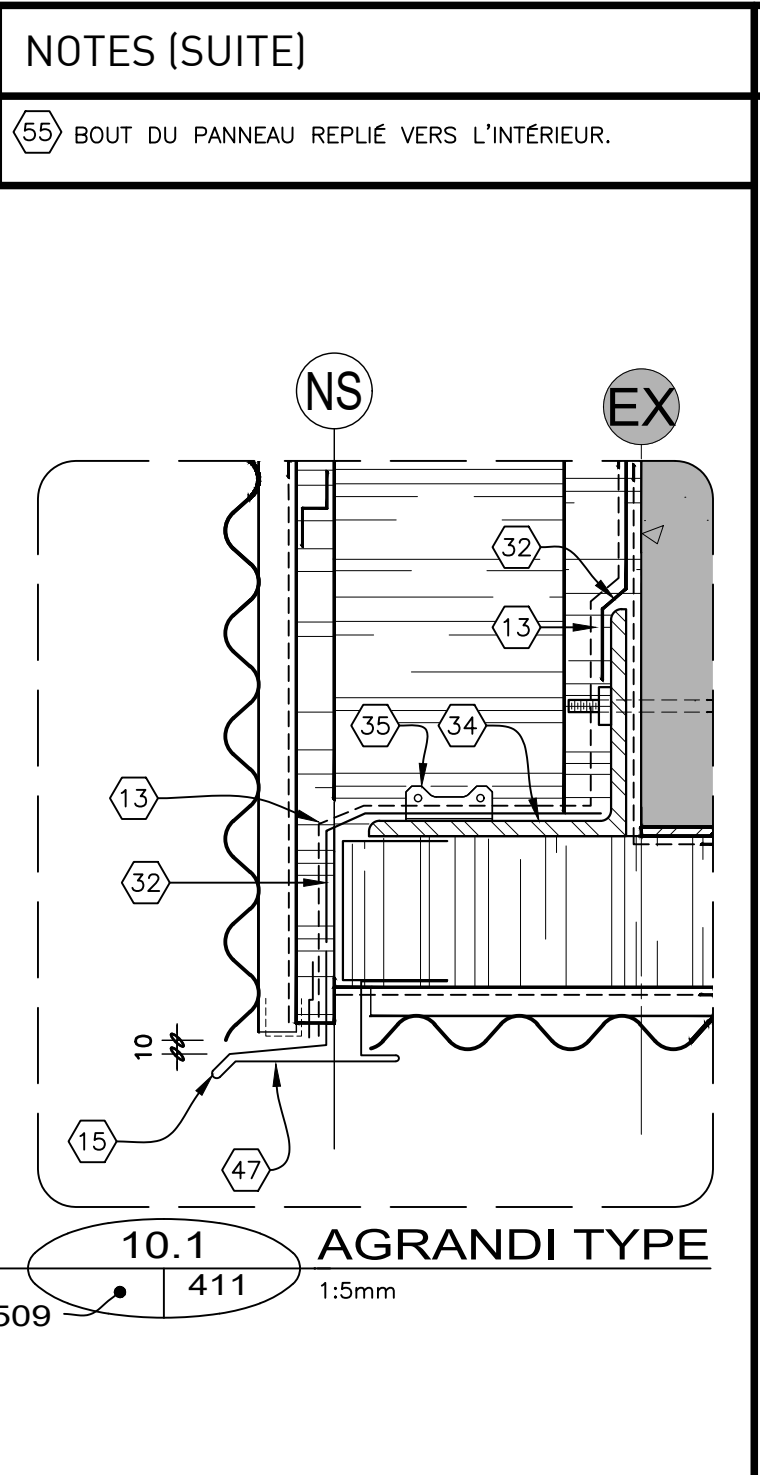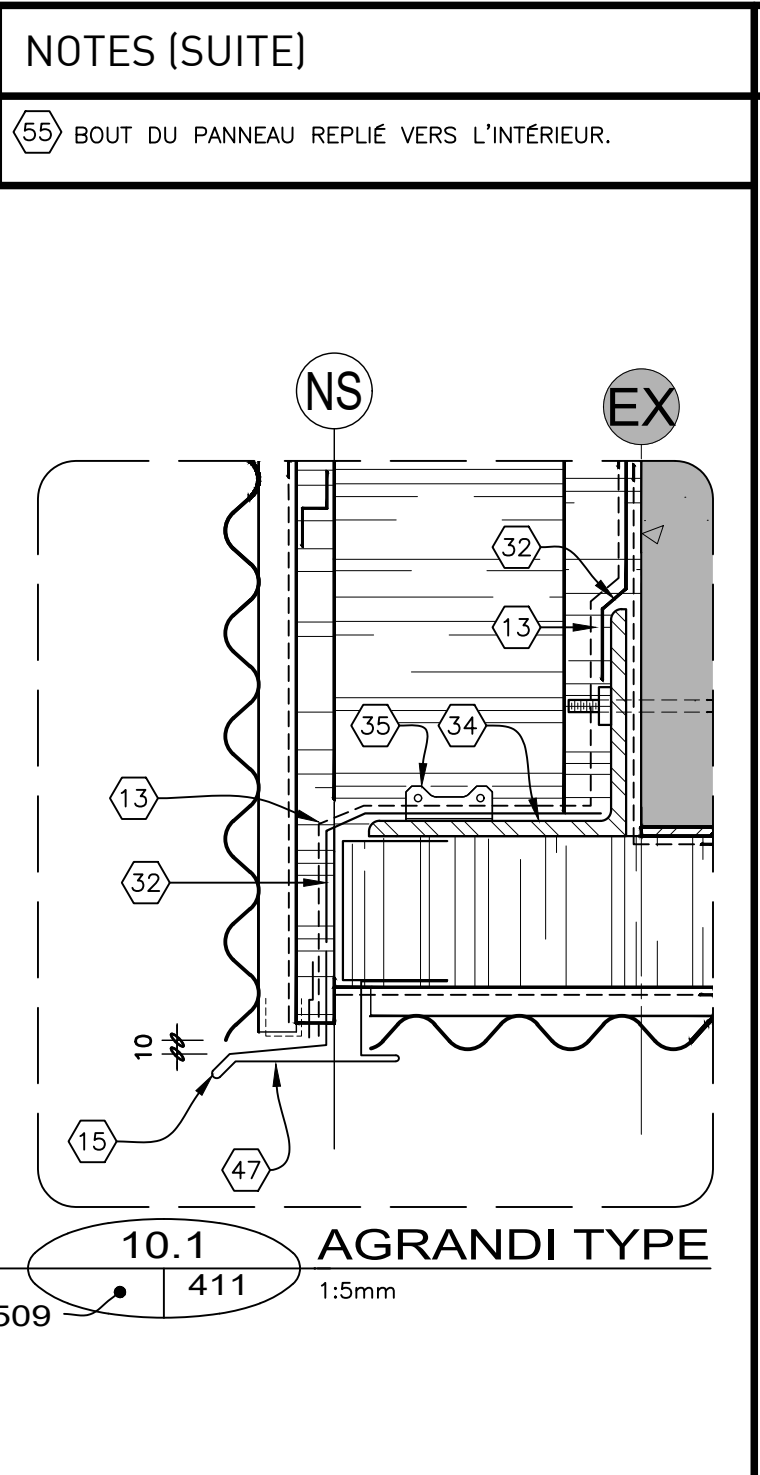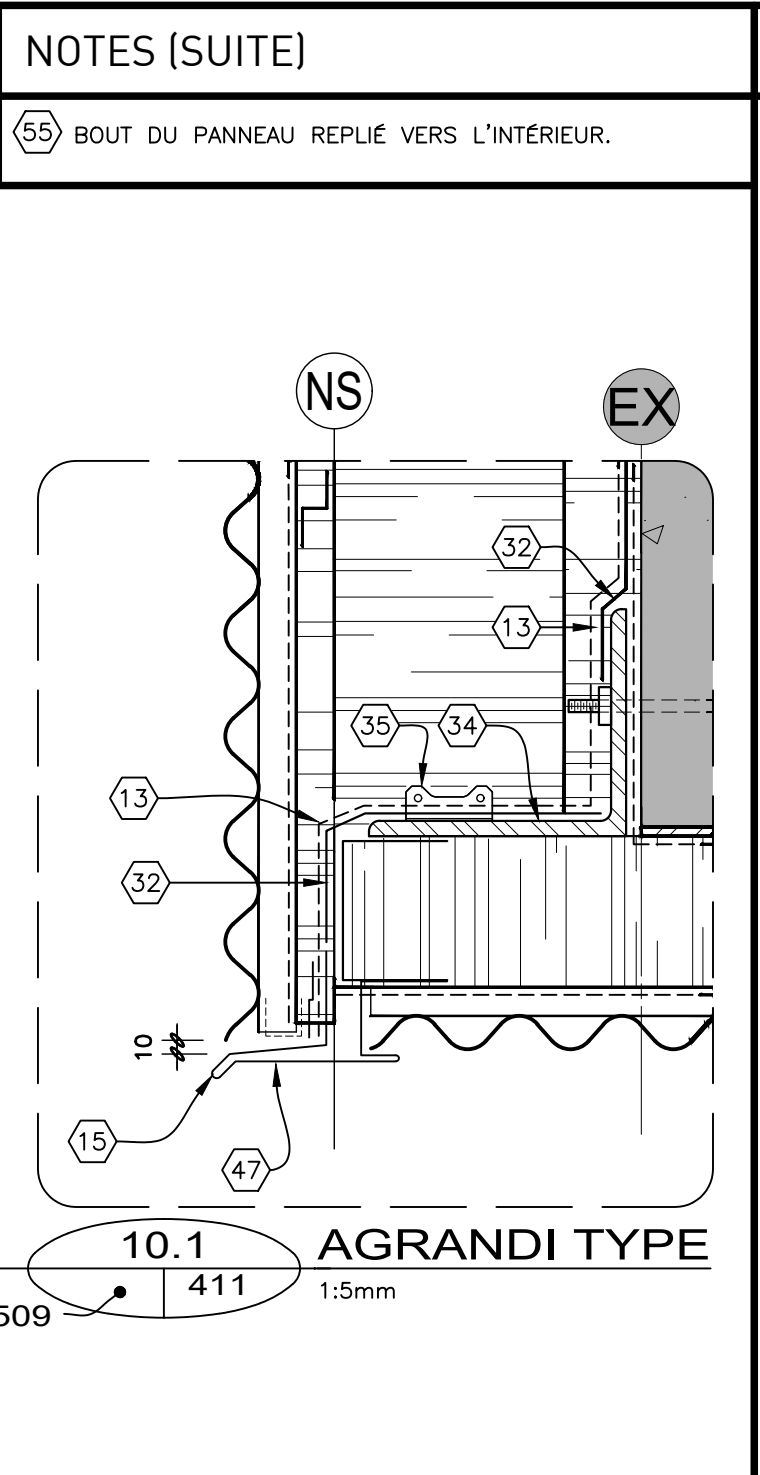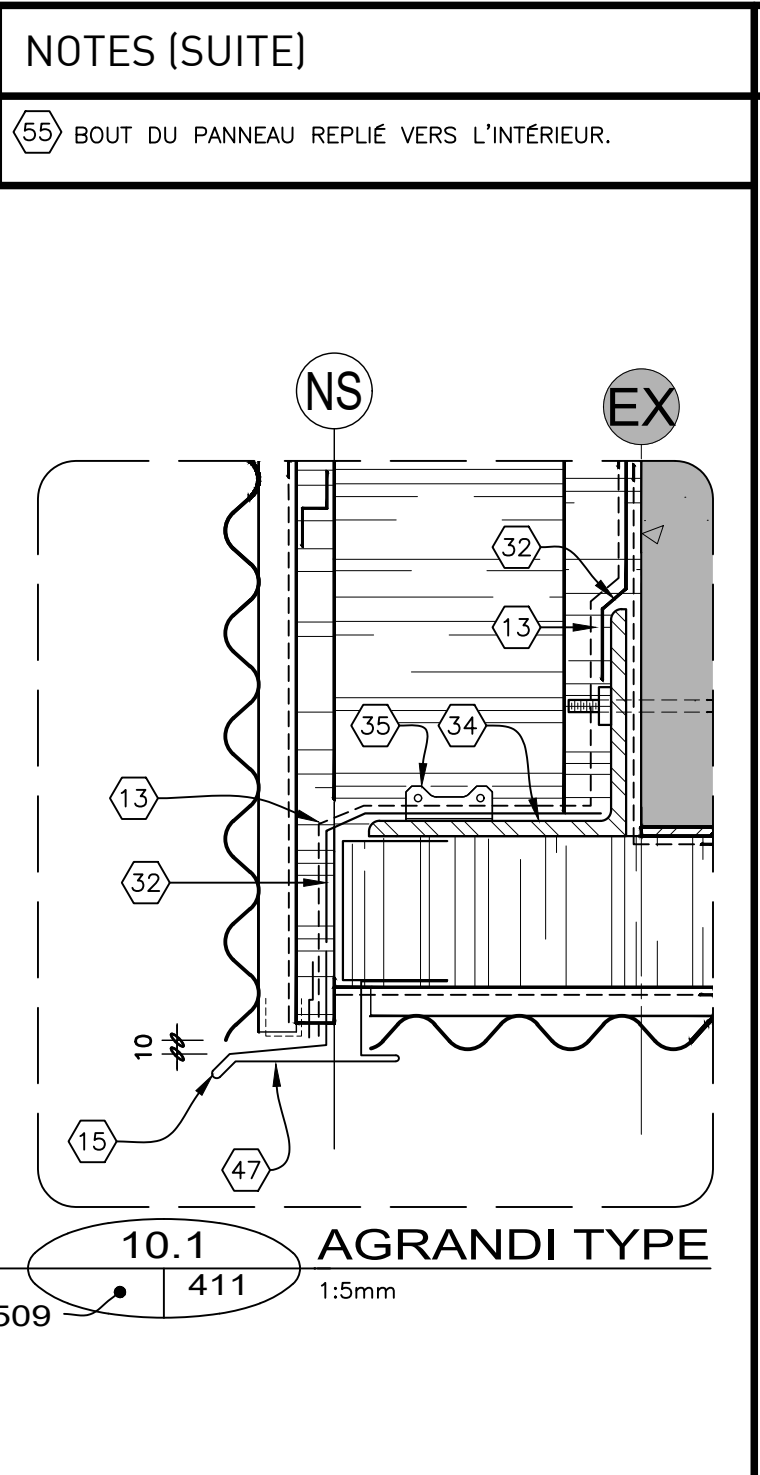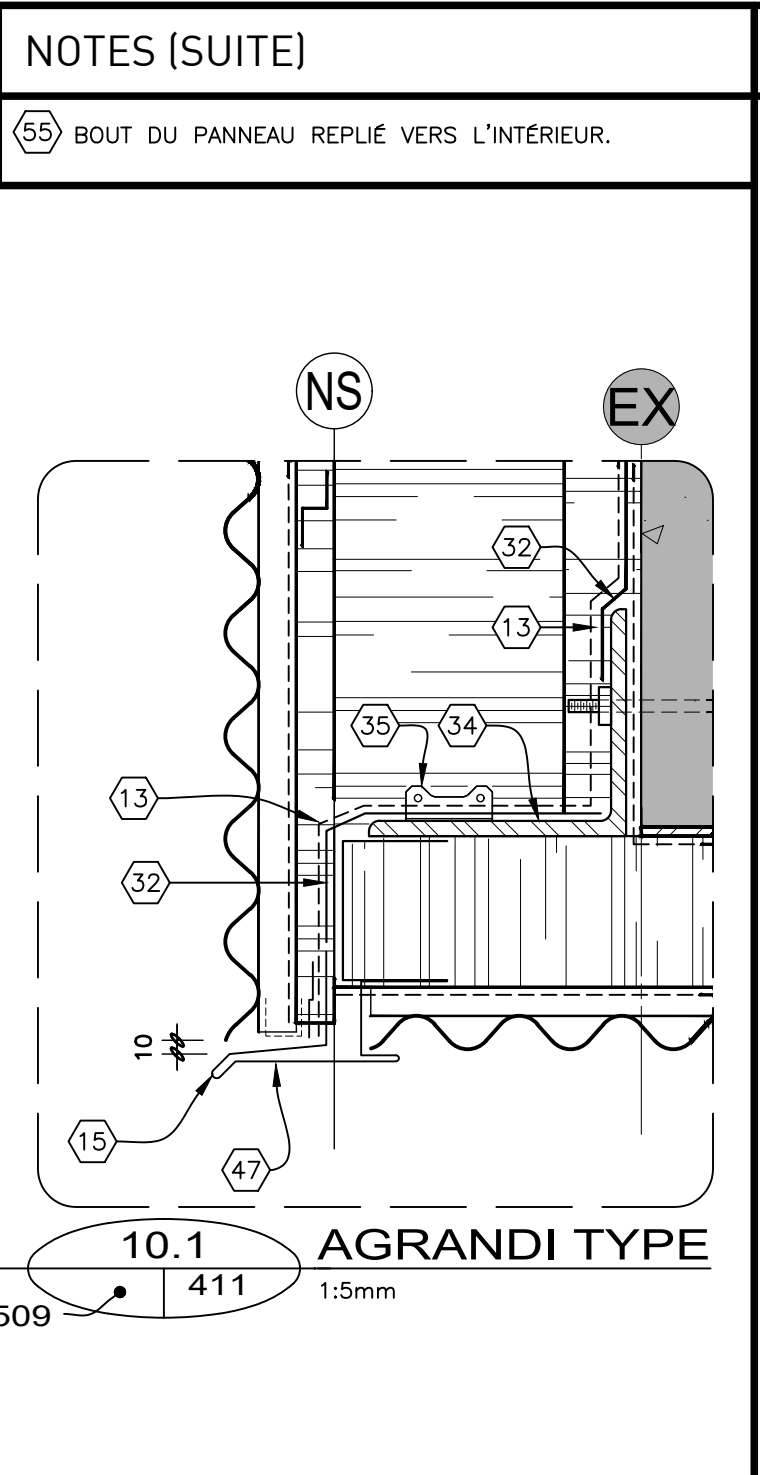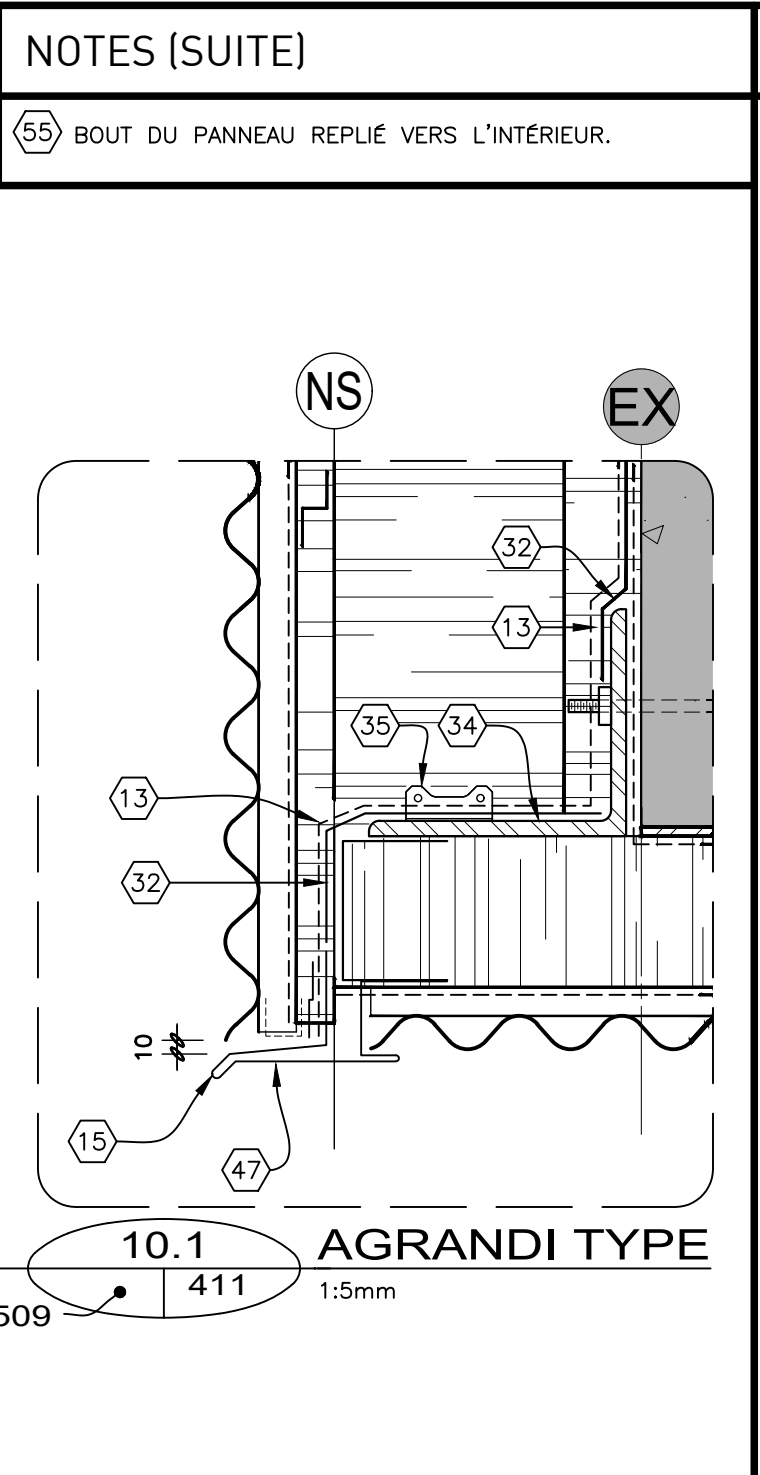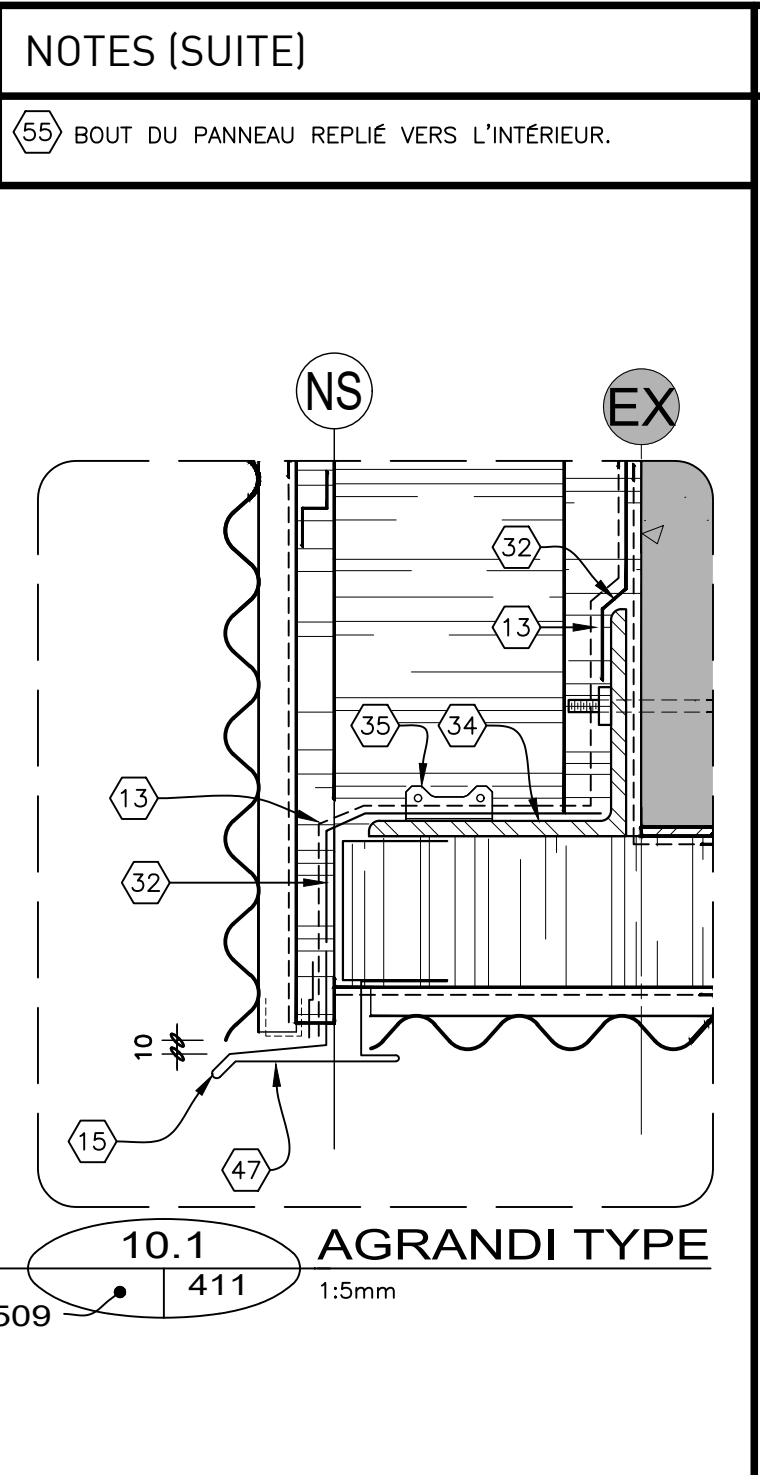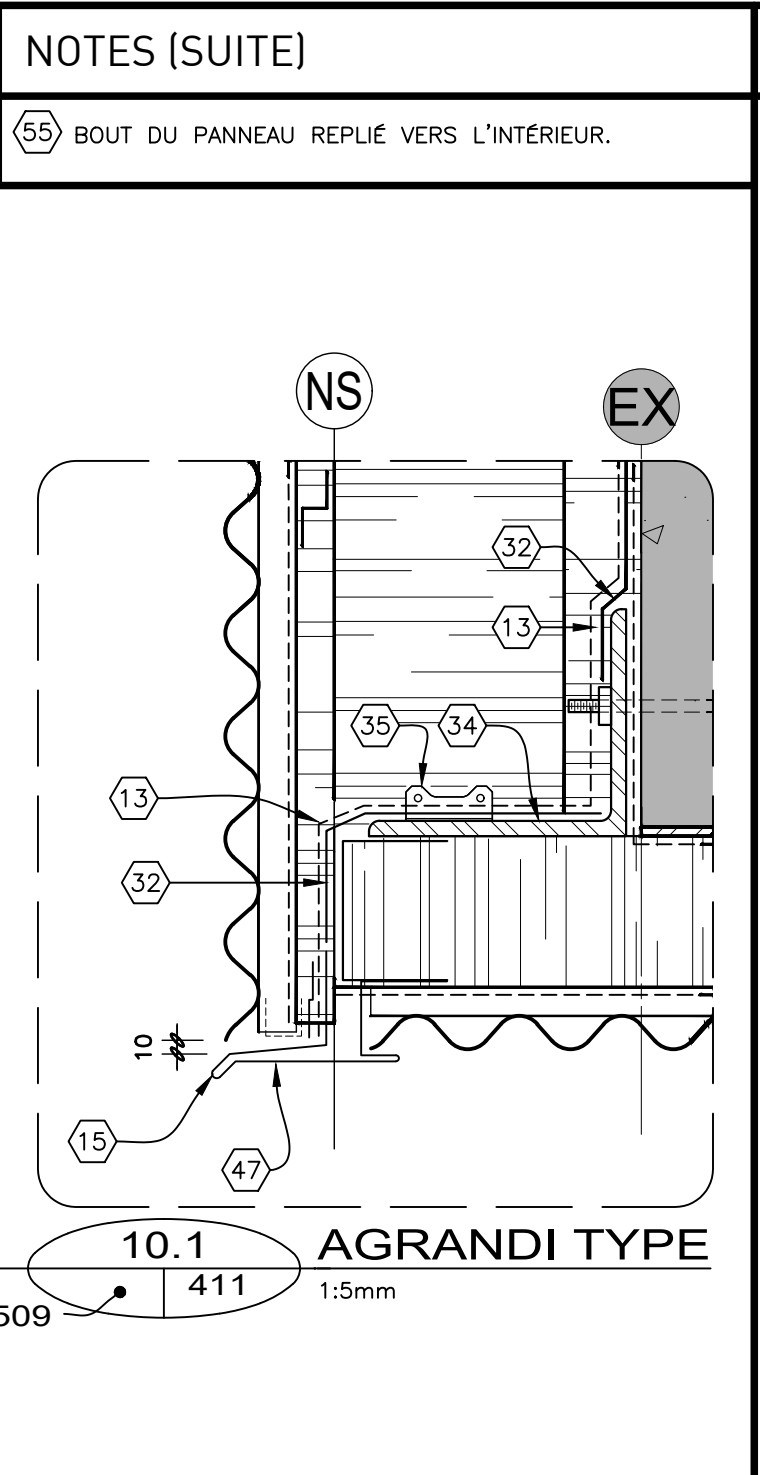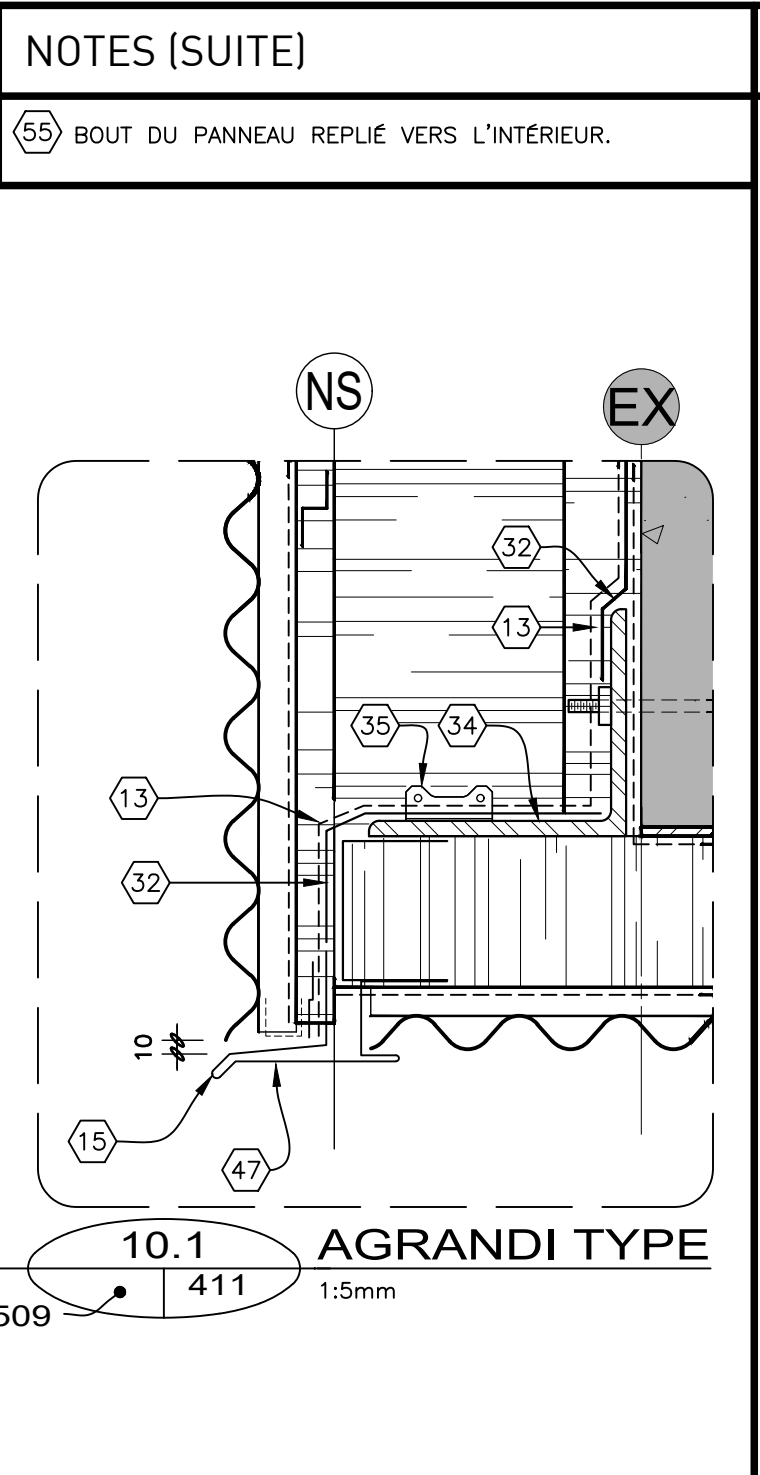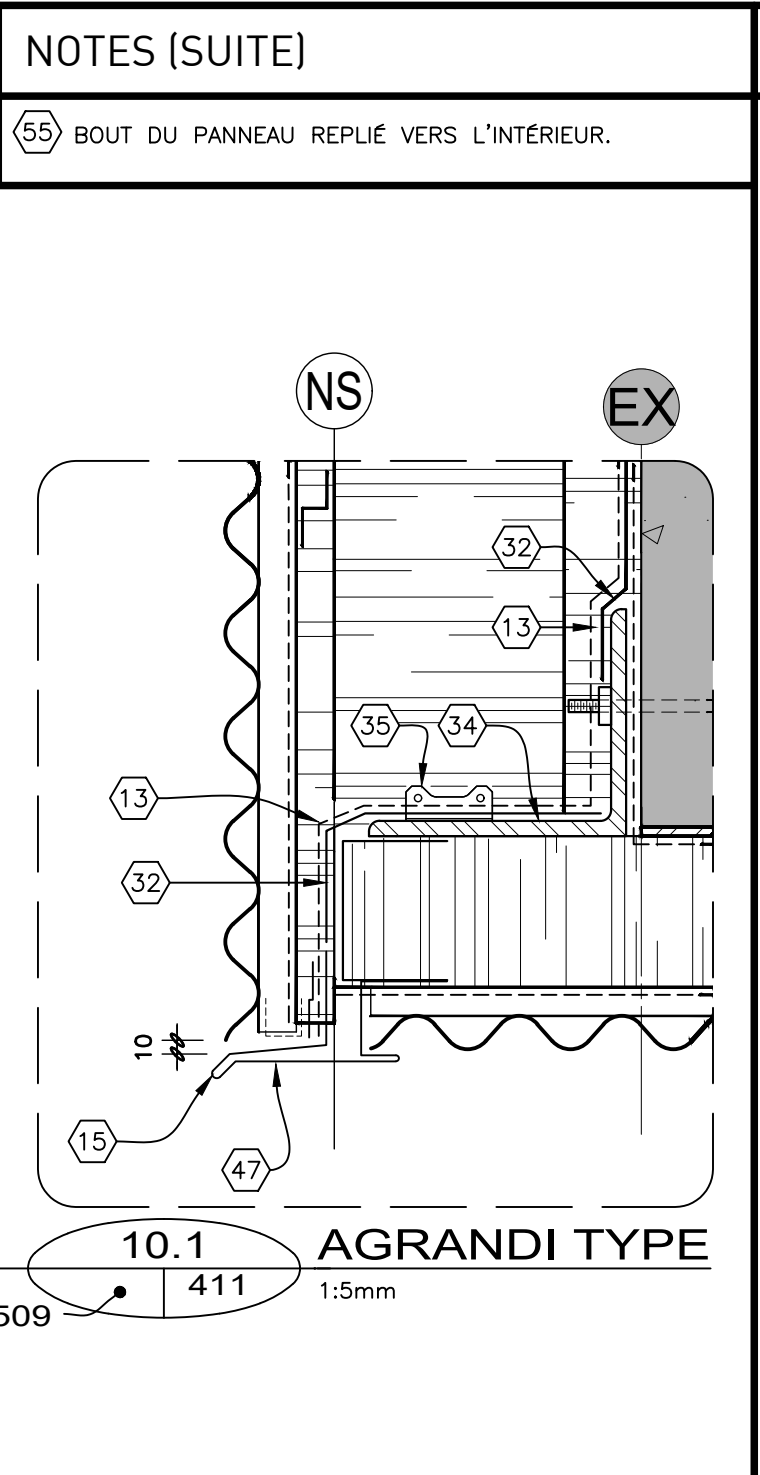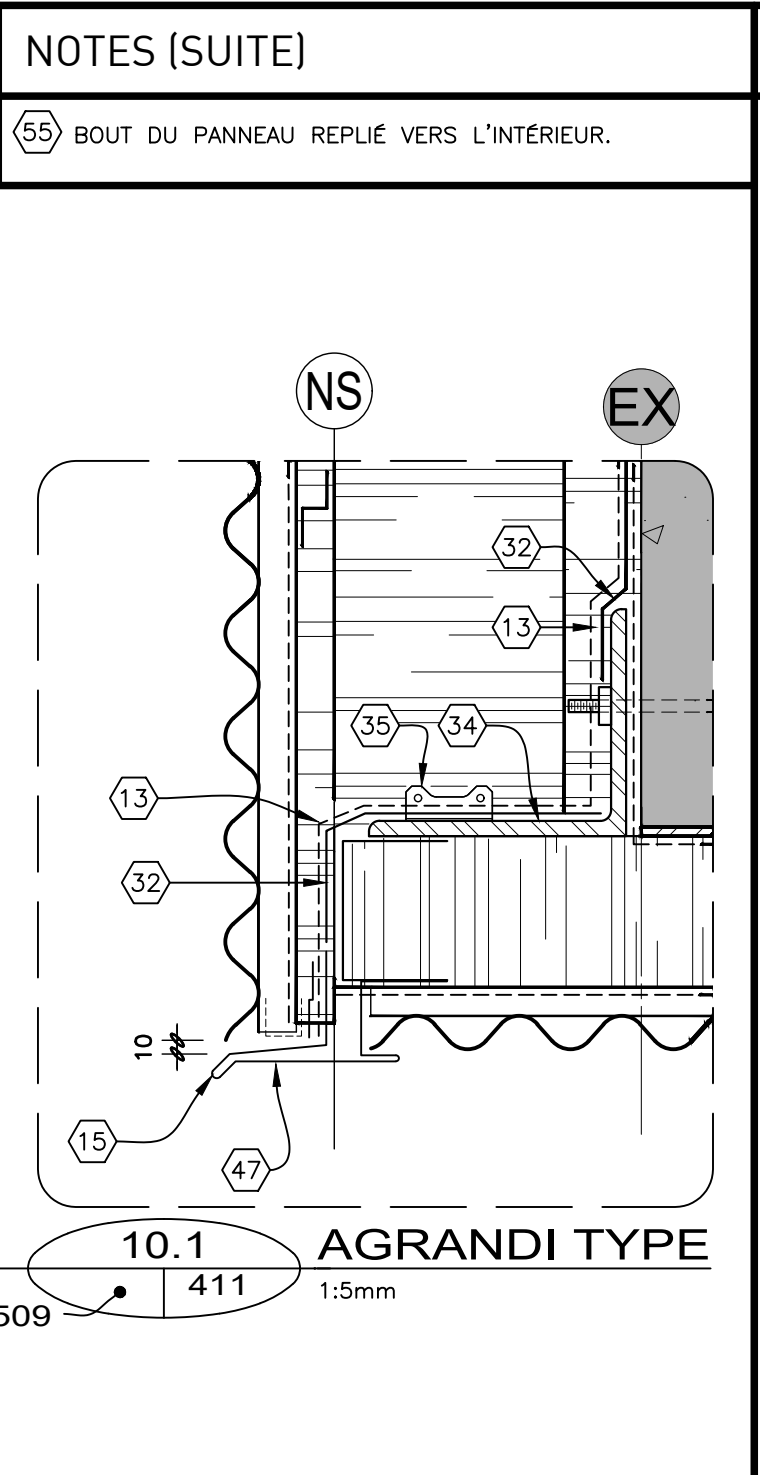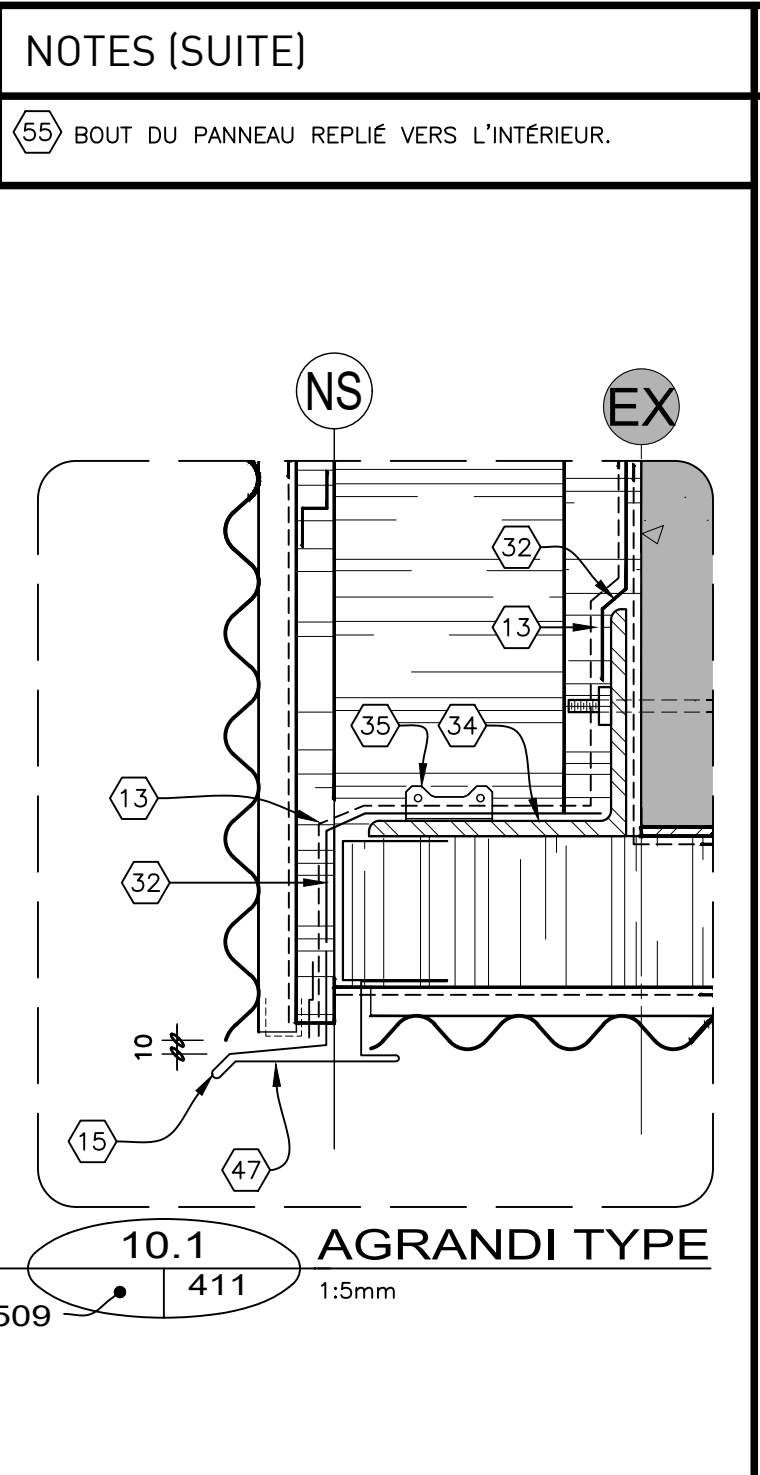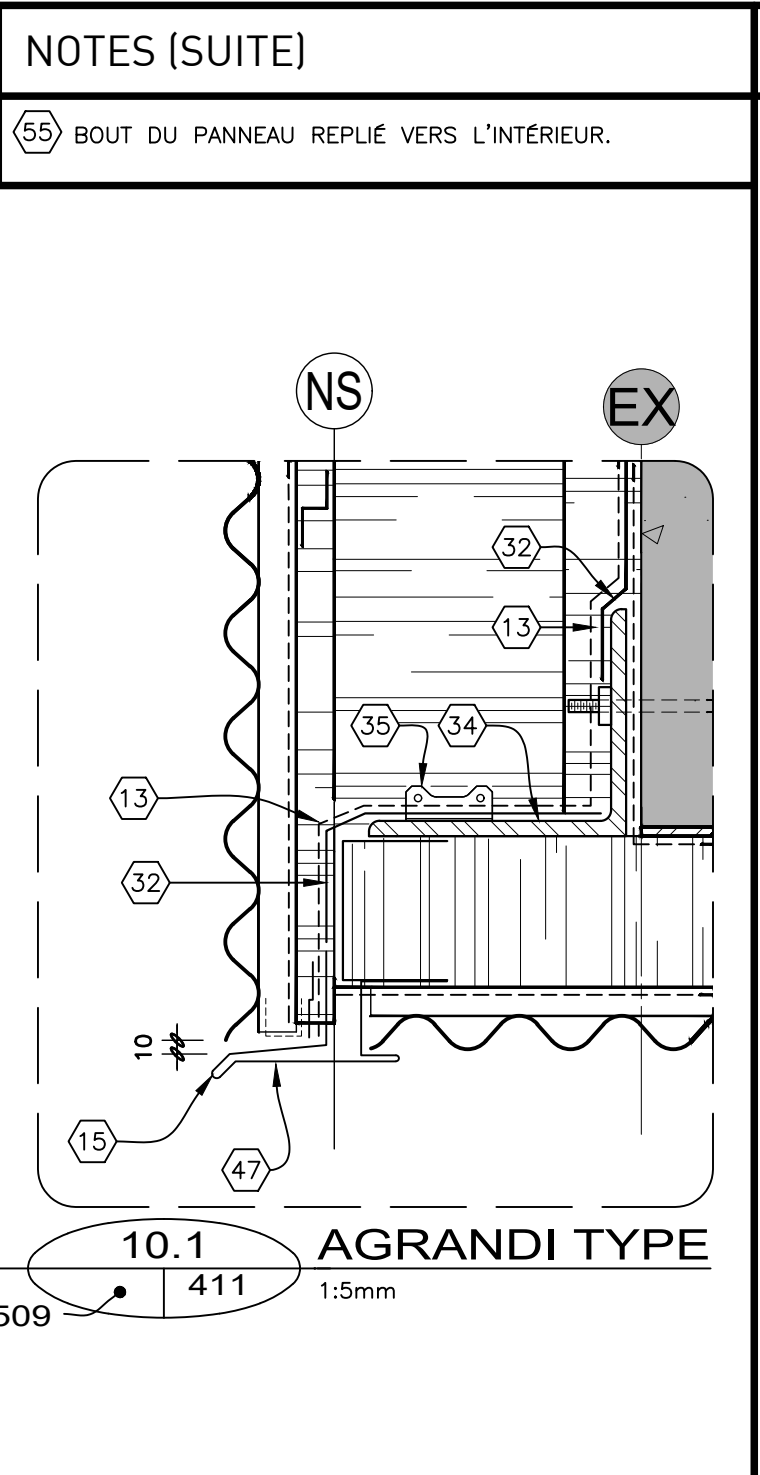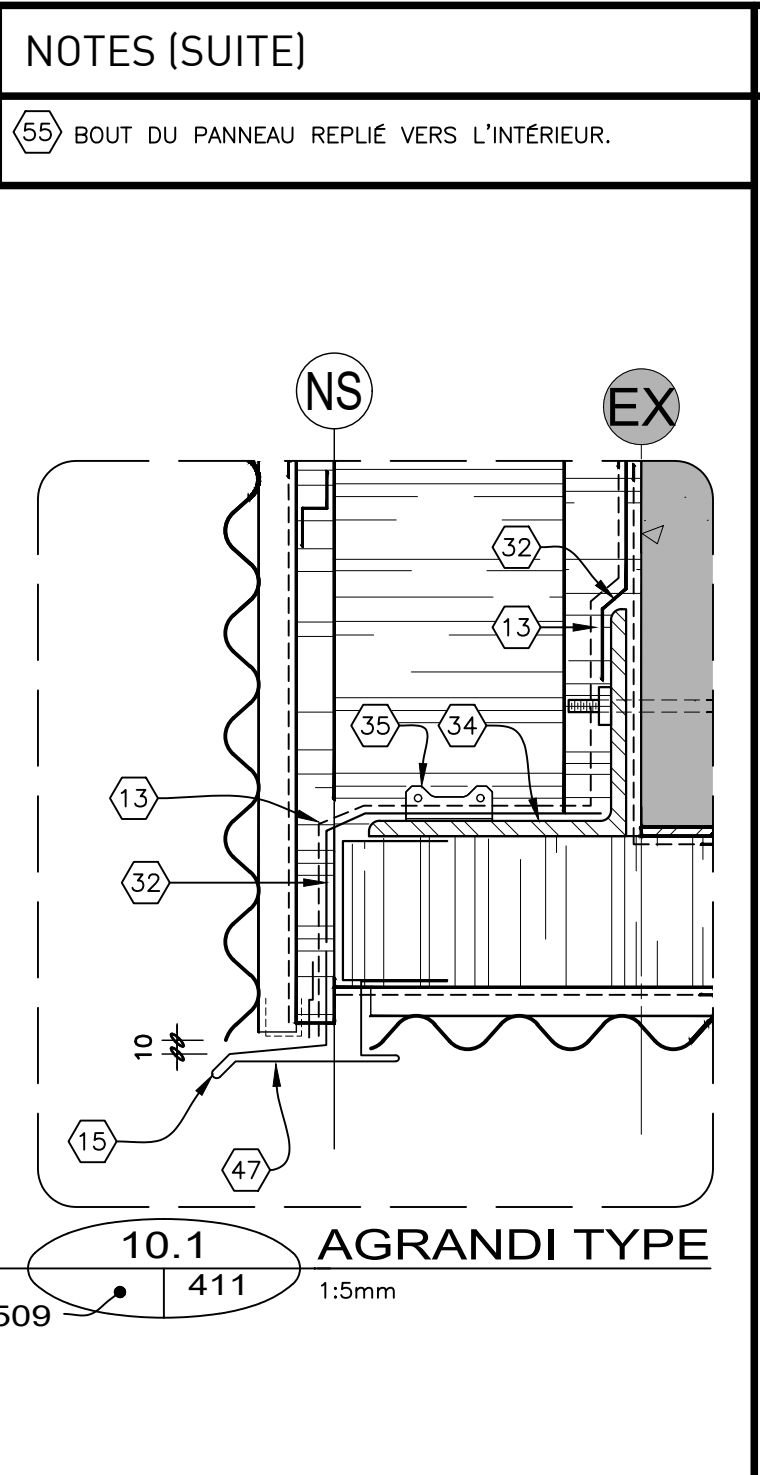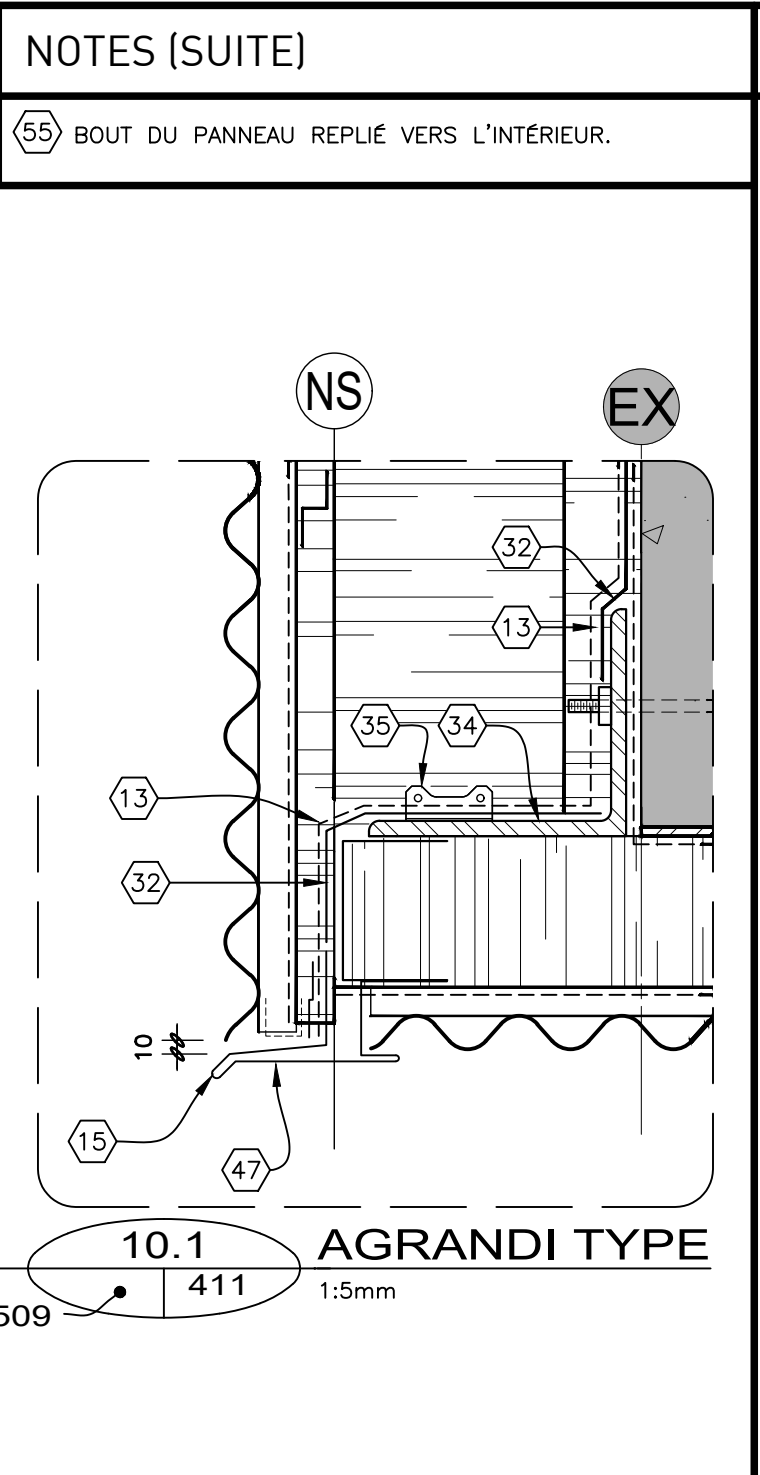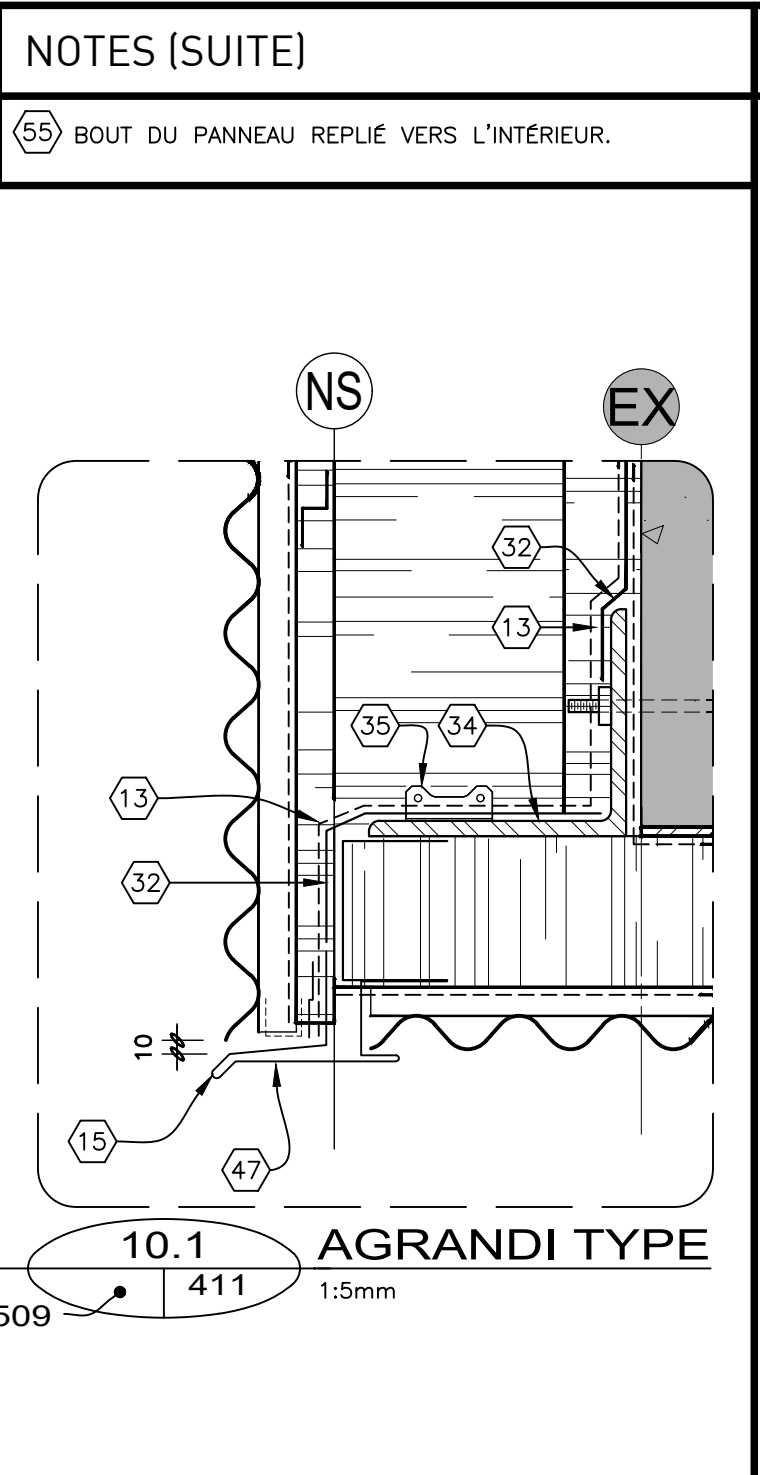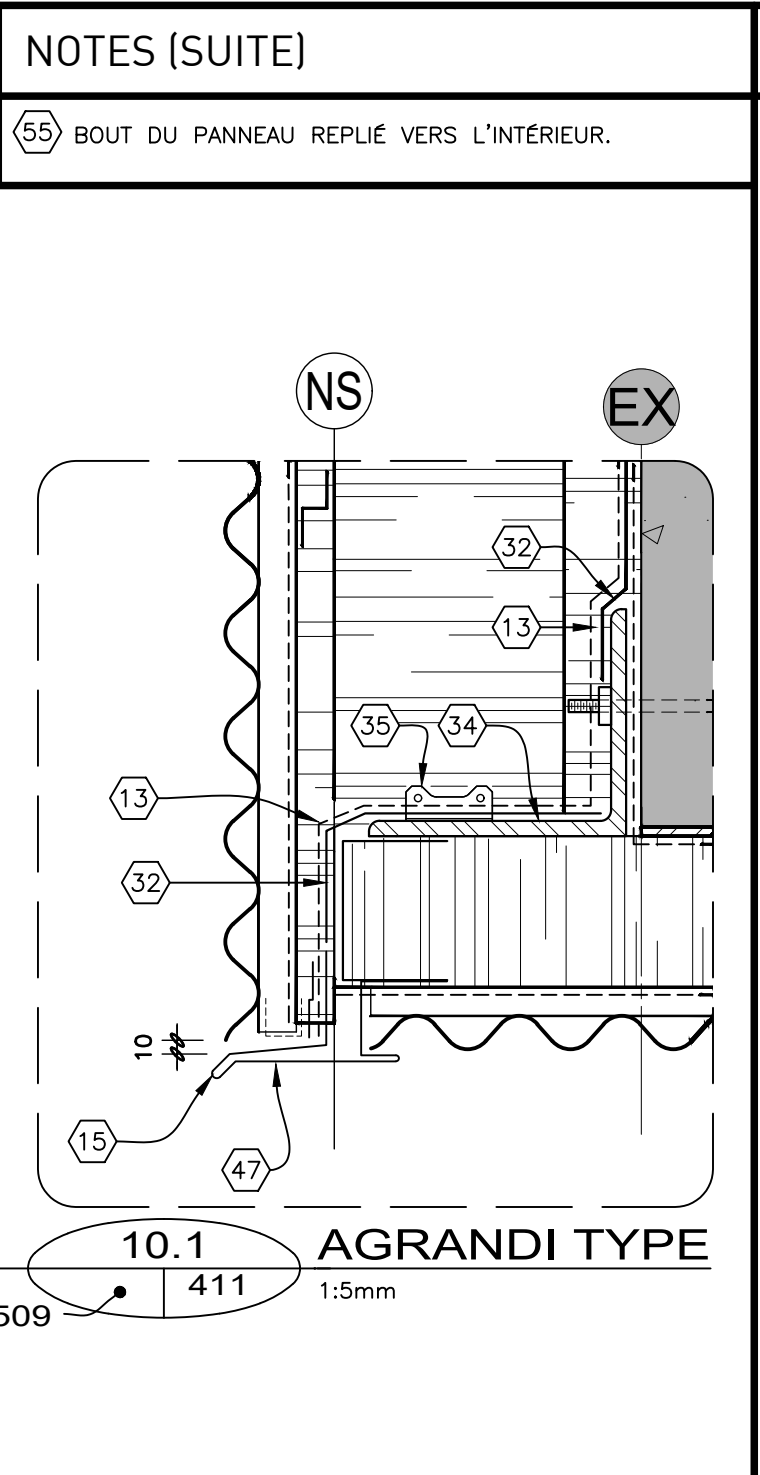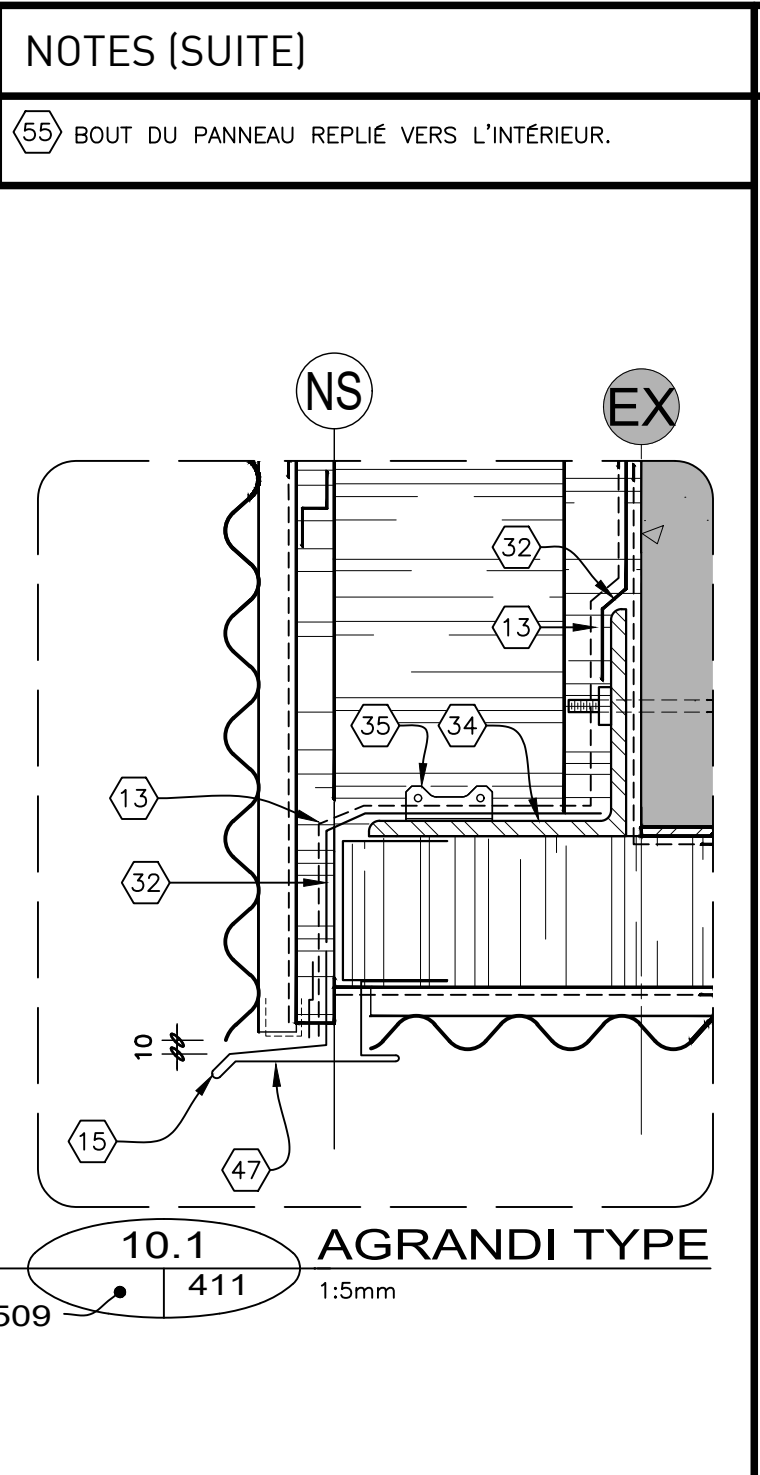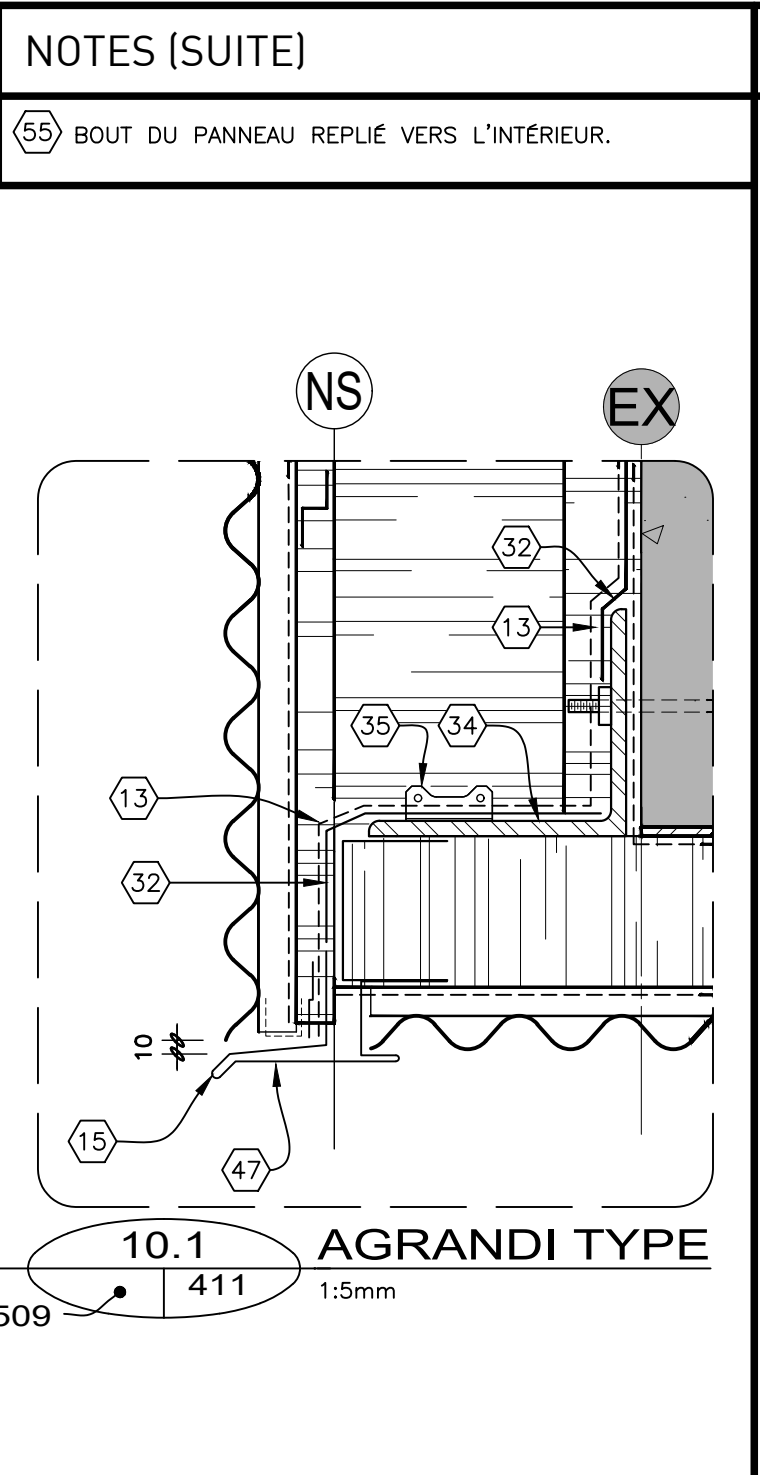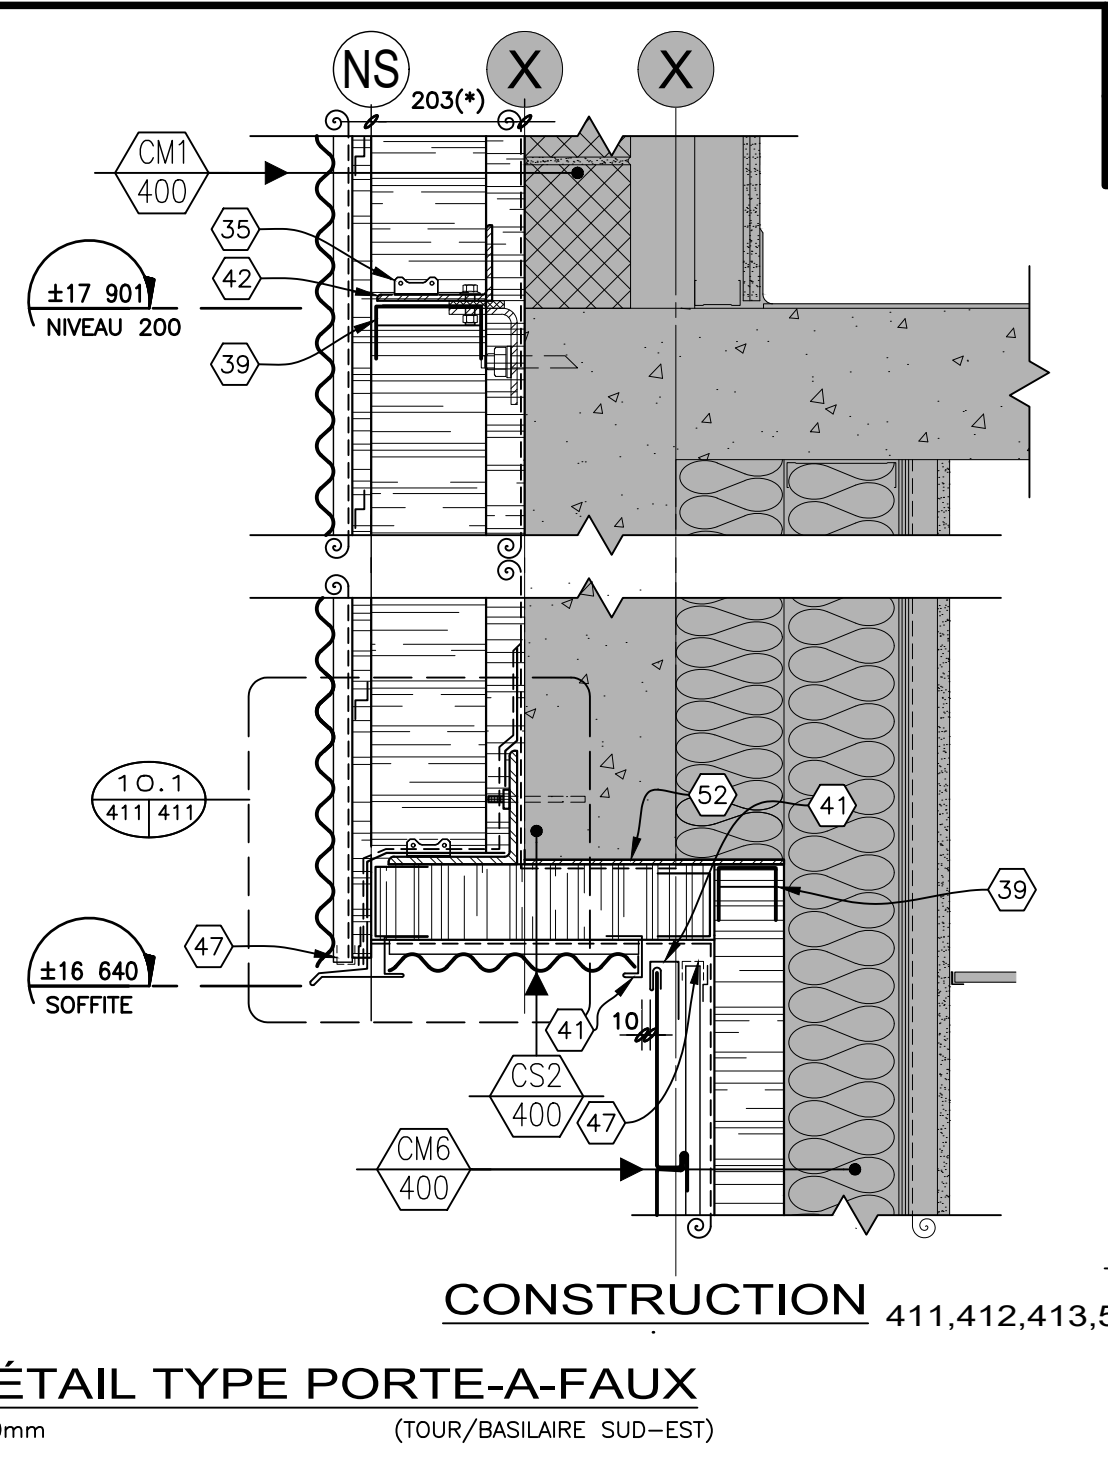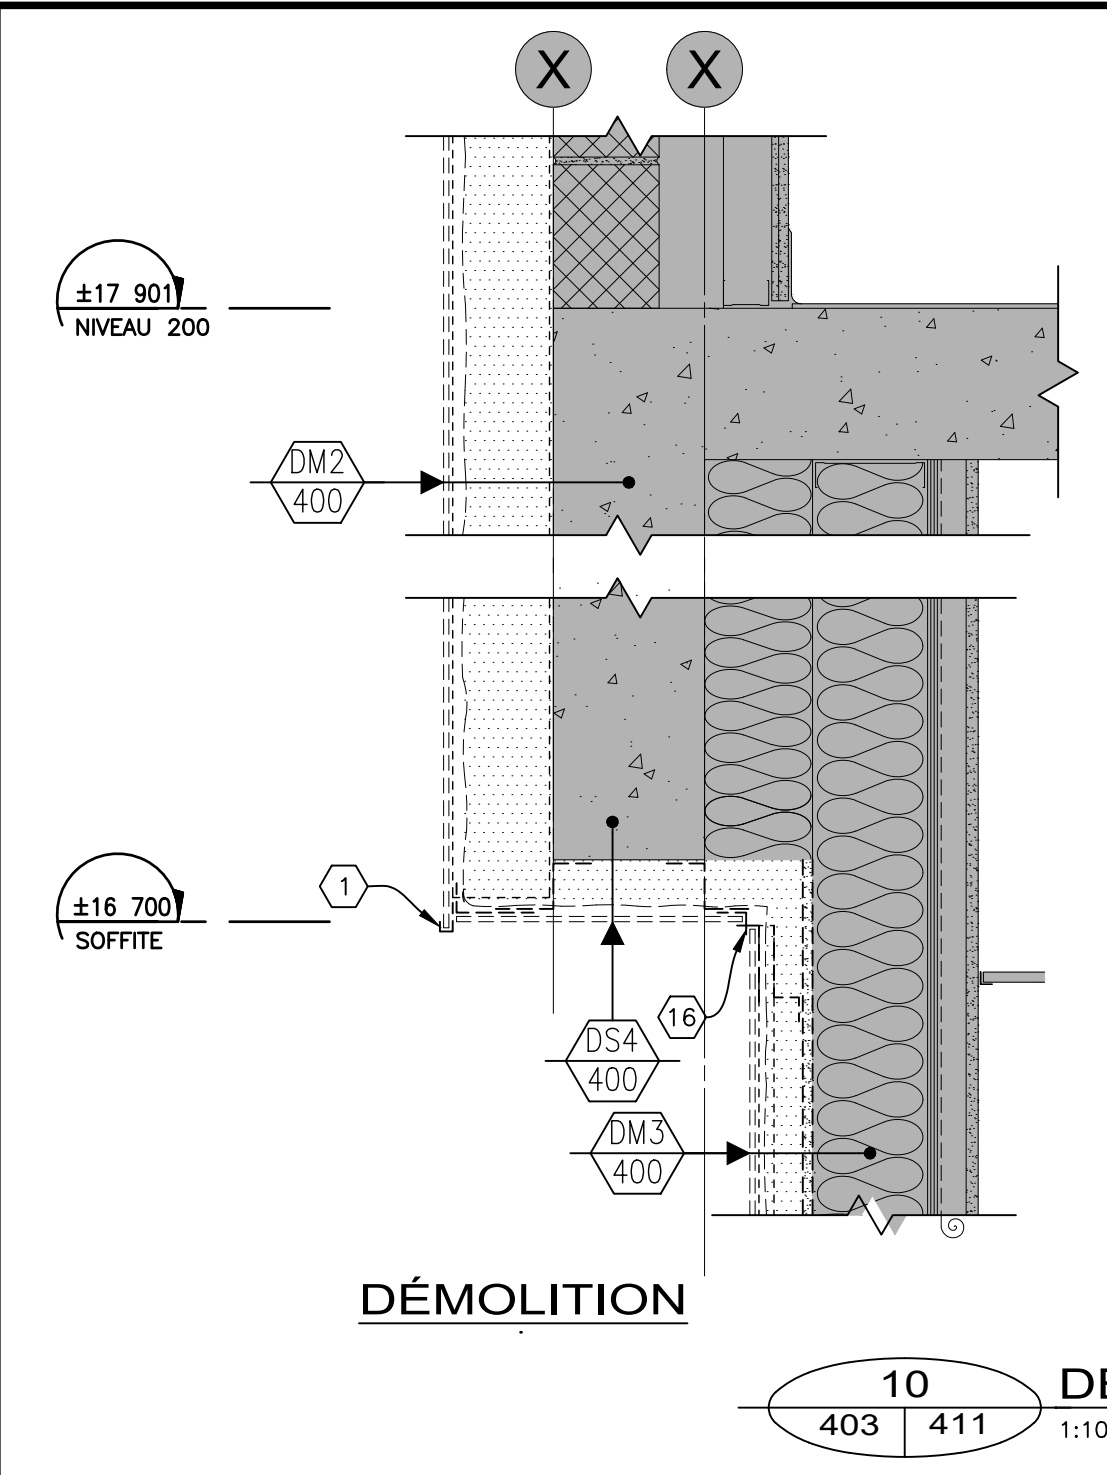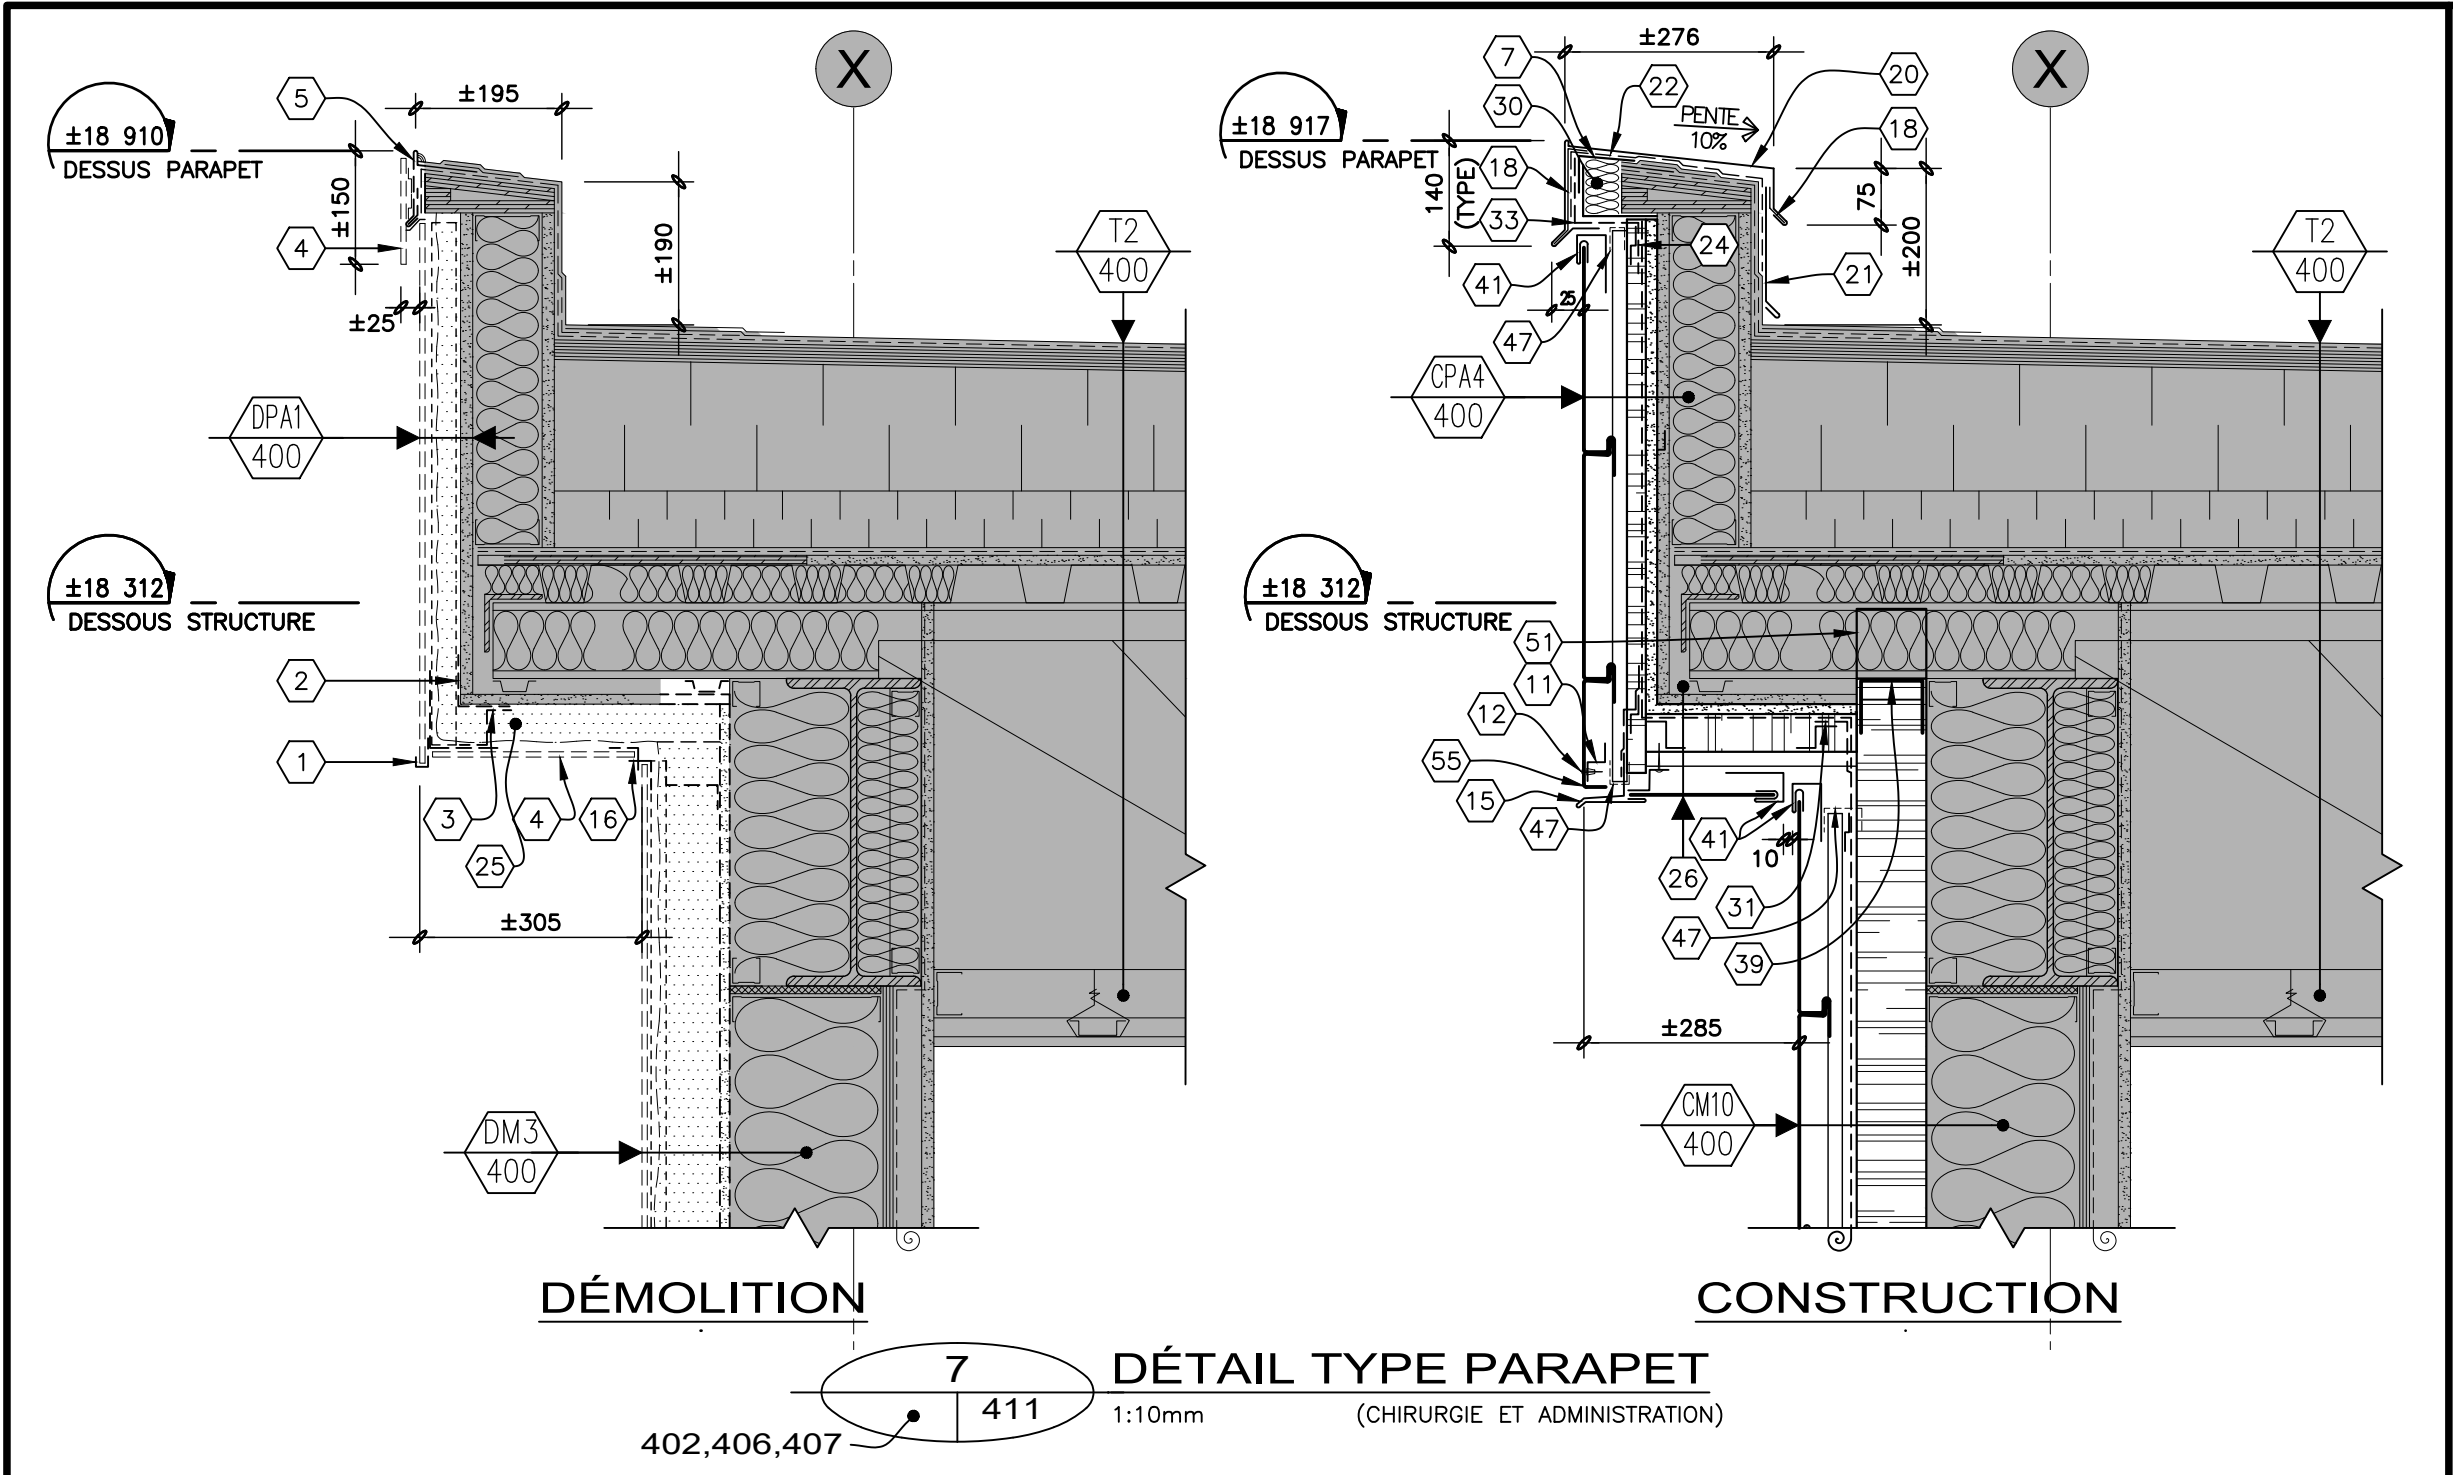


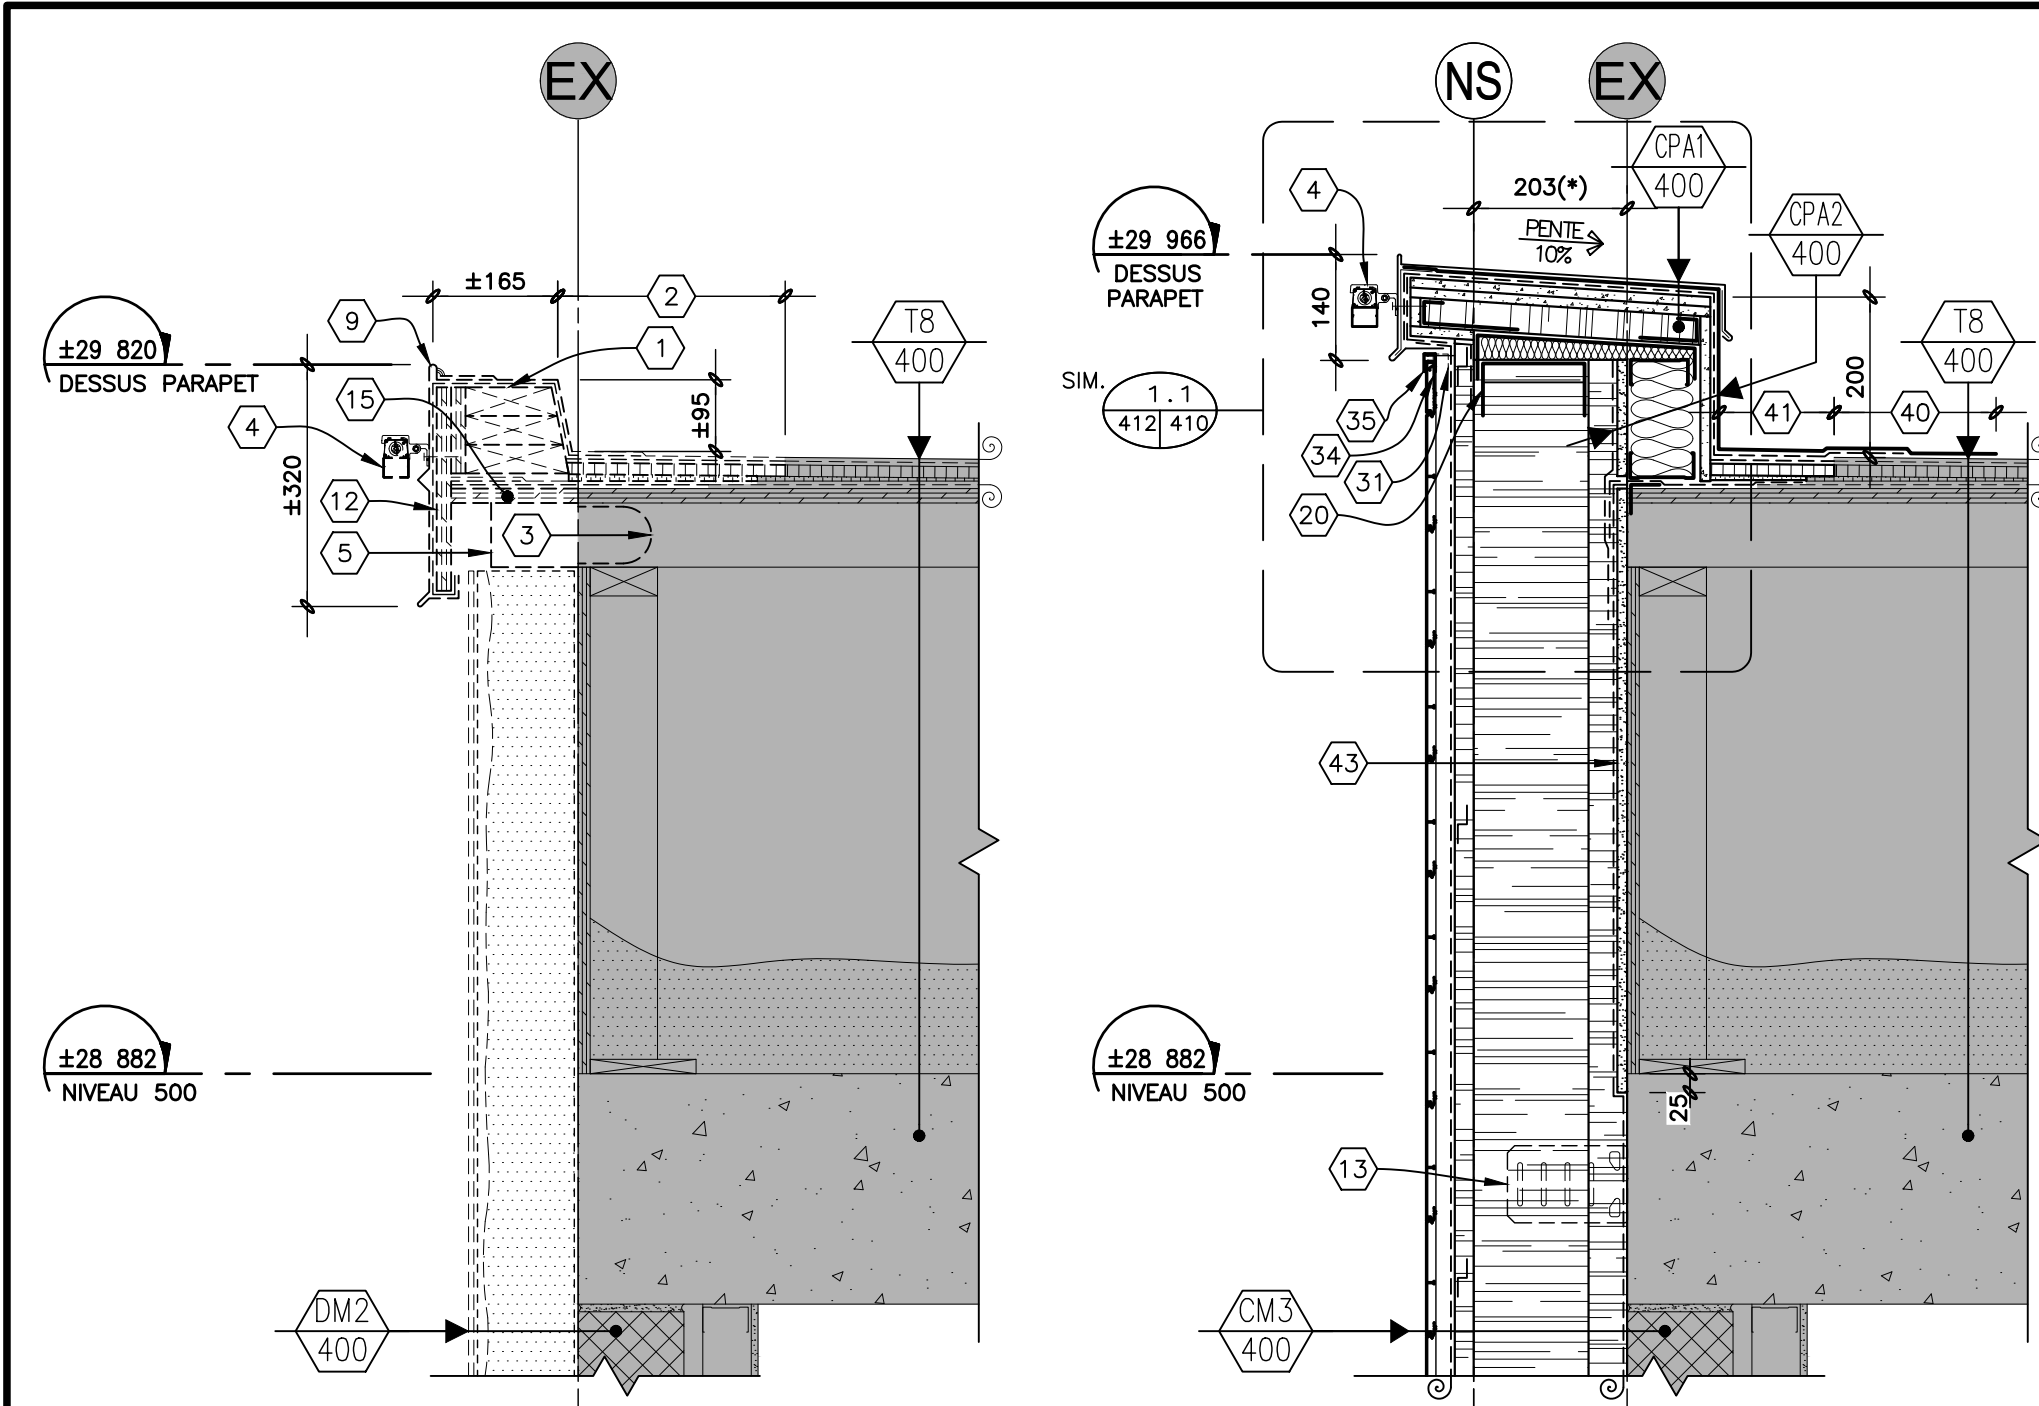


NOTE - PAREMENT ALUMINIUM

- FOURNIR ET INSTALLER DES SÉPARATEURS DIÉLECTRIQUES CONTINUS À TOUS LES APPUIS DES ÉLÉMENTS D'ACIER AVEC LE PAREMENT D'ALUMINIUM.
- FOURNIR ET INSTALLER DES SÉPARATEURS DIÉLECTRIQUES CONTINUS ENTRE LES MOULURES D'ALUMINIUM ET LES MOULURES OU SOLIN EN ACIER ÉMAILLÉ.

DÉMOLITION **CONSTRUCTION**
13 DÉTAIL TYPE PARAPET
1:10mm (TOUR ÉLEVATION OUEST)

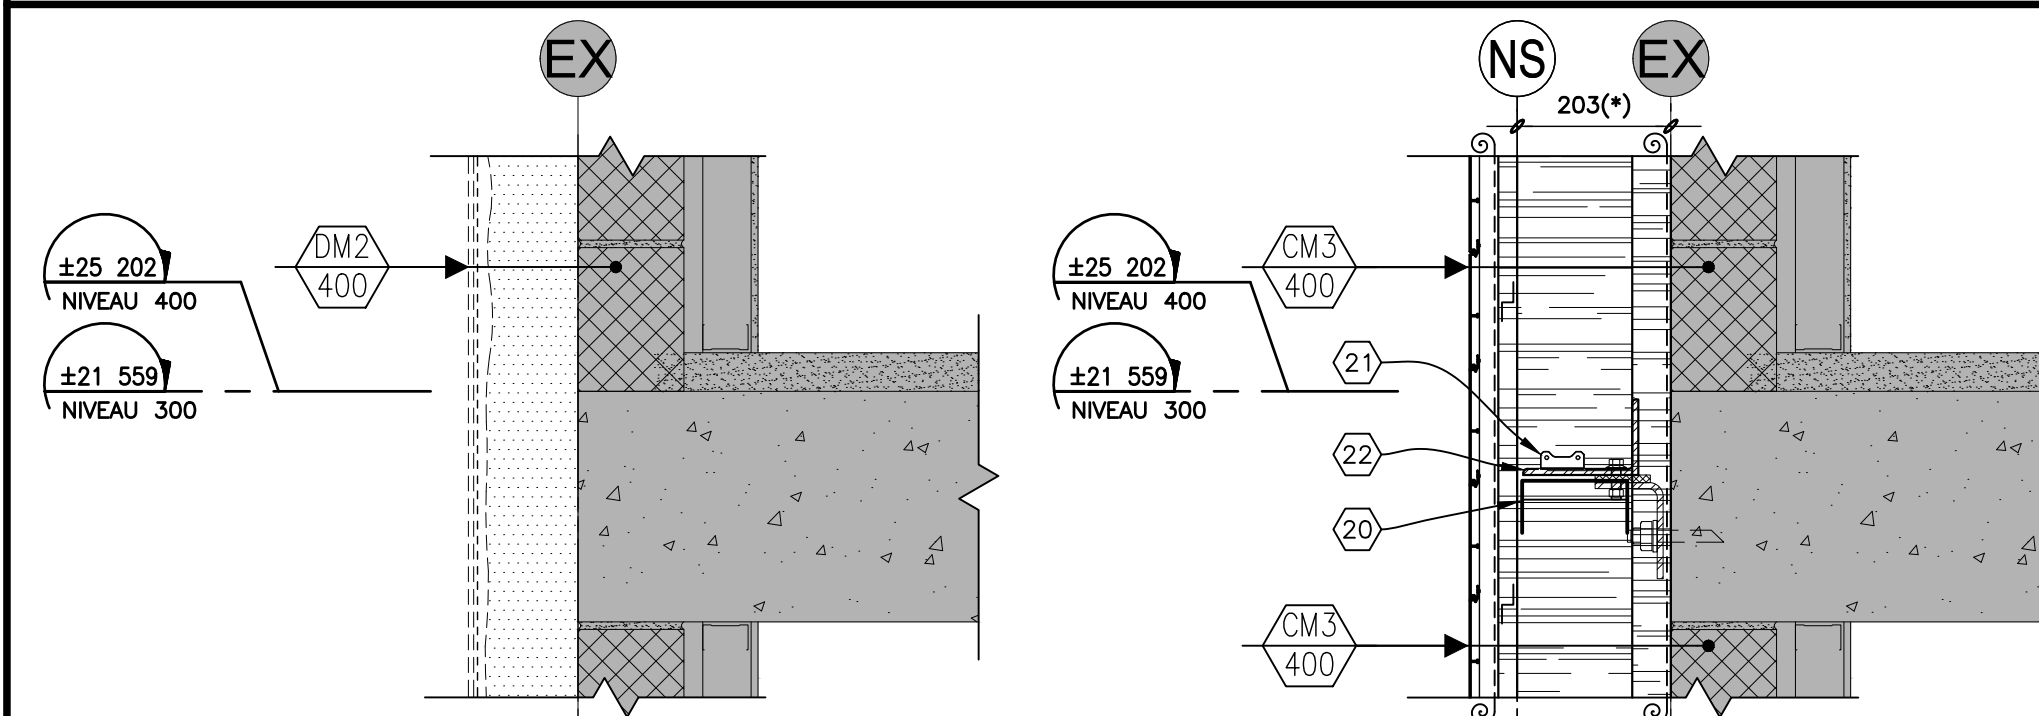

DÉMOLITION **CONSTRUCTION**
14 DÉTAIL TYPE
1:10mm (TOUR ÉLEVATION OUEST)

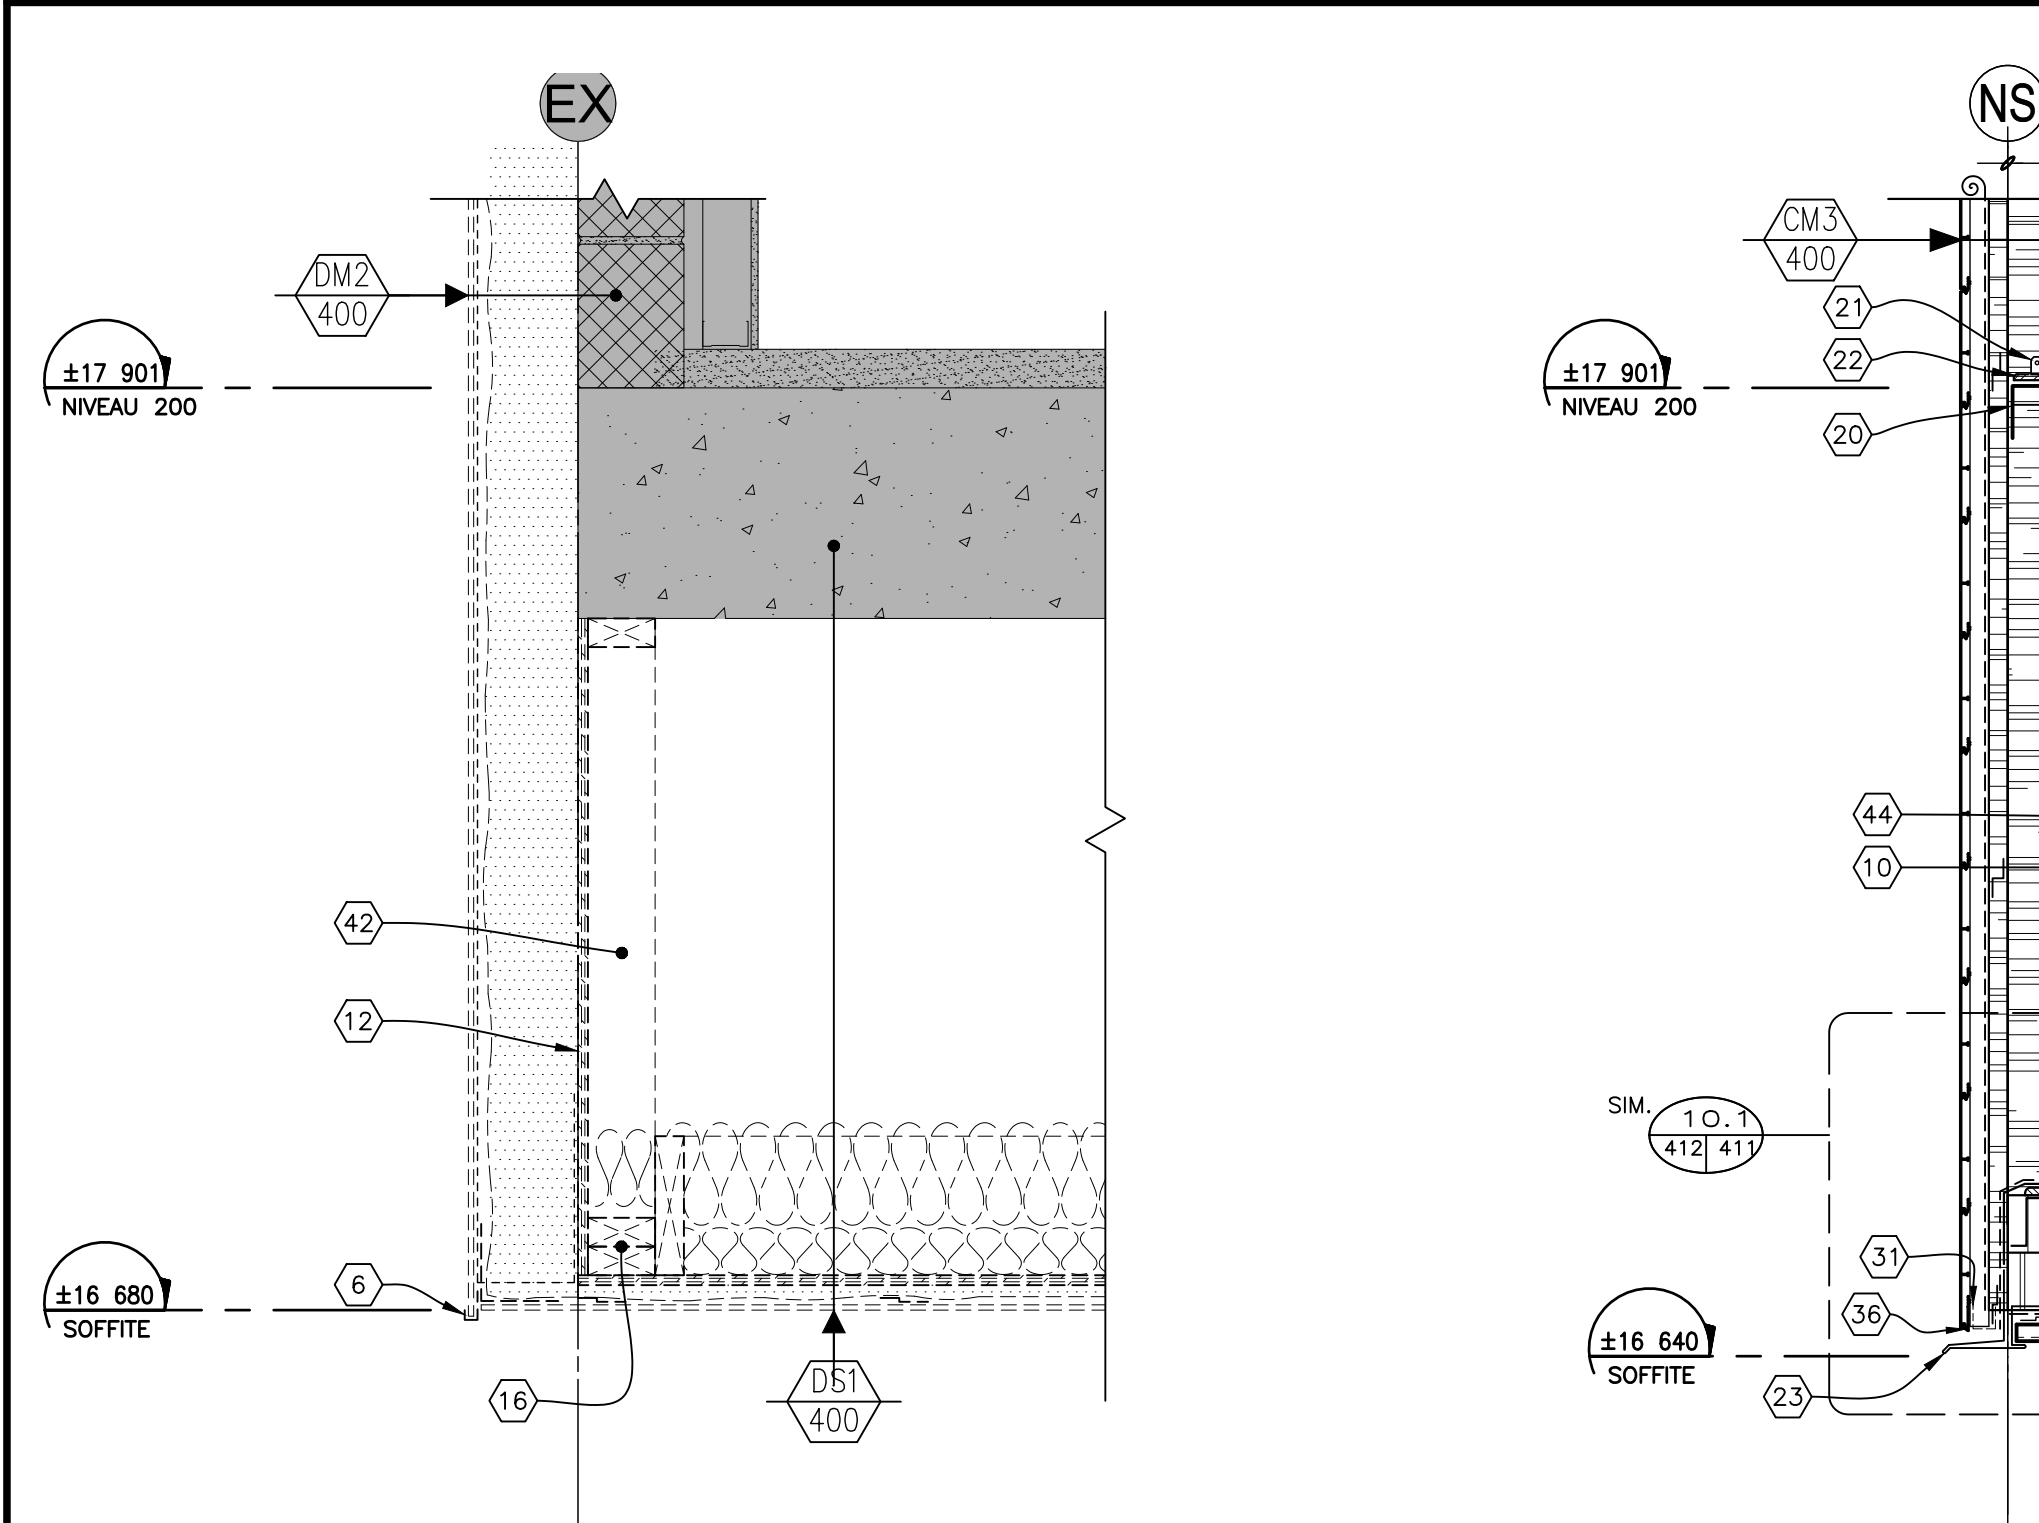


DÉMOLITION **CONSTRUCTION**
15 DÉTAIL TYPE PORTE-À-FAUX
1:10mm (TOUR ÉLEVATION OUEST)




DÉMOLITION **CONSTRUCTION**
16 DÉTAIL TYPE PORTE-FAUX
1:10mm (TOUR/BASILAIRES NORD-EST, NORD-OUEST ET SUD-OUEST)



DÉMOLITION **CONSTRUCTION**
17 DÉTAIL TYPE
1:10mm (GARAGE AMBULANCE)

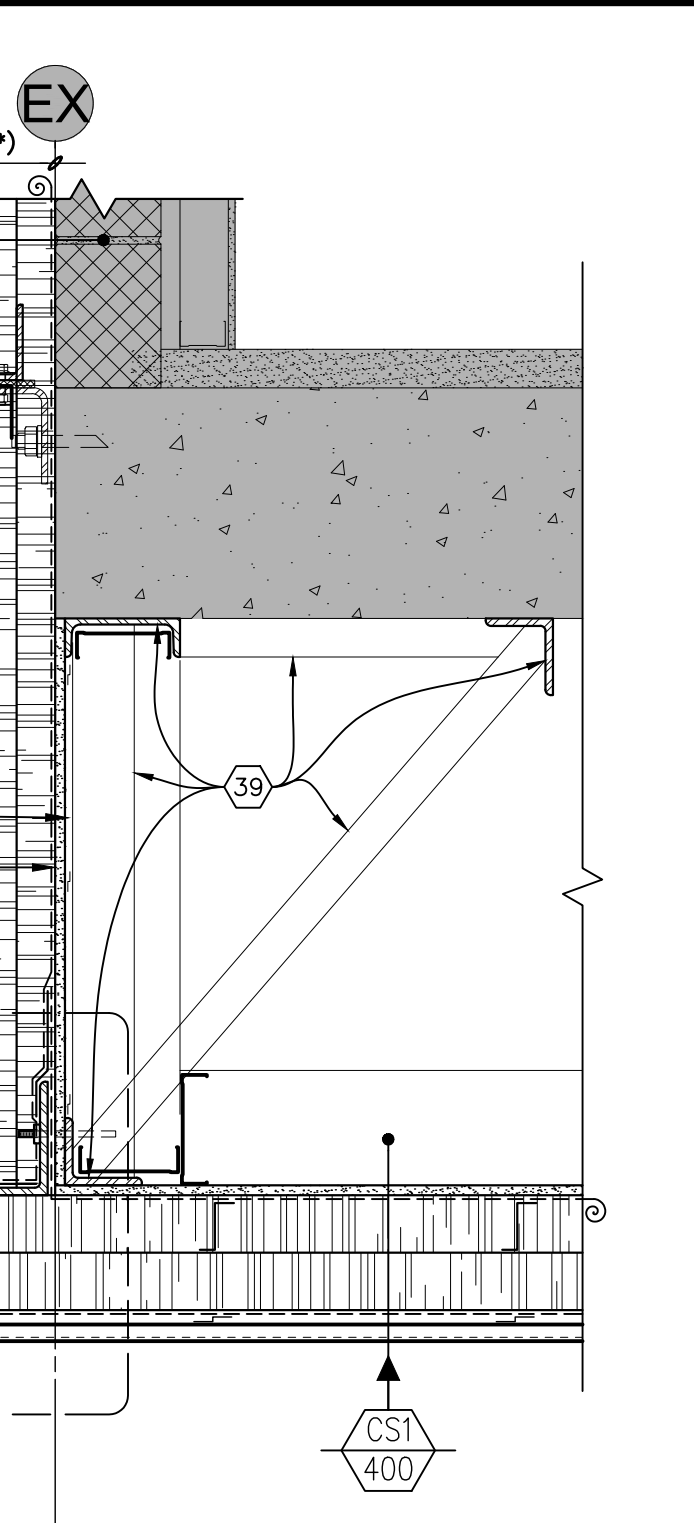

DÉMOLITION **CONSTRUCTION**
18 DÉTAIL TYPE PARAPET
1:10mm (GARAGE AMBULANCE)

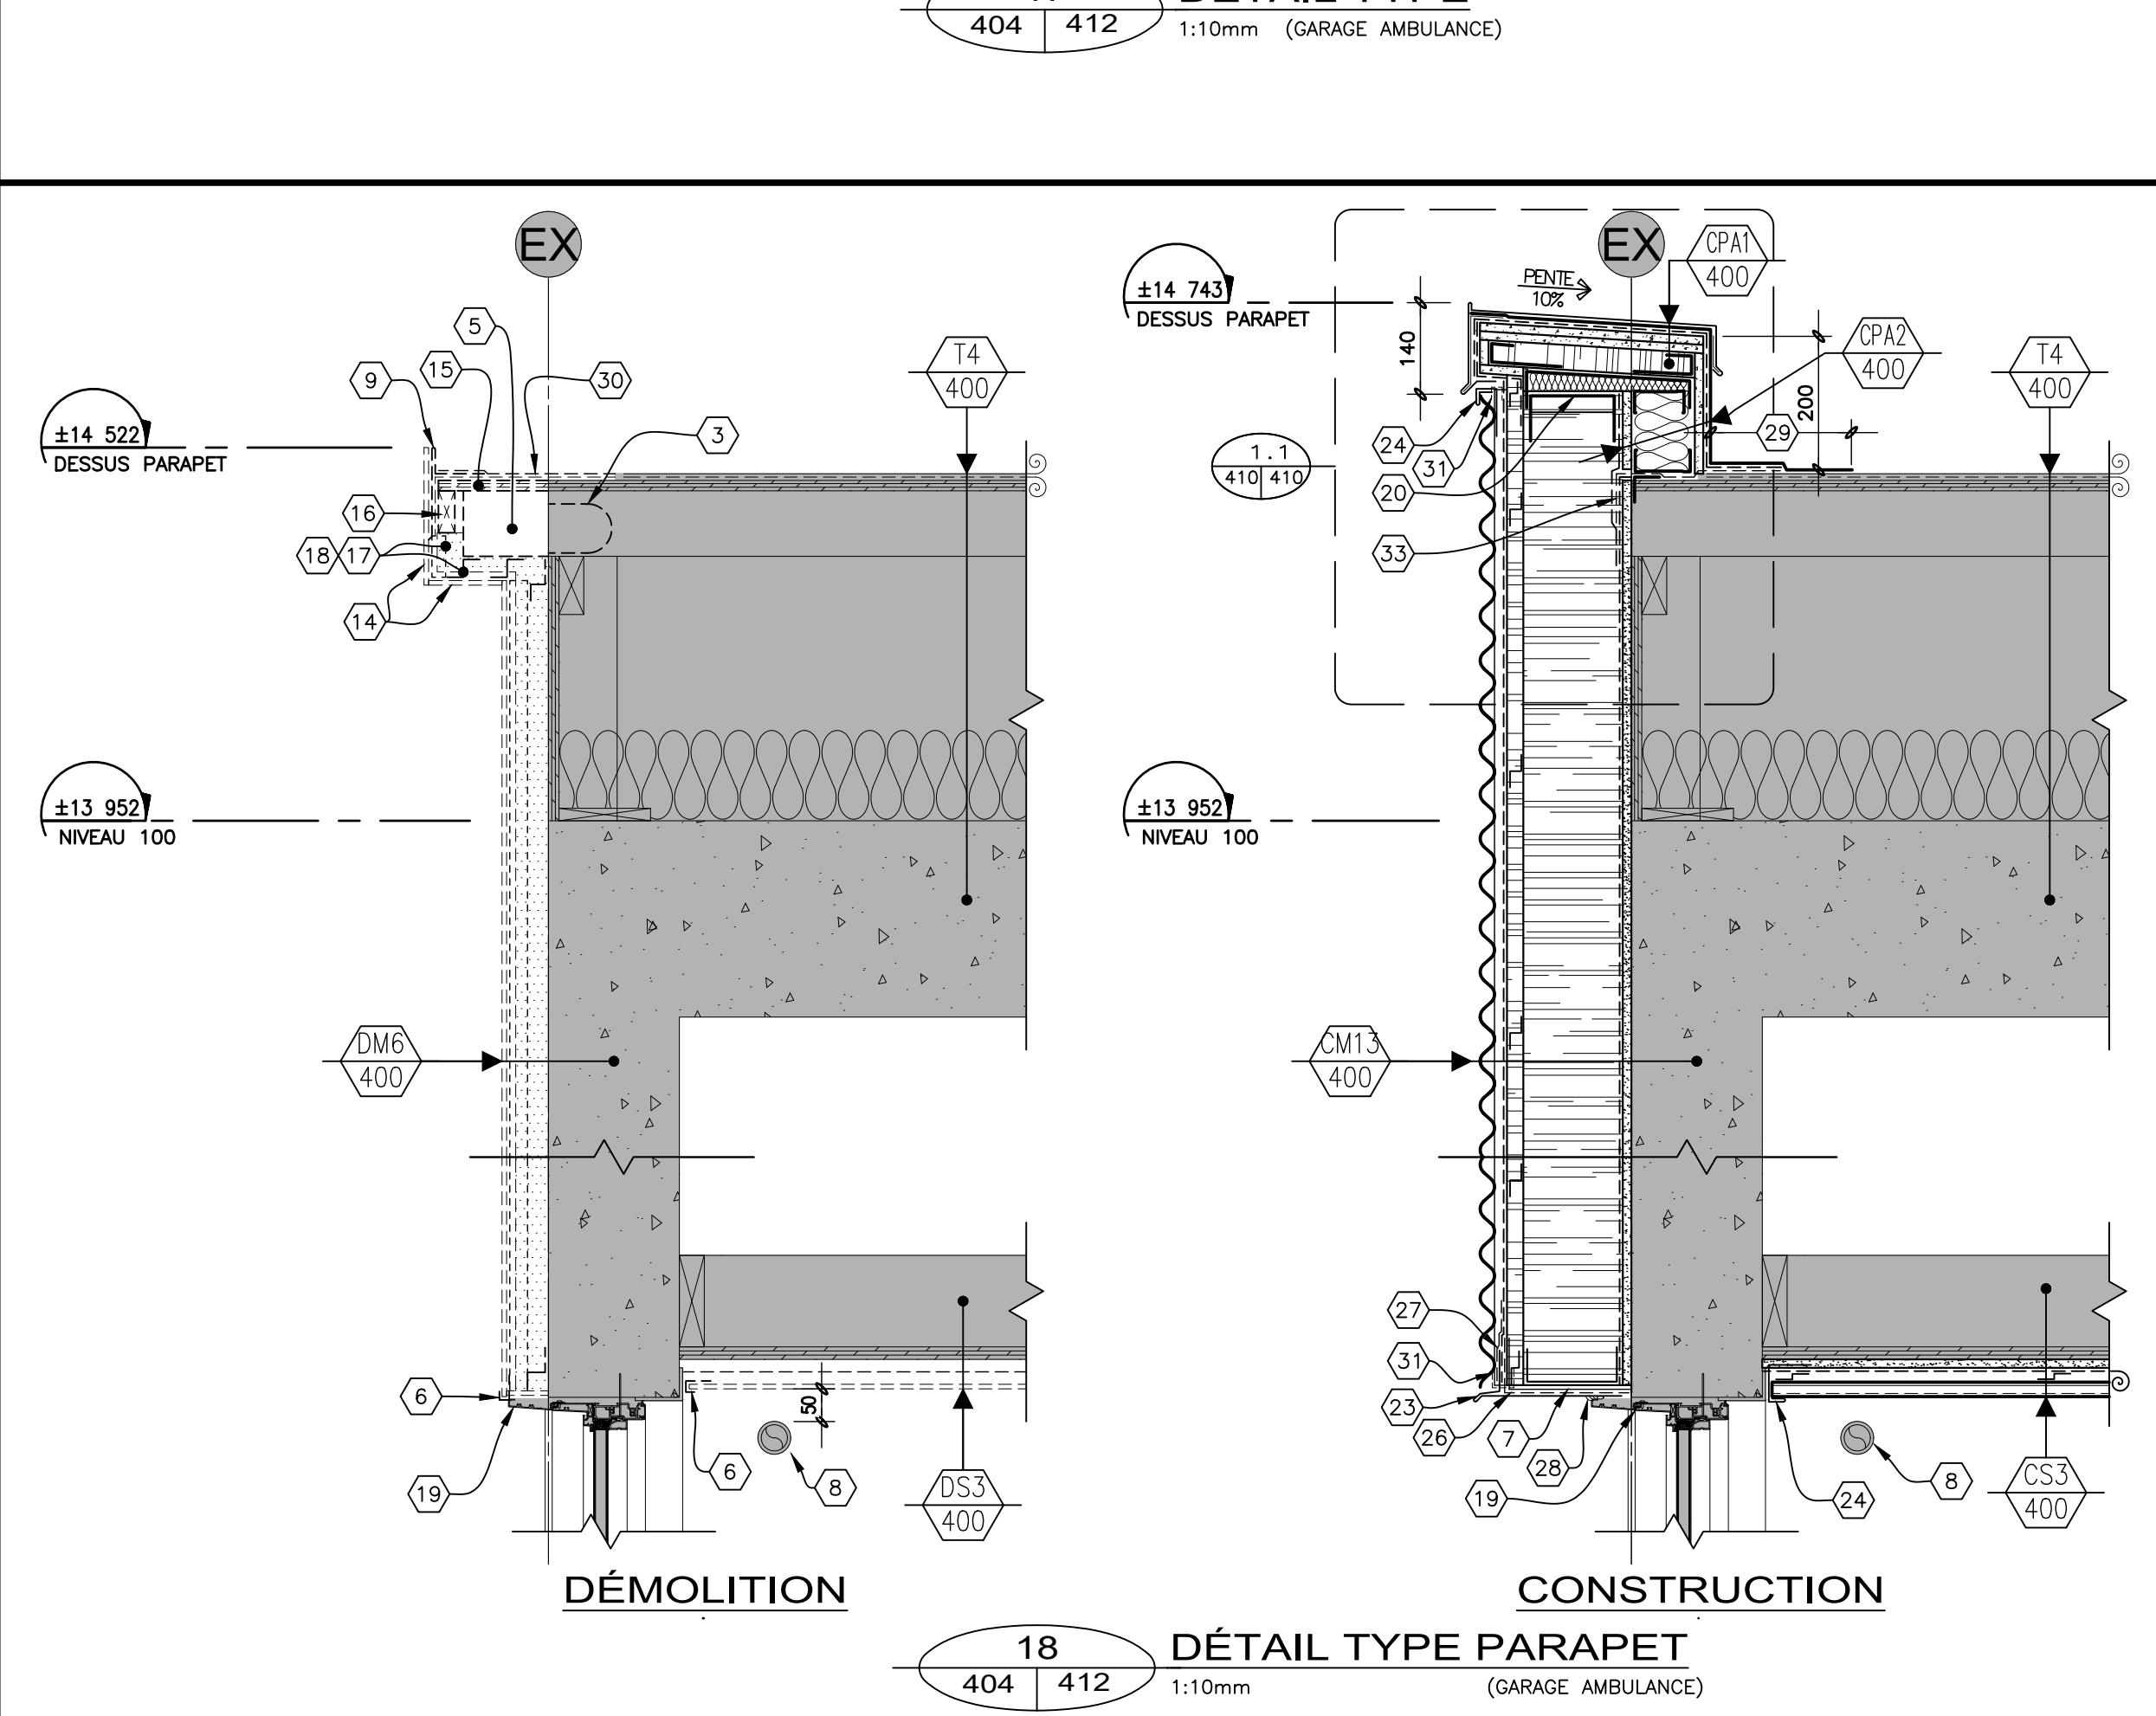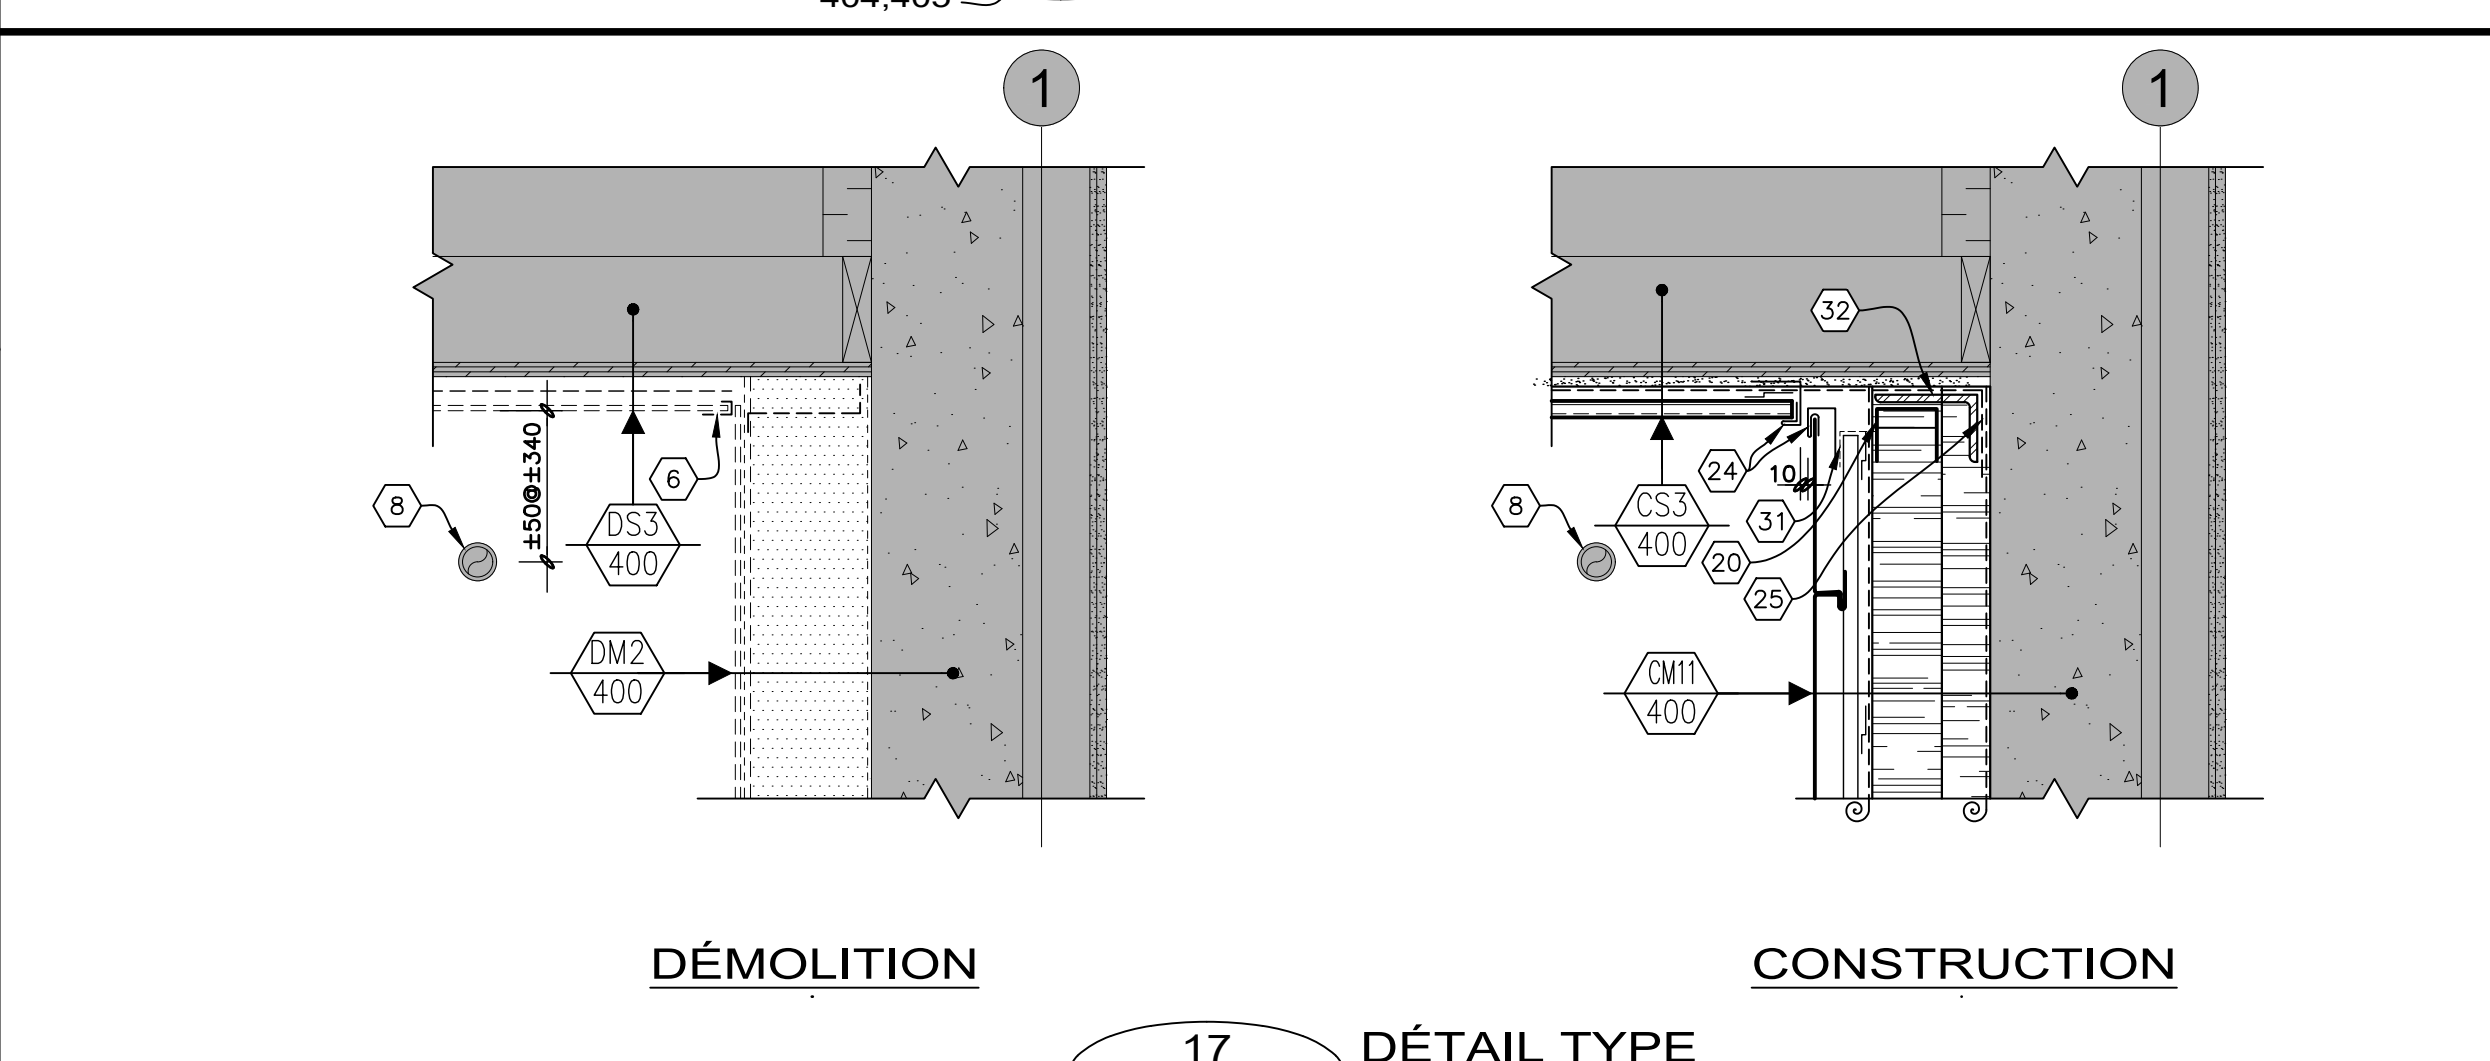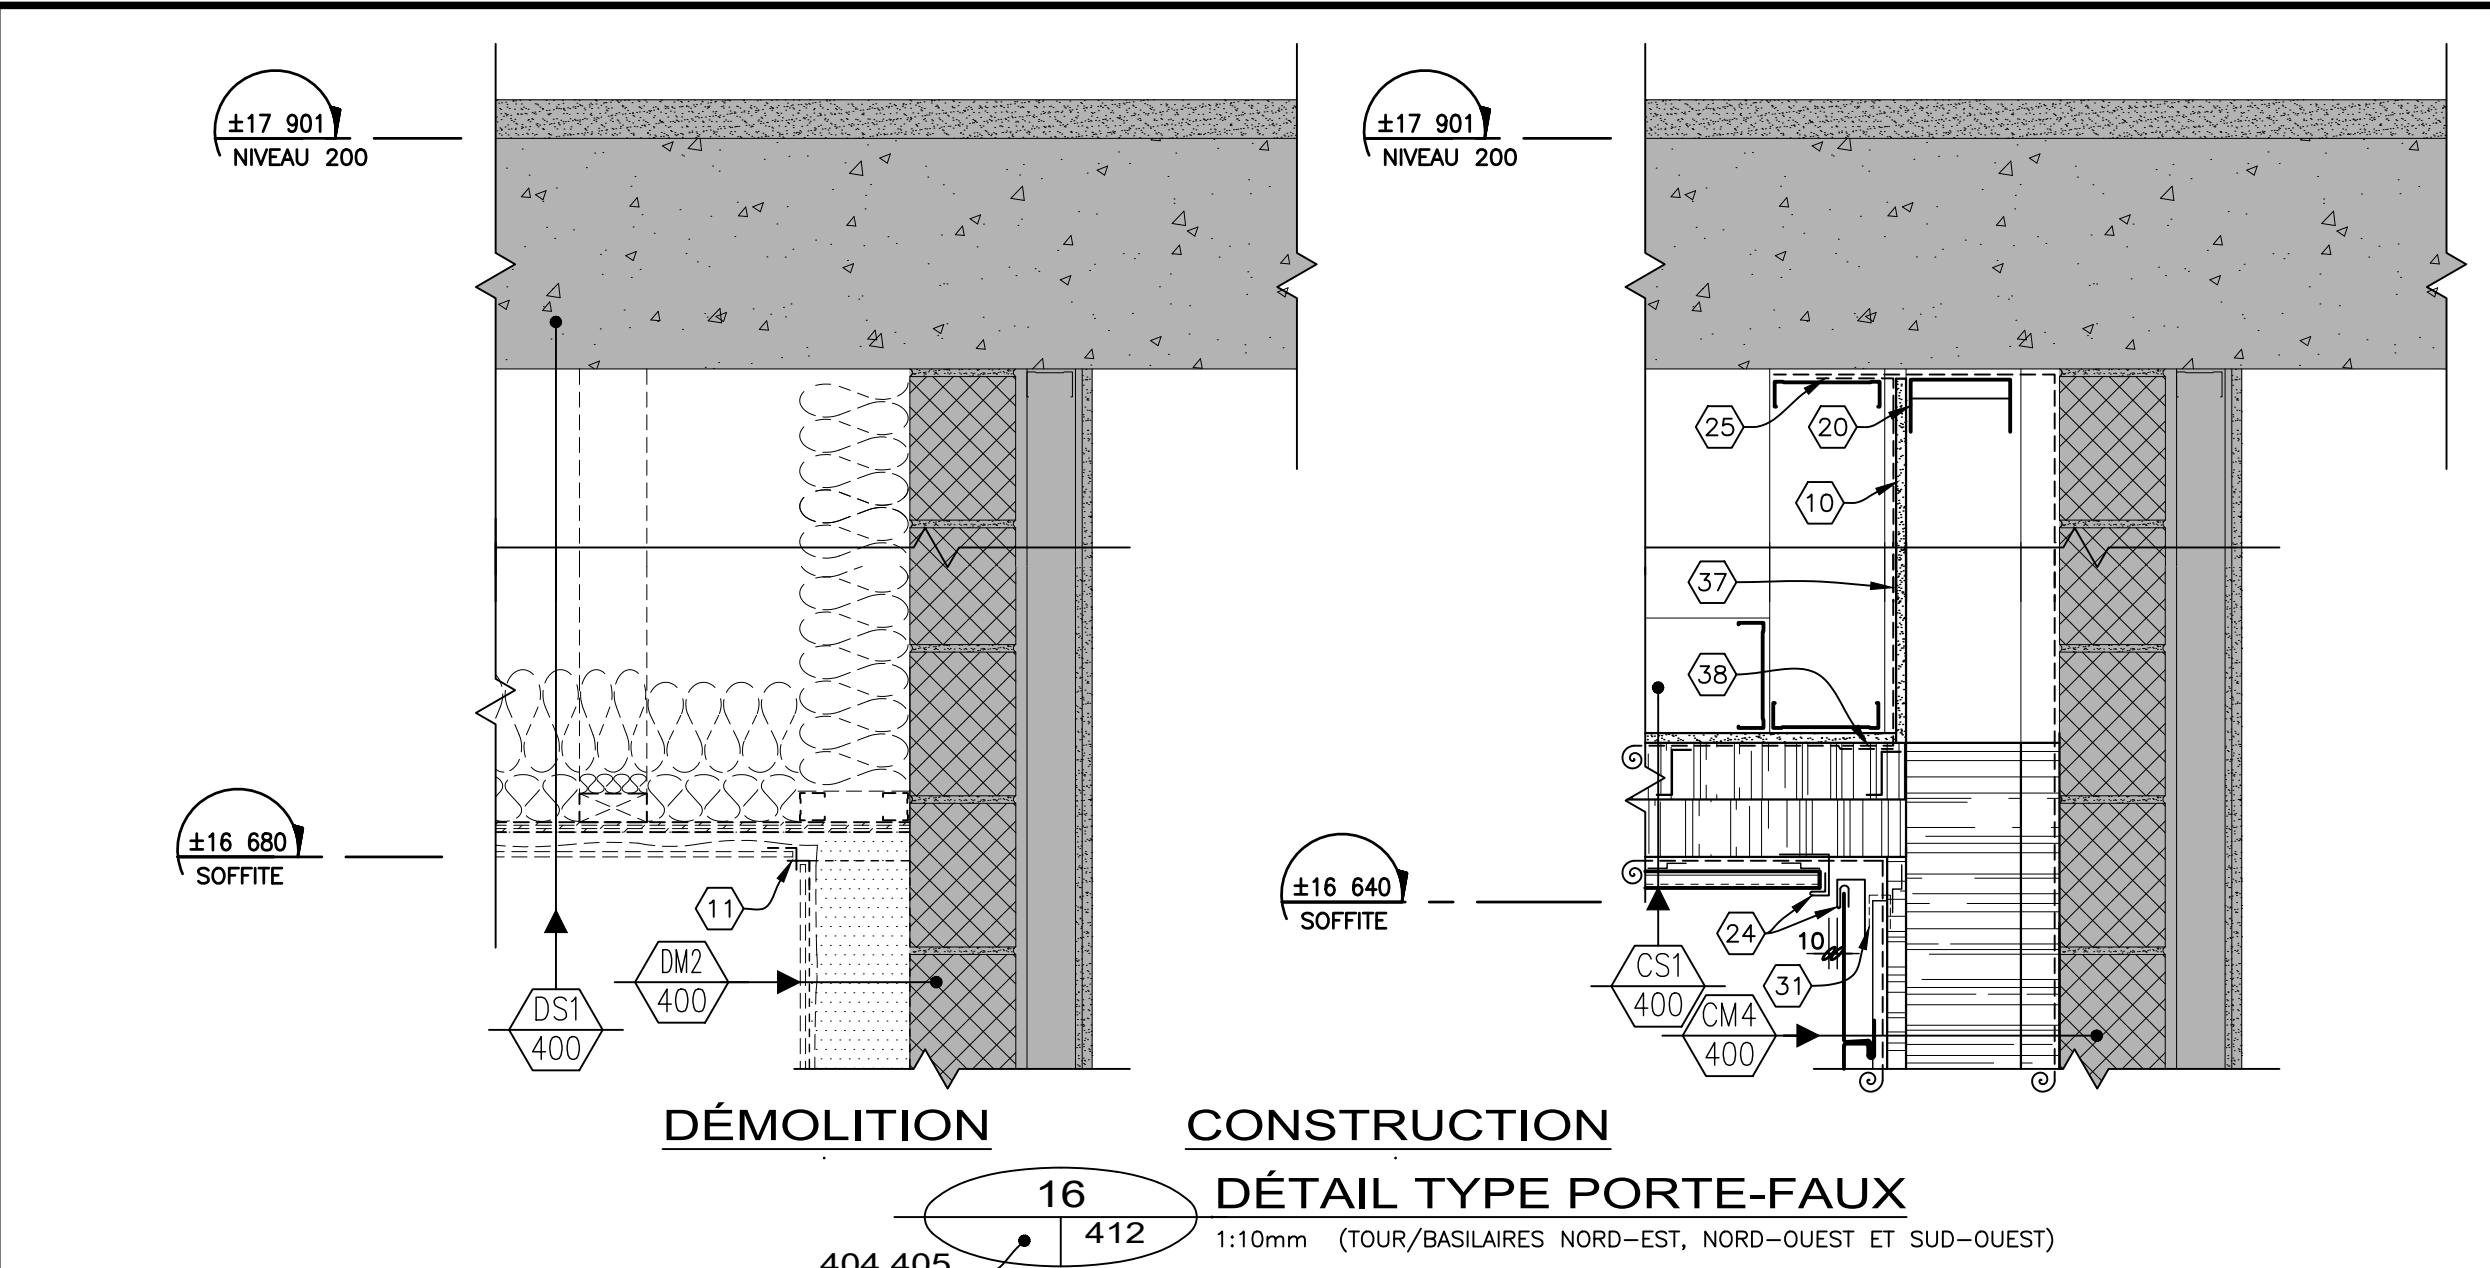

NOTES

- PARAPET PÉRIMÉTRIQUE EN PIÈCE DE BOIS 38mmX140mm RECOUVERT D'UNE MEMBRANE DE BITUME MODIFIÉE EXISTANT À DÉMOLIR.
- MEMBRANE DE BITUME MODIFIÉE BI-COUCHES SUR PANNEAU DE SUPPORT À DÉMOLIR SUR LA LARGEUR REQUISE POUR LA CONSTRUCTION DU NOUVEAU PARAPET.
- FILTRE MÉDIA EXISTANT À ENLEVER.
- APPAREIL D'ÉCLAIRAGE CONTINUE SUR LA FAÇADE PRINCIPALE (SUD), EST ET OUEST DE LA TOUR À ENLEVER ET À REINSTALLER, VOIR INGÉNIEUR.
- MEMBRURE EXISTANTE DE 38mmX89mm À COUPER, VOIR STRUCTURE.
- MOULURE EN ALUMINIUM À DÉMOLIR.
- TÔLE D'APPUI CONTINUE EN ACIER GALVANISÉ CAL.18.
- TUYAU DE GICLÉUR EXISTANT À ±500340mm SOUS LE PAREMENT EXISTANT À CONSERVER.
- SOLIN MÉTALLIQUE À DÉMOLIR.
- PANNEAU DE MAT DE FIBRE DE VERRE 13mm.
- MOULURE DE COIN INTÉRIEUR EXISTANTE À DÉMOLIR.
- CONTREPLAQUÉ À PLUS EXISTANT À DÉMOLIR.
- ÉTRIER À CHAQUE COLOMBAGES OU BARRE "Z" SELON LE CAS, VOIR STRUCTURE.
- PANNEAU DE POLYMÈRES RENFORCÉ DE FIBRES DE VERRE 7mm D'ÉPAISSEUR À DÉMOLIR.
- CONTREPLAQUÉ À PLUS EXISTANT À COUPER SUR LARGEUR REQUISE.
- PIÈCE DE BOIS EXISTANT À DÉMOLIR.
- BARRE "Z" À DÉMOLIR.
- ISOLANT DE POLYURÉTHANE GICLÉ À DÉMOLIR.
- FENÊTRE EXISTANTE À CONSERVER.
- LISSE DE DÉFLEXION, VOIR STRUCTURE.
- CONNECTEUR À CHAQUE BARRE "Z" OU COLOMBAGE SELON LE CAS, VOIR STRUCTURE.
- CORNIÈRE CONTINUE ET CONSOLE, VOIR STRUCTURE.
- SOLIN EN ACIER ÉMAILLÉ, CAL.24 (JOINT AGRAFÉS).
- MOULURE EN "J" EN ACIER ÉMAILLÉ CAL.24.
- CHEVAUCHER D'AU MOINS 75mm LA MEMBRANE.
- MEMBRANE AUTOCOLLANTE.
- SCELLER LA MEMBRANE PARE-INTÉMPIRIES SUR LE SOLIN AVEC UN RUBAN AUTOCOLLANT.
- SCELLANT SUR FOND DE JOINT.
- CHEVAUCHER LA NOUVELLE MEMBRANE SUR LES MEMBRANES DE LA TOITURE EXISTANTE SUR MINIMUM 150mm. DÉGRANULER LA MEMBRANE EXISTANTE AU PRÉALABLE.
- MEMBRANE DE BITUME MODIFIÉE BI-COUCHES À DÉMOLIR SUR LA LARGEUR REQUISE POUR LA CONSTRUCTION DU NOUVEAU PARAPET.
- MOUSTQUAIRE.
- CORNIÈRE, VOIR STRUCTURE.
- MEMBRANE AUTOCOLLANTE. CHEVAUCHER D'AU MOINS 75mm LA MEMBRANE DU MUR ET LA MEMBRANE EXISTANTE DE LA TOITURE.
- SECTION DE MOULURE DE DÉPART POUR APPUI DU PAREMENT DE DÉCLIN D'ALUMINIUM. PAR LE MANUFACTURIER DU PAREMENT DE DÉCLIN D'ALUMINIUM.
- MOULURE EN "J" PAR LE MANUFACTURIER DU PAREMENT DE DÉCLIN D'ALUMINIUM.
- MOULURE DE DÉPART PAR LE MANUFACTURIER DU PAREMENT DE DÉCLIN D'ALUMINIUM.
- MEMBRANE AUTOCOLLANTE PARE-VAPEUR.
- EXCÉDENT DE LA MEMBRANE PARE-VAPEUR. SCELLER LA MEMBRANE SUR LE PANNEAU VERTICALE AVEC LA MEMBRANE AUTOCOLLANTE DU SOFFITE.
- STRUCTURE D'ACIER, VOIR STRUCTURE.
- CHEVAUCHER LA NOUVELLE MEMBRANE SUR LES MEMBRANES DE LA TOITURE EXISTANTE SUR MINIMUM 300mm. DÉGRANULER LA MEMBRANE EXISTANTE AU PRÉALABLE.
- RAGRÉER LA TOITURE TEL QUE L'EXISTANT, VOIR COMPOSITION SUR LE DÉTAIL.
- MURET EN 38X89mm @400mm c/c À DÉMOLIR.
- PANNEAU DE MAT DE FIBRE DE VERRE 16mm, TYPE X.
- FOURRURE D'ÉPAISSEUR REQUISE.

LÉGENDE

- EXISTANT À CONSERVER.
- ÉLÉMENT À DÉMOLIR.
- AXE EXISTANT
- EX EXTÉRIEUR DE LA STRUCTURE DE BÉTON EXISTANTE DE LA TOUR.
- NOUVEL AXE: FACE EXTÉRIEURE DES BARRES Z ET COLOMBAGES DE LA TOUR. VOIR STRUCTURE.
- (*) VOIR NOTE GÉNÉRAL PAGE 400.

NE DOIT PAS SERVIR À L'EXÉCUTION

Le présent document est émis par la seule loi identifiée. Son contenu est protégé par les droits d'auteur et toute reproduction ou modification, partielle ou totale, est interdite sans l'autorisation écrite de gagnon, letellier, cyr, ricard, mathieu, proulx, savard consortium d'architectes.

GLCRM | Proulx Savard |

GLCRM:
128, Avenue de la Cathédrale,
Bureau 201
Rimouski, QC, G5L 5H7
(418) 722-7655

2406, Ch. des Quatres-Bourgeois,
Bureau 100
Québec, QC, G1V 1W5
(418) 647-1700

Proulx Savard Architectes:
75, boul. Arthur-Buies Ouest,
Rimouski QC G5L 5C2
(418) 723-5543

ARCHITECTURE

CONSULTANTS


DESSIN	COUPE DE MUR TYPE	DÉMOLITION ET CONSTRUCTION	PROJET	HÔPITAL DE CHANDLER, Chandler (Redaction de l'enveloppe)	PROPRIÉTAIRE	Santé Québec
DESSIN	COUPE DE MUR TYPE	DÉMOLITION ET CONSTRUCTION	PROJET	HÔPITAL DE CHANDLER, Chandler (Redaction de l'enveloppe)	PROPRIÉTAIRE	Santé Québec

DOSSIER No.	DATE	REVISIONS
24-187 / 687-24	SEPTEMBRE 2024	

DESSINATEUR (S)	DATE	REVISIONS
DB AL	INDIQUÉE	


PROJET	DATE	REVISIONS
05	2024-09-04	DÉFINITIVES POUR SOUMISSION
06	2024-08-21	DÉFINITIVES 100% POUR APPROBATION
03	2024-08-03	DÉFINITIVES 80% POUR APPROBATION
02	2024-05-14	DÉFINITIVES 40% POUR APPROBATION
01	2024-02-27	PRÉLIMINAIRES 20% POUR APPROBATION

412

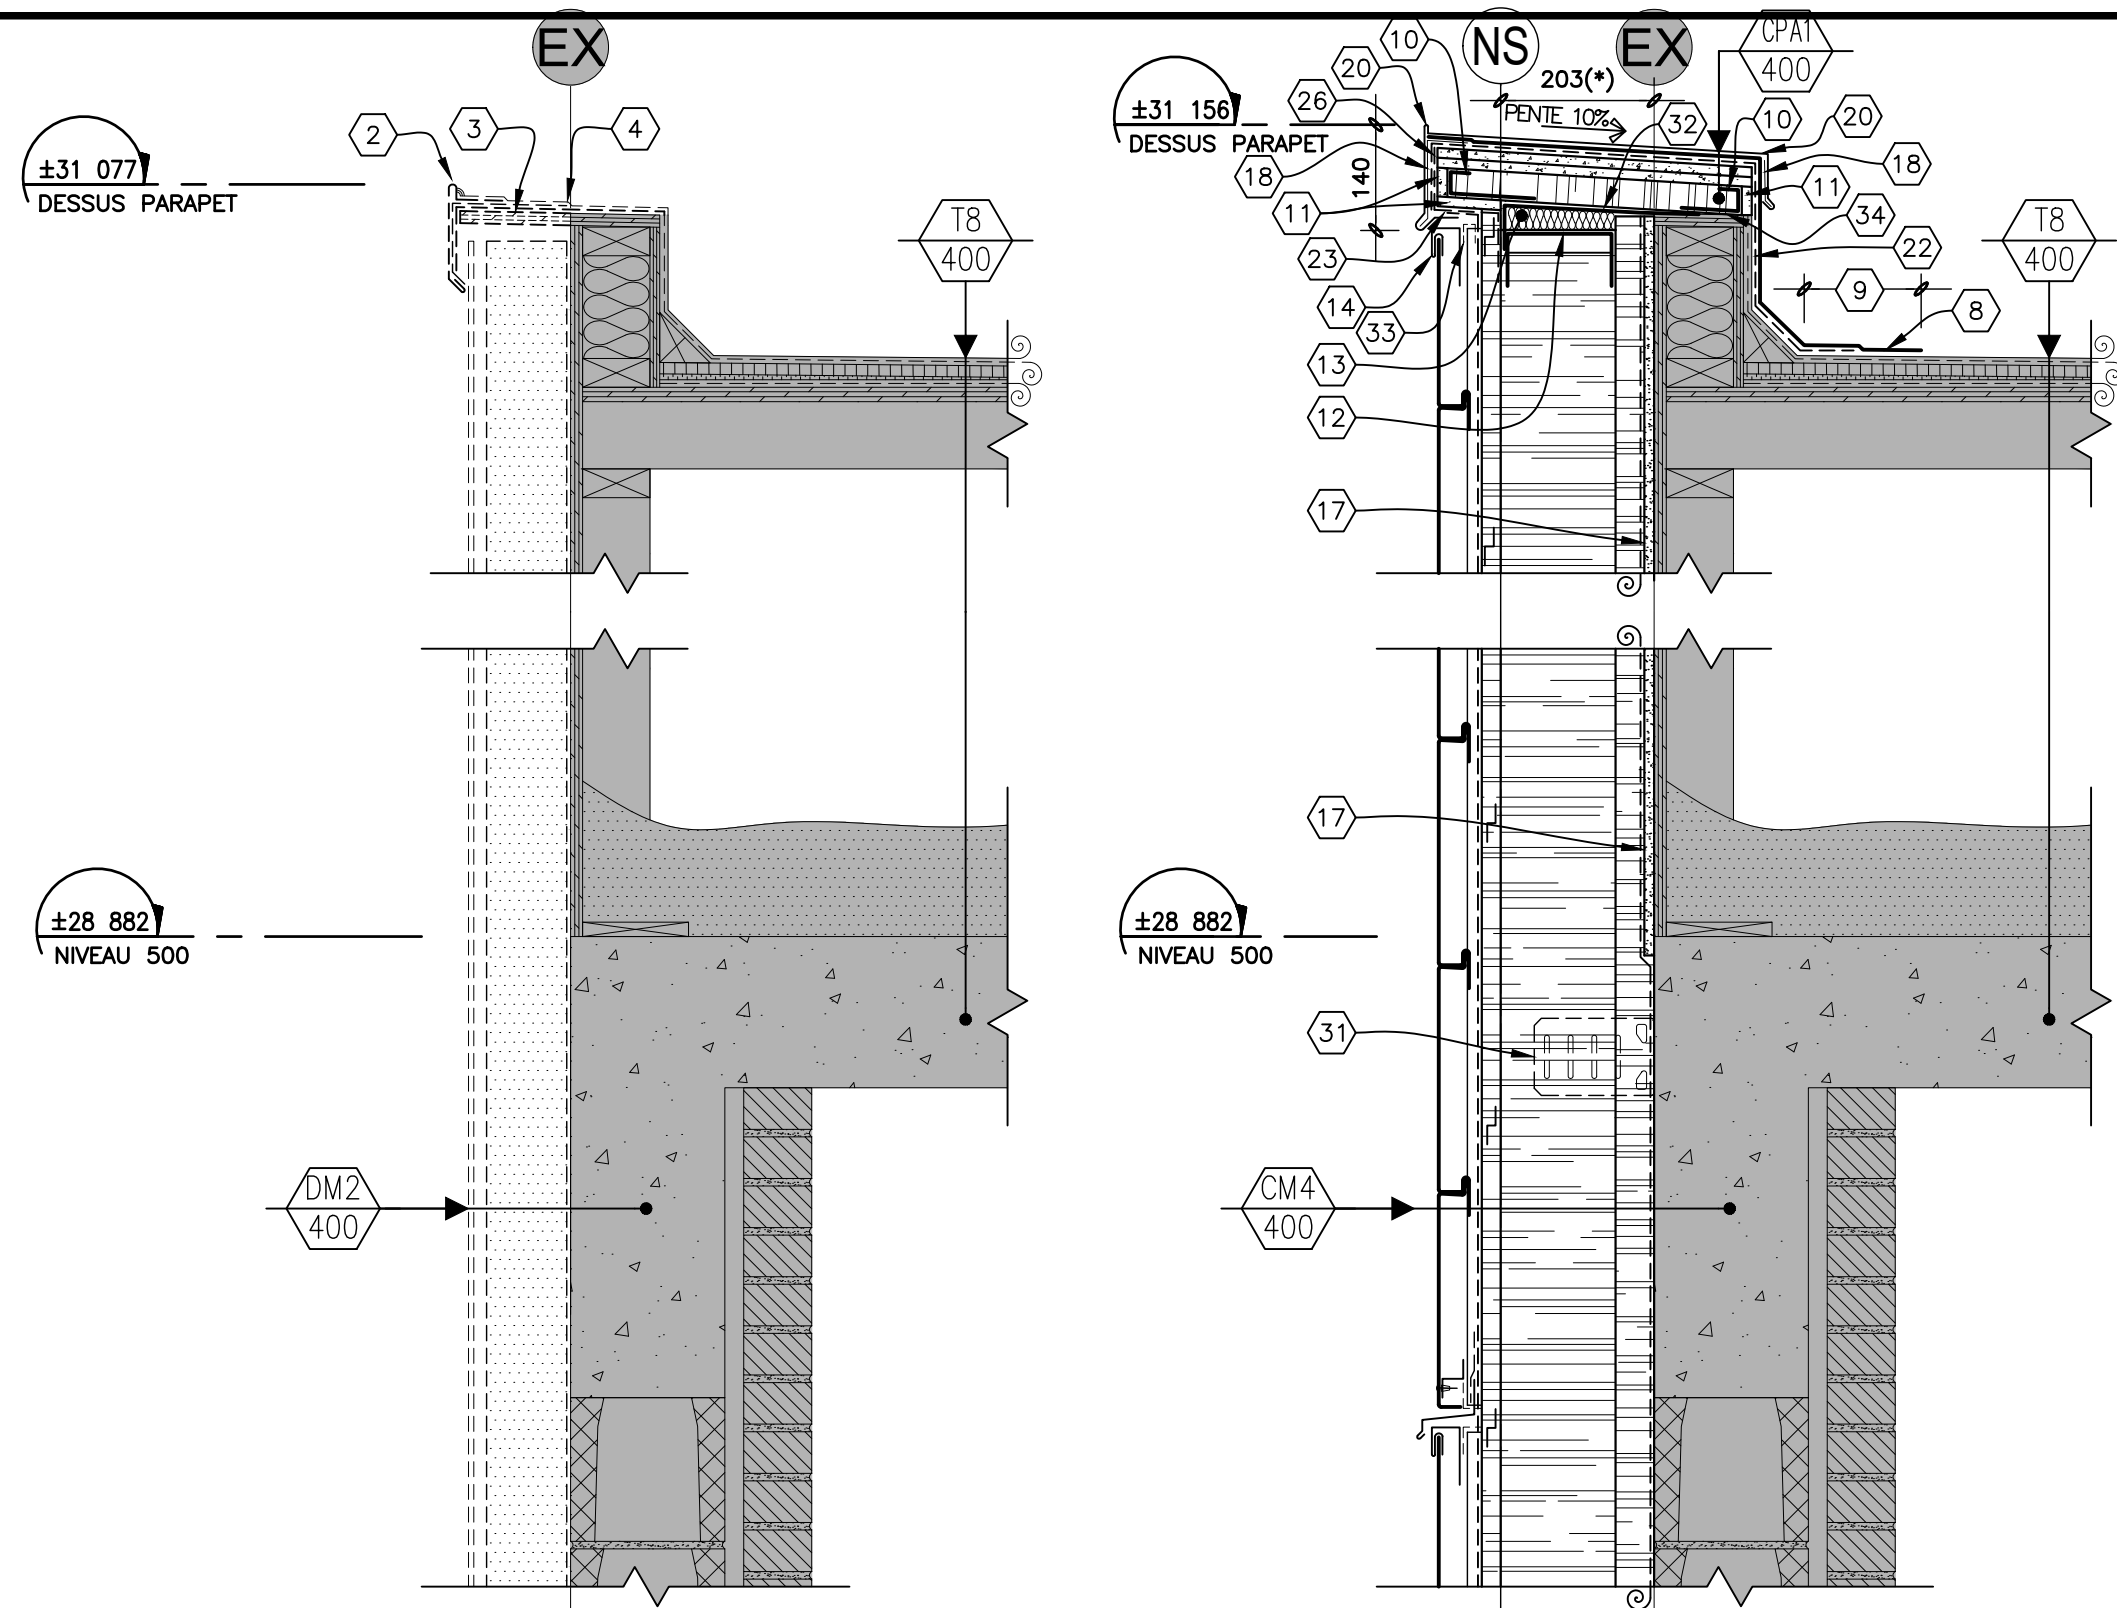


DÉMOLITION **CONSTRUCTION**

19 DÉTAIL TYPE PARAPET
(ESCALIER #3 - TOUR)
1:10mm
406 413

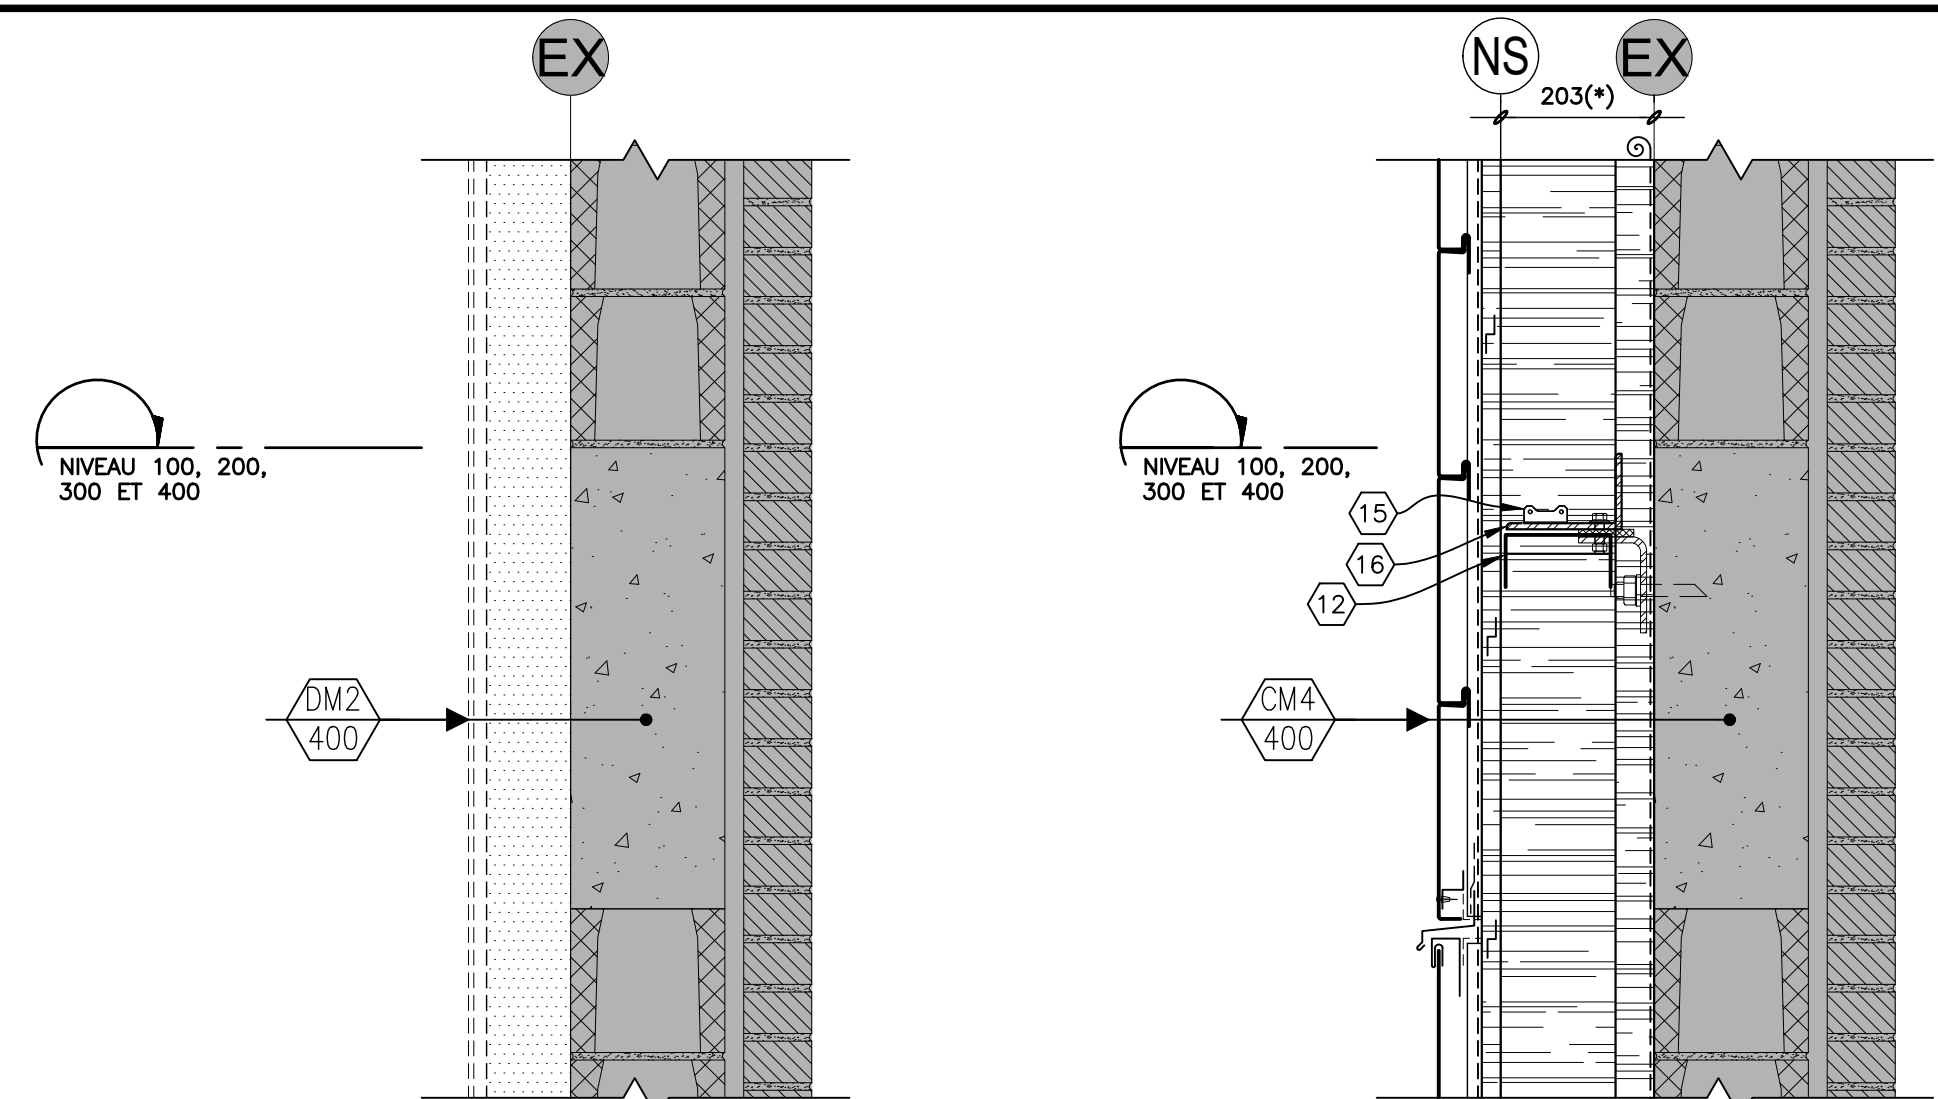

DÉMOLITION **CONSTRUCTION**


20 DÉTAIL TYPE
(ESCALIER #3 - TOUR)
1:10mm
406 413

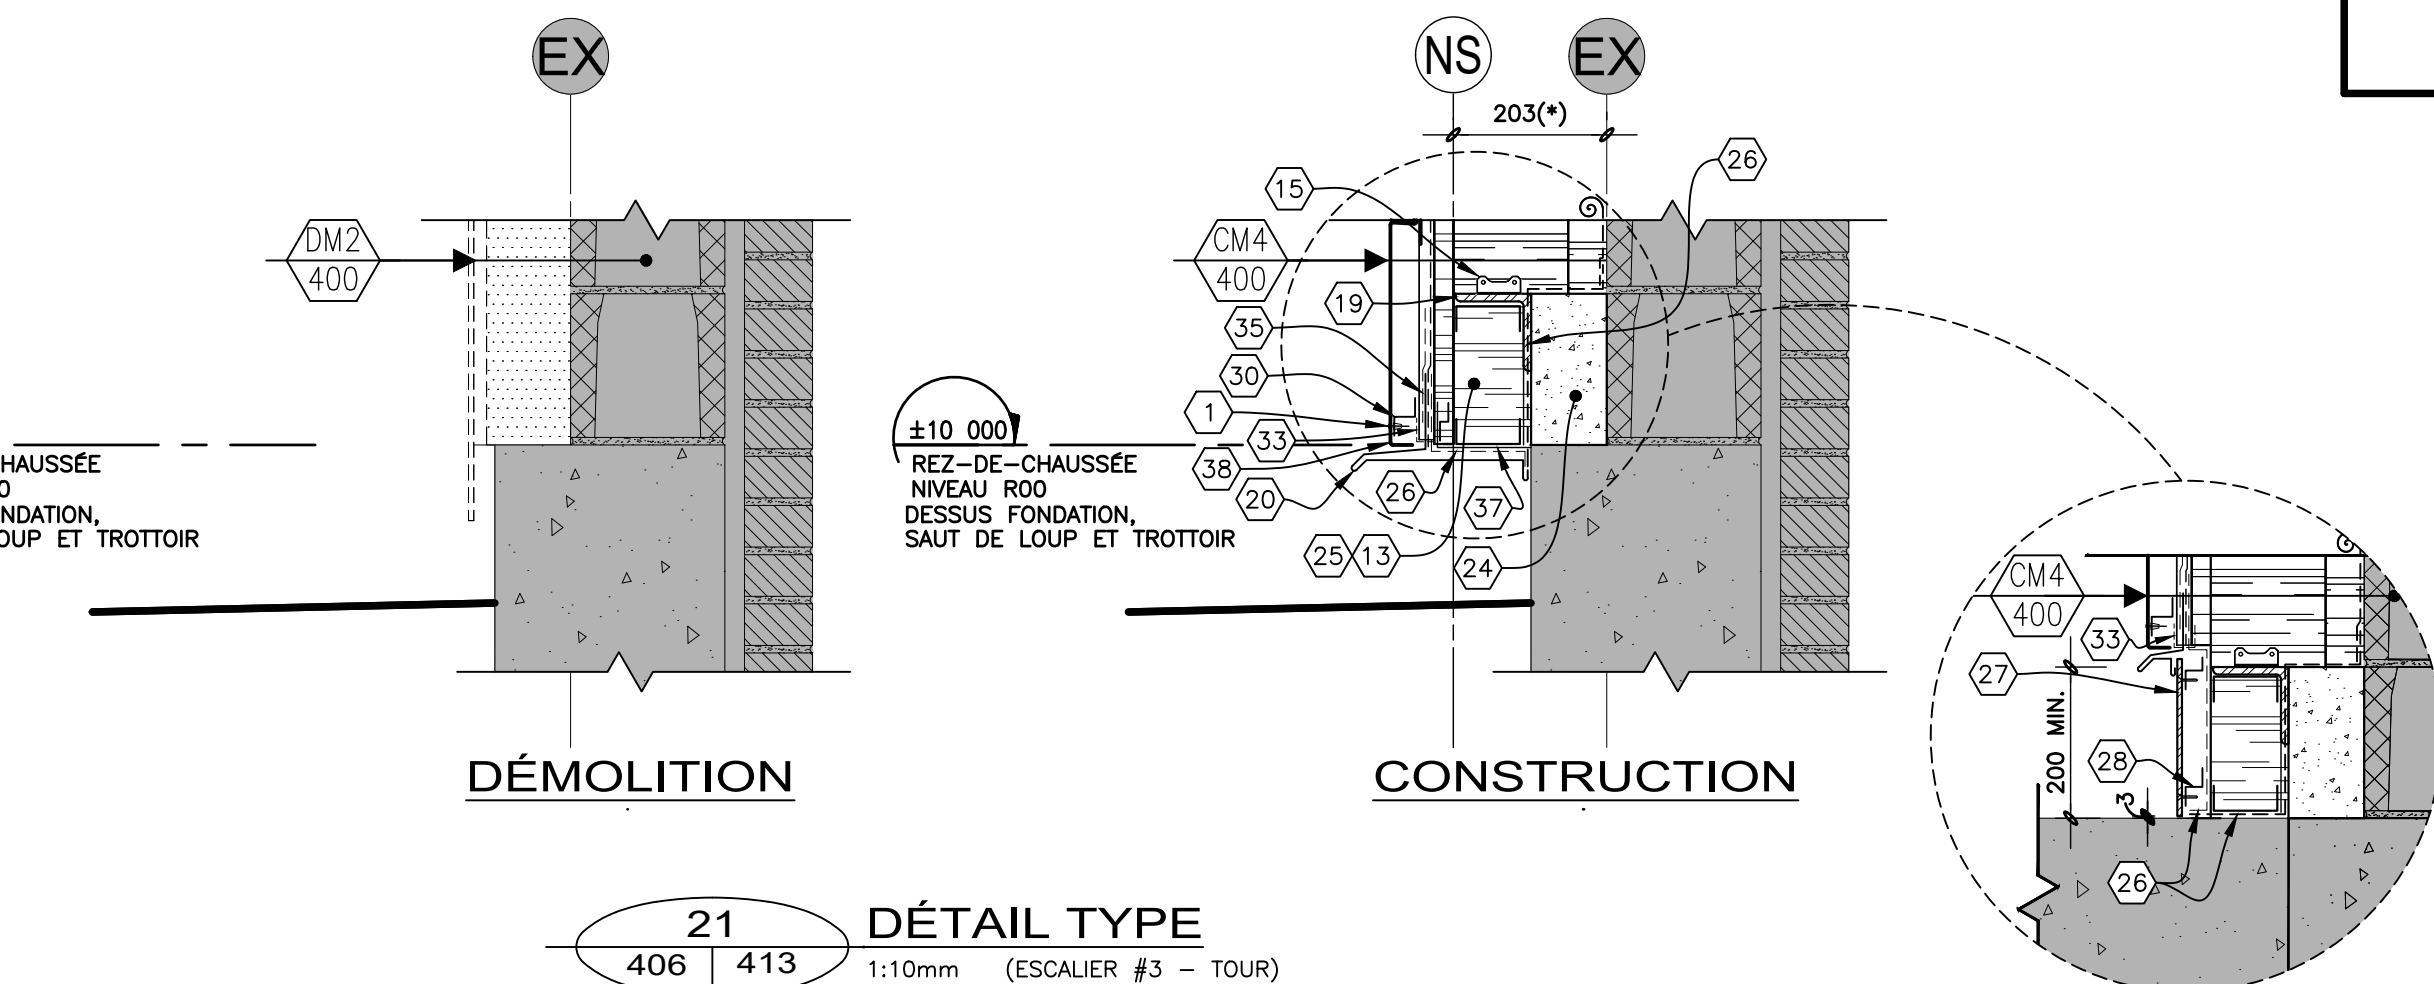

DÉMOLITION **CONSTRUCTION**


21 DÉTAIL TYPE
(ESCALIER #3 - TOUR)
1:10mm
406 413

21.1 VIS-À-VIS TROTTOIR ET SAUT DE LOUP
1:10mm
204 413

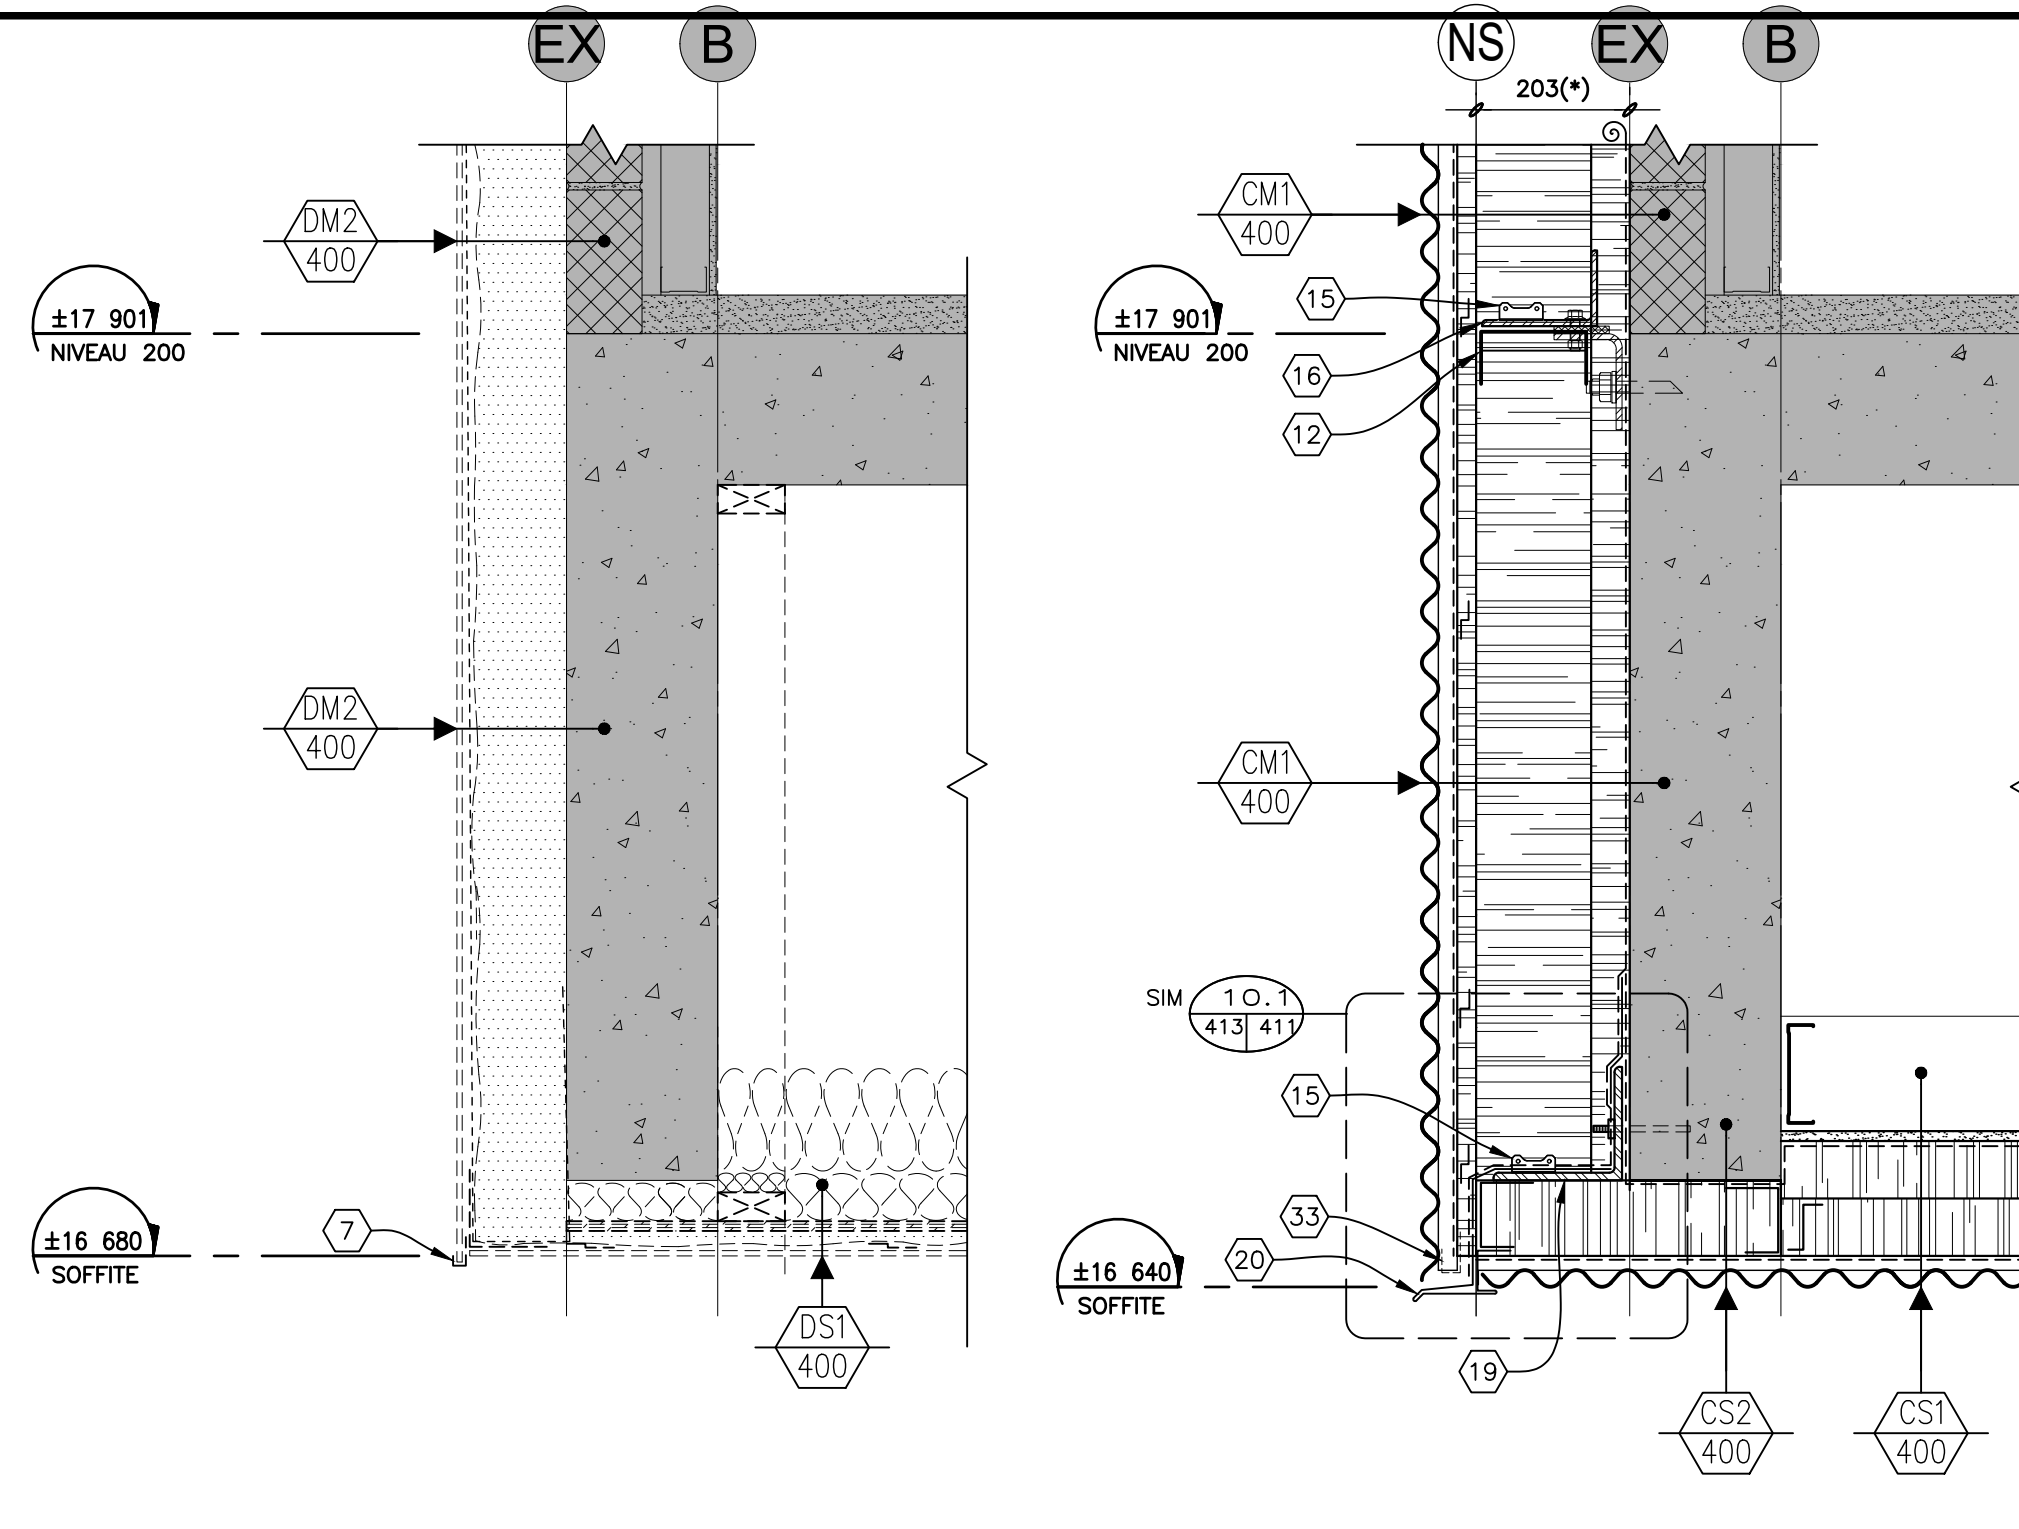


DÉMOLITION **CONSTRUCTION**

22 DÉTAIL TYPE PORTE-À-FAUX
(TOUR/BASILAIRE NORD-EST)
1:10mm
405 413

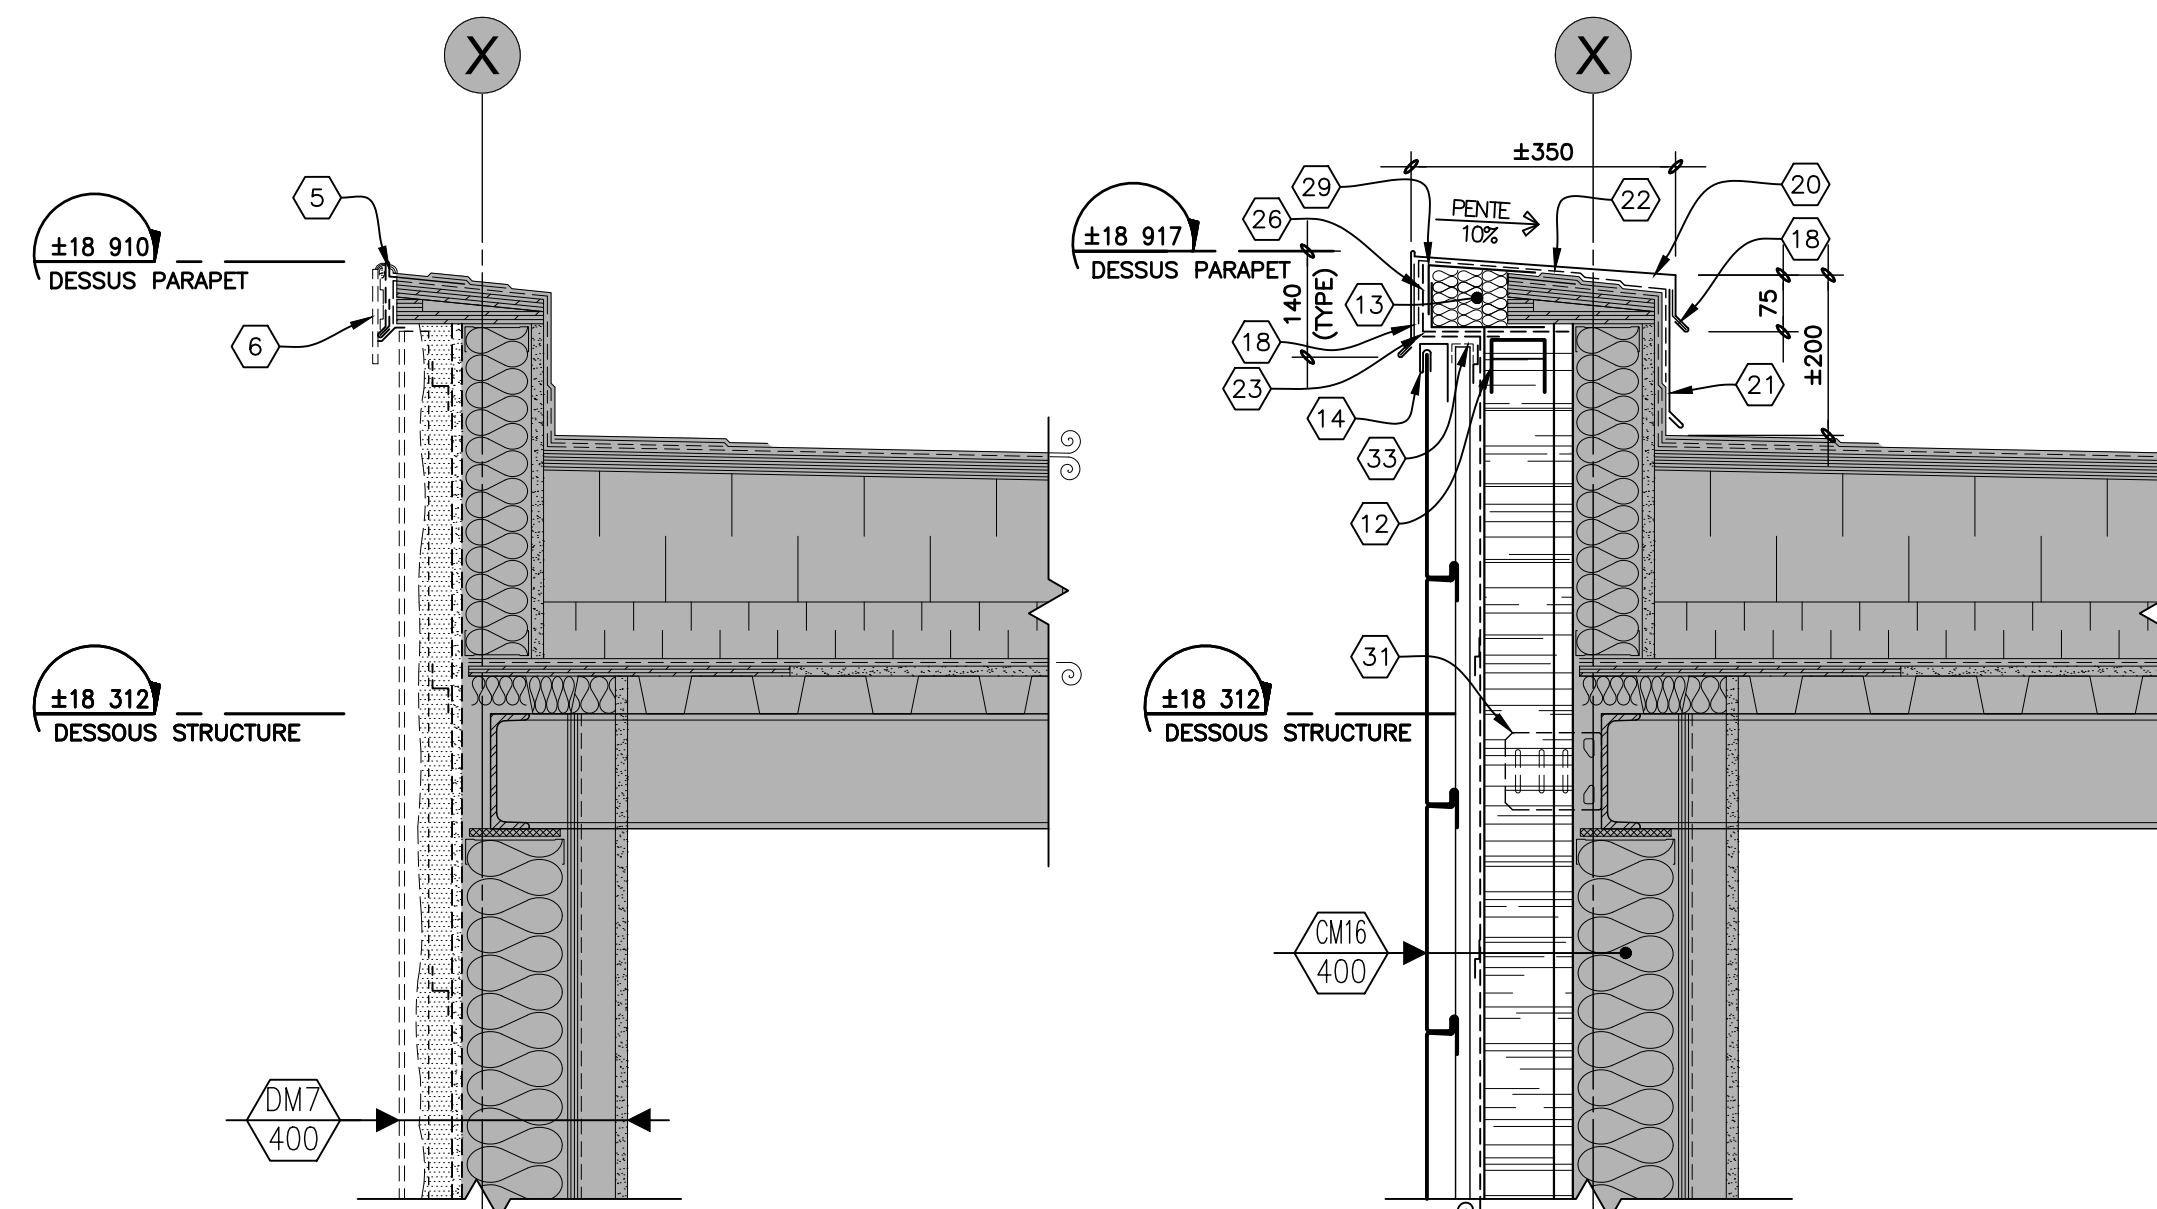

DÉMOLITION **CONSTRUCTION**

23 DÉTAIL TYPE PARAPET
(ESCALIER #6 - ADMIN.)
1:10mm
406 413

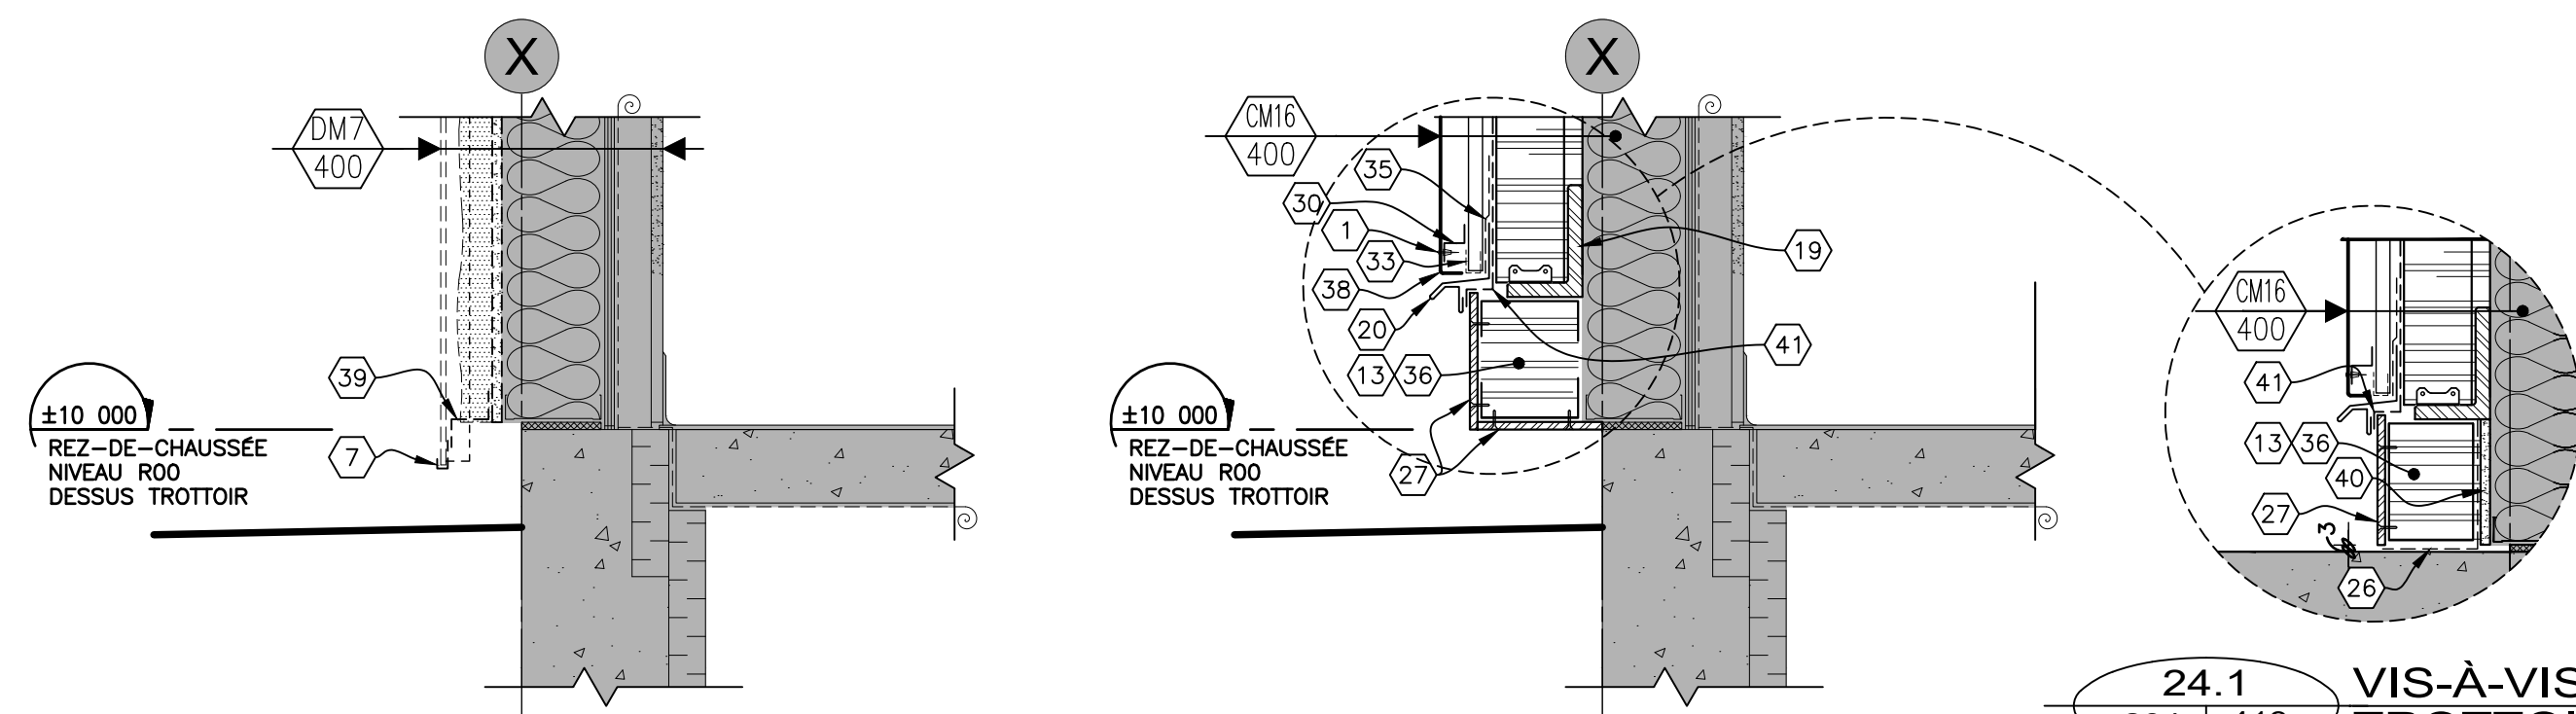

DÉMOLITION **CONSTRUCTION**

24 DÉTAIL TYPE
(ESCALIER #6 - ADMIN.)
1:10mm
406 413

24.1 VIS-À-VIS TROTTOIR
1:10mm
204 413

NOTES

- 1) RIVET EN ACIER INOXYDABLE.
- 2) SOLIN EXISTANT À DÉMOLIR.
- 3) CONTREPLAQUÉ À PLUS EXISTANT À COUPER.
- 4) MEMBRANES EXISTANTES À DÉMOLIR SUR LE DESSUS DU PARAPET.
- 5) SOLIN EXISTANT À COUPER ET ENLEVER.
- 6) PANNEAU DE POLYMERES RENFORCE DE FIBRES DE VERRE 7mm D'ÉPAISSEUR À DÉMOLIR.
- 7) MOULURE EN ALUMINIUM À DÉMOLIR.
- 8) MEMBRANE DE FINITION GRANULEE.
- 9) CHEVAUCHER LA NOUVELLE MEMBRANE SUR LES MEMBRANES DE LA TOITURE EXISTANTE SUR MINIMUM 150mm. DÉGRANULER LA MEMBRANE EXISTANTE AU PRÉALABLE.
- 10) PLAGIAGE DE TÔLE EN "J", CAL.18 EN ACIER GALVANISÉ.
- 11) PANNEAU DE CIMENT 13mm.
- 12) LISSE DE DÉFLEXION, VOIR STRUCTURE.
- 13) REMPLIR L'ESPACE DE LAINE DE FIBRE DE ROCHE.
- 14) MOULURE EN "J" ACIER ÉMAILLÉ, CAL.24.
- 15) CONNECTEUR À CHAQUE COLOMBAGES OU BARRE "Z" SELON LE CAS, VOIR STRUCTURE.
- 16) CORNIÈRE CONTINUE ET CONSOLE, VOIR STRUCTURE.
- 17) PANNEAU DE MAT DE FIBRE DE VERRE 16mm, TYPE X.
- 18) AGRAFE EN ACIER GALVANISÉ, CAL.24 CONTINUE.
- 19) CORNIÈRE, VOIR STRUCTURE.
- 20) SOLIN EN ACIER ÉMAILLÉ, CAL.24 (JOINT AGRAFÉS).
- 21) CONTRE-SOLIN EN ACIER ÉMAILLÉ CAL.24.
- 22) MEMBRANE SOUS-COUCHE.
- 23) SCELLER LA MEMBRANE PARE-INTÉMPÉRIES SUR LE PARAPET AVEC UN RUBAN AUTOCOLLANT.
- 24) BÉTON, VOIR STRUCTURE.
- 25) COLOMBAGE MÉTALLIQUE 92mm Ø400mm c/c.
- 26) MEMBRANE AUTOCOLLANTE.
- 27) PLAQUE EN ACIER GALVANISÉ À CHAUD 150mm DE HAUT X 6mm D'ÉPAISSEUR. FIXER LA PLAQUE À L'AIDE DE VIS EN ACIER INOXYDABLE À TÊTE FRAISÉE.
- 28) BARRE "Z" 38mm EN ACIER GALVANISÉ CAL.18.
- 29) DEUX (2) PLAGIAGES DE TÔLE EN "L", CAL.16 EN ACIER GALVANISÉ.
- 30) PLAGIAGE DE TÔLE EN ACIER GALVANISÉ, CAL.22.
- 31) ÉTRIER À CHAQUE COLOMBAGES OU BARRE "Z" SELON LE CAS, VOIR STRUCTURE.
- 32) PLAGIAGE DE TÔLE, CAL.16 EN ACIER GALVANISÉ, FIXÉ SUR LE DESSUS DU PARAPET EXISTANT.
- 33) MOUSTIQUEAIRE.
- 34) CALE D'AJUSTEMENT EN ACIER GALVANISÉ D'ÉPAISSEUR REQUISE.
- 35) SCELLER LA MEMBRANE PARE-INTÉMPÉRIES SUR LE SOLIN AVEC UN RUBAN AUTOCOLLANT.
- 36) BARRE Z OU COLOMBAGE EN ACIER GALVANISÉ DE DIMENSIONS REQUISES. CAL. 16. FIXÉ AU COLOMBAGE EXISTANT.
- 37) PLAGIAGE DE TÔLE EN ACIER GALVANISÉ CAL.18.
- 38) BOUT DU PANNEAU REPLIÉ VERS L'INTÉRIEUR.
- 39) BARRE EN "Z" EXISTANTE À DÉMOLIR.
- 40) PANNEAU DE MAT DE FIBRE DE VERRE 13mm.
- 41) RETOURNER LA MEMBRANE PARE-INTÉMPÉRIES SUR LE DEVANT DE LA PLAQUE.

LÉGENDE

- EXISTANT À CONSERVER.
- ÉLÉMENT À DÉMOLIR.
- AXE EXISTANT
- EX EXTÉRIEUR DE LA STRUCTURE DE BÉTON EXISTANTE DE LA TOUR.
- NS NOUVEL AXE: FACE EXTÉRIEURE DES BARRES Z ET COLOMBAGES DE LA TOUR. VOIR STRUCTURE.
- (*) VOIR NOTE GÉNÉRAL PAGE 400.

NE DOIT PAS SERVIR À L'EXÉCUTION

Le présent document est émis pour la seule fin identifiée. Son contenu est protégé par les droits d'auteur et toute reproduction ou modification, partielle ou totale, est interdite sans l'autorisation écrite de l'auteur, le letelier, cyr, ricard, mathieu, prout, savard consortium d'architectes.




GLCRM | Proulx Savard |

GLCRM:
128, Avenue de la Cathédrale,
Bureau 201
Rimouski, QC, G5L 5H7
(418) 722-7655



2406, Ch. des Quatres-Bourgeois,
Bureau 100
Québec, QC, G1V 1W5
(418) 647-1700

Proulx Savard Architectes:
75, boul. Arthur-Buies Ouest,
Rimouski, QC G5L 5C2
(418) 723-5543

ARCHITECTURE

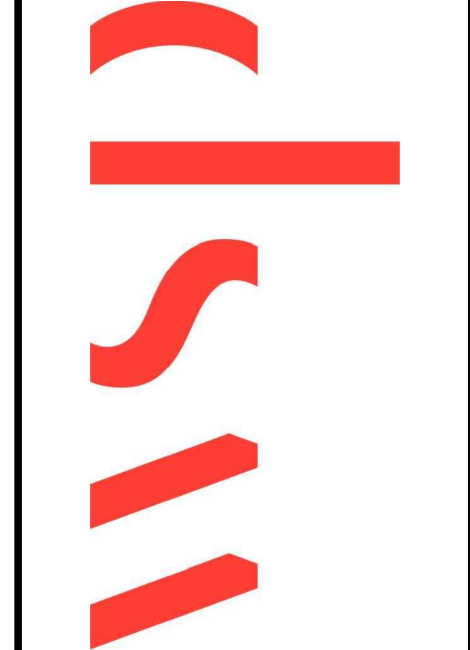

CONSULTANTS

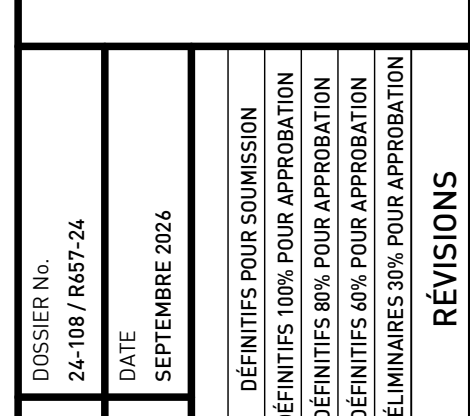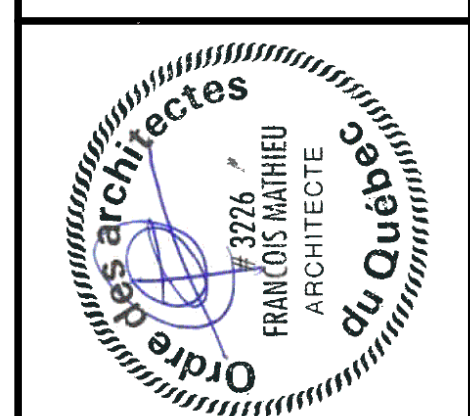

DESIGNATEUR(S)	DATE	REVISIONS
DB ALL	SEPTEMBRE 2026	
INDIQUEE		
08	2024-08-04	DÉFINITIVES POUR SOUMISSION
09	2024-08-21	DÉFINITIVES 100% POUR APPROBATION
10	2024-08-23	DÉFINITIVES 90% POUR APPROBATION
11	2024-08-24	DÉFINITIVES 80% POUR APPROBATION
12	2024-08-27	PRELIMINAIRES 50% POUR APPROBATION

PROJET	PROPRIÉTAIRE
HÔPITAL DE CHANDLER, Chandler (Réfection de l'enveloppe)	Santé Québec

COUPE DE MUR TYPE
DÉMOLITION ET CONSTRUCTION

413