




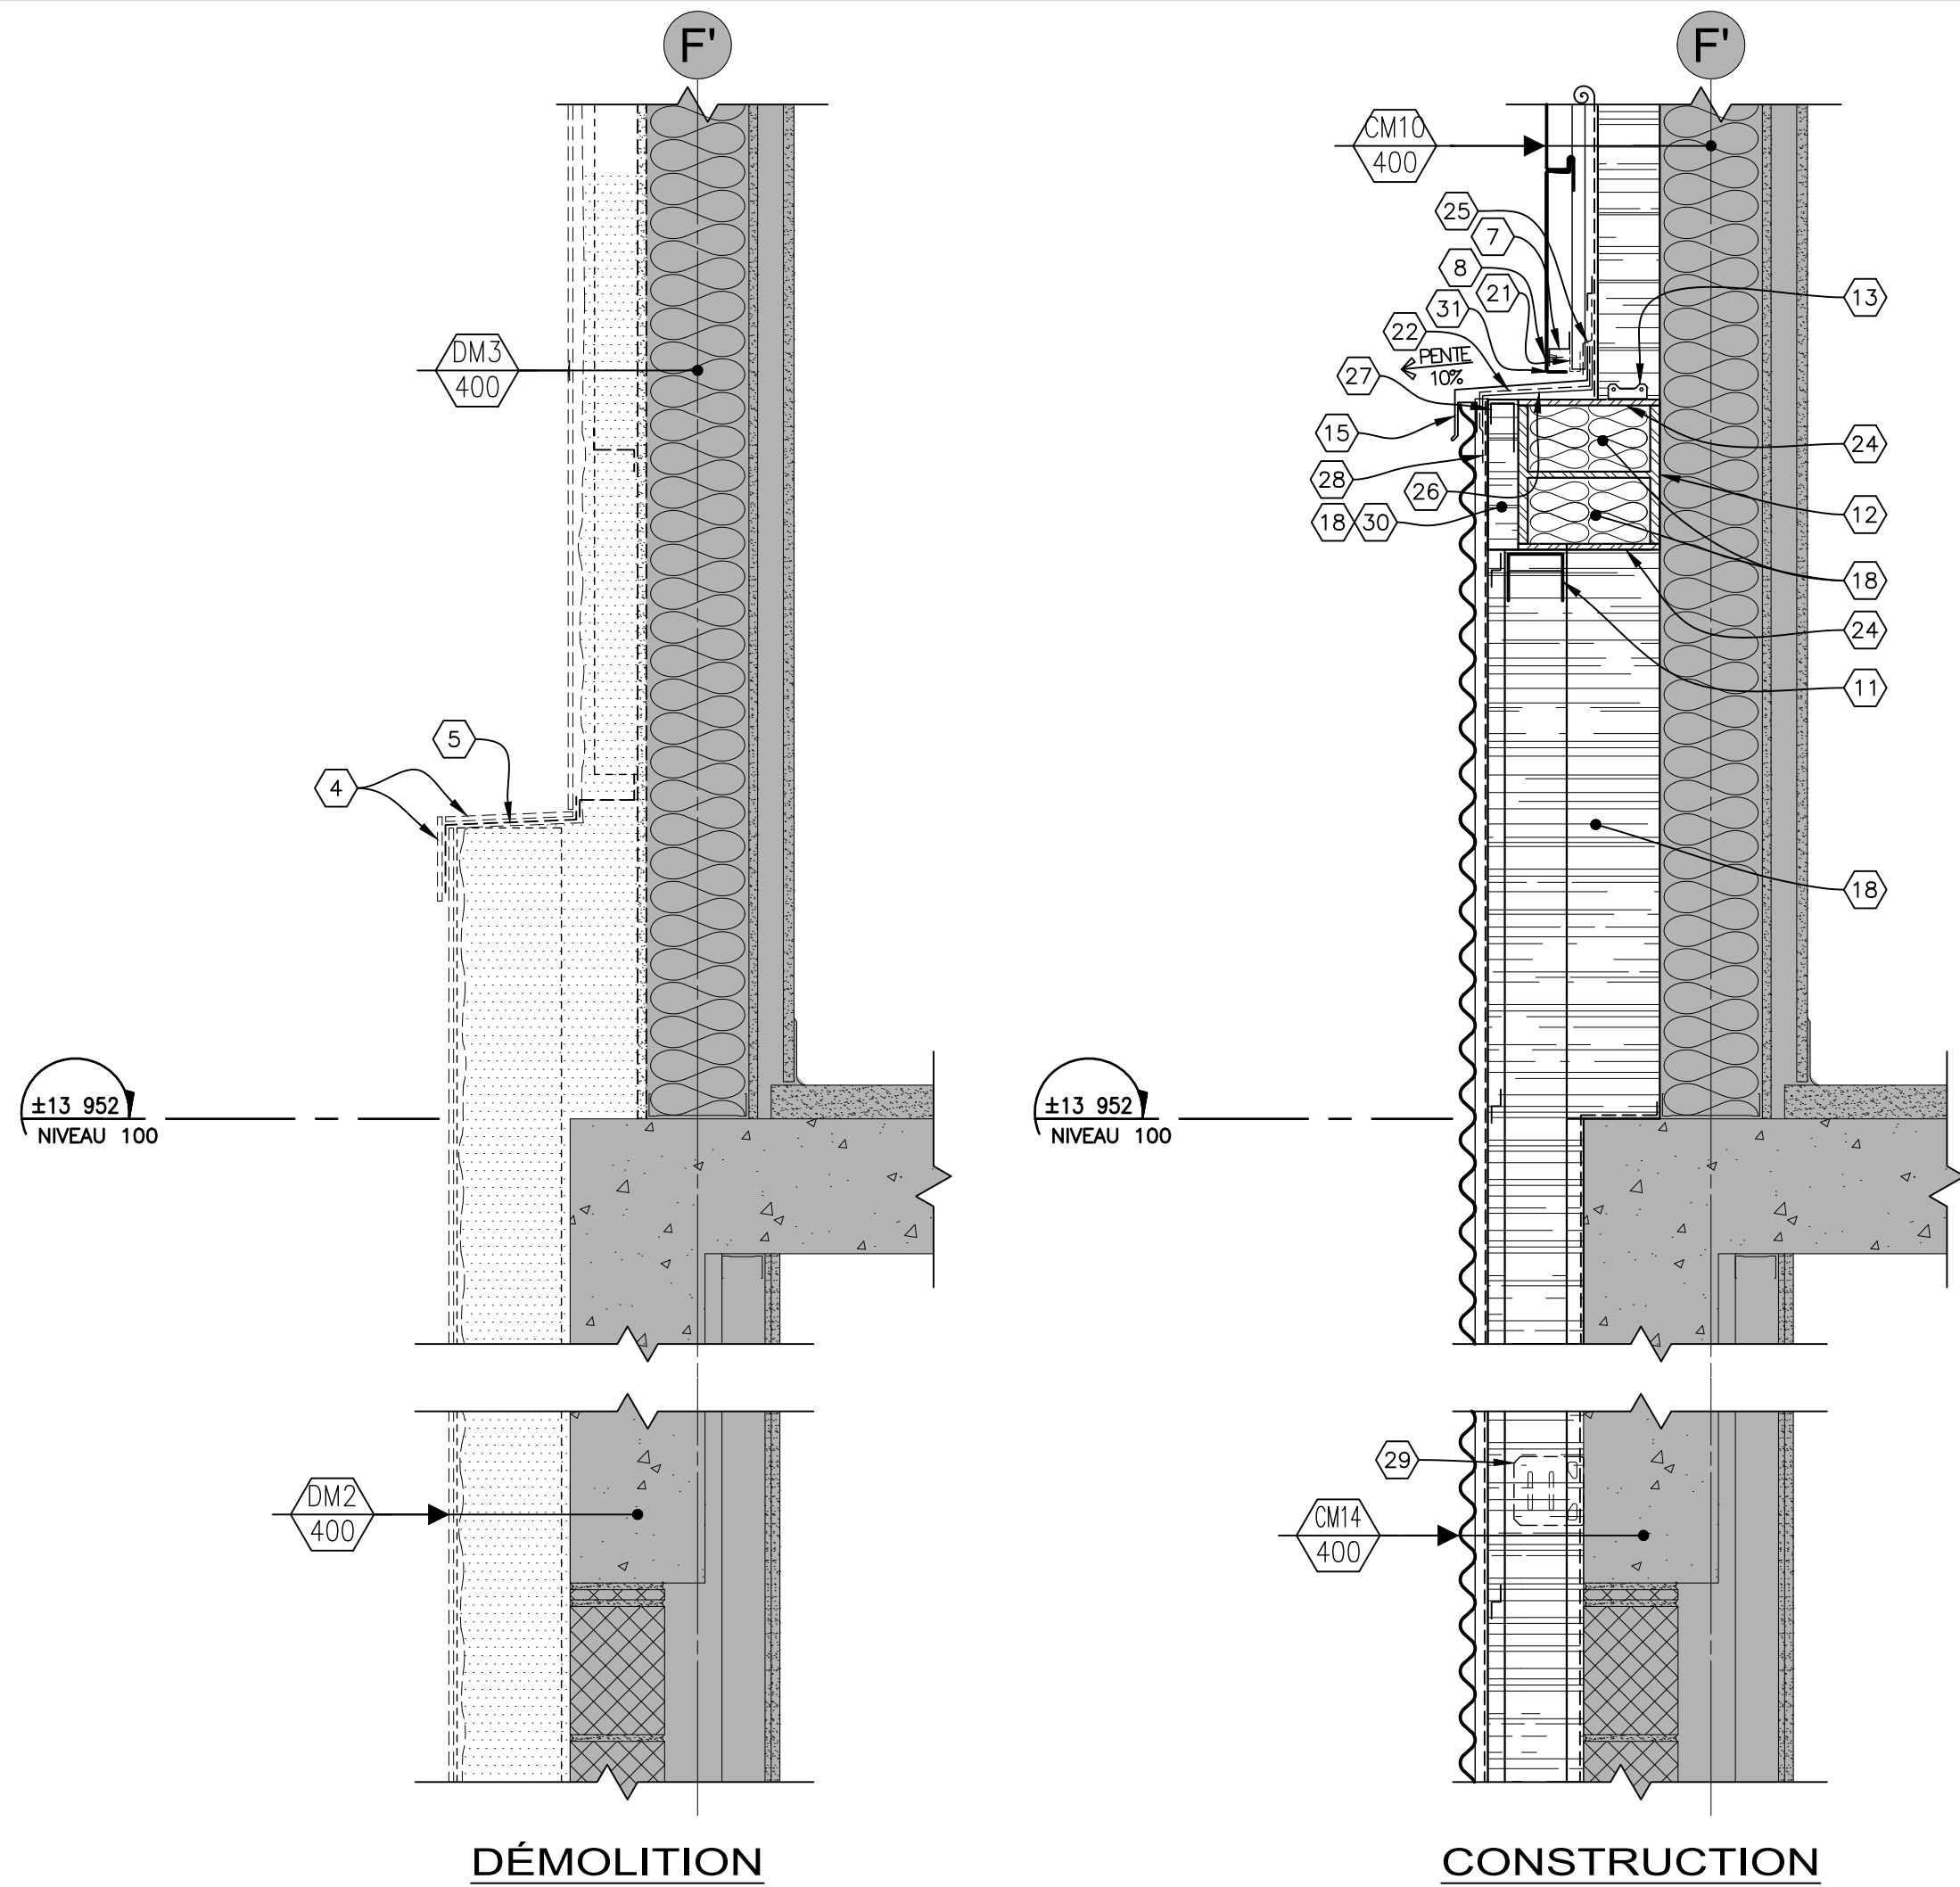


25 DÉTAIL TYPE PARAPET
406,513 414 1:10mm (ADMINISTRATION)

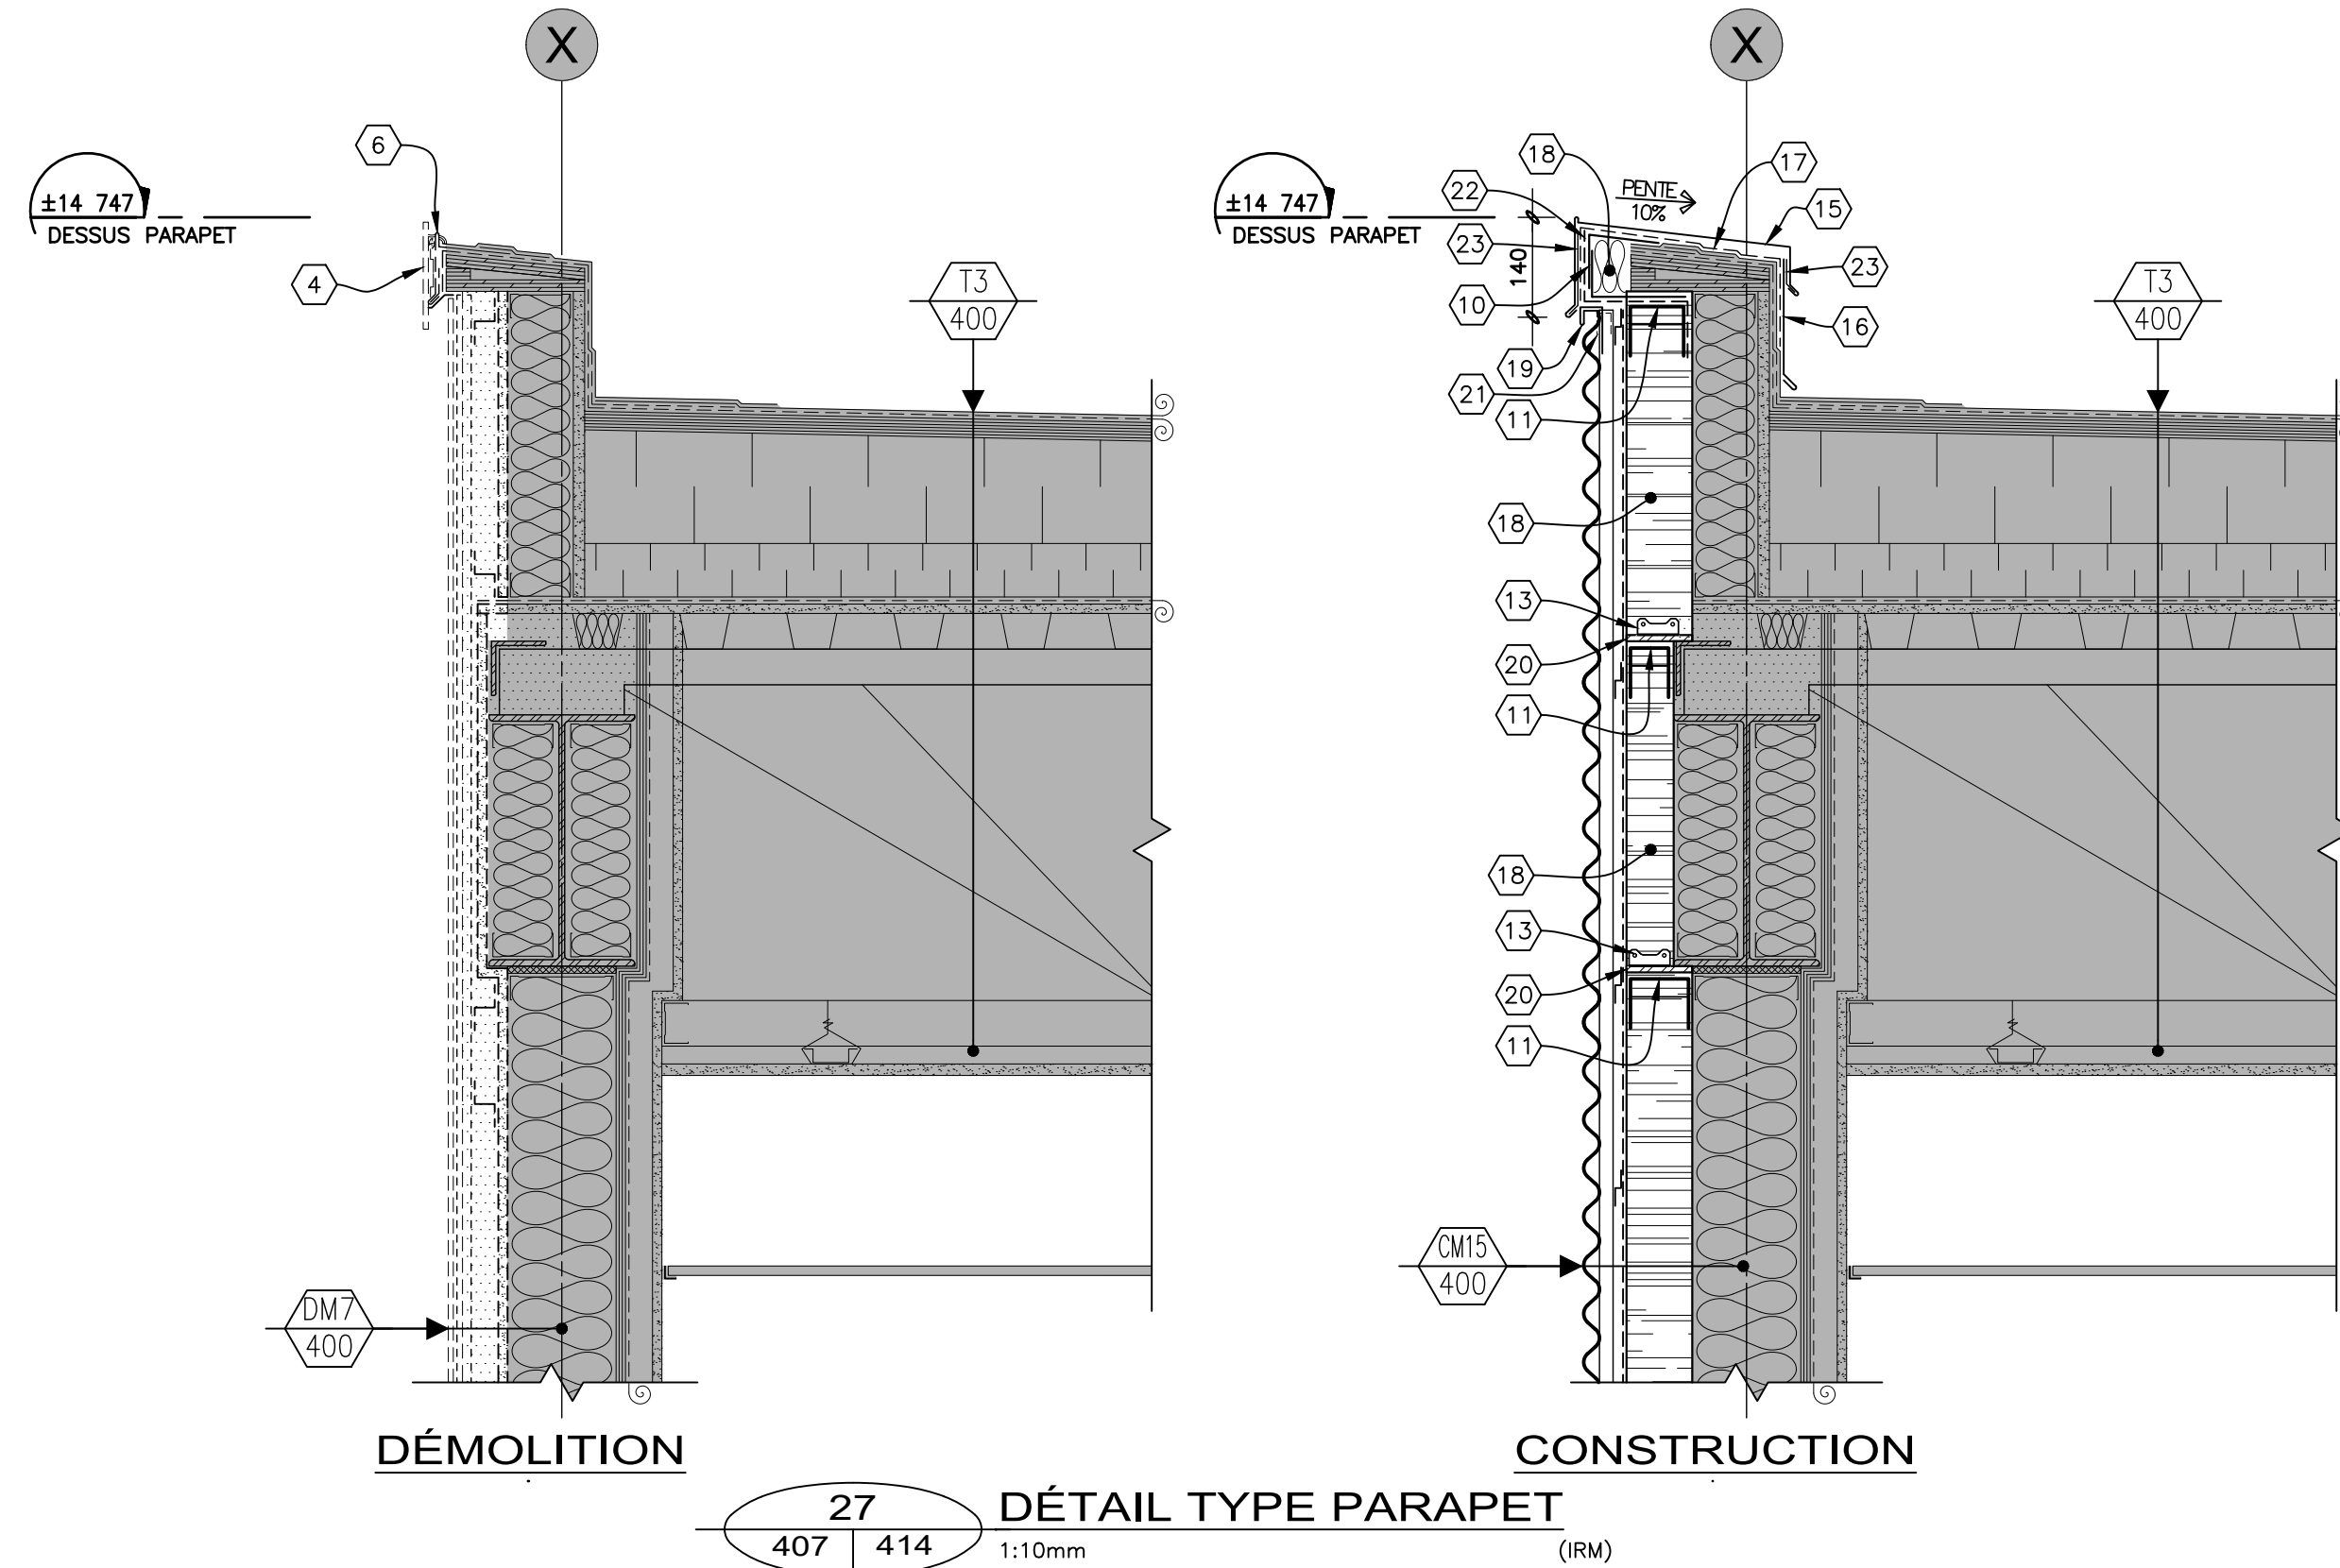

27 DÉTAIL TYPE PARAPET
407 414 1:10mm (IRM)

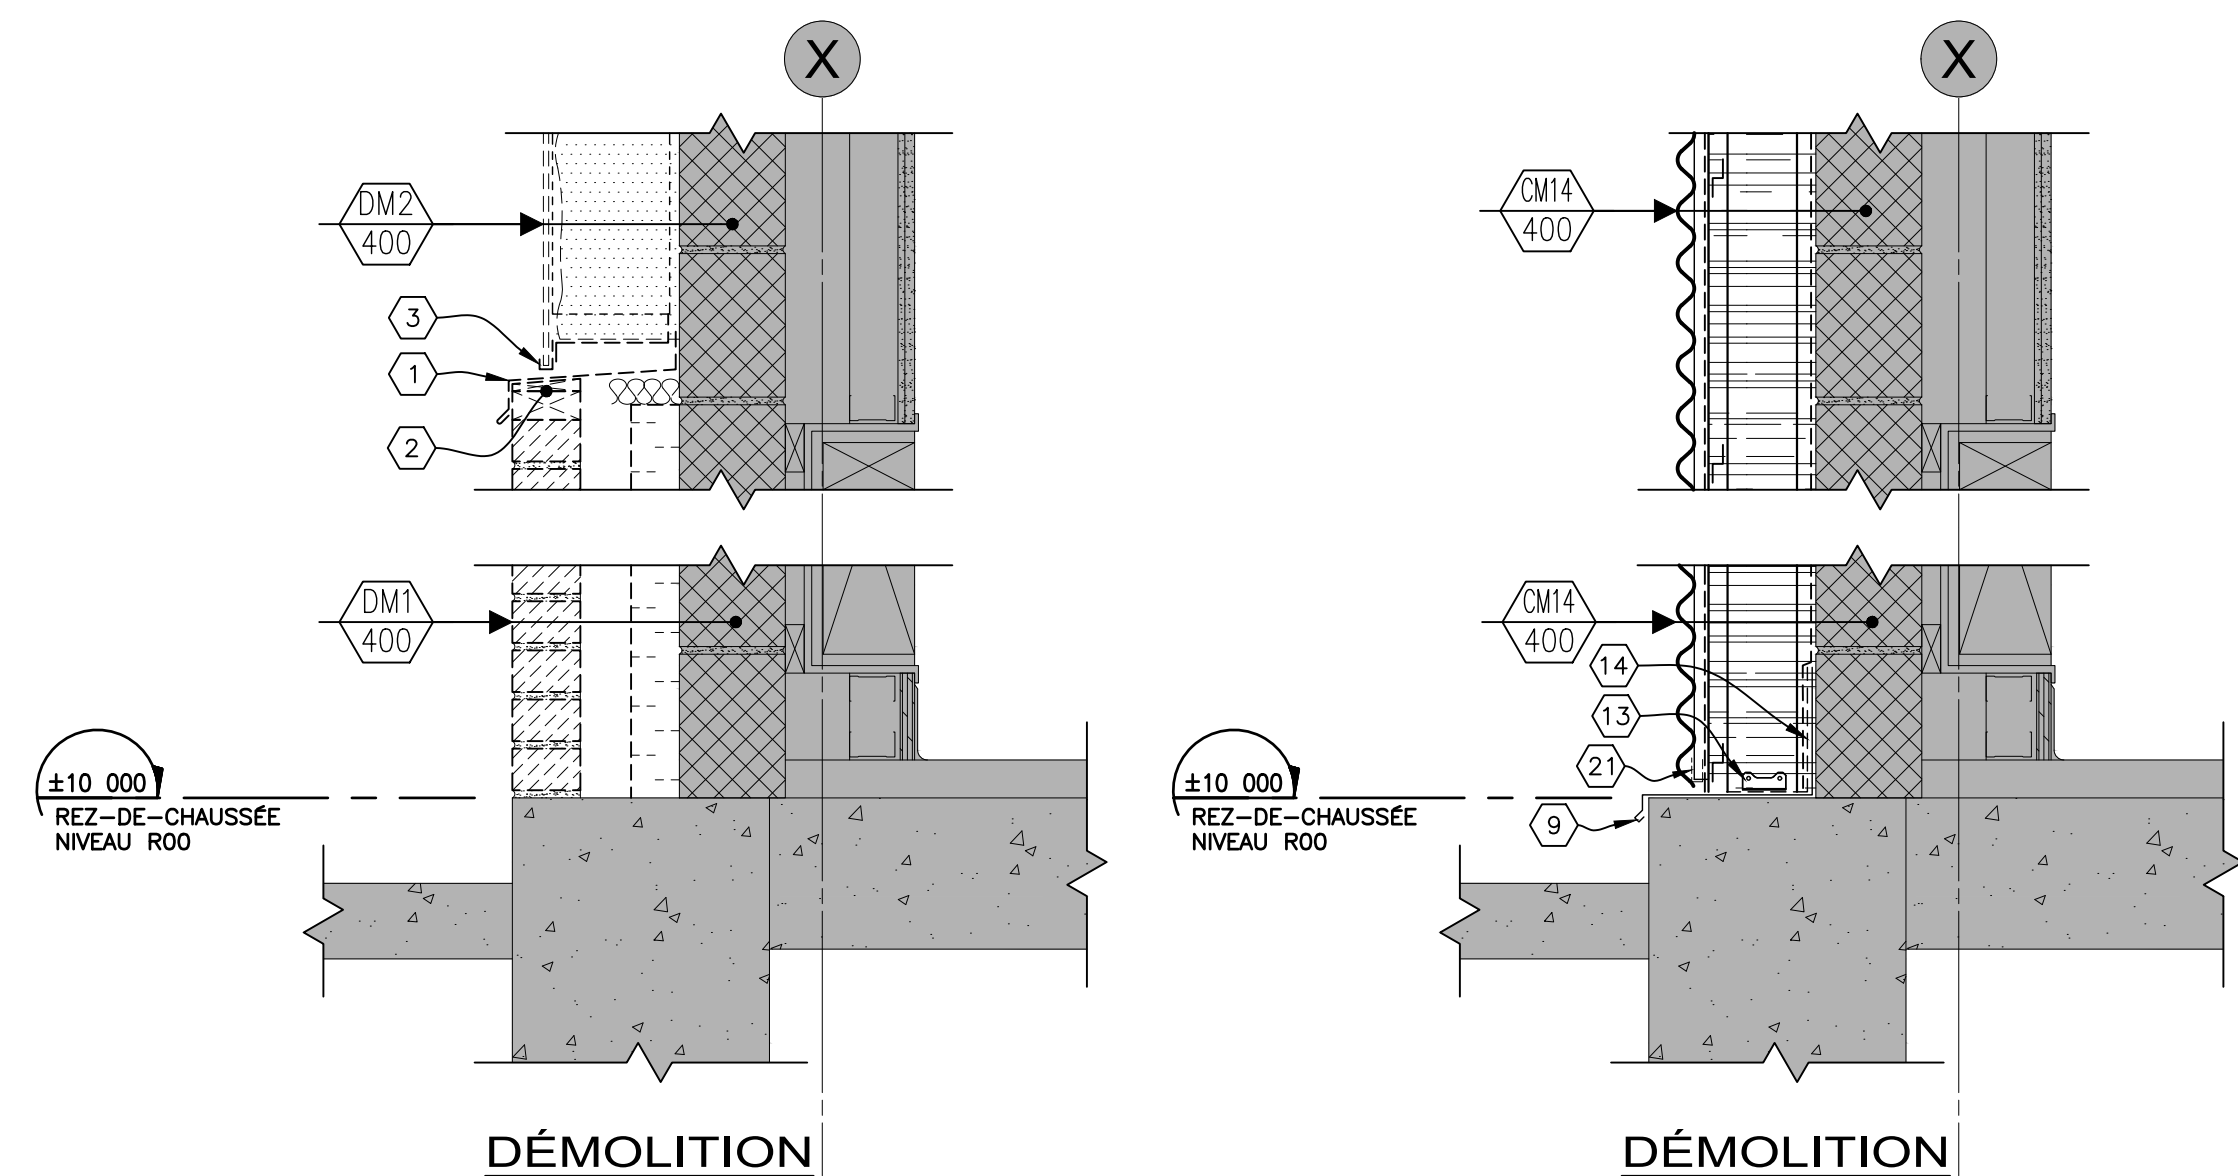

26 DÉTAIL TYPE
406,407 414 1:10mm (ADMINISTRATION)

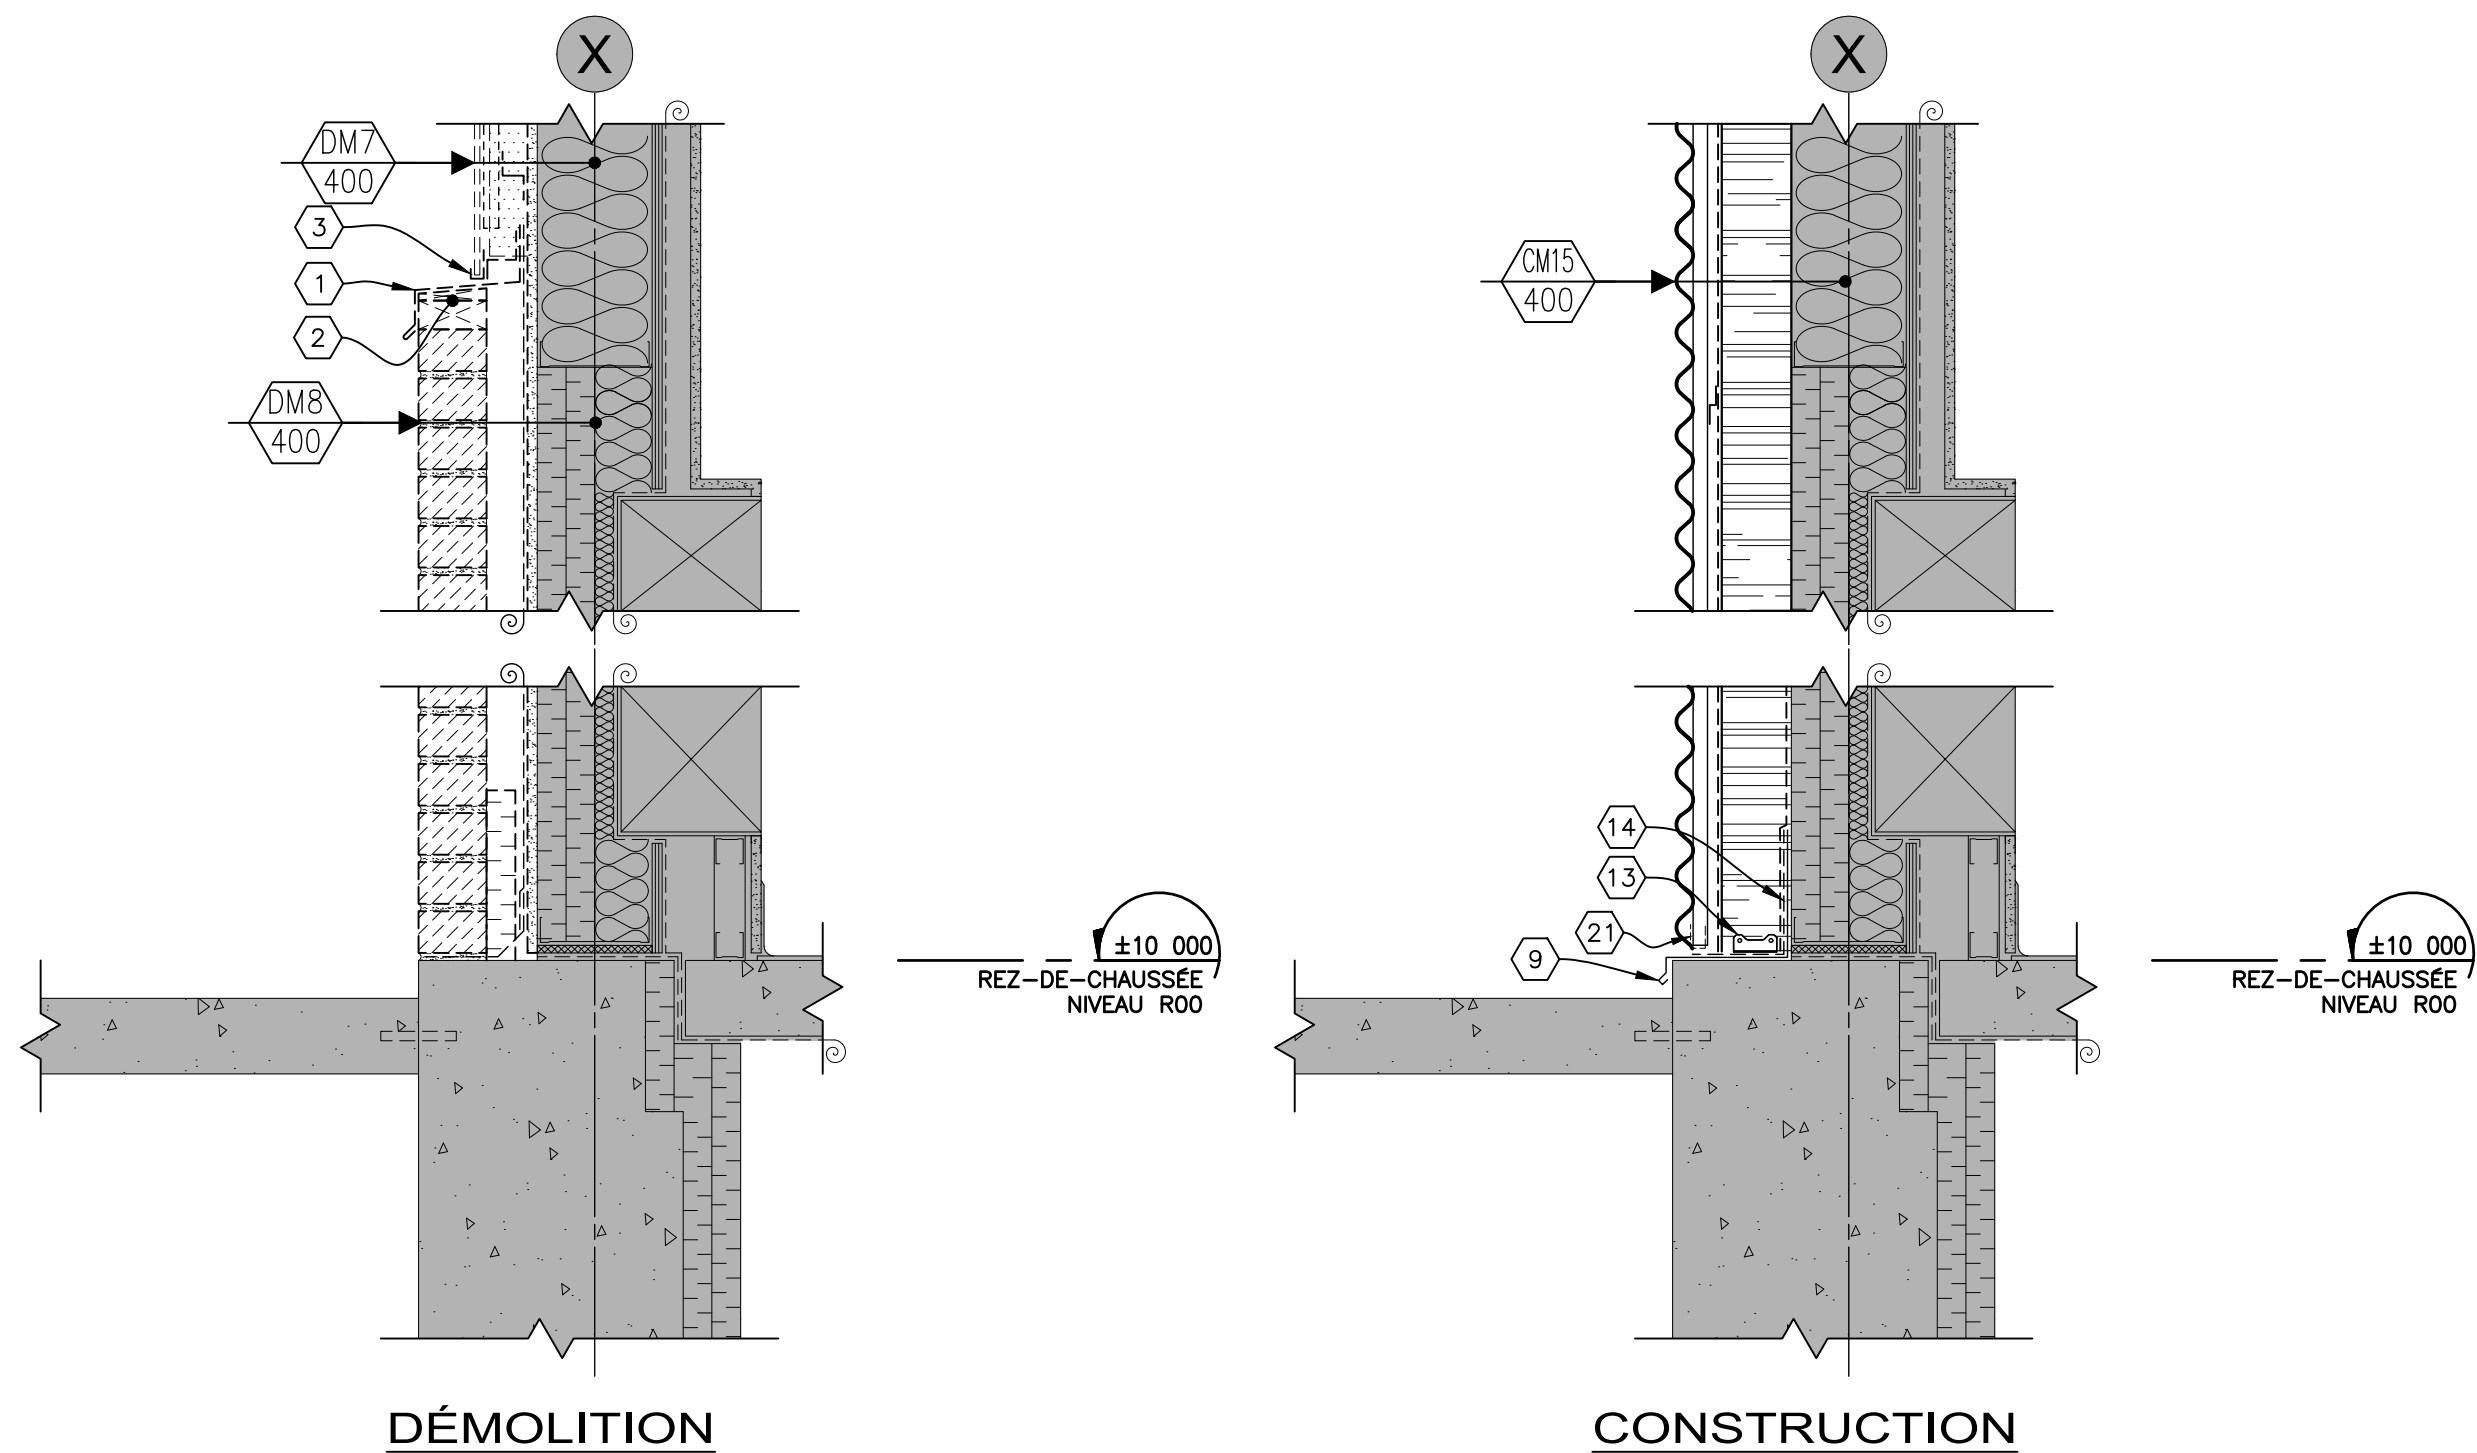

28 DÉTAIL TYPE
407 414 1:10mm (IRM)

NOTES

- SOLIN EXISTANT À DÉMOLIR.
- PIÈCE DE BOIS EXISTANTE À DÉMOLIR.
- MOULURE EN ALUMINIUM À DÉMOLIR.
- PANNEAU DE POLYMERES RENFORCÉ DE FIBRES DE VERRE 7mm D'ÉPAISSEUR À DÉMOLIR.
- TÔLE D'APPUI À DÉMOLIR.
- SOLIN EXISTANT À COUPER ET ENLEVER.
- PLIAGE DE TÔLE EN ACIER GALVANISÉ, CAL.22.
- RIVET EN ACIER INOXYDABLE.
- SOLIN EN ACIER ÉMAILLÉ, CAL. 24.
- DEUX (2) PLIAGES DE TÔLE EN "L", CAL.16 EN ACIER GALVANISÉ.
- LISSE DE DÉFLEXION, VOIR STRUCTURE.
- POUTRE D'ACIER, VOIR STRUCTURE.
- CONNECTEUR À CHAQUE COLOMBAGES OU BARRE "Z" SELON LE CAS, VOIR STRUCTURE.
- SOLIN MEMBRANÉ AUTOCOLLANT.
- SOLIN EN ACIER ÉMAILLÉ, CAL.24, JOINTS AGRAFÉS.
- CONTRE-SOLIN EN ACIER ÉMAILLÉ, CAL.24.
- MEMBRANE SOUS-COUCHE.
- REMPLEIR L'ESPACE DE LAINE DE FIBRE DE ROCHE.
- MOULURE EN "J" EN ACIER ÉMAILLÉ, CAL.24.
- PLAQUE D'ACIER CONTINUE, VOIR STRUCTURE.
- MOUSTIQUAIRE.
- MEMBRANE AUTOCOLLANT.
- AGRAFE EN ACIER GALVANISÉ, CAL.24 CONTINUE.
- PLAQUE D'ACIER PONCTUELLE, VOIR STRUCTURE.
- SCELLER LA MEMBRANE PARE-INTÉMPIERES SUR LE SOLIN AVEC UN RUBAN AUTOCOLLANT.
- TÔLE D'APPUI EN ACIER GALVANISÉ CAL.18 PENTE 6%.
- PLIAGE EN "J" EN ACIER GALVANISÉ CAL.18.
- SCELLER LA MEMBRANE AUTOCOLLANTE SUR LE PARE-INTÉMPIERES.
- ÉTRIER, VOIR STRUCTURE.
- BARRE "Z" CAL.16 VERTICAL Ø400mm c/c.
- BOUT DU PANNEAU REPLIÉ VERS L'INTÉRIEUR.

LÉGENDE

- EXISTANT À CONSERVER.
- ÉLÉMENT À DÉMOLIR.
- AXE EXISTANT
- EXTÉRIEUR DE LA STRUCTURE DE BÉTON EXISTANTE DE LA TOUR.
- NOUVEL AXE: FACE EXTÉRIEURE DES BARRES Z ET COLOMBAGES DE LA TOUR. VOIR STRUCTURE.
- (*) VOIR NOTE GÉNÉRAL PAGE 400.

NE DOIT PAS SERVIR À L'EXÉCUTION

Le présent document est émis pour la seule fin identifiée. Son contenu est protégé par les droits d'auteur et toute reproduction ou modification, partielle ou totale, est interdite sans l'autorisation écrite de gagnon, letellier, cyr, ricard, mathieu, proulx, savard consortium d'architectes.




GLCRM | Proulx Savard |

GLCRM:
128, Avenue de la Cathédrale,
Bureau 201
Rimouski, QC, G5L 5H7
(418) 722-7655


2406, Ch. des Quatres-Bourgeois,
Bureau 100
Québec, QC, G1V 1W5
(418) 647-1700

Proulx Savard Architectes:
75, boul. Arthur-Buies Ouest,
Rimouski QC G5L 5C2
(418) 723-5543

ARCHITECTURE

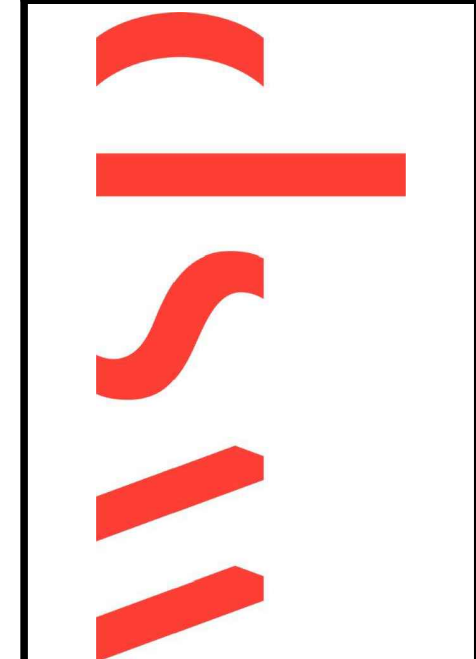

CONSULTANTS

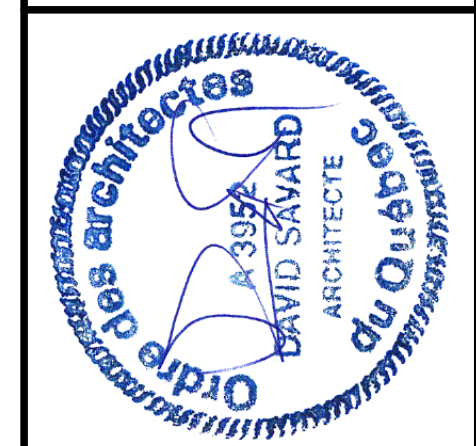

DESSINATEUR (S)	DOSSIER No.	DATE	REVISIONS
D.B. ALL	24-1087 / 1687-24	SEPTEMBRE 2024	
INDIQUÉE			
05	2024-09-04	DÉFINITIVES POUR SOUMISSION	
06	2024-08-21	DÉFINITIVES 100% POUR APPROBATION	
03	2024-08-03	DÉFINITIVES 80% POUR APPROBATION	
02	2024-05-14	DÉFINITIVES 40% POUR APPROBATION	
01	2024-02-27	PRÉLIMINAIRES 20% POUR APPROBATION	
No	DATE		

PROJET

HÔPITAL DE CHANDLER,


Chandler

(Réfection de l'enveloppe)


PROPRIÉTAIRE

Santé Québec


414

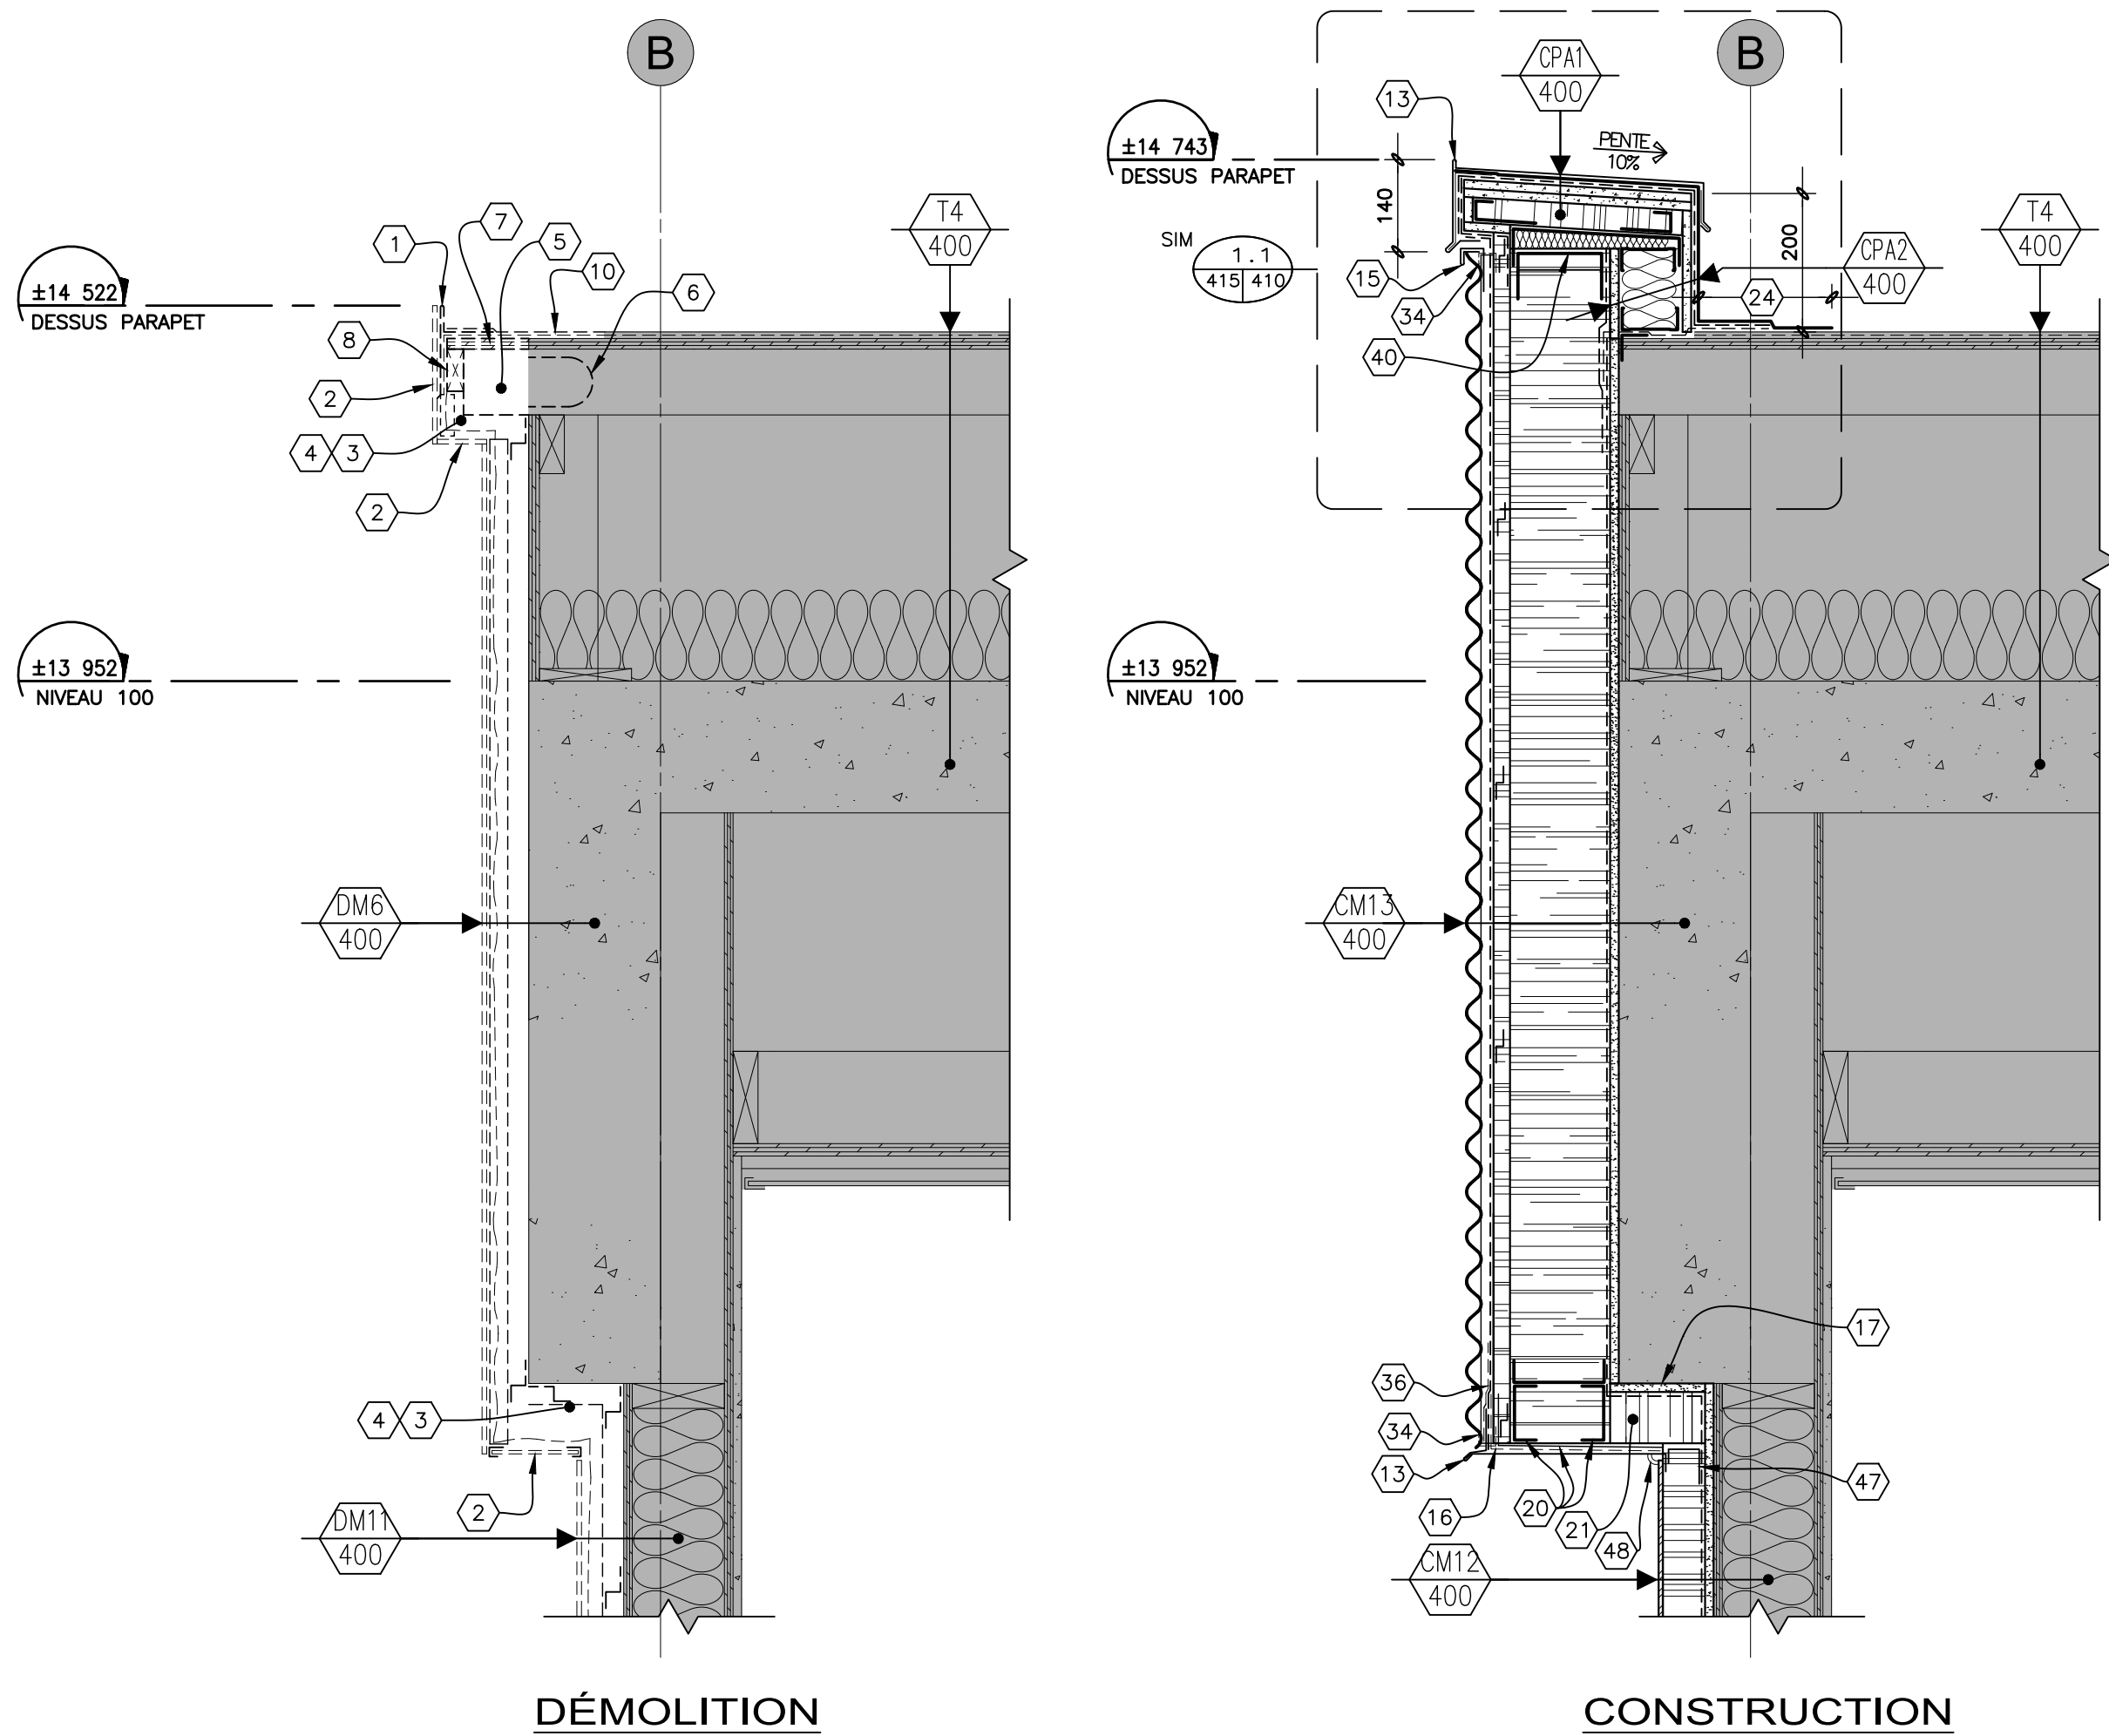

29 DÉTAIL TYPE PARAPET
407 415 1:10mm (GARAGE AMBULANCE)

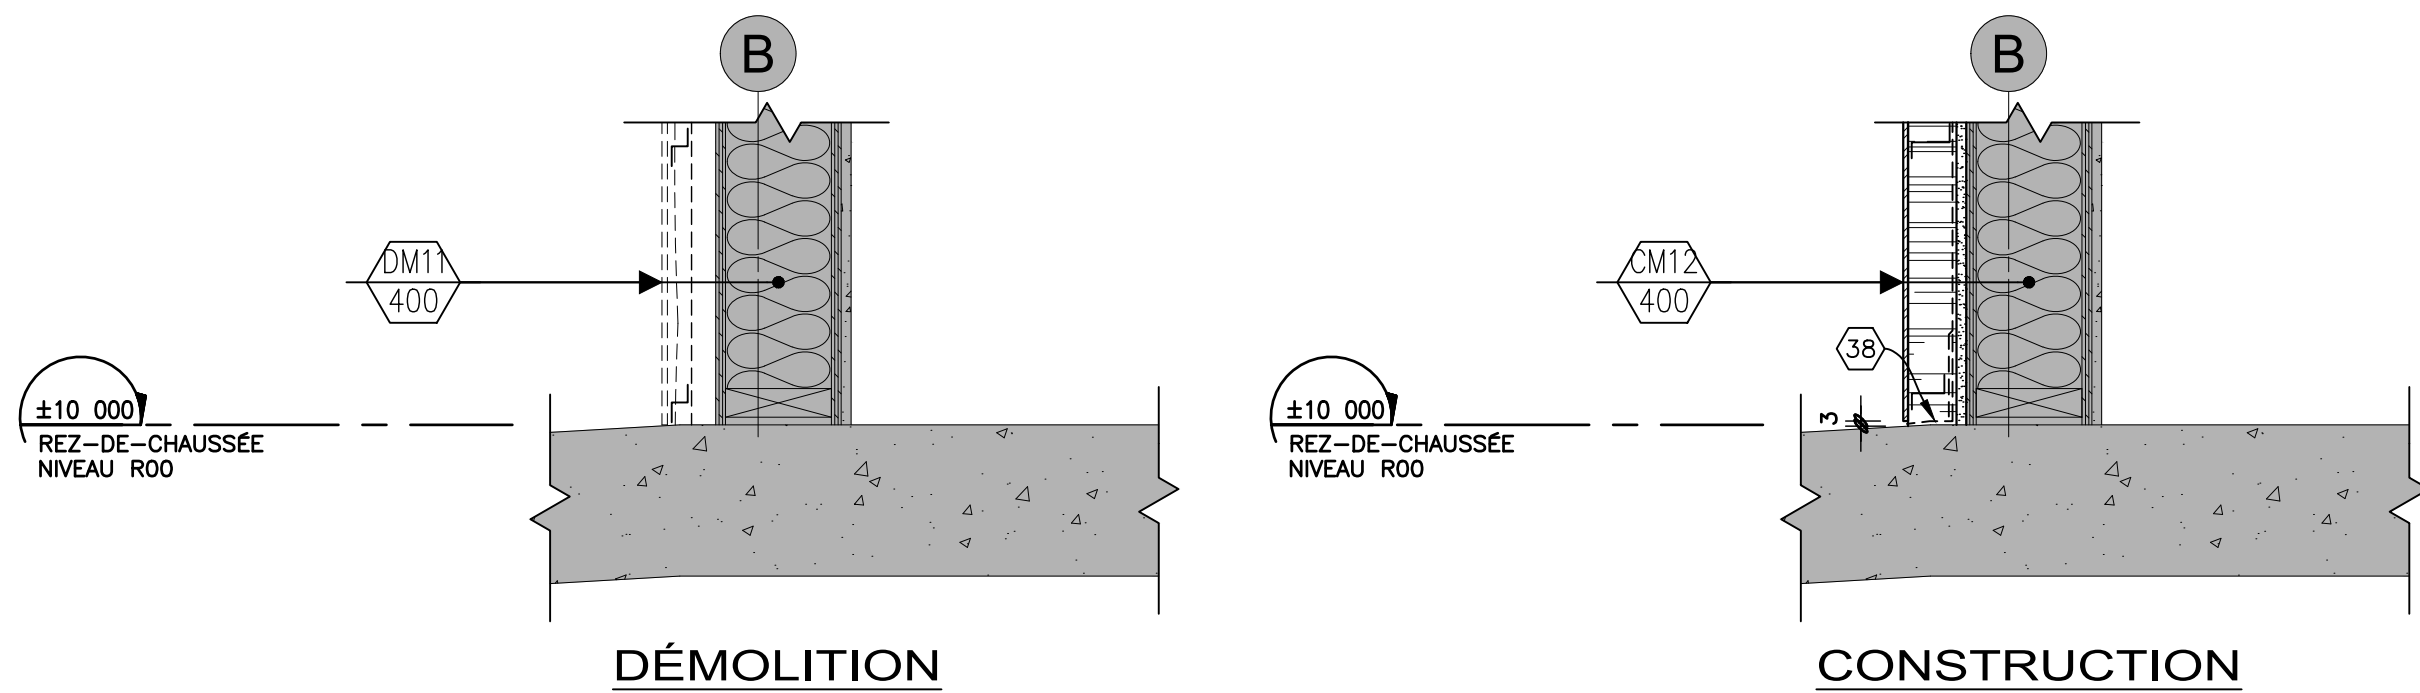


30 DÉTAIL TYPE
407 415 1:10mm (GARAGE AMBULANCE)

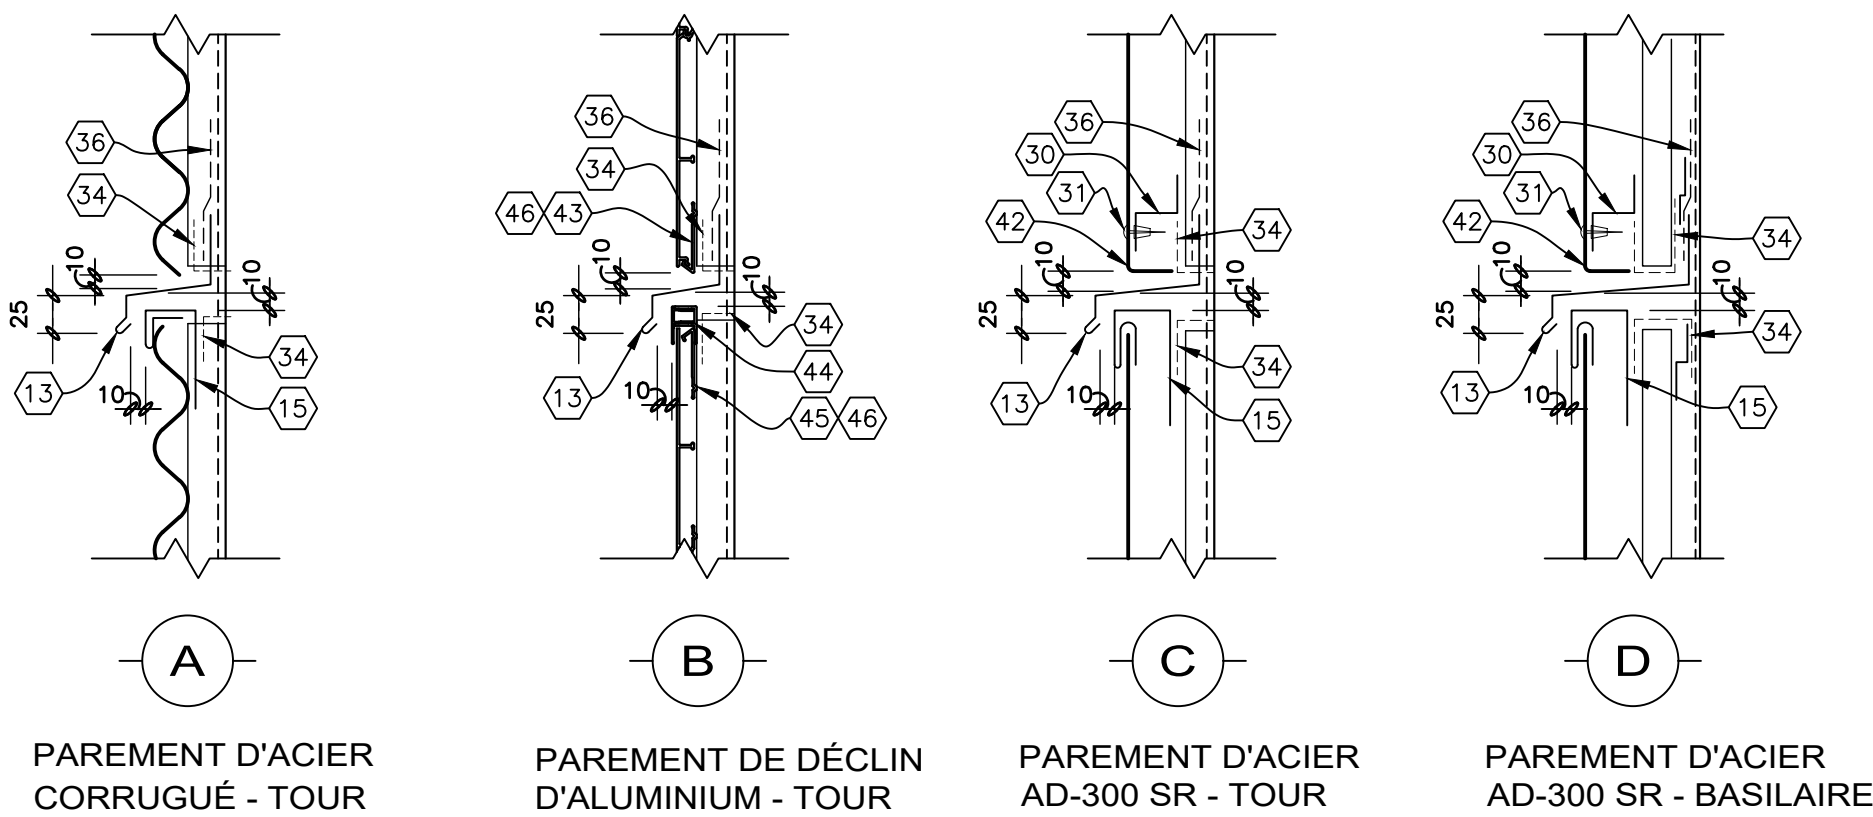


DÉTAILS TYPES DE COMPARTIMENTATION
1:5mm


NOTE - DÉTAILS DE COMPARTIMENTATION
- VOIR LES ÉLEVATIONS PAGES 203 ET 204 POUR LA LOCALISATION DES DÉTAILS DE COMPARTIMENTATION

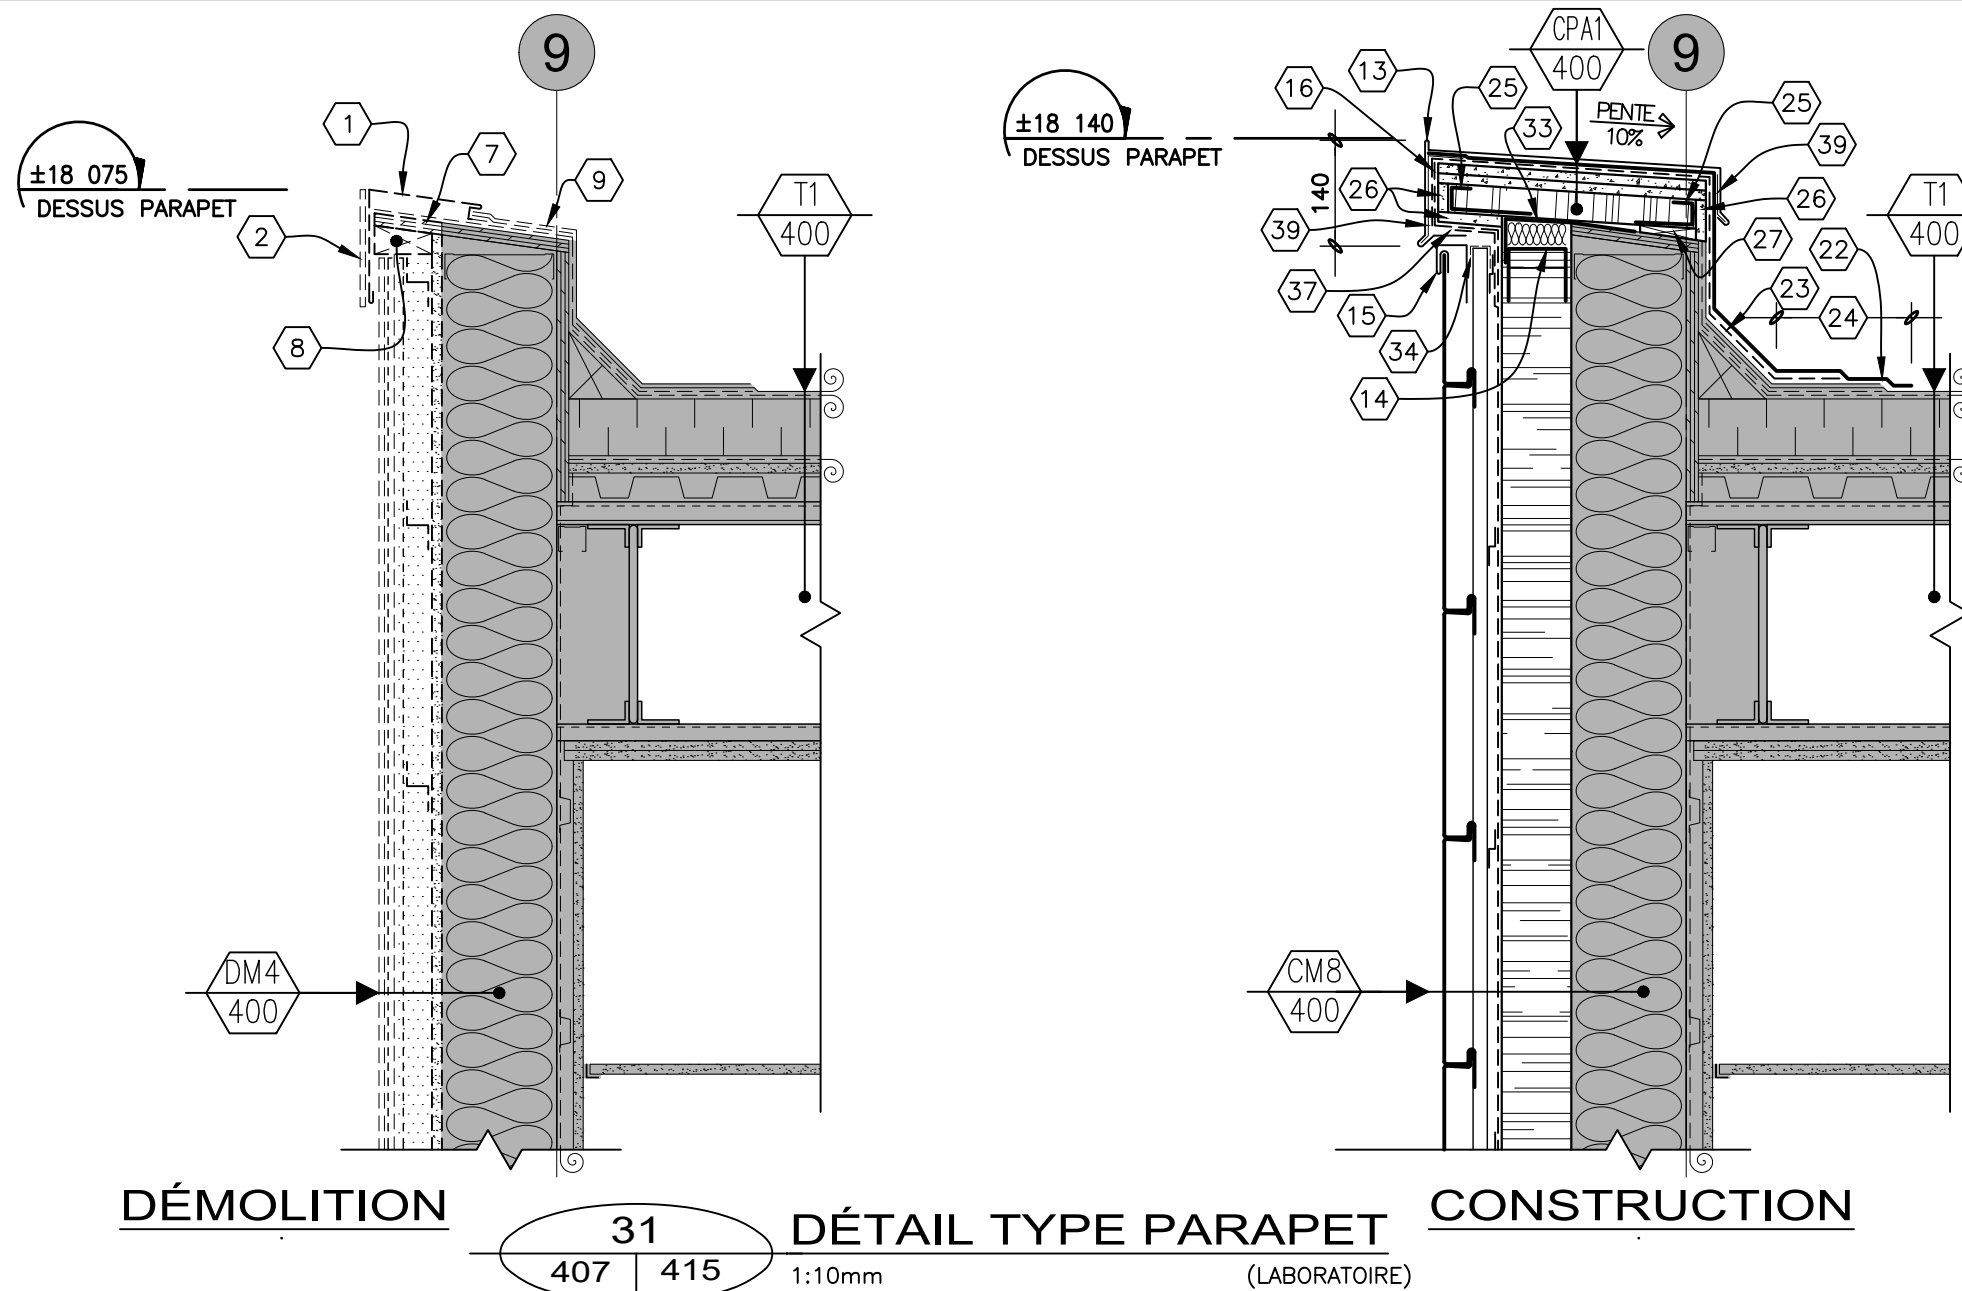

31 DÉTAIL TYPE PARAPET
407 415 1:10mm (LABORATOIRE)

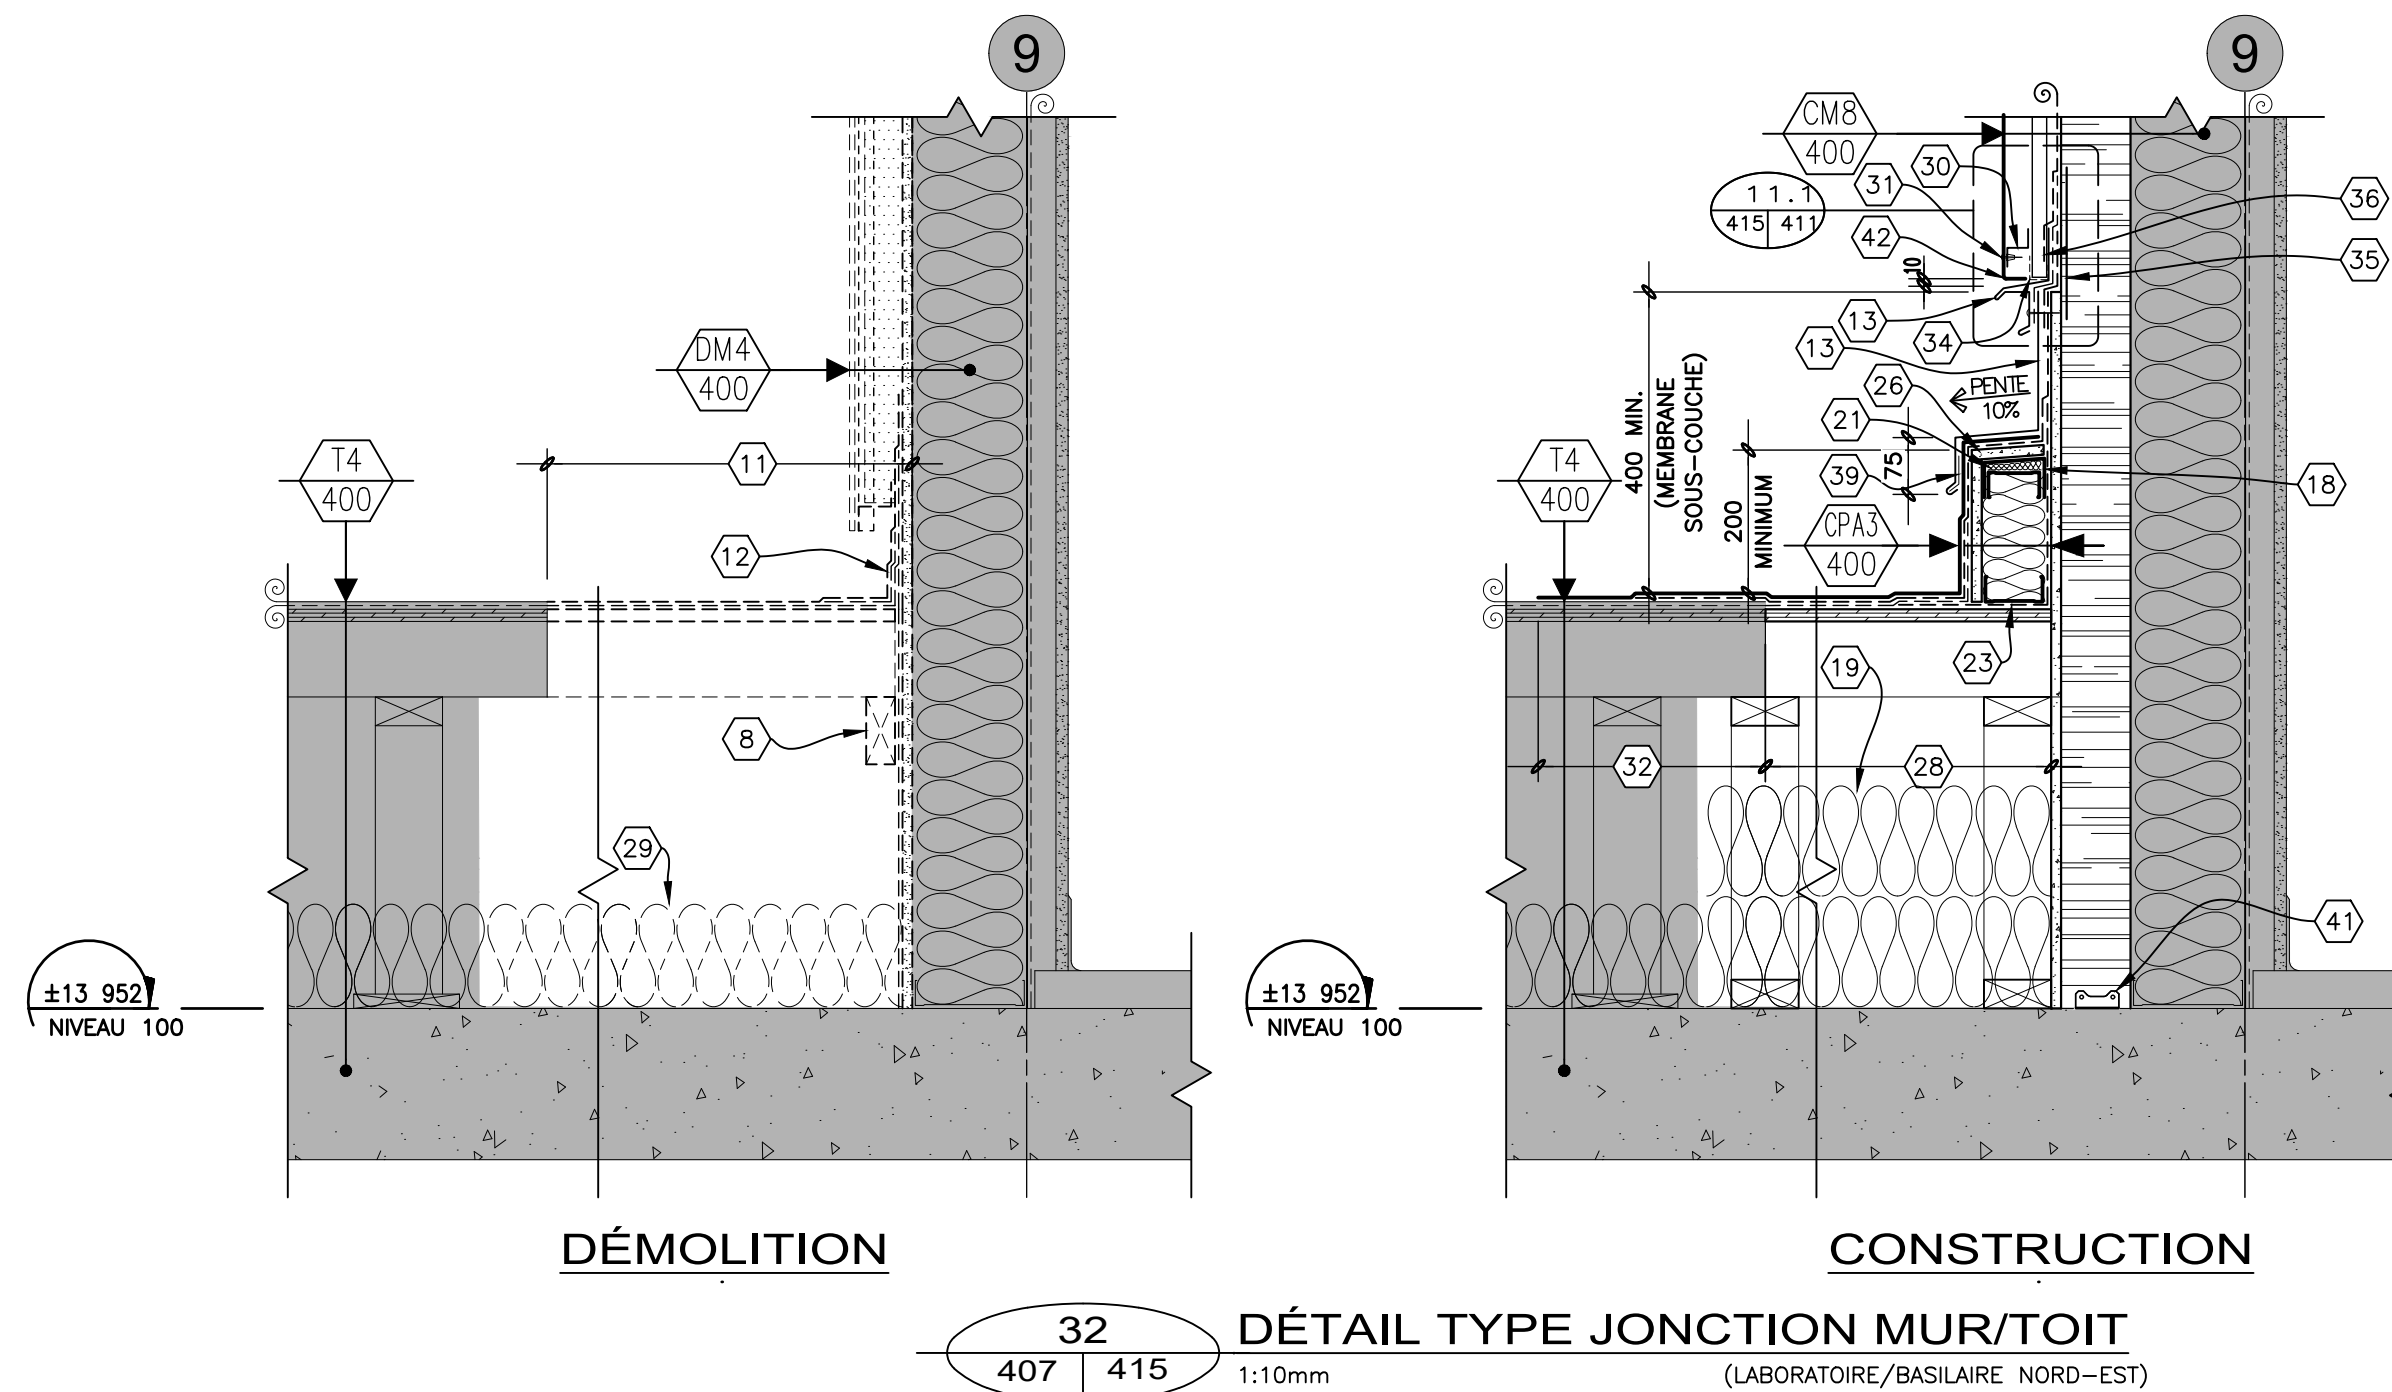

32 DÉTAIL TYPE JONCTION MUR/TOIT
407 415 1:10mm (LABORATOIRE/BASILAIRE NORD-EST)

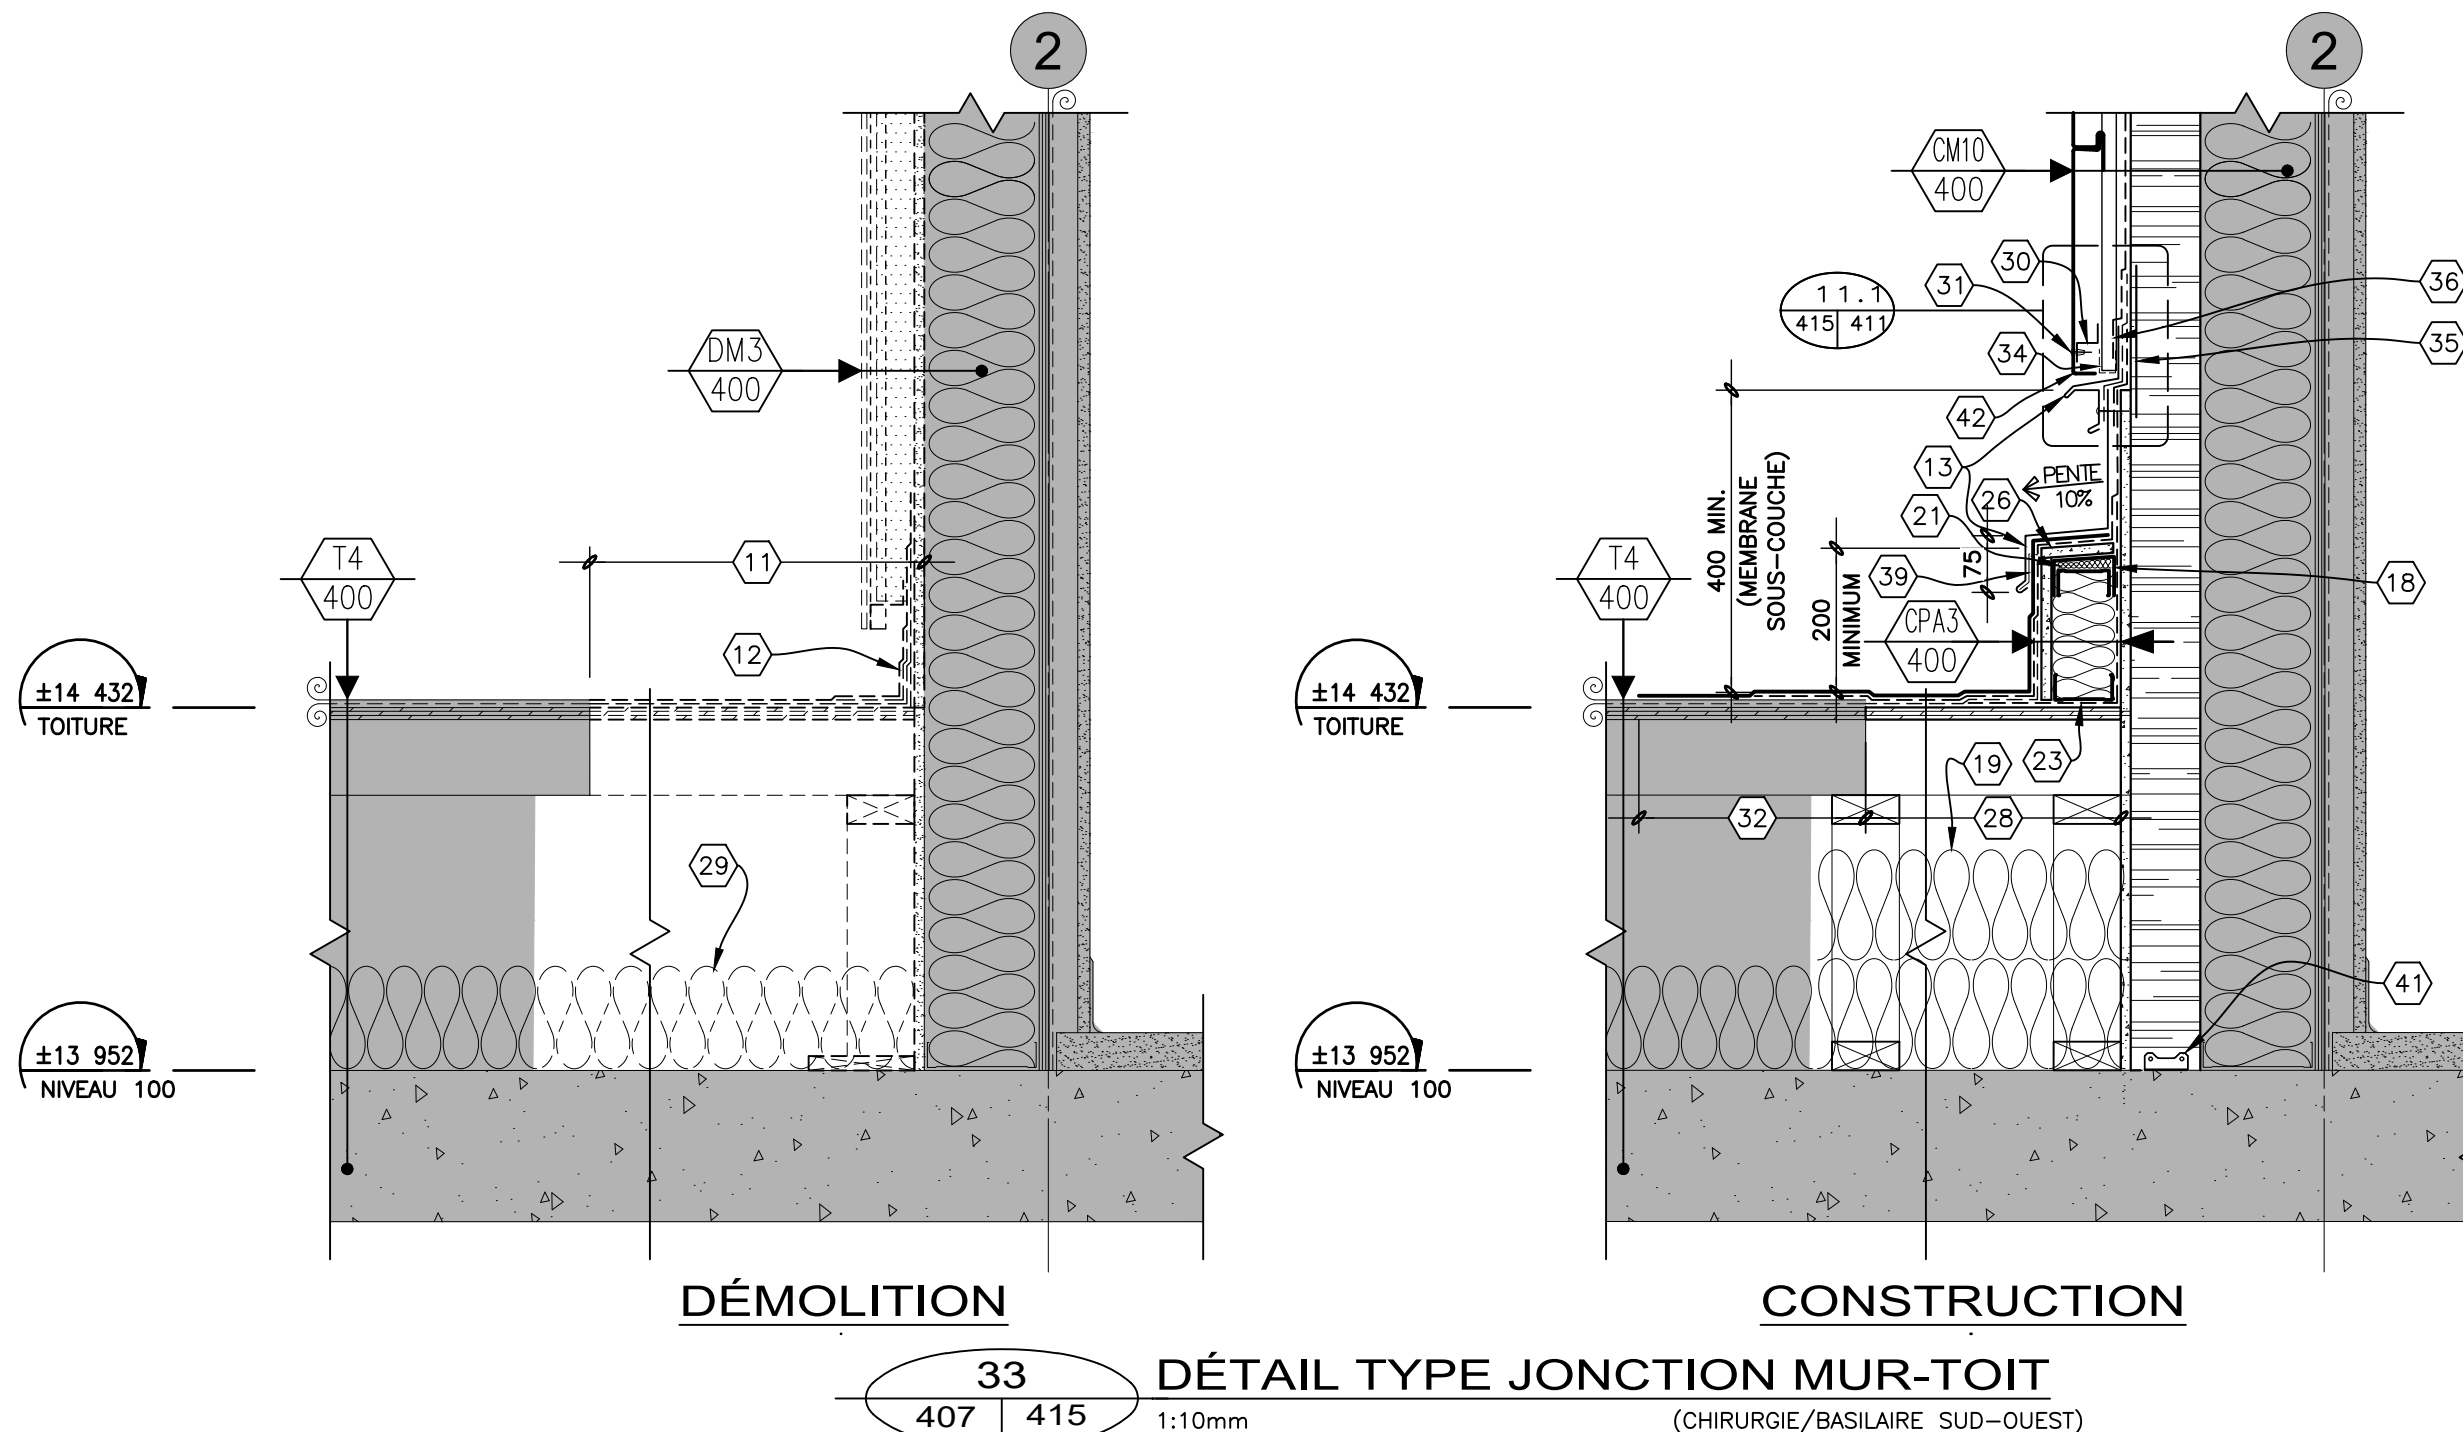

33 DÉTAIL TYPE JONCTION MUR-TOIT
407 415 1:10mm (CHIRURGIE/BASILAIRE SUD-OUEST)

NOTES

- SOLIN EXISTANT À DÉMOLIR.
- PANNEAU DE POLYMERES RENFORCE DE FIBRES DE VERRE 7mm D'ÉPAISSEUR À DÉMOLIR.
- BARRES "Z" EXISTANTES À DÉMOLIR.
- ISOLANT DE POLYURÉTHANE EXISTANT À DÉMOLIR.
- MEMBRURE EXISTANTE DE 38mmX89mm À COUPER, VOIR STRUCTURE.
- FILTRE MÉDIA EXISTANT À ENLEVER.
- CONTREPLAQUÉ À PLUS EXISTANT À COUPER.
- PIECE DE BOIS EXISTANTE À DÉMOLIR.
- MEMBRANES EXISTANTES À DÉMOLIR SUR LE DESSUS DU PARAPET.
- MEMBRANE DE BITUME MODIFIÉE BI-COUCHE À DÉMOLIR SUR LA LARGEUR REQUISE POUR LA CONSTRUCTION DU NOUVEAU PARAPET.
- OUVERTURE À FAIRE DANS LA TOITURE EXISTANTE SUR ±500mm POUR LA CONSTRUCTION DU NOUVEAU MUR. VOIR COMPOSITION DE TOIT SUR LE DÉTAIL. VOIR PLAN DE STRUCTURE POUR LES MODIFICATIONS À LA STRUCTURE DE LA TOITURE VENTILÉE.
- MEMBRANE DE BITUME MODIFIÉE BI-COUCHE À DÉMOLIR.
- SOLIN EN ACIER ÉMAILLÉ, CAL.24 (JOINTS AGRAFES).
- LISSE DE DÉFLEXION, VOIR STRUCTURE.
- MOULURE EN "J" EN ACIER ÉMAILLÉ, CAL.24.
- MEMBRANE AUTOCOLLANTE.
- PANNEAU DE MÂT DE FIBRE DE VERRE 13mm.
- PLIAGE DE TOLE EN "U", CAL.16 EN ACIER GALVANISÉ.
- NOUVEL ISOLANT EN LAINE DE FIBRE DE VERRE, DEUX RANGS DE 150mm SUR 610mm DE LARGEUR.
- TOLE D'APPUI EN ACIER GALVANISÉ, CAL.18.
- REMPLEUR L'ESPACE DE LAINE DE FIBRE DE ROCHE.
- MEMBRANE DE FINITION GRANULÉE.
- MEMBRANE SOUS-COUCHE.
- CHEVAUCHER LA NOUVELLE MEMBRANE SUR LES MEMBRANES DE LA TOITURE EXISTANTE SUR MINIMUM 150mm, DÉGRANULER LA MEMBRANE EXISTANTE AU PRÉALABLE.
- PLIAGE DE TOLE EN "J", CAL.18 EN ACIER GALVANISÉ.
- PANNEAU DE CIMENT 13mm.
- CALE D'AJUSTEMENT EN ACIER GALVANISÉ D'ÉPAISSEUR REQUISE.
- RAGRÉER LA TOITURE TEL QUE L'EXISTANT. VOIR COMPOSITION DE TOIT SUR LE DÉTAIL. VOIR PLAN DE STRUCTURE POUR LES MODIFICATIONS À LA STRUCTURE DE LA TOITURE VENTILÉE.
- ENLEVER L'ISOLANT DE LAINE DE FIBRE DE VERRE SUR 610mm POUR LA RÉALISATION DES TRAVAUX.
- PLIAGE DE TOLE EN ACIER GALVANISÉ, CAL.22.
- RIVET EN ACIER INOXYDABLE.
- CHEVAUCHER LA NOUVELLE MEMBRANE SUR LES MEMBRANES DE LA TOITURE EXISTANTE SUR MINIMUM 300mm, DÉGRANULER LA MEMBRANE EXISTANTE AU PRÉALABLE.
- PLIAGE DE TOLE, CAL.16 EN ACIER GALVANISÉ, FIXÉ SUR LE DESSUS DU PARAPET EXISTANT.
- MOUSTIQUAIRE.
- TOLE D'APPUI EN ACIER GALVANISÉ, CAL.18. 200mm DE HAUTEUR.
- SCELLER LA MEMBRANE PARE-INTÉMPIERIES SUR LE SOLIN AVEC UN RUBAN AUTOCOLLANT.
- SCELLER LA MEMBRANE PARE-INTÉMPIERIES SUR LE PARAPET AVEC UN RUBAN AUTOCOLLANT.
- SOLIN MEMBRANE AUTOCOLLANT.
- AGRAFE EN ACIER GALVANISÉ, CAL.24 CONTINUE.
- LISSE DE DÉFLEXION.
- CONNECTEUR À CHAQUE COLOMBAGES OU BARRE "Z" SELON LE CAS, VOIR STRUCTURE.
- BOUT DU PANNEAU REPLIÉ VERS L'INTÉRIEUR.
- MOULURE DE DÉPART PAR LE MANUFACTURIER DU PAREMENT DE DÉCLIN D'ALUMINIUM.
- MOULURE EN "J" PAR LE MANUFACTURIER DU PAREMENT DE DÉCLIN D'ALUMINIUM.
- SECTION DE MOULURE DE DÉPART POUR APPUI DU PAREMENT DE DÉCLIN D'ALUMINIUM, PAR LE MANUFACTURIER DU PAREMENT DE DÉCLIN D'ALUMINIUM.
- SÉPARATEUR DIÉLECTRIQUE.
- PLIAGE EN "U" EN ACIER GALVANISÉ CAL.16.
- SCELLANT CONTINU.

LÉGENDE

- EXISTANT À CONSERVER.
- ÉLÉMENT À DÉMOLIR.
- AXE EXISTANT
- EX EXTÉRIEUR DE LA STRUCTURE DE BÉTON EXISTANTE DE LA TOUR.
- NS NOUVEL AXE: FACE EXTERIEURE DES BARRES Z ET COLOMBAGES DE LA TOUR. VOIR STRUCTURE.
- (*) VOIR NOTE GÉNÉRAL PAGE 400.

NE DOIT PAS SERVIR À L'EXÉCUTION

Le présent document est émis par la seule fin identifiée. Son contenu est protégé par les droits d'auteur et toute reproduction ou modification, partielle ou totale, est interdite sans l'autorisation écrite de gagnon, letellier, cyr, ricard, mathieu, proulx, savard consortium d'architectes.




GLCRM | Proulx Savard |

GLCRM:
128, Avenue de la Cathédrale,
Bureau 201
Rimouski, QC, G5L 5H7
(418) 722-7655



2406, Ch. des Quatres-Bourgeois,
Bureau 100
Québec, QC, G1V 1W5
(418) 647-1700

Proulx Savard Architectes:
75, boul. Arthur-Buies Ouest,
Rimouski QC G5L 5C2
(418) 722-5543


ARCHITECTURE

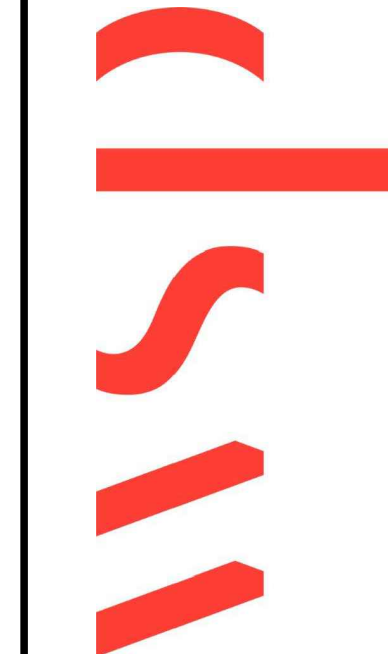

CONSULTANTS

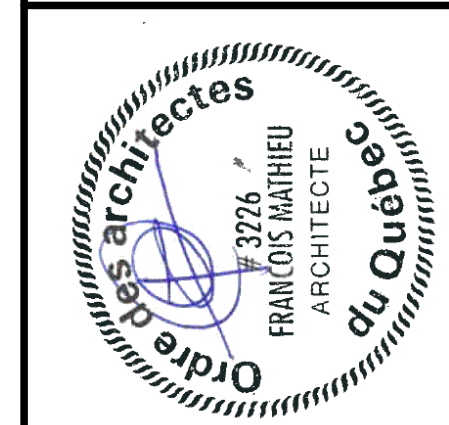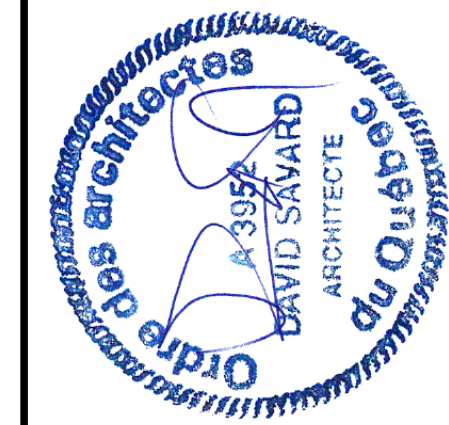


DESSIN	DESIGNATEUR (S)	DOSSIER No.	DATE	DATE	RÉVISIONS
COUPE DE MUR TYPE DÉMOLITION ET CONSTRUCTION	DB AL ÉCHELLE INDIQUÉE	24-187 / 687-24	SEPTEMBRE 2024		
PROJET HÔPITAL DE CHANDLER, Chandler (Réfection de l'enveloppe)	PROPRIÉTAIRE Santé Québec	05	2024-09-04	DÉFINITIVES 100% POUR APPROBATION	No
PROPRIÉTAIRE Santé Québec	06	2024-08-21	DÉFINITIVES 80% POUR APPROBATION	No	No
PROPRIÉTAIRE Santé Québec	07	2024-05-14	DÉFINITIVES 40% POUR APPROBATION	No	No
PROPRIÉTAIRE Santé Québec	08	2024-02-27	PRÉLIMINAIRES 20% POUR APPROBATION	No	No

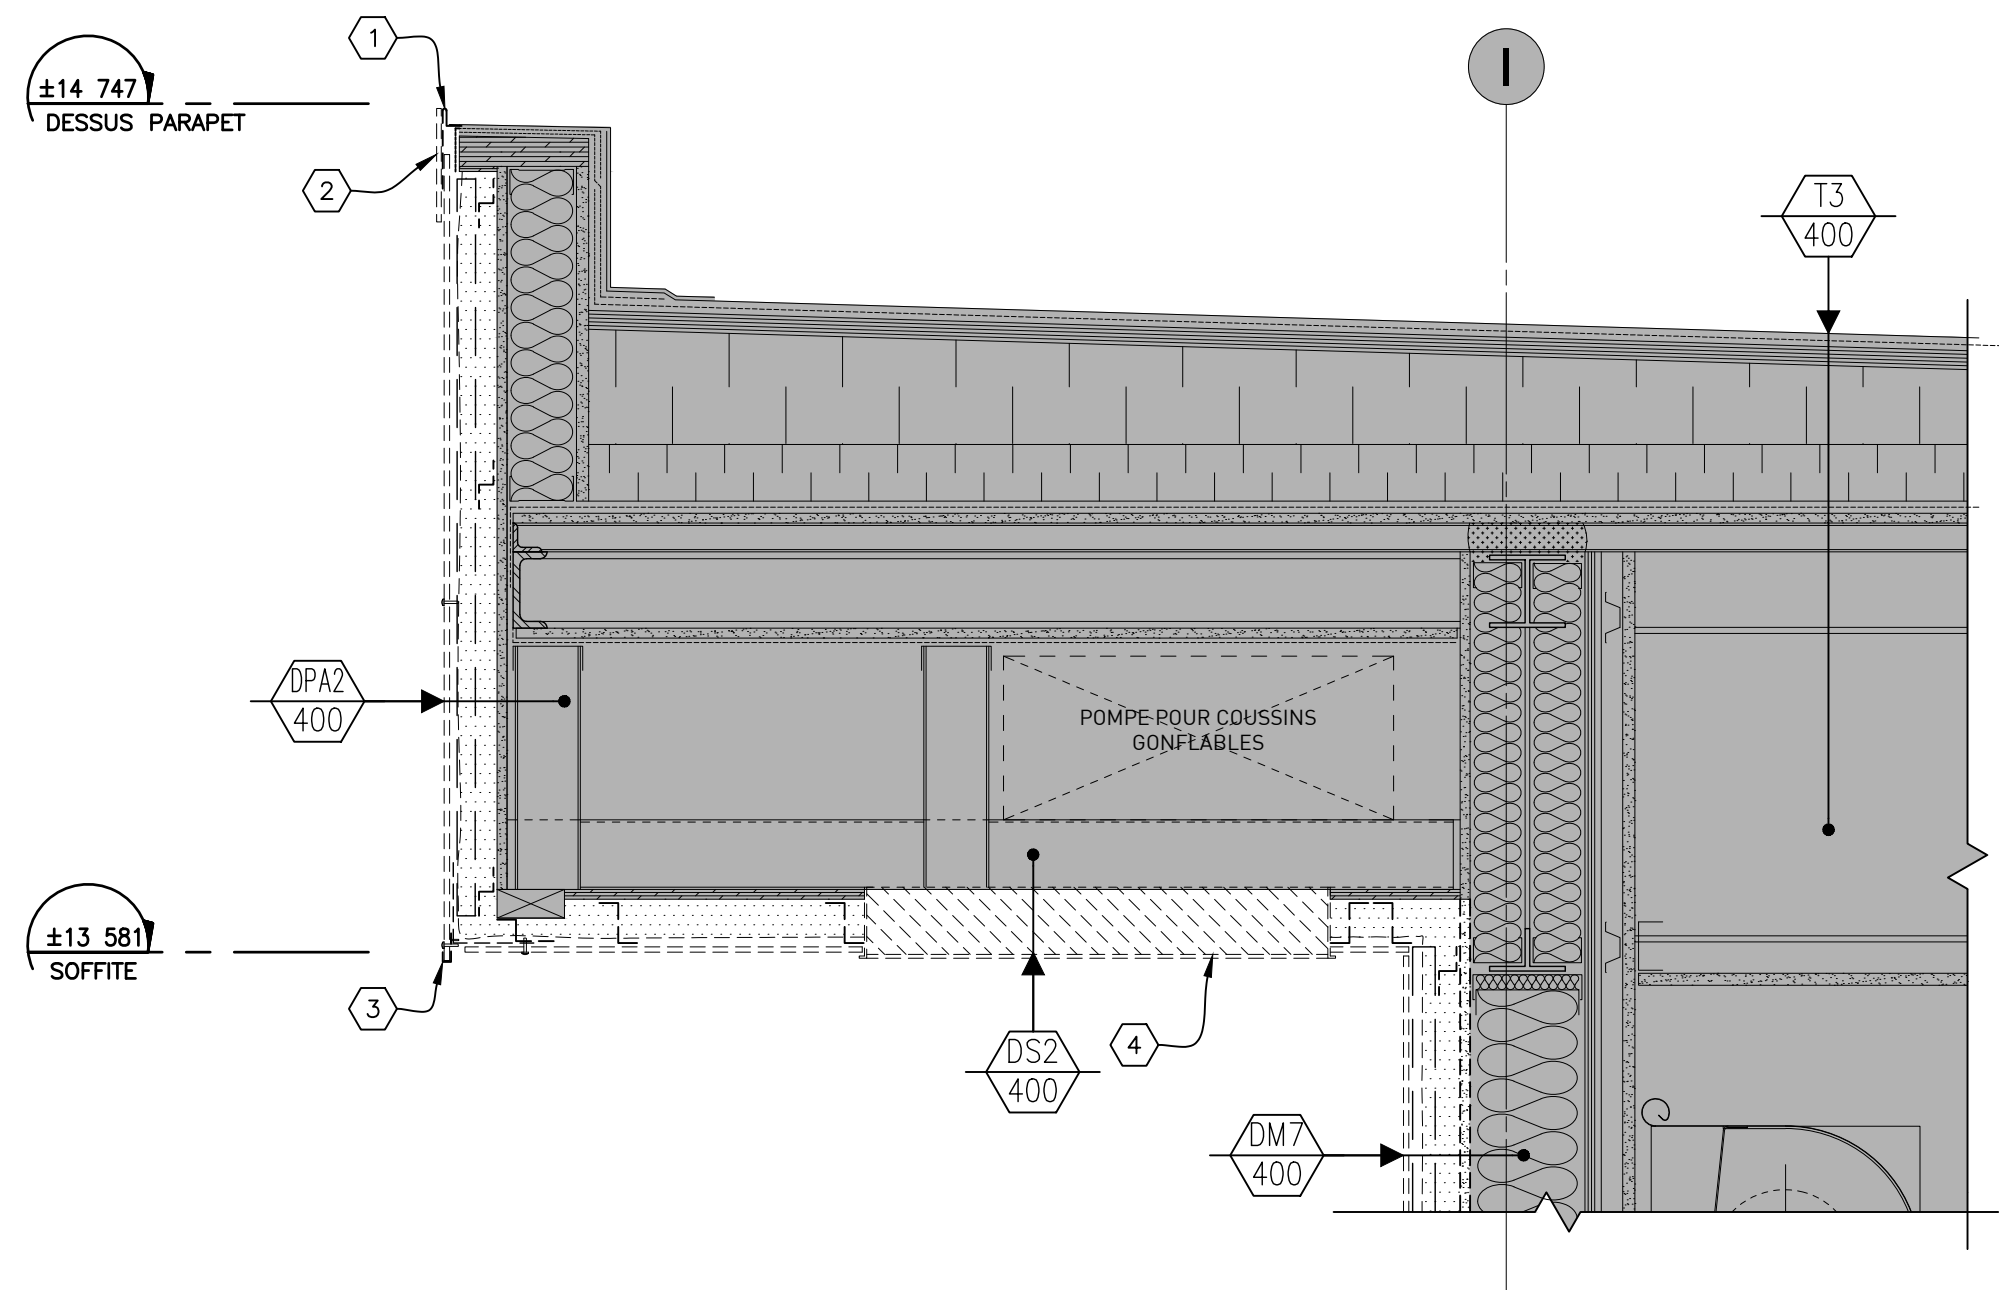


DÉMOLITION

34
407 416
1:10mm
(IRM)

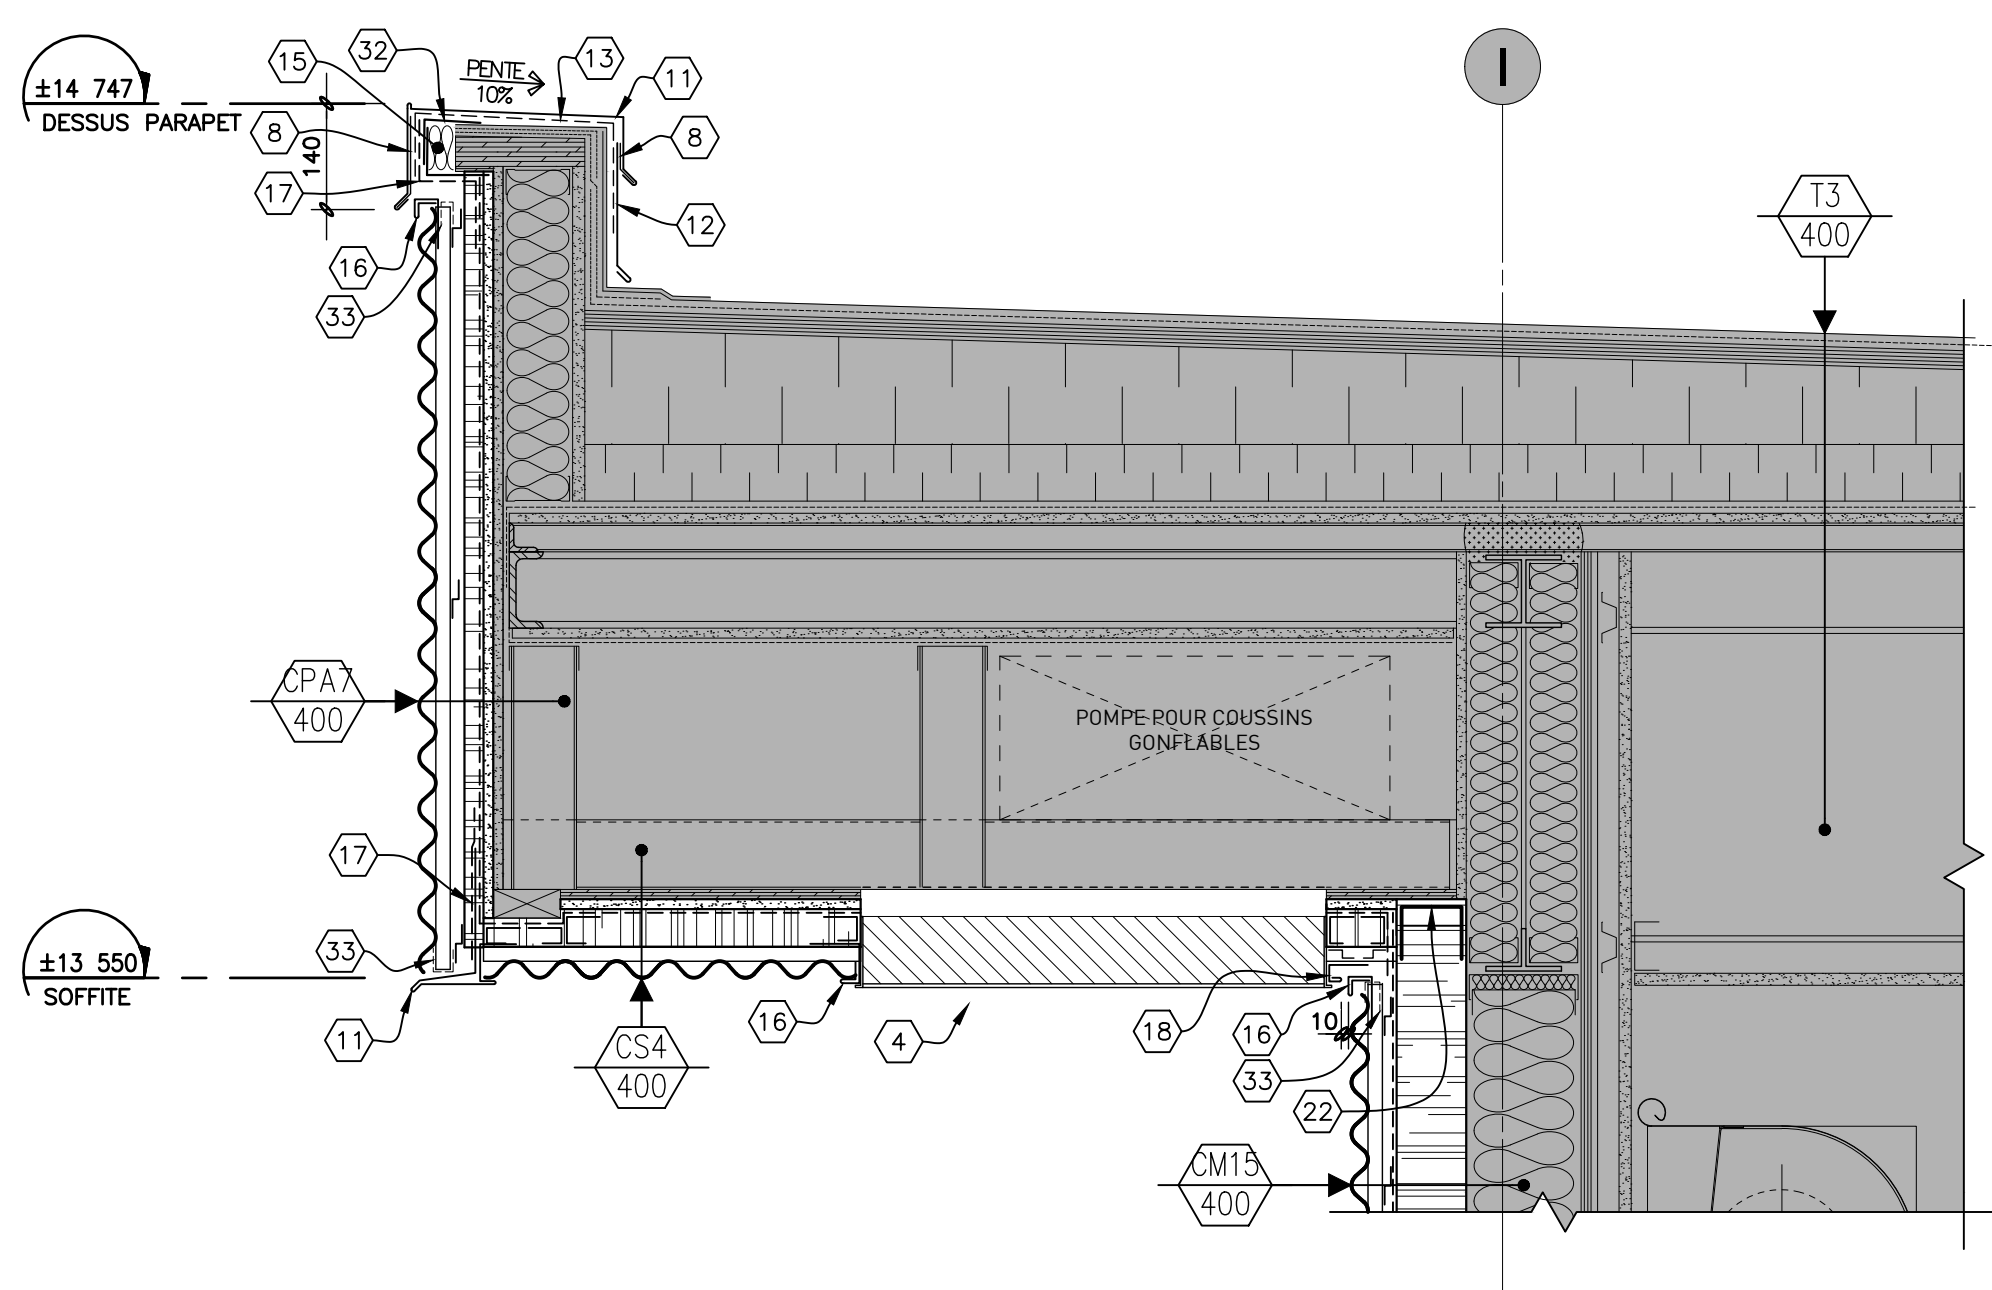


CONSTRUCTION

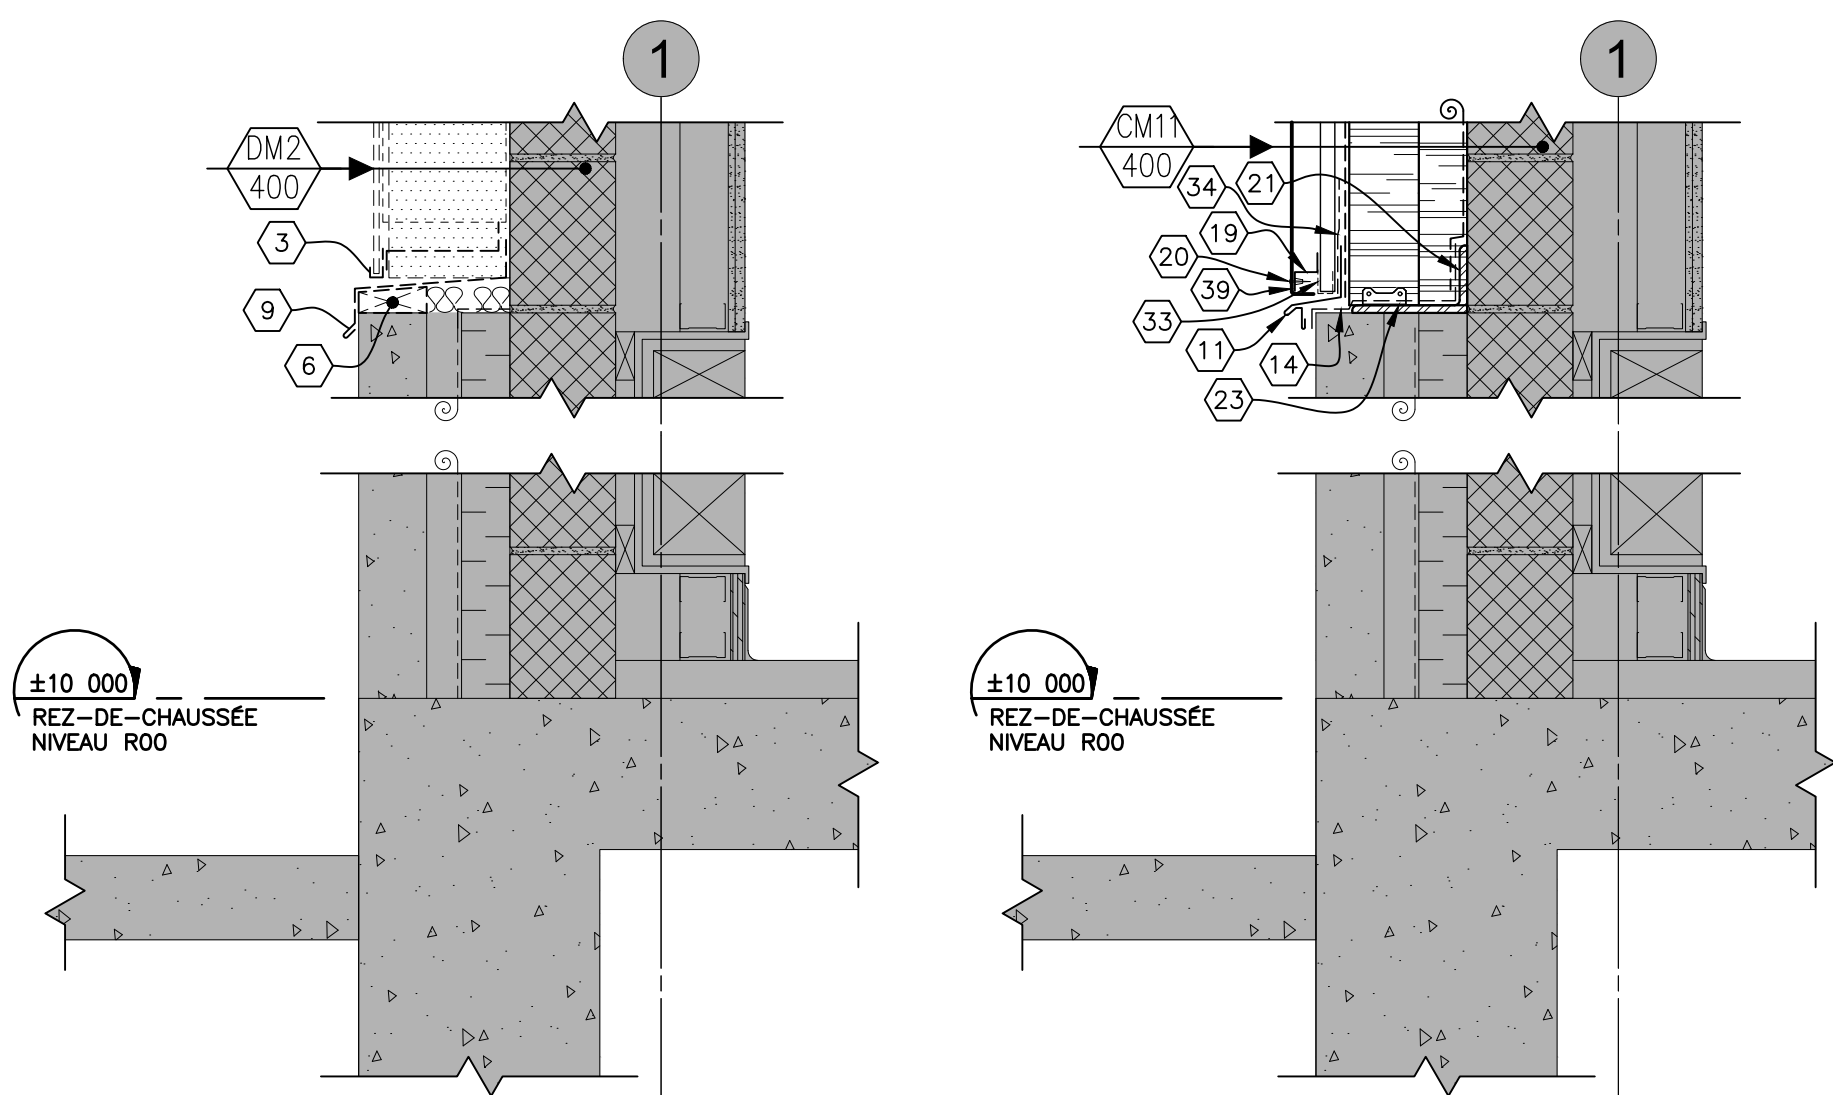

DÉMOLITION

CONSTRUCTION


35
404,407 416
1:10mm (BASILAIRE SUD-OUEST)

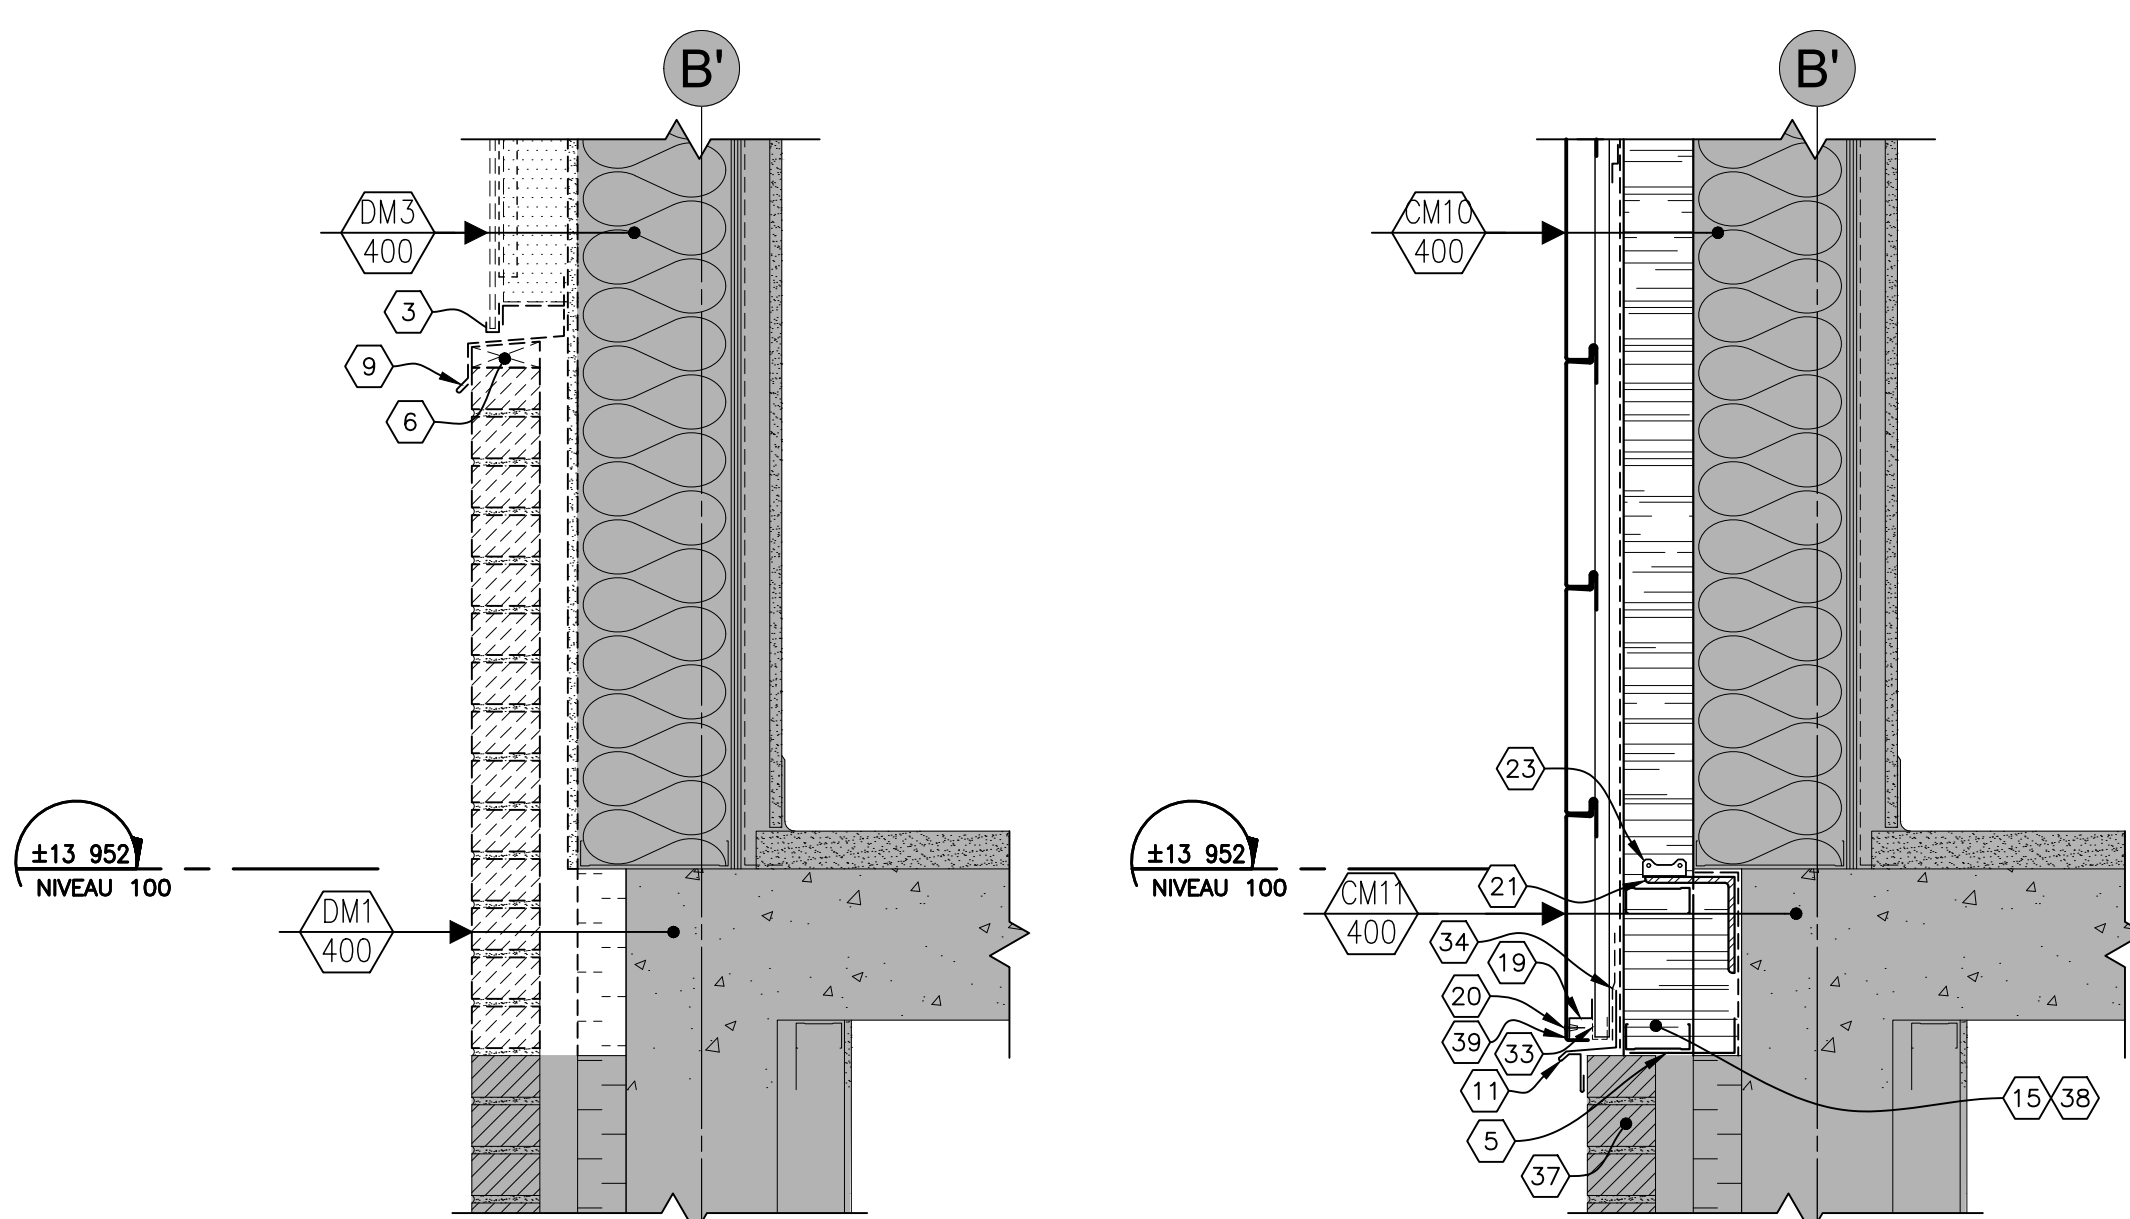

DÉMOLITION

CONSTRUCTION


36
201,202,203,204,407 416
1:10mm (ADMINISTRATION)

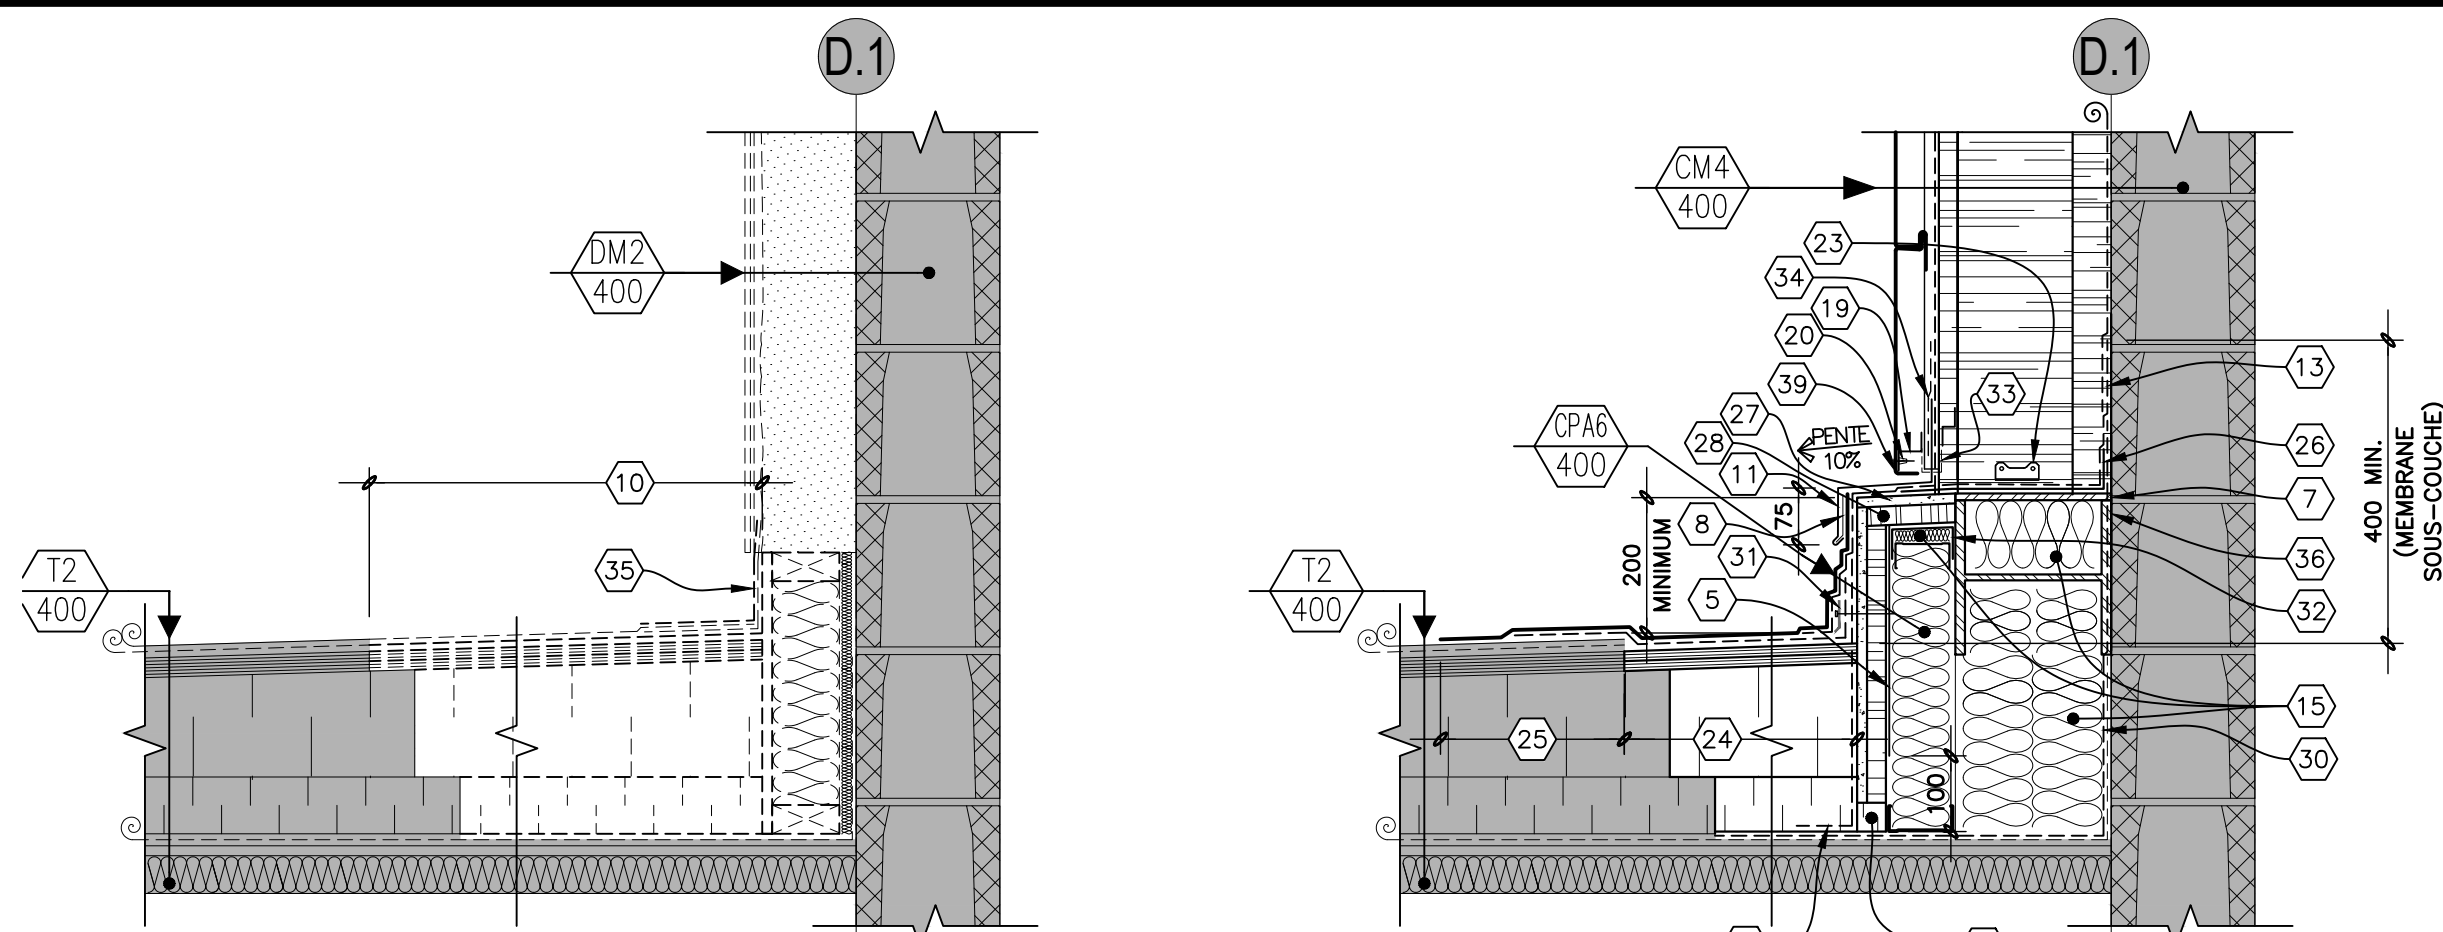

DÉMOLITION

CONSTRUCTION

37
201,203,504 416
1:10mm
(MUR ESCALIER #3 / TOITURE ADMINISTRATION)

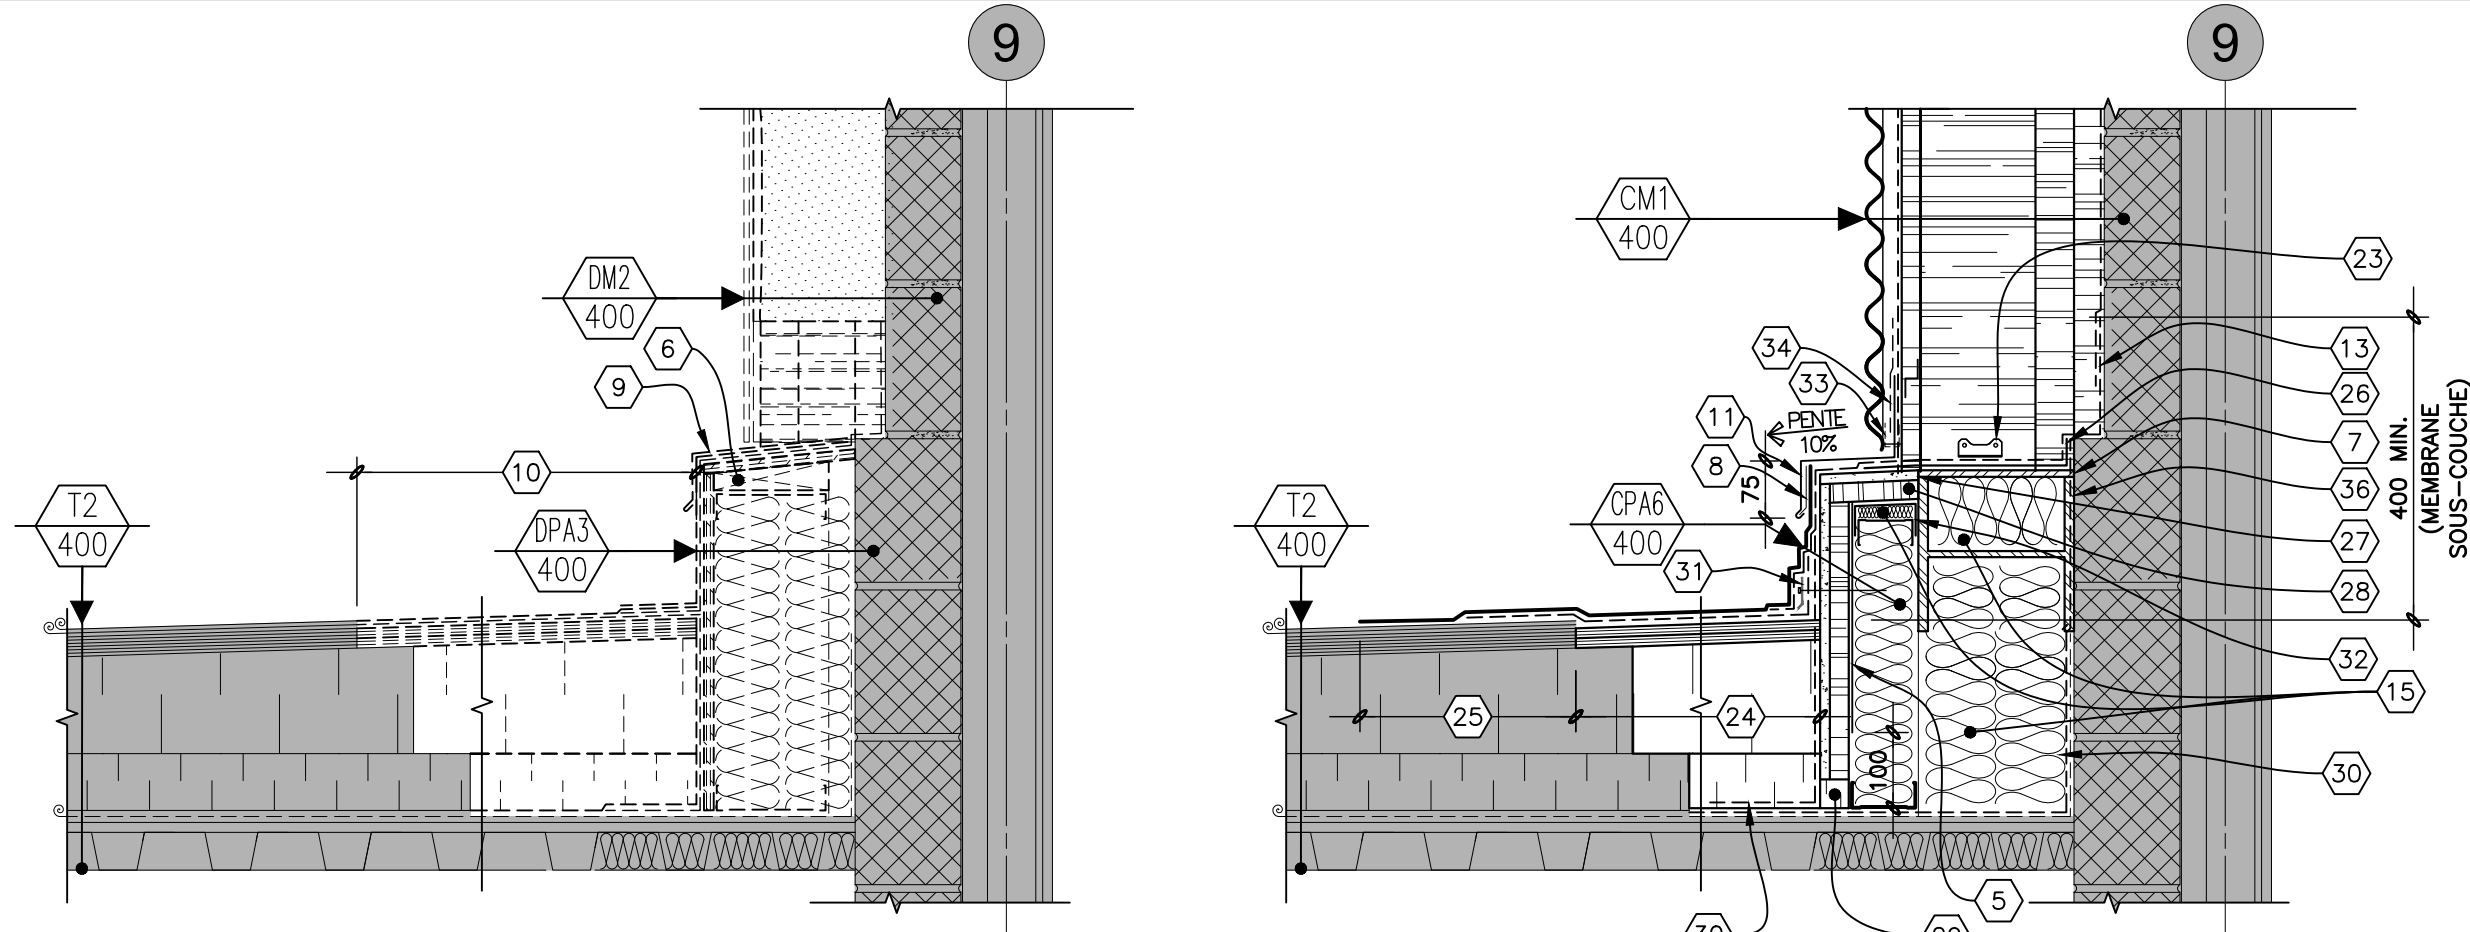

DÉMOLITION

CONSTRUCTION

38
202,204,507 416
1:10mm
(TOUR / TOITURE ADMINISTRATION)

NOTES

- SOLIN EXISTANT À COUPER ET ENLEVER.
- PANNEAU DE POLYMERES RENFORCE DE FIBRES DE VERRE 7mm D'ÉPAISSEUR À DÉMOLIR.
- MOULURE D'ALUMINIUM À DÉMOLIR.
- GRILLE DE VENTILATION À ENLEVER AVEC CADRE À ENLEVER ET RÉINSTALLER.
- TÔLE D'APPUÏE EN ACIER GALVANISÉ CAL.18.
- PIÈCE DE BOIS EXISTANTE À DÉMOLIR.
- PLAQUE D'ACIER PONCTUELLE, VOIR STRUCTURE.
- AGRAFE EN ACIER GALVANISÉ, CAL.24 CONTINUE.
- SOLIN EXISTANT À DÉMOLIR.
- OUVERTURE À FAIRE DANS LA TOITURE EXISTANTE SUR 4500mm POUR LA CONSTRUCTION DU NOUVEAU PARAPET. VOIR COMPOSITION DE TOIT SUR LE DÉTAIL.
- SOLIN EN ACIER ÉMAILLÉ CAL.24, JOINTS AGRAFÉS.
- CONTRE-SOLIN EN ACIER ÉMAILLÉ, CAL.24.
- MEMBRANE SOUS-COUCHE
- SOLIN MEMBRANE AUTOCOLLANT.
- REMPLIR L'ESPACE DE LAINE DE FIBRE DE ROCHE.
- MOULURE EN "J" EN ACIER ÉMAILLÉ CAL.24.
- MEMBRANE AUTOCOLLANTE.
- TÔLE PLIÉE EN ACIER ÉMAILLÉ CAL.24 .
- PLIAGE DE TÔLE EN ACIER GALVANISÉ, CAL.22.
- RIVET EN ACIER INOXYDABLE.
- CORNIÈRE, VOIR STRUCTURE.
- LISSE DE DÉFLEXION, VOIR STRUCTURE.
- CONNECTEUR À CHAQUE COLOMBAGES OU BARRE "Z" SELON LE CAS, VOIR STRUCTURE.
- RAGRÉER LA TOITURE TEL QUE L'EXISTANT. VOIR COMPOSITION DE TOIT SUR LE DÉTAIL.
- CHEVAUCHER LA NOUVELLE MEMBRANE SUR LES MEMBRANES DE LA TOITURE EXISTANTE SUR MINIMUM 300mm. DÉGRANULER LA MEMBRANE EXISTANTE AU PRÉALABLE.
- TÔLE PLIÉE CONTINUE EN ACIER GALVANISÉ, CAL. 18.
- PANNEAU DE CIMENT 13mm.
- ISOLANT RIGIDE DE FIBRE DE ROCHE 25mm.
- ISOLANT SEMI-RIGIDE DE FIBRE DE ROCHE DE 38mm D'ÉPAISSEUR.
- MEMBRANE PARE-VAPEUR AUTOCOLLANTE.
- BARRE D'ANCRAGE DE LA MEMBRANE.
- DEUX (2) PLIAGES DE TÔLE EN "L", CAL.16 EN ACIER GALVANISÉ.
- MOUSTQUAIRE.
- SCELLER LA MEMBRANE PARE-INTÉPIÉRIES SUR LE SOLIN AVEC UN RUBAN AUTOCOLLANT.
- PARAPET À DÉMOLIR:
 - MEMBRANES À DÉMOLIR;
 - PANNEAU DE CIMENT À DÉMOLIR;
 - COLOMBAGE DE BOIS À DÉMOLIR;
 - ISOLANT DE FIBRE DE VERRE À DÉMOLIR.
- POUTRE D'ACIER, VOIR STRUCTURE.
- CRÉER DES ÉVÈNTS À MAÇONNERIE DANS L'AVANT DERNIER RANG DE BRIQUES DU MUR EXISTANT, EN ÉVITANT LE JOINT DE MORTIER VERTICAL À TOUS LES 3 BRIQUES.
- MURET EN COLOMBAGES MÉTALLIQUES 92mm Ø400mm c/c.
- BOUT DU PANNEAU REPLIÉ VERS L'INTÉRIEUR.

LÉGENDE

- EXISTANT À CONSERVER.
- ÉLÉMENT À DÉMOLIR.
- AXE EXISTANT
- EXTÉRIEUR DE LA STRUCTURE DE BÉTON EXISTANTE DE LA TOUR.
- NOUVEL AXE: FACE EXTÉRIEURE DES BARRES Z ET COLOMBAGES DE LA TOUR. VOIR STRUCTURE.
- (*) VOIR NOTE GÉNÉRAL PAGE 400.

NE DOIT PAS SERVIR À L'EXÉCUTION

Le présent document est émis pour la seule fin identifiée. Son contenu est protégé par les droits d'auteur et toute reproduction ou modification, partielle ou totale, est interdite sans l'autorisation écrite de gagnon, letellier, cyr, ricard, mathieu, proulx, savard consortium d'architectes.



GLCRM | Proulx Savard |


GLCRM:
128, Avenue de la Cathédrale,
Bureau 201
Rimouski, QC, G5L 5H7
(418) 722-7655

2406, Ch. des Quatres-Bourgeois,
Bureau 100
Québec, QC, G1V 1W5
(418) 647-1700

Proulx Savard Architectes:
75, boul. Arthur-Buies Ouest,
Rimouski QC G5L 5C2
(418) 723-5543

ARCHITECTURE

CONSULTANTS

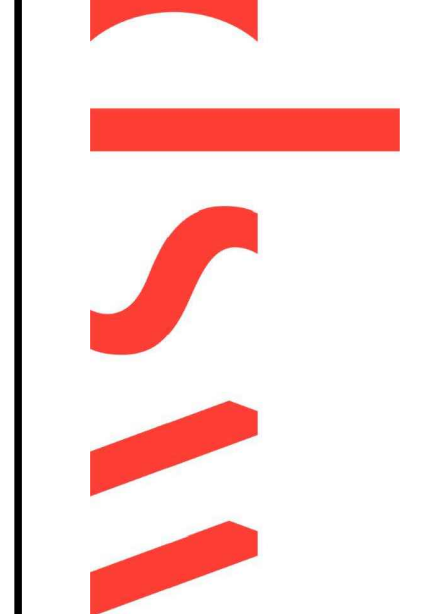



CONSULTANTS








DESSINATEUR (S)	DOSSIER N°	DATE	REVISIONS
DB AL	24-1087 / 687-24	SEPTEMBRE 2024	
INDICÉE			
05	2024-09-04	DÉFINITIVES POUR SOUMISSION	
04	2024-08-21	DÉFINITIVES 100% POUR APPROBATION	
03	2024-08-03	DÉFINITIVES 80% POUR APPROBATION	
02	2024-05-14	DÉFINITIVES 40% POUR APPROBATION	
01	2024-02-27	PRÉLIMINAIRES 20% POUR APPROBATION	
No		DATE	

DESSIN	COUPE DE MUR TYPE DÉMOLITION ET CONSTRUCTION	PROJET	HÔPITAL DE CHANDLER, Chandler (Réfection de l'enveloppe)	PROPRIÉTAIRE	Santé Québec
--------	---	--------	--	--------------	--------------

416

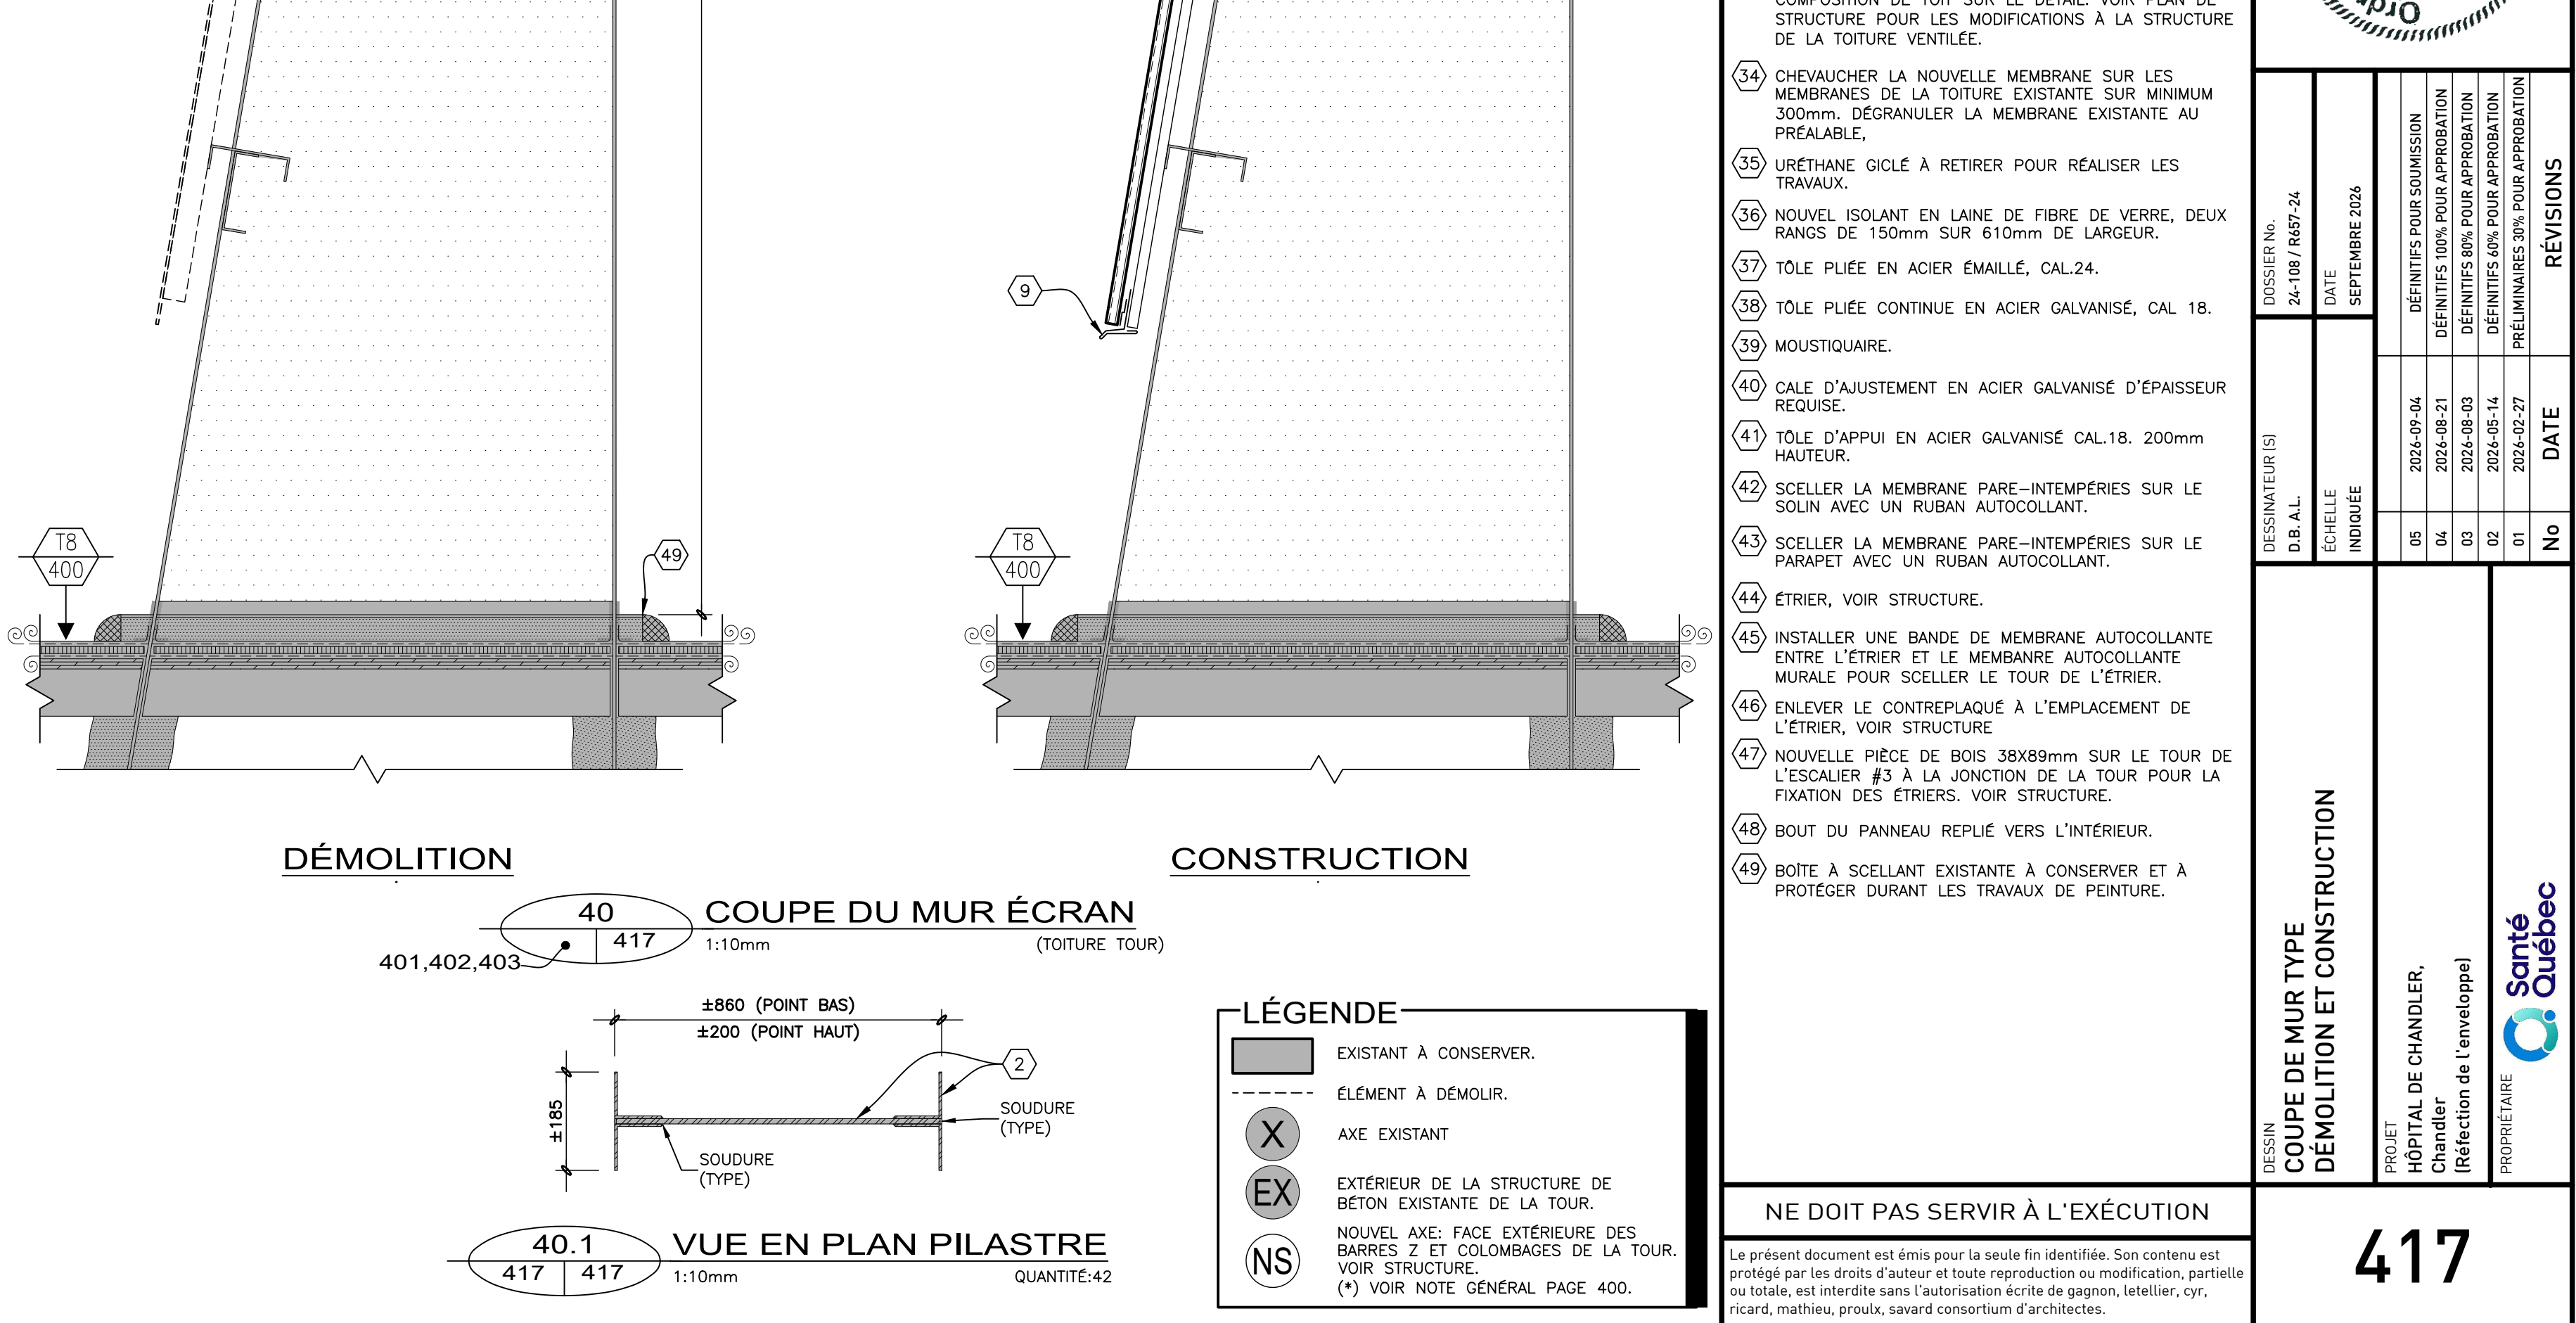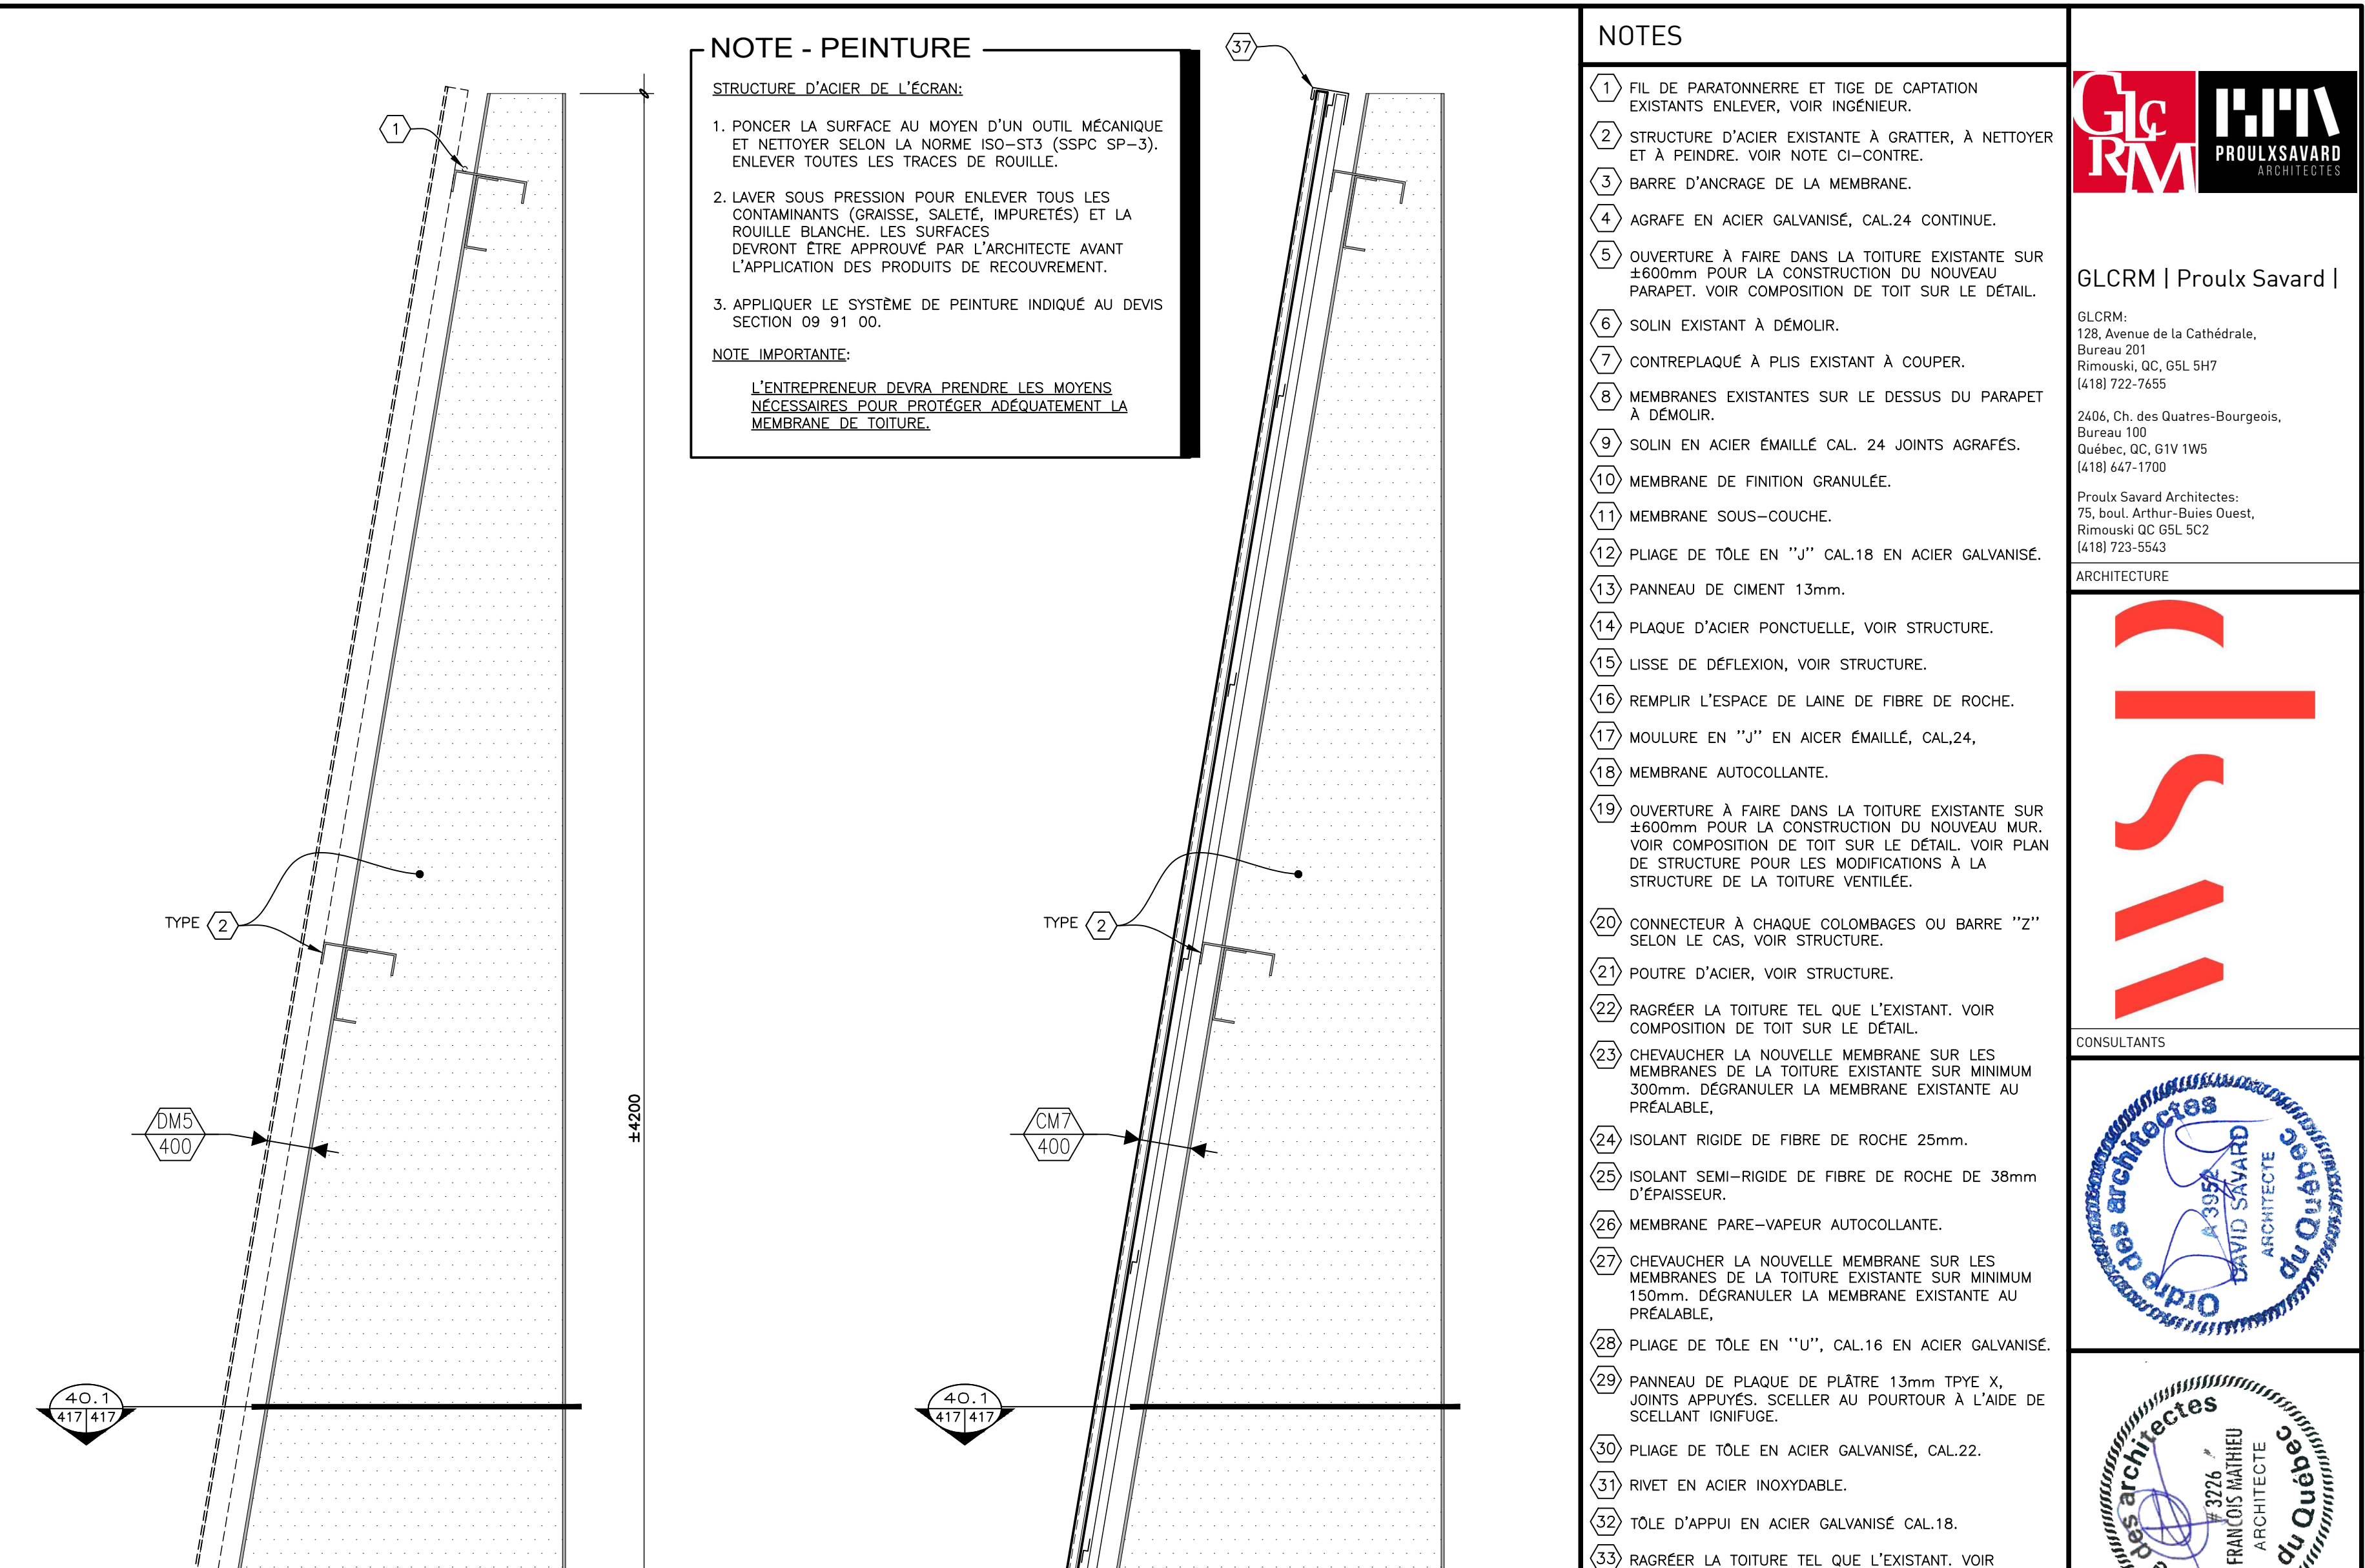

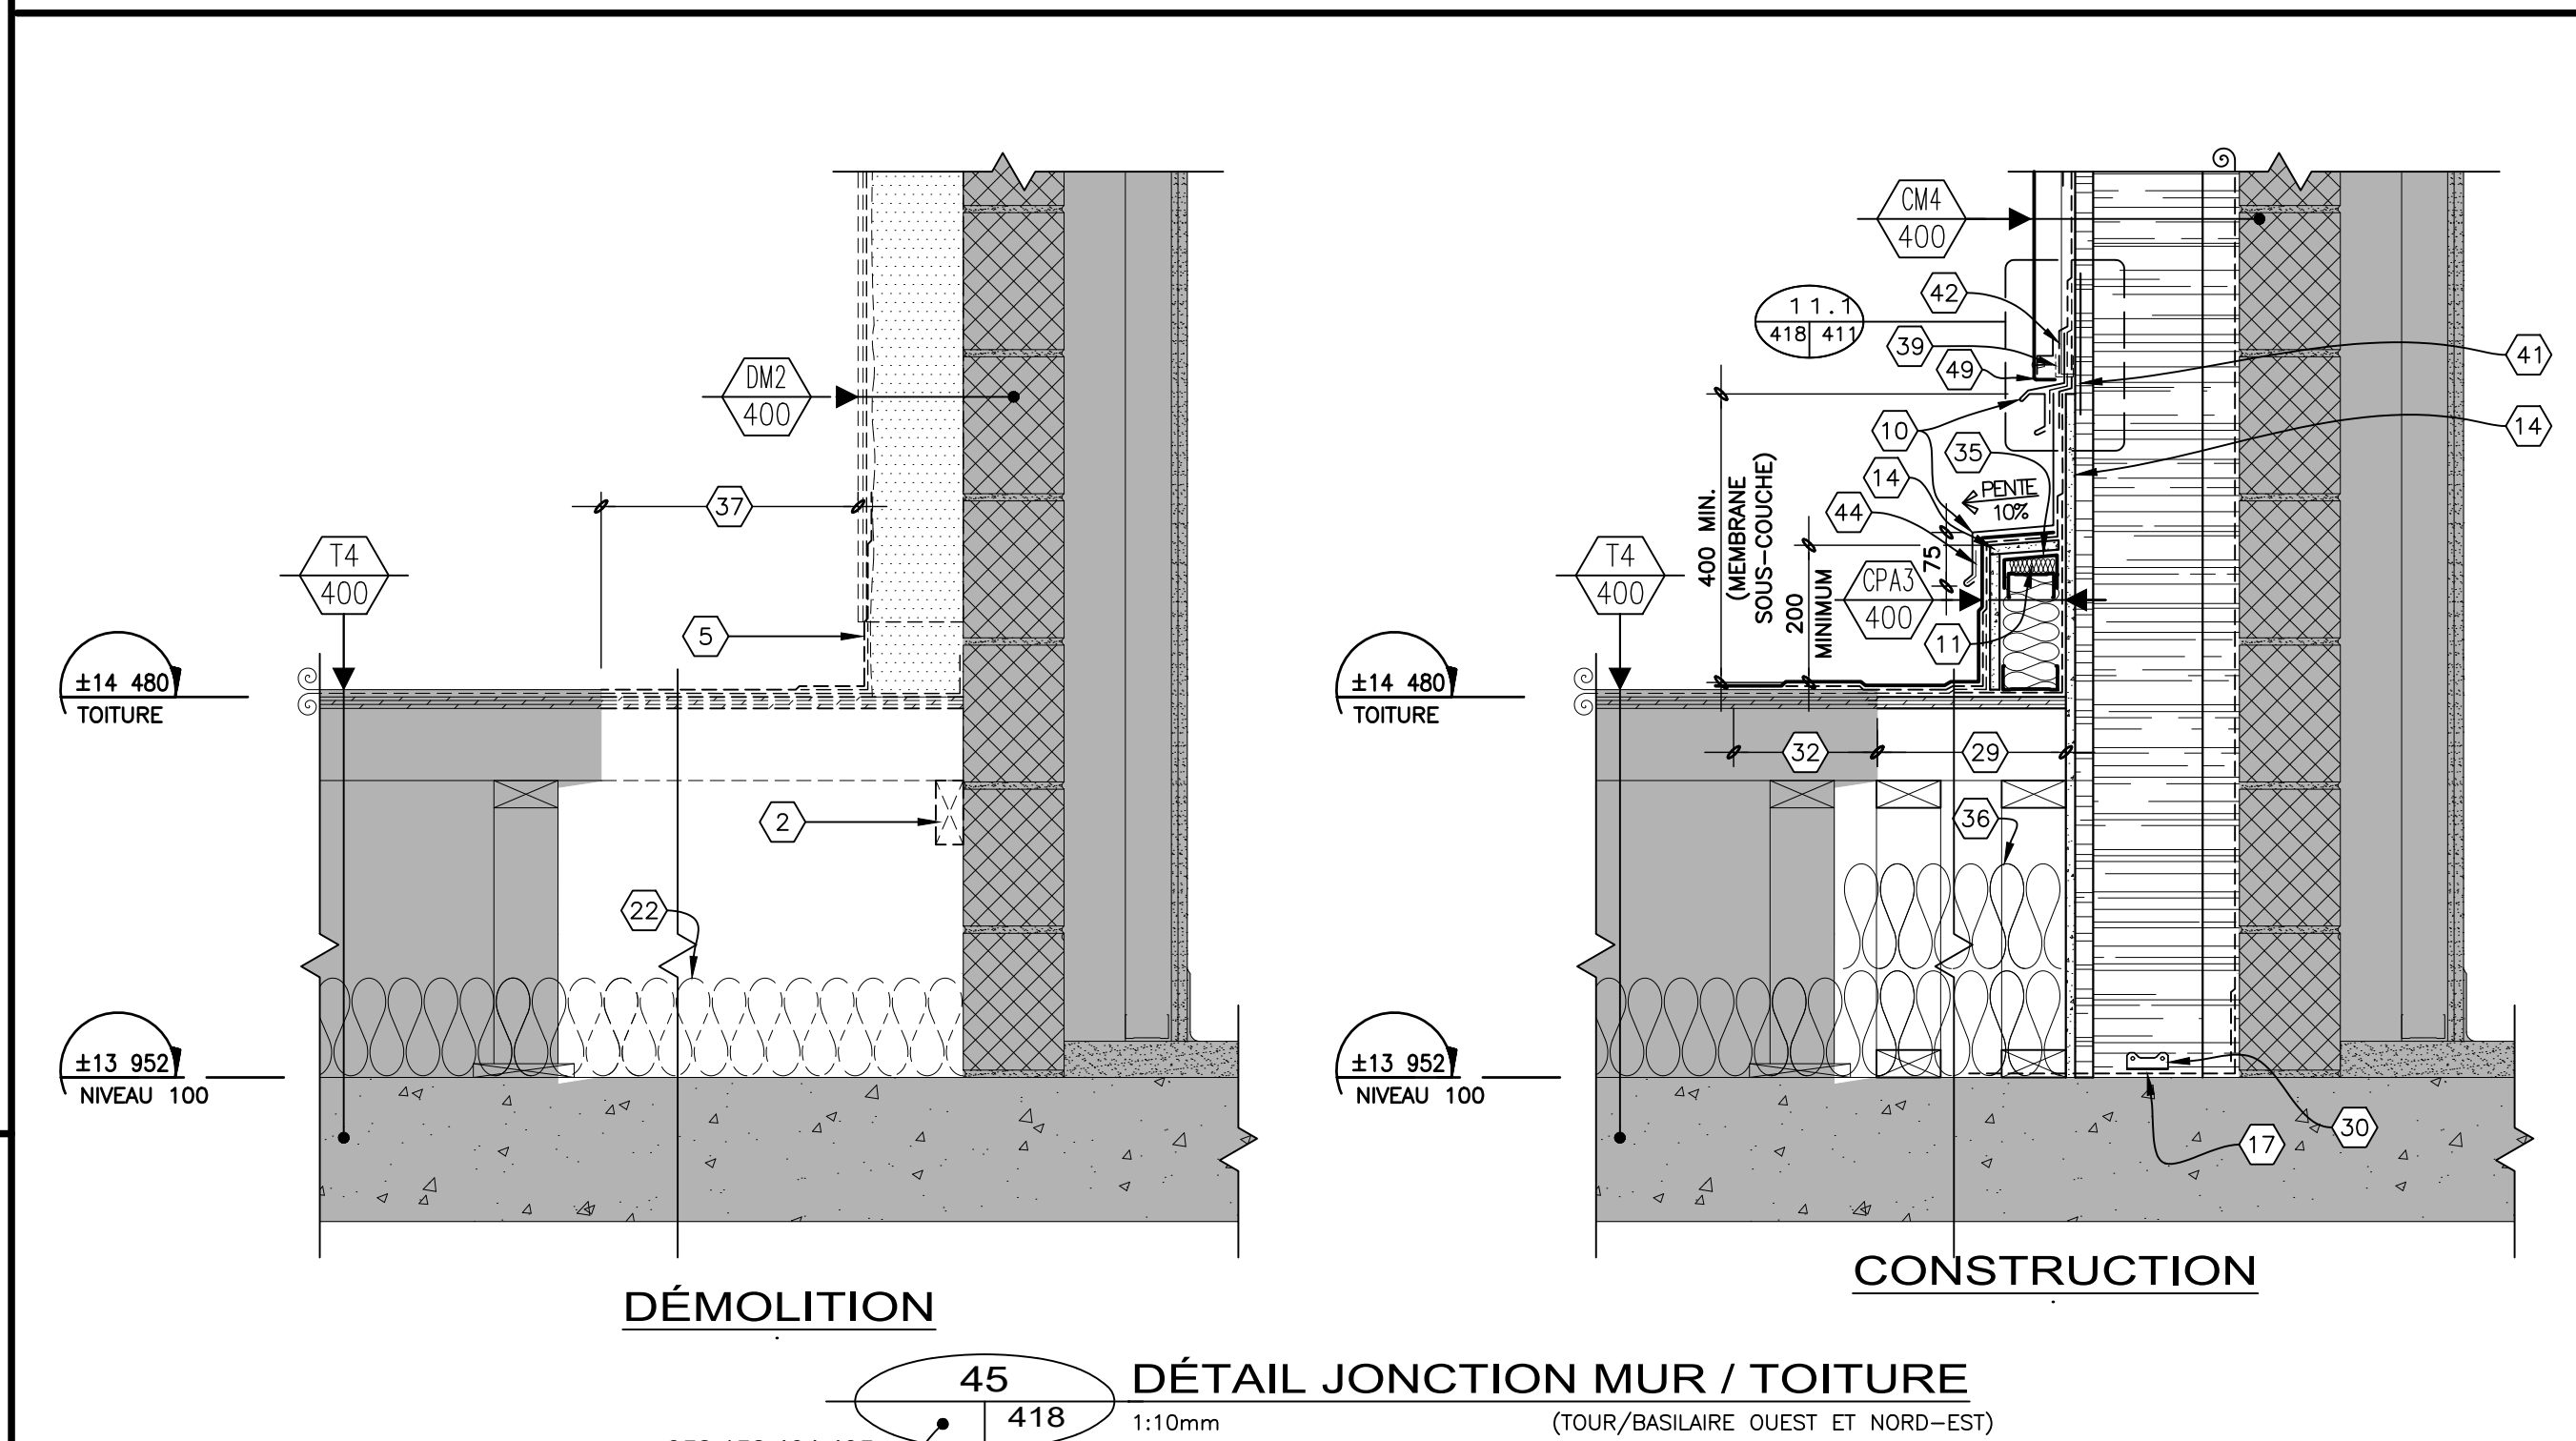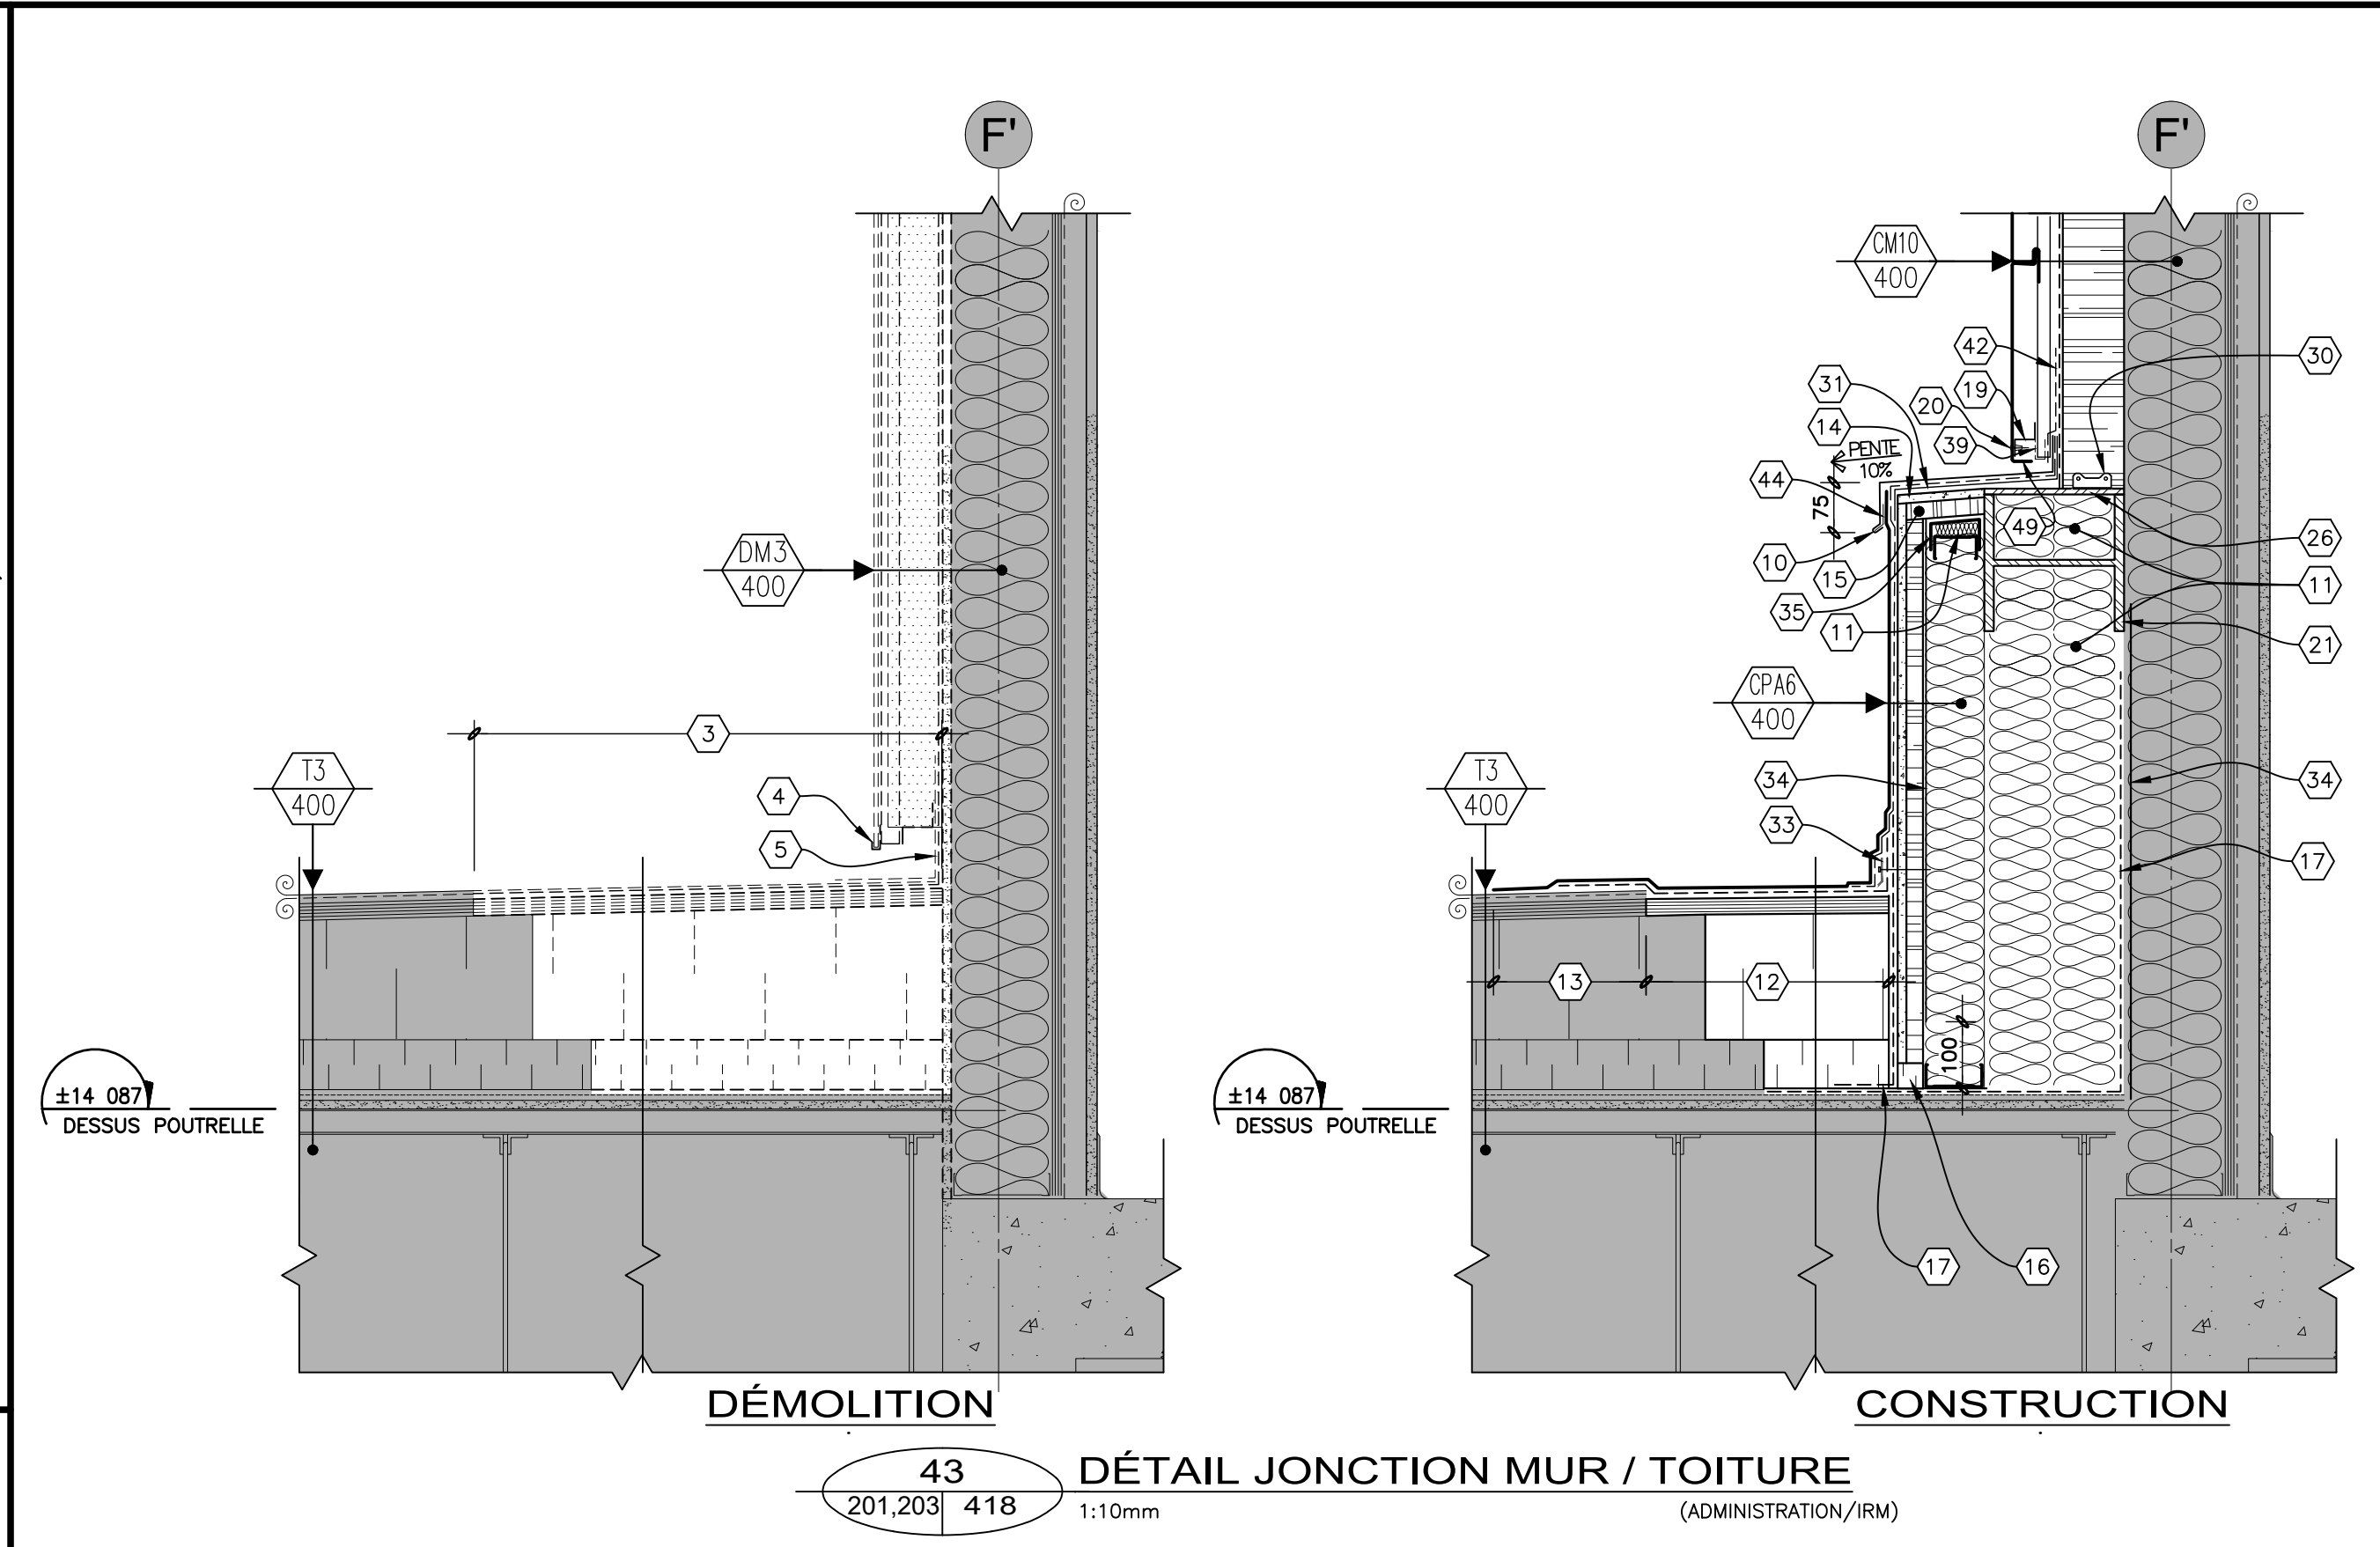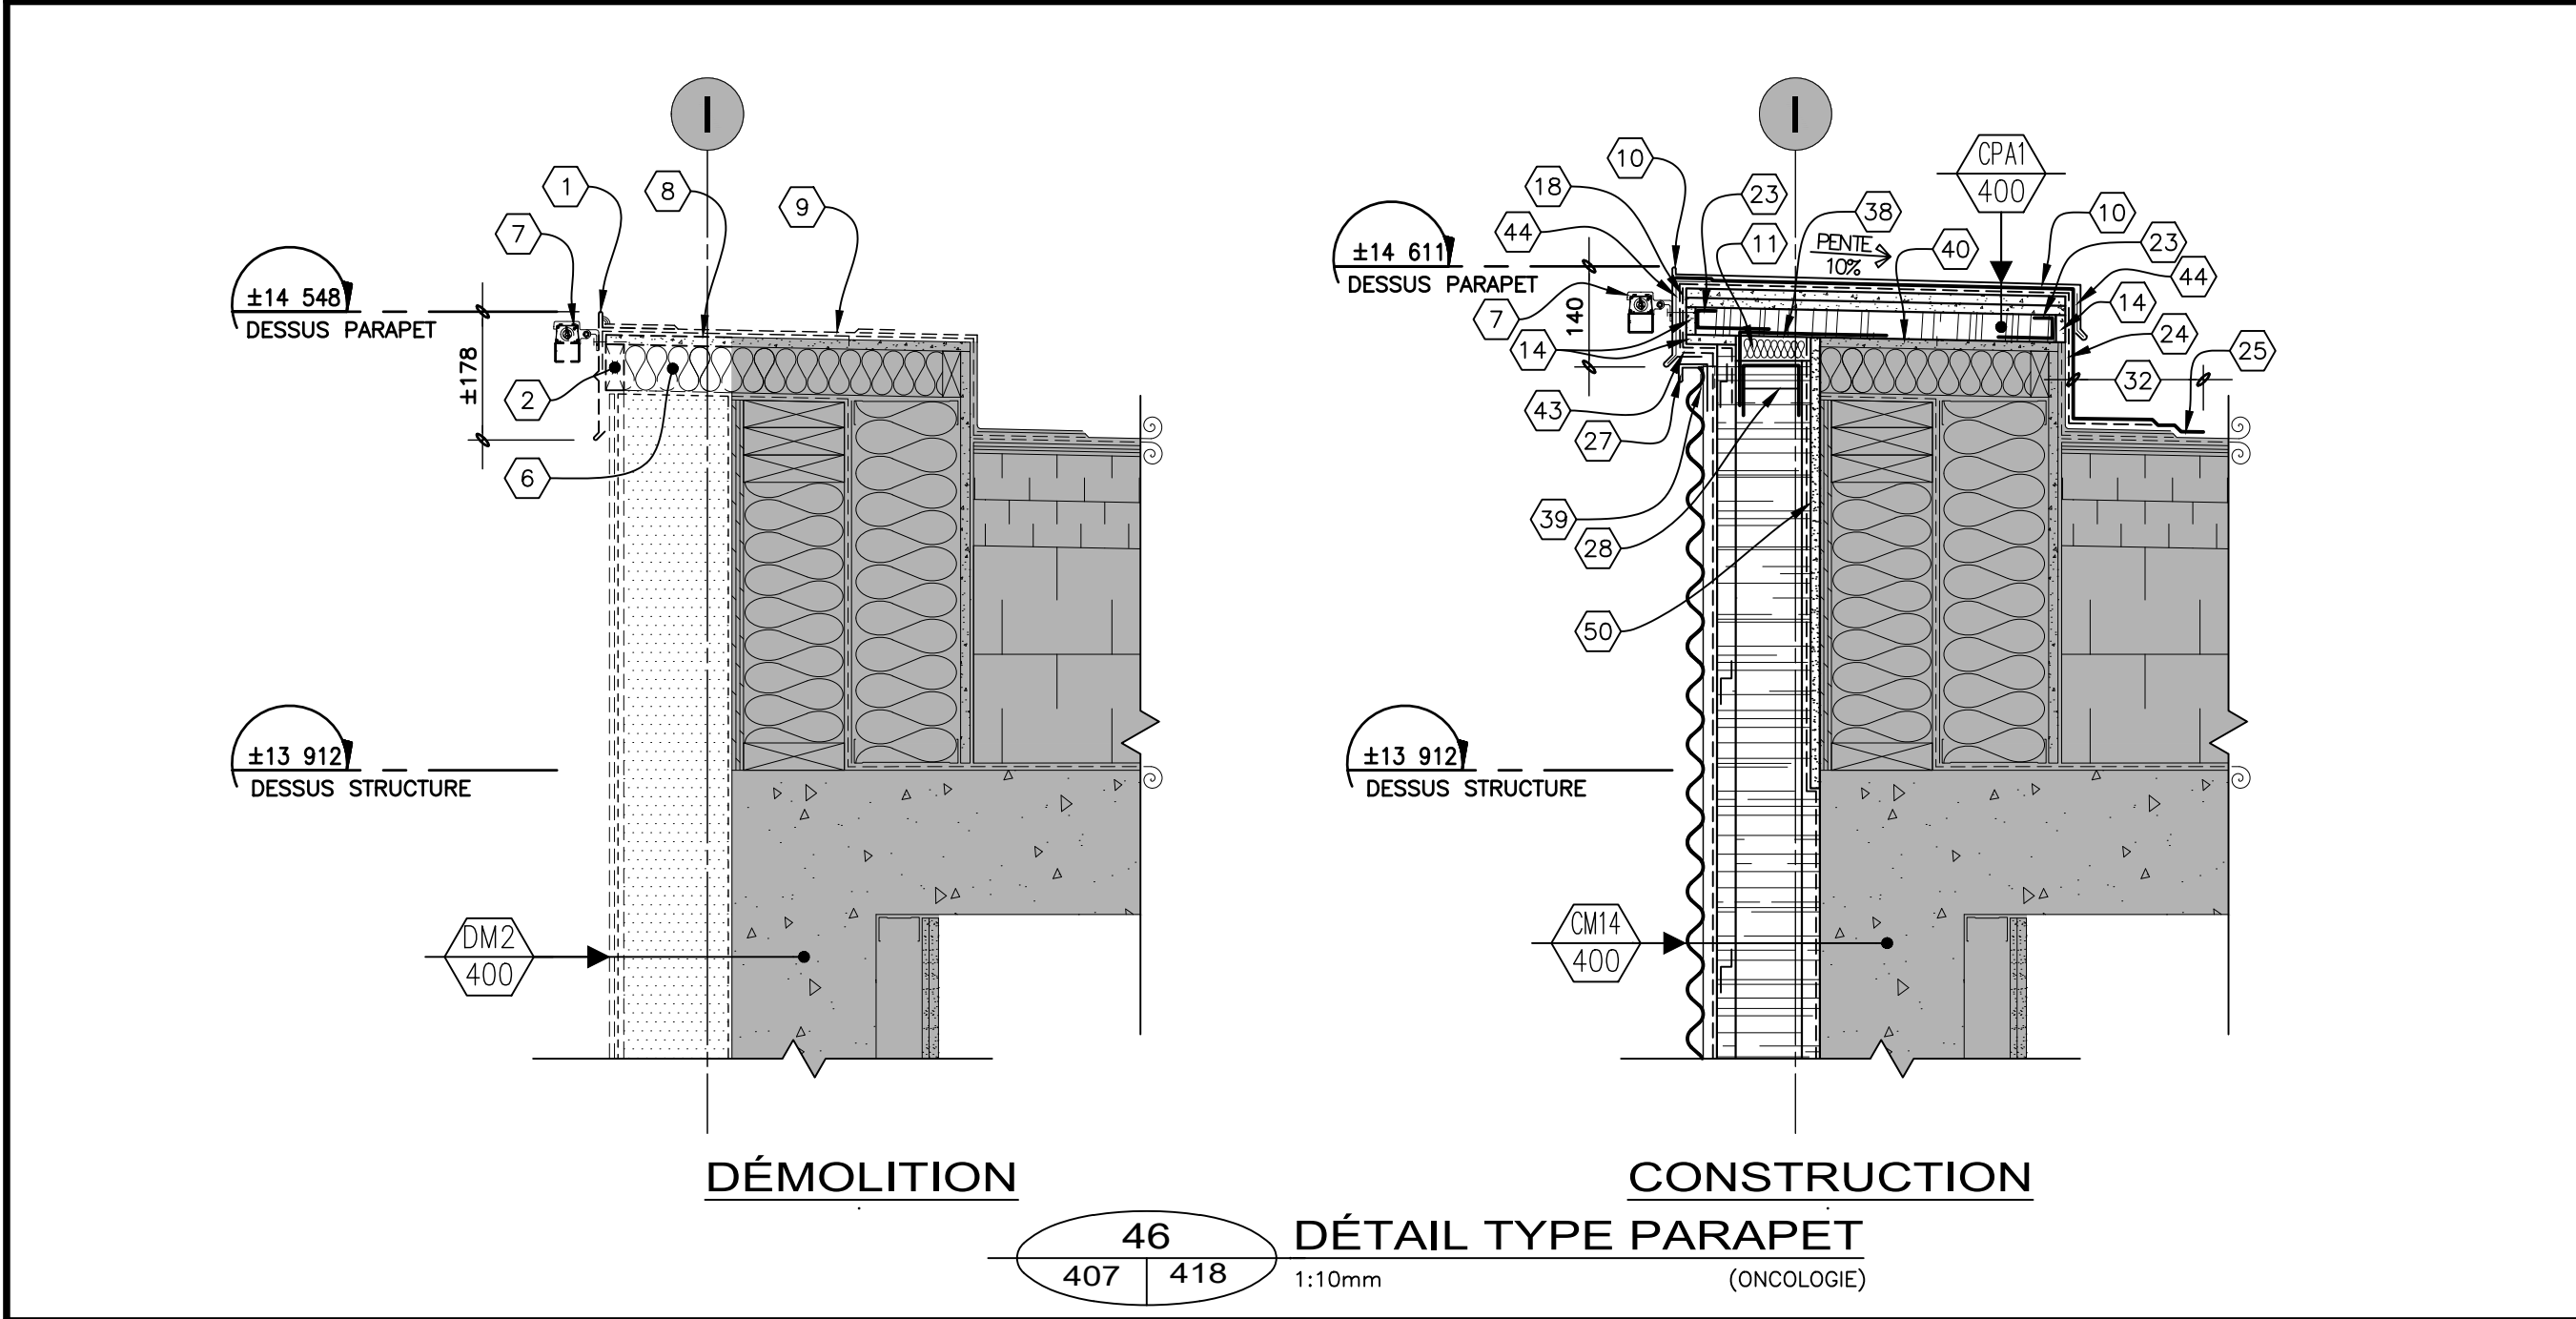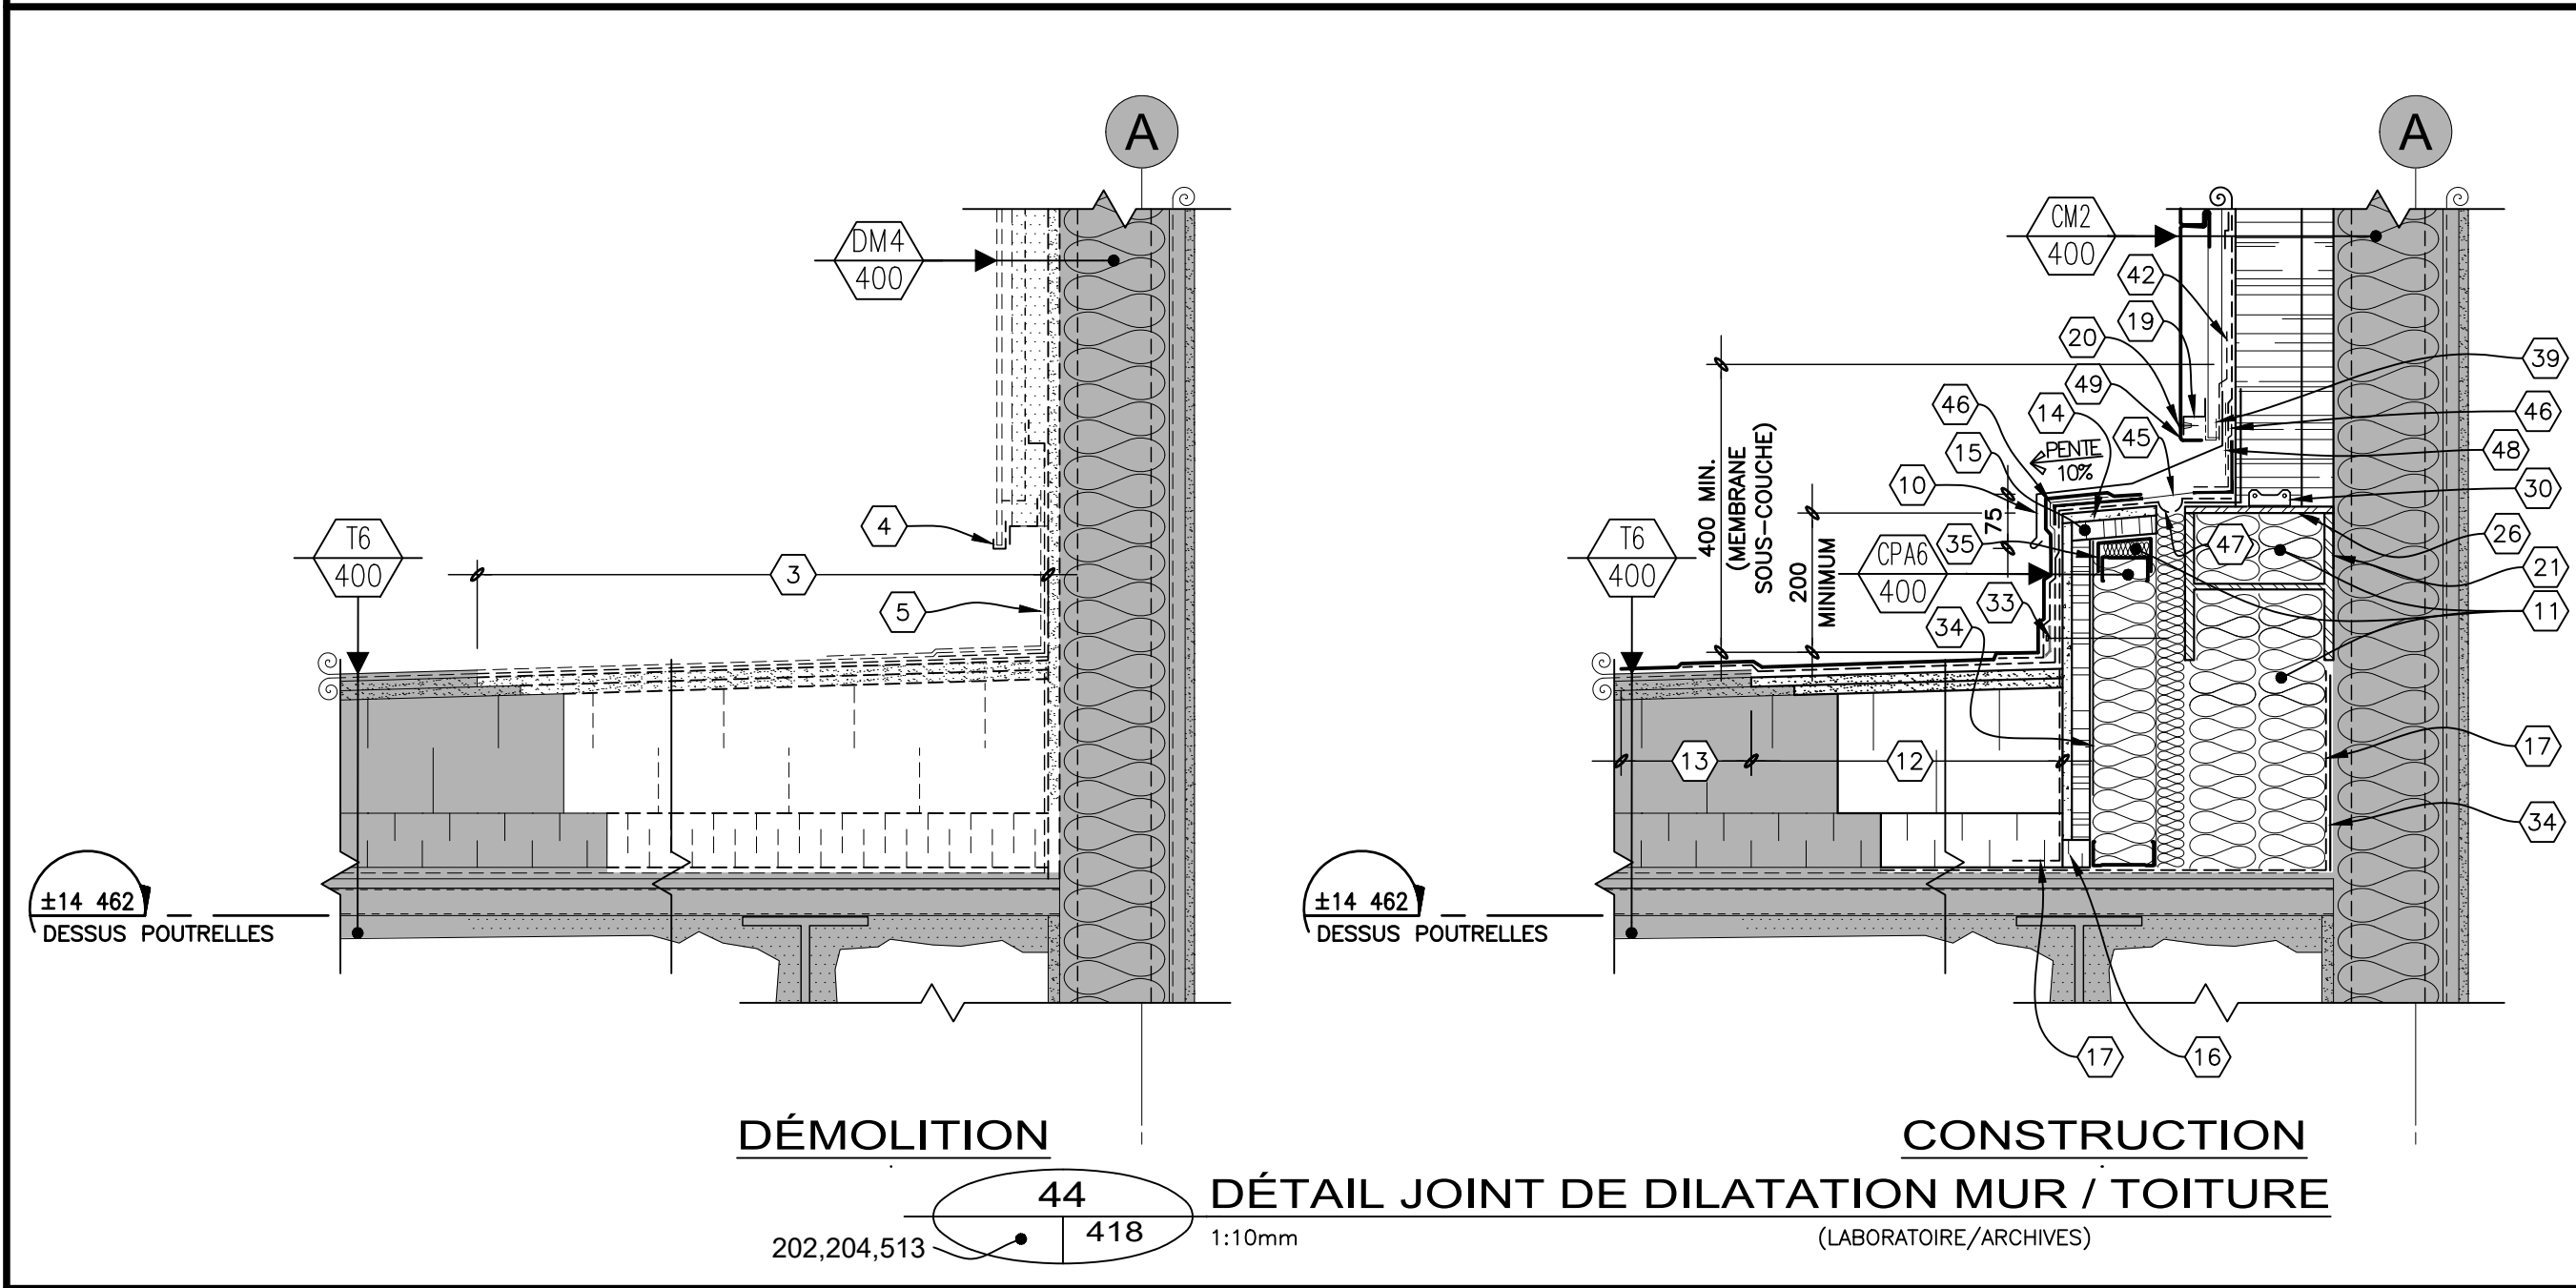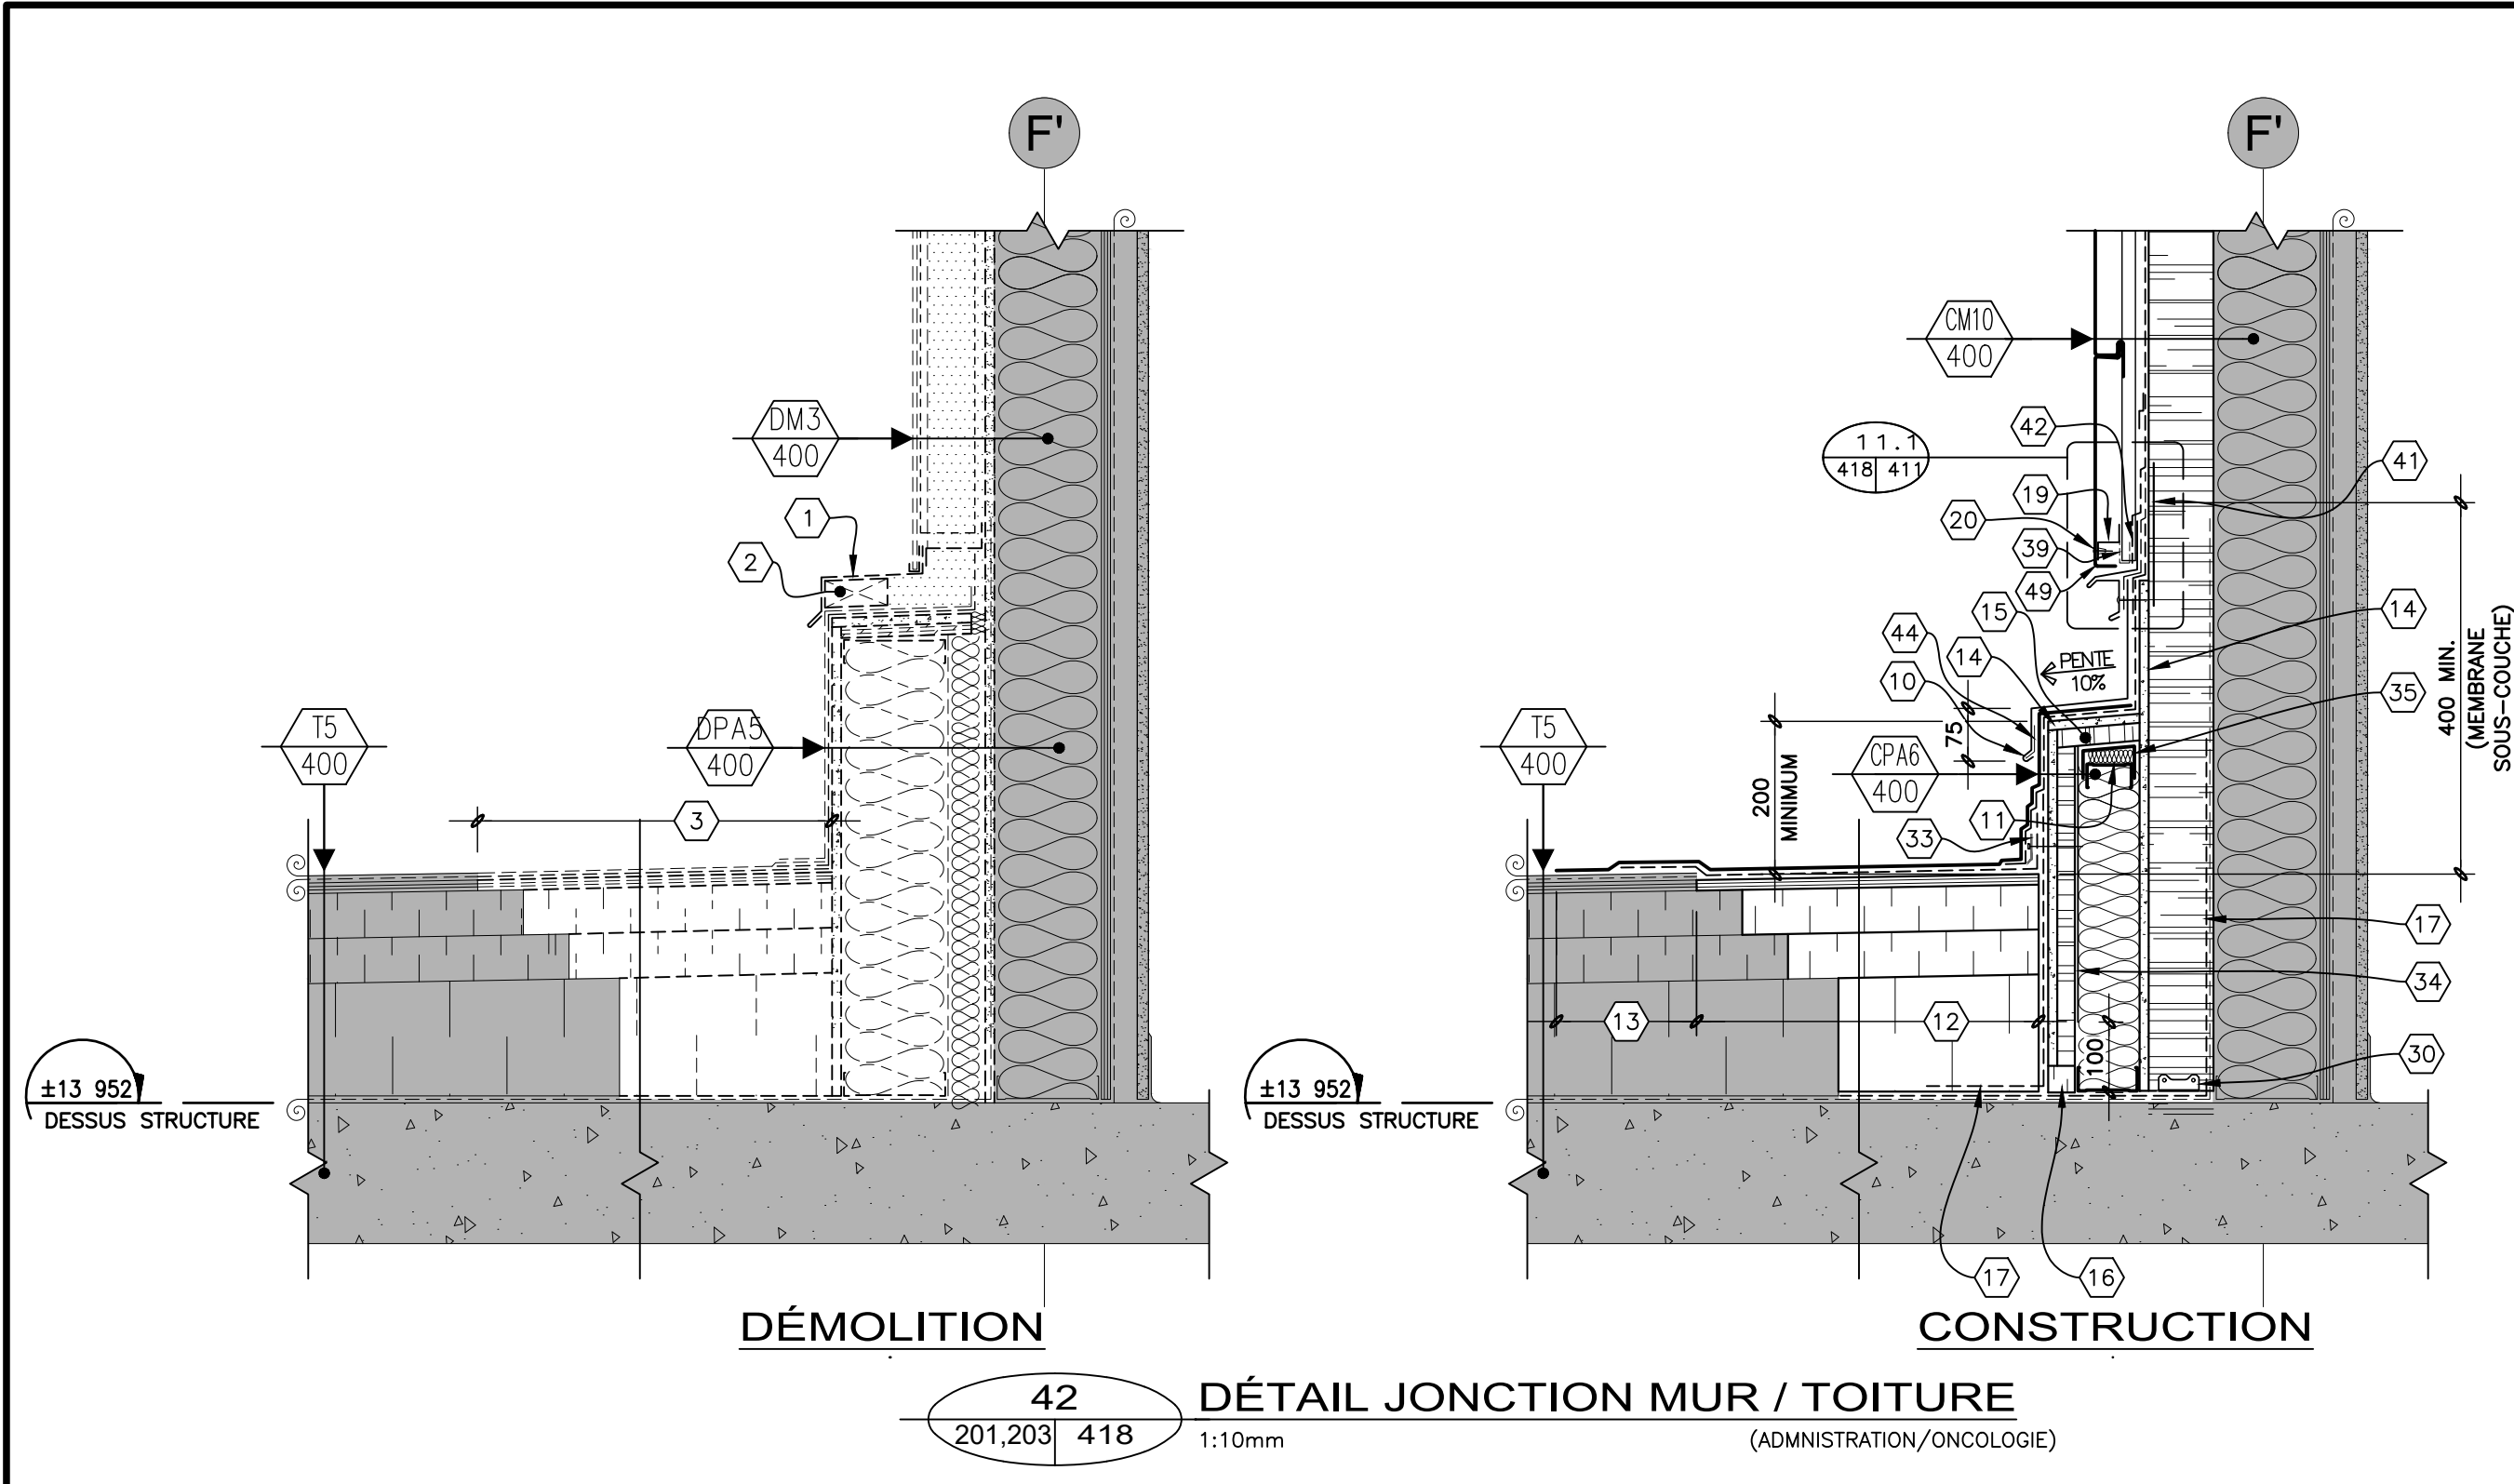

NOTES

1

SOLIN EXISTANT   DEMOLIR.

2

PI  CE DE BOIS EXISTANTE   DEMOLIR.

3

OUVERTURE   FAIRE DANS LA TOITURE EXISTANTE SUR  600mm POUR LA CONSTRUCTION DU NOUVEAU PARAPET. VOIR COMPOSITION DE TOIT SUR LE D  TAIL.

4

MOULURE D'ALUMINIUM   DEMOLIR.

5

REMONTER DES MEMBRANES   DEMOLIR.

6

PI  CE DE BOIS EXISTANTE   COUPER.

7

APPAREIL D'  CLAIRAGE CONTINUE SUR LA FA  DE SUD DU BASILAIRE SECTEUR ONCOLOGIE   ENLEVER ET   REINSTALLER. VOIR ING  NIEUR.

8

PANNEAU DE CIMENT 13mm   COUPER.

9

ENLEVER LES MEMBRANES EXISTANTES SUR LE DESSUS DU PARAPET.

10

SOLIN EN ACIER   MAILL   CAL.24.

11

REMPLIR L'ESPACE DE LAINE DE FIBRE DE ROCHE.

12

RAGRE  R LA TOITURE TEL QUE L'EXISTANT. VOIR COMPOSITION DE TOIT SUR LE D  TAIL.

13

CHEVAUCHER LA NOUVELLE MEMBRANE SUR LES MEMBRANES DE LA TOITURE EXISTANTE SUR MINIMUM 300mm. D  GRANULER LA MEMBRANE EXISTANTE AU PR  ALABLE.

14

PANNEAU DE CIMENT 13mm.

15

ISOLANT RIGIDE DE FIBRE DE ROCHE 25mm.

16

ISOLANT SEMI-RIGIDE DE FIBRE DE ROCHE DE 38mm D'  PAISSEUR.

17

MEMBRANE PARE-VAPEUR AUTOCOLLANTE.

18

MEMBRANE AUTOCOLLANTE.

19

PLIAGE DE TOLE EN ACIER GALVANIS  , CAL.22.

20

RIVET EN ACIER INOXYDABLE.

21

POUTRE D'ACIER. VOIR STRUCTURE.

22

ENLEVER L'ISOLANT DE LAINE DE FIBRE DE VERRE SUR 610mm POUR LA R  ALISATION DES TRAVAUX.

23

PLIAGE DE TOLE EN "J" CAL.18 EN ACIER GALVANIS  .

24

MEMBRANE SOUS-COUCHE.

25

MEMBRANE DE FINITION GRANUL  E.

26

PLAQUE D'ACIER PONCTUELLE. VOIR STRUCTURE.

27

MOULURE EN "J" EN ACIER   MAILL  , CAL.24.

28

LISSE DE D  FLEXION. VOIR STRUCTURE.

29

RAGRE  R LA TOITURE TEL QUE L'EXISTANT. VOIR COMPOSITION DE TOIT SUR LE D  TAIL. VOIR PLAN DE STRUCTURE POUR LES MODIFICATIONS   LA STRUCTURE DE LA TOITURE VENTIL  E.

30

CONNECTEUR   CHAQUE COLOMBAGES OU BARRE "Z" SELON LE CAS. VOIR STRUCTURE.

31

TOLE D'APPUI EN ACIER GALVANIS   CAL.18. PENTE 10  .

32

CHEVAUCHER LA NOUVELLE MEMBRANE SUR LES MEMBRANES DE LA TOITURE EXISTANTE SUR MINIMUM 150mm. D  GRANULER LA MEMBRANE EXISTANTE AU PR  ALABLE.

33

BARRE D'ANCRAGE DE LA MEMBRANE.

34

TOLE D'APPUI EN ACIER GALVANIS   CAL.18.

35

PLIAGE DE TOLE EN "U", CAL.16 EN ACIER GALVANIS  .

36

NOUVEL ISOLANT EN LAINE DE FIBRE DE VERRE, DEUX RANGS DE 150mm SUR 610mm DE LARGEUR.

37

OUVERTURE   FAIRE DANS LA TOITURE EXISTANTE SUR  600mm POUR LA CONSTRUCTION DU NOUVEAU MUR. VOIR COMPOSITION DE TOIT SUR LE D  TAIL. VOIR PLAN DE STRUCTURE POUR LES MODIFICATIONS   LA STRUCTURE DE LA TOITURE VENTIL  E.

38

PLIAGE DE TOLE, CAL.16 EN ACIER GALVANIS  , FIX   SUR LE DESSUS DU PARAPET EXISTANT.

39

MOUSTIQUAIRE.

40

CALE D'AJUSTEMENT EN ACIER GALVANIS   D'  PAISSEUR REQUISE.

41

TOLE D'APPUI EN ACIER GALVANIS   CAL.18.

42

SCELLER LA MEMBRANE PARE-INT  MP  RIES SUR LE SOLIN AVEC UN RUBAN AUTOCOLLANT.

43

SCELLER LA MEMBRANE PARE-INT  MP  RIES SUR LE PARAPET AVEC UN RUBAN AUTOCOLLANT.

44

AGRAFE EN ACIER GALVANIS  , CAL.24 CONTINUE.

45

JOINT DE DILATATION MONOLITHIQUE D'  TANCH  IT  .

46

MEMBRANE DE RENFORT.

47

SURPLUS DE MEMBRANE.

48

SCELLER LA MEMBRANE PARE-INT  MP  RIES SUR LA MEMBRANE DE RENFORT AVEC UN RUBAN AUTOCOLLANT.

49

BOUT DU PANNEAU REPLI   VERS L'INT  RIEUR.

50

PANNEAU DE MAT DE FIBRE DE VERRE 16mm TYPE X.

L  GENDE

EXISTANT   CONSERVER.

  L  MENT   DEMOLIR.

AXE EXISTANT

EXT  RIEUR DE LA STRUCTURE DE B  TON EXISTANTE DE LA TOUR.

NOUVEL AXE: FACE EXT  RIEURE DES BARRES Z ET COLOMBAGES DE LA TOUR. VOIR STRUCTURE.

(*) VOIR NOTE G  N  RALE PAGE 400.

NE DOIT PAS SERVIR   L'EX  CUTION

Le pr  sent document est  mis pour la seule fin identifi  e. Son contenu est prot  g   par les droits d'auteur et toute reproduction ou modification, partielle ou totale, est interdite sans l'autorisation  crite de gagnon, letellier, cyr, ricard, mathieu, proulx, savard consortium d'architectes.

GLC RM

Proulx Savard Architectes

GLCRM | Proulx Savard |

GLCRM:
128, Avenue de la Cath  drale,
Bureau 201
Rimouski, QC, G5L 5H7
(418) 722-7655

2406, Ch. des Quatres-Bourgeois,
Bureau 100
Qu  bec, QC, G1V 1W5
(418) 647-1700

Proulx Savard Architectes:
75, boul. Arthur-Buies Ouest,
Rimouski QC G5L 5C2
(418) 722-5543

ARCHITECTURE

CONSULTANTS

Oire des architectes
A-3996
DAVID SAVARD
ARCHITECTE
du Qu  bec

Oire des architectes
A-3726
FRAN  OIS MATHIEU
ARCHITECTE
du Qu  bec

DOSSIER NO:
24-187 / 687-24

DATE
SEPTEMBRE 2024

DESIGNATEUR (S)
DB AL
  CHELLE
INDIQU  E

DEFINIES POUR SOUMISSION
DEFINIES 100% POUR APPROBATION
DEFINIES 80% POUR APPROBATION
DEFINIES 40% POUR APPROBATION
PRELIMINAIRES 20% POUR APPROBATION

REVISIONS

COUPE DE MUR TYPE
DEMOLITION ET CONSTRUCTION

PROJET
H  PITAL DE CHANDLER,
Chandler
(Ref  ction de l'enveloppe)

PROPRI  TAIRE
Sant   Qu  bec

418