

PROJET

HÔPITAL DE CHANDLER, Chandler (Réfection de l'enveloppe)

PROPRIÉTAIRE



LISTE DES PLANS

PLAN DU SITE	000
--------------	-----

- 001 PLAN D'IMPLANTATION
- 002 GESTION DE CHANTIER DÉTAILLÉ
- 005 ÉTUDE DE CODE ET NOTES GÉNÉRALES

PHASAGE DES TRAVAUX	010
---------------------	-----

- 010 PLANS DES NIVEAUX - IDENTIFICATION DES ZONES DE TRAVAUX
- 011 ÉLÉVATIONS - IDENTIFICATION DES ZONES DE TRAVAUX

PLANS DES NIVEAUX - DÉMOLITION	050
--------------------------------	-----

- 050 PLAN DU SOUS-SOL - DÉMOLITION
- 051 PLAN DU REZ-DE-CHAUSSÉE - DÉMOLITION
- 052 PLAN DU NIVEAU 100 - DÉMOLITION
- 053 PLAN DU NIVEAU 200 - DÉMOLITION
- 054 PLANS DES NIVEAUX 300 ET 400 - DÉMOLITION

PLANS DES NIVEAUX - CONSTRUCTION	100
----------------------------------	-----

- 100 PLAN DU SOUS-SOL - CONSTRUCTION
- 101 PLAN DU REZ-DE-CHAUSSÉE - CONSTRUCTION
- 102 PLAN DU NIVEAU 100 - CONSTRUCTION
- 103 PLAN DU NIVEAU 200 - CONSTRUCTION
- 104 PLANS DES NIVEAUX 300 ET 400 - CONSTRUCTION

ÉLÉVATIONS DU BÂTIMENT	200
------------------------	-----

- 201 ÉLÉVATIONS - DÉMOLITION
- 201-A ÉLÉVATIONS - DÉMOLITION
- 202 ÉLÉVATIONS - DÉMOLITION
- 203 ÉLÉVATIONS - CONSTRUCTION
- 204 ÉLÉVATIONS - CONSTRUCTION
- 205 DÉTAILS TYPES MOULURES PAREMENTS TYPES

PLAN DES TOITURES ET DÉTAILS DE TOITURE	300
---	-----

- 301 PLAN DES TOITURES - DÉMOLITION
- 302 PLAN DES TOITURES - CONSTRUCTION
- 303 PLAN DES SOFFITES - DÉMOLITION
- 304 PLAN DES SOFFITES - CONSTRUCTION
- 305 DÉTAILS TOITURES - DÉMOLITION ET CONSTRUCTION
- 306 DÉTAILS TOITURES - DÉMOLITION ET CONSTRUCTION

COUPES DE MURS TYPES	400
----------------------	-----

- 400 COMPOSITIONS TYPES
- 401 COUPE DE MUR TYPE
- 402 COUPE DE MUR TYPE

COUPES DE MURS TYPES (SUITE)	400
------------------------------	-----

- 403 COUPE DE MUR TYPE
- 404 COUPE DE MUR TYPE
- 405 COUPE DE MUR TYPE
- 406 COUPE DE MUR TYPE
- 407 COUPE DE MUR TYPE

COUPES DE MUR AGRANDIES ET DÉTAILS	410
------------------------------------	-----

- 410 COUPE DE MUR TYPE AGRANDI DÉMOLITION ET CONSTRUCTION
- 411 COUPE DE MUR TYPE AGRANDI DÉMOLITION ET CONSTRUCTION
- 412 COUPE DE MUR TYPE AGRANDI DÉMOLITION ET CONSTRUCTION
- 413 COUPE DE MUR TYPE AGRANDI DÉMOLITION ET CONSTRUCTION
- 414 COUPE DE MUR TYPE AGRANDI DÉMOLITION ET CONSTRUCTION
- 415 COUPE DE MUR TYPE AGRANDI DÉMOLITION ET CONSTRUCTION
- 416 COUPE DE MUR TYPE AGRANDI DÉMOLITION ET CONSTRUCTION
- 417 COUPE DE MUR TYPE AGRANDI DÉMOLITION ET CONSTRUCTION
- 418 COUPE DE MUR TYPE AGRANDI DÉMOLITION ET CONSTRUCTION
- 419 COUPE DE MUR TYPE AGRANDI DÉMOLITION ET CONSTRUCTION
- 420 COUPE ET DÉTAIL TYPE AGRANDI DÉMOLITION ET CONSTRUCTION
- 421 DÉTAIL TYPE AGRANDI DÉMOLITION ET CONSTRUCTION
- 422 COUPE - PERSIENNE DÉMOLITION ET CONSTRUCTION

DÉTAILS EN PLAN	450
-----------------	-----

- 451 DÉTAILS EN PLAN - DÉMOLITION ET CONSTRUCTION
- 452 DÉTAILS EN PLAN - DÉMOLITION ET CONSTRUCTION
- 453 DÉTAILS EN PLAN - DÉMOLITION ET CONSTRUCTION
- 454 DÉTAILS EN PLAN - DÉMOLITION ET CONSTRUCTION
- 455 DÉTAILS EN PLAN - DÉMOLITION ET CONSTRUCTION

ÉLÉVATIONS ET DÉTAILS DE FENÊTRES	500
-----------------------------------	-----

- 501 ÉLÉVATIONS TYPES DES FENÊTRES ET MURS RIDEAUX
- 502 ÉLÉVATIONS - IDENTIFICATION DES DÉTAILS DES FENÊTRES DÉMOLITION
- 503 ÉLÉVATIONS - IDENTIFICATION DES DÉTAILS DES FENÊTRES CONSTRUCTION

ÉLÉVATIONS ET DÉTAILS DE FENÊTRES (SUITE)	500
---	-----

- 504 DÉTAIL FENÊTRE À OBTURER ESCALIER #3
- 505 DÉTAIL TYPE DU PRINCIPE DE REMPLACEMENT DES FENÊTRES DÉMOLITION ET CONSTRUCTION EN 2 ÉTAPES
- 506 DÉTAIL TYPE DE FENÊTRE (TOUR) DÉMOLITION ET CONSTRUCTION
- 507 DÉTAIL TYPE DE FENÊTRE (TOUR) DÉMOLITION ET CONSTRUCTION
- 508 DÉTAIL DE FENÊTRE (BASILAIRE) DÉMOLITION ET CONSTRUCTION
- 509 DÉTAIL DE FENÊTRE (BASILAIRE) DÉMOLITION ET CONSTRUCTION
- 510 DÉTAIL DE FENÊTRE (BASILAIRE) DÉMOLITION ET CONSTRUCTION
- 511 DÉTAIL DE FENÊTRE (BASILAIRE) DÉMOLITION ET CONSTRUCTION
- 512 DÉTAIL DE FENÊTRE (BASILAIRE) DÉMOLITION ET CONSTRUCTION
- 513 DÉTAIL DE FENÊTRE (BASILAIRE) DÉMOLITION ET CONSTRUCTION

DÉTAILS DE PORTES	600
-------------------	-----

- 601 DÉTAILS DE PORTE - DÉMOLITION ET CONSTRUCTION
- 602 DÉTAILS DE PORTE - DÉMOLITION ET CONSTRUCTION
- 603 DÉTAILS DE PORTE - DÉMOLITION ET CONSTRUCTION
- 604 DÉTAILS DE PORTE - DÉMOLITION ET CONSTRUCTION
- 605 DÉTAILS DE PORTE - DÉMOLITION ET CONSTRUCTION
- 606 DÉTAILS DE PORTE - DÉMOLITION ET CONSTRUCTION
- 607 DÉTAILS DE PORTE - DÉMOLITION ET CONSTRUCTION

MÉTAUX OUVRÉS	700
---------------	-----

- 701 MÉTAUX OUVRÉS
- 702 MÉTAUX OUVRÉS
- 703 MÉTAUX OUVRÉS
- 704 MÉTAUX OUVRÉS
- 705 MÉTAUX OUVRÉS



BÂTIMENT EXISTANT



PERSPECTIVE PROJETÉ




GLCRM | Proulx Savard |

GLCRM:
128, Avenue de la Cathédrale,
Bureau 201
Rimouski, QC, G5L 5H7
(418) 722-7655

2406, Ch. des Quatres-Bourgeois,
Bureau 100
Québec, QC, G1V 1W5
(418) 647-1700

Proulx Savard Architectes:
75, boul. Arthur-Buies Ouest,
Rimouski QC G5L 5C2
(418) 723-5543

ARCHITECTURE

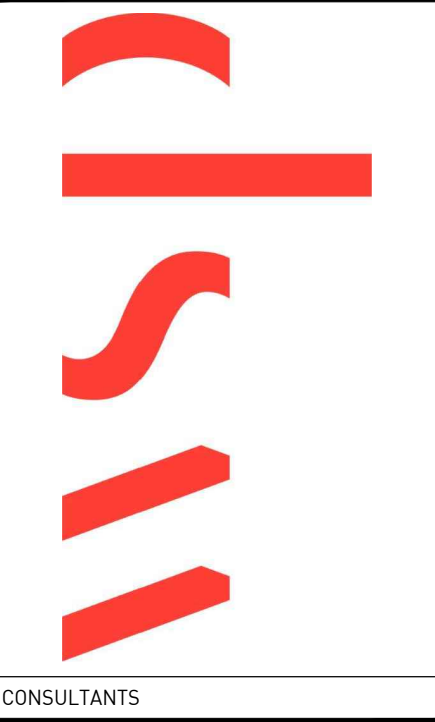


CONSULTANTS

ARCHITECTURE

DÉFINITIFS POUR SOUMISSION

4 SEPTEMBRE 2026

DOSSIER: 24-108 / R657-24

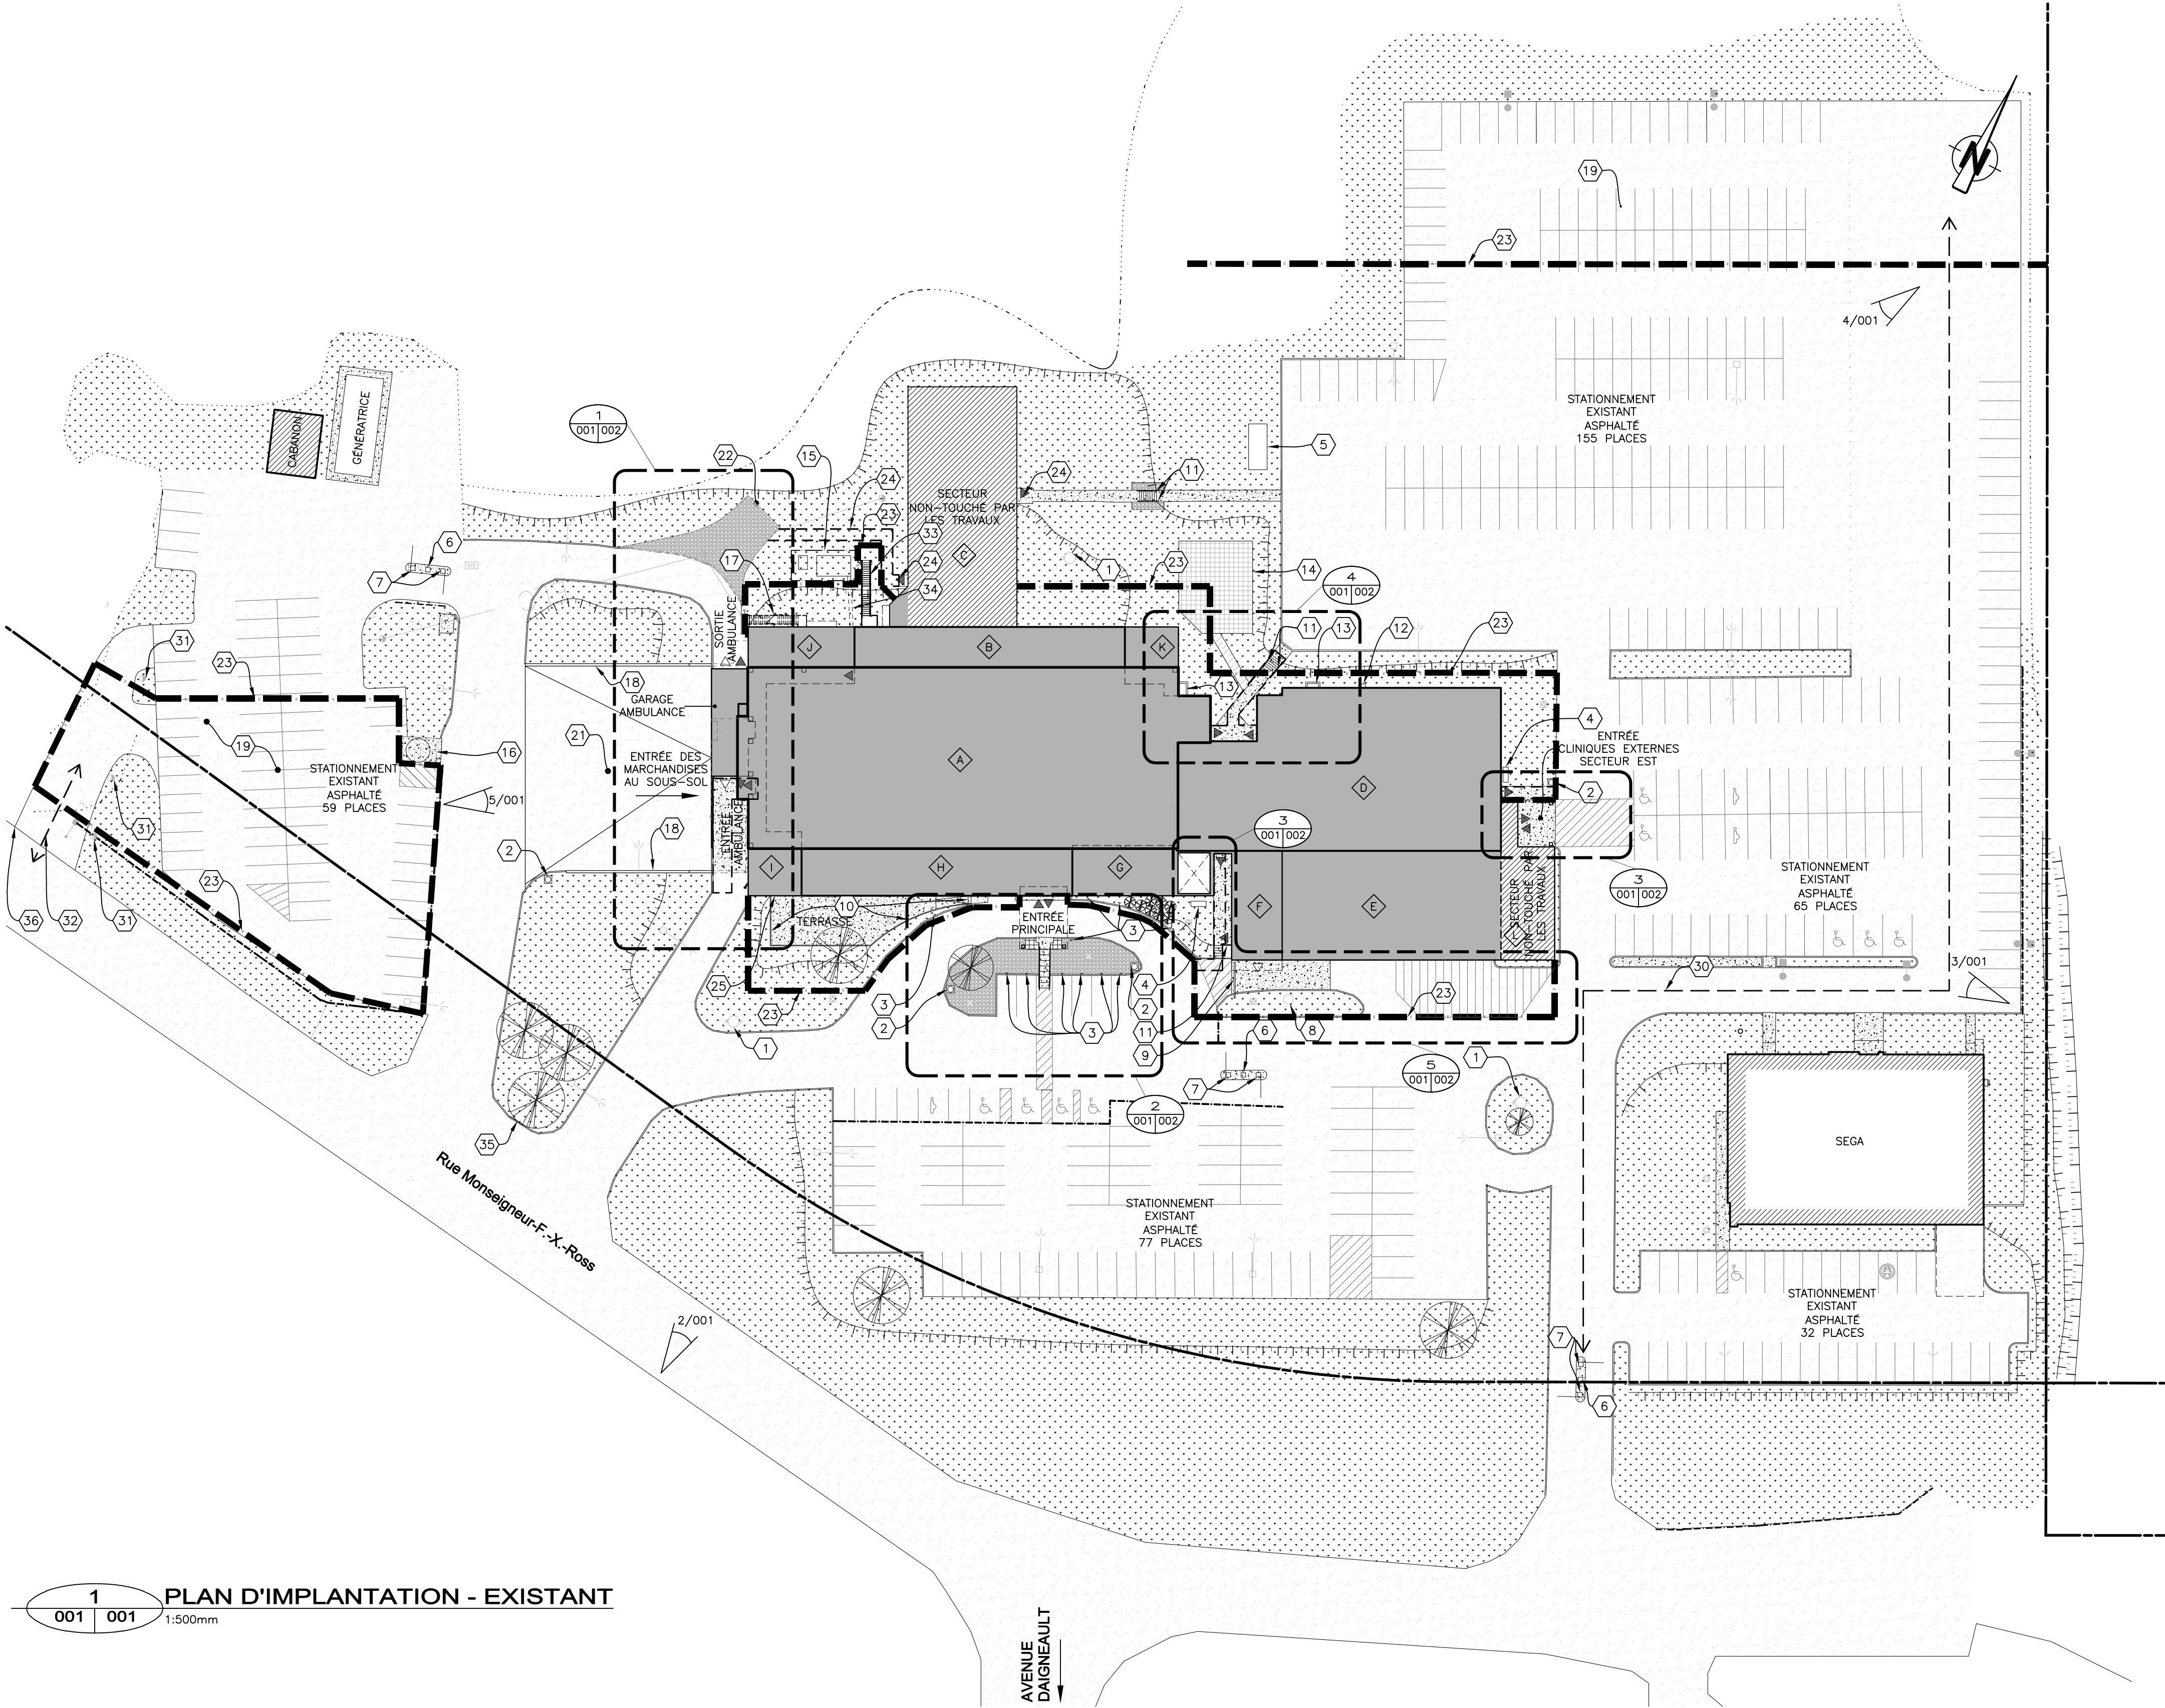

1 PLAN D'IMPLANTATION - EXISTANT
001 001 1:500mm



2 PHOTOGRAPHIE 1
001 001 1:1mm



3 PHOTOGRAPHIE 2
001 001 1:1mm



4 PHOTOGRAPHIE 3
001 001 1:1mm



5 PHOTOGRAPHIE 4
001 001 1:1mm

LÉGENDE

- (X) NOTE DESCRIPTIVE.
- LIGNE DE LOT.
- BAS DE TALUS.
- HAUT DE TALUS.
- SECTION NON TOUCHÉ PAR LES TRAVAUX.
- SECTEUR TOUCHÉ PAR LES TRAVAUX.
- ASPHALTE EXISTANT À CONSERVER ET À RAGRÉER À LA FIN DES TRAVAUX (VOIR NOTE CI-CONTRE).
- BÉTON EXISTANT À CONSERVER ET À RAGRÉER À LA FIN DES TRAVAUX (VOIR NOTE CI-CONTRE).
- GRAVIER EXISTANT À CONSERVER.
- TROTTOIR DE BOIS EXISTANT À CONSERVER ET À RAGRÉER À LA FIN DES TRAVAUX (VOIR NOTE CI-CONTRE).
- GAZON EXISTANT À CONSERVER ET À RAGRÉER À LA FIN DES TRAVAUX (VOIR NOTE CI-CONTRE).
- DALLAGE EXISTANT À CONSERVER ET À RAGRÉER À LA FIN DES TRAVAUX (VOIR NOTE CI-CONTRE).
- PORTE DE GARAGE ACCÈS AU BÂTIMENT.
- ISSUE / ACCÈS AU BÂTIMENT. (PROTECTION DURANT LE CHANTIER)
- CLÔTURE DE CHANTIER 1830MM DE HAUTEUR À ÉRIGER PAR L'ENTREPRENEUR POUR DÉLIMITER LA ZONE DE CHANTIER.
- GLISSIÈRE DE SÉCURITÉ (GARDE-FOU) EXISTANTE À CONSERVER.
- LAMPADAIRE EXISTANT À CONSERVER ET PROTÉGER PENDANT LES TRAVAUX.
- POTEAU ÉLECTRIQUE EXISTANT À CONSERVER ET PROTÉGER PENDANT LES TRAVAUX.
- ARBRE OU ARBUSTE EXISTANT À CONSERVER.
- CONTENEUR À DÉCHETS / RECYCLAGE.
- STATIONNEMENT POUR PERSONNE À MOBILITÉ RÉDUITE.
- STATIONNEMENT POUR VOITURE ÉLECTRIQUE.
- STATIONNEMENT POUR FAMILLE.
- FLECHE DE CIRCULATION.
- ZONE PROTÉGÉE.

LÉGENDE DES ZONES

- A TOUR CHAMBRES (NIVEAU 200,300 ET 400) (1974).
- B LABORATOIRE (NIVEAU 100)(1990).
- C ARCHIVES (REZ-DE-CHAUSSEE)(2001).
- D ADMINISTRATIVE (NIVEAU 100) (2005) ET CLINIQUES EXTERNES (REZ-DE-CHAUSSEE) (1974)
- E ONCOLOGIE (REZ-DE-CHAUSSEE) (1974).
- F IRM (REZ-DE-CHAUSSEE) (2007)
- G BASILAIRE SUD-EST(1974)
- H CLINIQUE CHIRURGIE D'UN JOUR (NIVEAU 100) (2005)ET URGENCE (REZ-DE-CHAUSSEE)
- I BASILAIRE SUD-OUEST (1974)
- J BASILAIRE NORD-OUEST (1974)
- K BASILAIRE NORD-EST (1974)
- L ONCOLOGIE (REZ-DE-CHAUSSEE) (2023)

TERMINOLOGIE

- TOUR (NIVEAUX 200, 300, 400 ET CABANON AU TOIT).
- BASILAIRE (NIVEAUX SOUS-SOL, REZ-DE-CHAUSSEE ET NIVEAU 100.

NOTES

- BORNE FONTAINE EXISTANTE. CONSERVER UN ACCÈS POMPIER À LA BORNE EN TOUT TEMPS PENDANT LA DURÉE DES TRAVAUX.
- POUBELLE EXISTANTE. À CONSERVER ET PROTÉGER PENDANT LES TRAVAUX.
- PANNEAU INDICATEUR EXISTANT À CONSERVER ET PROTÉGER PENDANT LES TRAVAUX.
- SUPPORT À VÉLO EXISTANT À REMETTRE AU PROPRIÉTAIRE.
- CONTENEUR À VÉLO.
- BORNE DE PAIEMENT POUR LE STATIONNEMENT EXISTANTE. À CONSERVER ET PROTÉGER PENDANT LES TRAVAUX.
- GUÉRITE EXISTANTE À CONSERVER ET PROTÉGER PENDANT LES TRAVAUX.
- MAT DE DRAPEAU EXISTANT À CONSERVER ET PROTÉGER PENDANT LES TRAVAUX.
- BARRIÈRE MÉTALLIQUE À BATTANT EXISTANTE À CONSERVER ET PROTÉGER PENDANT LES TRAVAUX.
- GARDE-CORPS EXISTANT À DÉMONTÉ ET ENTREPOSER PENDANT LES TRAVAUX POUR RÉINSTALLATION FUTURE, VOIR FEUILLES DE LA SÉRIE 700 POUR LES INTERVENTIONS SUR LES MÉTAUX-OUVRÉS EXISTANTS.
- GARDE-CORPS EXISTANT À CONSERVER ET PROTÉGER PENDANT LES TRAVAUX.
- COL DE CYGNE EXISTANT, VOIR DOCUMENTS D'INGÉNIEURIE.
- SAUT DE LOUP EXISTANT, VOIR DOCUMENTS D'INGÉNIEURIE.
- TERRASSE EXISTANTE À CONSERVER ET PROTÉGER PENDANT LES TRAVAUX.
- ENCLÔT POUR APPARELS ÉLECTRIQUES HAUTE TENSION EXISTANT À CONSERVER ET PROTÉGER PENDANT LES TRAVAUX. REMPLACER LE CÔTÉ DE LA CLÔTURE ADJACENT AU NOUVEL ESCALIER, PAR UNE SECTION DE CLÔTURE PLUS HAUTE, VOIR COUPE DE L'ESCALIER #7 SUR LA FEUILLE 705.
- ENCLÔT POUR RESERVOIR DE GAZ EXISTANT À CONSERVER ET PROTÉGER PENDANT LES TRAVAUX.
- ESCALIER EXISTANT À DÉMOLIR.
- MUR DE BÉTON EN PENTE AVEC GARDE-CORPS EXISTANTS À CONSERVER.
- CASE DE STATIONNEMENT ET ESPACE RÉSERVÉ POUR L'ENTREPRENEUR.
- ZONE DE DÉBARCADE POUR L'ENTREPRENEUR. COORDONNER AVEC L'ÉTABLISSEMENT POUR LES PÉRIODES DE TRAVAUX.
- CHEMIN EN GRAVIER TEMPORAIRE PENDANT LES TRAVAUX. REMETTRE LE TERRAIN DANS SON ÉTAT ORIGINAL APRÈS LES TRAVAUX. VOIR CIVIL.
- ZONE DE CHANTIER CLÔTURER.
- PORTE D'ISSUE EXTERIEURE ET CHEMIN D'ÉVACUATION À MAINTENIR OPÉRATIONNELLE. LIBRE D'OBSTRUCTION DURANT LE CHANTIER. ASSURER UN PASSAGE D'ISSUE EXTERIEURE DE 1650mm MINIMUM LIBRE, PROTÉGÉ, DÉGAGÉ ET LIBRE DE LA PORTE JUSQU'À LA VOIE PUBLIQUE.
- PORTE EXTERIEURE HORS SERVICE PENDANT LES TRAVAUX.
- COORDONNER AVEC L'ÉTABLISSEMENT POUR LES TEMPS DE TRAVAUX SOUS LA MARQUISE ET AUTOUR DES PORTES. L'ENTREPRENEUR DOIT PROPOSER UN PLAN D'ACTION POUR ASSURER L'ÉVACUATION EN CAS D'URGENCE ET L'ACCESSIBILITÉ DE L'ENTRÉE PRINCIPALE.
- ZONE RÉSERVÉ À L'IRM (IMAGERIE PAR RÉSONANCE MAGNÉTIQUE), COORDONNER AVEC L'ÉTABLISSEMENT POUR LES TEMPS DES TRAVAUX. AUCUN ÉLÉMENT OU ENTREPOSAGE MÉTALLIQUE SERA PERMIS DANS CETTE ZONE LORSQUE L'IRM EST EN SERVICE.
- COORDONNER AVEC L'ÉTABLISSEMENT POUR LES SERVICES DE LA PORTE IRM.
- POUR LES TRAVAUX AUTOURS DES PORTES D'ISSUE QUI POURRAIENT NUIRE À L'ÉVACUATION EN CAS D'URGENCE, L'ENTREPRENEUR DOIT PROPOSER UN PLAN D'ACTION POUR ASSURER LA SÉCURITÉ D'ÉVACUATION ET COORDONNER AVEC L'ÉTABLISSEMENT AVANT LE DÉBUT DES TRAVAUX.
- ACCÈS GÉNÉRAL AU CHANTIER POUR L'ENTREPRENEUR. COORDONNER AVEC L'ÉTABLISSEMENT POUR LA GESTION DES FLUX DE CIRCULATION ENTRE L'ENTREPRENEUR ET LA CLIENTÈLE.
- POTEAU D'ÉLECTRICITÉ EXISTANT À CONSERVER ET PROTÉGER DURANT LES TRAVAUX.
- ACCÈS AU CHANTIER POUR L'ENTREPRENEUR.
- NOUVEL ESCALIER, VOIR DÉTAILS DE LA FEUILLE 705.
- CÂBLAGE ÉLECTRIQUE SOUTERRAIN EXISTANT DANS CETTE ZONE, VOIR DOCUMENTS D'INGÉNIEURIE. PRENDRE TOUTES LES PRÉCAUTIONS REQUIS LORS DE L'EXCAVATION ET DES TRAVAUX DE CONSTRUCTION DU NOUVEL ESCALIER POUR ÉVITER ET PROTÉGER LE CÂBLAGE EXISTANT.
- PANNEAU INDICATEUR TEMPORAIRE POUR L'ENTRÉE DES AMBULANCES. PRÉVOIR DEUX PANNEAUX AVEC UNE FLECHE INDICANT L'ENTRÉE DES AMBULANCES. UN PANNEAU PAR PHASE DE TRAVAUX DU SECTEUR AMBULANCES DONT L'ENTRÉE NE SE FERA PAS AU MEME ENDROIT. COORDONNER L'EMPLACEMENT, LA DIMENSION ET LE TEXTE DES PANNEAUX TEMPORAIRES AVEC L'ÉTABLISSEMENT.
- PISTE CYCLABLE EXISTANTE. COORDONNER AVEC L'ÉTABLISSEMENT ET LA VILLE POUR ASSURER LA SÉCURITÉ DE CIRCULATION.

NE DOIT PAS SERVIR À L'EXÉCUTION

Le présent document est émis pour la seule fin identifiée. Son contenu est protégé par les droits d'auteur et toute reproduction ou modification, partielle ou totale, est interdite sans l'autorisation écrite de gagnon, letelier, cyr, ricard, mathieu, proulx, savard consortium d'architectes.




GLCRM | Proulx Savard |

GLCRM:
128, Avenue de la Cathédrale,
Bureau 201
Rimouski, QC, G5L 5H7
(418) 722-7655



2406, Ch. des Quatres-Bourgeois,
Bureau 100
Québec, QC, G1V 1W5
(418) 647-1700

Proulx Savard Architectes:
75, boul. Arthur-Buies Ouest,
Rimouski QC G5L 5C2
(418) 722-5543

ARCHITECTURE

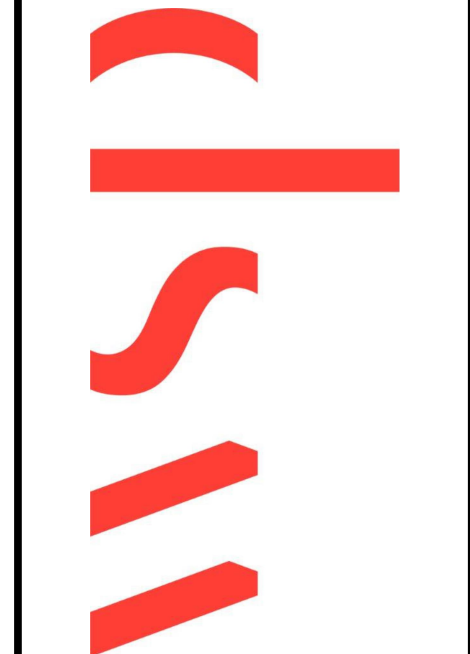


CONSULTANTS

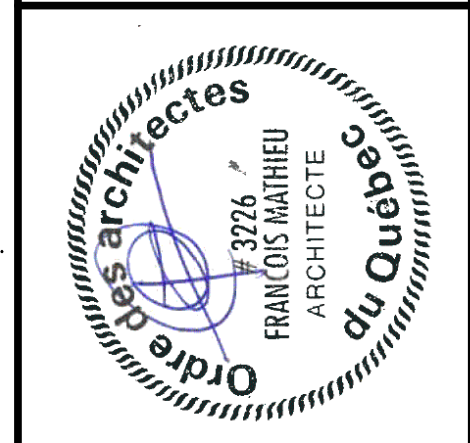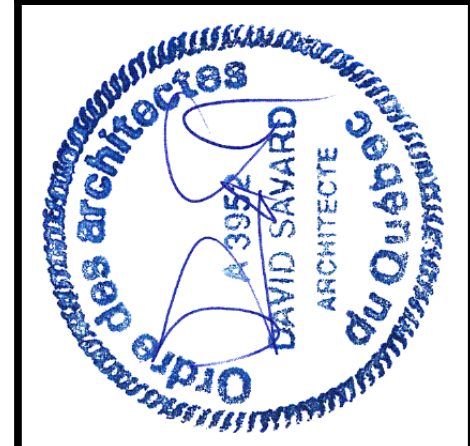


DOSSIER No.		DATE		REVISIONS	
DESSINATEUR (S)	J.L. A.C. A.B.	ÉCHELLE	INDIQUÉE	DATE	No
PROJET	HÔPITAL DE CHANDLER, Chandler (Réfection de l'enveloppe)	PROPRIÉTAIRE	Santé Québec	2024-09-04	05
DESSIN	PLAN D'IMPLANTATION	J.L. A.C. A.B.	ÉCHELLE	INDIQUÉE	No

001

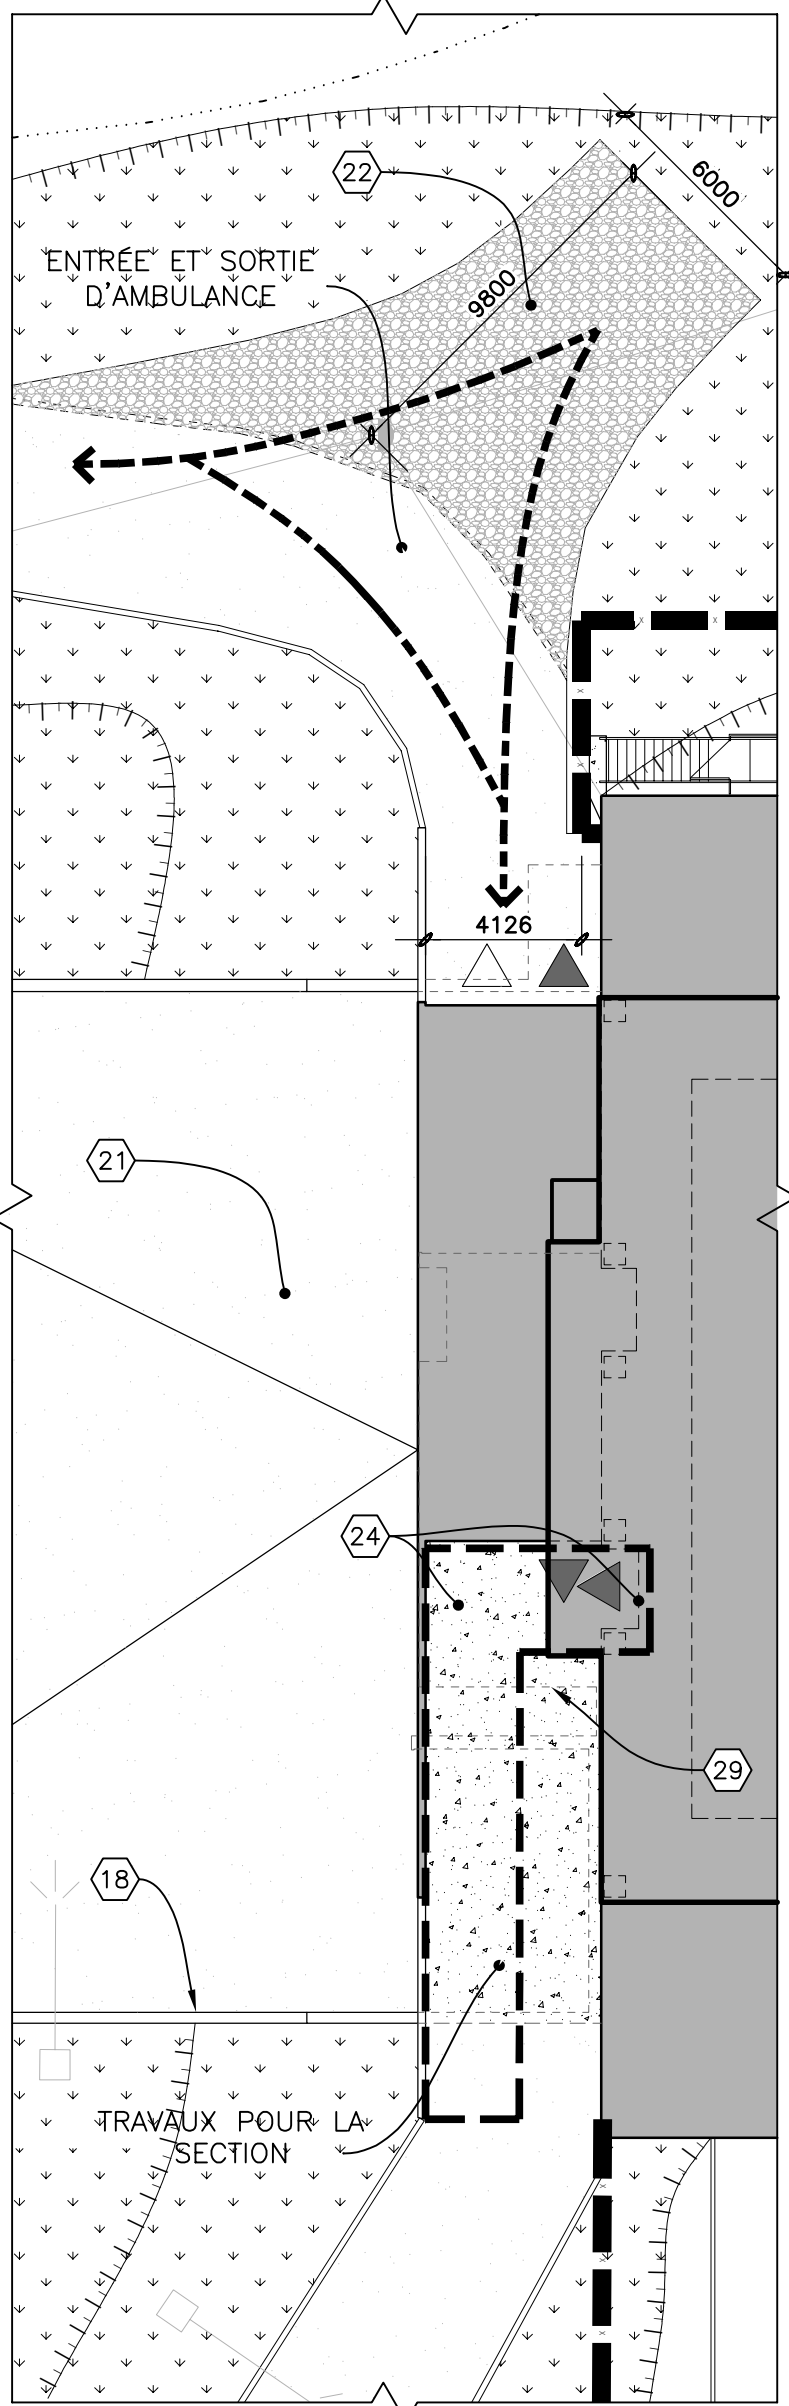


PHASE 1


1
001 002
1:200mm
GESTION POUR LA ZONE D'AMBULANCE

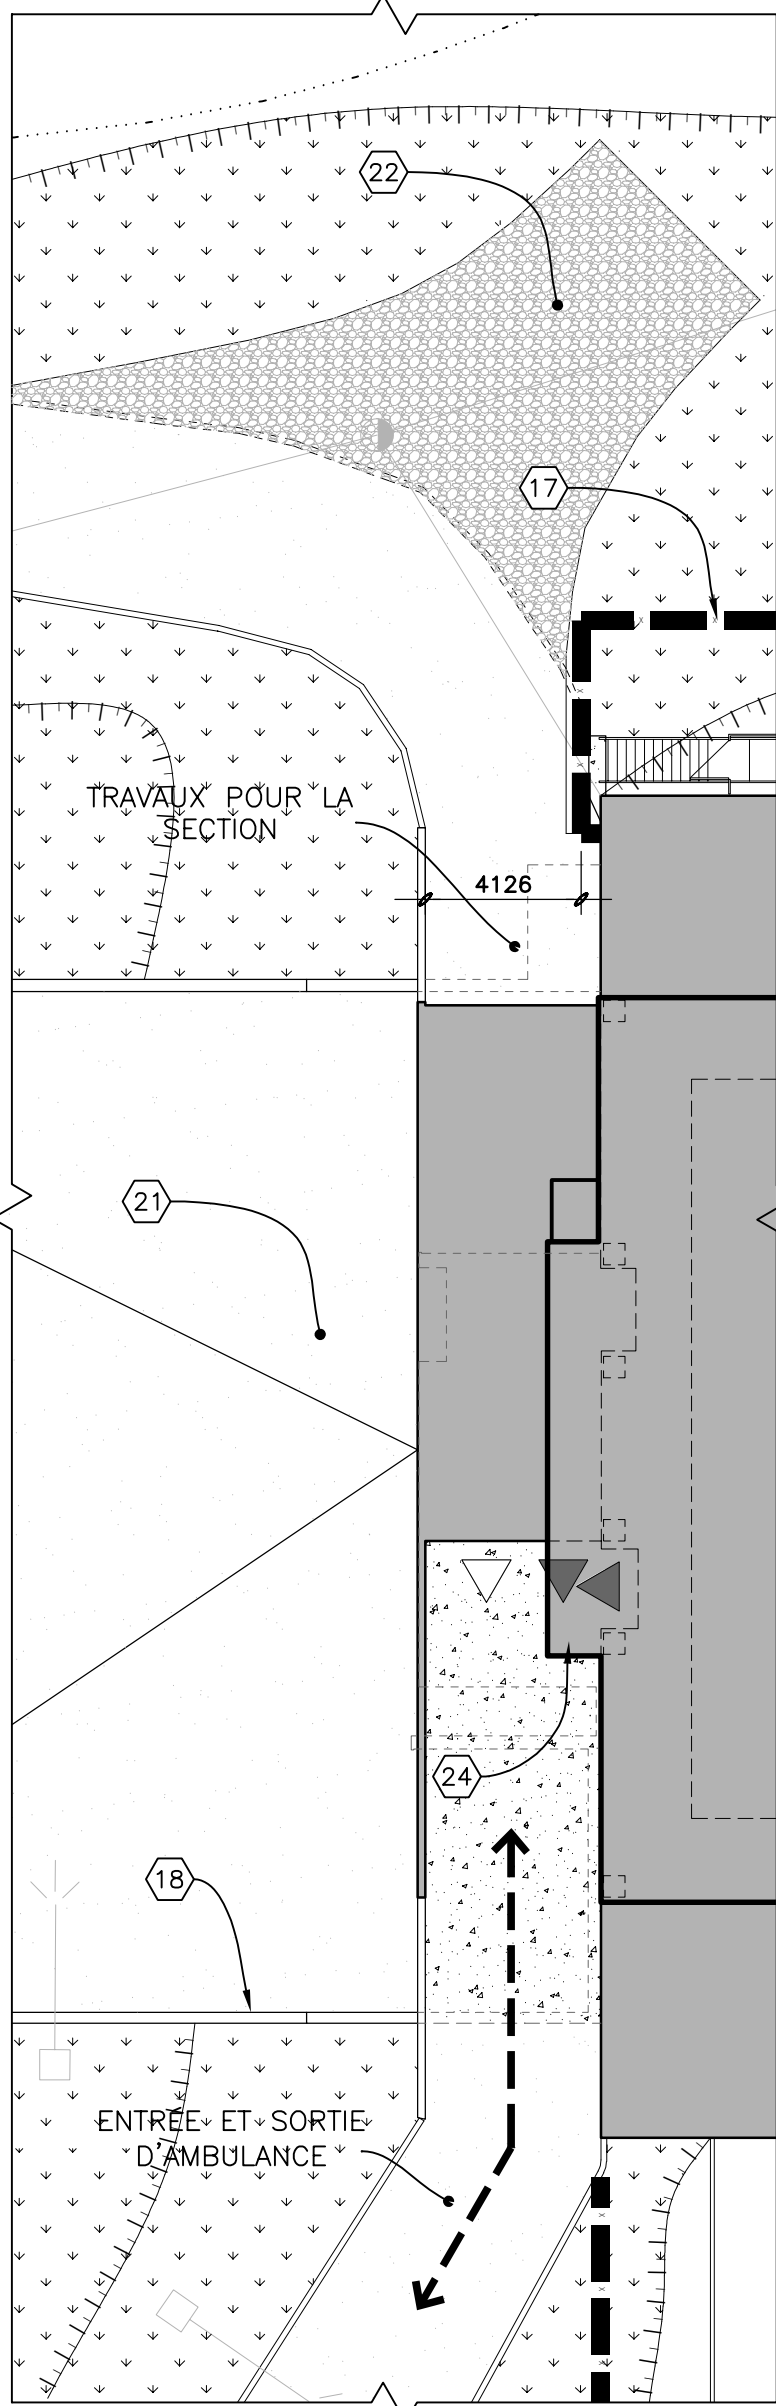


PHASE 2

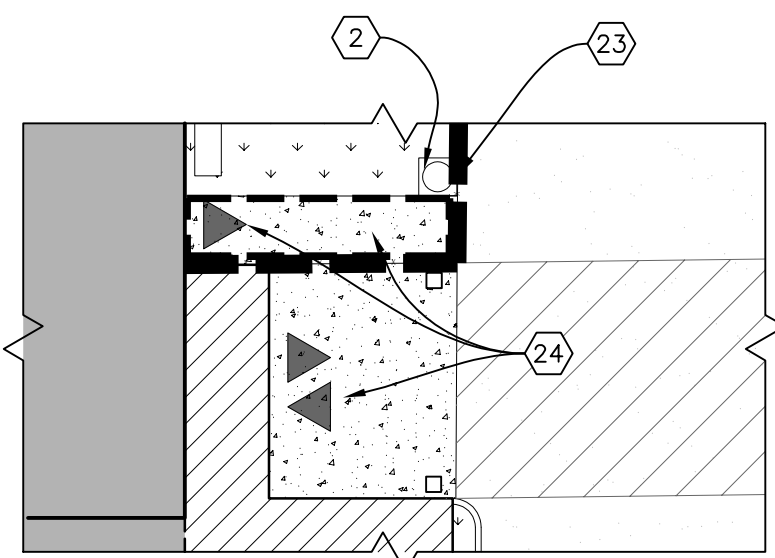


3
001 002
1:200mm
GESTION D'ENTRÉE

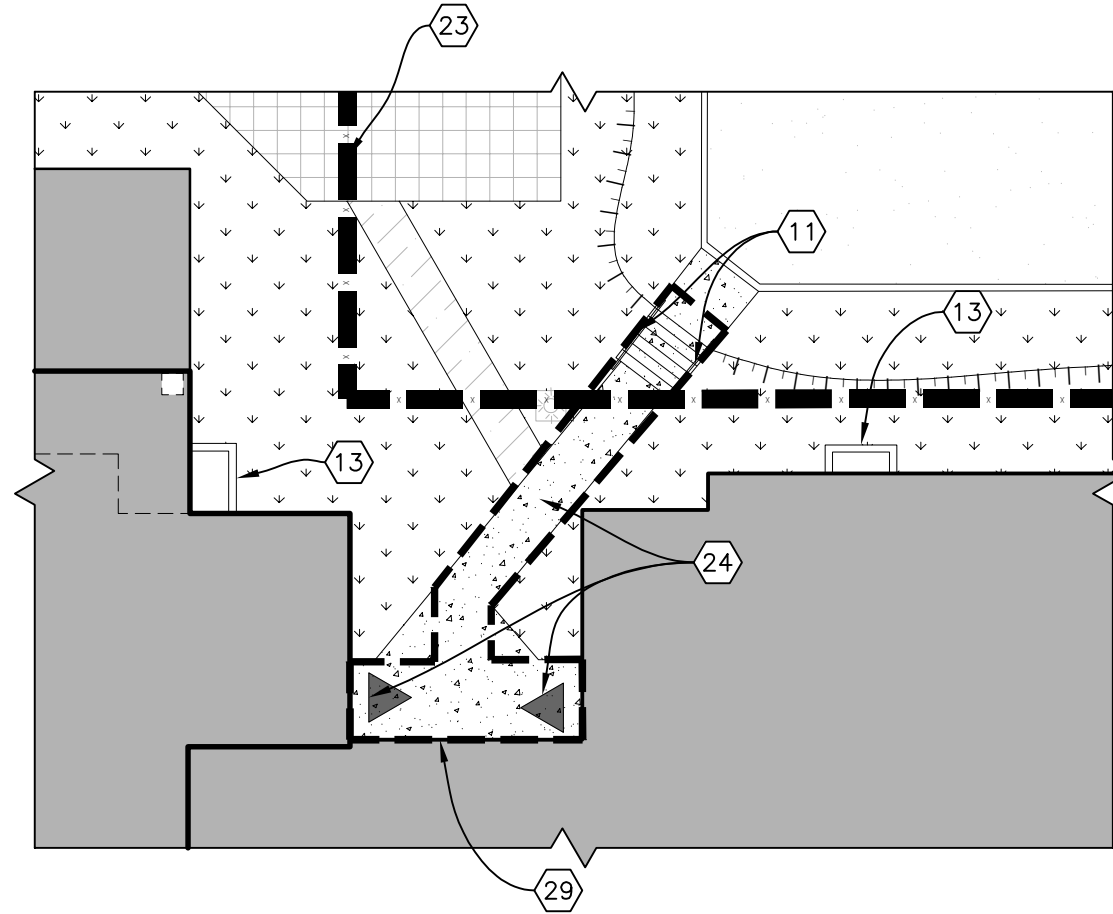


4
001 002
1:200mm
GESTION D'ÉVACUATION

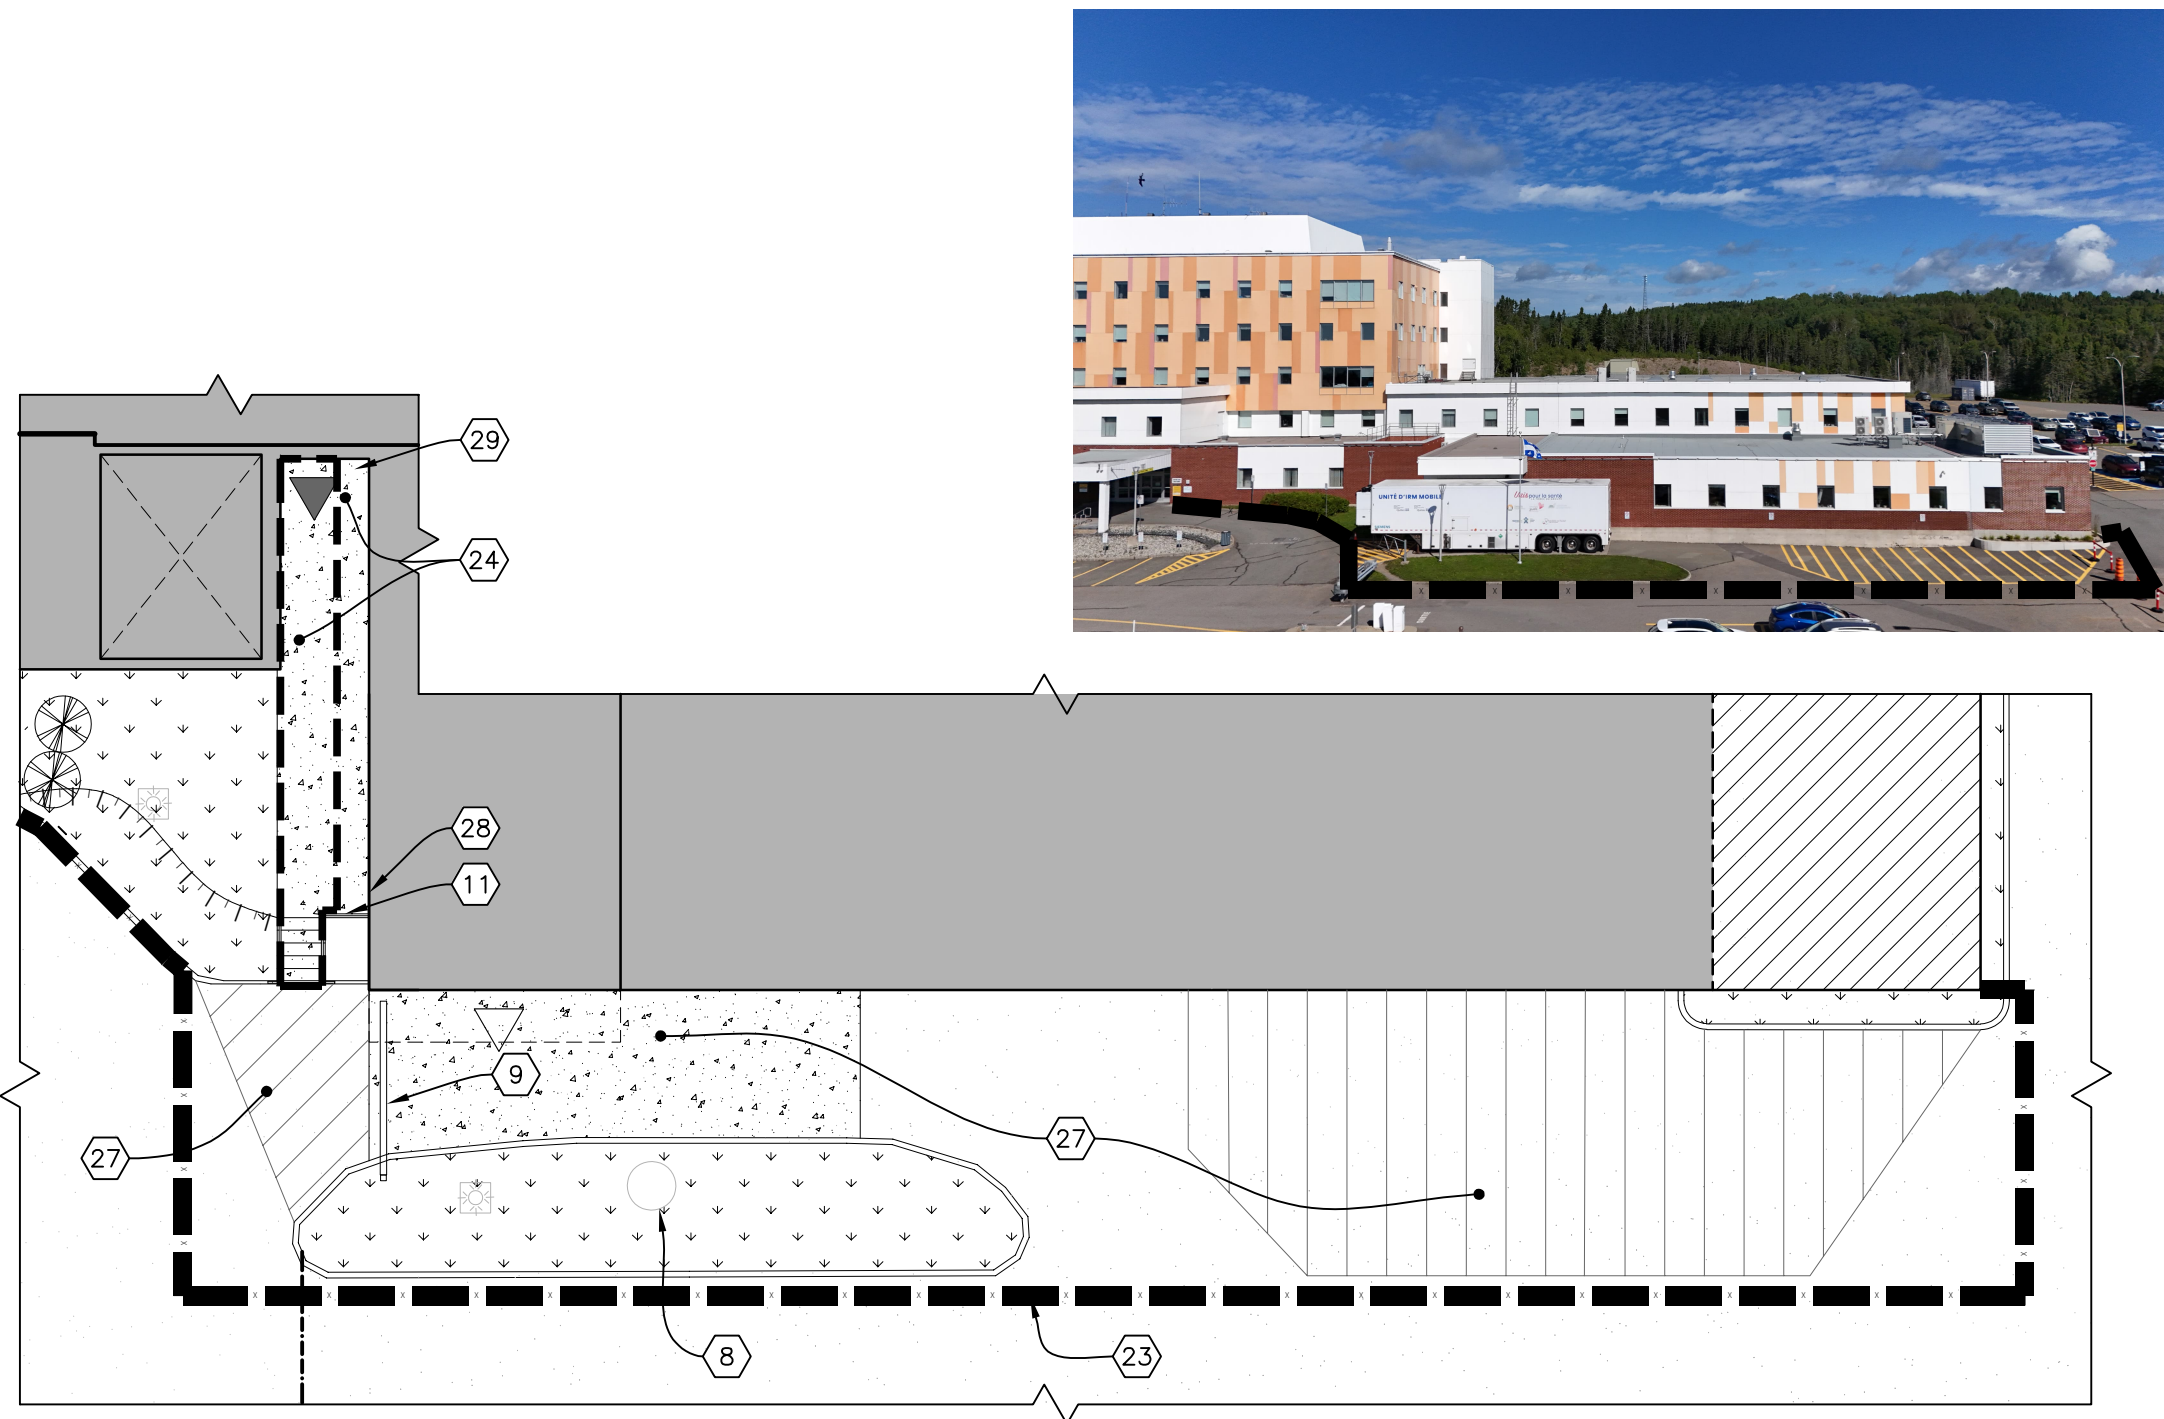


5
001 002
1:200mm
GESTION POUR LA ZONE IRM

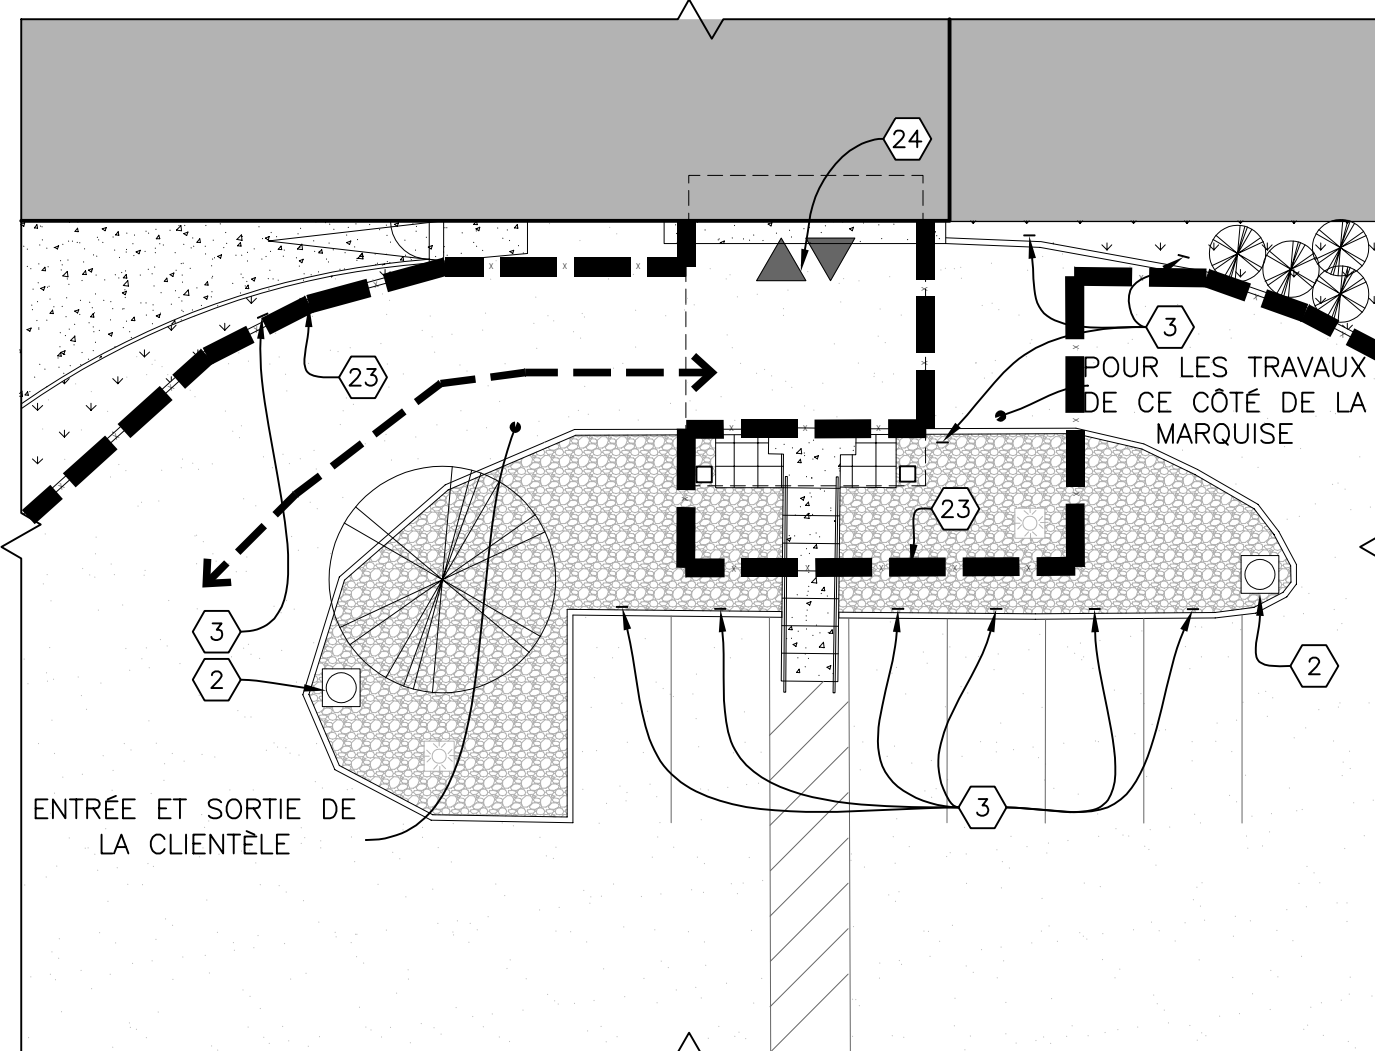

PHASE 1

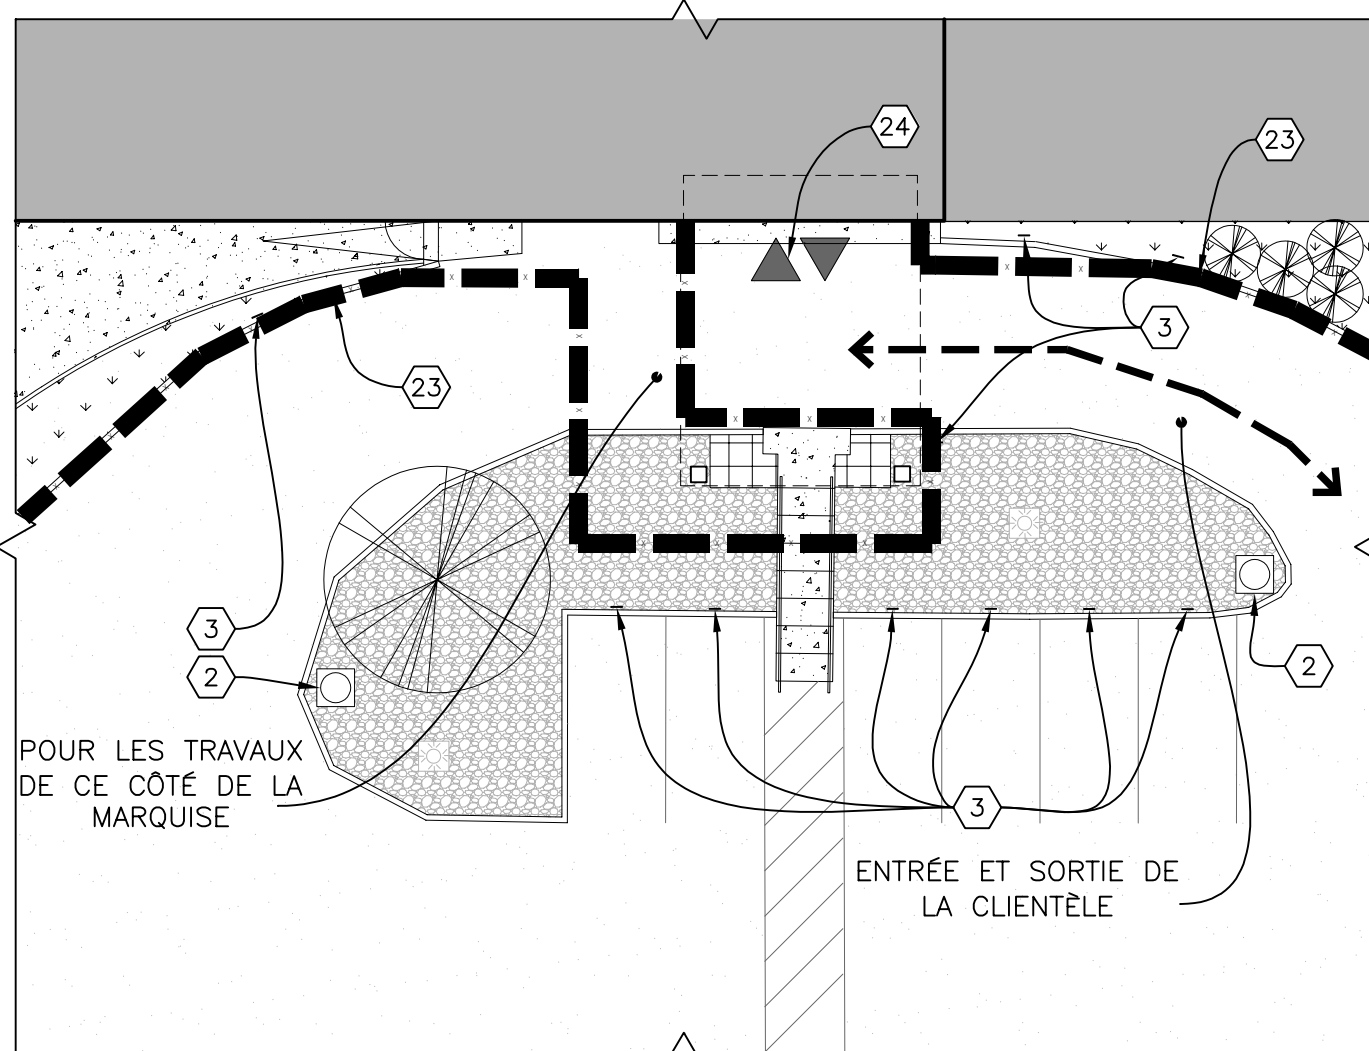

PHASE 2

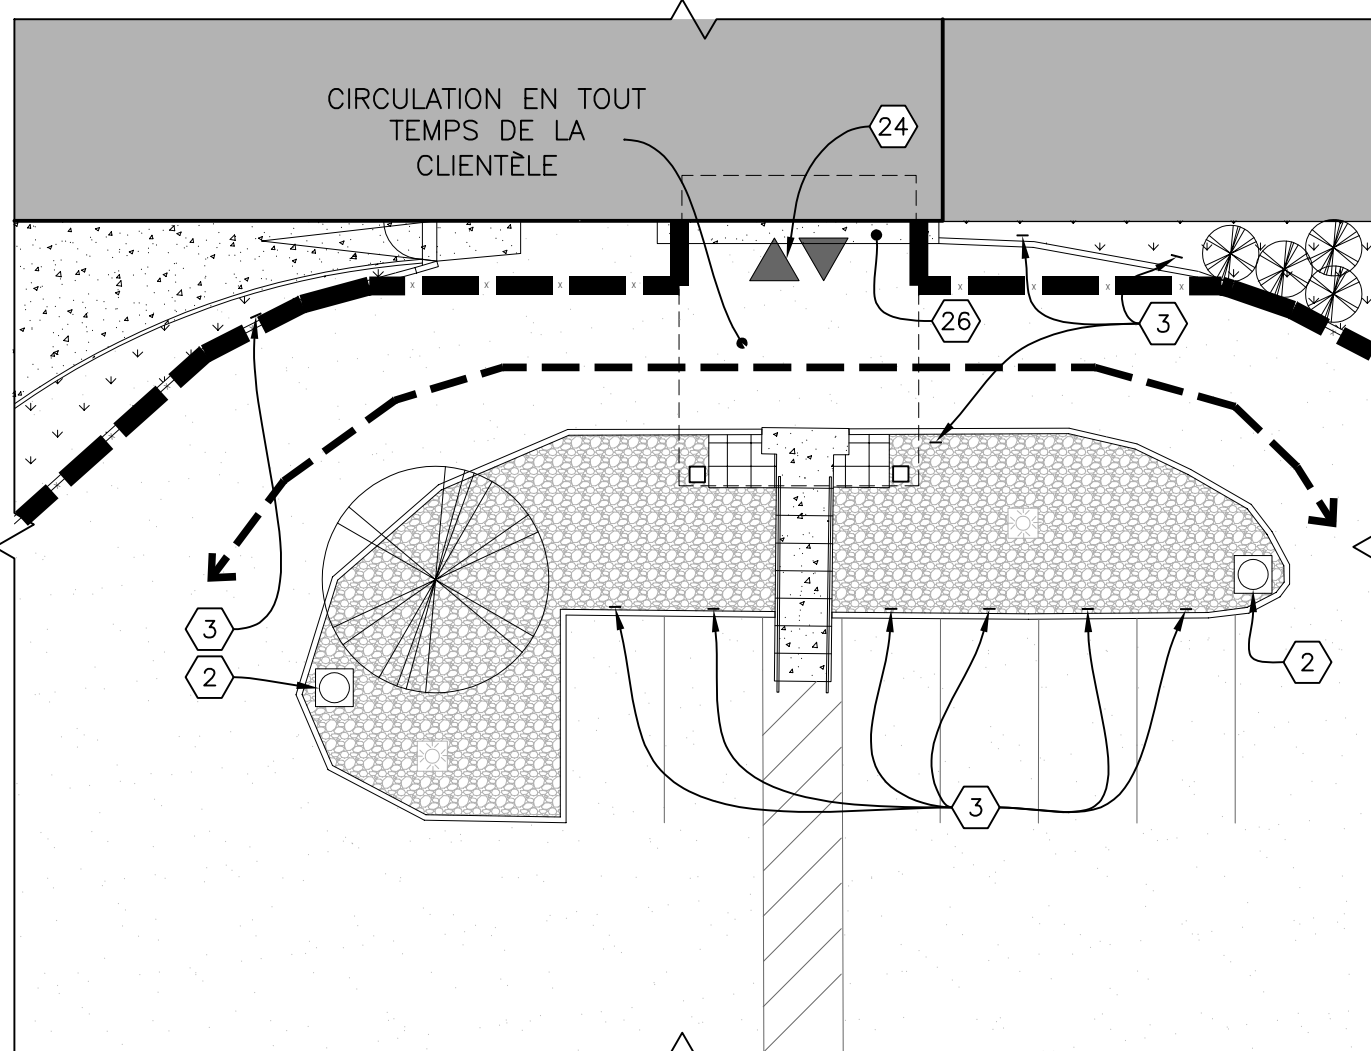


PHASE 3

2
001 002
1:200mm
GESTION POUR L'ENTRÉE PRINCIPALE DU BÂTIMENT

LÉGENDE

- (X) NOTE DESCRIPTIVE.
- LIGNE DE LOT.
- BAS DE TALUS.
- HAUT DE TALUS.
- SECTION NON TOUCHÉ PAR LES TRAVAUX.
- SECTEUR TOUCHÉ PAR LES TRAVAUX.
- ASPHALTE EXISTANT À CONSERVER ET À RAGREER À LA FIN DES TRAVAUX (VOIR NOTE CI-CONTRE).
- BÉTON EXISTANT À CONSERVER ET À RAGREER À LA FIN DES TRAVAUX (VOIR NOTE CI-CONTRE).
- GRAVIER EXISTANT À CONSERVER.
- TROTTOIR DE BOIS EXISTANT À CONSERVER ET À RAGREER À LA FIN DES TRAVAUX (VOIR NOTE CI-CONTRE).
- GAZON EXISTANT À CONSERVER ET À RAGREER À LA FIN DES TRAVAUX (VOIR NOTE CI-CONTRE).
- DALLAGE EXISTANT À CONSERVER ET À RAGREER À LA FIN DES TRAVAUX (VOIR NOTE CI-CONTRE).
- PORTE DE GARAGE ACCÈS AU BÂTIMENT. (PROTECTION DURANT LE CHANTIER)
- ISSUE / ACCÈS AU BÂTIMENT. (PROTECTION DURANT LE CHANTIER)
- CLÔTURE DE CHANTIER 1830MM DE HAUTEUR À ERIGER PAR L'ENTREPRENEUR POUR DÉLIMITER LA ZONE DE CHANTIER.
- GLISSIÈRE DE SÉCURITÉ (GARDE-FOU) EXISTANTE À CONSERVER.
- LAMPADAIRE EXISTANT À CONSERVER ET PROTÉGER PENDANT LES TRAVAUX.
- POTEAU ÉLECTRIQUE EXISTANT À CONSERVER ET PROTÉGER PENDANT LES TRAVAUX.
- ARBRE OU ARBUSTE EXISTANT À CONSERVER.
- CONTENEUR À DÉCHETS / RECYCLAGE.
- STATIONNEMENT POUR PERSONNE À MOBILITÉ RÉDUITE.
- STATIONNEMENT POUR VOITURE ÉLECTRIQUE.
- STATIONNEMENT POUR FAMILLE.
- FLECHE DE CIRCULATION.
- ZONE PROTÉGER.

TERMINOLOGIE

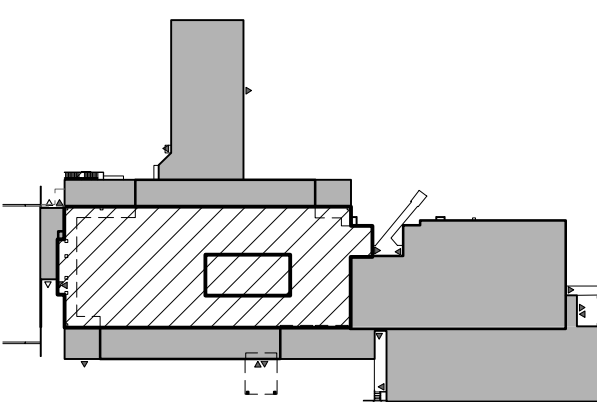

- TOUR (NIVEAUX 200, 300, 400 ET CABANON AU TOIT).
- BASILAIRES (NIVEAUX SOUS-SOL, REZ-DE-CHAUSSEE ET NIVEAU 100).

NOTES

- BORNE FONTAINE EXISTANTE. CONSERVER UN ACCÈS POMPIER À LA BORNE EN TOUT TEMPS PENDANT LA DURÉE DES TRAVAUX.
- POUBELLE EXISTANTE. À CONSERVER ET PROTÉGER PENDANT LES TRAVAUX.
- PANNEAU INDICATEUR EXISTANT À CONSERVER ET PROTÉGER PENDANT LES TRAVAUX.
- SUPPORT À VÉLO EXISTANT À REMETTRE AU PROPRIÉTAIRE.
- CONTENEUR À VÉLO.
- BORNE DE PAIEMENT POUR LE STATIONNEMENT EXISTANTE. À CONSERVER ET PROTÉGER PENDANT LES TRAVAUX.
- QUÉRITE EXISTANTE À CONSERVER ET PROTÉGER PENDANT LES TRAVAUX.
- MAT DE DRAPEAU EXISTANT À CONSERVER ET PROTÉGER PENDANT LES TRAVAUX.
- BARRIÈRE MÉTALLIQUE À BATTANT EXISTANTE À CONSERVER ET PROTÉGER PENDANT LES TRAVAUX.
- GARDE-CORPS EXISTANT À DÉMONTÉ ET ENTREPOSER PENDANT LES TRAVAUX POUR RÉINSTALLATION FUTURE. VOIR FEUILLES DE LA SÉRIE 700 POUR LES INTERVENTIONS SUR LES MÉTAUX-OUVRES EXISTANTS.
- GARDE-CORPS EXISTANT À CONSERVER ET PROTÉGER PENDANT LES TRAVAUX.
- COL DE CYGNE EXISTANT. VOIR DOCUMENTS D'INGÉNIEURIE.
- SAUT DE LOUP EXISTANT. VOIR DOCUMENTS D'INGÉNIEURIE.
- TERRASSE EXISTANTE À CONSERVER ET PROTÉGER PENDANT LES TRAVAUX.
- ENCLÔT POUR APPARELS ÉLECTRIQUES HAUTE TENSION EXISTANT À CONSERVER ET PROTÉGER PENDANT LES TRAVAUX.
- ENCLÔT POUR RÉSERVOIR DE GAZ EXISTANT À CONSERVER ET PROTÉGER PENDANT LES TRAVAUX.
- ESCALIER EXISTANT À DÉMOLIR.
- MUR DE BÉTON EN PENTE AVEC GARDE-CORPS EXISTANTS À CONSERVER.
- CASE DE STATIONNEMENT ET ESPACE RÉSERVÉ POUR L'ENTREPRENEUR.
- ZONE DE DÉBARCADERE POUR L'ENTREPRENEUR. COORDONNER AVEC L'ÉTABLISSEMENT POUR LES PÉRIODES DE TRAVAUX.
- CHEMIN EN GRAVIER TEMPORAIRE PENDANT LES TRAVAUX. REMETTRE LE TERRAIN DANS SON ÉTAT ORIGINAL APRÈS LES TRAVAUX. VOIR CIVIL.
- ZONE DE CHANTIER CLÔTURER.
- PORTE D'ISSUE EXTERIEUR ET CHEMIN D'ÉVACUATION À MAINTENIR OPÉRATIONNELLE ET LIBRE D'OBSTRUCTION DURANT LE CHANTIER. ASSURER UN PASSAGE D'ISSUE EXTERIEUR DE 1650mm MINIMUM LIBRE, PROTÉGÉ, DÉGAGÉ ET LIBRE DE LA PORTE JUSQU'À LA VOIE PUBLIQUE.
- PORTE EXTERIEUR HORS SERVICE PENDANT LES TRAVAUX.
- COORDONNER AVEC L'ÉTABLISSEMENT POUR LES TEMPS DE TRAVAUX SOUS LA MARQUISE ET AUTOUR DES PORTES. L'ENTREPRENEUR DOIT PROPOSER UN PLAN D'ACTION POUR ASSURER L'ÉVACUATION EN CAS D'URGENCE ET L'ACCESSIBILITÉ DE L'ENTRÉE PRINCIPALE.
- ZONE RÉSERVÉE À L'IRM (IMAGERIE PAR RÉSONANCE MAGNÉTIQUE). COORDONNER AVEC L'ÉTABLISSEMENT POUR LE TEMPS DES TRAVAUX. AUCUN ÉLÉMENT OU ENTREPOSAGE MÉTALLIQUE SERA PERMIS DANS CETTE ZONE LORSQUE L'IRM EST EN SERVICE.
- COORDONNER AVEC L'ÉTABLISSEMENT POUR LES SERVICE DE LA PORTE IRM.
- POUR LES TRAVAUX AUTOUR DES PORTES D'ISSUE QUI POURRAIENT NUIRE À L'ÉVACUATION EN CAS D'URGENCE, L'ENTREPRENEUR DOIT PROPOSER UN PLAN D'ACTION POUR ASSURER LA SÉCURITÉ D'ÉVACUATION ET COORDONNER AVEC L'ÉTABLISSEMENT AVANT LE DÉBUT DES TRAVAUX.
- ACCÈS GÉNÉRAL AU CHANTIER POUR L'ENTREPRENEUR. COORDONNER AVEC L'ÉTABLISSEMENT POUR LA GESTION DES FLUX DE CIRCULATION ENTRE L'ENTREPRENEUR ET LA CLIENTÈLE.
- POTEAU D'ÉLECTRICITÉ EXISTANT À CONSERVER ET PROTÉGER DURANT LES TRAVAUX.
- ACCÈS AU CHANTIER POUR L'ENTREPRENEUR.
- NOUVEL ESCALIER. VOIR DÉTAILS DE LA FEUILLE 705.
- CÂBLAGE ÉLECTRIQUE SOUTERRAIN EXISTANT DANS CETTE ZONE. VOIR DOCUMENTS D'INGÉNIEURIE. PRENDRE TOUTES LES PRÉCAUTIONS REQUIS LORS DE L'EXCAVATION ET DES TRAVAUX DE CONSTRUCTION DU NOUVEL ESCALIER POUR ÉVITER ET PROTÉGER LE CÂBLAGE EXISTANT.
- PANNEAU INDICATEUR TEMPORAIRE POUR L'ENTRÉE DES AMBULANCES. PRÉVOIR DEUX PANNEAUX AVEC UNE FLECHE INDICANT L'ENTRÉE DES AMBULANCES. UN PANNEAU PAR PHASE DE TRAVAUX DU SECTEUR AMBULANCES DONT L'ENTRÉE NE SE FERA PAS AU MÊME ENDROIT. COORDONNER L'EMPLACEMENT, LA DIMENSION ET LE TEXTE DES PANNEAUX TEMPORAIRES AVEC L'ÉTABLISSEMENT.
- PISTE CYCLABLE EXISTANTE. COORDONNER AVEC L'ÉTABLISSEMENT ET LA VILLE POUR ASSURER LA SÉCURITÉ DE CIRCULATION.




GLCRM | Proulx Savard |

GLCRM:
128, Avenue de la Cathédrale,
Bureau 201
Rimouski, QC, G5L 5H7
(418) 722-7455



2406, Ch. des Quatres-Bourgeois,
Bureau 100
Québec, QC, G1V 1W5
(418) 647-1700

Proulx Savard Architectes:
75, boul. Arthur-Buies Ouest,
Rimouski QC G5L 5C2
(418) 723-5543

ARCHITECTURE

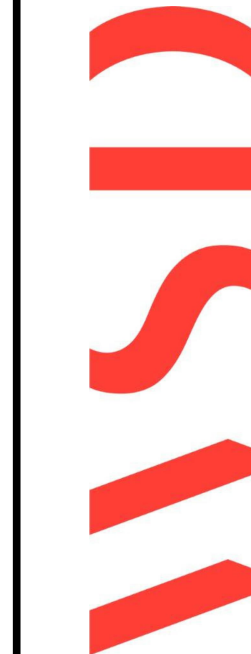

CONSULTANTS

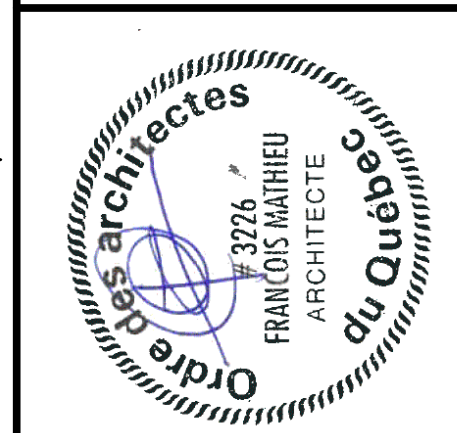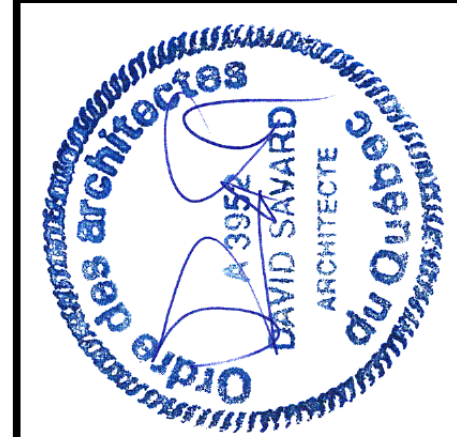

DOSSIER N°:	24-102 1637-24	DATE	SEPTEMBRE 2024	ÉCHELLE	INDIQUÉE	RÉVISIONS	
						DATE	No
DESIGNATEUR (S)	A.S.						
DESIGN	Gestion du Chantier Détaillé						
PROJET	HÔPITAL DE CHANDLER, Chandler (Réfection de l'enveloppe)						
PROPRIÉTAIRE	Santé Québec						

NE DOIT PAS SERVIR À L'EXÉCUTION

Le présent document est émis pour la seule fin identifiée. Son contenu est protégé par les droits d'auteur et toute reproduction ou modification, partielle ou totale, est interdite sans l'autorisation écrite de gagnon, letellier, cyr, ricard, mathieu, proulx, savard consortium d'architectes.

002

SOMMAIRE DES EXIGENCES - CODE DE CONSTRUCTION		
ANNÉE	DESCRIPTION DES TRAVAUX	CODE APPLICABLE
1974	CONSTRUCTION INITIALE	S-3, r.4
1990	AGRANDISSEMENT (LABORATOIRE)	CNB1985 mod. QC
2001	AGRANDISSEMENT (ARCHIVE)	CNB1990 / 1995 mod.QC
2005	AJOUT D'UN ÉTAGE SUR BASILAIRE	CNB1995 mod.QC
2007	AGRANDISSEMENT (IRM)	CNB1995 mod.QC
2012	RÉFECTION DE L'ENVELOPPE	CNB2005 mod.QC
2021	RÉFECTION DE LA TOITURE	CNB2010 mod.QC
2023	AGRANDISSEMENT (ONCOLOGIE)	CNB2010 mod.QC
2026	RÉFECTION DE L'ENVELOPPE	CNB2020 mod.QC (PROJET)

1. NATURE DE L'INTERVENTION

1.1. RÉFECTION DE L'ENVELOPPE

1.2. TRANSFORMATION MINEURE

2. USAGE PRINCIPAL

2.1. B2 - ÉTABLISSEMENT DE TRAITEMENT

2.2. PROTECTION CIVIL: OUI

3. AIRE DE BÂTIMENT

3.1. ± 4075m²

4. HAUTEUR DE BÂTIMENT

4.1. 5 ÉTAGES HORS SOL ET 1 ÉTAGE SOUS-SOL

4.2. BÂTIMENT DE GRANDE HAUTEUR: OUI

4.3. PREMIÈRE ÉTAGE SELON PARTIE 10: REZ-DE-CHAUSSÉE

5. FAÇADE SUR RUE

5.1. NOMBRE DE FAÇADE DONNANT SUR RUE: AU MOINS 1 RUE

6. CLASSIFICATION DU BÂTIMENT

6.1. 3.2.2.38.

6.2. INCOMBUSTIBLE

6.3. PARTIELLEMENT PROTÉGÉS PAR GICLEURS

7. DEGRÉ DE RÉSISTANCE AU FEU

7.1. NON TOUCHÉ

8. TOITURE COMBUSTIBLE

8.1. LES SUPPORTS DE COUVERTURE COMBUSTIBLES SONT PERMIS SOUS CERTAINES CONDITIONS.

3.1.2.1.

1.4.1.2.

1.4.1.2.

3.2.2.1.

3.2.6.

10.2.1.1.

3.2.5.4.

3.1.5.3.

NOTES GÉNÉRALES

1. L'ENTREPRENEUR GÉNÉRAL, AINSI QUE LES ENTREPRENEURS SPÉCIALISÉS DOIVENT SE CONFORMER À TOUTES LES NORMES, RÉGLEMENTATIONS ET EXIGENCES DE SÉCURITÉ EN VIGUEUR (CNB, COQ, CNESST, MUNICIPALITÉ, PROPRIÉTAIRE, ETC.).

2. POUR LA DESCRIPTION DES TRAVAUX DE DÉMOLITION, DE CONSTRUCTION ET RÉAMÉNAGEMENT EN ÉLECTRICITÉ, EN MÉCANIQUE, EN STRUCTURE ET EN GÉNIE CIVIL, SE RÉFÉRER AUX DOCUMENTS D'INGÉNÉRIE. LES MENTIONS «VOIR DOCUMENTS D'INGÉNÉRIE» OU «VOIR INGÉNIEUR» SIGNIFIE QU'IL FAUT SE RÉFÉRER AUX PLANS ET DEVIS DES DISCIPLINES D'INGÉNÉRIE POUR LA DESCRIPTION COMPLÈTE DES TRAVAUX À EXÉCUTER. SE RÉFÉRER ÉGALEMENT AU «TABLEAU DE COORDINATION DES ÉQUIPEMENTS ÉLECTROMÉCANIQUES» INCLUS DANS LES PLANS D'ÉLECTROMÉCANIQUES POUR CONNAÎTRE LA PORTÉE DES INTERVENTIONS ET DU SÉQUENÇAGE POUR CHAQUE ÉLÉMENT D'ÉLECTROMÉCANIQUE. L'ENTREPRENEUR EST RESPONSABLE DE VÉRIFIER CES INFORMATIONS POUR COMPLÉTER SES SOUMISSIONS ET EXÉCUTER LES TRAVAUX.

3. LES DOCUMENTS D'ARCHITECTURE DOIVENT ÊTRE LUS ET EXAMINÉS DE CONCERT AVEC LES DOCUMENTS D'INGÉNÉRIE. TOUS LES DESSINS ET SPÉCIFICATIONS SUR LES DOCUMENTS D'ARCHITECTURE ET D'INGÉNÉRIE FONT PARTIE D'UN TOUT EN VUE D'EXÉCUTION COMPLÈTE ET FONCTIONNELLE DES TRAVAUX DEMANDÉS DANS LE CADRE DU PRÉSENT MANDAT. TOUTES DIVERGENCES ENTRE LES DOCUMENTS DOIVENT ÊTRE SIGNALÉES AUX PROFESSIONNELS DE LA CONSTRUCTION AVANT D'ENTREPRENDRE LES TRAVAUX.

4. TOUS LES ÉLÉMENTS D'INGÉNÉRIE REPRÉSENTÉS AUX DOCUMENTS D'ARCHITECTURE LE SONT À TITRE INDICATIF SEULEMENT. SE RÉFÉRER AUX DOCUMENTS DE LA DISCIPLINE APPROPRIÉE POUR OBTENIR DE L'INFORMATION PRÉCISE ET COMPLÈTE CONCERNANT LES ÉLÉMENTS SPÉCIFIÉS PAR CETTE DISCIPLINE.

5. LA DESCRIPTION DÉTAILLÉE DES TRAVAUX N'EST PAS LIMITATIVE. L'ENTREPRENEUR DOIT FOURNIR ET INSTALLER TOUS LES ÉLÉMENTS NÉCESSAIRES À L'EXÉCUTION DES TRAVAUX IDENTIFIÉS AFIN D'EN ARRIVER À UN PRODUIT COMPLÈT ET FONCTIONNEL.

6. LES NOTES GÉNÉRALES, LES NOTES PARTICULIÈRES ET LES ANNOTATIONS AUX PLANS SONT COMPLÉMENTAIRES. S'IL Y A AMBIGUÏTÉ ENTRE CES DERNIÈRES, LA NOTE LA PLUS PRÉCISE FACE À UNE INTERVENTION DONNÉ AURA PRIORITÉ SUR LES AUTRES. AU BESOIN, CONSULTER LE PROFESSIONNEL DE LA CONSTRUCTION.

7. AUCUNE DIMENSION OU MESURE NE DOIT ÊTRE RELEVÉE DIRECTEMENT SUR LES PLANS ET AUTRES DESSINS TECHNIQUES. TOUTES LES DIMENSIONS DOIVENT FAIRE L'OBJET D'UNE VÉRIFICATION SUR PLACE. TOUTES LES DIMENSIONS DES ÉLÉMENTS EXISTANTS IDENTIFIÉS AUX PLANS SONT APPROXIMATIVES (±) ET À TITRE INDICATIF SEULEMENT.

8. AVANT DE PROCÉDER À L'EXÉCUTION DES TRAVAUX, L'ENTREPRENEUR DOIT VÉRIFIER TOUTES LES DIMENSIONS ET/OU CONDITIONS SUR LES LIEUX. IL DOIT AVISER SANS DÉLAI LES PROFESSIONNELS DE LA CONSTRUCTION DE TOUTES CONTRADICTIONS, ERREURS, OMISSIONS OU DIVERGENCES.

9. SI L'ENTREPRENEUR A UN DOUTE QUANT À LA PRÉSENCE D'AMIANTE DANS UN MATÉRIAU À DÉMOLIR OU À PERCER, IL DEVRA EN AVERTIR LE PROFESSIONNEL DE LA CONSTRUCTION DANS LES PLUS BREFS DÉLAIS. DES MESURES APPROPRIÉES SERONT MISES EN PLACE POUR CARACTÉRISER LE MATÉRIEL EN QUESTION ET EN DISPOSER ADEQUATEMENT, LE CAS ÉCHÉANT. SE RÉFÉRER AU DEVIS D'ARCHITECTURE.

10. L'ENTREPRENEUR GÉNÉRAL A LA RESPONSABILITÉ DE COORDONNER AVEC LES ENTREPRENEURS SPÉCIALISÉS TOUTES LES MODIFICATIONS EMISES PAR LES PROFESSIONNELS DE LA CONSTRUCTION.

11. L'ENTREPRENEUR EST RESPONSABLE DE PRÉVOIR ET FOURNIR TOUS LES MATÉRIAUX, ÉQUIPEMENTS ET ÉTAIEMENTS REQUIS POUR L'EXÉCUTION DES TRAVAUX.

12. L'ENTREPRENEUR EST RESPONSABLE D'ASSURER LA CONTINUITÉ ET L'INTÉGRITÉ DES SÉPARATIONS COUPE-FEU.

13. TOUTS BRIS AU BÂTIMENT ET/OU MATÉRIEL EXISTANT À REINSTALLER OU À MAINTENIR EN PLACE DEVRONT ÊTRE RÉPARÉS OU REMPLACÉS À LA SATISFACTION DES PROFESSIONNELS DE LA CONSTRUCTION.

14. PROTÉGER ADEQUATEMENT CONTRE LES INTEMPÉRIES, L'HUMIDITÉ ET LES INFILTRATIONS D'EAU LES MATÉRIAUX ET/OU LES PARTIES D'OUVRAGES SUSCEPTIBLES D'ÊTRE ENDOMMAGÉS PAR CES ÉLÉMENTS, TOUS LES MATÉRIAUX OU PARTIES D'OUVRAGES NON PROTÉGÉS QUI SERONT ENDOMMAGÉS PAR CES ÉLÉMENTS DEVRONT ÊTRE RÉPARÉS OU REMPLACÉS À LA SATISFACTION DES PROFESSIONNELS DE LA CONSTRUCTION.

15. PROTÉGER ADEQUATEMENT TOUTES LES PLANTATIONS EXISTANTES, LE GAZON ET LES AMÉNAGEMENTS PAYSAGERS EXISTANTS IDENTIFIÉS "À CONSERVER" À PROXIMITÉ DES ZONES DE TRAVAUX. LES LIEUX DEVRONT ÊTRE REMIS DANS LEUR ÉTAT D'ORIGINE À LA FIN DES TRAVAUX, CECI INCLUT LE REMPLACEMENT D'ARBRES AYANT LE MÊME DIAMÈTRE QUE CEUX EXISTANTS, DANS LE CAS OÙ CES DERNIERS SERONT ABIMÉS OU DÉRACINÉS EN COURS DE TRAVAUX.

16. L'ENTREPRENEUR À LA RESPONSABILITÉ DE PROTÉGER L'ENSEMBLE DES INSTALLATIONS EXISTANTES ET NOUVELLEMENT CONSTRUITES EN PRÉPARATION À LA LIVRAISON D'ÉQUIPEMENTS FOURNIS PAR LE PROPRIÉTAIRE. TOUTES LES INSTALLATIONS ENDOMMAGÉES AU COURS DES TRAVAUX DEVRONT ÊTRE RÉPARÉES/RAGRÉÉES AUX FRAIS DE L'ENTREPRENEUR, À LA SATISFACTION DU PROFESSIONNEL DE LA CONSTRUCTION.

17. PRÉVOIR UN FOND DE VISSAGE POUR TOUS LES ÉLÉMENTS PRÉSENT SUR L'ENVELOPPE DU BÂTIMENT QUI SONT À REINSTALLER, INCLUANT LES ÉLÉMENTS MÉCANIQUES ET ÉLECTRIQUES, SAUF INDICATIONS CONTRAIRES AUX DESSINS, PRÉVOIR UNE TÔLE EN ACIER GALVANISÉ CAL-16 DE DIMENSIONS REQUISES.

18. LES MÉTHODES DE DÉMOLITION ET DE PERCEMENTS POUR LES TRAVAUX À RÉALISER DANS ET À PROXIMITÉ DES INSTALLATIONS EXISTANTES DOIVENT GÉNÉRER LE MOINS DE BRUIT POSSIBLE.

19. L'ENTREPRENEUR DOIT S'ASSURER QUE LES CHUTES À DÉCHETS (SI REQUISES) ET LES CONTENEURS INSTALLÉS AU CHANTIER SONT ÉTANCHES PROTÉGÉS, DES INTEMPÉRIES ET MUNIS DE TOILES ÉTANCHES POUR PROTÉGER DE LA POUSSIÈRE.

20. PRÉVOIR DE CONSERVER UNE PARTIE DE LA BRIQUE DÉMOLIE POUR FAIRE LA RÉFECTION DE LA BRIQUE, ENTREPOSER, NETTOYER ET PROTÉGER LA MAÇONNERIE, EN VUE DE SA REINSTALLATION. VOIR LES ÉLEVATIONS POUR LES SECTIONS DE BRIQUES À RECONSTRUIRE.SAUF INDICATION CONTRAIRE, POUR TOUS LES LOCAUX AVEC DES TRAVAUX EFFECTUÉS À PROXIMITÉ DES FENÊTRES EXISTANTES, DEMANTELER SOIGNEUSEMENT LES PARURES DE FENÊTRES EXISTANTES (RIDEAUX, STORES, TOILES SOLAIRES, ETC.) ET LES REMETTRE AU PROPRIÉTAIRE.

21. LORSQUE DES TRAVAUX DE DÉMOLITION D'UN ÉLÉMENT OU D'UN ÉQUIPEMENT SONT PRÉVU SUR UN REVÊTEMENT EXISTANT À CONSERVER, DÉMONTÉ SOIGNEUSEMENT L'ÉLÉMENT OU L'ÉQUIPEMENT AFIN D'ÉVITER D'ABÎMER LE REVÊTEMENT EXISTANT. FAIRE TOUTES LES RÉPARATIONS REQUISES AU REVÊTEMENT EXISTANT À CONSERVER SI CELUI-CI EST ABÎMÉ LORS DE TRAVAUX DE DÉMOLITION. BOUCHER TOUS LES TROUS DES FIXATIONS ET ANCRAGES DÉMOLUES DANS LE REVÊTEMENT DE MAÇONNERIE À L'AIDE D'UN MORTIER DE MÊME COULEUR QUE CELUI EXISTANT. SI DES BRIQUES SONT TROP ABÎMÉES, LES REMPLACER AVEC DES BRIQUES EXISTANTES RECUPÉRÉES.

22. LA MENTION «À DÉMONTÉ ET ENTREPOSER POUR REINSTALLATION FUTURE» SIGNIFIE QUE L'ENTREPRENEUR DOIT DÉMONTÉ SOIGNEUSEMENT L'ÉLÉMENT DU BÂTIMENT ET L'ENTREPOSER POUR LA DURÉE DES TRAVAUX, JUSQU'À SA REINSTALLATION, DANS UN ENDROIT À L'ABRIS DES INTEMPÉRIES, AFIN QUE L'ÉLÉMENT NE SE DÉGRADE PAS.

23. SAUF INDICATIONS CONTRAIRES AUX DESSINS, TOUTES LES PERSIENNES EXISTANTES À REINSTALLER DOIVENT ÊTRE REPEINTÉ EN ARCHITECTURE AVANT D'ÊTRE REINSTALLÉES, DE LA MÊME COULEUR QUE LE REVÊTEMENT DANS LEQUEL ELLE SERONT INSTALLÉES.

24. LORS DE LA DÉMOLITION ET DE L'OUVERTURE DES COMPOSITIONS D'ENVELOPPE, SI DES COMPOSANTES EXISTANTES À CONSERVERS PRÉSENTES DES TRACES D'HUMIDITÉ OU DE MOISSISURE, PRÉVOIR DE DÉMOLIR ET DE REMPLACER CES COMPOSANTES, AVANT DE POURSUIVRE LES TRAVAUX DE CONSTRUCTION. REMPLACER TOUS MATÉRIAUX DÉGRADÉ PAR DES MATÉRIAUX NEUF DE MÊME NATURE QUE CEUX EXISTANTS. INFORMER LES PROFESSIONNELS DE LA CONSTRUCTION DE TOUTES COMPOSANTES À REMPLACER QUI N'ÉTAIENT PAS IDENTIFIÉES À REMPLACER AUX DOCUMENTS. DANS LE CAS OÙ L'ISOLANT EXISTANT EST REMPLACÉ, OBSERVER LES CONDITIONS EXISTANTES DES COMPOSANTES DERRIÈRE (Panneau de support et pare-vapeur) ET FAIRE LES RÉPARATION OU LE REMPLACEMENT DES COMPOSANTES ABÎMÉES.

25. LORS DE LA DÉMOLITION ET DE L'OUVERTURE DES COMPOSITIONS D'ENVELOPPE, SI DES COMPOSANTES MÉTALLIQUES EXISTANTES À CONSERVÉES PRÉSENTES DES TRACES DE ROUILLE, PRÉVOIR DE TRAITER LE MATÉRIEL AVEC UN ENDUIT POUR NEUTRALISER LA ROUILLE.

26. TOUS LES ÉLÉMENTS FIXÉS OU ACCROCHÉS SUR LES MURS ET LES CLOISONS EXISTANTES À DÉMOLIR À L'INTÉRIEUR DU BÂTIMENT (AFFICHAGES, TABLETTES, TABLEAUX, CADRES ET TOUS AUTRE ÉQUIPEMENTS) DEVRONT ÊTRE RETIRÉS PAR L'ENTREPRENEUR ET REMIS AU PROPRIÉTAIRE.

27. TOUS LES ÉLÉMENTS OU ÉQUIPEMENTS À L'INTÉRIEUR DU BÂTIMENT QUI SE TROUVENT DANS LA ZONE DES TRAVAUX, MAIS QUI NE PEUVENT PAS ÊTRE DÉPLACÉS, DEVRONT ÊTRE PROTÉGÉS ADEQUATEMENT PENDANT LA PÉRIODE DES TRAVAUX. COORDONNER AVEC L'ÉTABLISSEMENT LES ÉLÉMENTS ET ÉQUIPEMENT À RETIRER TEMPORAIREMENT.

NOTES PARTICULIÈRES EN LIEN AVEC LES TRAVAUX DE DÉMOLITION DE TOITURES

1. L'ENTREPRENEUR RESPONSABLE DES TRAVAUX DE DÉMOLITION DE TOITURE DEVRA FAIRE TOUS LES TRAVAUX DE DÉMOLITION ET DE PERCEMENTS REQUIS POUR LA RÉALISATION DES TRAVAUX DE TOITURES, TELS QUE MONTRES ET DECORIS DANS LES DOCUMENTS DES PROFESSIONNELS DE LA CONSTRUCTION.

2. METTRE EN PLACE DES PANNEAUX DE PROTECTION SUR LES TOITURES EXISTANTES AFIN DE CRÉER DES VOIES DE CIRCULATION VERS LES DIFFÉRENTES ZONES D'INTERVENTIONS. CONSERVER LES PANNEAUX DE PROTECTION EN PLACE JUSQU'À LA FIN DES TRAVAUX.

3. LORSQU'UN ÉLÉMENT EXISTANT (ARCHITECTURE OU ÉLECTROMÉCANIQUE) NON-REINSTALLÉ OU RELOCAUSÉ EST FIXÉ DANS UN SYSTÈME DE TOITURE EXISTANT OU UN PARAPET EXISTANT DONT AUCUN TRAVAUX DE RECOUVREMENT SONT INDICQUÉS AUX PLANS, FAIRE LES RÉPARATIONS REQUISES AU SYSTÈME (±150mm AUTOUR DES PERCEMENTS). PRÉVOIR DE DÉGRADULER LA MEMBRANE EXISTANTE ET INSTALLER UNE BANDE DE MEMBRANE DE FINITION SUR LE SYSTÈME EXISTANT.

NOTES




GLCRM | Proulx Savard |

GLCRM:
178, Avenue de la Cathédrale,
Bureau 201
Rimouski, QC, G5L 5H7
(418) 722-7655

2406, Ch. des Quatres-Bourgeois,
Bureau 100
Québec, QC G1V 1W5
(418) 647-1700

Proulx Savard Architectes:
75, boul. Arthur-Buies Ouest,
Rimouski QC G5L 5C2
(418) 723-5543

ARCHITECTURE

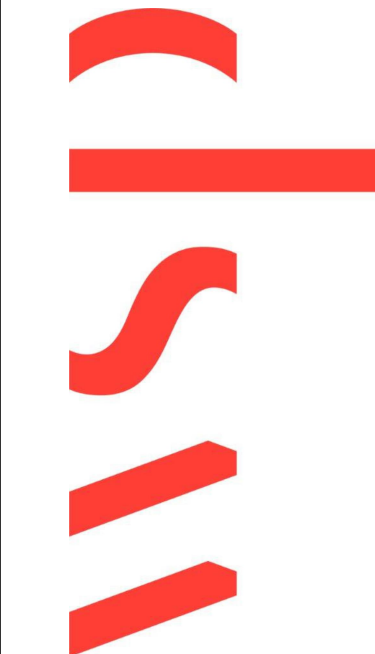


CONSULTANTS




DESSINATEUR (S)	DOSSIER No.		DATE	REVISIONS				
	J.X.	ÉCHELLE		INDIQUÉE	DATE	No	DATE	
PROJET HÔPITAL DE CHANDLER, Chandler [Réfection de l'enveloppe]	05	04	04	DÉFINITIVES POUR SOUMISSION	04	04	04	04
				DÉFINITIVES 100% POUR APPROBATION				
				DÉFINITIVES 80% POUR APPROBATION				
				DÉFINITIVES 60% POUR APPROBATION				
PROPRIÉTAIRE	01	02	02	PRÉLIMINAIRES 30% POUR APPROBATION	02	02	02	02


LISTE DES LOCAUX	LISTE DES LOCAUX
S2 DÉCHETS BIO-MÉDICAUX	S18 BUREAU
S3 CENTRALE THERMIQUE	S19 CHIEF DE SERVICE
S3-A BUREAU	S20 PRÉVENTIONNISTE
S4 VENTILATION	S21 VESTIBULE HOMMES
S5 ESCALIER	S22 SALLE DE PAUSE
S6 VESTIBULE	S23 / 24 CATERING / NUTRITIONNISTE
S7 CHIEF DE SERVICE	S25 CHUINE
S8 ARCHIVE	S26 RESERVE
S9 CONSULTAIRE DES	S27 ENTRETIEN MANAGER
S10 DÉPÔT	S28 CHAÎNES À DÉCHETS
S11 MAGASIN	S29 ESCALIER
S12 ARCHIVES	S30 BUCARDIE
S13 ESCALIER	S31 BIO-MÉDICAUX DÉCHETS
S14 DÉPÔT	S32 CONCIERGE
S15 DÉPÔT	S33 CONCIERGE
S16 MANUSCRIT	S37 CORRIDOR
S17 GEM	S41 ARCHIVES MORTES

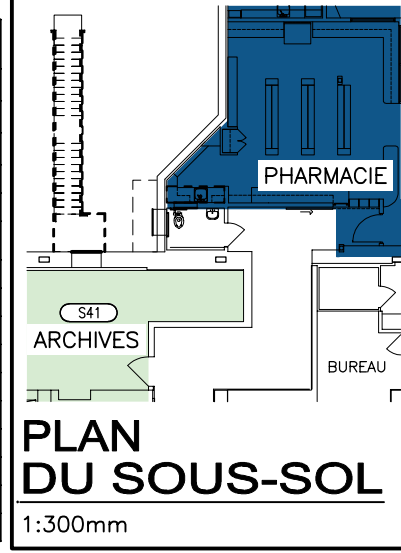

PLAN DU SOUS-SOL
1:300mm


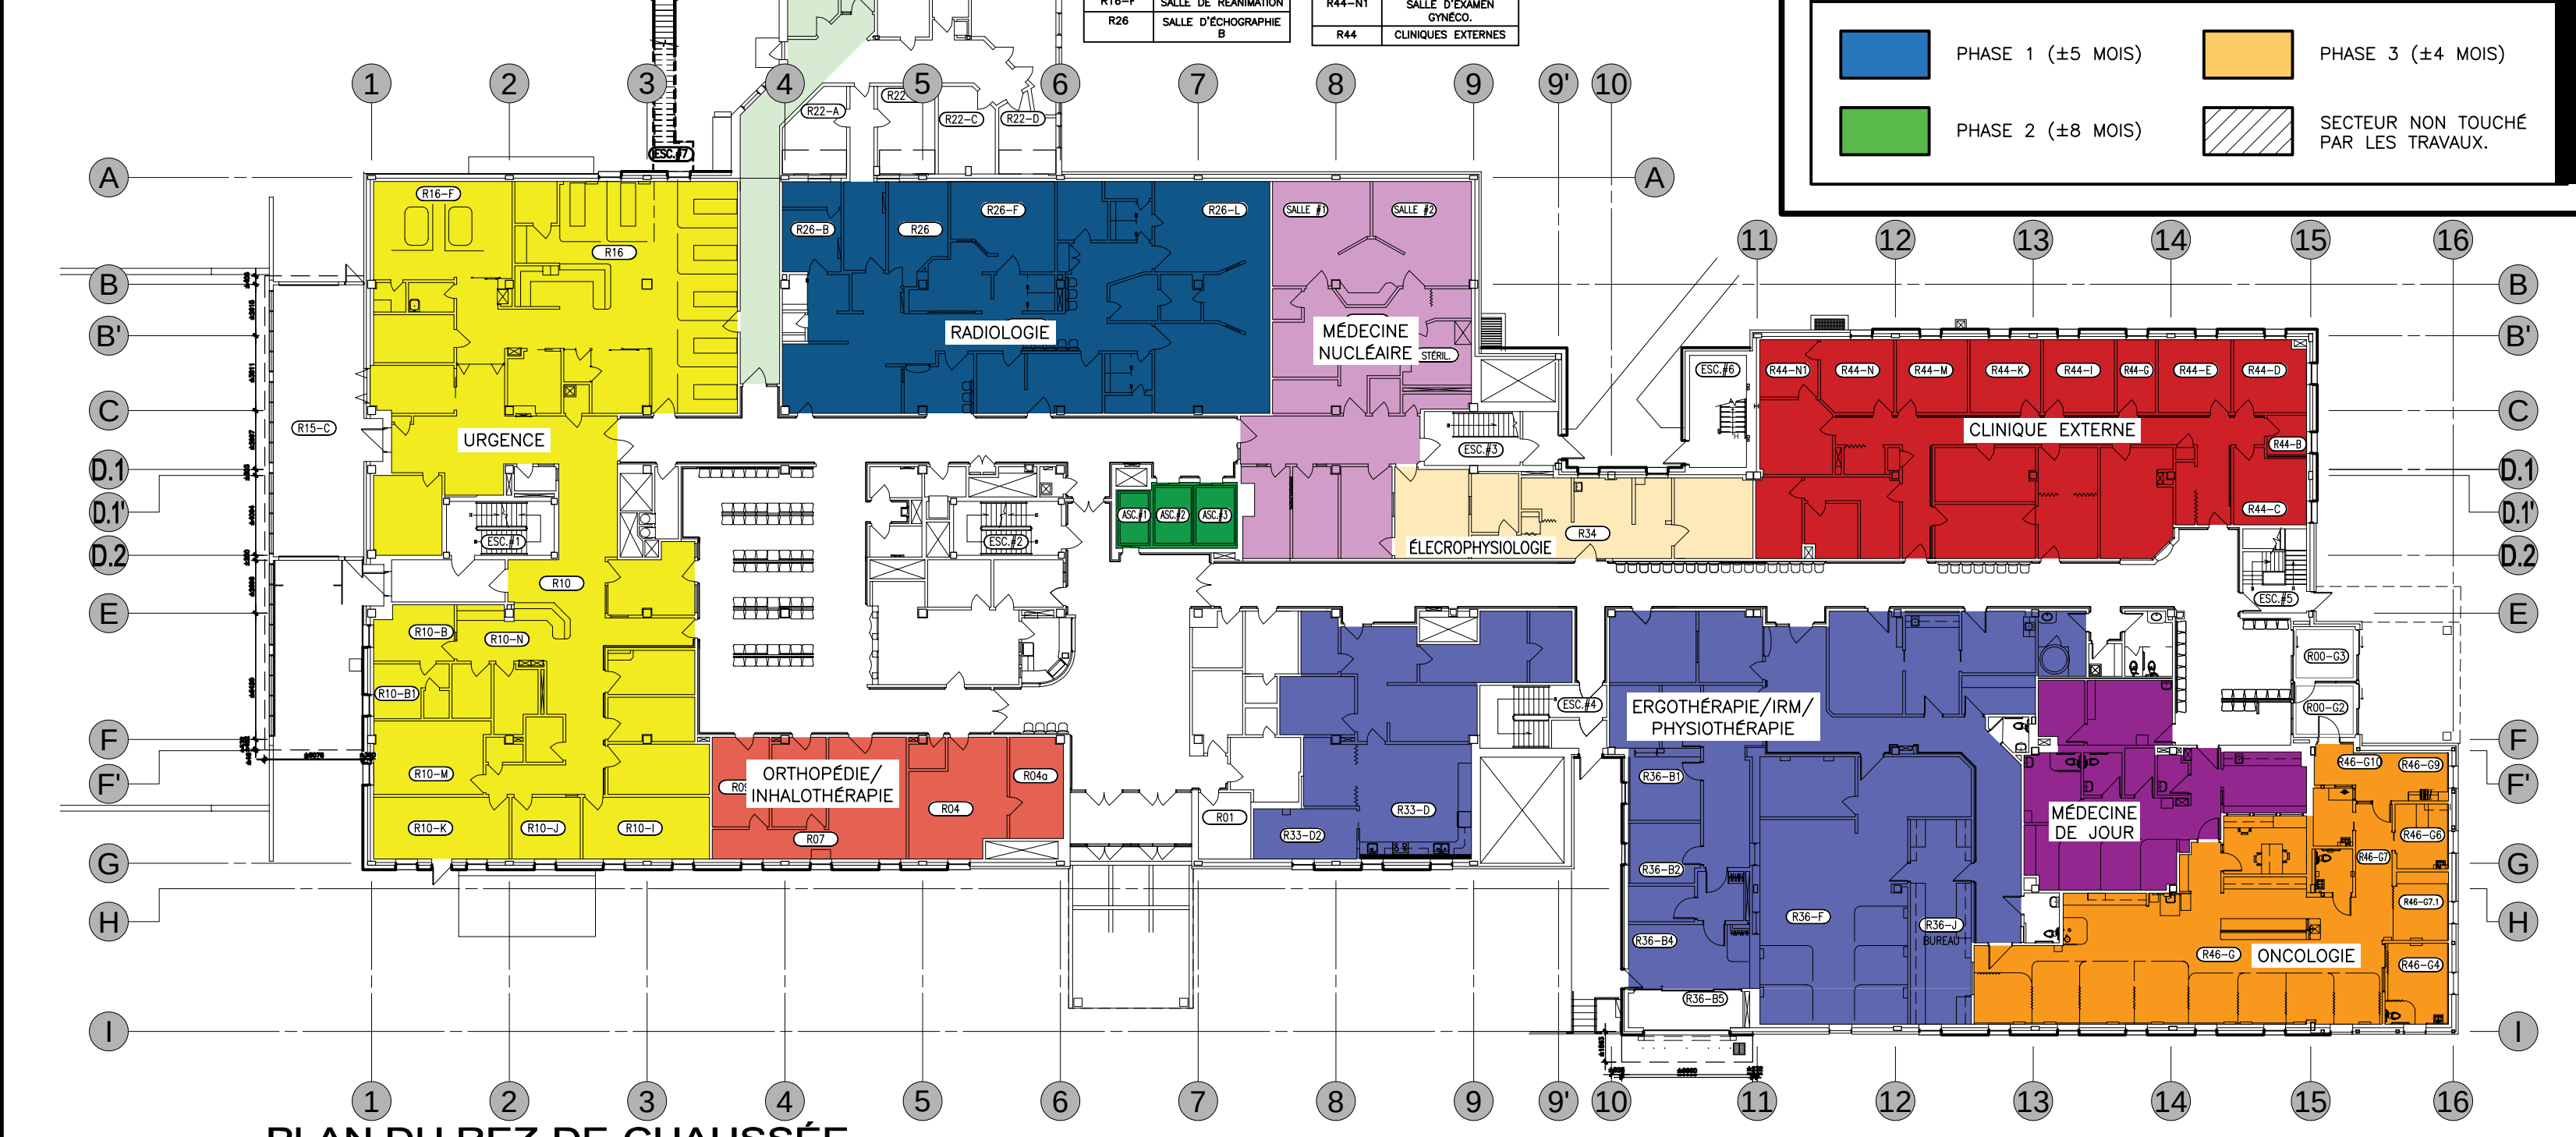


PLAN DU REZ-DE-CHAUSSEE
1:300mm

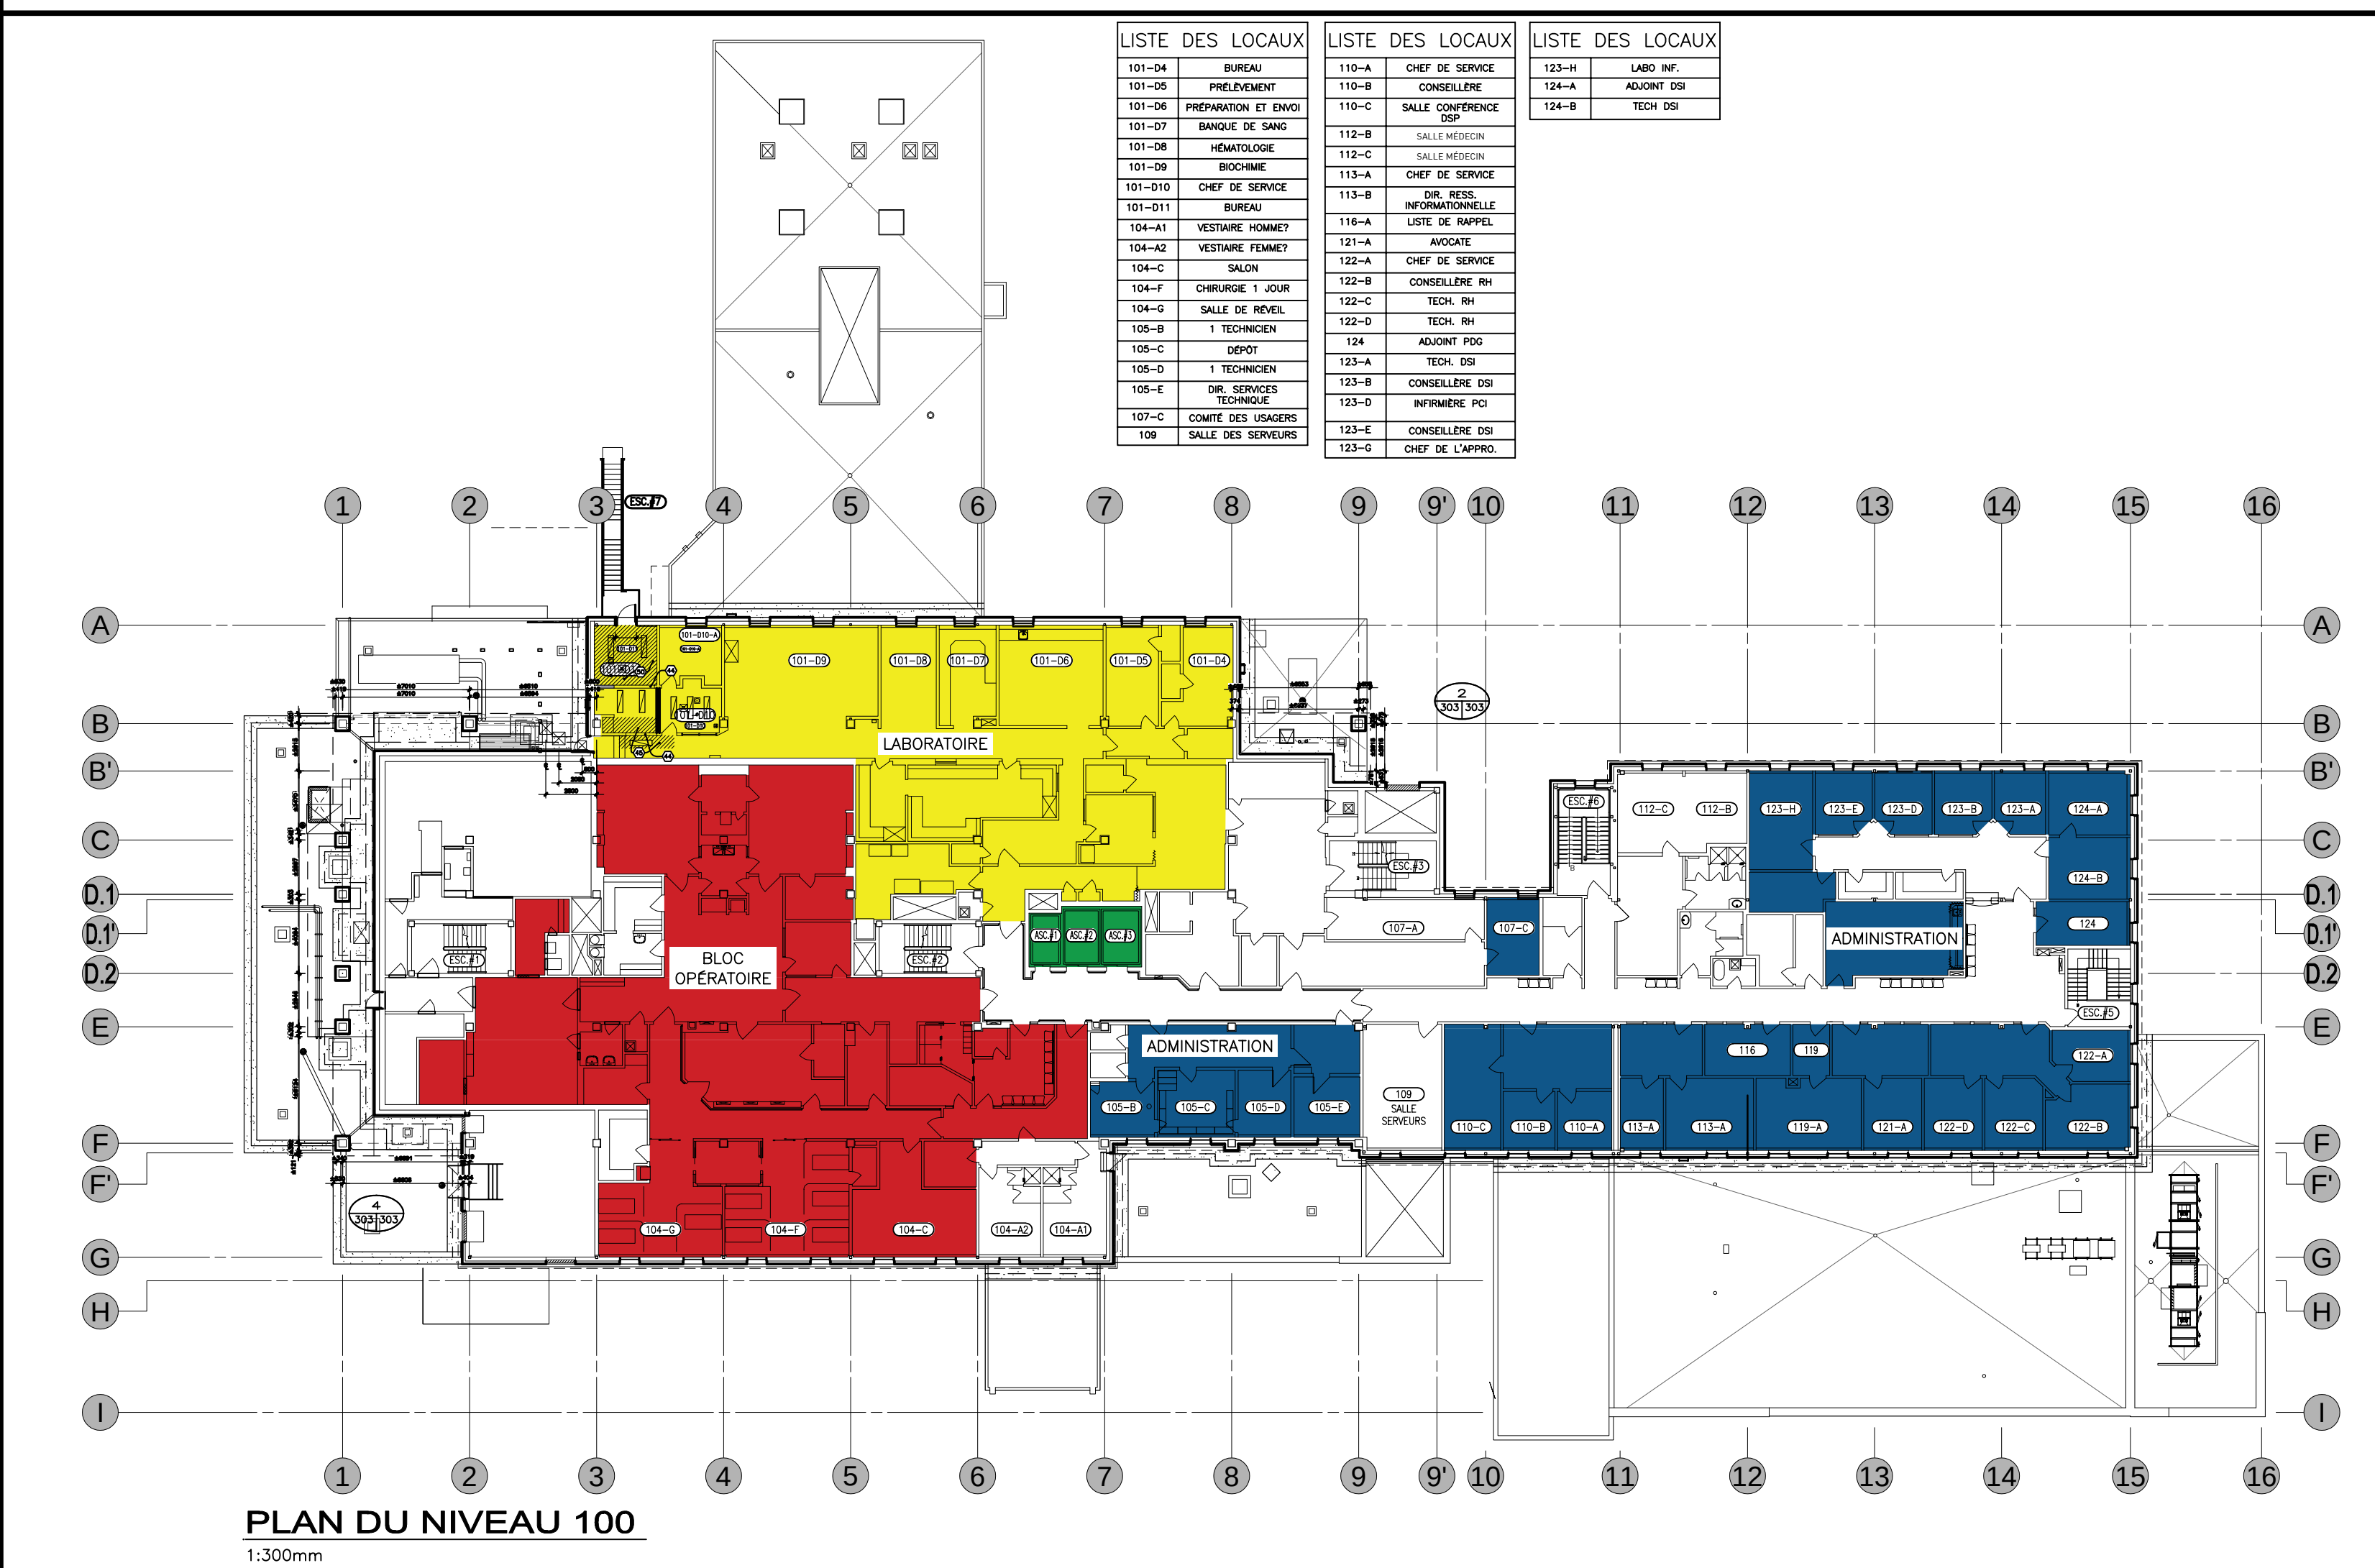


PLAN DU NIVEAU 100
1:300mm


LISTE DES LOCAUX	LISTE DES LOCAUX	LISTE DES LOCAUX
R02-G2 VESTIBULE ONCOLOGIE	R26-B MAMMOGRAPHIE	R44 CUNQUES EXTERNES
R02-G3 VESTIBULE	R26-B RADIO	R44-C BUREAU INT.
R03 COORDONNATRICE	R26-B SALLE DE RAYON X #3	R44-D BUREAU INT.
R04 INHALOTHÉRAPIE	R26-L TOMODENSITOMETRIE	R44-E BUREAU CHR.
R05 INHALOTHÉRAPIE	R29 MÉDECINE NUCLÉAIRE	R44-G SALLE D'EXAMEN CHR.
R06 INHALOTHÉRAPIE	R33 ENDOSCOPIE	R44-H BUREAU CHR.
R08 SALLE D'EXAMEN	R33-D SALLE DE THÉRAPIE	R44-I BUREAU INT.
R09 SALLE D'EXAMEN	R34 ELECTRO-PHYSIOLOGIE	R44-M BUREAU PED.
R10 URGENCE	R34-EUCLYD	R46 MÉDECINE DE JOUR
R10-S SALLE DE TRAITEMENT	R36 PHYSIOCHIMIE	R46-B BUREAU
R10-B1 MÉDECIN	R36-B BUREAU DU RESEAU	R46-G ONCOLOGIE
R10-B2 MÉDECIN	R36-B1 RESEAU READAPTATION	R46-G1 PREP. ET RANG.
R10-B3 ADJONTE INF. CHIEF	R36-B2 ENDOSCOPIE	R46-G2 BUREAU
R10-B4 SALON DU PERSONNEL	R36-B3 SALLE D'ISOLEMENT	R46-G3 BUREAU MEDICIN
R10-B5 DÉPÔT	R36-B4 SALLE DE PRÉPARATION	R46-G4 ALCOVE PÉDIATRIQUE
R10-B6 SÉCRÉTAIRE	R36-B5 SALLE D'AMBIANCE	R46-G5 MÉDECIN
R10-B7 SALLE D'AMBIANCE	R36-B6 SALLE D'AMBIANCE	R46-G6 SALLE D'ATTENTE
R10-B8 DÉCONTAMINATION	R36-B7 SALLE D'AMBIANCE	
R10-B9 SALLE D'OBSERVATION	R36-B8 SALLE D'AMBIANCE	
R10-B10 SALLE DE RETRAIT	R36-B9 SALLE D'AMBIANCE	
R10-B11 SALLE DE REANIMATION	R36-B10 SALLE D'AMBIANCE	
R10-B12 SALLE D'ECGONOMIE	R36-B11 SALLE D'AMBIANCE	
R28 SALLE D'ECGONOMIE	R36-B12 SALLE D'AMBIANCE	
	R44-B1 SALLE D'AMBIANCE	
	R44-B2 SALLE D'AMBIANCE	
	R44-B3 SALLE D'AMBIANCE	
	R44-B4 SALLE D'AMBIANCE	
	R44-B5 SALLE D'AMBIANCE	
	R44-B6 SALLE D'AMBIANCE	
	R44-B7 SALLE D'AMBIANCE	
	R44-B8 SALLE D'AMBIANCE	
	R44-B9 SALLE D'AMBIANCE	
	R44-B10 SALLE D'AMBIANCE	
	R44-B11 SALLE D'AMBIANCE	
	R44-B12 SALLE D'AMBIANCE	

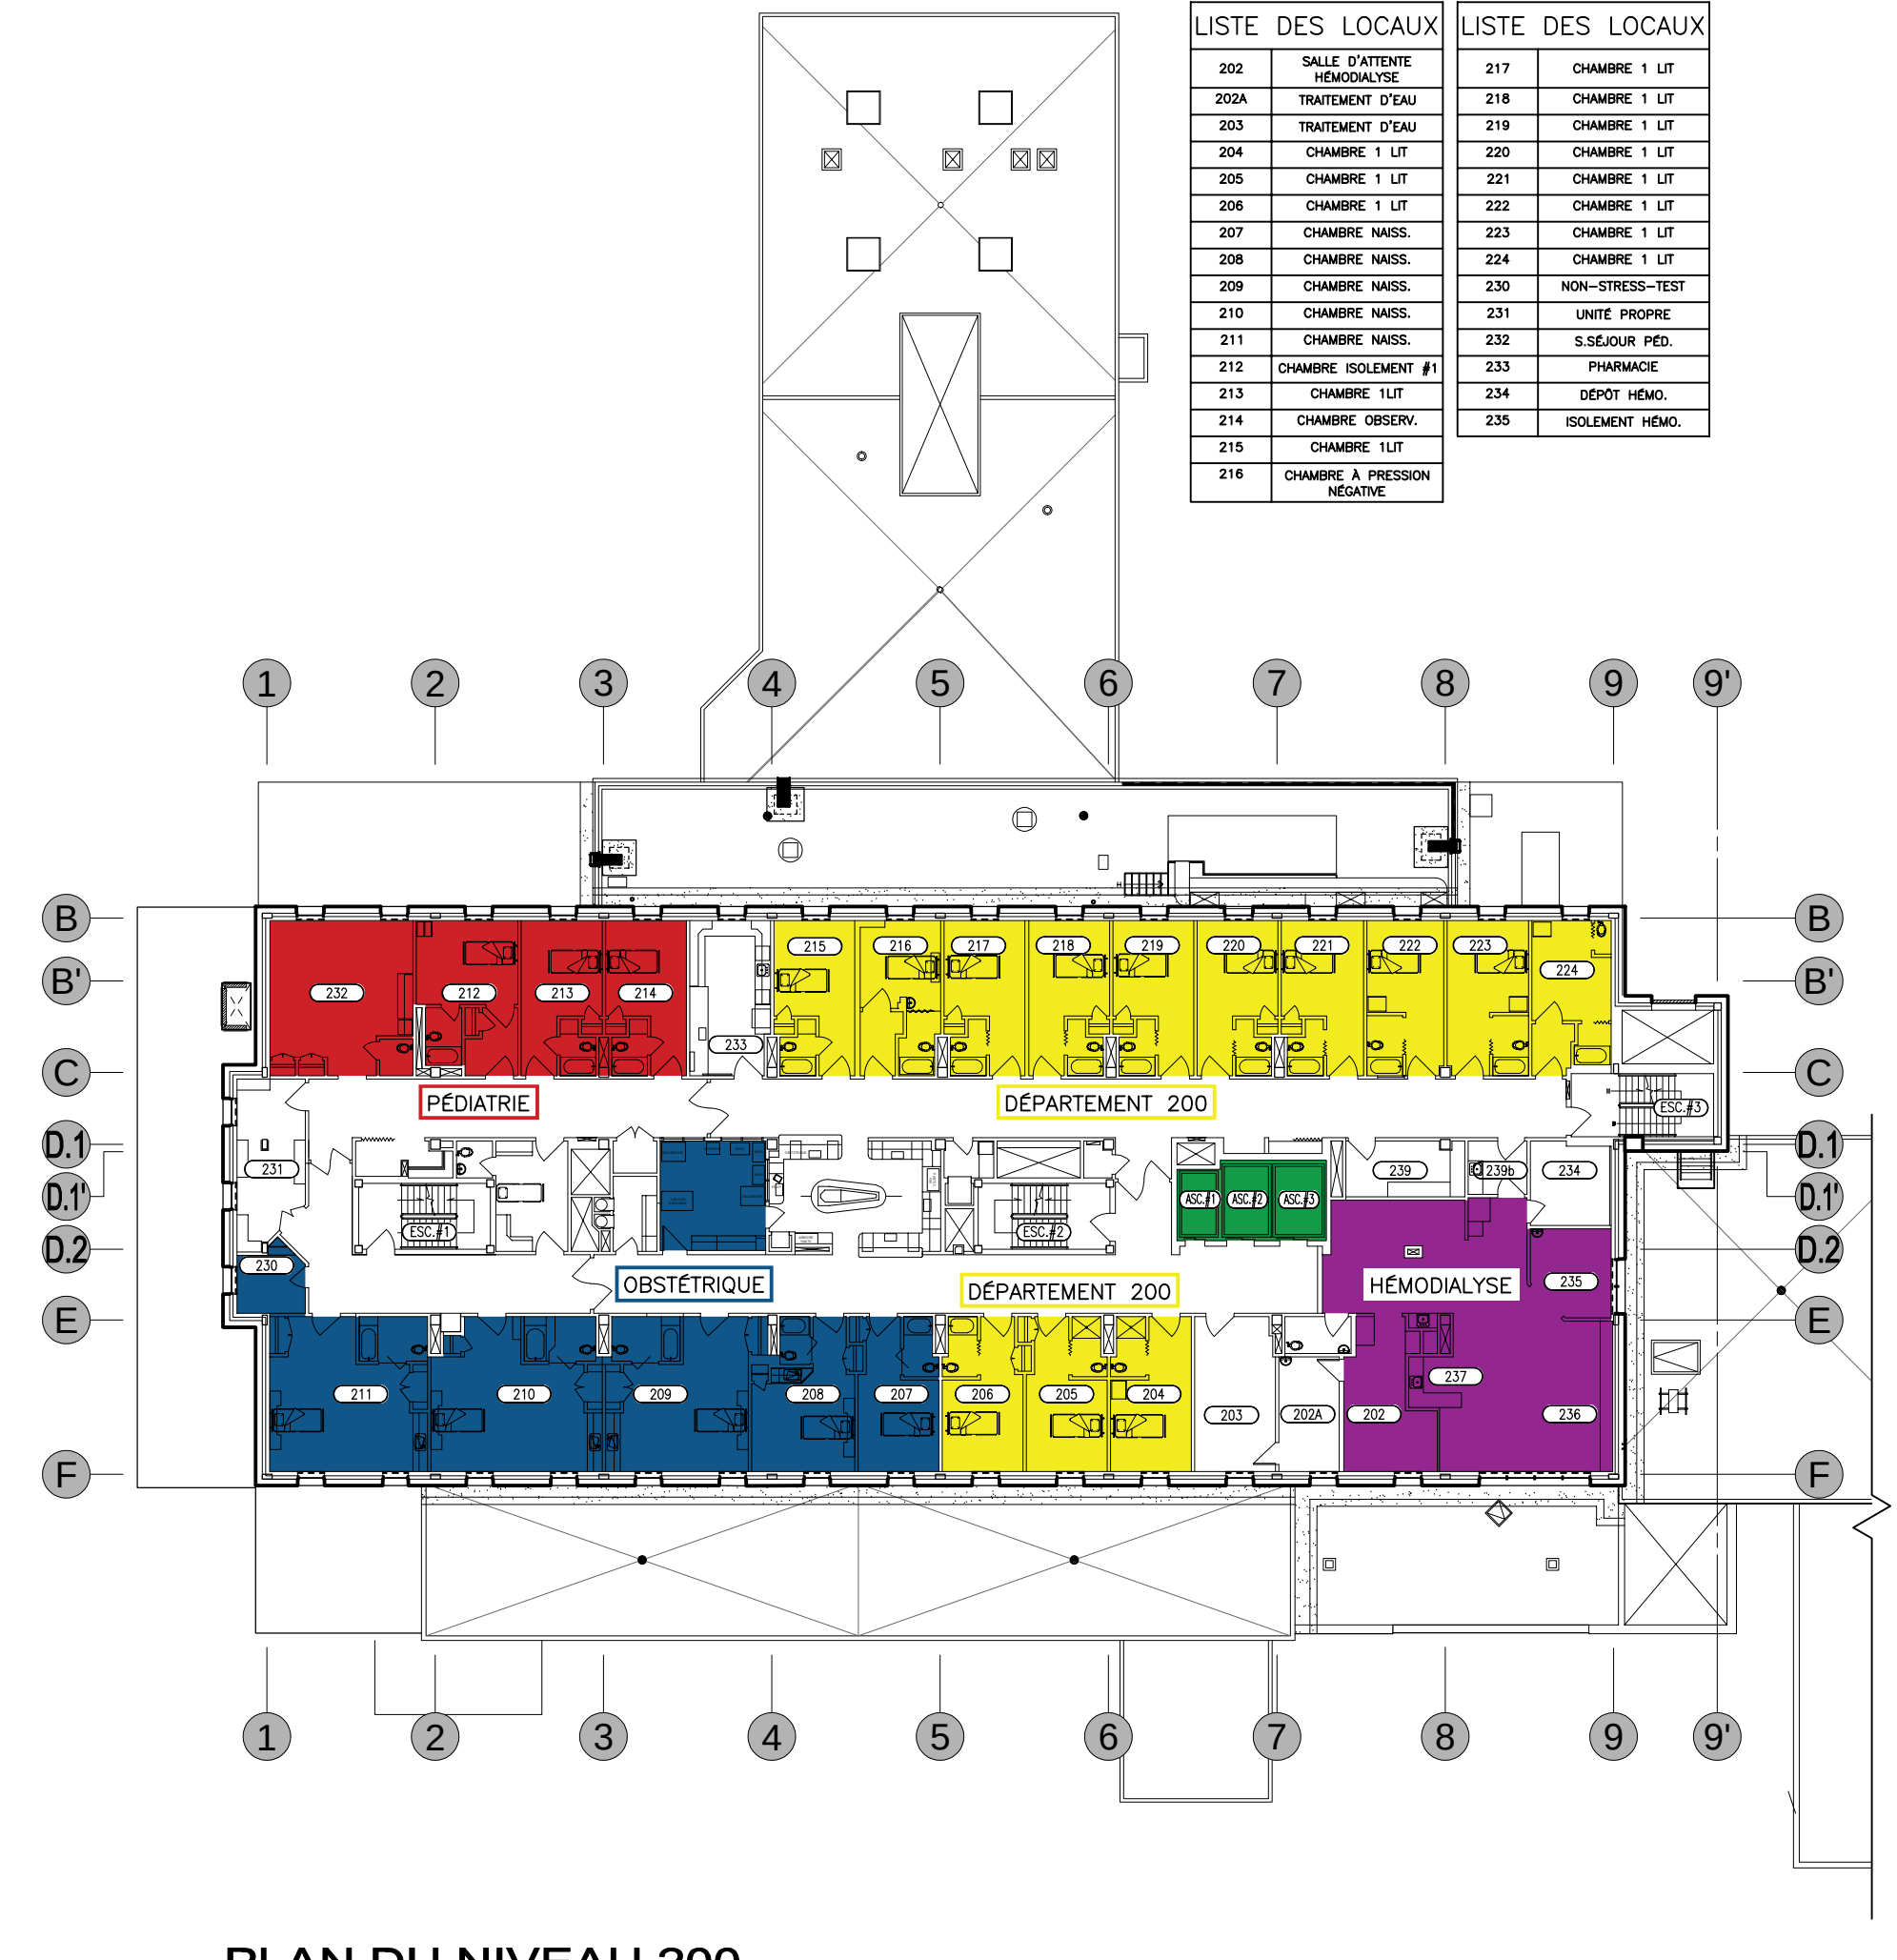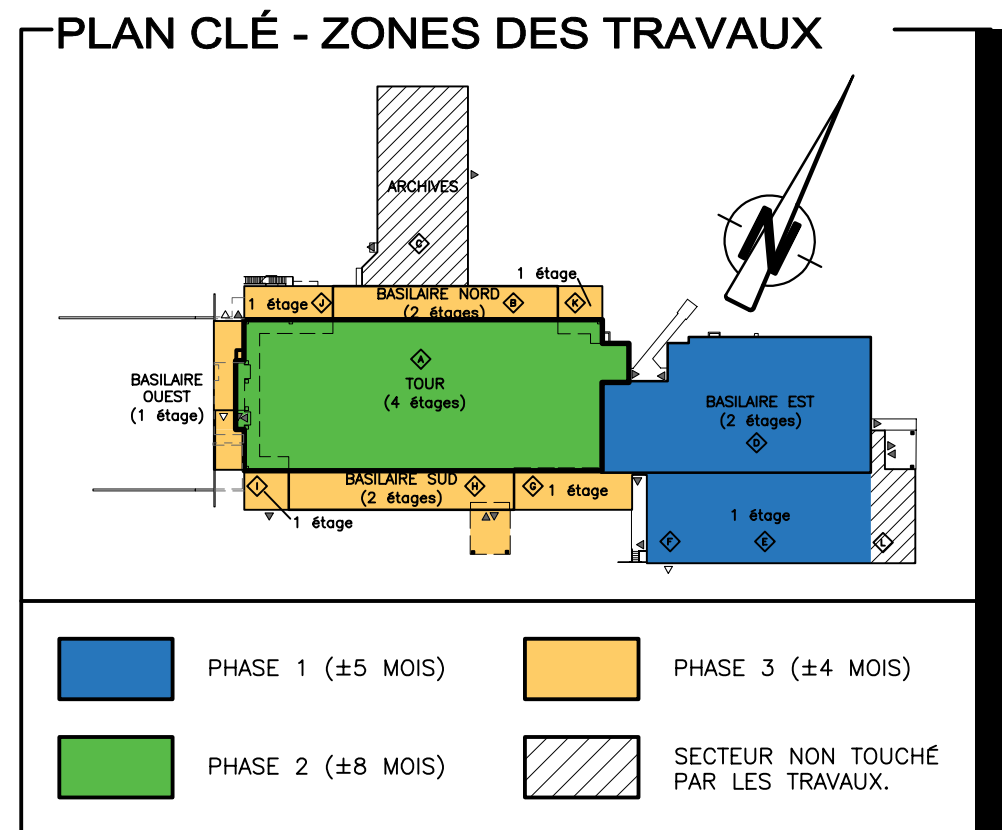

PLAN DU NIVEAU 200
1:300mm

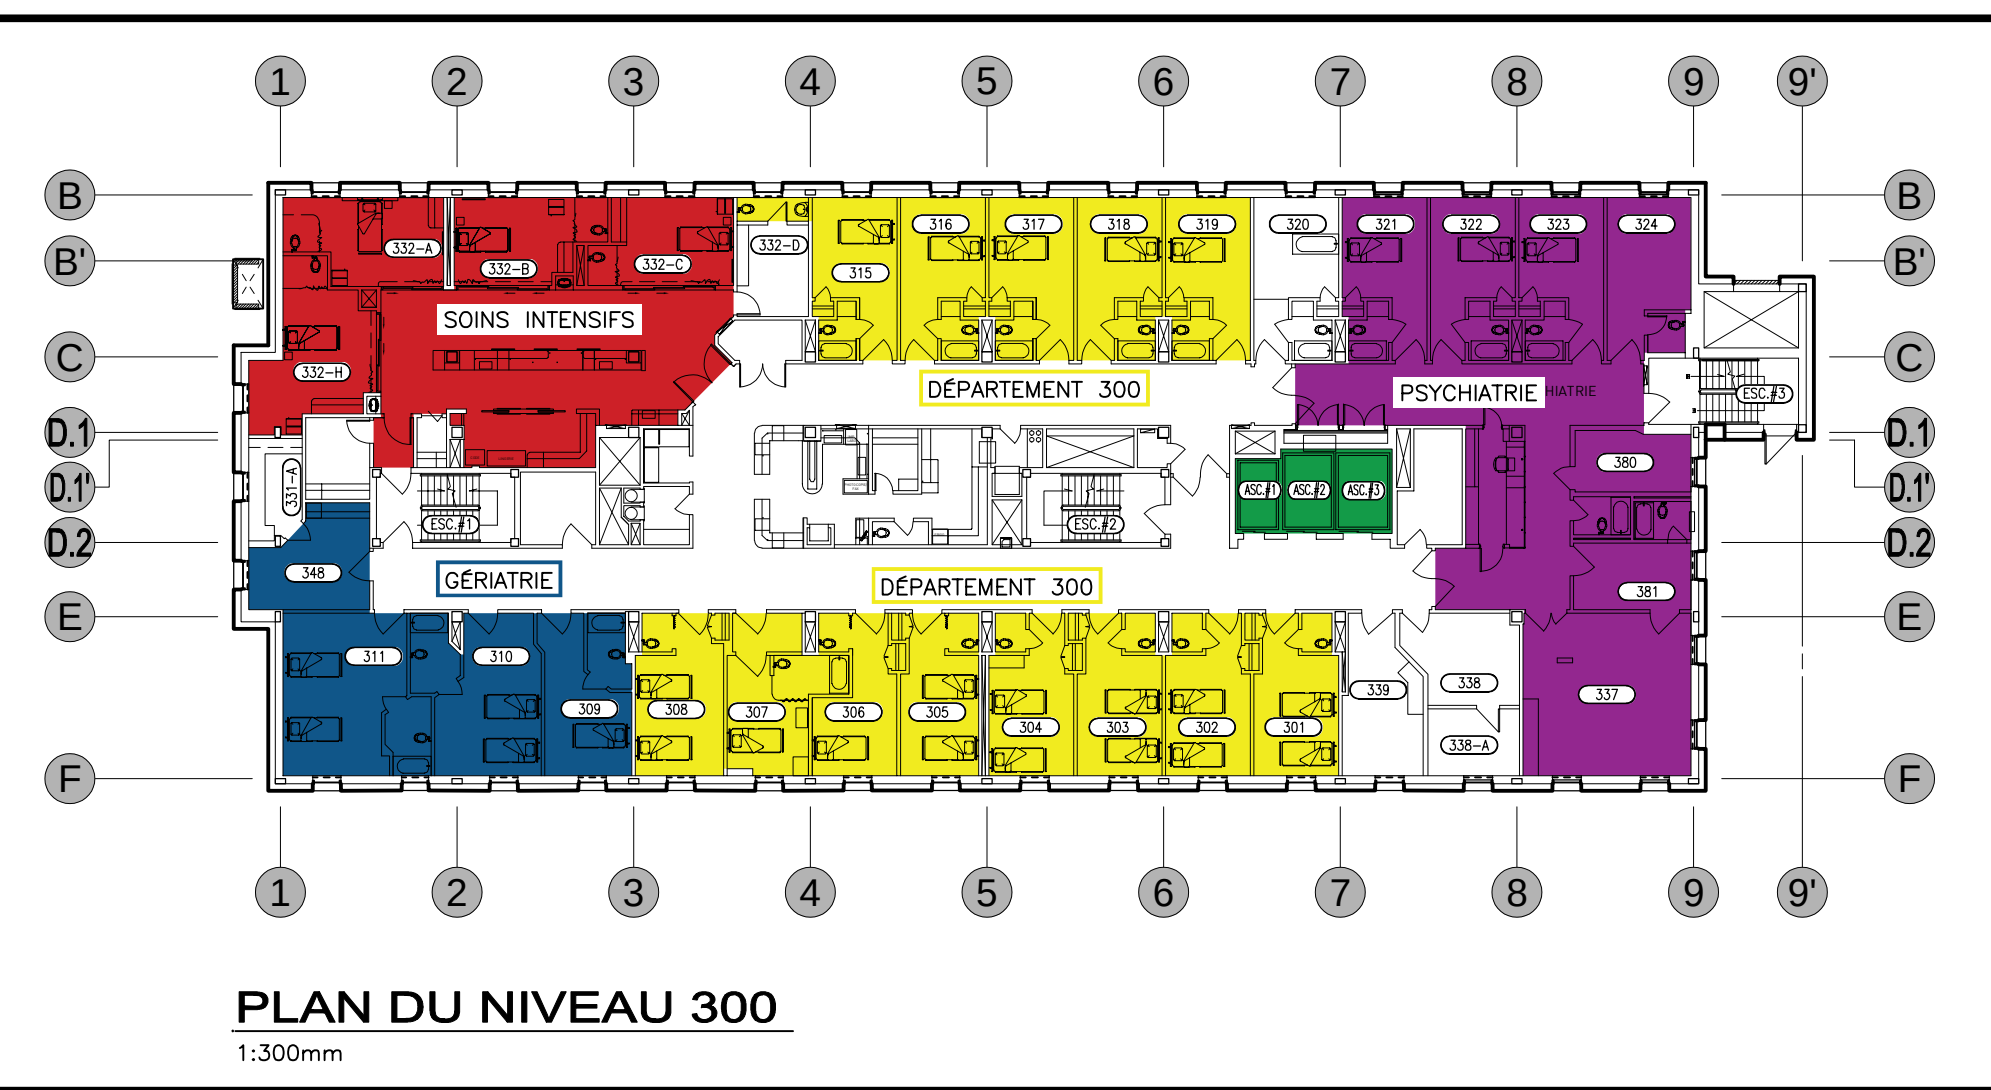

PLAN DU NIVEAU 300
1:300mm

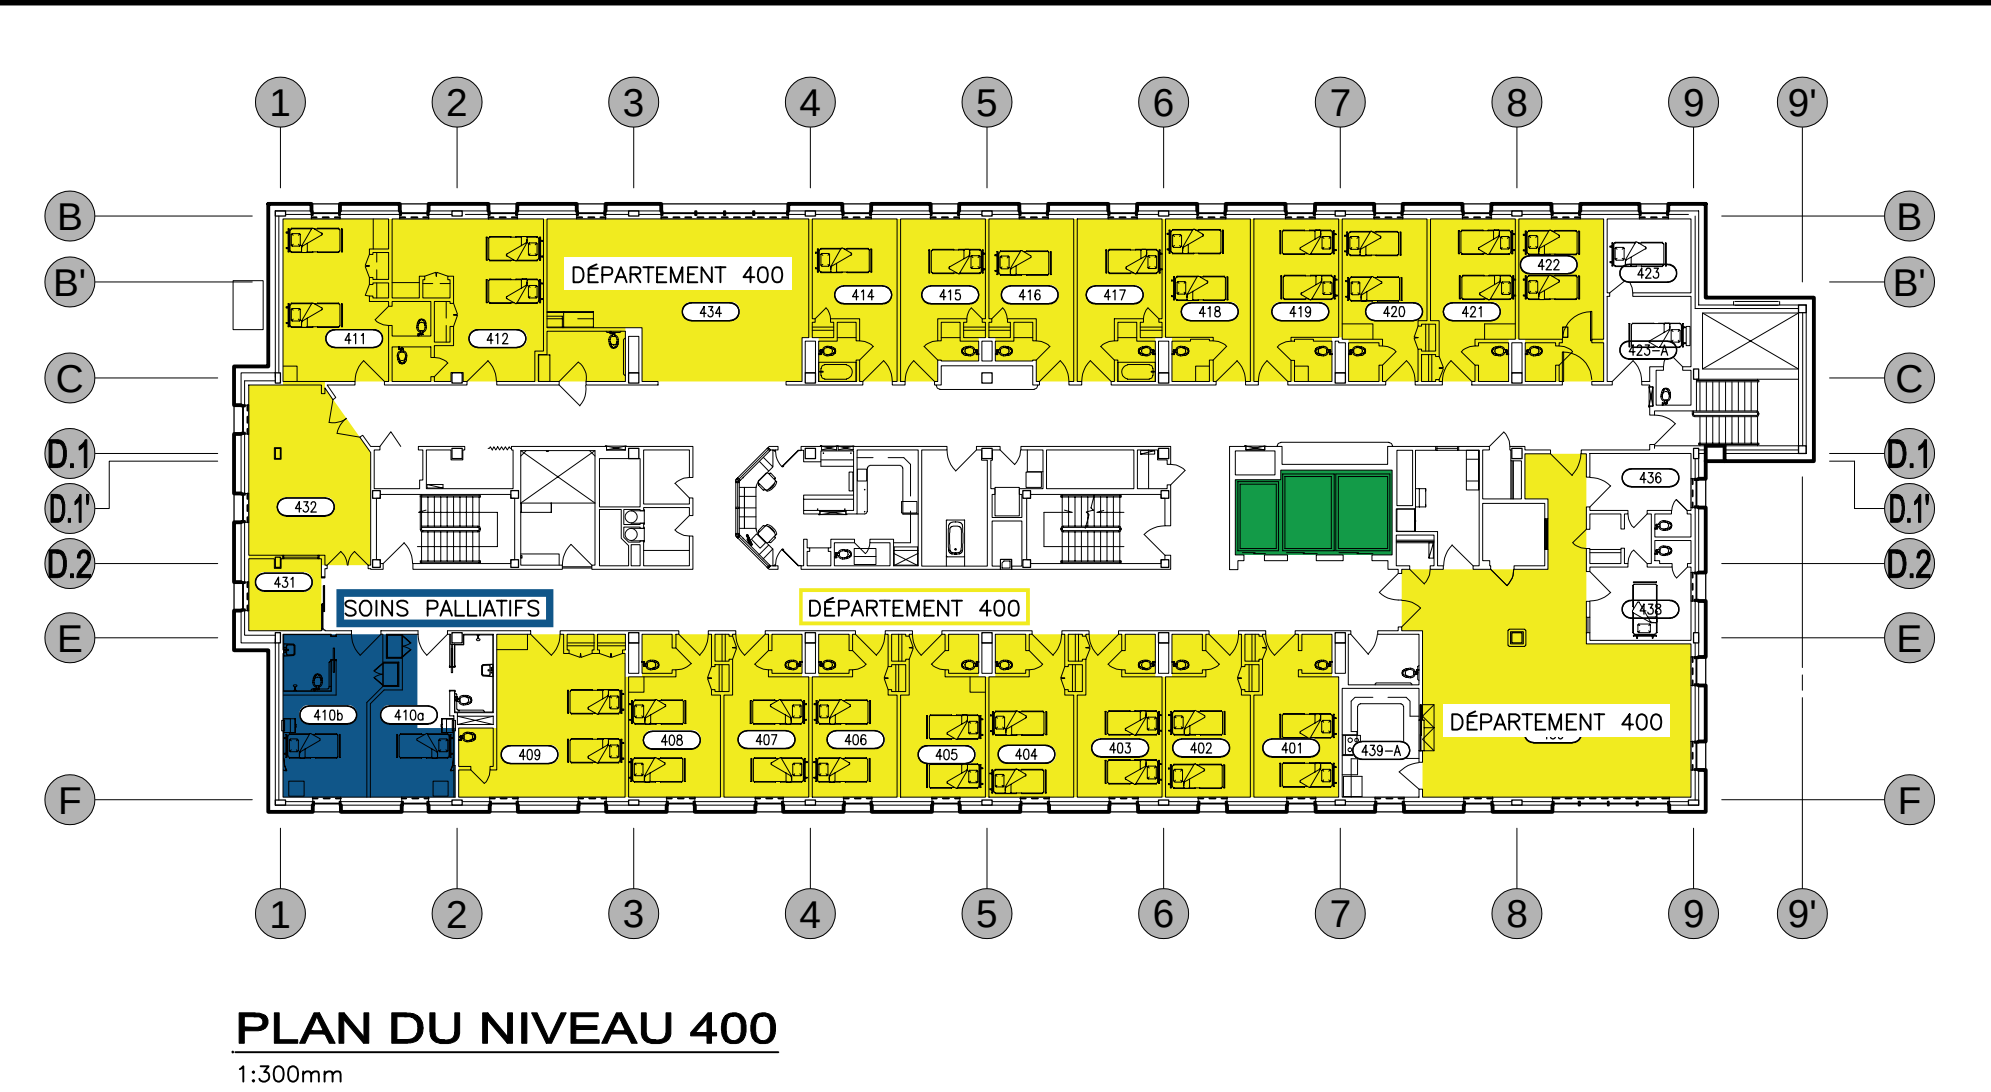

PLAN DU NIVEAU 400
1:300mm

LISTE DES LOCAUX	LISTE DES LOCAUX
202 SALLE D'ATTENTE	217 CHAMBRE 1 LIT
203 TRAITEMENT D'EAU	218 CHAMBRE 1 LIT
204 CHAMBRE 1 LIT	219 CHAMBRE 1 LIT
205 CHAMBRE 1 LIT	220 CHAMBRE 1 LIT
206 CHAMBRE 1 LIT	221 CHAMBRE 1 LIT
207 CHAMBRE 1 LIT	222 CHAMBRE 1 LIT
208 CHAMBRE 1 LIT	223 CHAMBRE 1 LIT
209 CHAMBRE 1 LIT	224 CHAMBRE 1 LIT
210 CHAMBRE 1 LIT	225 CHAMBRE 1 LIT
211 CHAMBRE 1 LIT	226 CHAMBRE 1 LIT
212 CHAMBRE 1 LIT	227 CHAMBRE 1 LIT
213 CHAMBRE 1 LIT	228 CHAMBRE 1 LIT
214 CHAMBRE 1 LIT	229 CHAMBRE 1 LIT
215 CHAMBRE 1 LIT	230 CHAMBRE 1 LIT
216 CHAMBRE 1 LIT	231 CHAMBRE 1 LIT
	232 CHAMBRE 1 LIT
	233 CHAMBRE 1 LIT
	234 CHAMBRE 1 LIT
	235 CHAMBRE 1 LIT

NOTES

GLCRM | Proulx Savard |

GLCRM: 120, Avenue de la Cathédrale, Bureau 201 Québec, QC, G5L 5H7 (418) 722-7655

2406, Ch. des Quatre-Bourgeois, Bureau 100 Québec, QC, G1V 1W5 (418) 647-1700

Proulx Savard Architectes: 75, boul. Arthur-Buies Ouest, Rimouski, QC G5L 5C2 (418) 723-5543

ARCHITECTURE

CONSULTANTS

LEGENDE DES ZONES DU PLAN CLÉ

- TOUR CHAMBRES (NIVEAU 200,300 ET 400) (1974).
- LABORATOIRE (NIVEAU 100)(1990).
- ARCHIVES (REZ-DE-CHAUSSEE)(2001).
- ADMINISTRATIVE (NIVEAU 100) (2005) ET CLINIQUE EXTERNES (REZ-DE-CHAUSSEE) (1974)
- ONCOLOGIE (REZ-DE-CHAUSSEE) (1974).
- IRM (REZ-DE-CHAUSSEE) (2007)
- BASILAIRE SUD-EST(1974)
- CLINIQUE CHIRURGIE D'UN JOUR (NIVEAU 100) (2005)ET URGENCE (REZ-DE-CHAUSSEE)
- BASILAIRE SUD-OUEST (1974)
- BASILAIRE NORD-OUEST (1974)
- BASILAIRE NORD-EST (1974)
- ONCOLOGIE (REZ-DE-CHAUSSEE) (2023)

LEGENDE

NO DE LOCAL.

AXE EXISTANT.

NE DOIT PAS SERVIR À L'EXÉCUTION

Le présent document est émis pour la seule fin identifiée. Son contenu est protégé par les droits d'auteur et toute reproduction ou modification, partielle ou totale, est interdite sans l'autorisation écrite de gagnon, letellier, cyr, ricard, mathieu, proulx, savard consortium d'architectes.

010

DESSINATEUR (S) : 24-107 / 1657-24

DATE : SEPTEMBRE 2024

ÉCHELLE : INDICÉE

PROJET : HÔPITAL DE CHANDLER, (Réfection de l'enveloppe)

PROPRIÉTAIRE : Santé Québec

REVISIONS

DATE

No