



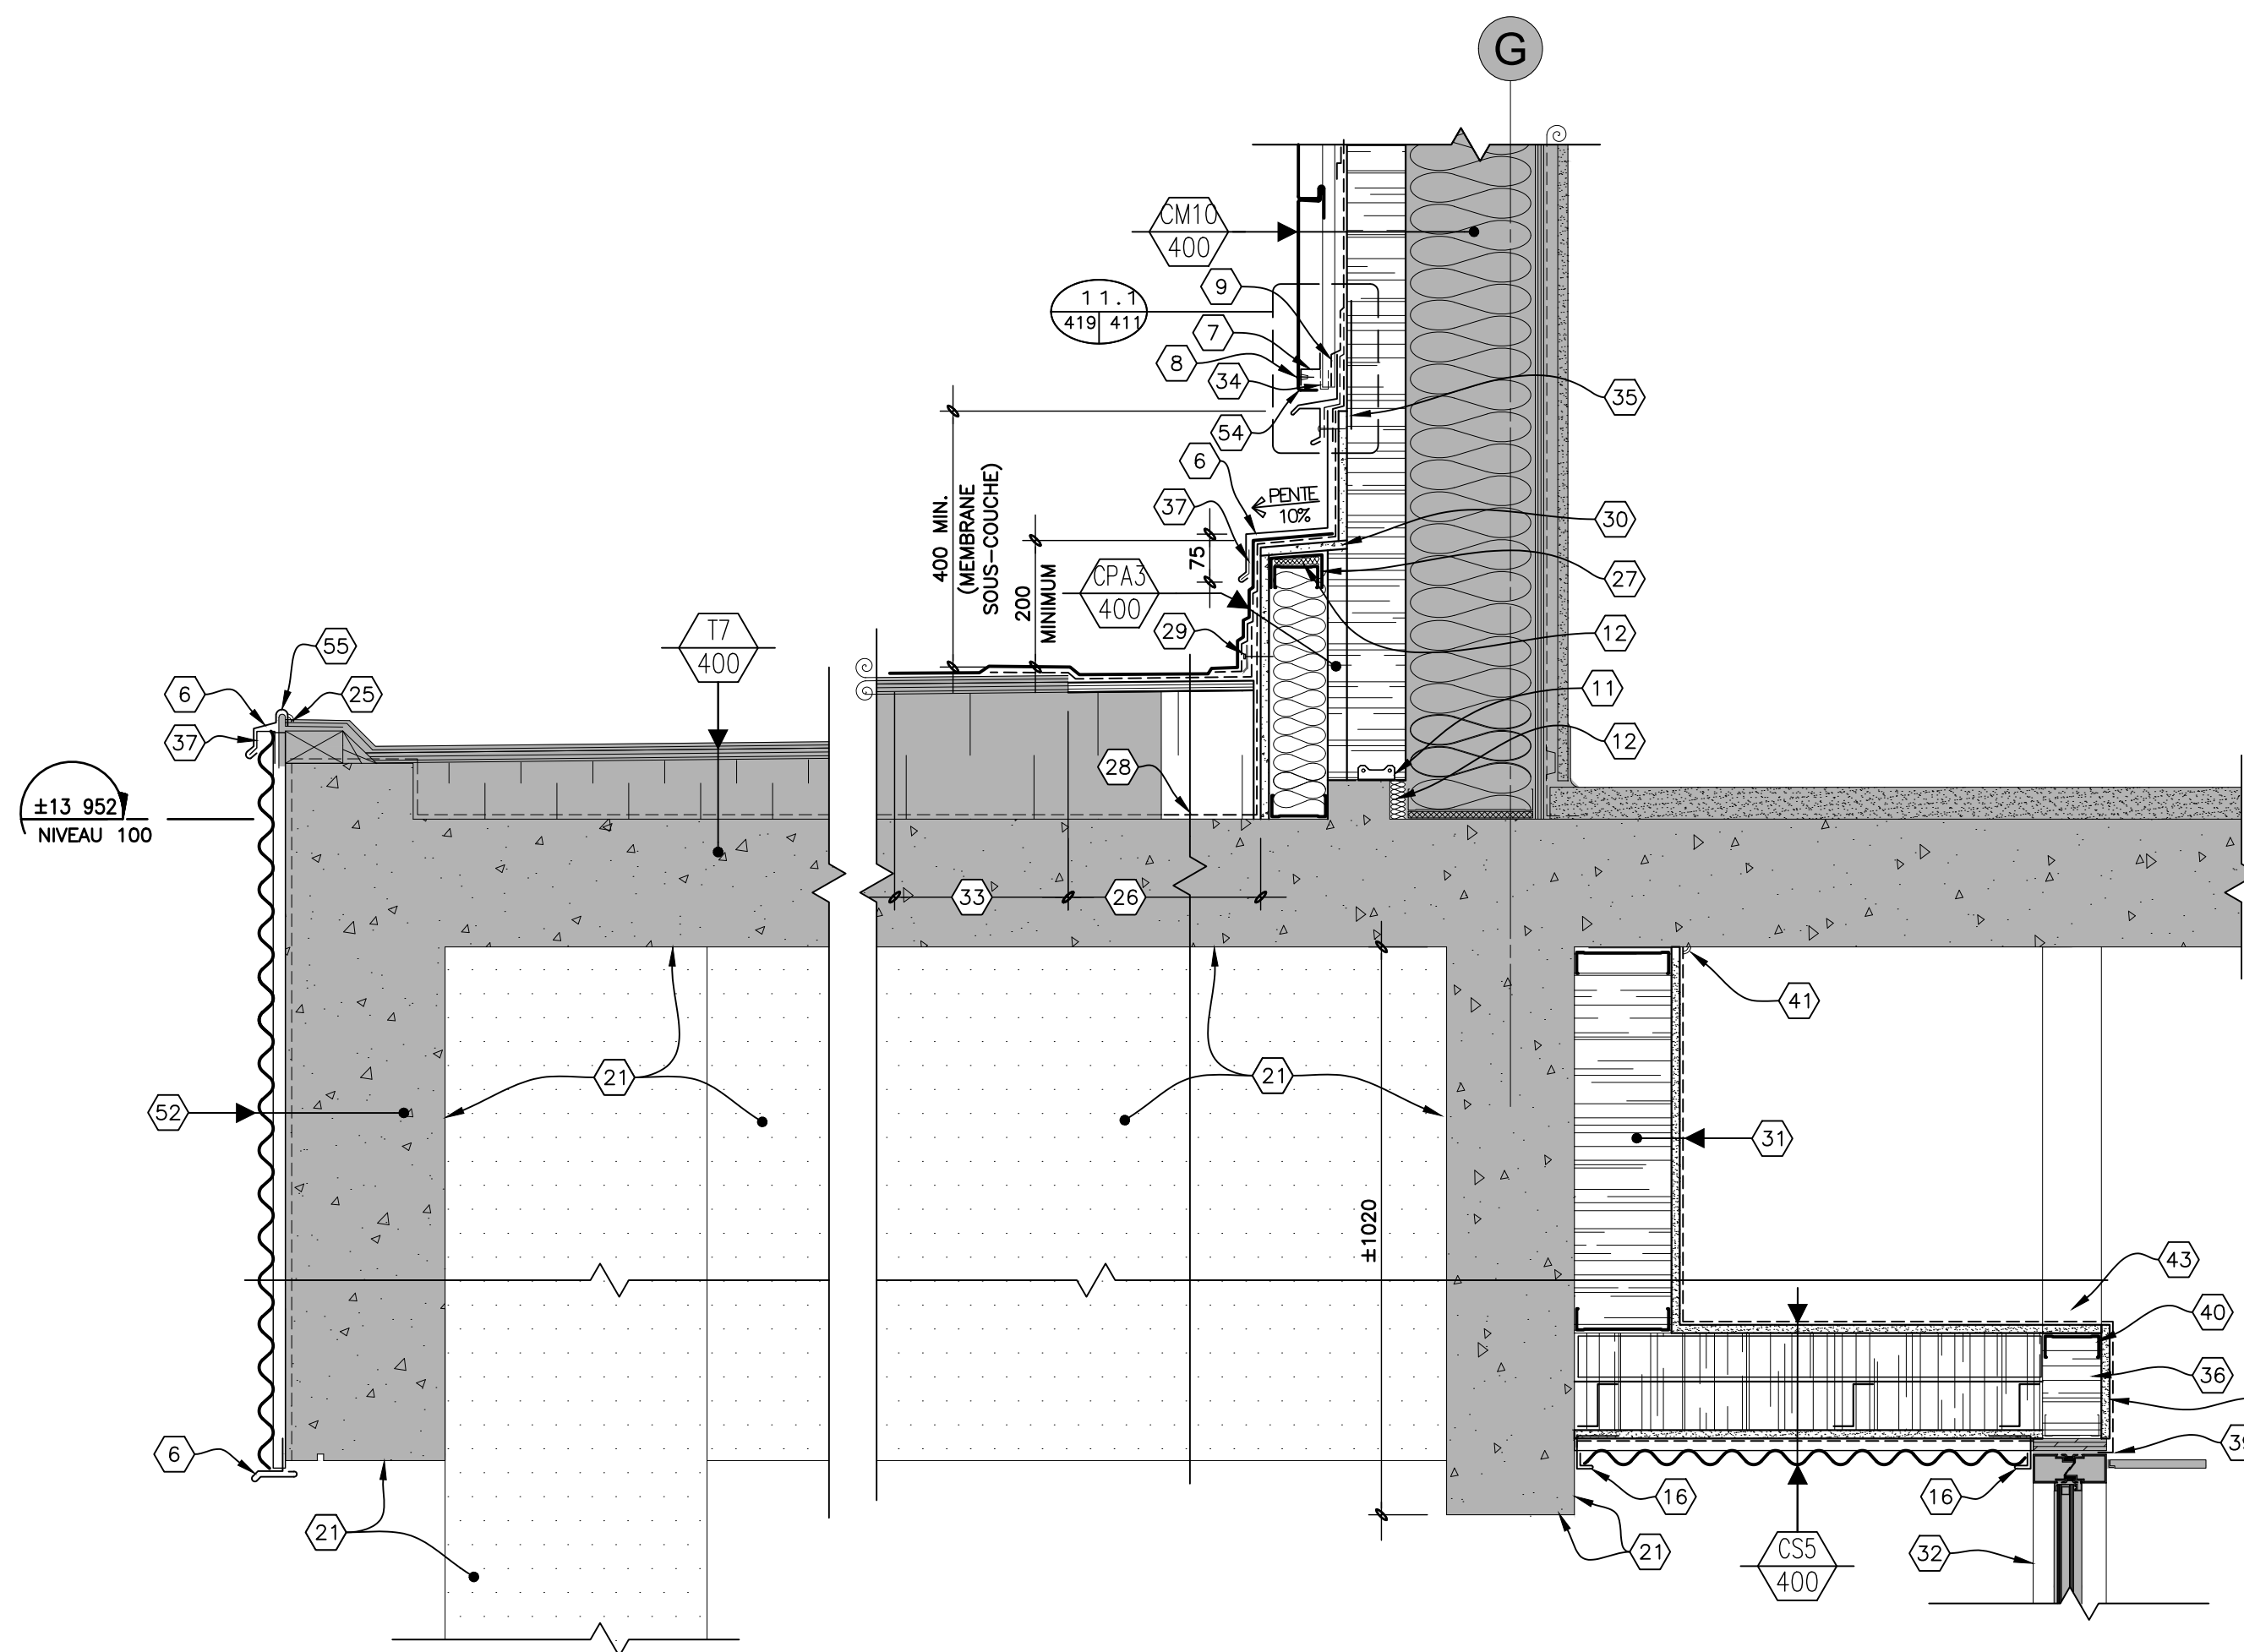

**DÉTAIL TYPE MARQUISE**  
1:10mm (ENTRÉE PRINCIPALE)

**DÉTAIL TYPE MARQUISE**  
1:10mm (ENTRÉE PRINCIPALE)

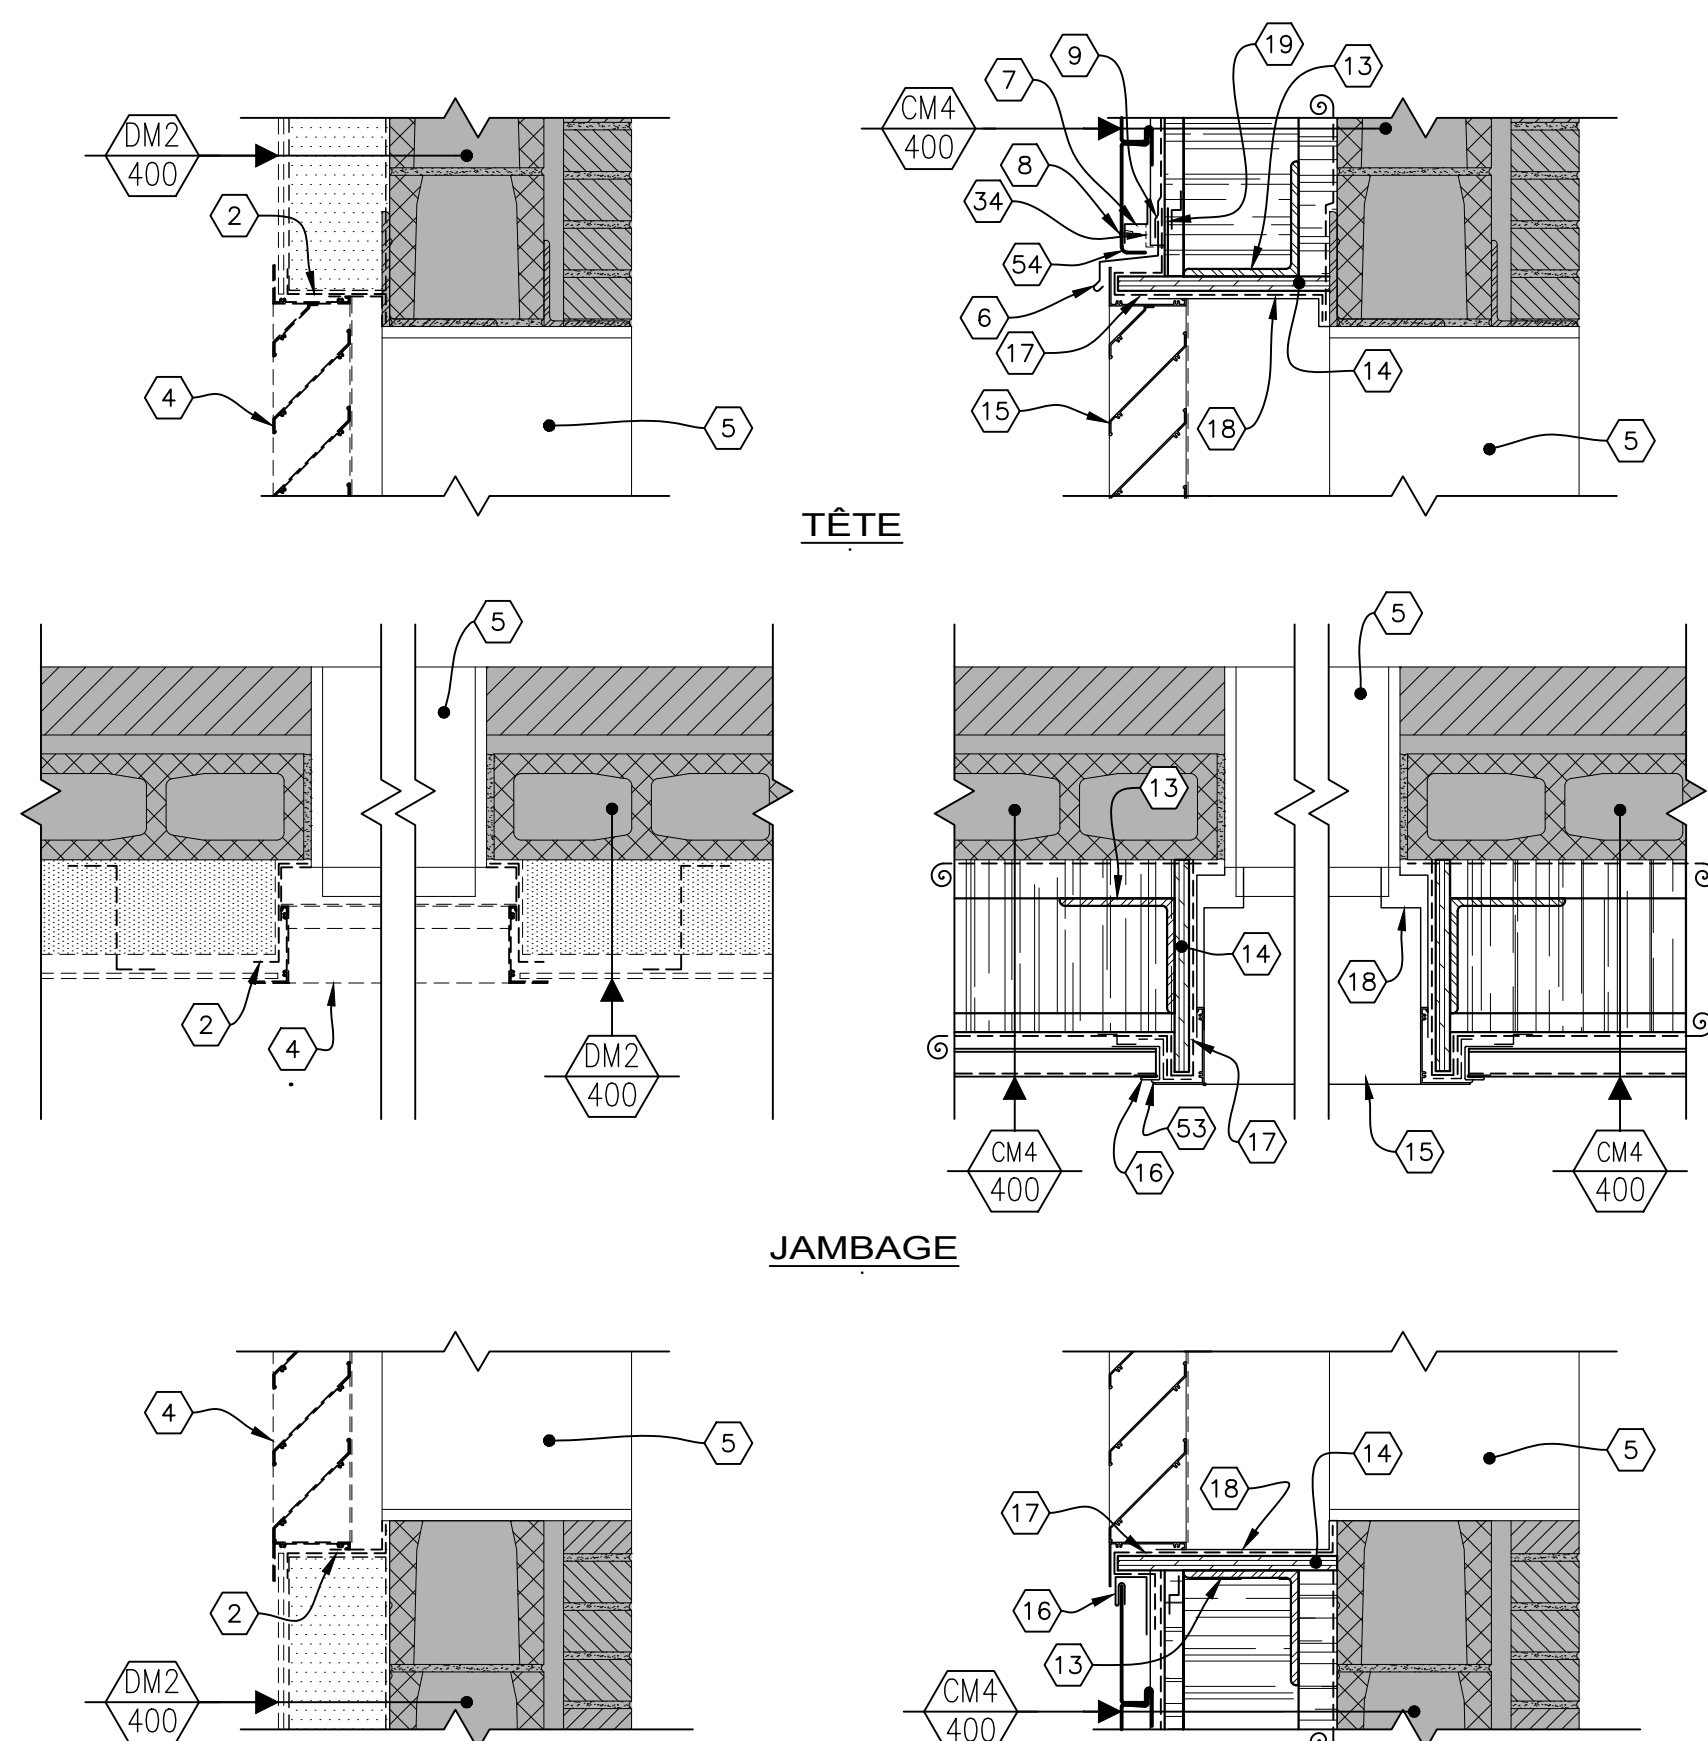

## CONSTRUCTION


**DÉTAIL PERSIENNE**  
1:10mm (ESCALIER #3 - TOUR)

**DÉTAIL PERSIENNE**  
1:10mm (ESCALIER #3 - TOUR)

|                                                                                       |                                                                                          |
|---------------------------------------------------------------------------------------|------------------------------------------------------------------------------------------|
|  | EXISTANT À CONSERVER.                                                                    |
|  | ÉLÉMENT À DÉMOLIR.                                                                       |
|  | AXE EXISTANT                                                                             |
|  | EXTÉRIEUR DE LA STRUCTURE DE<br>BETON EXISTANTE DE LA TOUR.                              |
|  | NOUVEL AXE; FACE EXTÉRIEURE DES<br>BARRES Z ET COLOMBAGES DE LA TOUR.<br>VOIR STRUCTURE. |

- (1) SOLIN EXISTANT À DÉMOURIR.
- (2) TÔLE PLUÏÉE EXISTANTE À DÉMOURIR.
- (3) MOULURE EN ALUMINIUM À DÉMOURIR.
- (4) PERSIENNE EXISTANTE À ENLEVER, GRATTER, PEINDRE ET RÉINSTALLER, COMPOSÉ DE 4 SECTIONS DE ±1900 LARGEUR X 2440mm DE HAUTEUR CHAQUE.
- (5) CONDUIT DE MÉCANIQUE EXISTANT À CONSERVER, VOIR INGENIEUR.
- (6) SOLIN EN ACIER ÉMAILLÉ, CAL.24 (JOINTS AGRAFÉS).
- (7) PLIAGE DE TÔLE EN ACIER GALVANISÉ, CAL.22.
- (8) RIVET EN ACIER INOXYDABLE.
- (9) SCELLER LA MEMBRANE PARE-INTÉPÉRIES SUR LE SOLIN AVEC UN RUBAN AUTOCOLLANT.
- (10) POUTRE D'ACIER, VOIR STRUCTURE.
- (11) CONNECTEUR À CHAQUE COLOMBAGES OU BARRE "Z" SELON LE CAS, VOIR STRUCTURE.
- (12) REMPLIR L'ESPACE DE LAINE DE FIBRE DE VERRE.
- (13) STRUCTURE EN "L" EN ACIER SUR TOUT LE PÉRIMÈTRE DE LA PERSIENNE, VOIR STRUCTURE.
- (14) CONTREPLAQUE À PLUS 19mm SUR TOUT LE PÉRIMÈTRE DE LA PERSIENNE.
- (15) PERSIENNE EXISTANTE REPEINTÉ RÉINSTALLÉE.
- (16) MOULURE EN "J" EN ACIER ÉMAILLÉ, CAL.24.
- (17) MEMBRANE AUTOCOLLANTE SUR TOUT LE PÉRIMÈTRE DE LA PERSIENNE.
- (18) PROLONGER LE CONDUIT DE LA PERSIENNE, VOIR MÉCANIQUE.
- (19) TÔLE D'APPUI EN ACIER GALVANISÉ CAL. 18.
- (20) SOLIN EXISTANT À COUPER.
- (21) POUTRES, DALLÉ ET COLONNES EXISTANTES EN BÉTON À GRATTER ET À PEINDRE.
- (22) OUVERTURE À FAIRE DANS LA TOITURE EXISTANTE SUR ±600mm POUR LA CONSTRUCTION DU NOUVEAU PARAPET. VOIR COMPOSITION DE TOIT SUR LE DETAIL.
- (23) REMONTER DE MEMBRANES ET SUPPORT À DÉMOURIR.
- (24) PIÈCE DE BOIS EXISTANTE À DÉMOURIR.
- (25) SCELLANT ELASTOMÈRE.
- (26) RAGRÉER LA TOITURE TEL QUE L'EXISTANT, VOIR COMPOSITION SUR LE DETAIL.
- (27) PLIAGE DE TÔLE EN "U", CAL.16 EN ACIER GALVANISÉ.
- (28) MEMBRANE PARE-VAPEUR AUTOCOLLANTE.
- (29) BARRE D'ANCRAGE DE LA MEMBRANE.
- (30) PANNEAU DE CIMENT 13mm.
- (31) -MEMBRANE PARE-VAPEUR AUTOCOLLANTE;  
-PANNEAU DE MAT DE FIBRE DE VERRE 13mm;  
-COLOMBAGE MÉTALLIQUE 92mmx152mm Ø400mm  
-LAINE DE FIBRE DE ROCHE 152mm.
- (32) PORTE ET CADRE EN ALUMINIUM EXISTANT À CONSERVER.
- (33) CHEVAUCHER LA NOUVELLE MEMBRANE SUR LES MEMBRANES DE LA TOITURE EXISTANTE SUR MINIMUM 300mm. DÉGRANULER LA MEMBRANE EXISTANTE AU PRÉALABLE.
- (34) MOUSTIQUAIRE.
- (35) TÔLE D'APPUI EN ACIER GALVANISÉ CAL. 18. 200mm DE HAUTEUR.
- (36) REMPLIR LE COLOMBAGE EXISTANT DE LAINE DE FIBRE DE VERRE SUR 150mm DE HAUTEUR.
- (37) AGRAFE EN ACIER GALVANISÉ, CAL.24 CONTINUE.
- (38) PANNEAU D'ISOLANT À ENLEVER.
- (39) INSÉRER LE PARE-VAPEUR LE PLUS LOIN POSSIBLE SOUS LE CADRE. SCELLER LA MEMBRANE AU CADRE.
- (40) COLOMBAGE D'ACIER DE DIMENSIONS REQUISE.
- (41) SCELLER LE PARE-VAPEUR À LA DALLÉ DE BÉTON.
- (42) PANNEAU DE MÂT DE FIBRE DE VERRE 13mm.
- (43) SCELLER LE PARE-VAPEUR SUR LES COLOMBAGES EXISTANT.
- (44) PLAQUE D'ACIER PONCTUELLE, VOIR STRUCTURE.
- (45) BRIQUES EXISTANTES À ENLEVER, NETTOYER SUR HAUTEUR ET LARGEUR REQUISE POUR L'INSTALLATION DE LA POUTRE.
- (46) BRIQUES EXISTANTES RÉINSTALLÉES.
- (47) TÔLE D'APPUI EN ACIER GALVANISÉ CAL.18 PENTE 10%.
- (48) MEMBRANE AUTOCOLLANTE.
- (49) BARRE "Z" CAL.16 VERTICALE Ø400mm c/c.
- (50) PLIAGE EN "J" EN ACIER GALVANISÉ CAL.18.
- (51) COLOMBAGE MÉTALLIQUE 92mm Ø400mm c/c.
- (52) - PAREMENT D'ACIER CORRUGUÉ 22mm, CAL.24, HORIZONTAL;  
- BARRE "Z" 19mm D'ÉPAISSEUR, CAL.16 Ø 405mm C/C, VERTICALE;  
- BÉTON EXISTANT.
- (53) SCELLANT CONTINUE.
- (54) BOUT DU PANNEAU REPLIÉ VERS L'INTÉRIEUR.
- (55) AGRAFER LE NOUVEAU SOLIN AVEC CELUI EXISTANT.






Le présent document est émis pour la seule fin identifiée. Son contenu est protégé par les droits d'auteur et toute reproduction ou modification, partielle ou totale, est interdite sans l'autorisation écrite de gagnon, letellier, cyr, ricard, mathieu, proulx, savard consortium d'architectes.

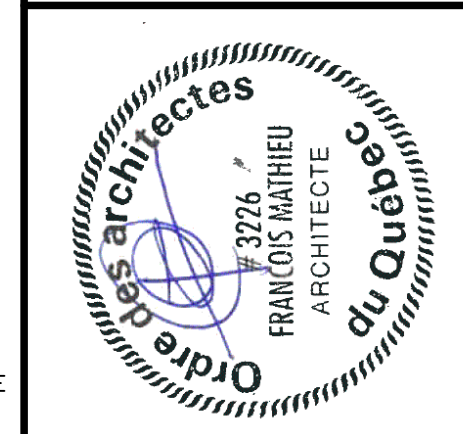

|                                                                         |   |  |                                  |
|-------------------------------------------------------------------------|---|--|----------------------------------|
| FISSIN<br><b>COUPE DE MUR TYPE</b><br><b>DEMOLITION ET CONSTRUCTION</b> | DESSINATEUR (S)<br>O.B. ALL.                                                                                              |  | DOSSIER No.<br>24-1109 / 1637-24 |
|                                                                         | ÉCHELLE<br>INDUITE   |  | DATE<br>SEPTEMBRE 2024           |
|                                                                         | PROJET<br>HÔPITAL DE CHANDLER,<br>Chandler<br>Réfection de l'enveloppe                                                    |  |                                  |
|                                                                         | PROPRIÉTAIRE<br> <b>Santé Québec</b> |  |                                  |

# JESSIN COUPE DE MUR TYPE DÉMOLITION ET CONSTRUCTION

PROJET  
HÔPITAL DE CHANDLER,

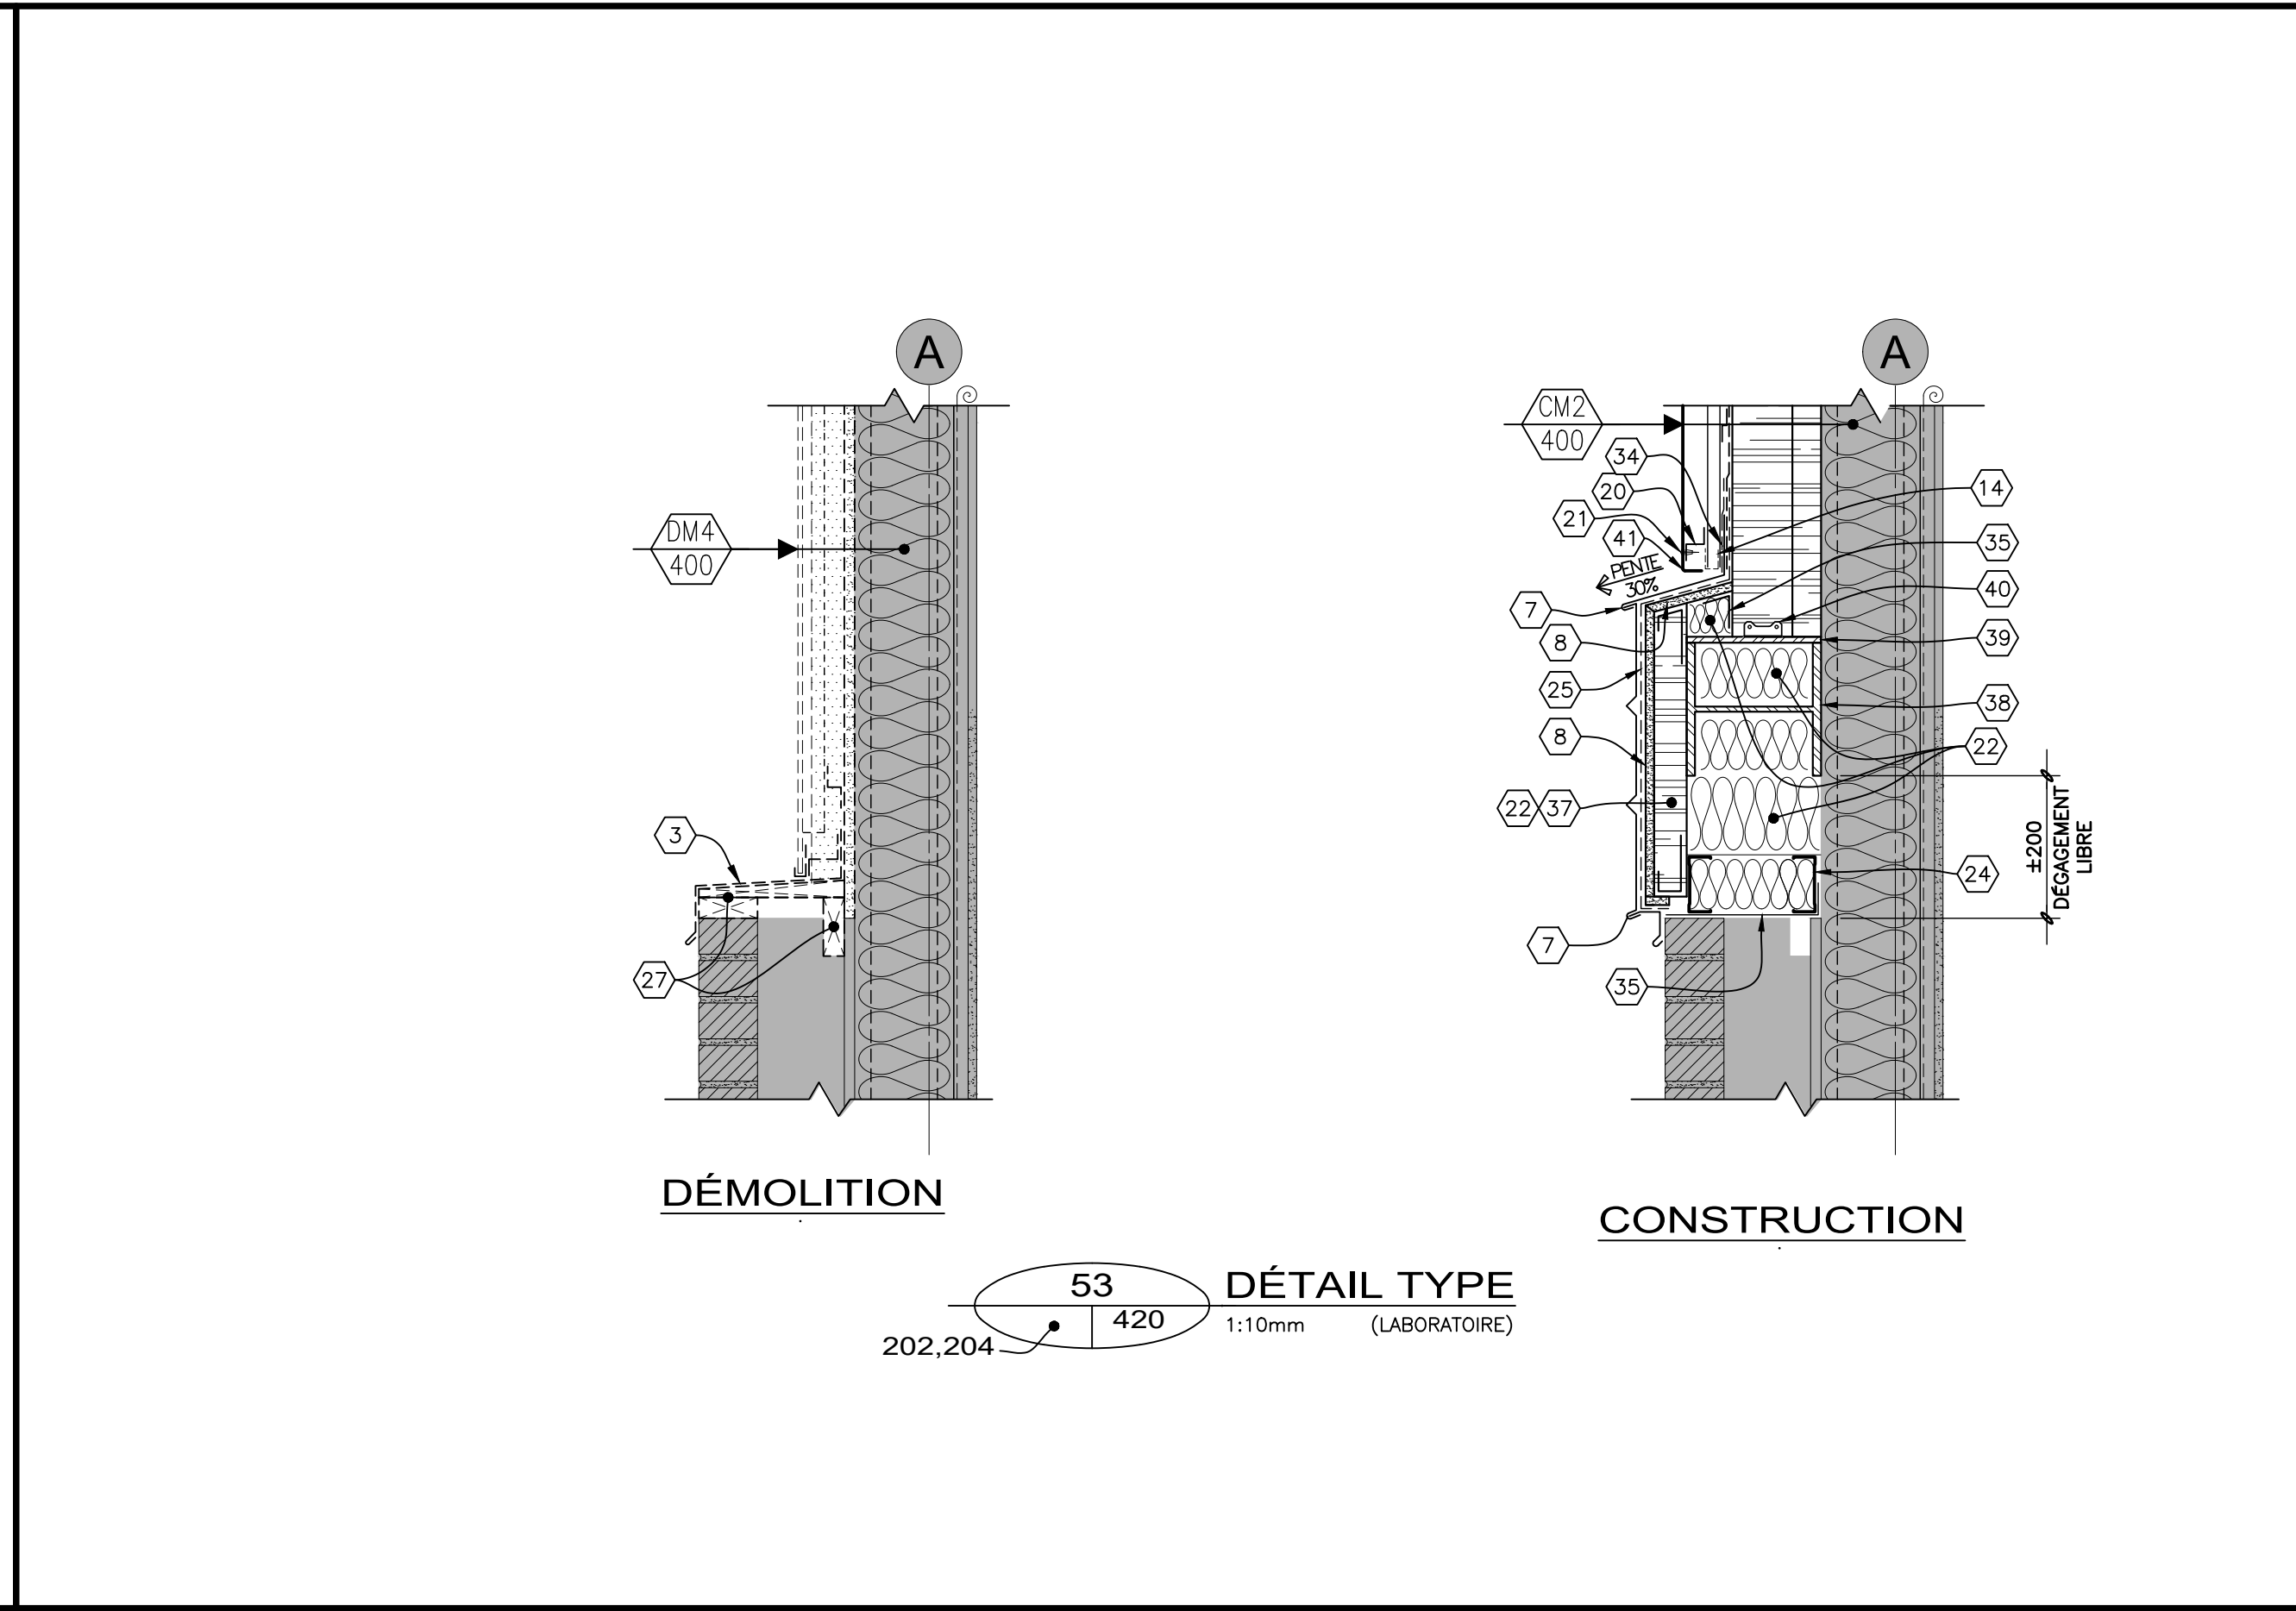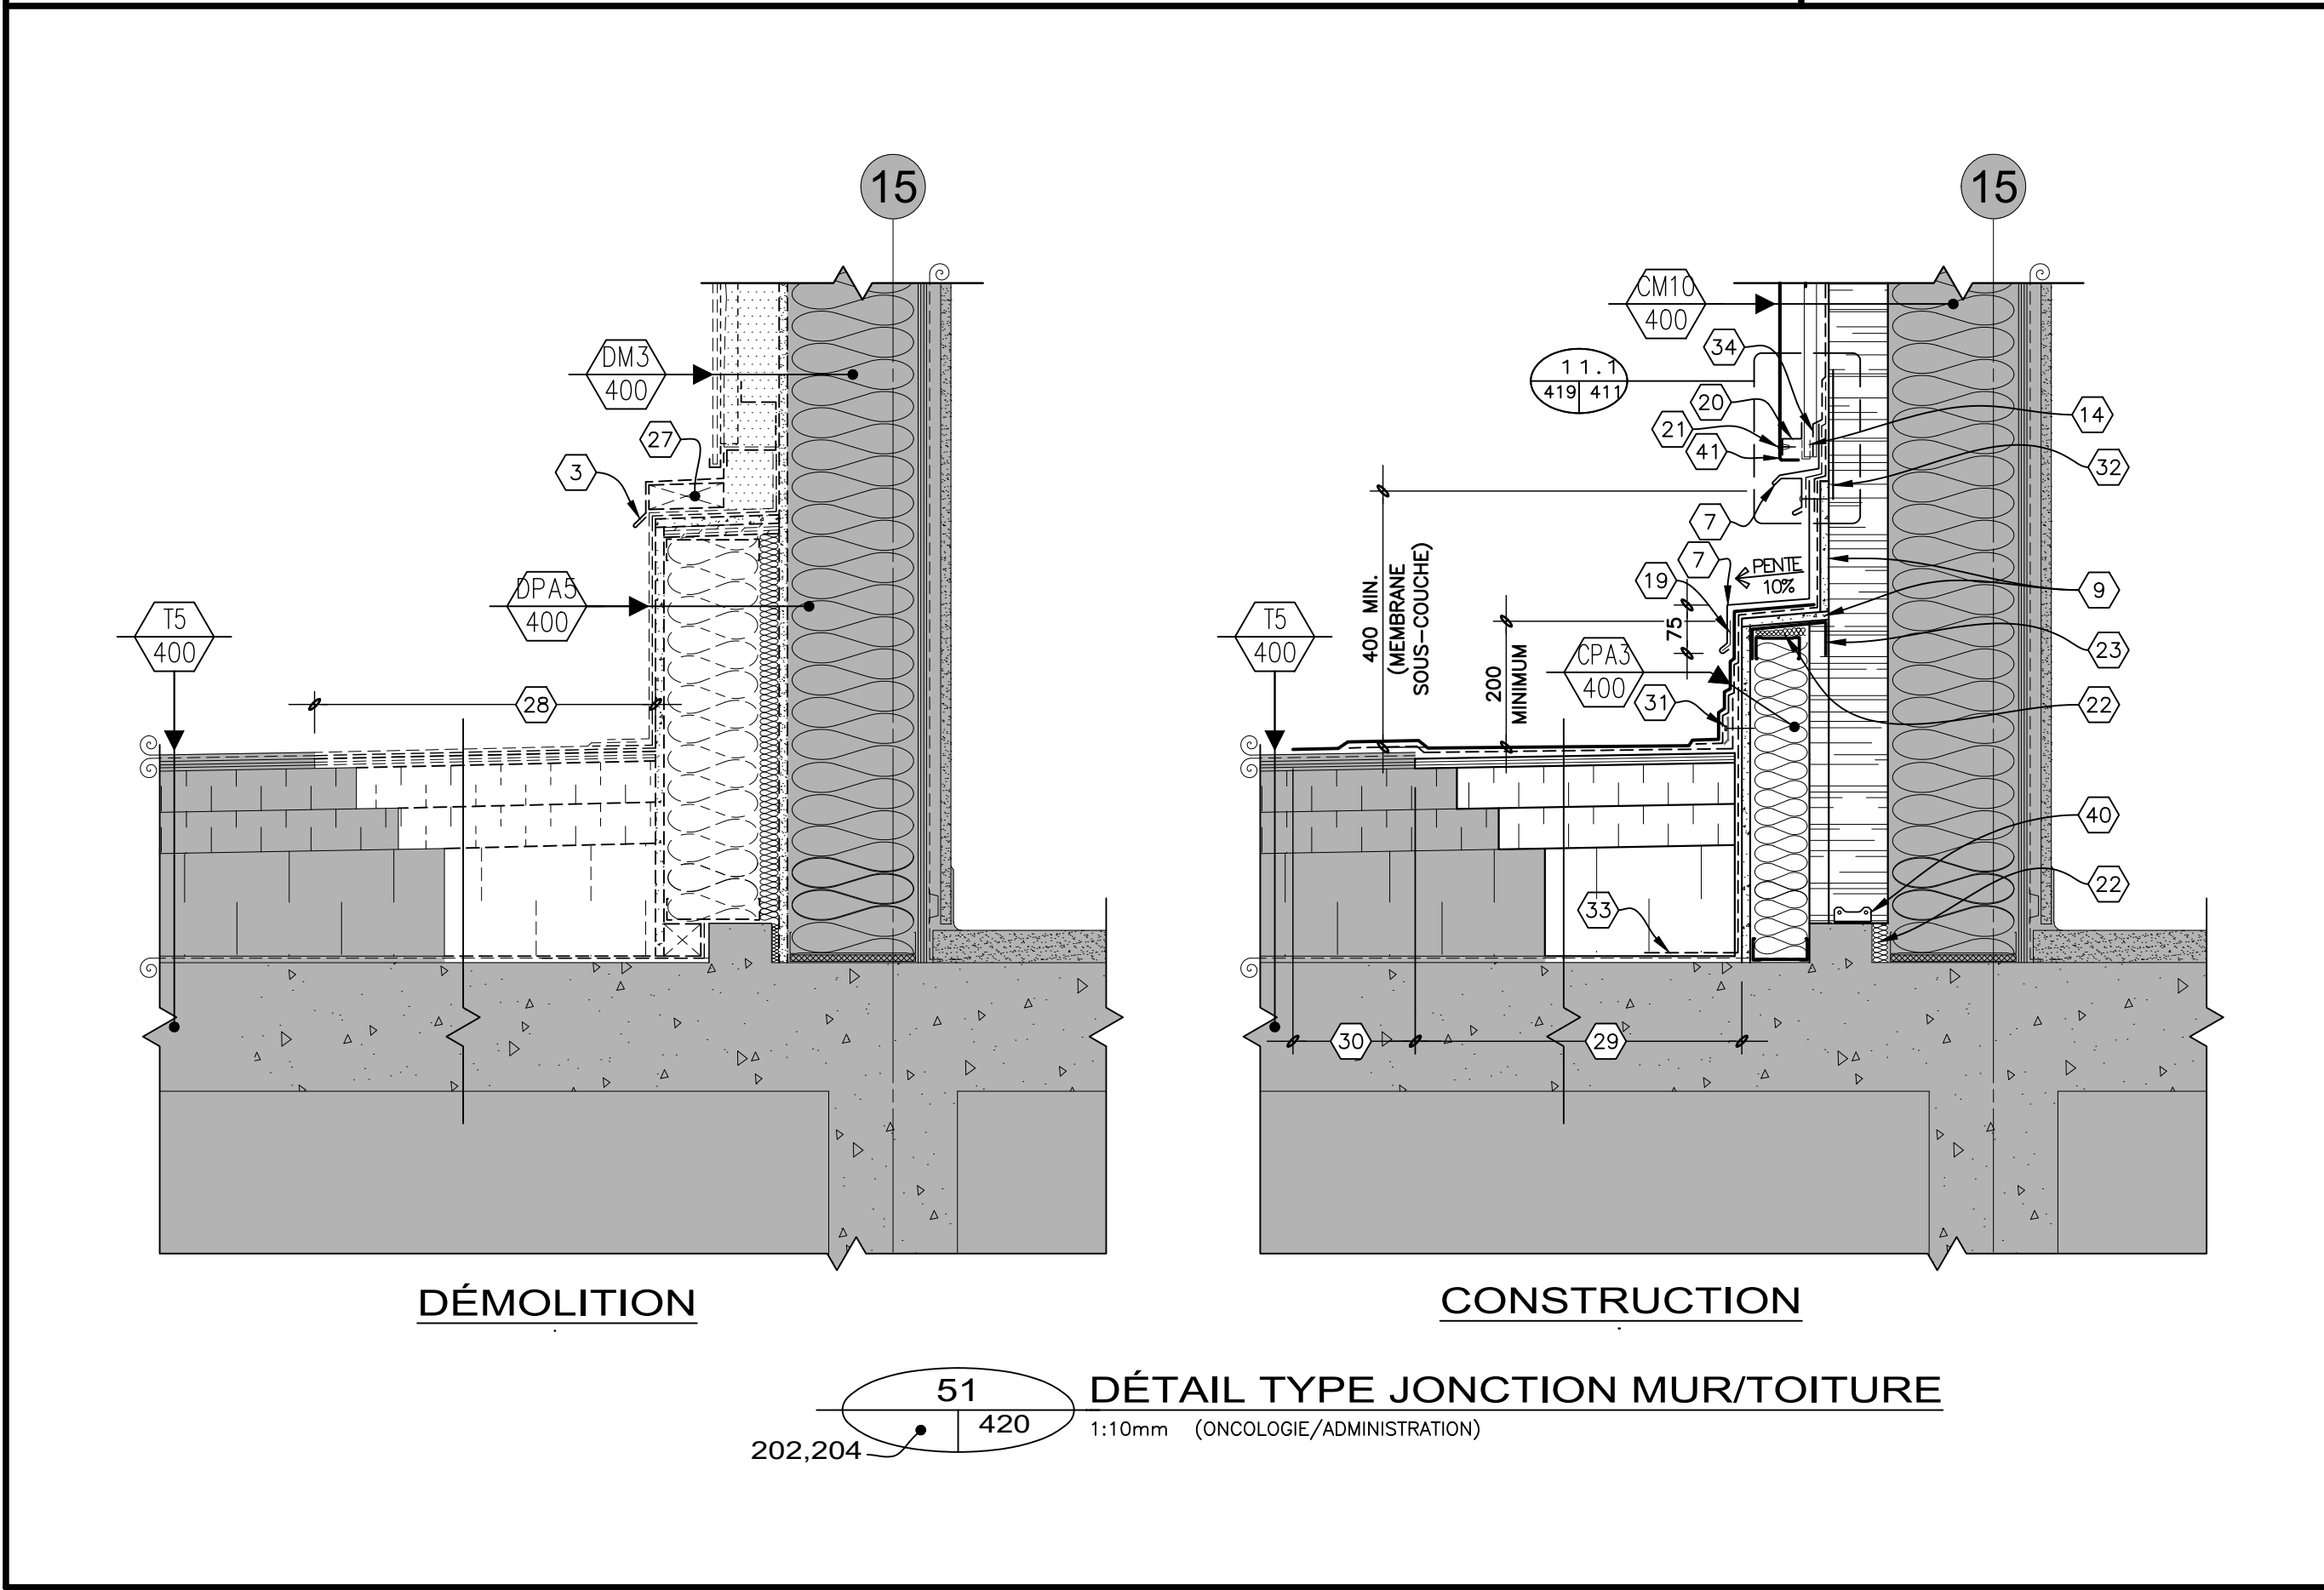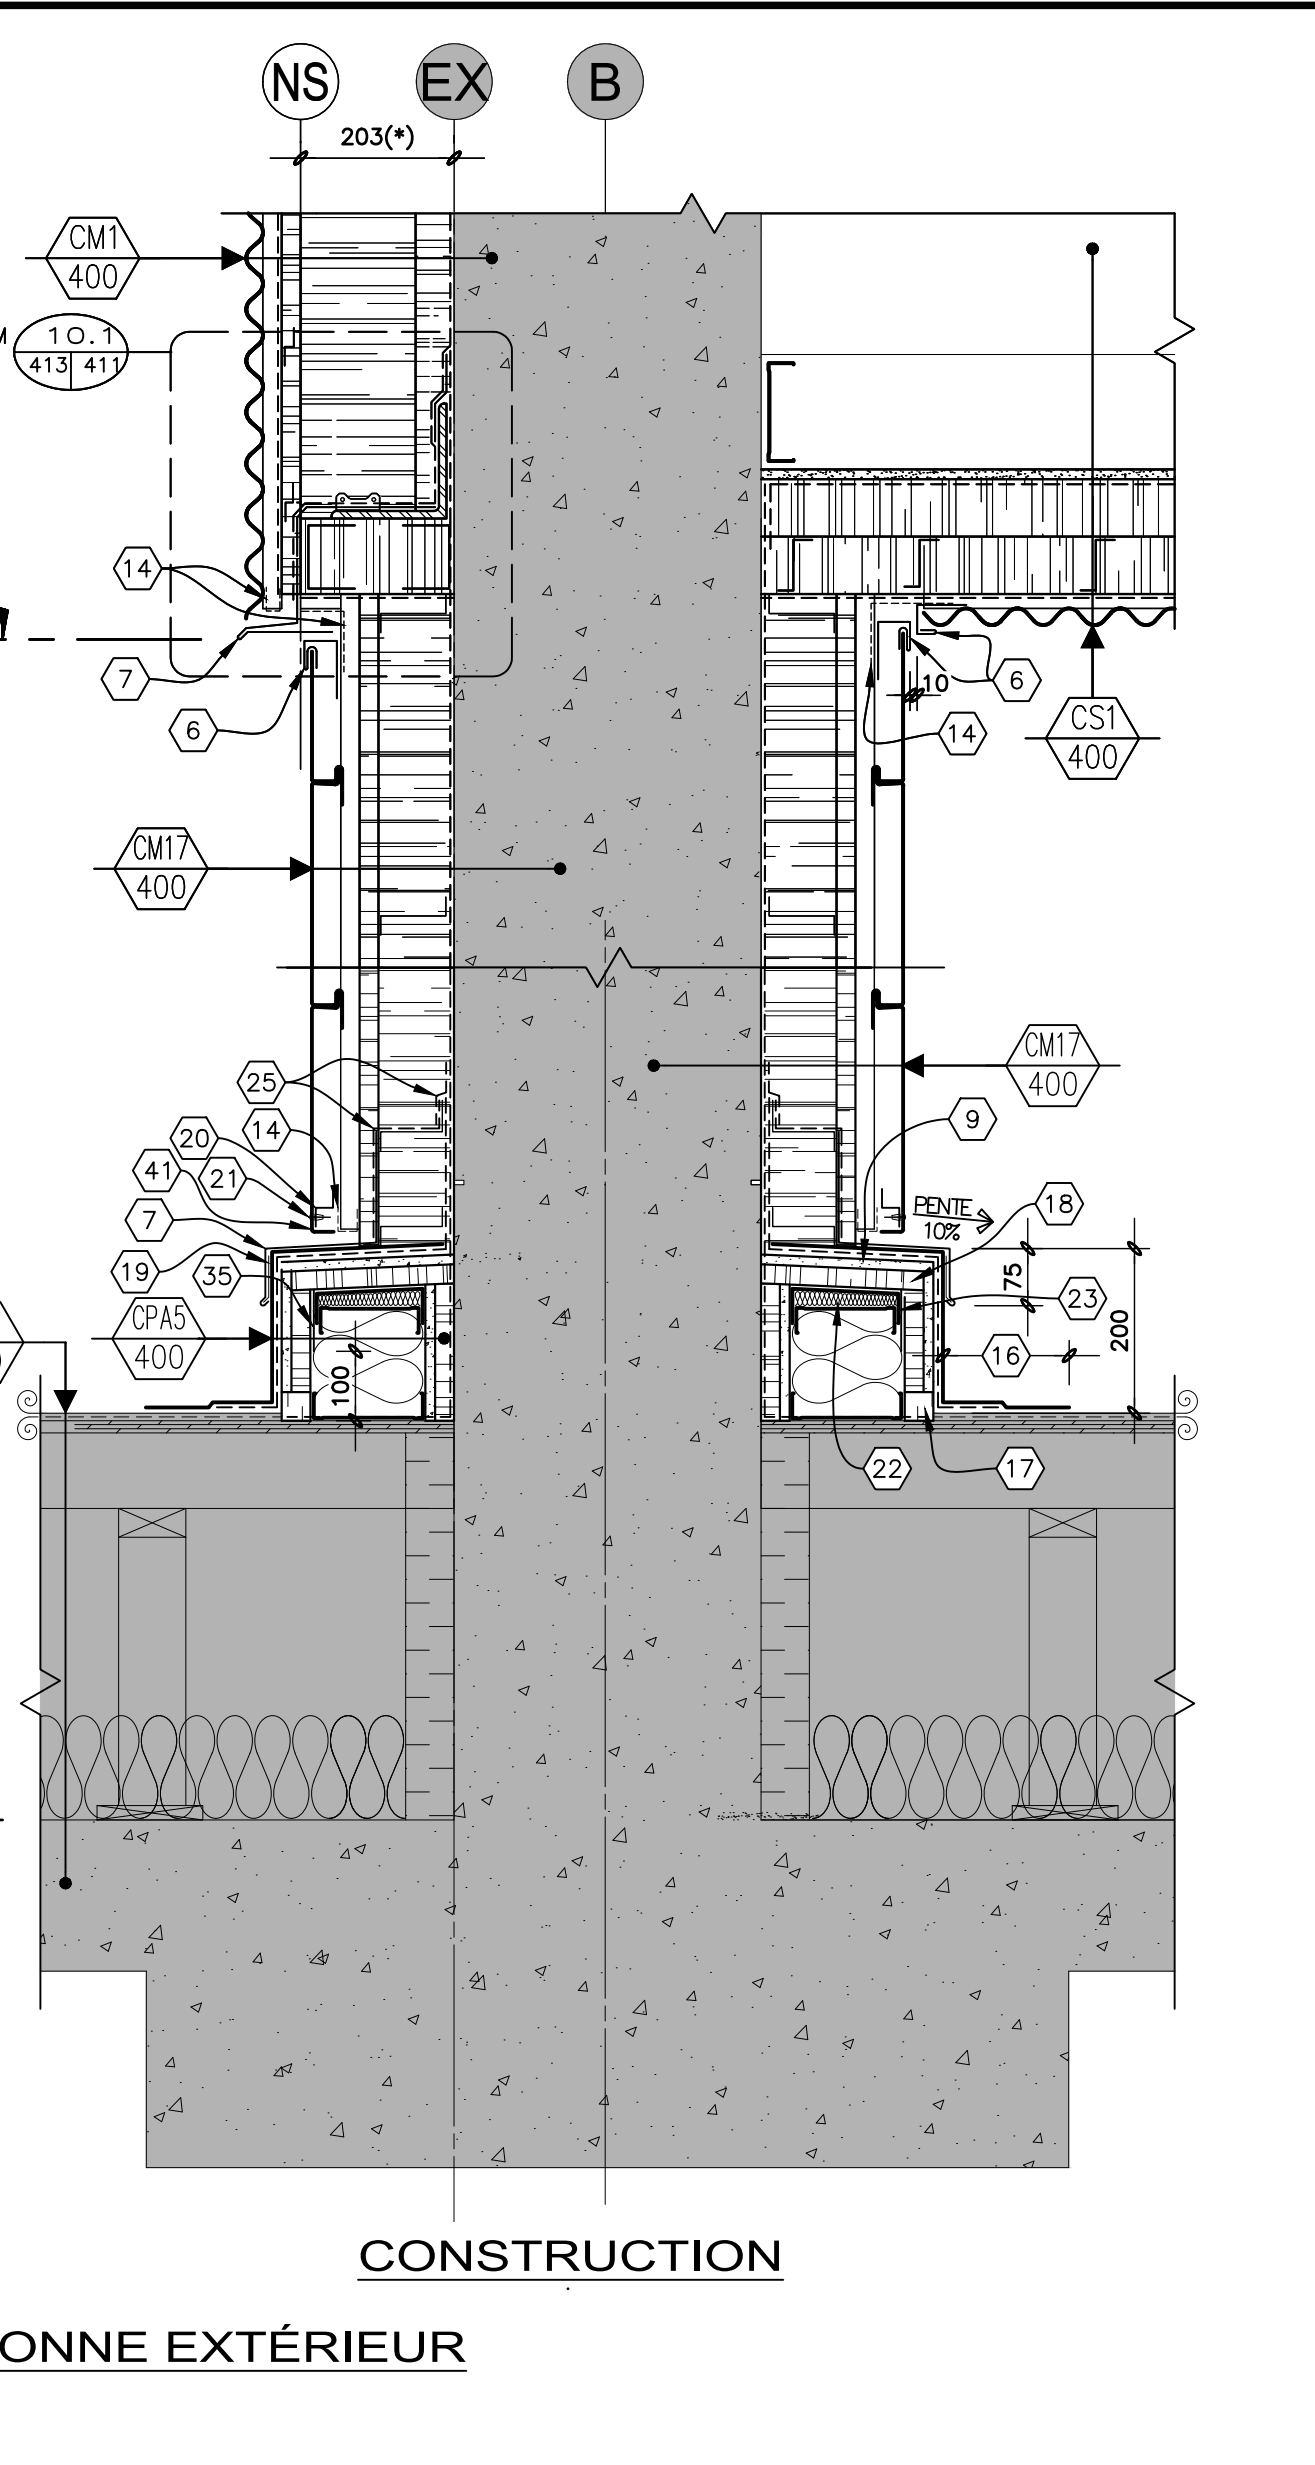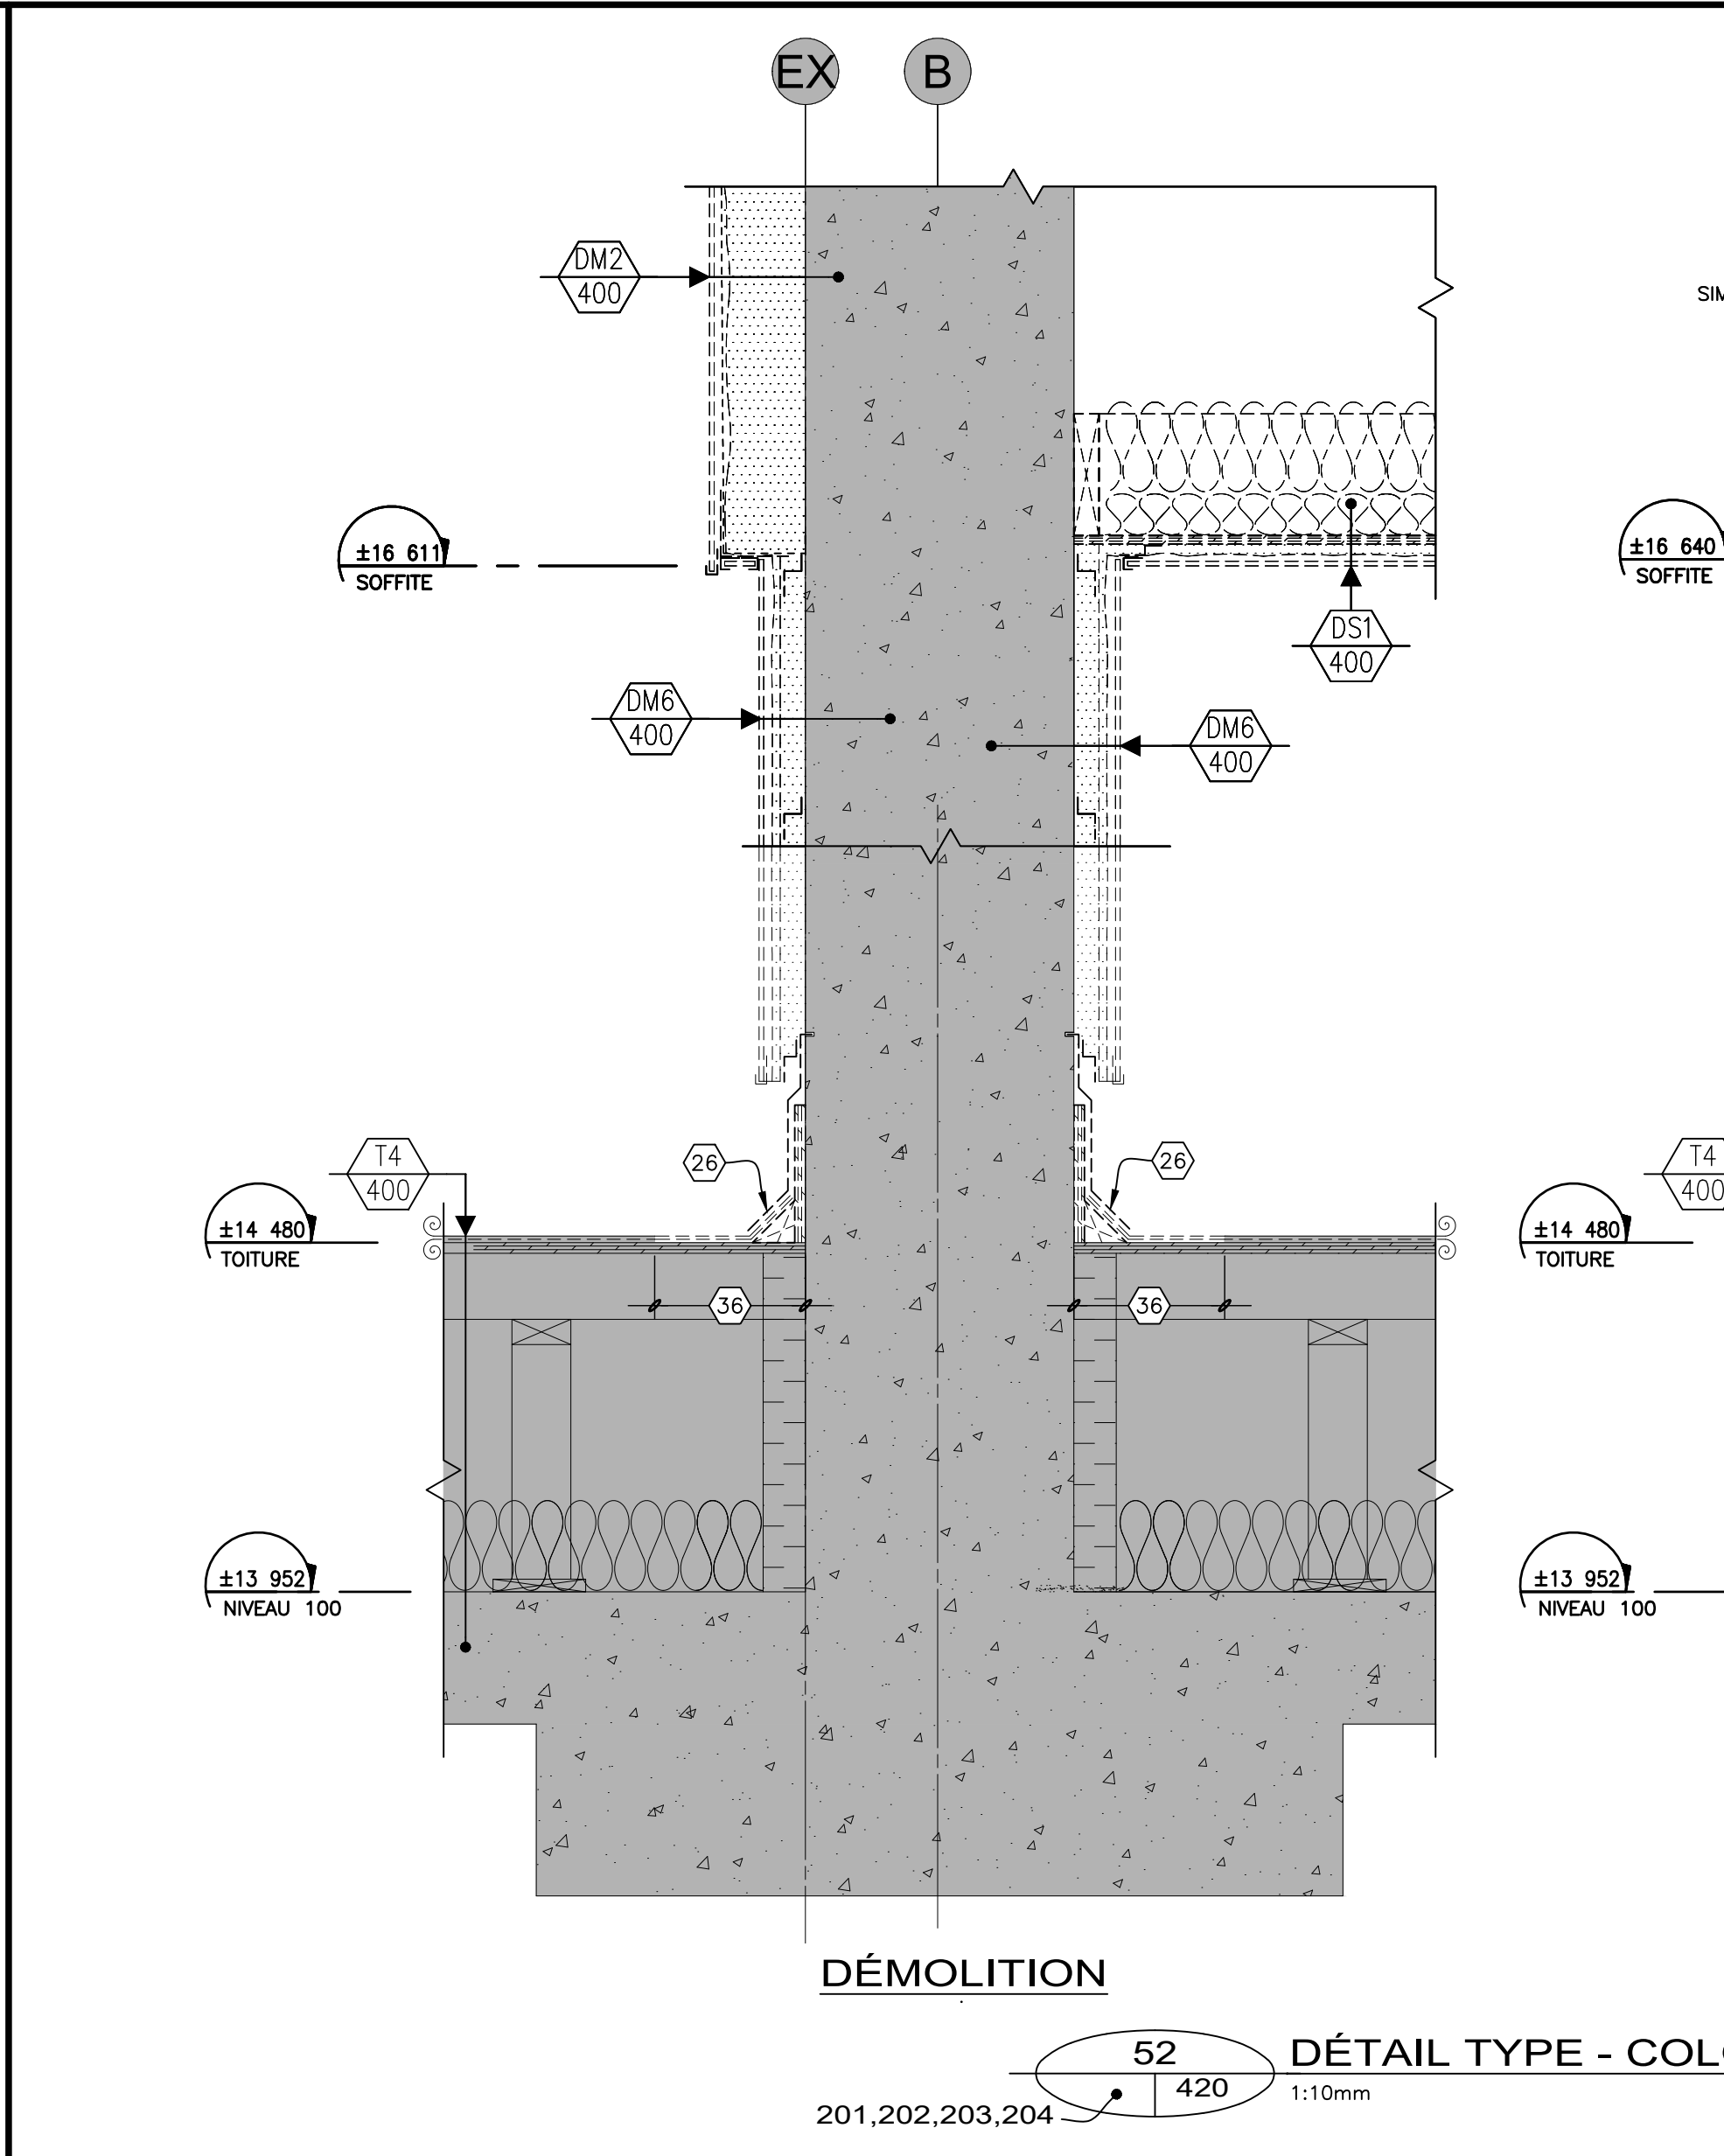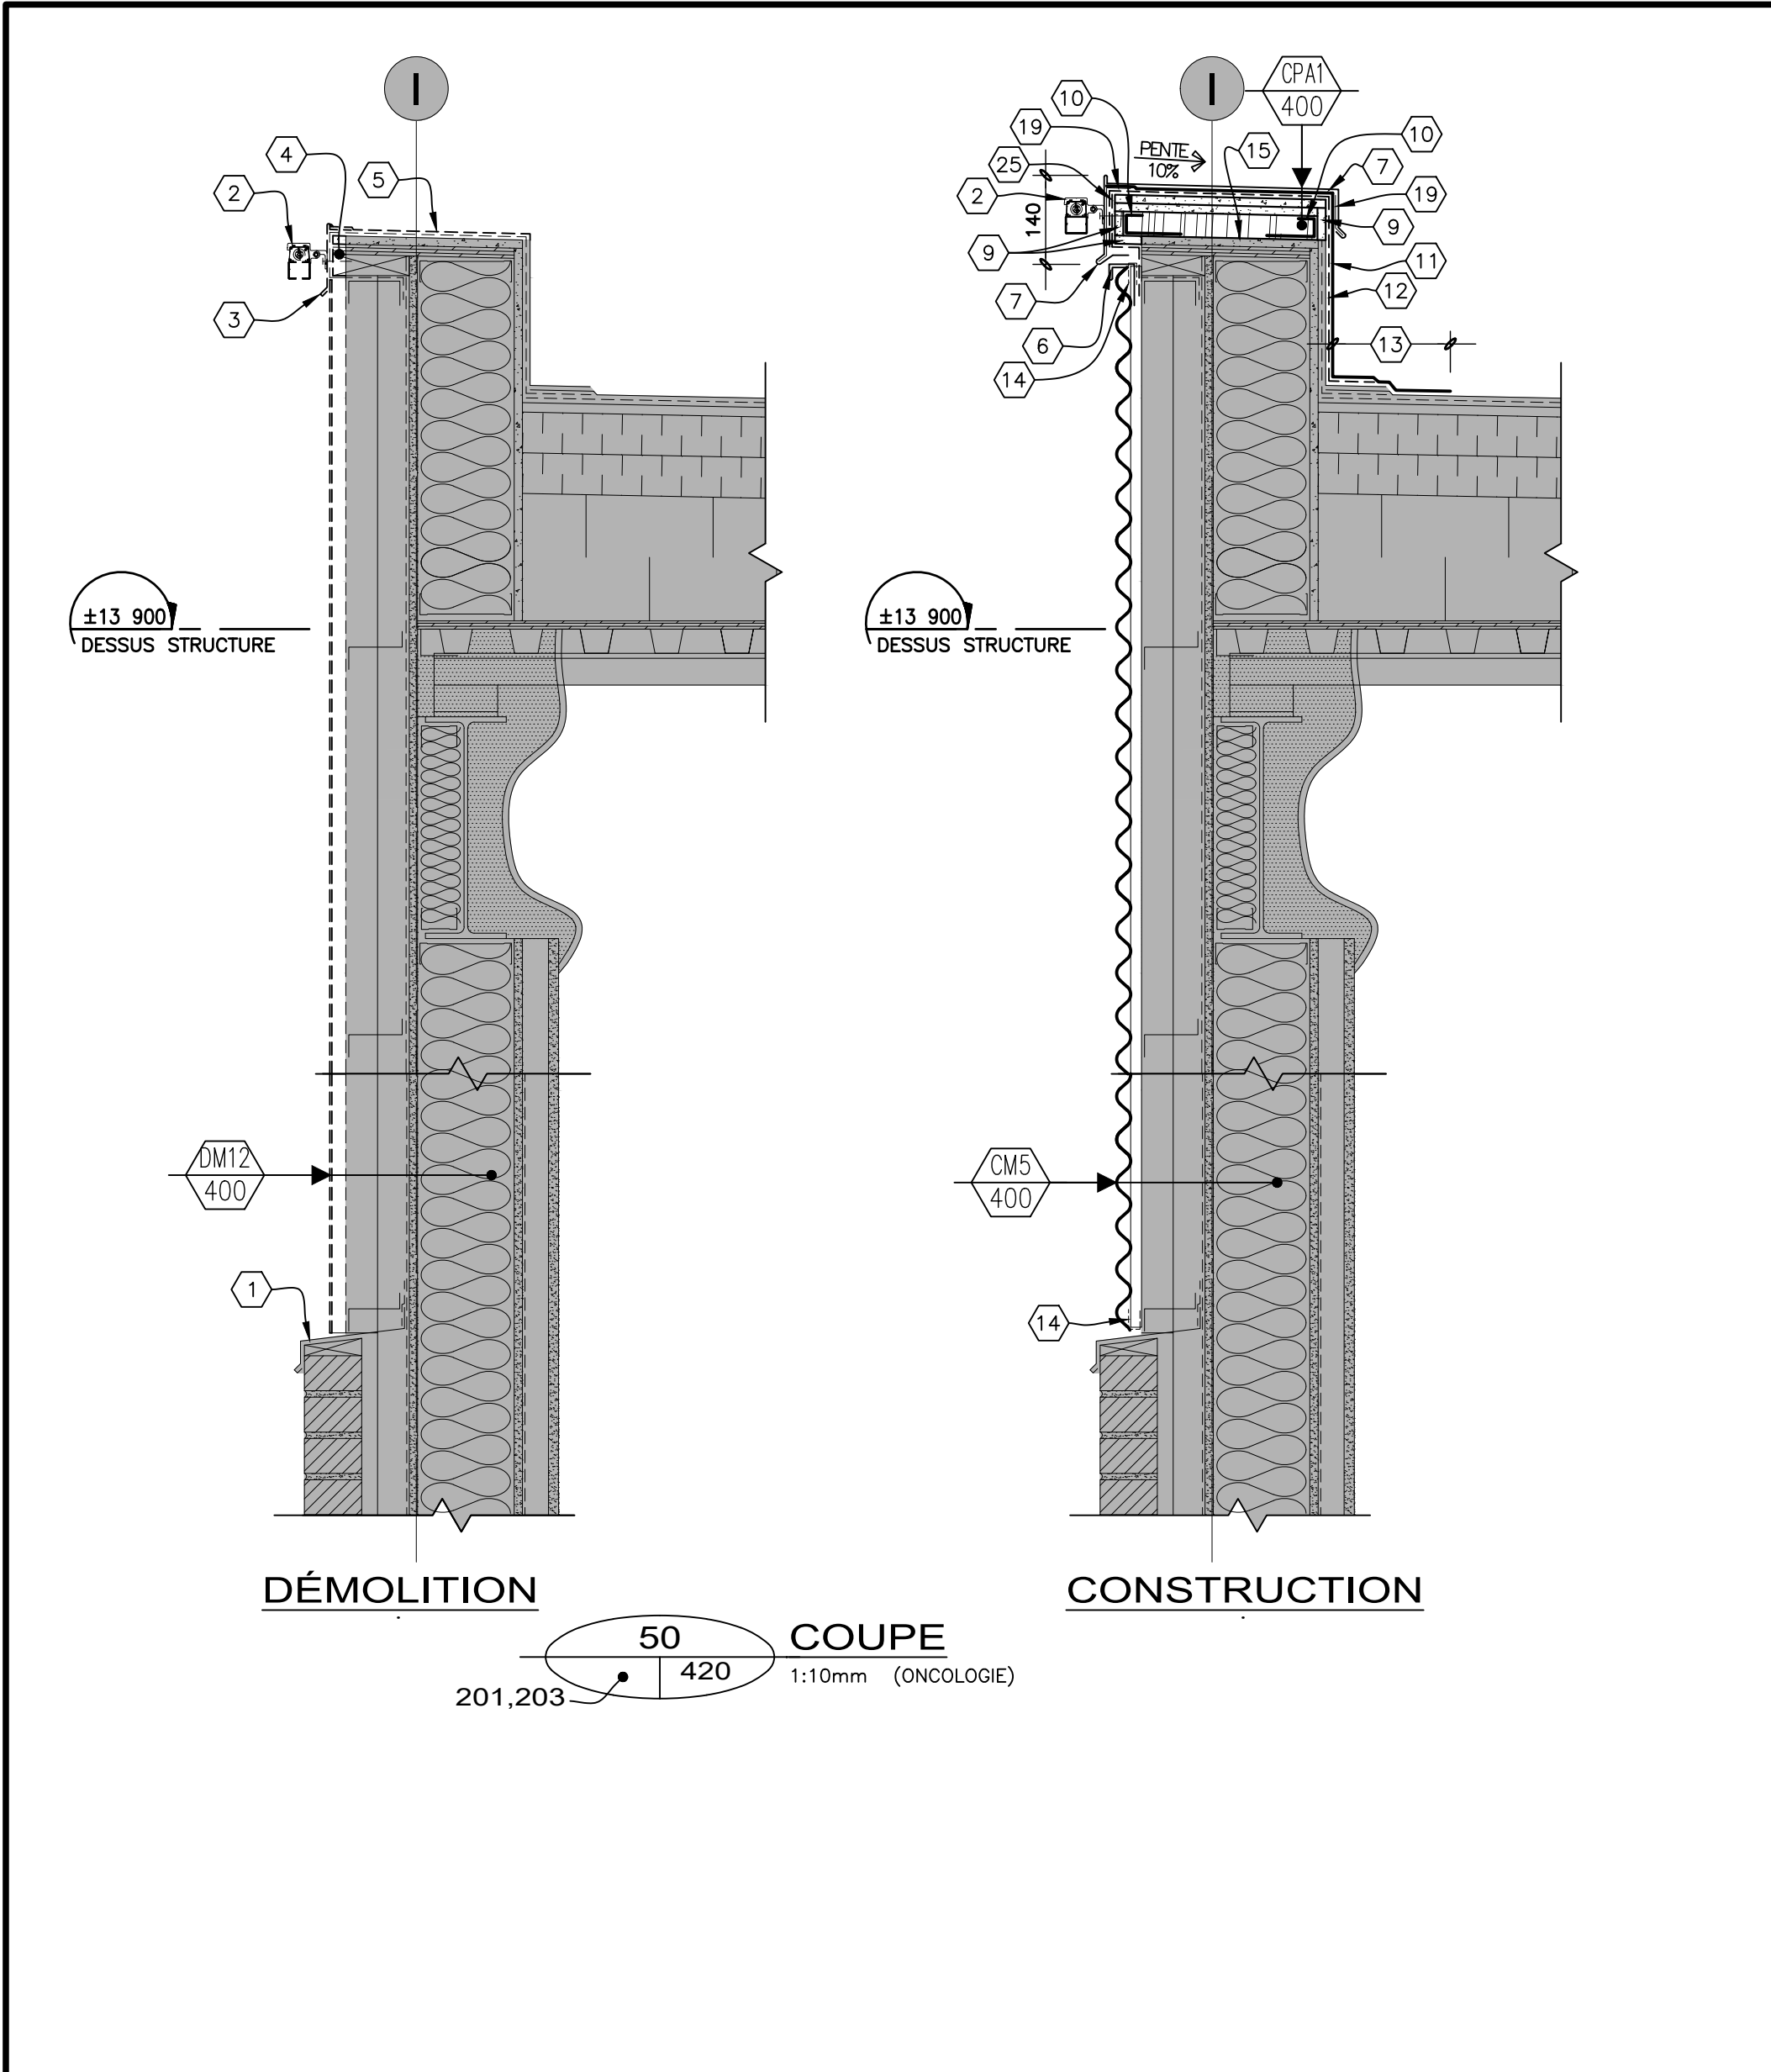

### NOTES

- SOLIN EXISTANT À CONSERVER.
- APPAREIL D'ÉCLAIRAGE CONTINUE SUR LA FAÇADE SUD DU BASILICAIRE SECTEUR ONCOLOGIE À ENLEVER ET À RÉINSTALLER, VOIR INGÉNIEUR.
- SOLIN EXISTANT À ENLEVER.
- PIÈCE DE BOIS, CONTREPLAQUÉ ET PANNEAU DE BÉTON À COUPER SUR LARGEUR REQUISE.
- DÉMOLIR LES MEMBRANES EXISTANTES SUR LE DESSUS DU PARAPET.
- MOULURE EN "J" EN ACIER ÉMAILLÉ CAL.24.
- SOLIN EN ACIER ÉMAILLÉ, CAL.24, JOINTS AGRAFÉS.
- PANNEAU DE MÂT DE FIBRE DE VERRE 13mm.
- PANNEAU DE CIMENT 13mm.
- PLIAGE DE TÔLE EN "J" CAL.18 EN ACIER GALVANISÉ.
- MEMBRANE DE FINITION.
- MEMBRANE SOUS-COUCHE.
- CHEVAUCHER LA NOUVELLE MEMBRANE SUR LES MEMBRANES DE LA TOITURE EXISTANTE SUR MINIMUM 150mm. DÉGRANULER LA MEMBRANE EXISTANTE AU PRÉALABLE.
- MOUSTIQUEAIRE.
- CALE D'AJUSTEMENT EN ACIER GALVANISÉ D'ÉPAISSEUR REQUISE.
- CHEVAUCHER LA NOUVELLE MEMBRANE SUR LES MEMBRANES DE LA TOITURE EXISTANTE SUR MINIMUM 150mm. DÉGRANULER LA MEMBRANE EXISTANTE AU PRÉALABLE.
- ISOLANT SEMI-RIGIDE DE FIBRE DE ROCHÉ DE 38mm D'ÉPAISSEUR.
- ISOLANT RIGIDE DE FIBRE DE ROCHÉ 25mm.
- AGRAFE EN ACIER GALVANISÉ, CAL.24 CONTINUE.
- PLIAGE DE TÔLE EN ACIER GALVANISÉ, CAL.22.
- RIVET EN ACIER INOXYDABLE.
- REMPLOIR L'ESPACE DE LAINE DE FIBRE DE VERRE.
- PLIAGE DE TÔLE EN "U", CAL.16 EN ACIER GALVANISÉ.
- COLOMBAGE MÉTALLIQUE 92mm Ø400mm c/c.
- MEMBRANE AUTOCOLLANTE.
- DÉMOLIR LE CONTREPLAQUÉ, PIÈCE BISEAUTÉ EN BOIS ET LES MEMBRANES SUR LARGEUR REQUISE POUR LA CONSTRUCTION DU NOUVEAU PARAPET.
- PIÈCES DE BOIS À DÉMOLIR.
- OUVERTURE À FAIRE DANS LA TOITURE EXISTANTE SUR ±800mm POUR LA CONSTRUCTION DU NOUVEAU PARAPET. VOIR COMPOSITION DE TOIT SUR LE DÉTAIL.
- RAGRÉER LA TOITURE TEL QUE L'EXISTANT. VOIR COMPOSITION DE TOIT SUR LE DÉTAIL.
- CHEVAUCHER LA NOUVELLE MEMBRANE SUR LES MEMBRANES DE LA TOITURE EXISTANTE SUR MINIMUM 300mm. DÉGRANULER LA MEMBRANE EXISTANTE AU PRÉALABLE.
- BARRE D'ANCRAGE DE LA MEMBRANE.
- TÔLE D'APPUI EN ACIER GALVANISÉ CAL.18 SUR 200mm DE HAUTEUR.
- MEMBRANE PARE-VAPEUR AUTOCOLLANTE.
- SCELLER LA MEMBRANE PARE-INTÉMPIÉRIES SUR LE SOLIN AVEC UN RUBAN AUTOCOLLANT.
- TÔLE D'APPUI EN ACIER GALVANISÉ CAL.18.
- MEMBRANES EXISTANTE À DÉMOLIR SUR LARGEUR REQUISE POUR L'INSTALLATION DU NOUVEAU PARAPET.
- BARRE "Z" VERTICALE CAL.16 Ø400mm c/c.
- POUTRE D'ACIER, VOIR STRUCTURE.
- PLAQUE D'ACIER PONCTUELLE, VOIR STRUCTURE.
- CONNECTEUR À CHAQUE COLOMBAGES OU BARRE "Z" SELON LE CAS, VOIR STRUCTURE.
- BOUT DU PANNEAU REPLIÉ VERS L'INTÉRIEUR.

### LÉGENDE

- EXISTANT À CONSERVER.
- ÉLÉMENT À DÉMOLIR.
- AXE EXISTANT
- EX EXTÉRIEUR DE LA STRUCTURE DE BÉTON EXISTANTE DE LA TOUR.
- NS NOUVEL AXE: FACE EXTÉRIEURE DES BARRES Z ET COLOMBAGES DE LA TOUR. VOIR STRUCTURE.
- (\*) VOIR NOTE GÉNÉRAL PAGE 400.

### NE DOIT PAS SERVIR À L'EXÉCUTION

Le présent document est émis pour la seule fin identifiée. Son contenu est protégé par les droits d'auteur et toute reproduction ou modification, partielle ou totale, est interdite sans l'autorisation écrite de gagnon, letellier, cyr, ricard, mathieu, proulx, savard consortium d'architectes.

GLCRM | Proulx Savard |

GLCRM:  
128, Avenue de la Cathédrale,  
Bureau 201  
Rimouski, QC, G5L 5H7  
(418) 722-7655

2406, Ch. des Quatres-Bourgeois,  
Bureau 100  
Québec, QC, G1V 1W5  
(418) 647-1700








Proulx Savard Architectes:  
75, boul. Arthur-Buies Ouest,  
Rimouski QC G5L 5C2  
(418) 722-5543

ARCHITECTURE

CONSULTANTS

|         |                            |        |                                                                |              |              |
|---------|----------------------------|--------|----------------------------------------------------------------|--------------|--------------|
| DESSIN  | COUPE ET DÉTAIL TYPE       | PROJET | HÔPITAL DE CHANDLER,<br>Chandler<br>(Refaction de l'enveloppe) | PROPRIÉTAIRE | Santé Québec |
| DB AL   | DÉMOLITION ET CONSTRUCTION | 05     | 2024-09-04                                                     | 05           | 2024-09-04   |
| ÉCHELLE | INDIQUÉE                   | 04     | 2024-08-21                                                     | 04           | 2024-08-21   |
|         |                            | 03     | 2024-08-03                                                     | 03           | 2024-08-03   |
|         |                            | 02     | 2024-05-14                                                     | 02           | 2024-05-14   |
|         |                            | 01     | 2024-02-27                                                     | 01           | 2024-02-27   |

420

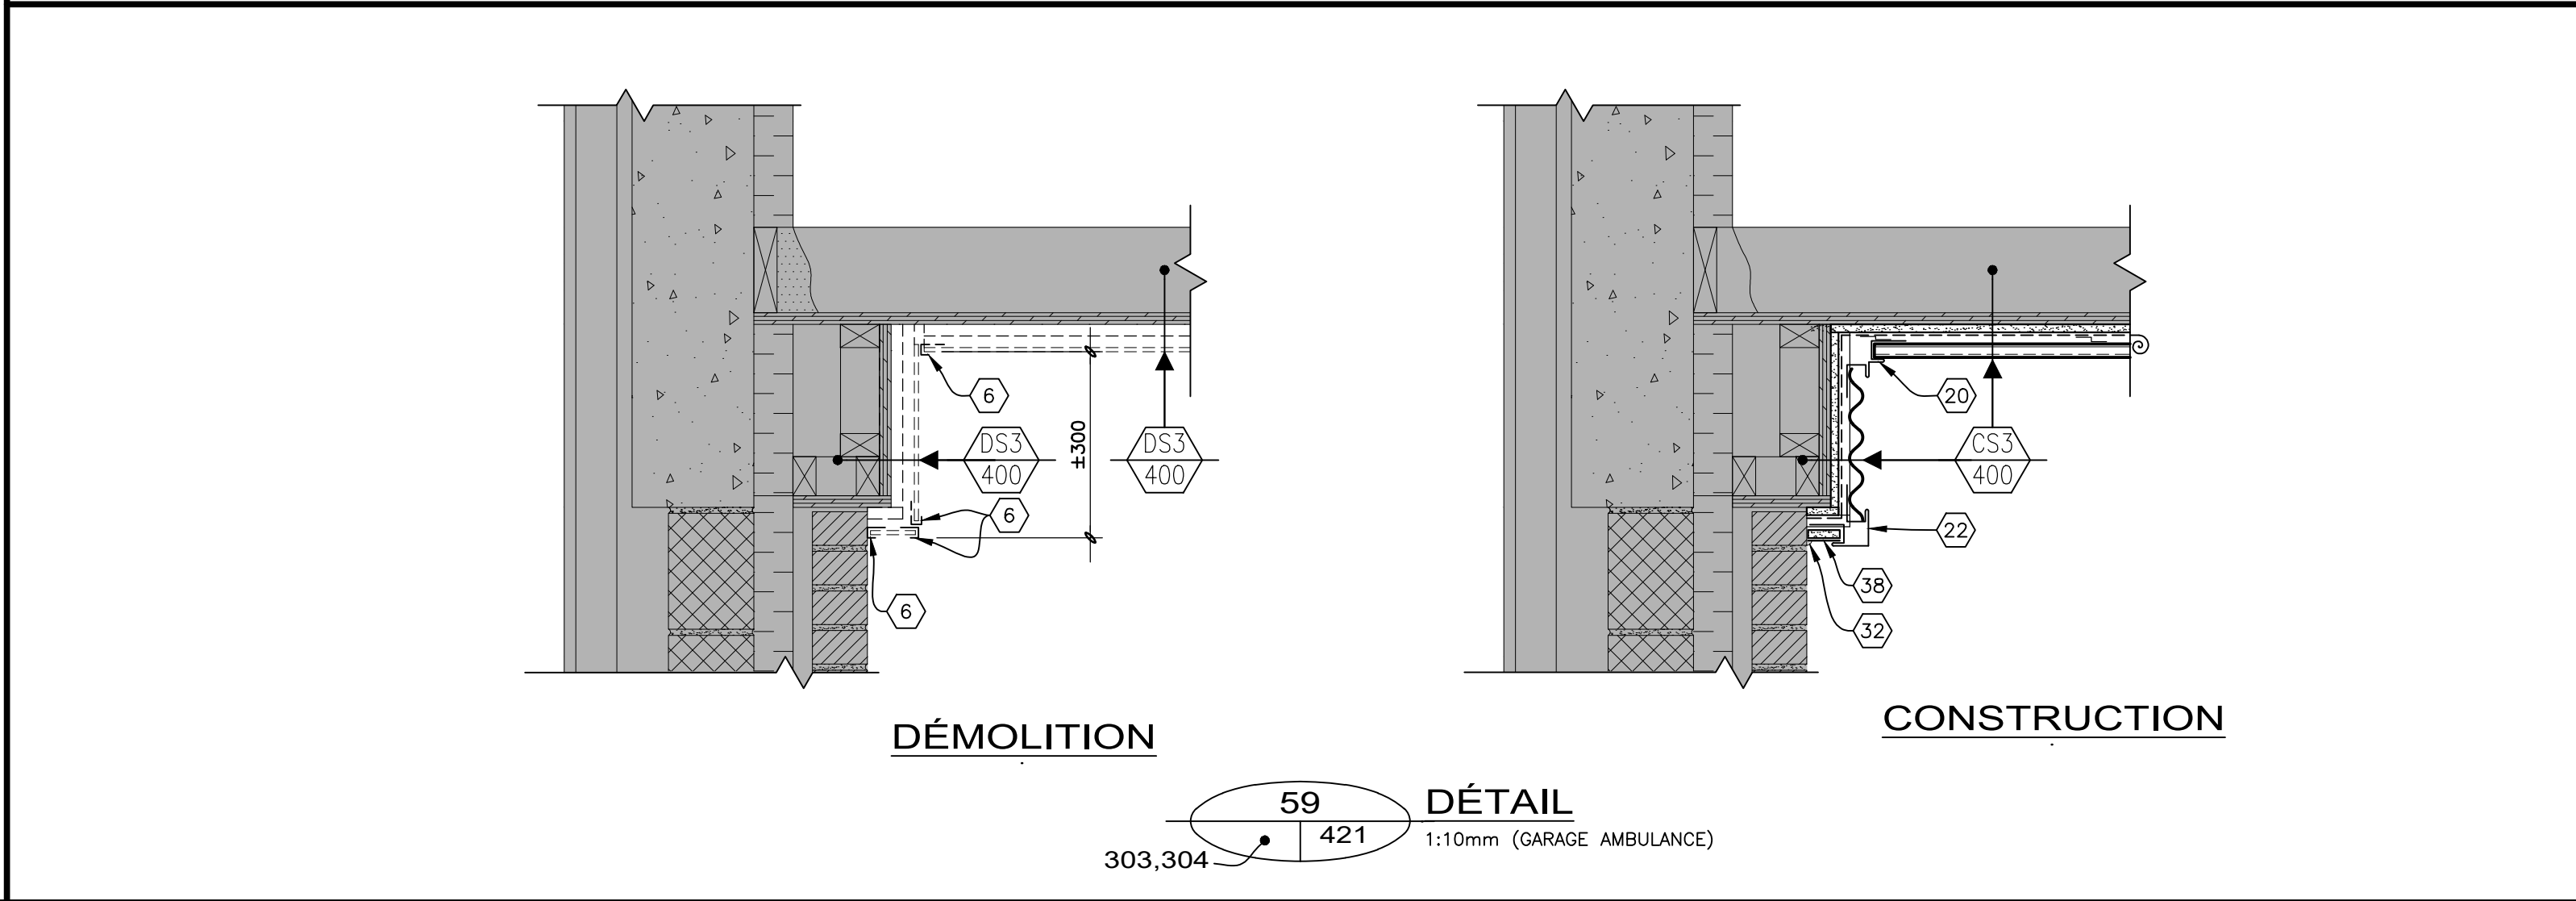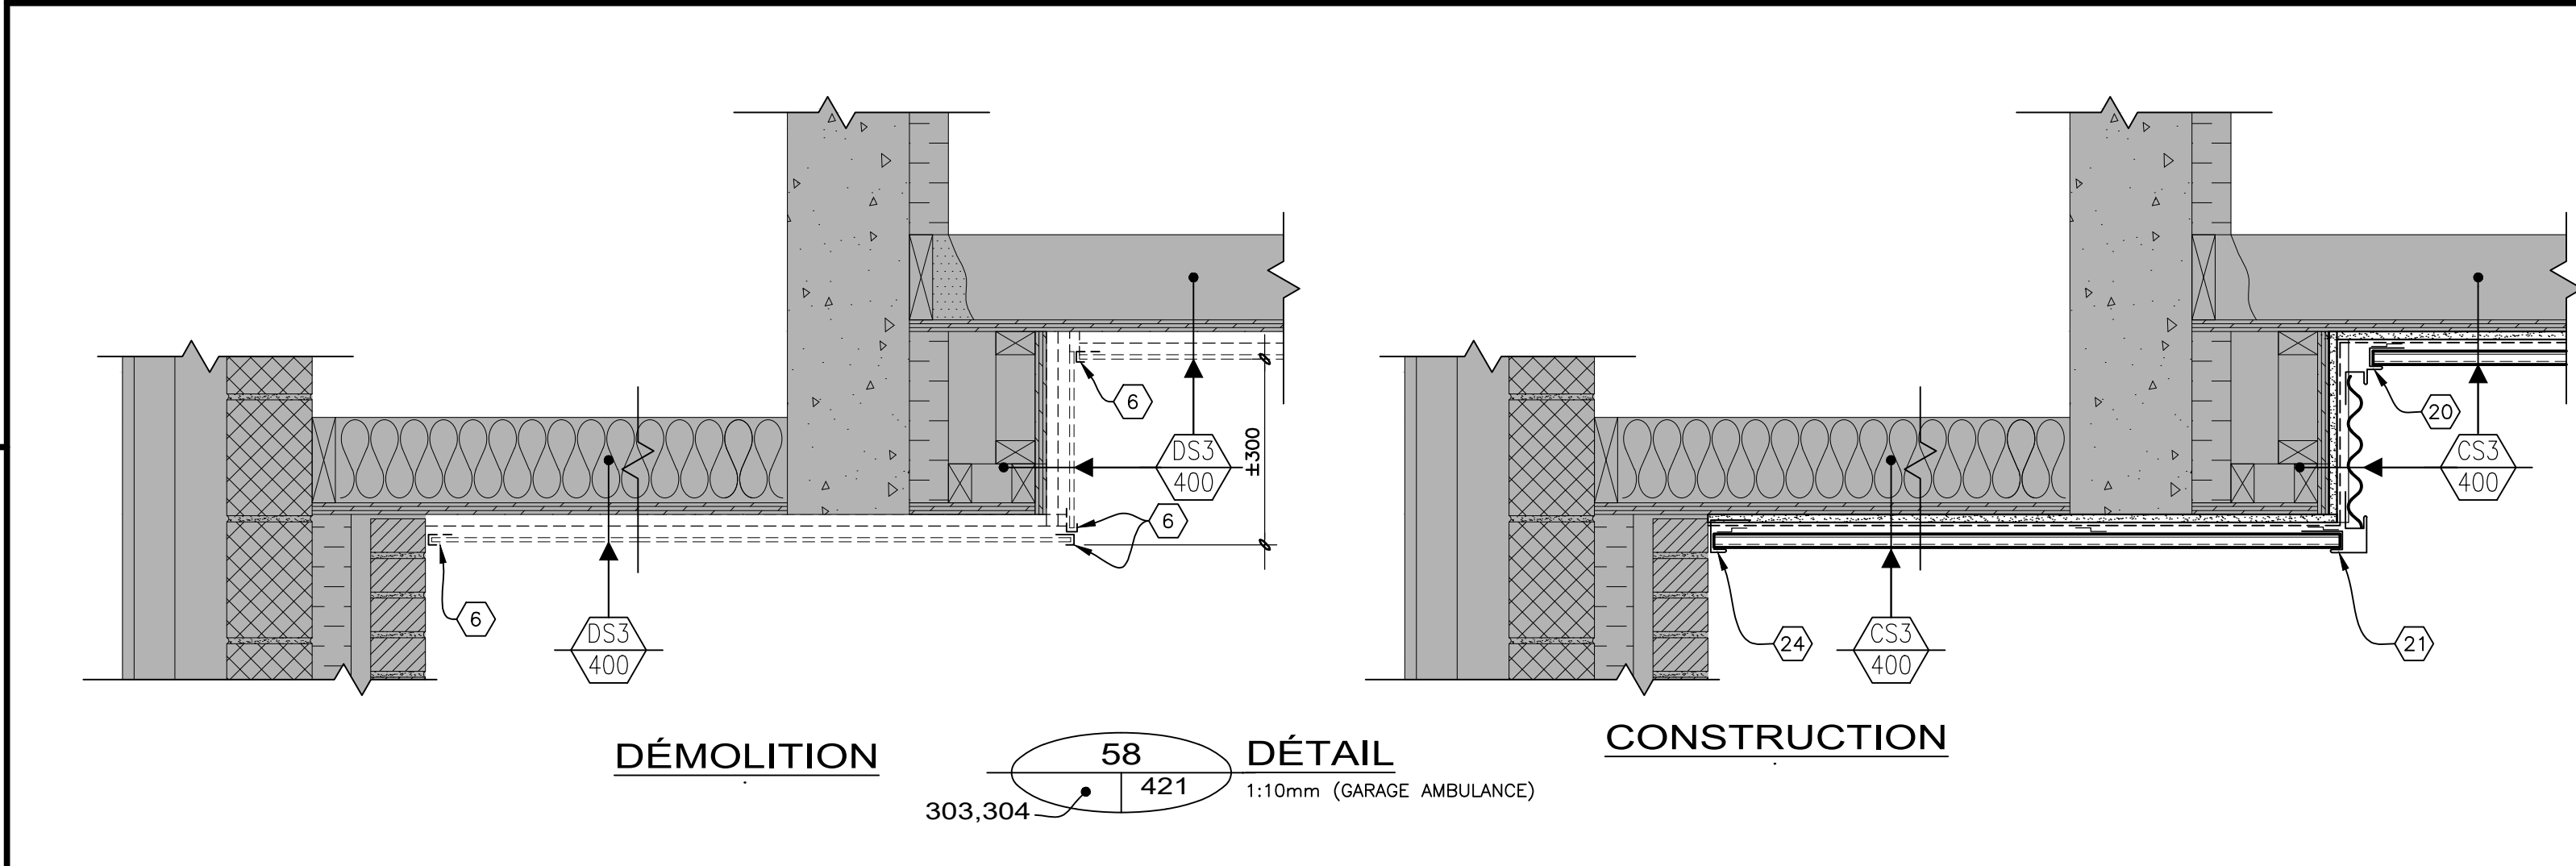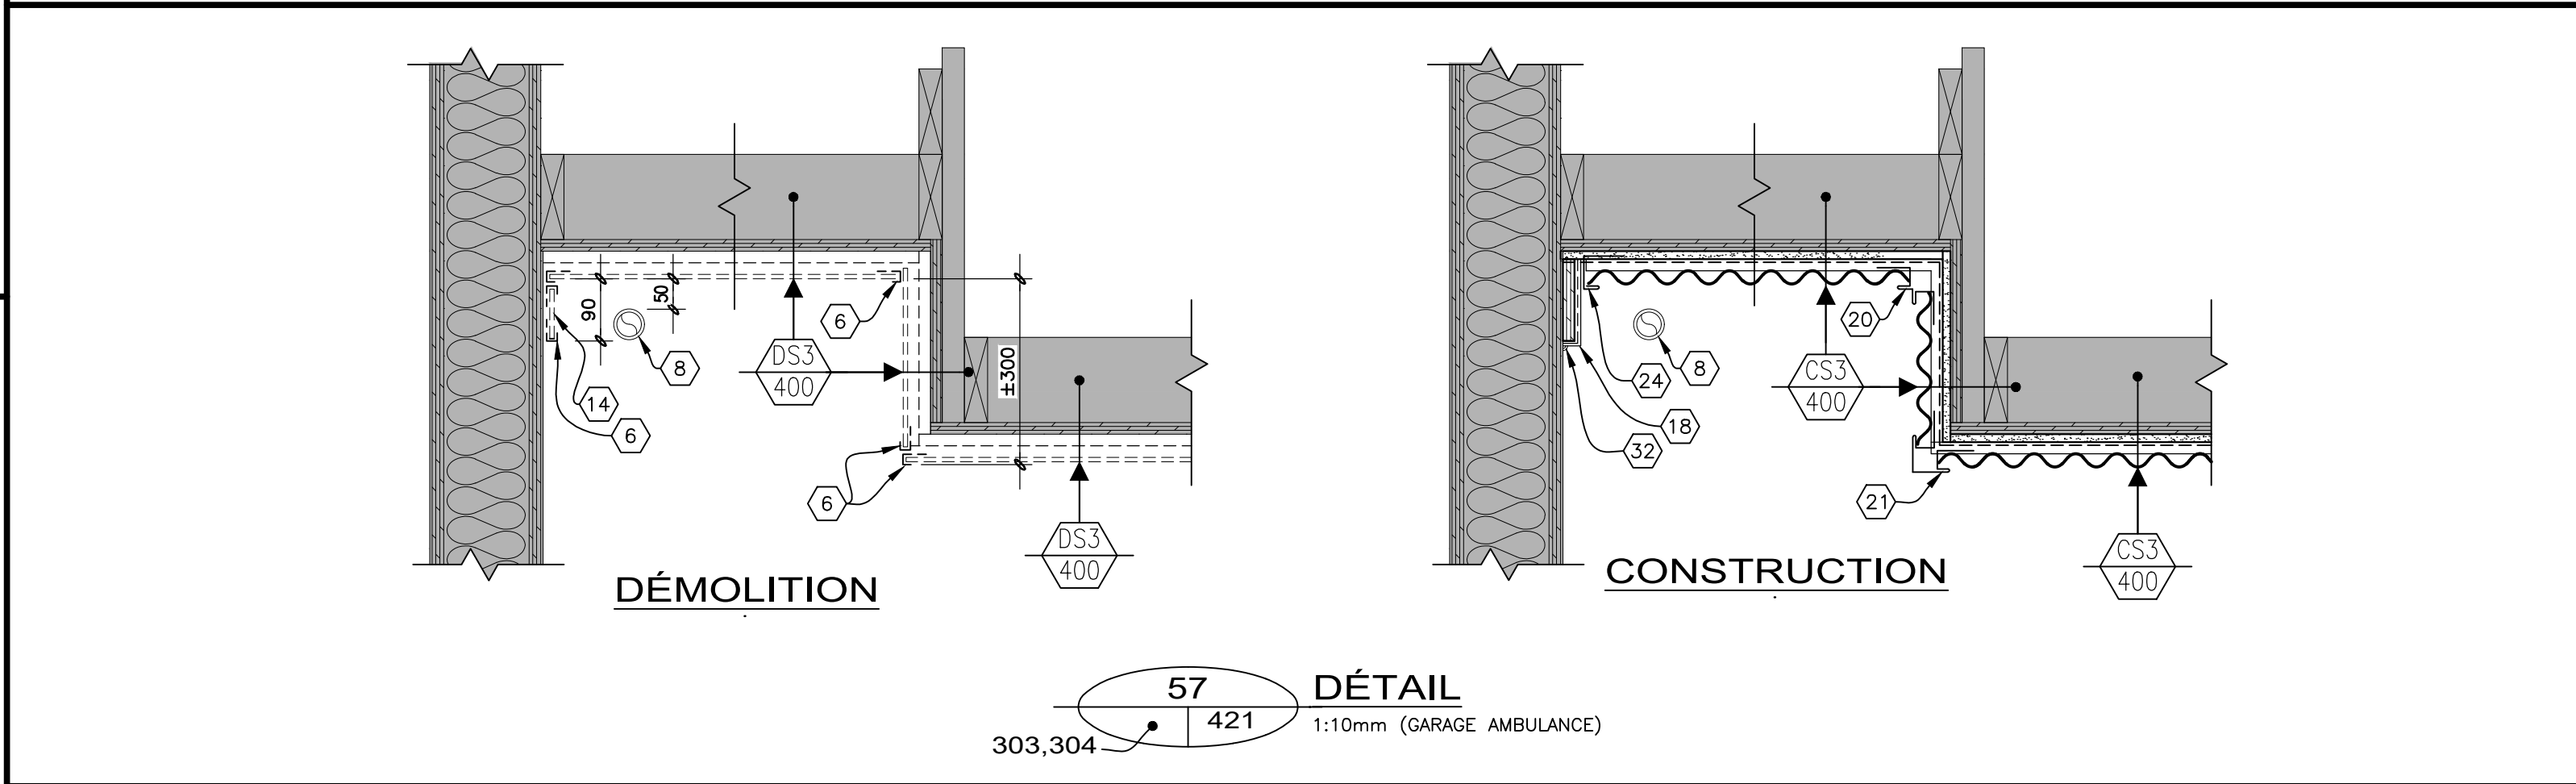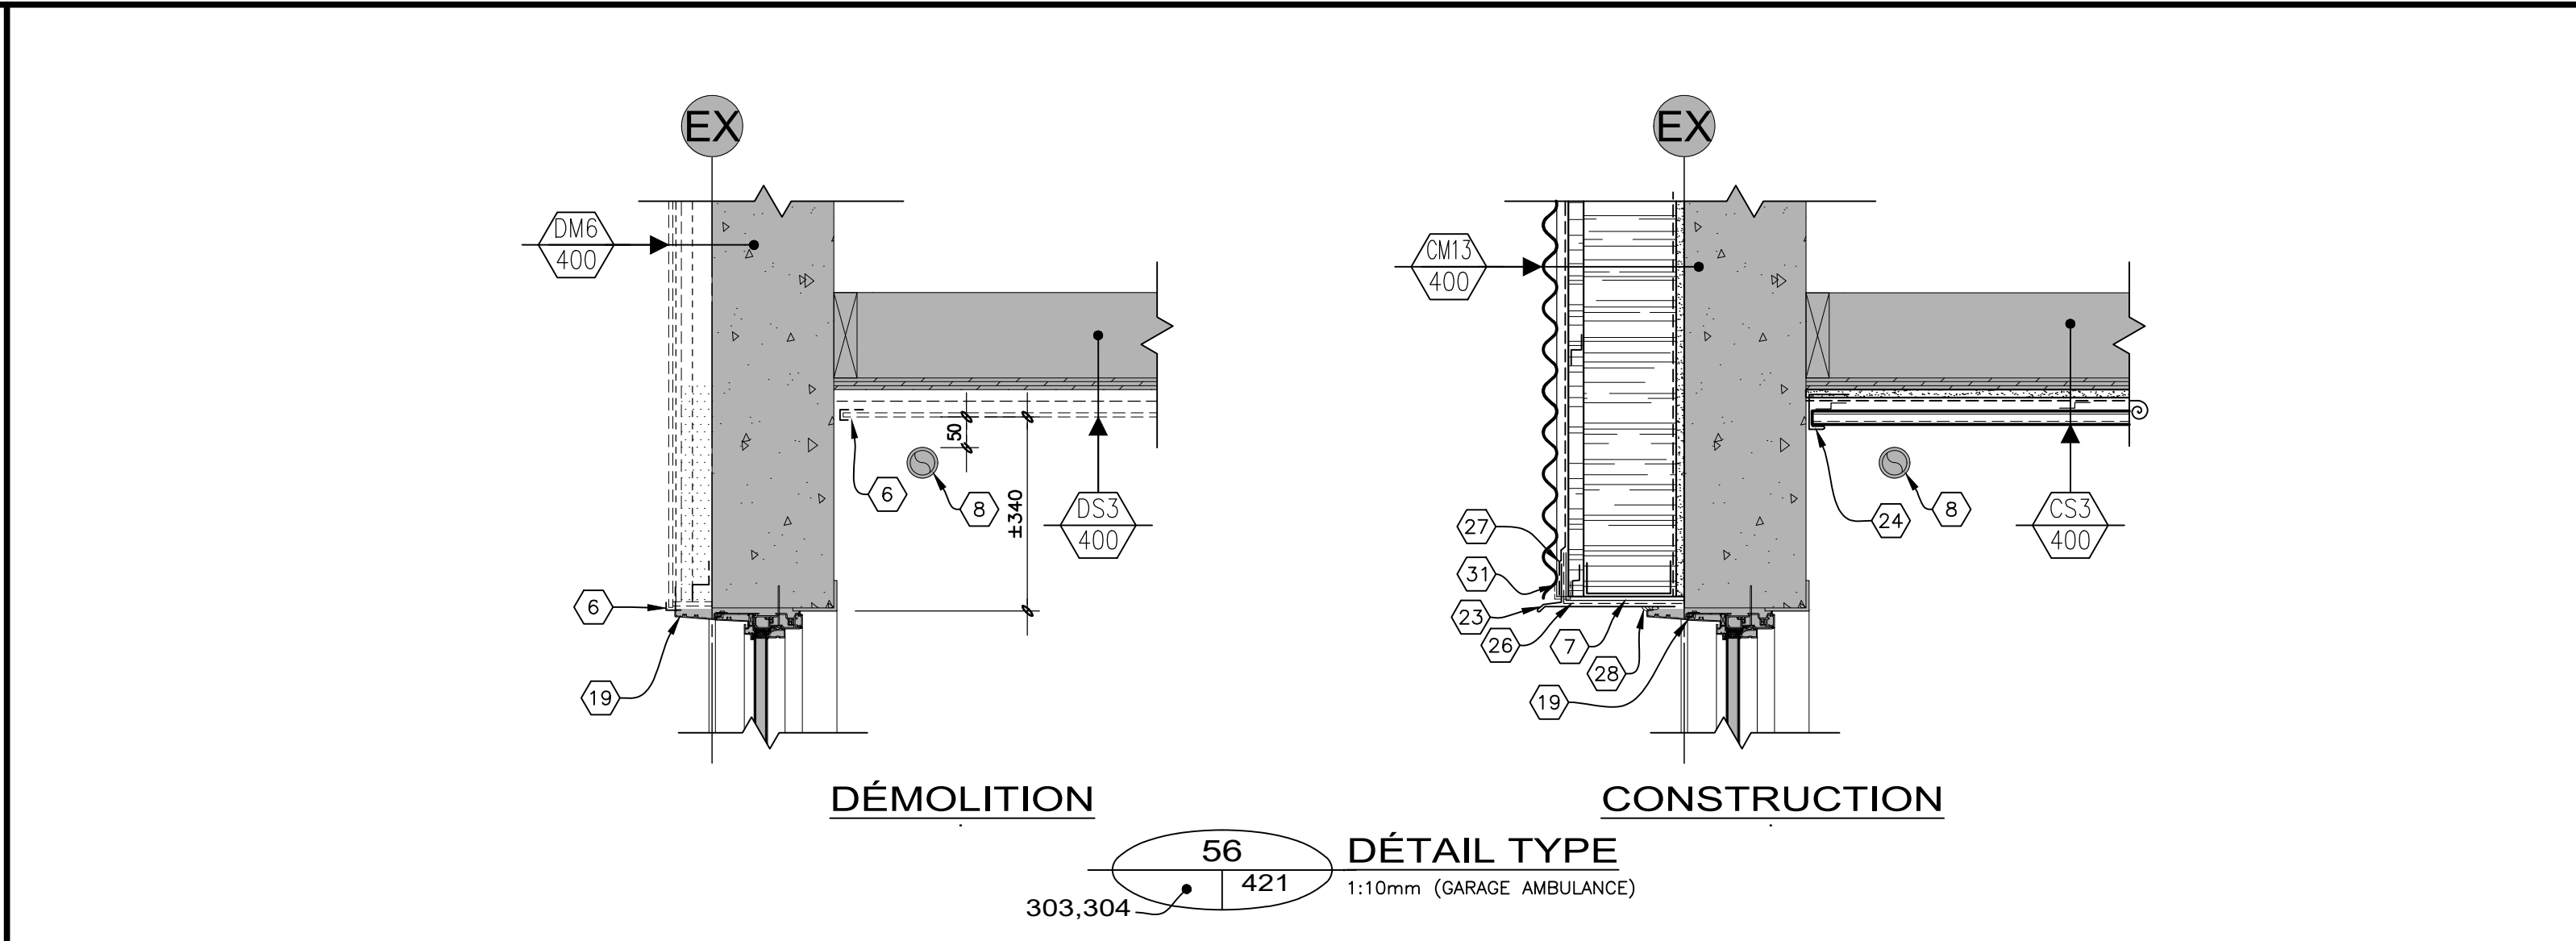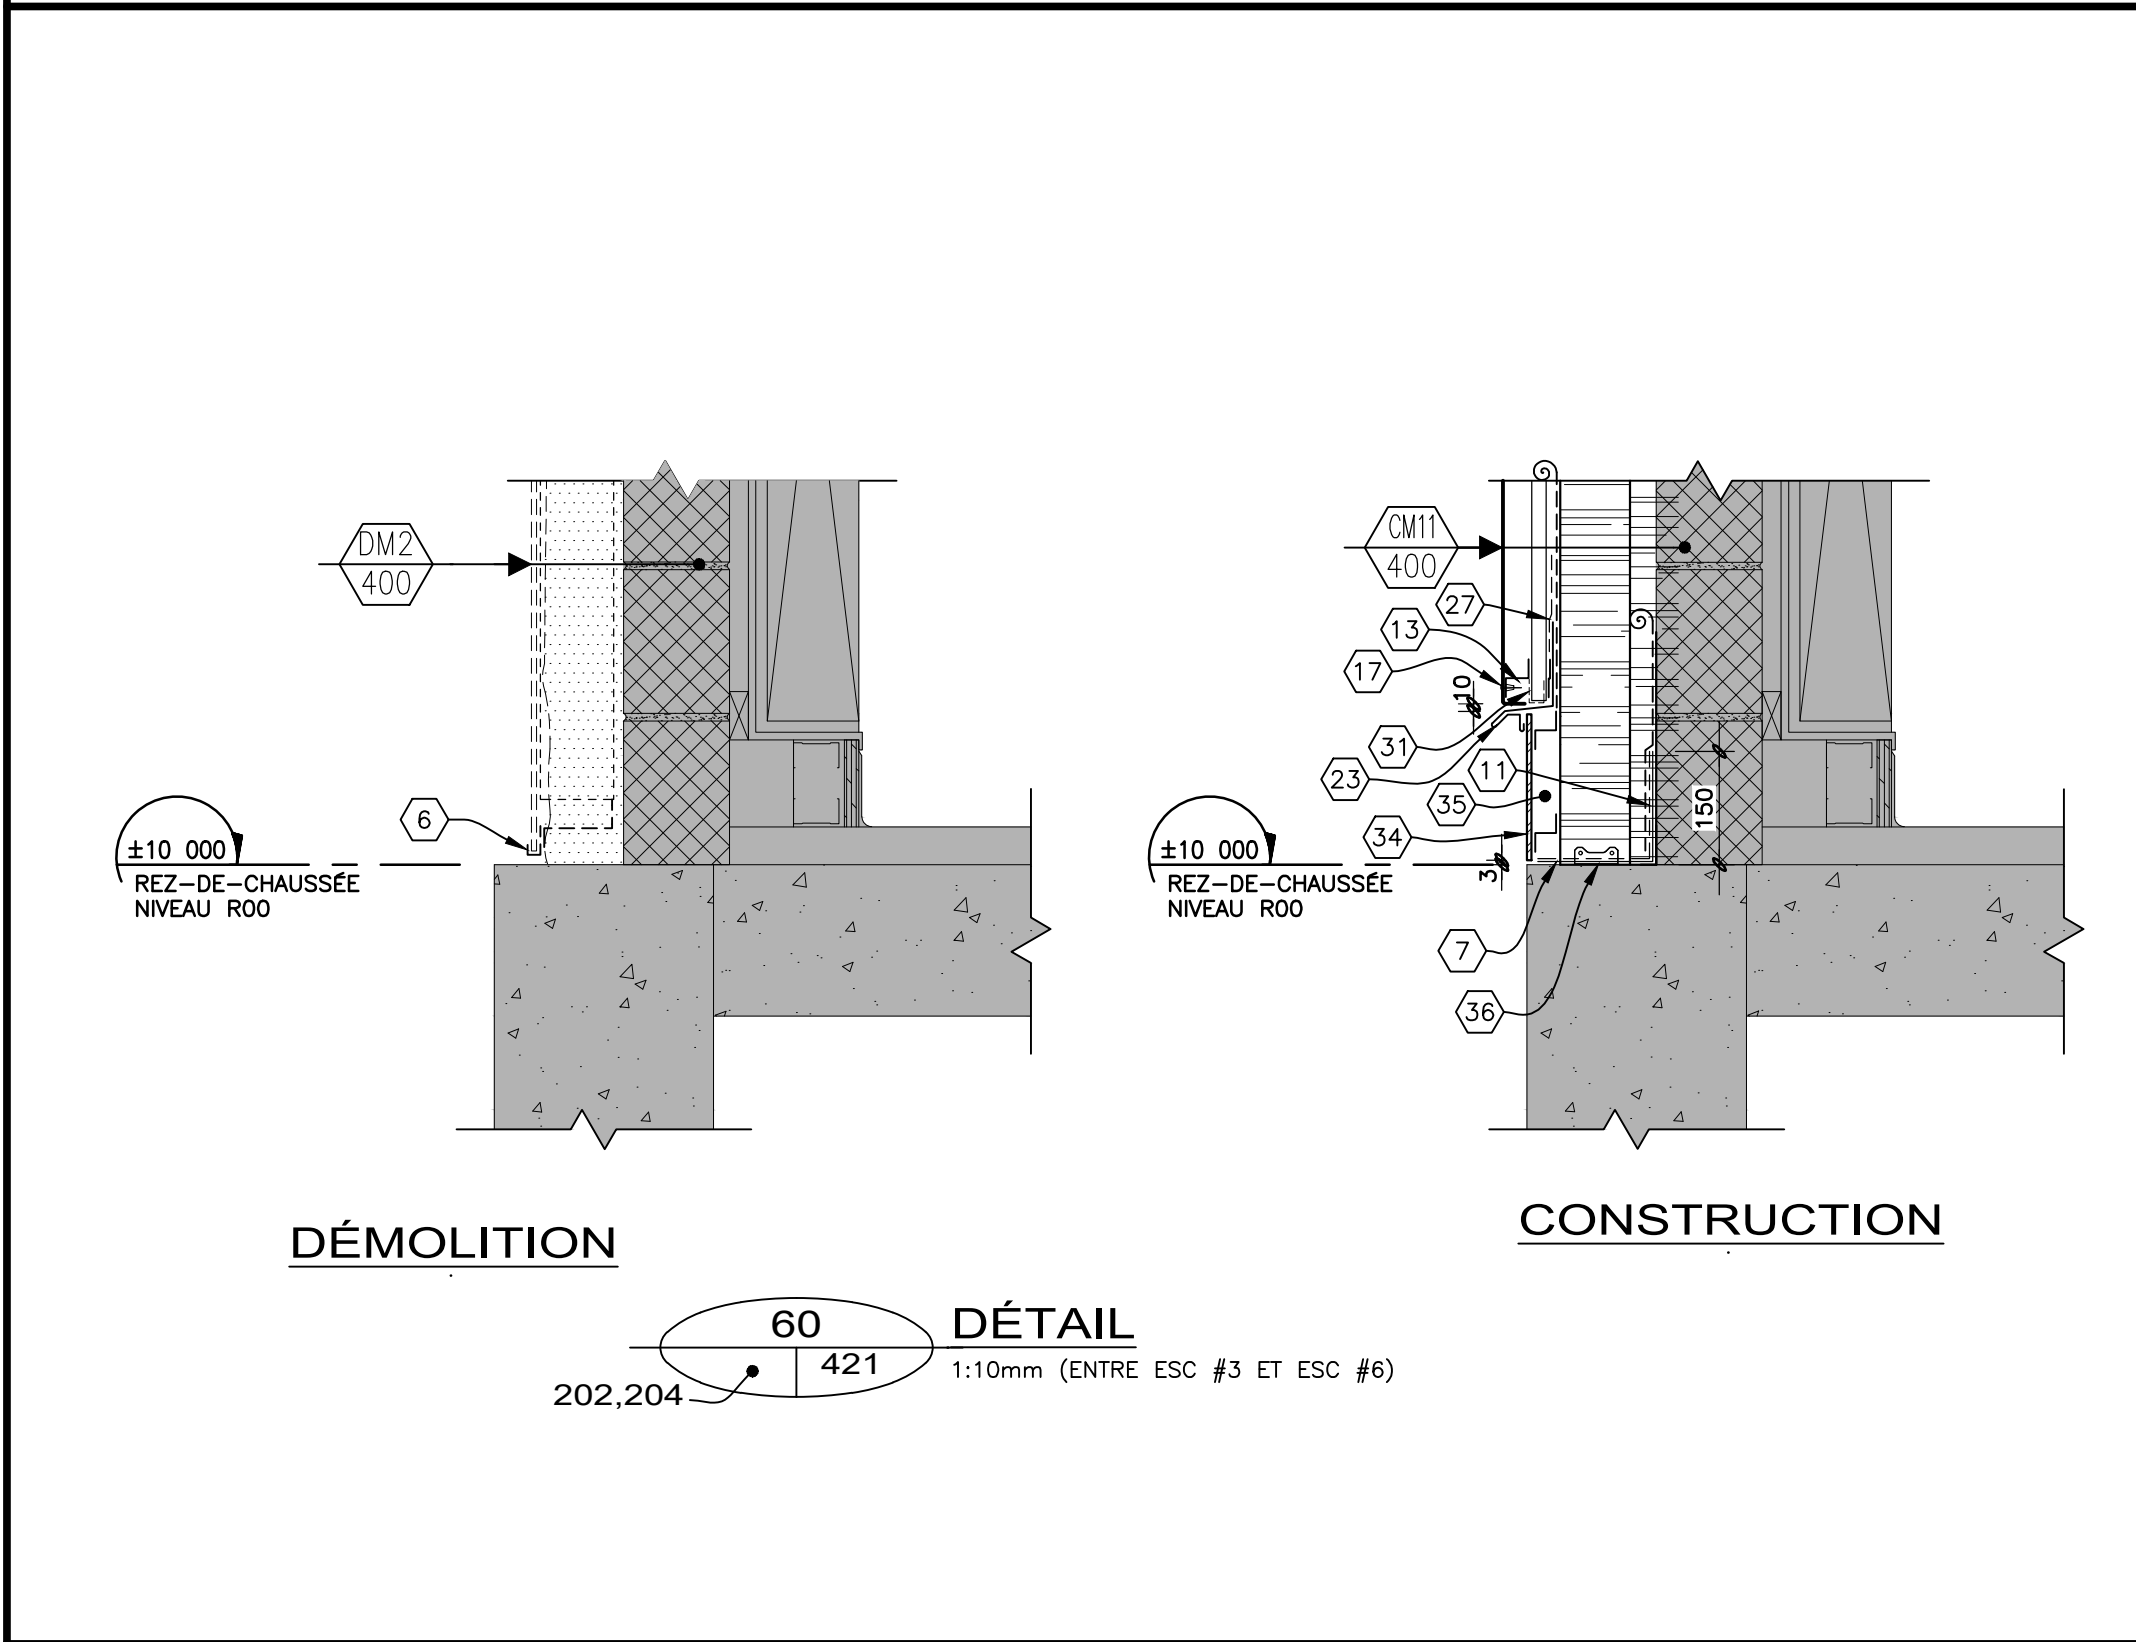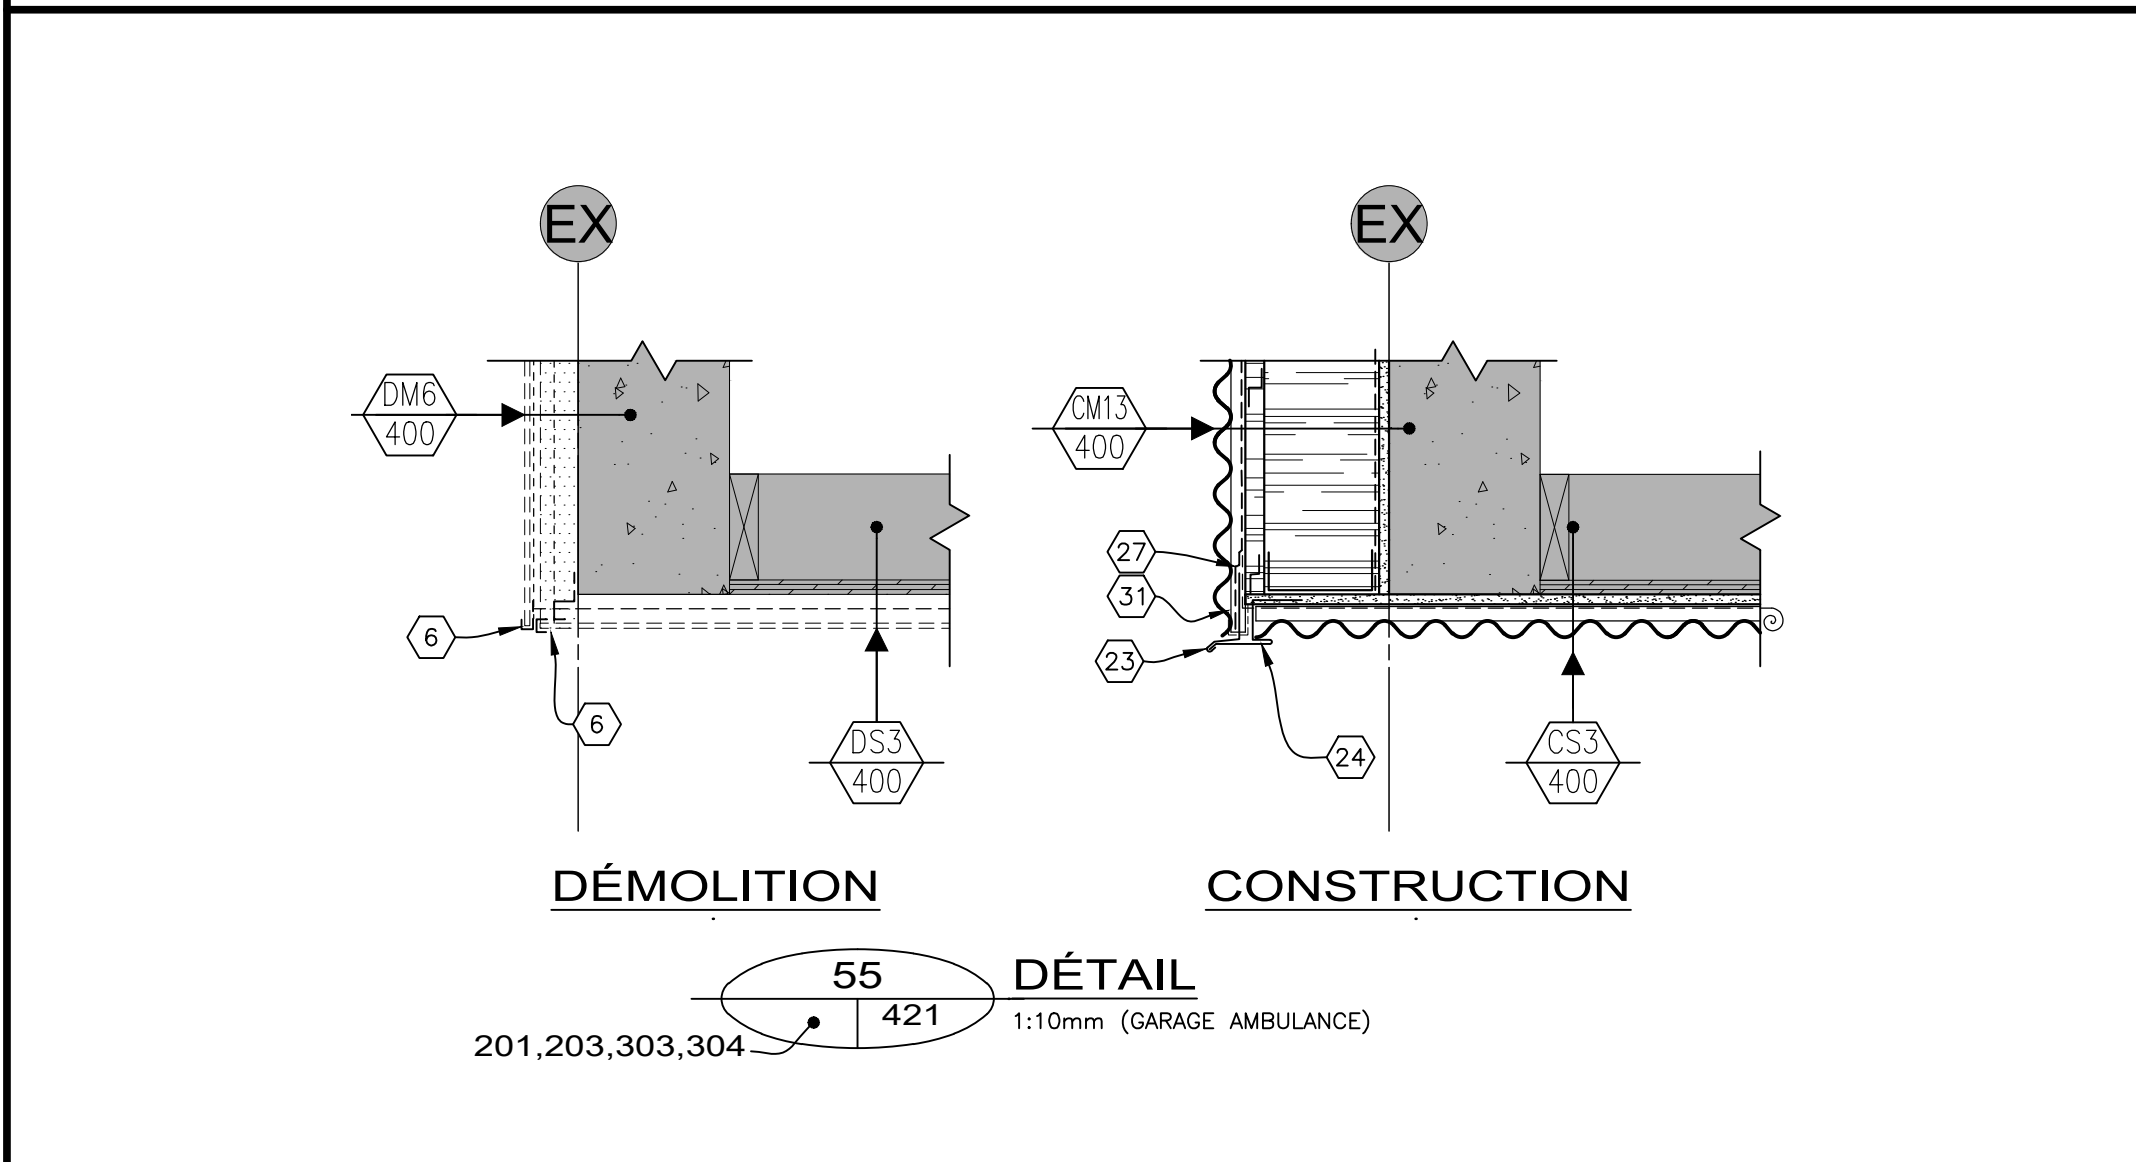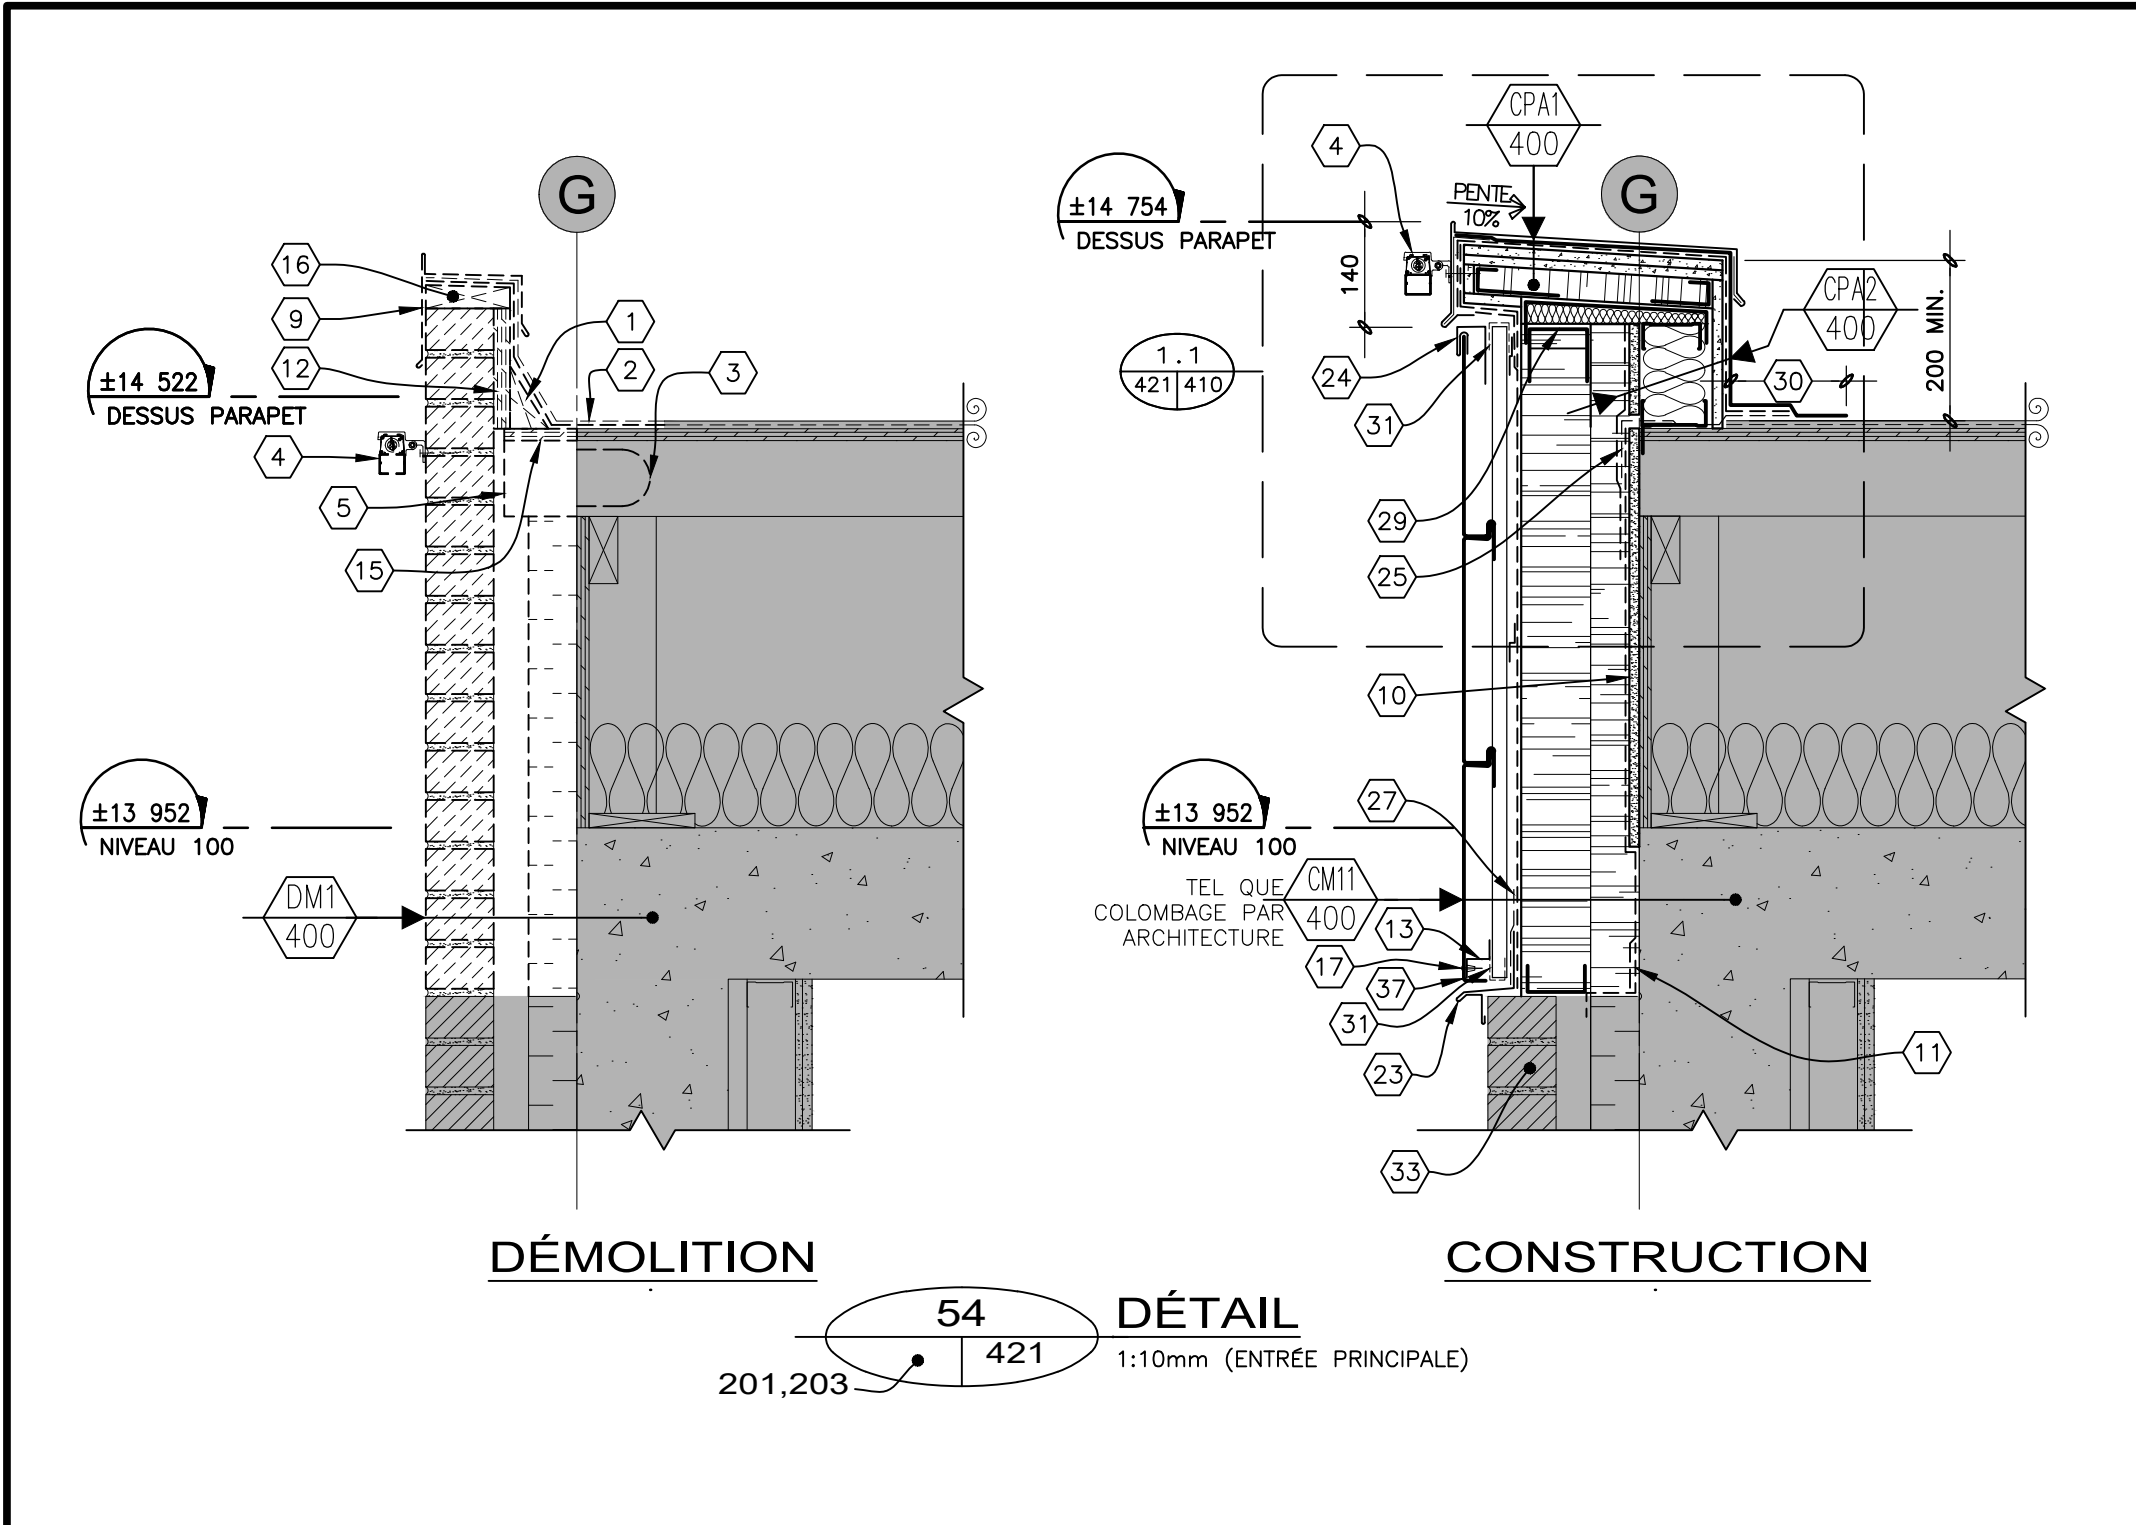

### NOTES

- PARAPET PERIMETRIQUE EN 38mmX140mm ET CONTREPLAQUE A DEMOLIR.
- MEMBRANE DE BITUME MODIFIEE BI-COUCHE A DEMOLIR SUR LA LARGEUR REQUISE POUR LA CONSTRUCTION DU NOUVEAU PARAPET.
- FILTRE MEDIA EXISTANT A ENLEVER.
- APPAREIL D'ECLAIRAGE CONTINUE SUR LA FAÇADE PRINCIPALE (SUD) DU BASILIAIRE A ENLEVER ET A REINSTALLER, VOIR INGENIEUR.
- MEMBRURE EXISTANTE DE 38mmX89mm A COUPER, VOIR STRUCTURE.
- MOULURE EN ALUMINIUM A DEMOLIR.
- TÔLE D'APPUI EN ACIER GALVANISE CAL.18.
- TUYAU DE GICLIER EXISTANT A ±509±340mm SOUS LE PAREMENT EXISTANT A CONSERVER / MODIFIER, VOIR MECANIQUE.
- SOLIN METALLIQUE A DEMOLIR.
- PANNEAU DE MAT DE FIBRE DE VERRE 16mm, TYPE X.
- SOLIN MEMBRANE.
- CONTREPLAQUE A PLUS EXISTANT A DEMOLIR.
- PLIAGE DE TÔLE EN ACIER GALVANISE, CAL.22.
- PANNEAU DE POLYMERES RENFORCE DE FIBRES DE VERRE 7mm D'EPaisseur A DEMOLIR.
- CONTREPLAQUE A PLUS EXISTANT A COUPER SUR LARGEUR REQUISE.
- PIECE DE BOIS EXISTANT A DEMOLIR.
- RIVET EN ACIER INOXYDABLE.
- CONTREPLAQUE A PLUS 16mm RECOUVRE D'UNE MEMBRANE AUTOCOLLANTE ET D'UNE TÔLE PLIEE EN ACIER EMAILLE CAL.24.
- FENÊTRE EXISTANTE A CONSERVER.
- MOULURE DE COIN INTERIEUR EN ACIER EMAILLE CAL.24.
- MOULURE DE COIN EXTERIEUR EN ACIER EMAILLE CAL.24.
- TÔLE PLIEE EN ACIER EMAILLE CAL.24.
- SOLIN EN ACIER EMAILLE, CAL.24 (JOINTS AGRAFES).
- MOULURE EN "J" EN ACIER EMAILLE CAL.24.
- MEMBRANE AUTOCOLLANTE. CHEVAUCHER D'AU MOINS 75mm LA MEMBRANE DU MUR ET LA MEMBRANE EXISTANTE DE LA TOITURE.
- MEMBRANE AUTOCOLLANTE.
- SCELLER LA MEMBRANE PARE-INTÉMPIRIES SUR LE SOLIN AVEC UN RUBAN AUTOCOLLANT.
- SCELLANT SUR FOND DE JOINT.
- LISSE DE DEFLEXION, PAR ARCHITECTURE.
- CHEVAUCHER LA NOUVELLE MEMBRANE SUR LES MEMBRANES DE LA TOITURE EXISTANTE SUR MINIMUM 150mm, DEGRANULER LA MEMBRANE EXISTANTE AU PREALABLE.
- MOUSTIQUEAIRE.
- SCELLANT.
- CREER DES EVENTS A MACONNERIE DANS L'AVANT DERNIER RANG DE BRIQUES DU MUR EXISTANT, EN EVIDANT LE JOINT DE MORTIER VERTICAL A TOUS LES 3 BRIQUES.
- PLAQUE EN ACIER GALVANISE A CHAUDE 150mm DE HAUT X 6mm D'EPaisseur. FIXER LA PLAQUE A L'AIDE DE VIS EN ACIER INOXYDABLE A TETE FRAISEE.
- BARRE "Z" 38mm CAL.18.
- CONNECTEUR A CHAQUE COLOMBAGES OU BARRE "Z" SELON LE CAS, VOIR STRUCTURE.
- BOUT DU PANNEAU REPLIE VERS L'INTERIEUR.
- PANNEAU DE MAT DE FIBRE DE VERRE RECOUVRE D'UE TÔLE EN ACIER EMAILLE CAL.24. INSTALLER LE PANNEAU SUR DES FOURRURES D'EPaisseurs REQUISES

### LÉGENDE

|                                 |                                                                                    |
|---------------------------------|------------------------------------------------------------------------------------|
|                                 | EXISTANT A CONSERVER.                                                              |
|                                 | ELÉMENT A DEMOLIR.                                                                 |
|                                 | AXE EXISTANT                                                                       |
|                                 | EXTERIEUR DE LA STRUCTURE DE BETON EXISTANTE DE LA TOUR.                           |
|                                 | NOUVEL AXE: FACE EXTERIEURE DES BARRES Z ET COLOMBAGES DE LA TOUR. VOIR STRUCTURE. |
| (*) VOIR NOTE GENERAL PAGE 400. |                                                                                    |

### NE DOIT PAS SERVIR À L'EXÉCUTION

Le présent document est émis pour la seule fin identifiée. Son contenu est protégé par les droits d'auteur et toute reproduction ou modification, partielle ou totale, est interdite sans l'autorisation écrite de gagnon, letellier, cyr, ricard, mathieu, proulx, savard consortium d'architectes.

GLCRM | Proulx Savard |  
GLCRM:  
128, Avenue de la Cathédrale,  
Bureau 201  
Rimouski, QC, G5L 5H7  
(418) 722-7655  
2406, Ch. des Quatres-Bourgeois,  
Bureau 100  
Québec, QC, G1V 1W5  
(418) 647-1700  
Proulx Savard Architectes:  
75, boul. Arthur-Buies Ouest,  
Rimouski QC G5L 5C2  
(418) 722-5543  
ARCHITECTURE

CONSULTANTS  
  
Ode des architectes  
3276  
FRANÇOIS MATHIEU  
ARCHITECTE  
Ode des architectes  
3276  
FRANÇOIS MATHIEU  
ARCHITECTE

| DESIGNATEUR (S) | DOSSIER No.     | DATE           | REVISIONS                          |
|-----------------|-----------------|----------------|------------------------------------|
| DB ALL          | 24-1087-6857-24 | SEPTEMBRE 2024 |                                    |
| ÉCHELLE         |                 |                |                                    |
|                 | 05              | 2024-09-04     | DÉFINITIVES POUR SOUMISSION        |
|                 | 06              | 2024-08-21     | DÉFINITIVES 100% POUR APPROBATION  |
|                 | 03              | 2024-08-03     | DÉFINITIVES 80% POUR APPROBATION   |
|                 | 02              | 2024-05-14     | DÉFINITIVES 40% POUR APPROBATION   |
|                 | 01              | 2024-02-27     | PRÉLIMINAIRES 20% POUR APPROBATION |
| No              |                 | DATE           |                                    |


DESIGN  
DÉTAIL TYPE  
DEMOLITION ET CONSTRUCTION

PROJET  
HÔPITAL DE CHANDLER,  
Chandler  
(réfection de l'enveloppe)

PROPRIÉTAIRE  
Santé Québec

421




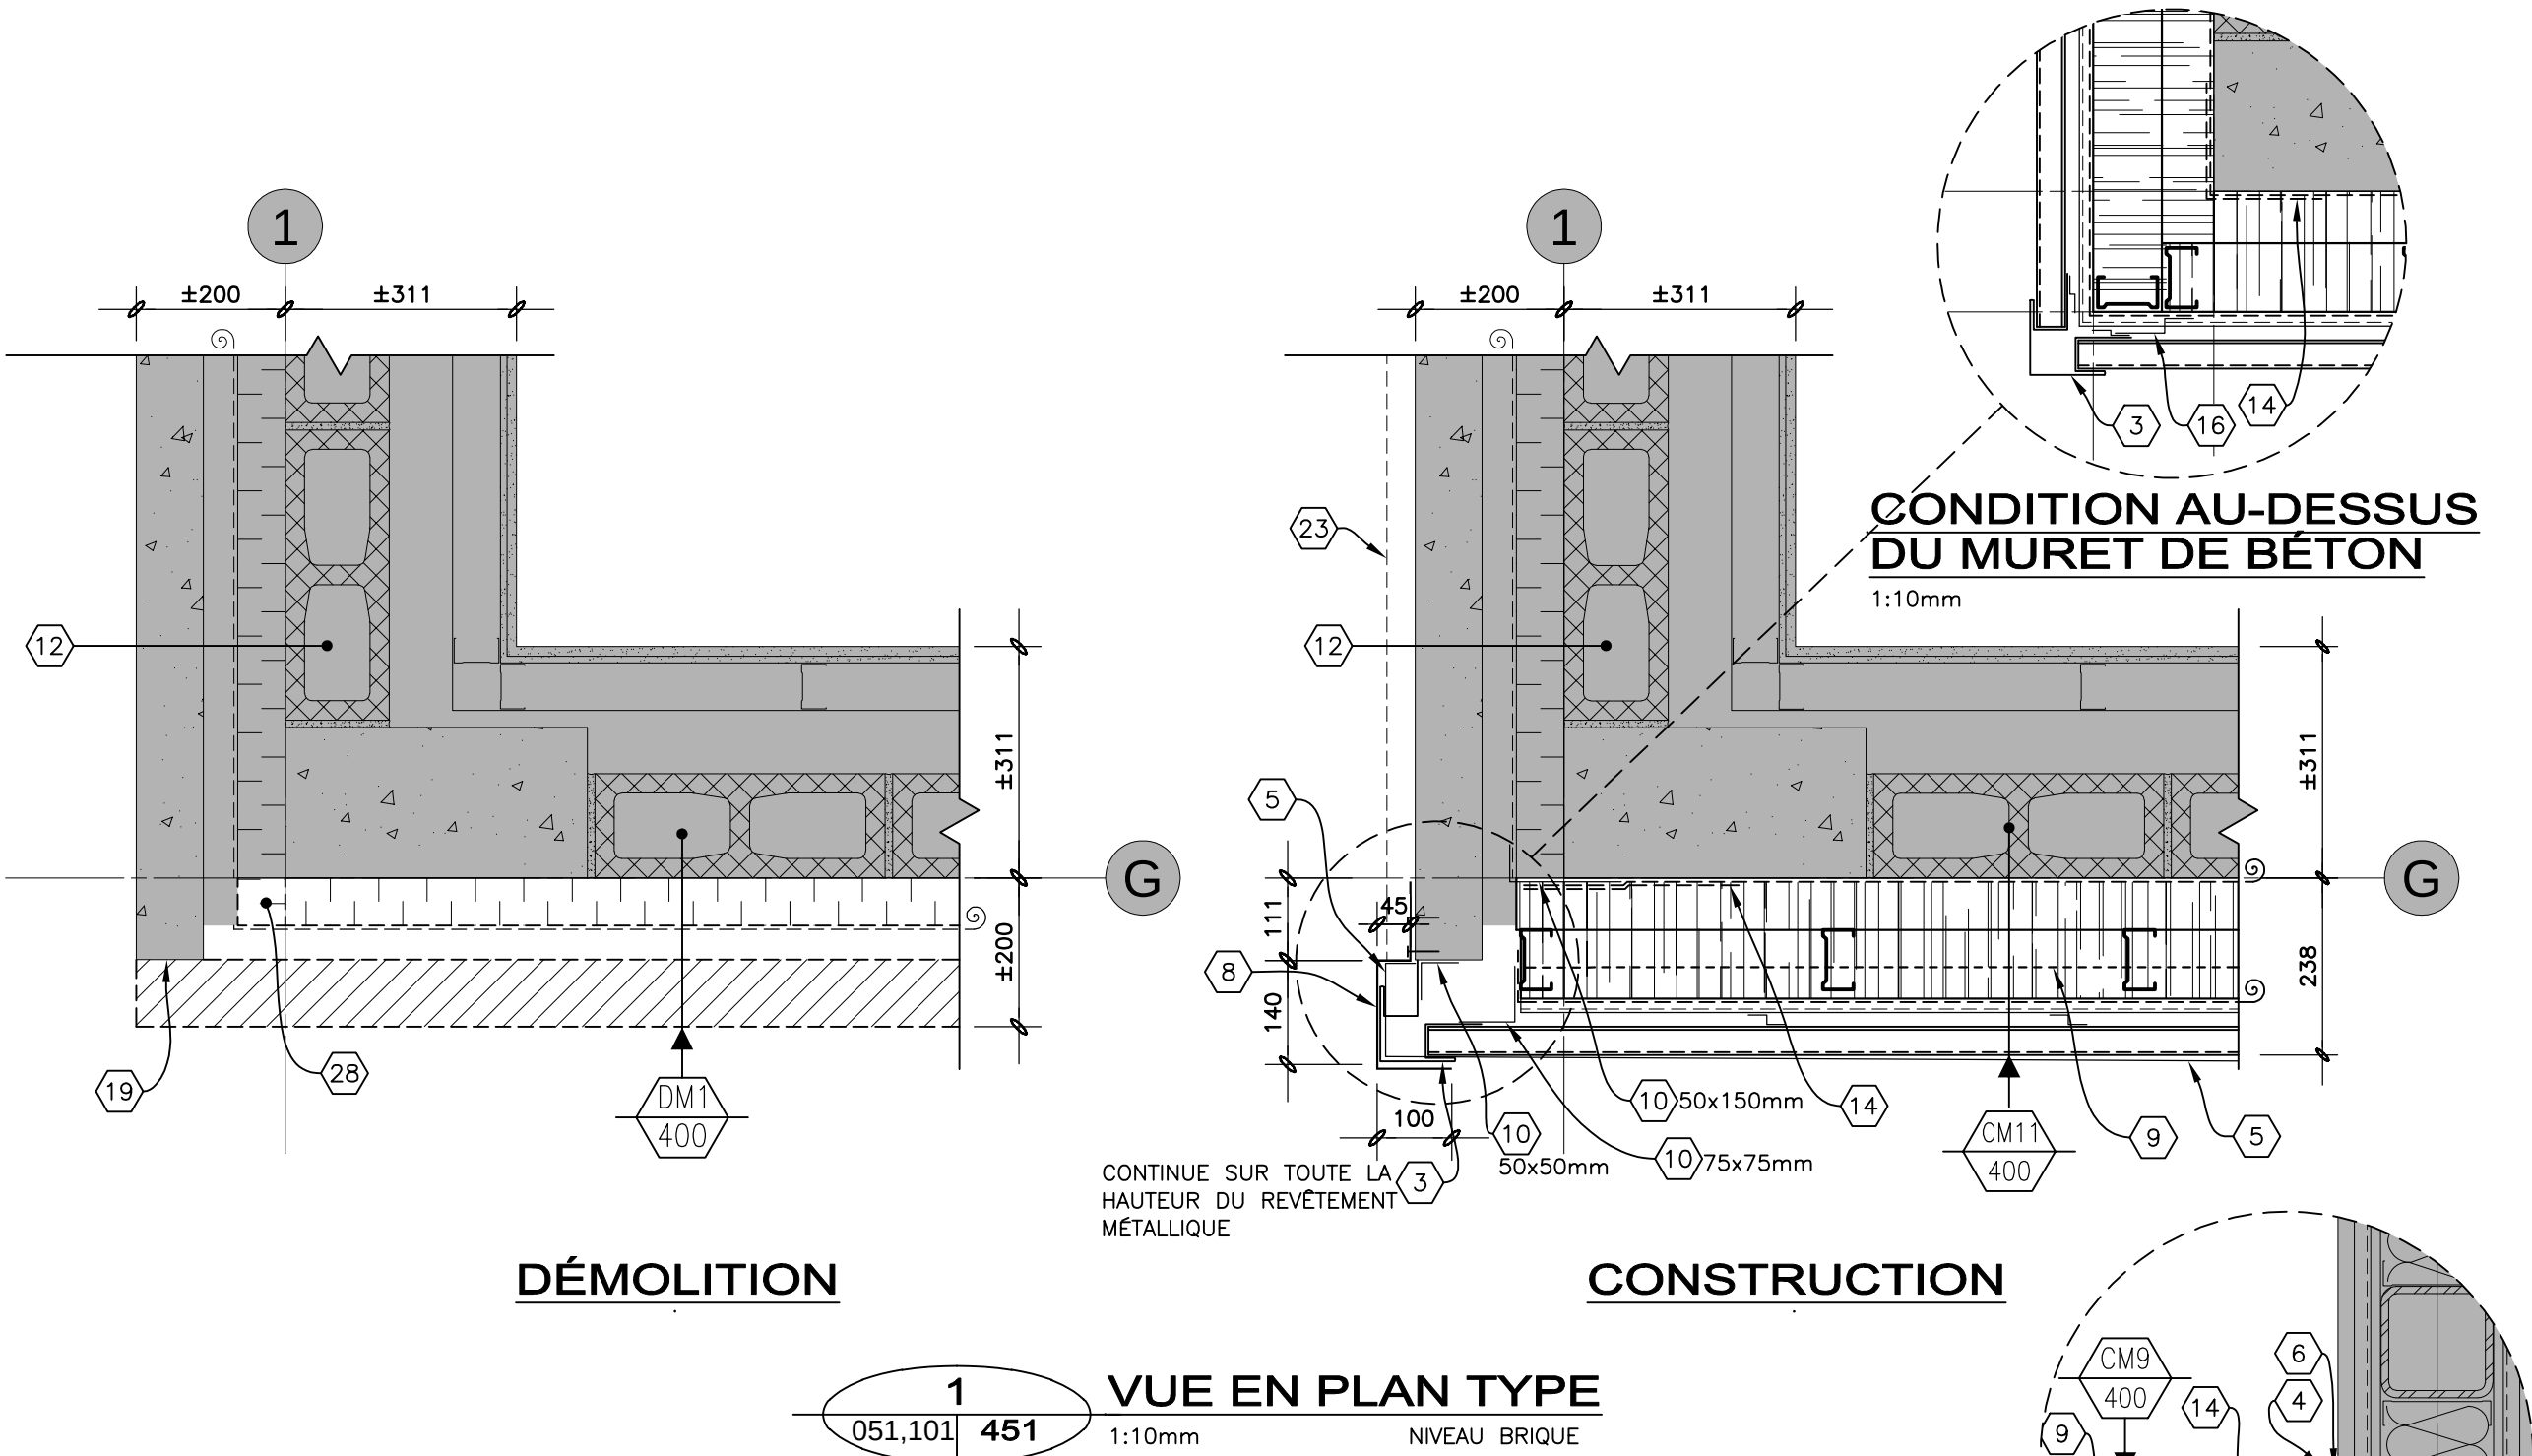

DÉMOLITION

CONSTRUCTION


1 VUE EN PLAN TYPE  
051.101 451  
1:10mm  
NIVEAU BRIQUE

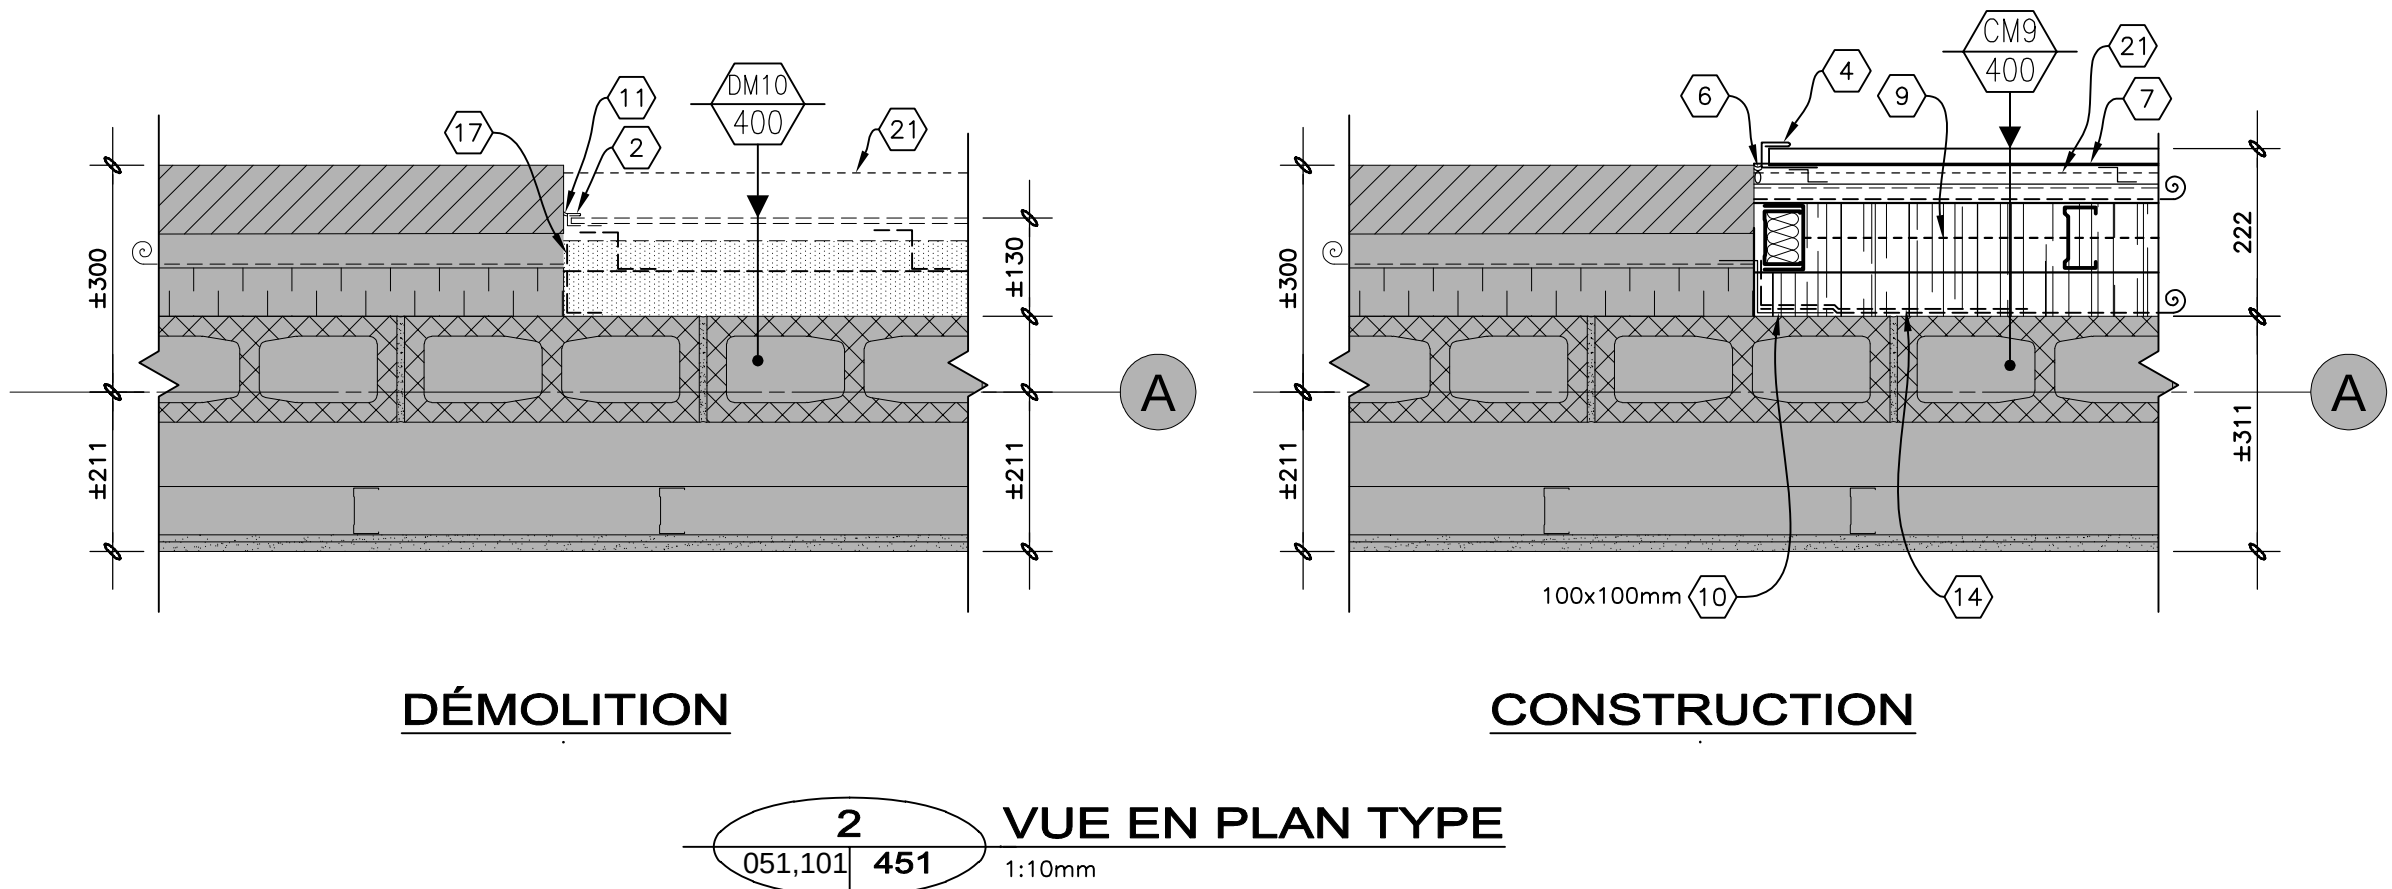

DÉMOLITION

CONSTRUCTION


2 VUE EN PLAN TYPE  
051.101 451  
1:10mm

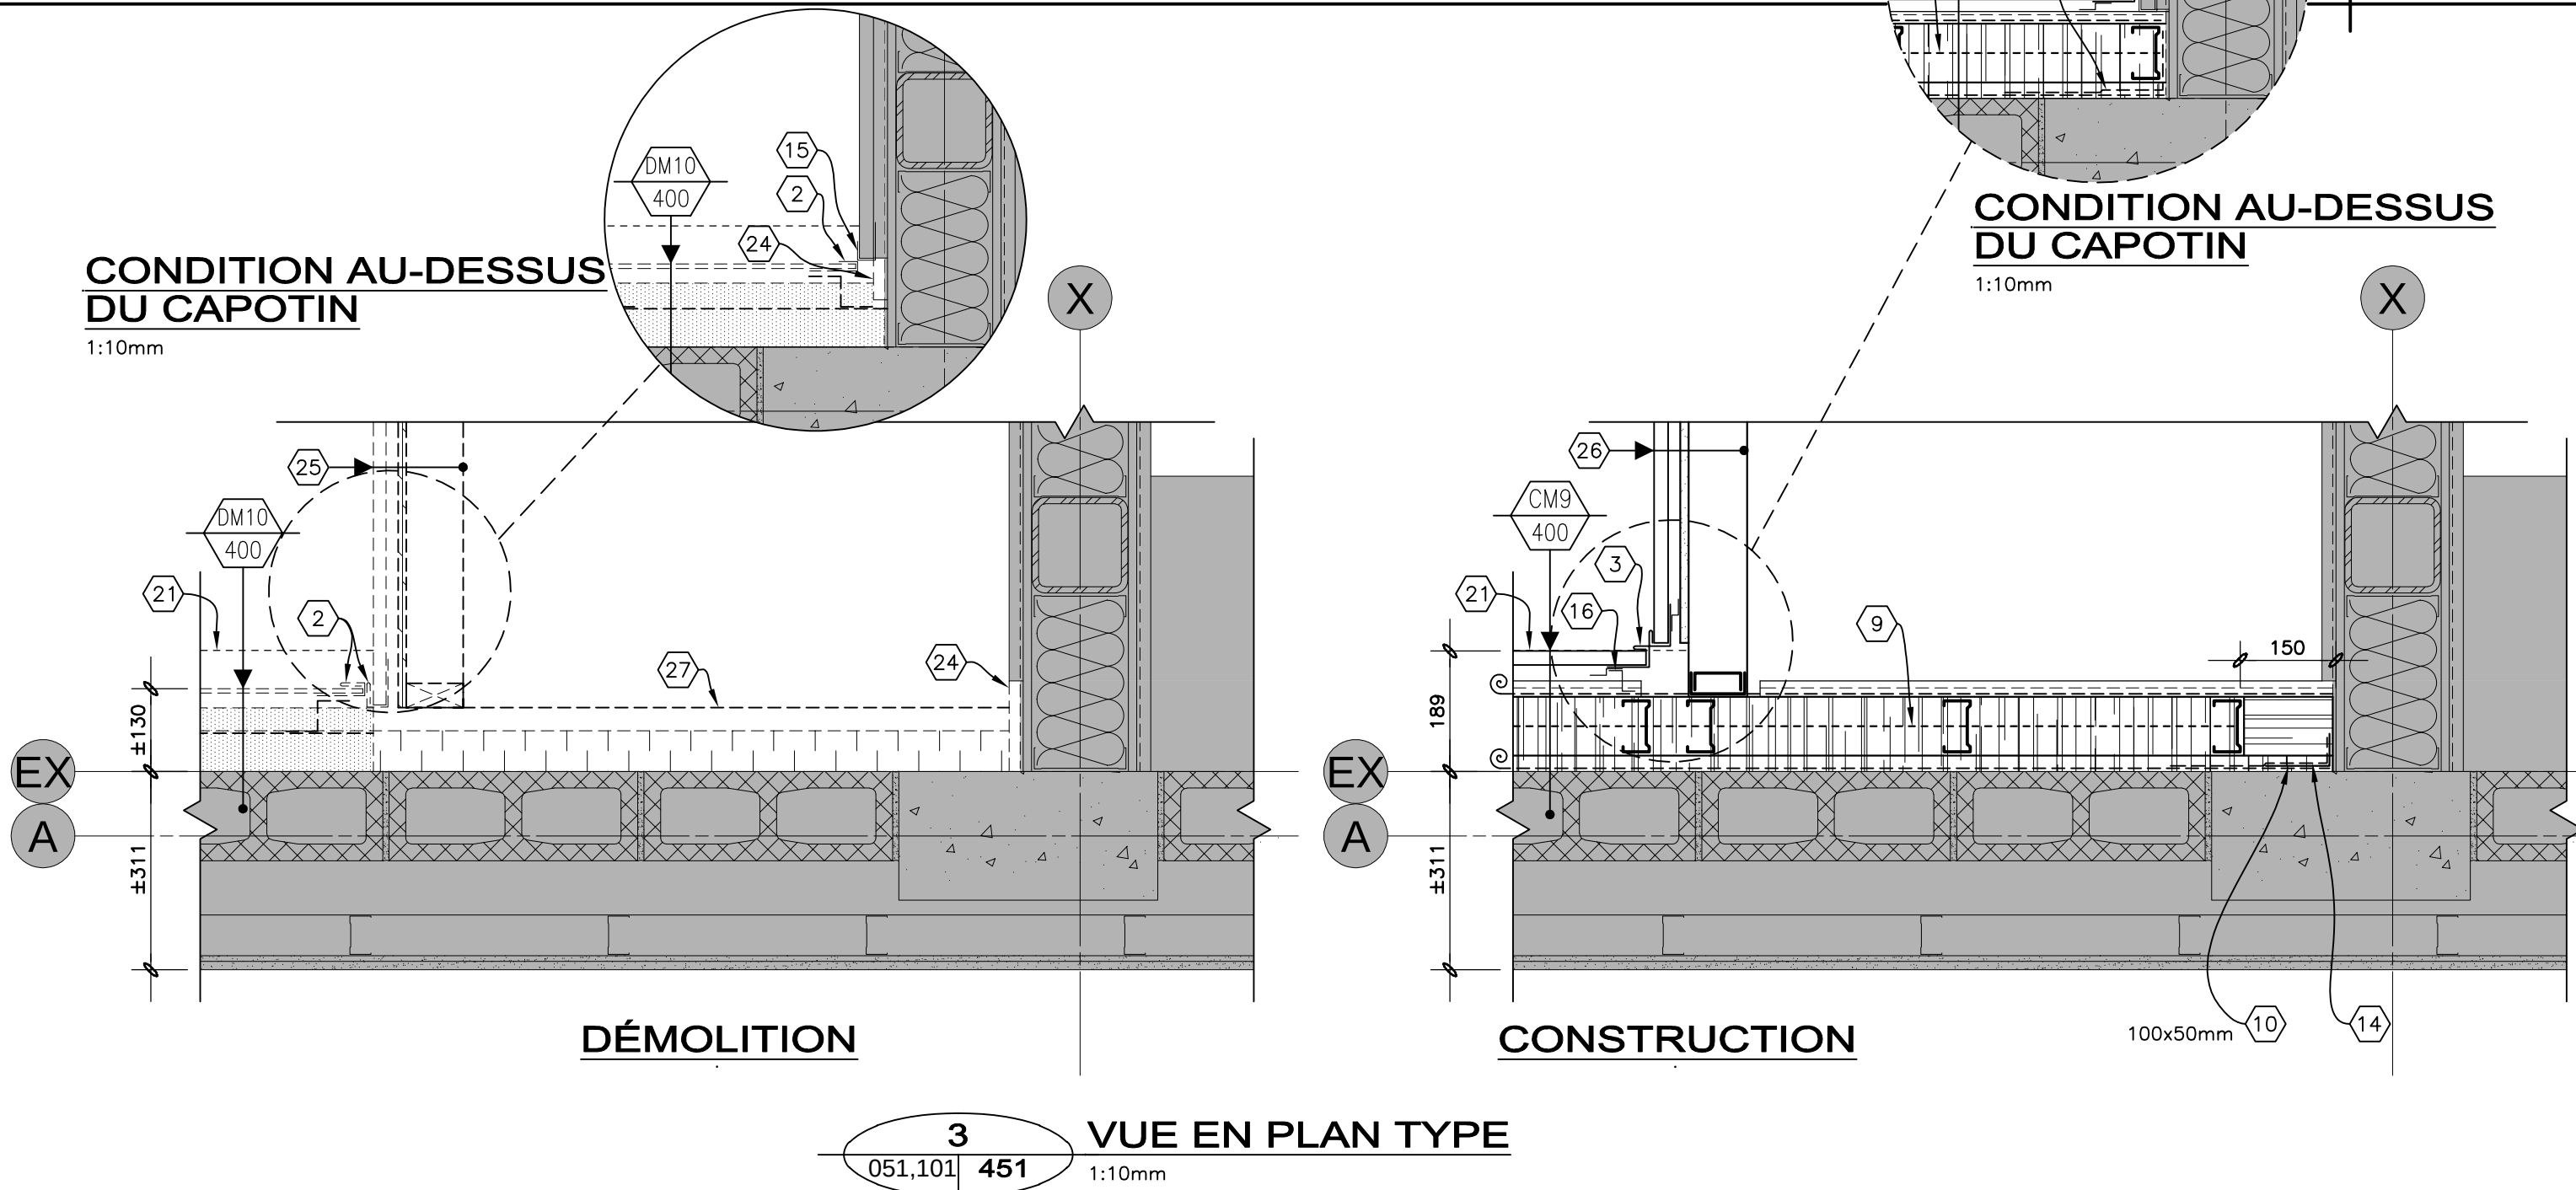

DÉMOLITION

CONSTRUCTION


3 VUE EN PLAN TYPE  
051.101 451  
1:10mm

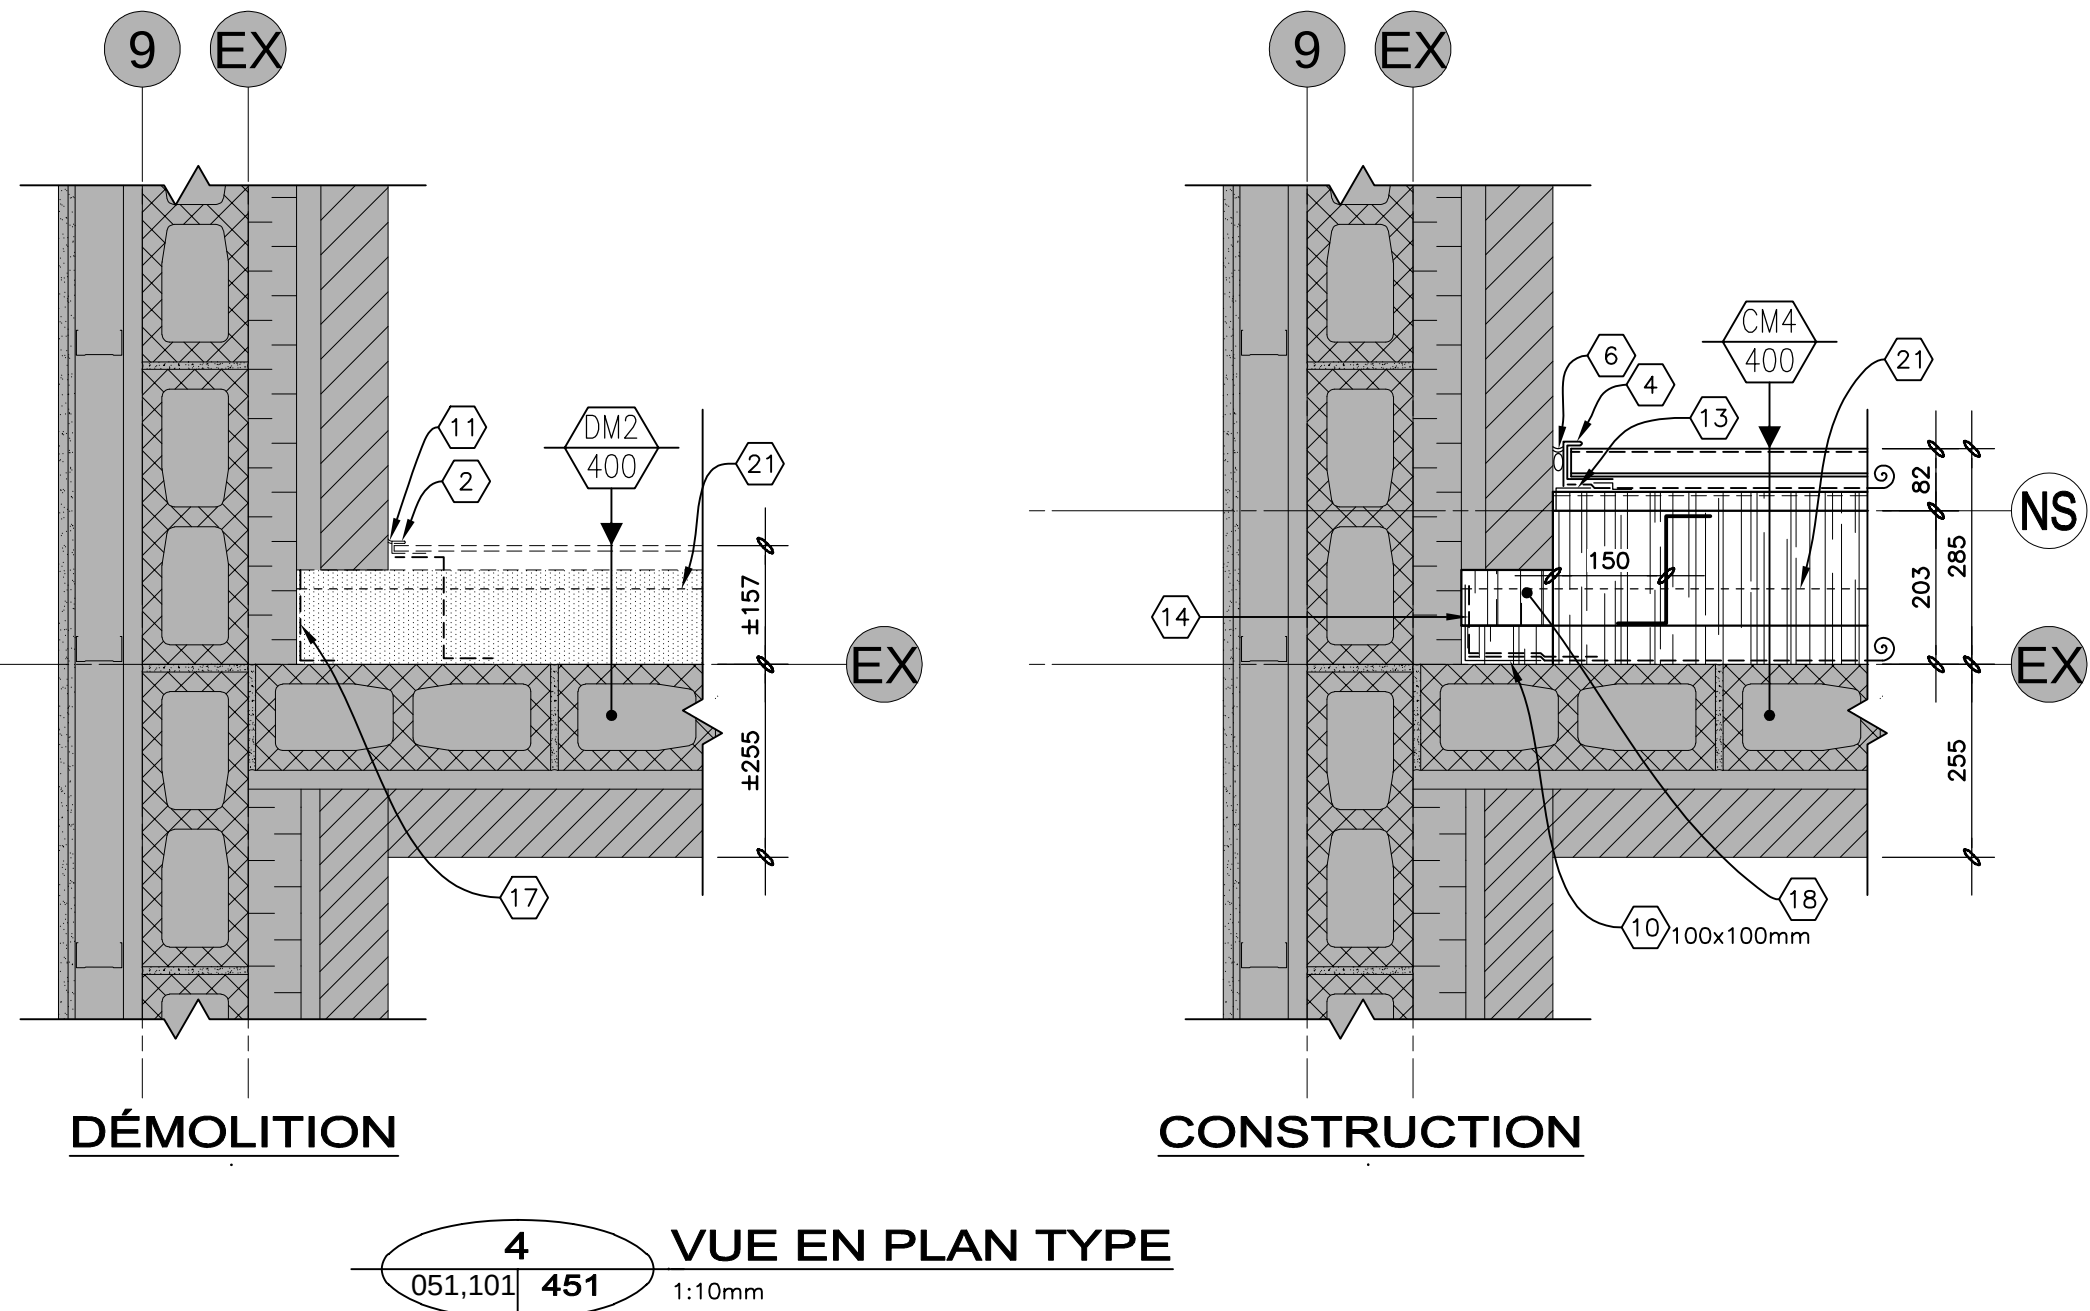

DÉMOLITION

CONSTRUCTION


4 VUE EN PLAN TYPE  
051.101 451  
1:10mm

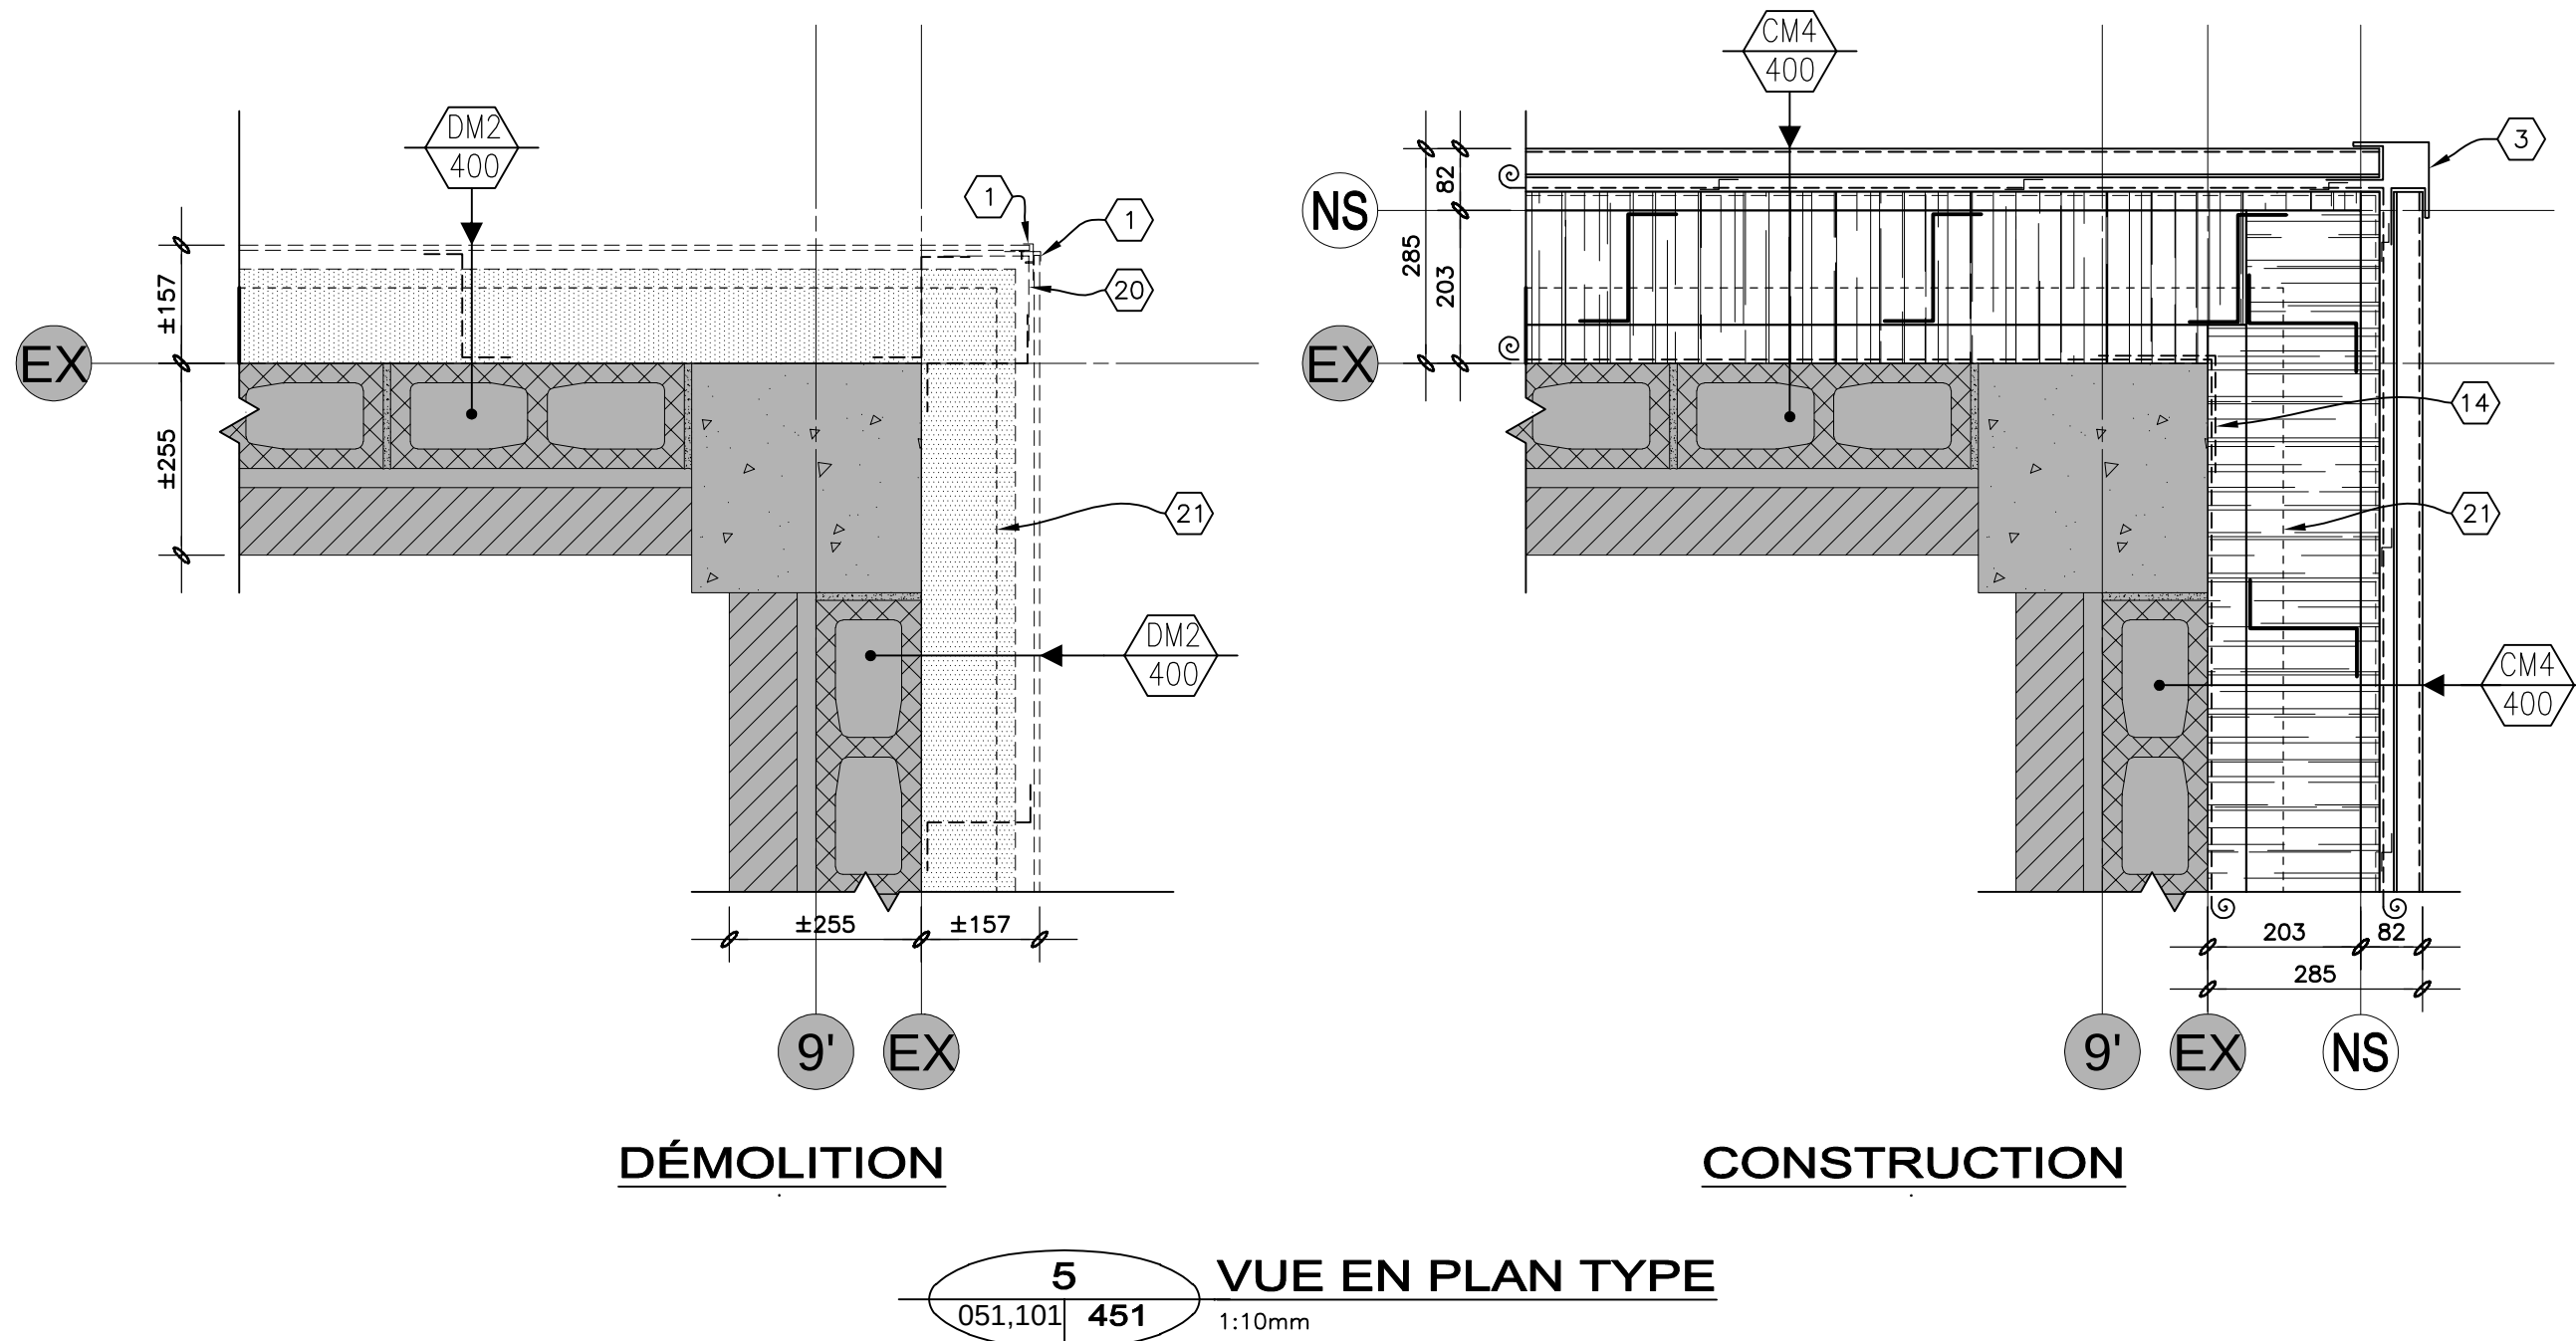

DÉMOLITION

CONSTRUCTION

5 VUE EN PLAN TYPE  
051.101 451  
1:10mm

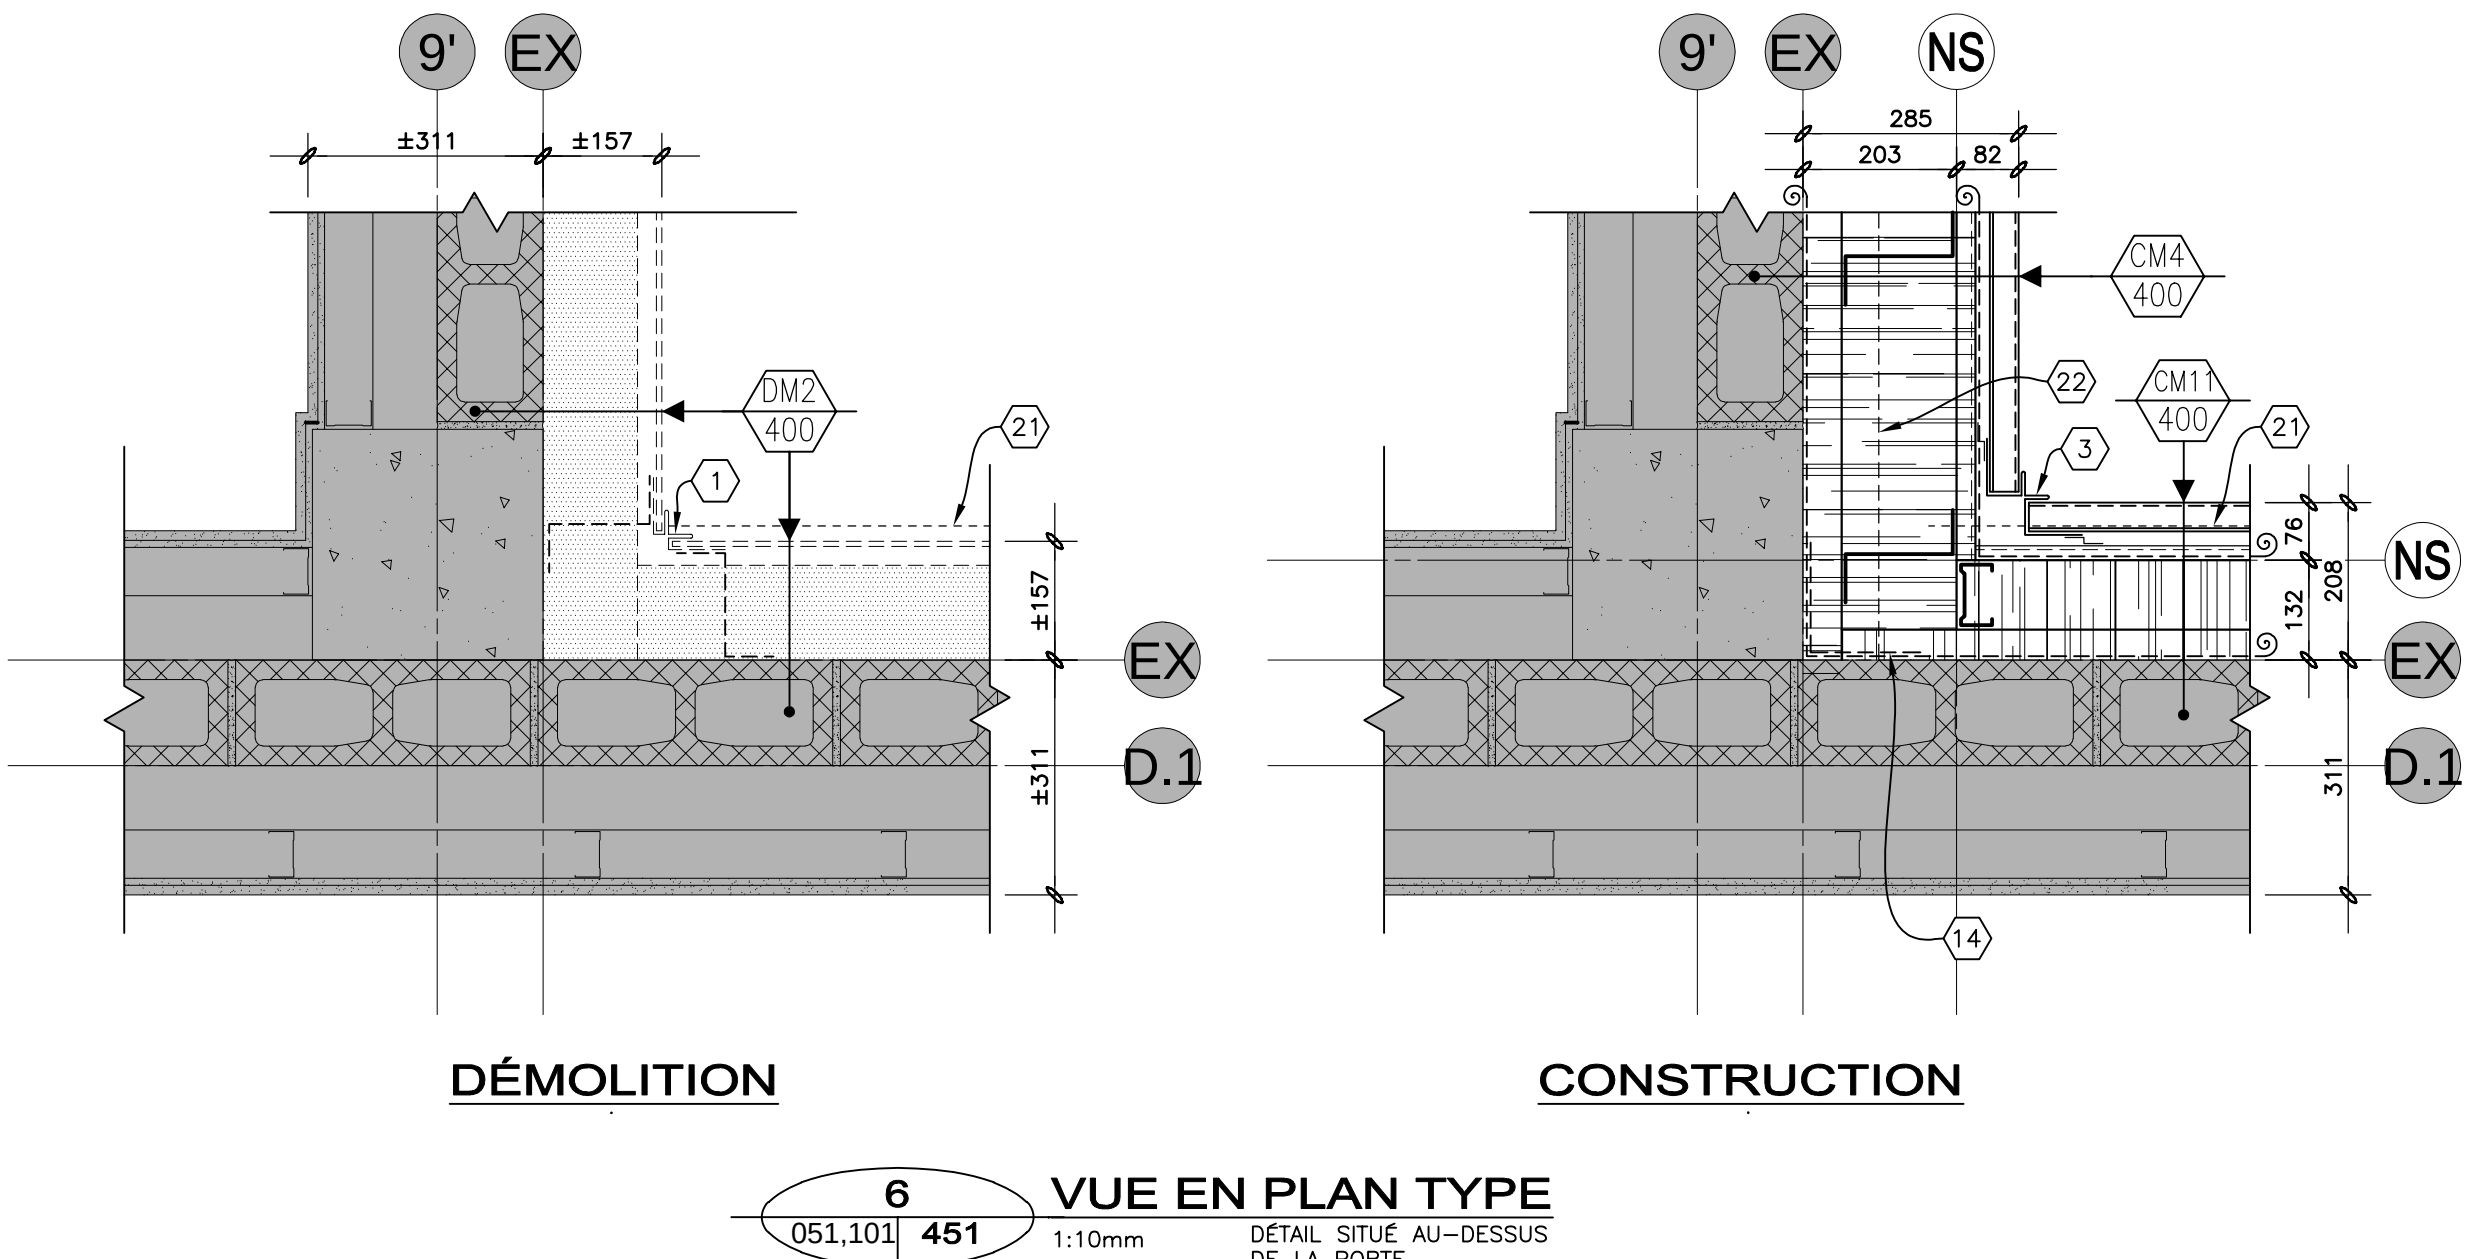

DÉMOLITION

CONSTRUCTION

6 VUE EN PLAN TYPE  
051.101 451  
1:10mm  
DÉTAIL SITUÉ AU-DESSUS  
DE LA PORTE

## NOTES

- MOULURE DE COIN EXISTANTE À DÉMOLIR.
- MOULURE EN "J" EXISTANTE À DÉMOLIR.
- MOULURE DE COIN DE PAREMENT EN ACIER ÉMAILLÉ, CAL.22.
- MOULURE EN "J" EN ACIER ÉMAILLÉ, CAL.22.
- PROFIL DU SOLIN SUR LA FONDATION. LE SOLIN DOIT TOURNER LE COIN JUSQU'AU MUR DE BÉTON EXISTANT.
- SCÉLLANT CONTINU SUR BOUDIN COMPRESSIBLE 10mm MINIMUM.
- LIMITE DE SOLIN EN-DESSOUS.
- PLIAGE EN ACIER INOXYDABLE DE 3mm AVEC ANCRAGE CHIMIQUE @ 610mm C/C. HAUTEUR DE ± 1930mm.
- REMPUR L'ENTREMISE ET LES ESPACES DE PART ET D'AUTRE D'ISOLANT DE FIBRE DE ROCHE FLEXIBLE, VOIR DÉTAIL #8.1 DE LA FEUILLE 411.
- PLIAGE EN ACIER GALVANISÉ EN "L", CAL.18.
- SCÉLLANT EXISTANT À DÉMOLIR.
- COMPOSITION EXISTANTE À CONSERVER:
  - MUR DE BÉTON;
  - ESPACE D'AIR;
  - ISOLANT 64mm D'ÉPAISSEUR;
  - BLOC DE BÉTON 140mm D'ÉPAISSEUR.
- PLIAGE EN ACIER GALVANISÉ EN "L" VERTICAL CONTINU, CAL.18 POUR RELIER LES FOURRURES ENTRE ELLES.
- MEMBRANE DE TYPE-1.
- MOULURE DE PAREMENT EXISTANTE À CONSERVER.
- TÔLE DE COMPARTIMENTATION CONTINU SUR TOUTE LA HAUTEUR DE L'ETAGE, CAL.24.
- PLIAGE DE TÔLE EN "L" À DÉMOLIR.
- REMPUR L'ESPACE AVEC UN BLOC D'ISOLANT DE FIBRE DE ROCHE SEMI-RIGIDE DE 150mm ET UN DE 75mm.
- NETTOYER ET GRATTER TOUS LES RÉSIDUS DE MORTIER EXISTANT.
- TÔLE DE COIN EXISTANTE À DÉMOLIR.
- PROFIL DE LA FONDATION EXISTANTE.
- PROFIL DU MURET DE BÉTON.
- PAREMENT D'ACIER AU-DESSUS DU MURET DE BÉTON.
- COUPER LA BARRE "Z" DE DIMENSION APPROPRIÉE.
- EMBOÎTEMENT À DÉMOLIR:
  - PAREMENT D'ACIER À DÉMOLIR;
  - FOURRURE DE BOIS À DÉMOLIR;
  - CONTREPLAQUE À DÉMOLIR;
  - STRUCTURE DE BOIS À DÉMOLIR.
- NOUVEAU SOUFFLAGE POUR CONDUIT DE MÉCANIQUE:
  - PAREMENT D'ACIER CORRUGUÉ 22mm, CAL.24;
  - BARRE "Z" 19mm D'ÉPAISSEUR, CAL.16 @ 400mm C/C;
  - MEMBRANE PARE-AIR/INTÉPIÉRIES (TYPE 4) FERMÉABLE À LA VAPEUR D'EAU AUTO-ADHÉSIVE, JOINTS CHEVAUCHÉS;
  - PANNEAU DE MÂT DE FIBRE DE VERRE 13mm D'ÉPAISSEUR;
  - COULMBAGE MÉTALLIQUE 92mm @ 400mm C/C CAL.16.
- PIECE DE BOIS EXISTANTE À DÉMOLIR.
- ISOLANT À DÉMOLIR.




GLCRM | Proulx Savard |

GLCRM:  
178, Avenue de la Cathédrale,  
Bureau 201  
Rimouski, QC, G5L 5H7  
(418) 722-7655


2406, Ch. des Quatres-Bourgeois,  
Bureau 100  
Québec, QC G1V 1W5  
(418) 647-1700

Proulx Savard Architectes:  
75, boul. Arthur-Buies Ouest,  
Rimouski QC G5L 5C2  
(418) 723-5543

ARCHITECTURE

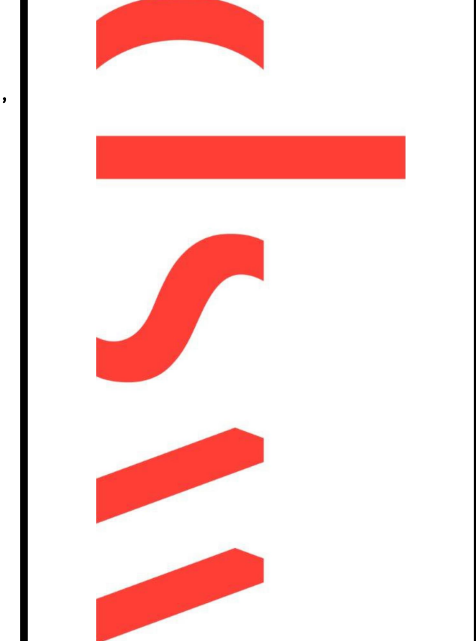

CONSULTANTS

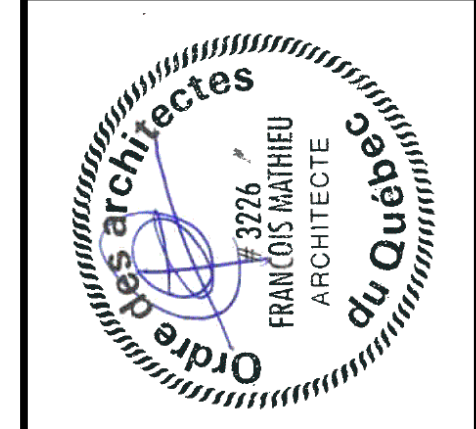

| DESSINATEUR (S)  | AC.        | ÉCHELLE                            | INDIQUÉE | DATE           | REVISIONS |
|------------------|------------|------------------------------------|----------|----------------|-----------|
| 24-107 / 1637-24 |            |                                    |          | SEPTEMBRE 2024 |           |
| 05               | 2024-09-04 | DÉFINITIVES POUR SOUMISSION        |          |                |           |
| 04               | 2024-08-21 | DÉFINITIVES 100% POUR APPROBATION  |          |                |           |
| 03               | 2024-08-03 | DÉFINITIVES 80% POUR APPROBATION   |          |                |           |
| 02               | 2024-05-14 | DÉFINITIVES 60% POUR APPROBATION   |          |                |           |
| 01               | 2024-02-27 | PRÉLIMINAIRES 30% POUR APPROBATION |          |                |           |

| DESSIN                                      | PROJET                                                         | PROPRIÉTAIRE |
|---------------------------------------------|----------------------------------------------------------------|--------------|
| DÉTAIL EN PLAN<br>DÉMOLITION / CONSTRUCTION | HÔPITAL DE CHANDLER,<br>Chandler<br>(Réfection de l'enveloppe) | Santé Québec |

NE DOIT PAS SERVIR À L'EXÉCUTION

Le présent document est émis pour la seule fin identifiée. Son contenu est protégé par les droits d'auteur et toute reproduction ou modification, partielle ou totale, est interdite sans l'autorisation écrite de gagnon, letellier, cyr, ricard, mathieu, proulx, savard consortium d'architectes.