



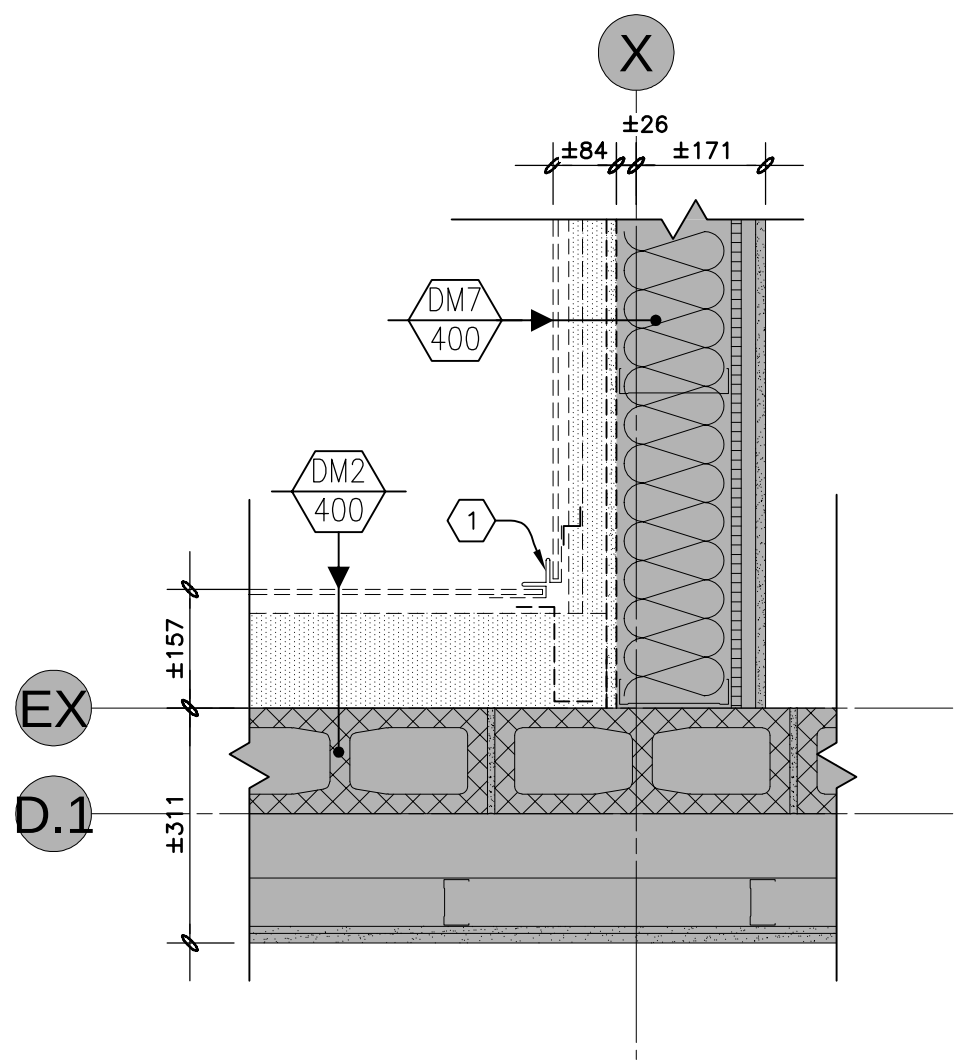


DÉMOLITION

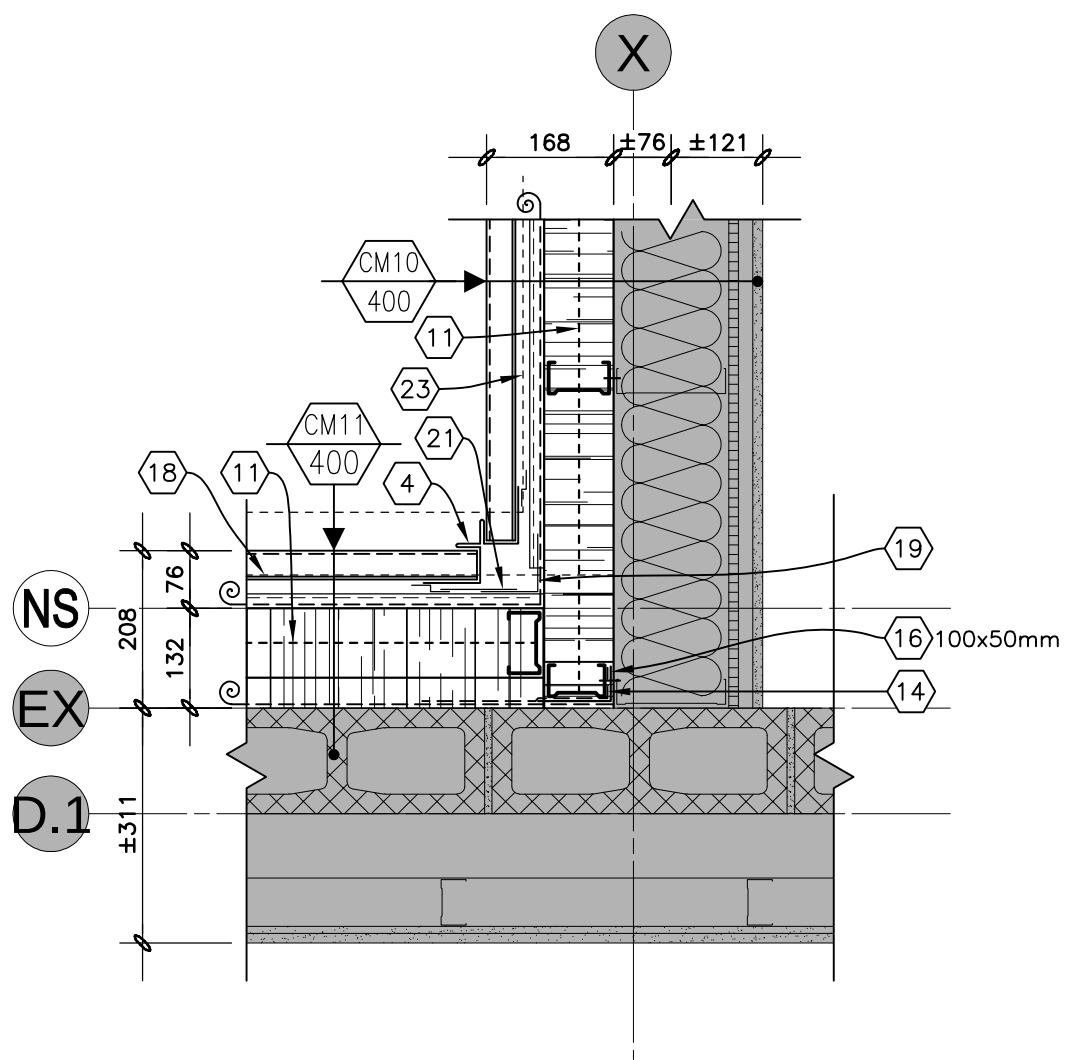


CONSTRUCTION

7 VUE EN PLAN TYPE
051,101 452 1:10mm
DÉTAIL SITUÉ AU-DESSUS DE LA PORTE

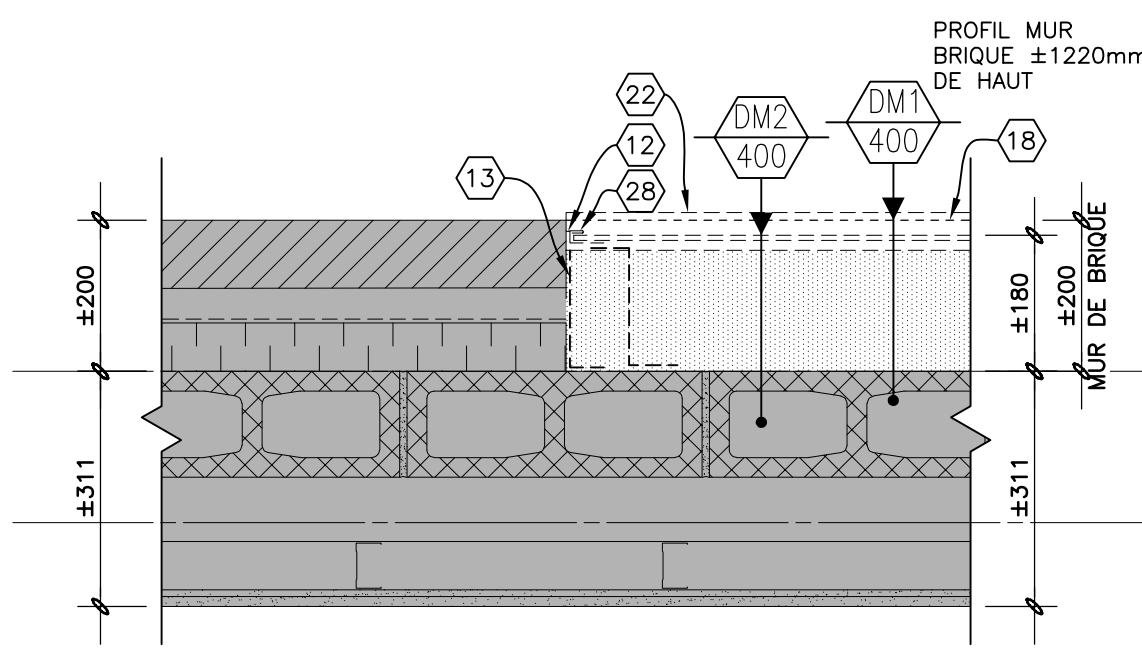


DÉMOLITION

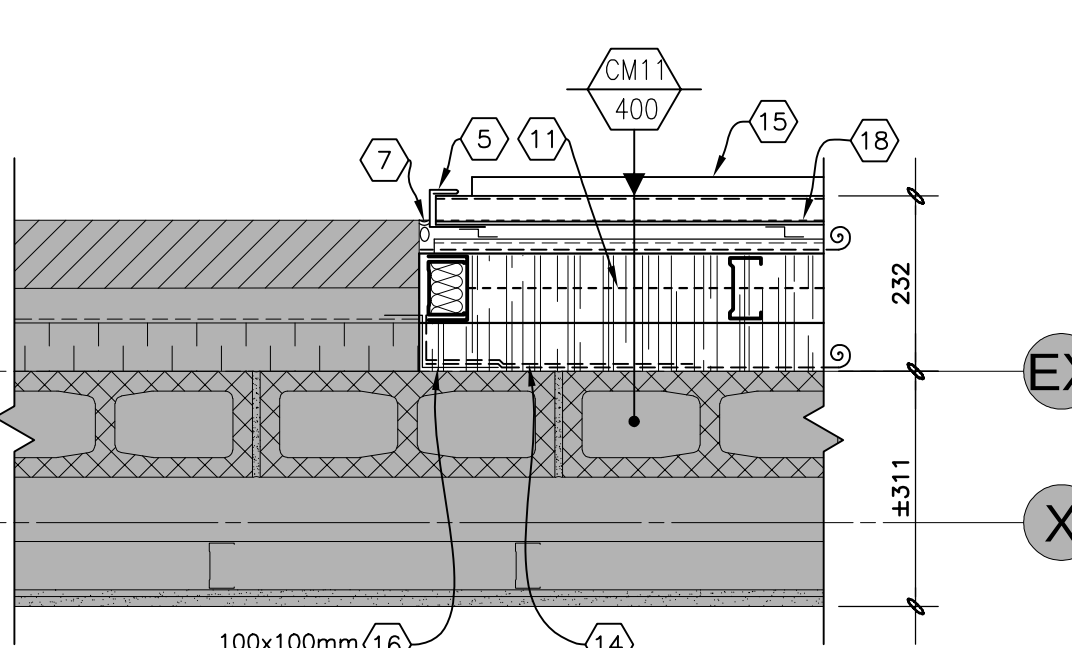


CONSTRUCTION

8 VUE EN PLAN TYPE
051,101 452 1:10mm

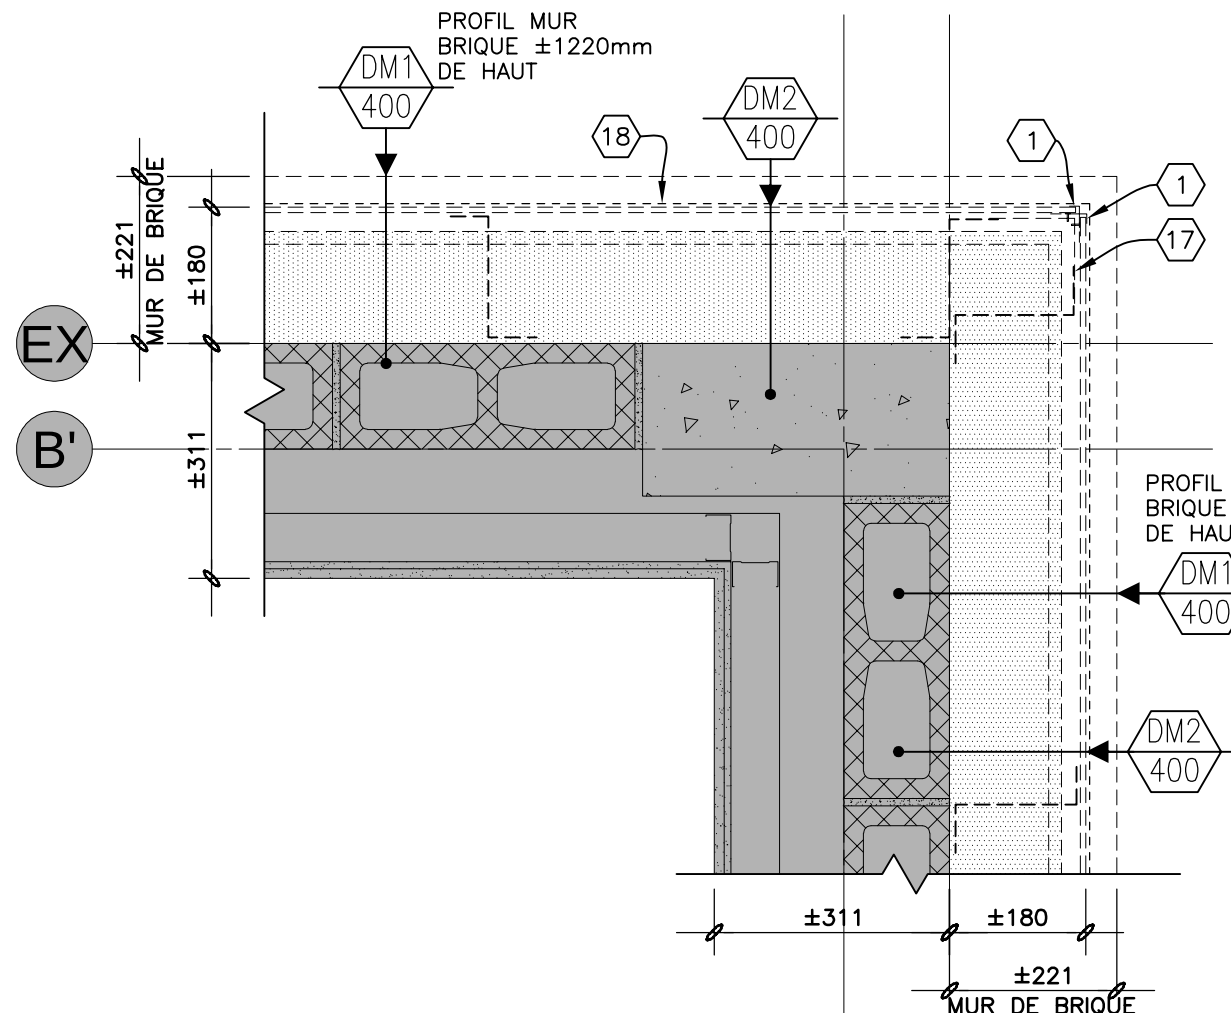


DÉMOLITION

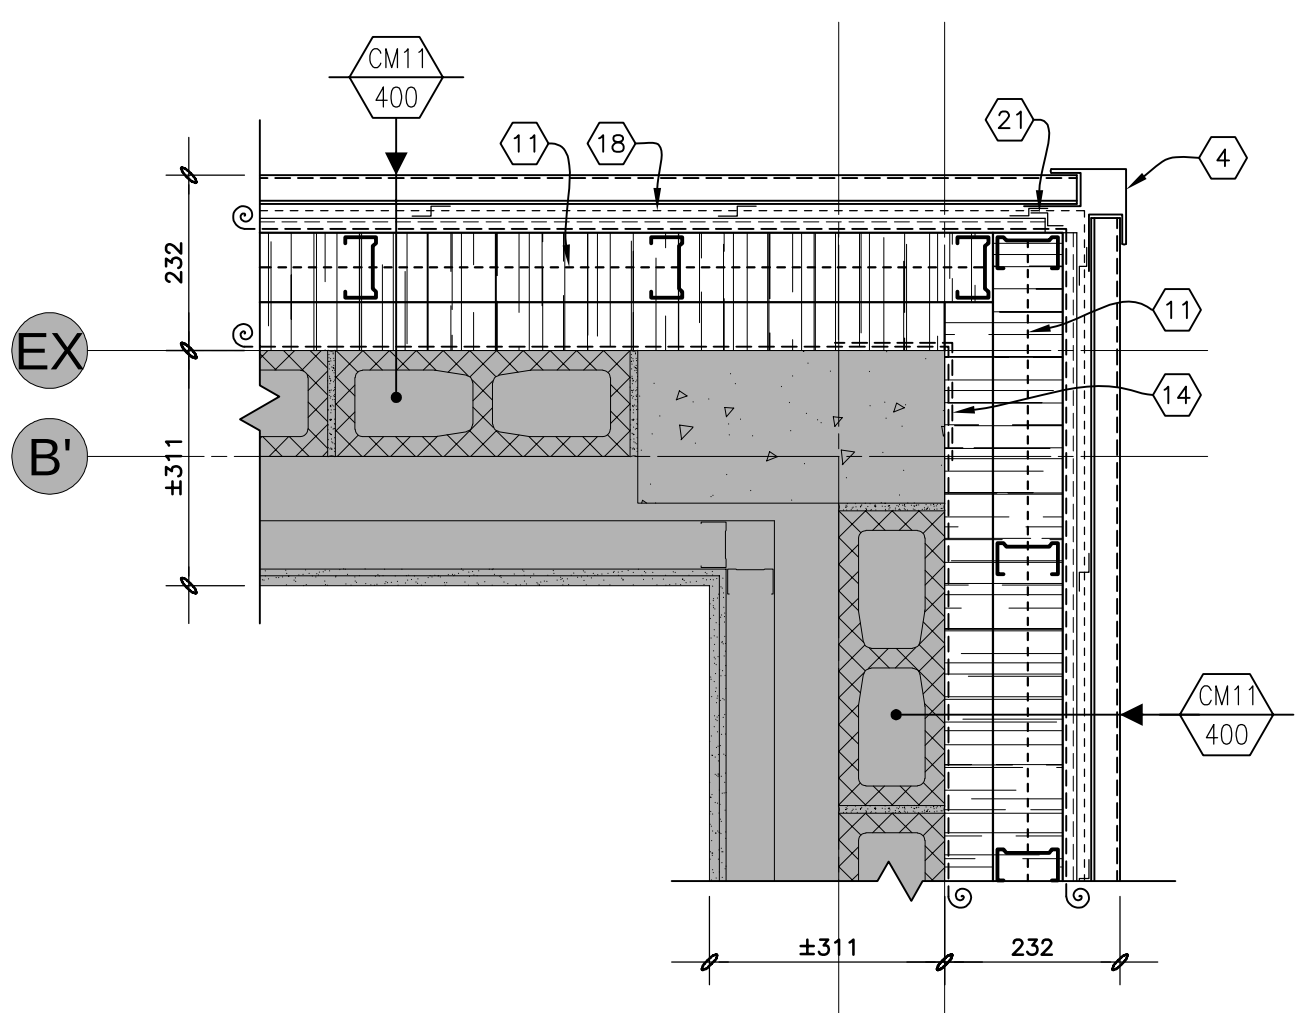


CONSTRUCTION

9 VUE EN PLAN TYPE
051,101 452 1:10mm

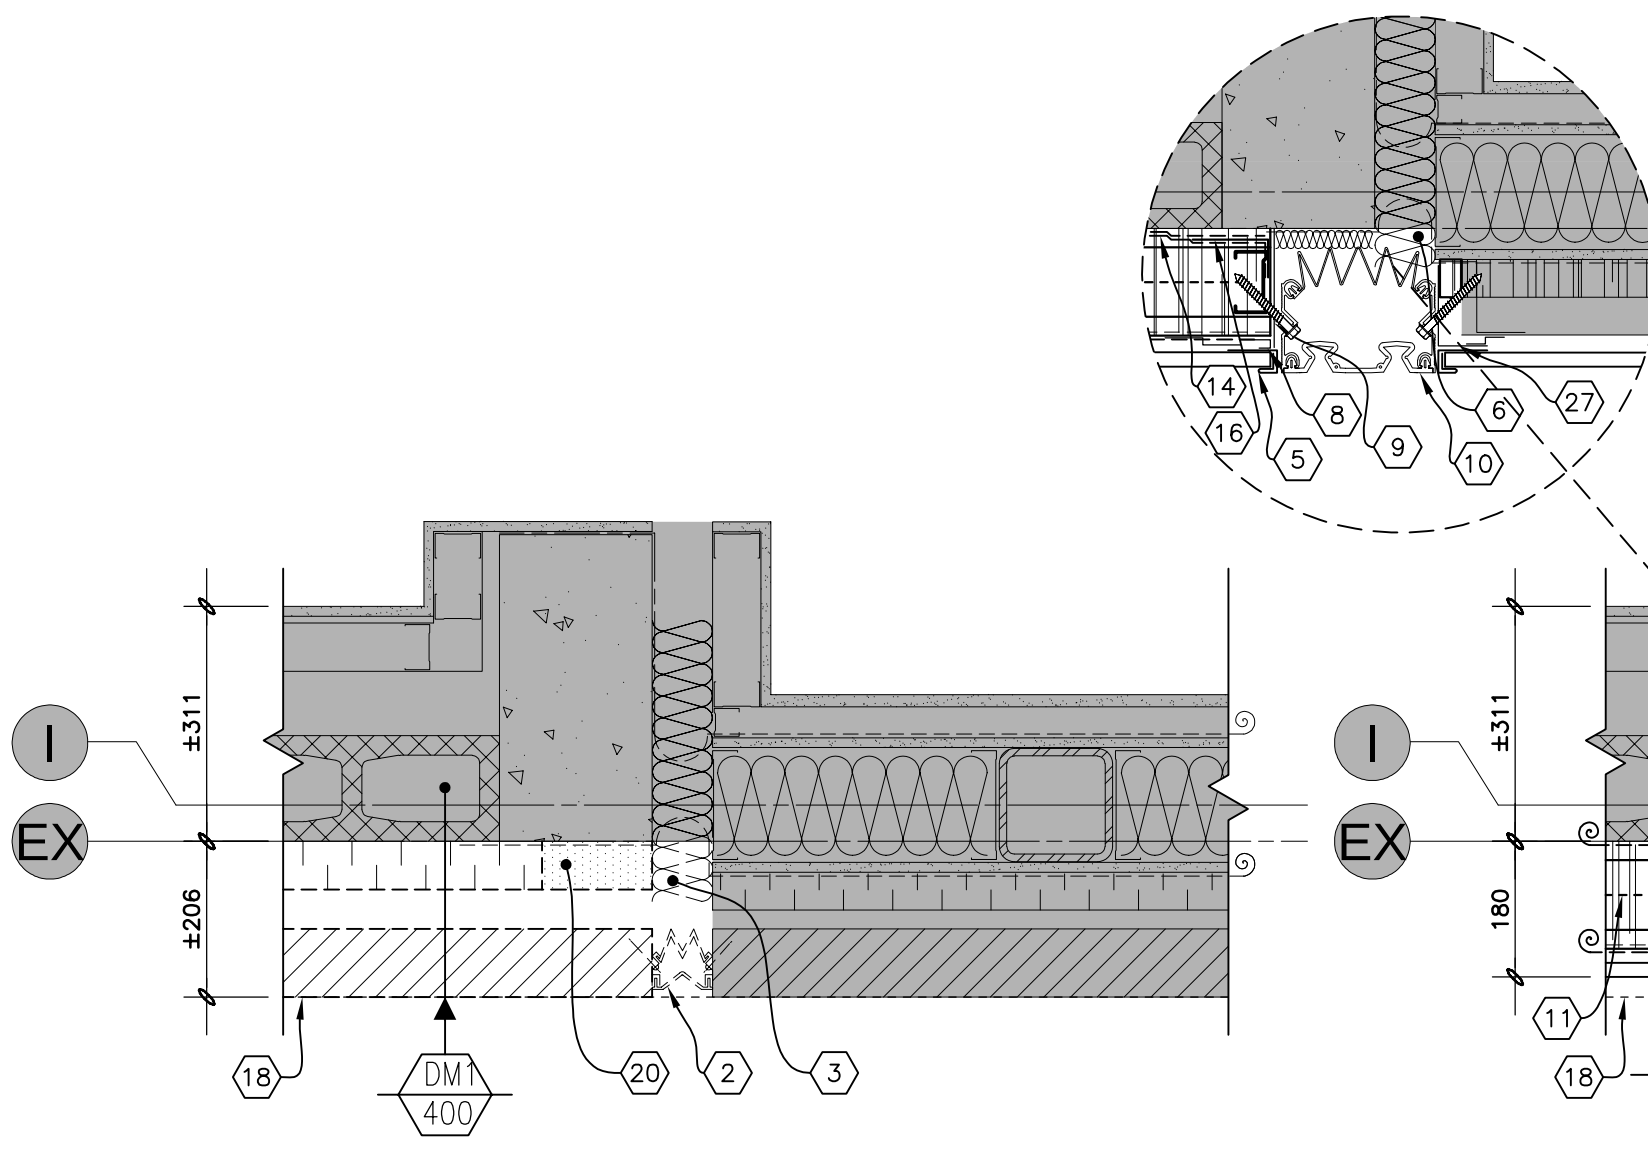


DÉMOLITION

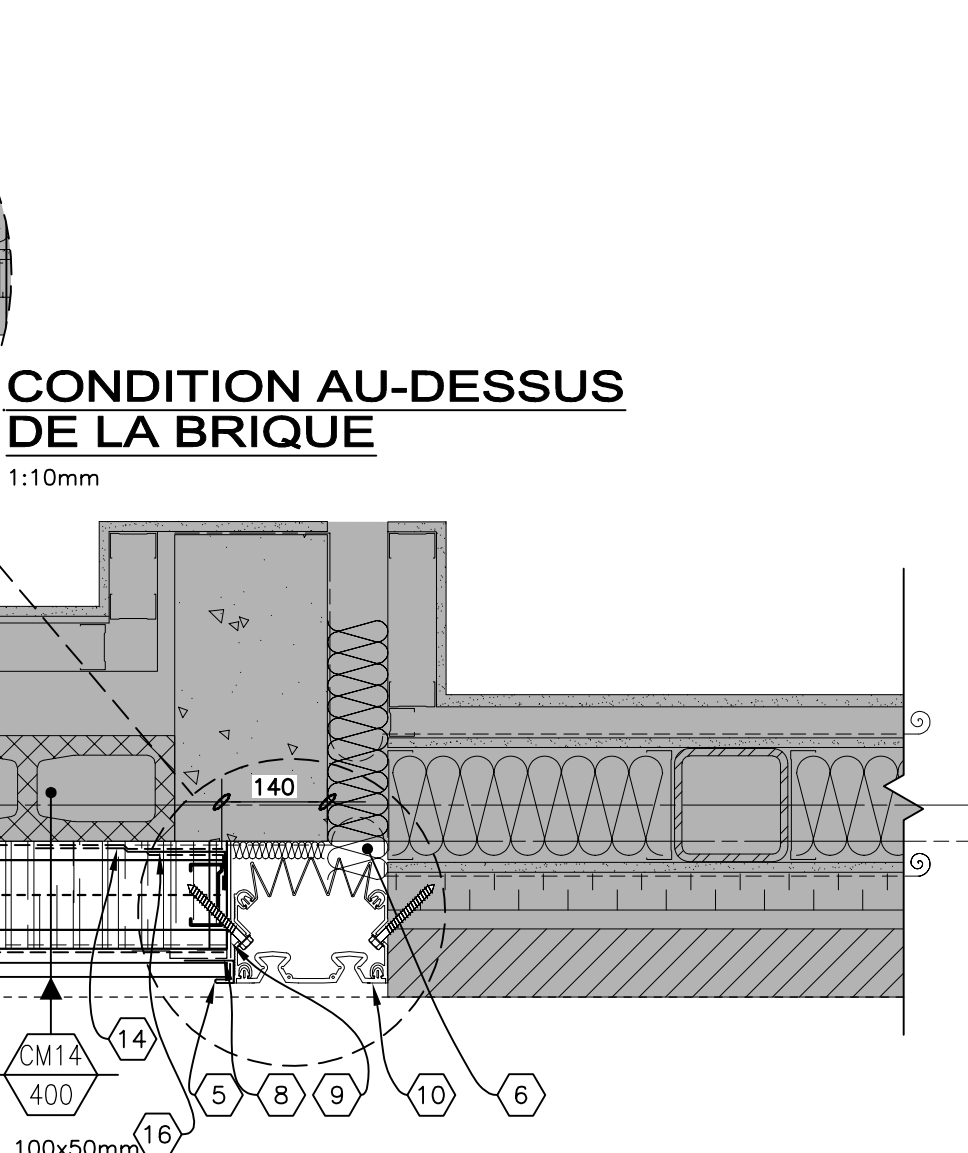


CONSTRUCTION

10 VUE EN PLAN
051,101 452 1:10mm

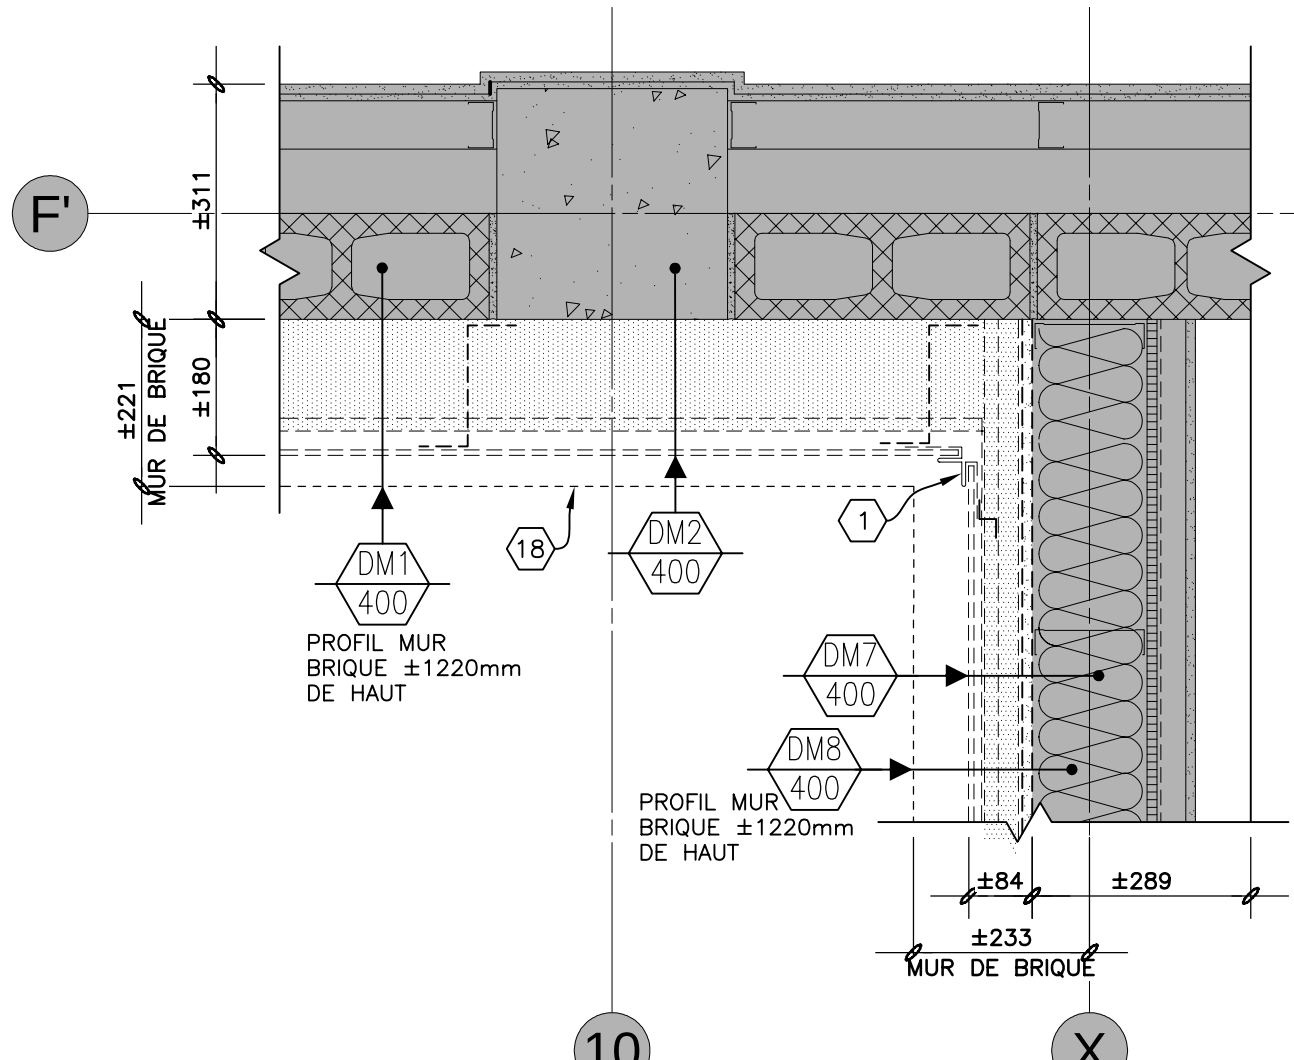


DÉMOLITION

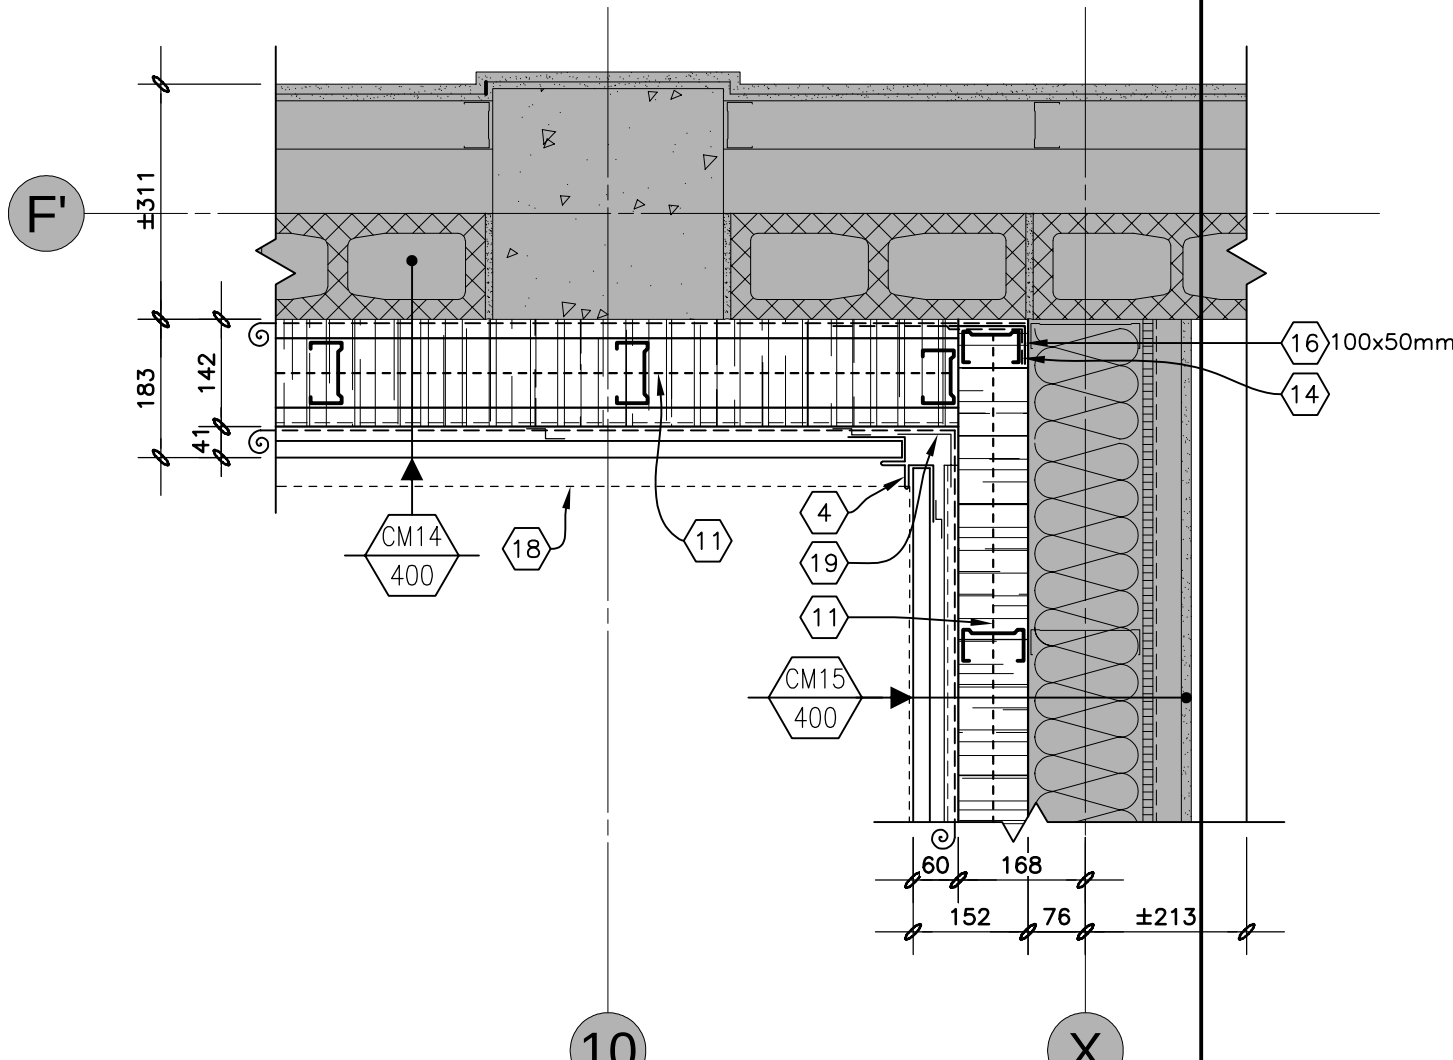


CONSTRUCTION

11 VUE EN PLAN TYPE
051,101 452 1:10mm

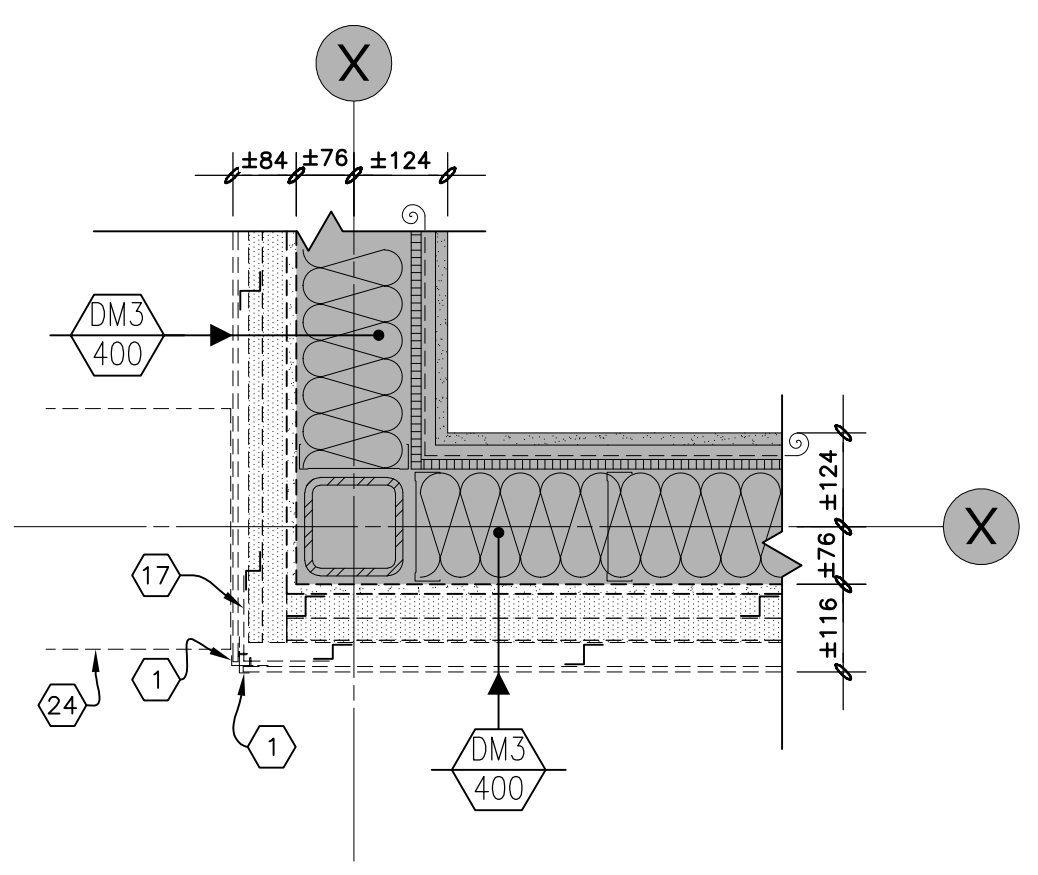

DÉMOLITION

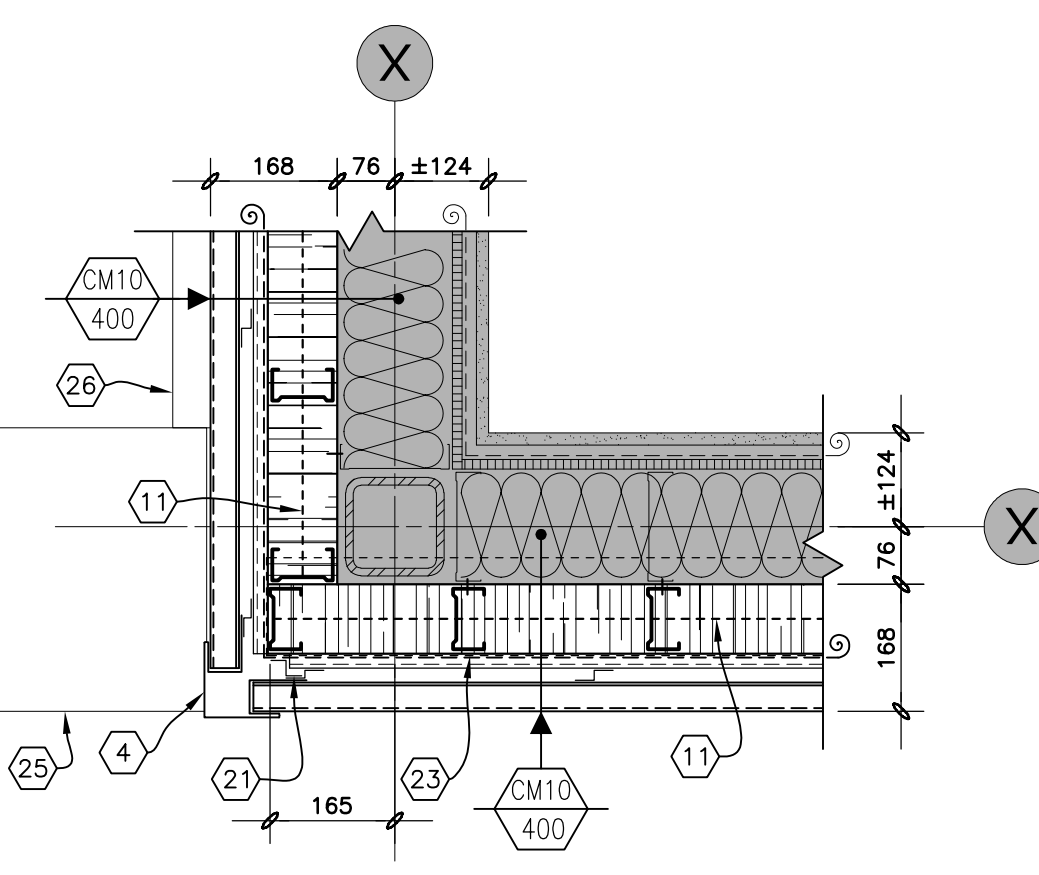

CONSTRUCTION

12 VUE EN PLAN TYPE
052,102 452 1:10mm

NOTES

- 1 MOULURE DE COIN EXISTANTE À DÉMOLIR.
- 2 JOINT D'EXPANSION EXISTANT À DÉMOLIR. PRÉVOIR D'ENLEVER LES ATTACHES UNE PAR UNE POUR ÉVITER DE BRISER LE MORTIER.
- 3 ISOLANT DE LAINE DE FIBRE DE VERRE EXISTANT À DÉMOLIR.
- 4 MOULURE DE COIN DE PAREMENT EN ACIER ÉMAILLÉ, CAL.22.
- 5 MOULURE EN "J" EN ACIER ÉMAILLÉ, CAL.22.
- 6 REMPLIR L'ESPACE D'ISOLANT DE FIBRE DE ROCHE EN MATELAS.
- 7 SCELLANT CONTINUE SUR BOUDIN COMPRESSIBLE 10mm MINIMUM.
- 8 PLIAGE EN ACIER ÉMAILLÉ, CAL.22.
- 9 PLIAGE EN ACIER ÉMAILLÉ, CAL.18.
- 10 NOUVEAU JOINT D'EXPANSION.
- 11 REMPLIR L'ENTREMISE ET LES ESPACES DE PART ET D'AUTRE D'ISOLANT DE FIBRE DE ROCHE FLEXIBLE, VOIR DÉTAIL #8.1 DE LA FEUILLE 411.
- 12 SCELLANT EXISTANT À DÉMOLIR.
- 13 PLIAGE DE TÔLE EN "L" À DÉMOLIR.
- 14 MEMBRANE DE TYPE-1.
- 15 LIMITE DE SOLIN EN-DESSOUS.
- 16 PLIAGE EN ACIER GALVANISÉ EN "L", CAL.18.
- 17 TÔLE DE COIN EXISTANTE À DÉMOLIR.
- 18 PROFIL DE LA FONDATION EXISTANTE.
- 19 PLIAGE EN ACIER GALVANISÉ EN "L" 75x75mm, CAL.18 POUR RELIER LES BARRES "Z".
- 20 ISOLANT DE POLYURÉTHANE GICLÉ À DÉMOLIR.
- 21 TÔLE EN ACIER GALVANISÉ DE COMPARTIMENTATION CONTINU SUR TOUTE LA HAUTEUR DE L'ÉTAGE, CAL.24.
- 22 LIMITE DE SOLIN EN-DESSOUS.
- 23 LIMITE DU LITEAU DE STRUCTURE.
- 24 PROFIL DU PARAPET EXISTANT À DÉMOLIR.
- 25 PROFIL DU NOUVEAU PARAPET.
- 26 PROFIL DU PARAPET INTRAMURAL.
- 27 PLIAGE EN ACIER GALVANISÉ, CAL.16.
- 28 MOULURE EN "J" EXISTANTE À DÉMOLIR.




GLCRM | Proulx Savard |

GLCRM:
128, Avenue de la Cathédrale,
Bureau 201
Rimouski, QC, G5L 5H7
(418) 722-7655



2406, Ch. des Quatres-Bourgeois,
Bureau 100
Québec, QC, G1V 1W5
(418) 647-1700

Proulx Savard Architectes:
75, boul. Arthur-Buies Ouest,
Rimouski QC G5L 5C2
(418) 723-5543

ARCHITECTURE

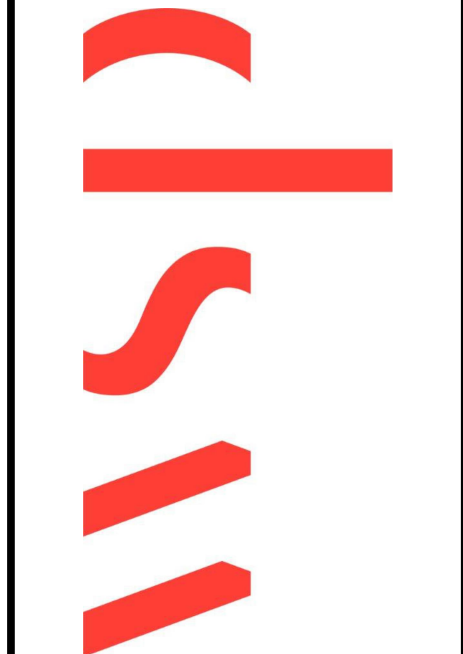


CONSULTANTS

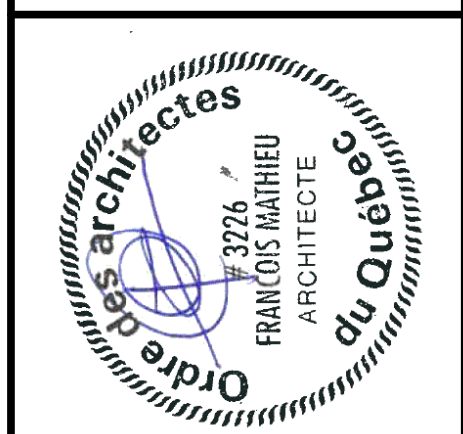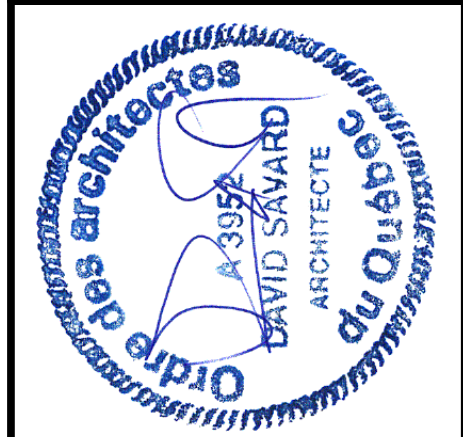

DOSSIER No.	24-107 / 1657-24	DATE	SEPTEMBRE 2024	REVISIONS
DESSINATEUR (S)	A.C.	ÉCHELLE	INDIQUÉE	No
PROJET HÔPITAL DE CHANDLER, Chandler (Réfection de l'enveloppe)	05	2024-09-04	DÉFINITIVES POUR SOUMISSION	DATE
			DÉFINITIVES 100% POUR APPROBATION	
			DÉFINITIVES 80% POUR APPROBATION	
			DÉFINITIVES 60% POUR APPROBATION	
			DÉFINITIVES 50% POUR APPROBATION	
PROPRIÉTAIRE Santé Québec	06	2024-09-04	DÉFINITIVES POUR SOUMISSION	DATE
			DÉFINITIVES 100% POUR APPROBATION	
			DÉFINITIVES 80% POUR APPROBATION	
			DÉFINITIVES 60% POUR APPROBATION	
			DÉFINITIVES 50% POUR APPROBATION	


NE DOIT PAS SERVIR À L'EXÉCUTION

Le présent document est émis pour la seule fin identifiée. Son contenu est protégé par les droits d'auteur et toute reproduction ou modification, partielle ou totale, est interdite sans l'autorisation écrite de gagnon, letellier, cyr, ricard, mathieu, proulx, savard consortium d'architectes.

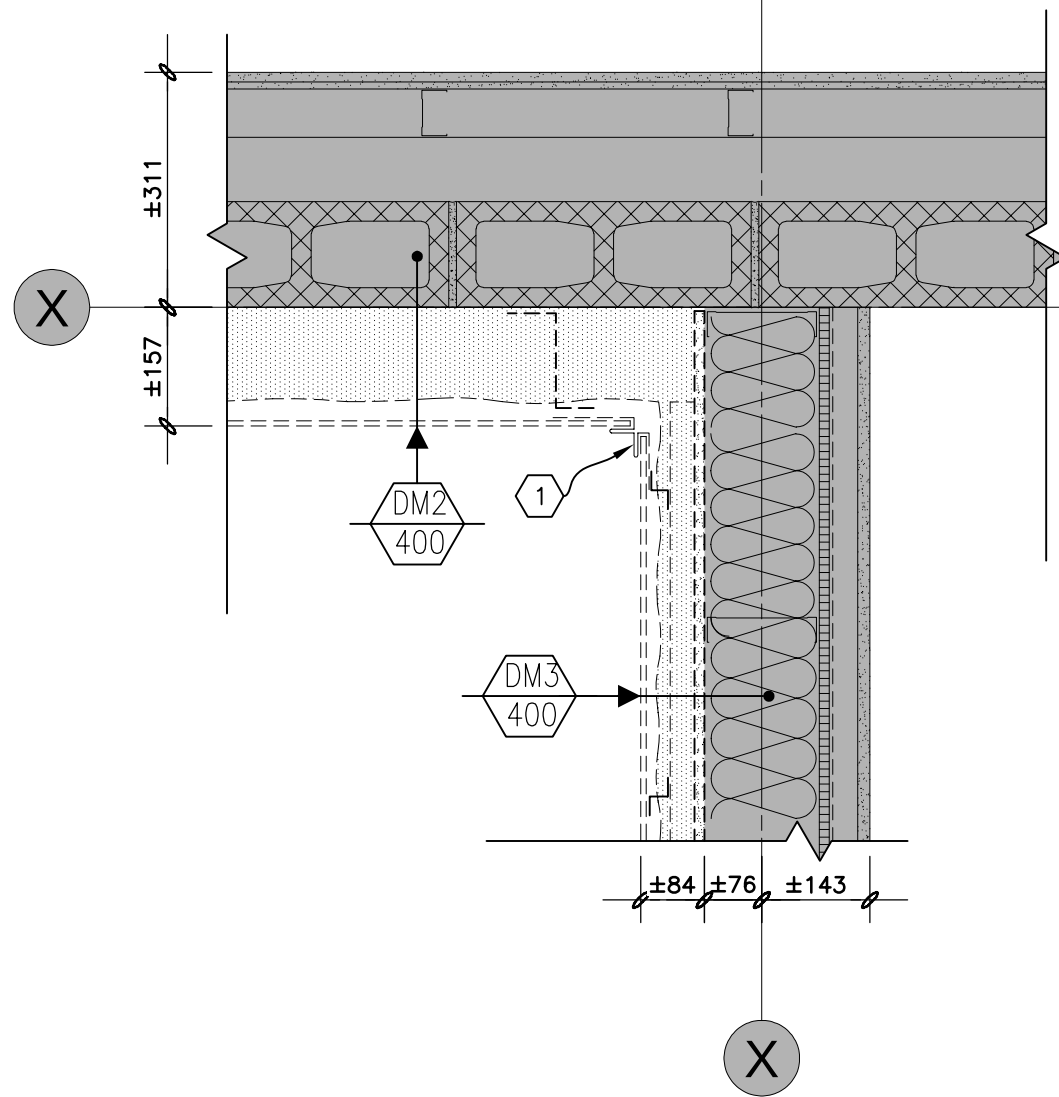


DÉMOLITION

13 VUE EN PLAN TYPE
052,102 453 1:10mm

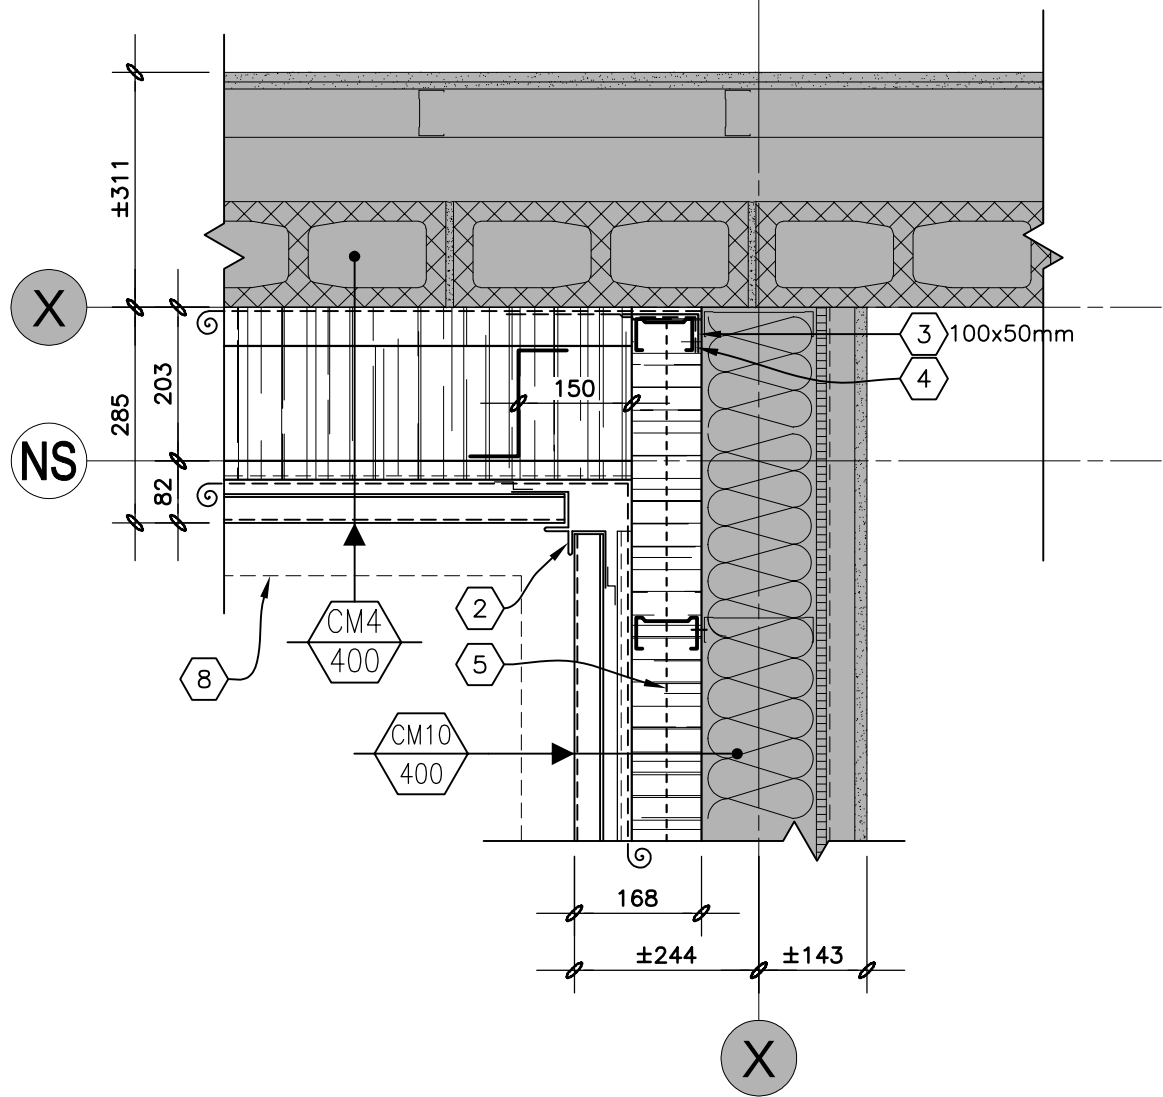


CONSTRUCTION

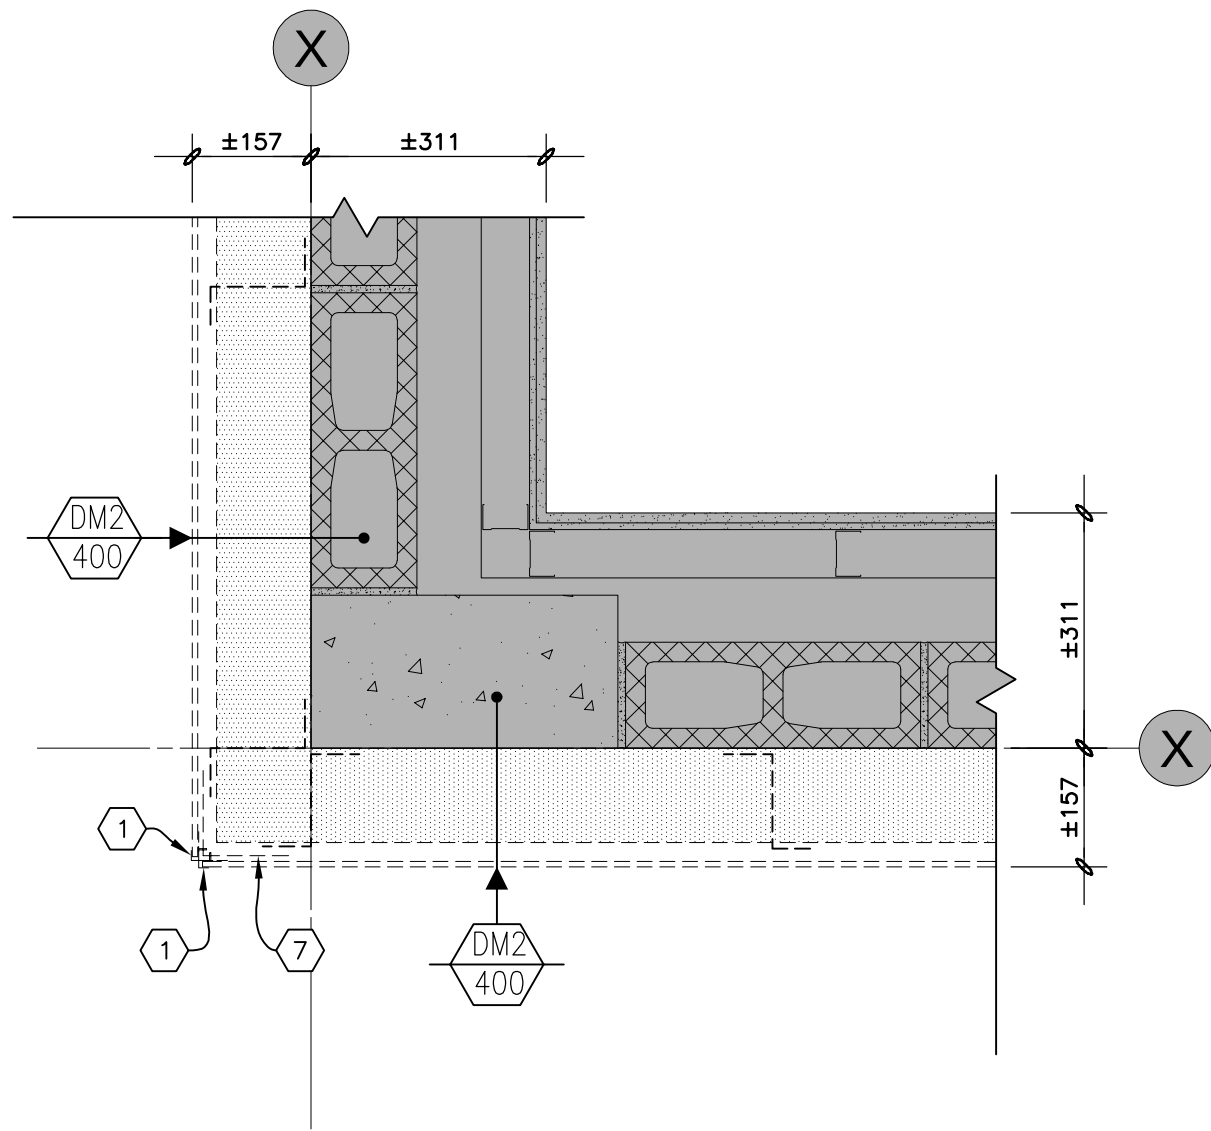


DÉMOLITION

14 VUE EN PLAN TYPE
052,102 453 1:10mm

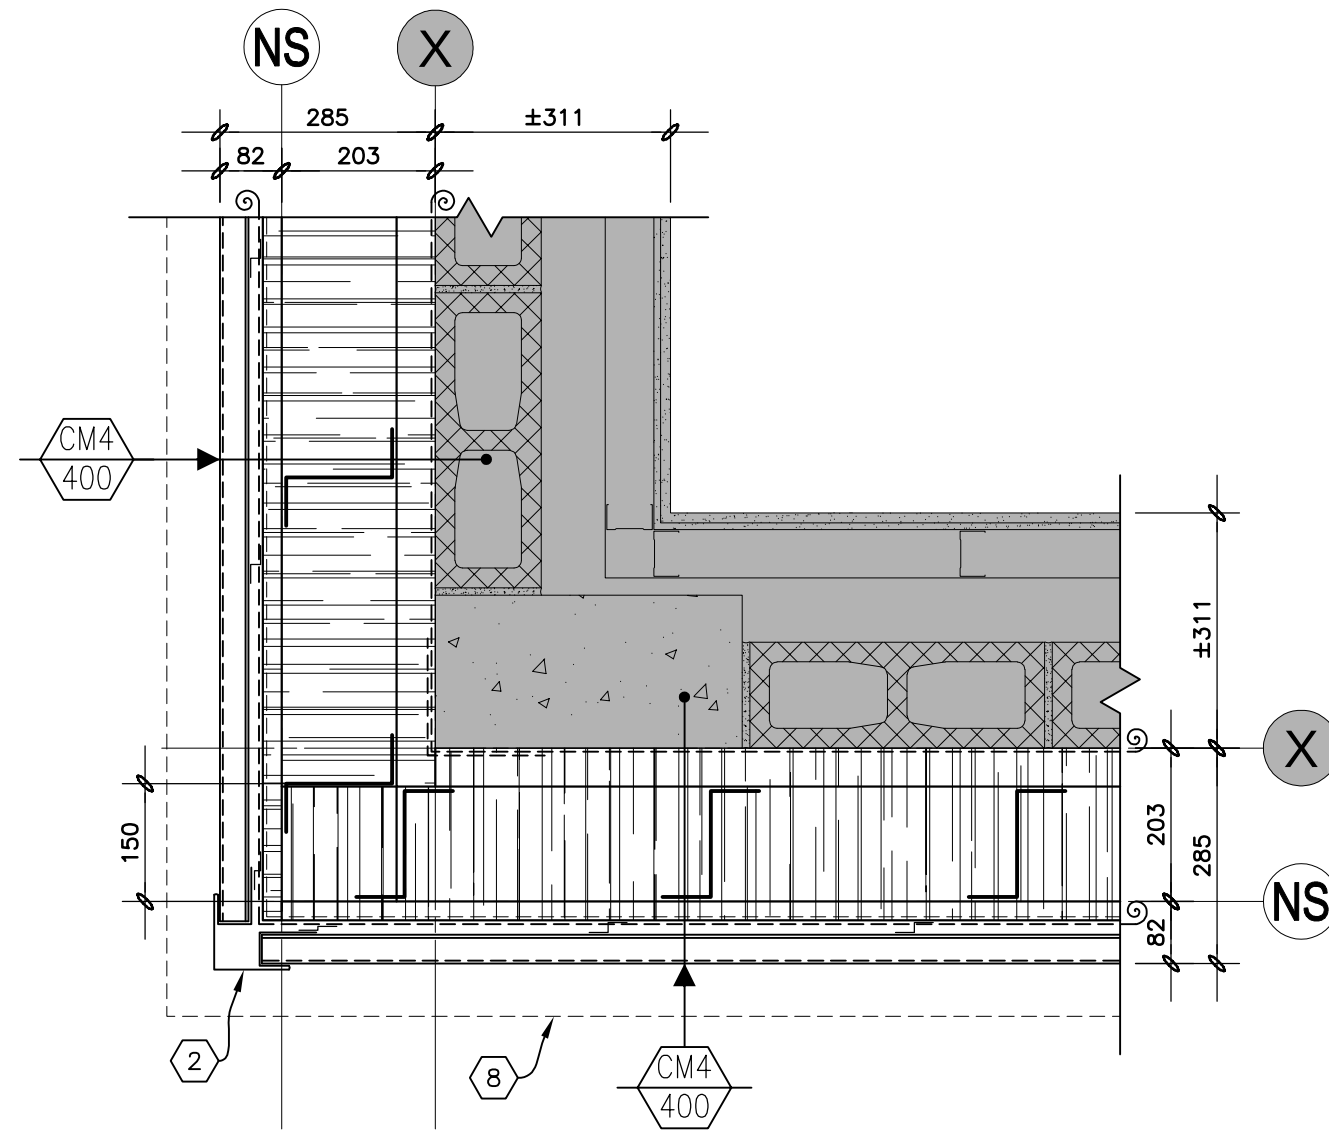


CONSTRUCTION

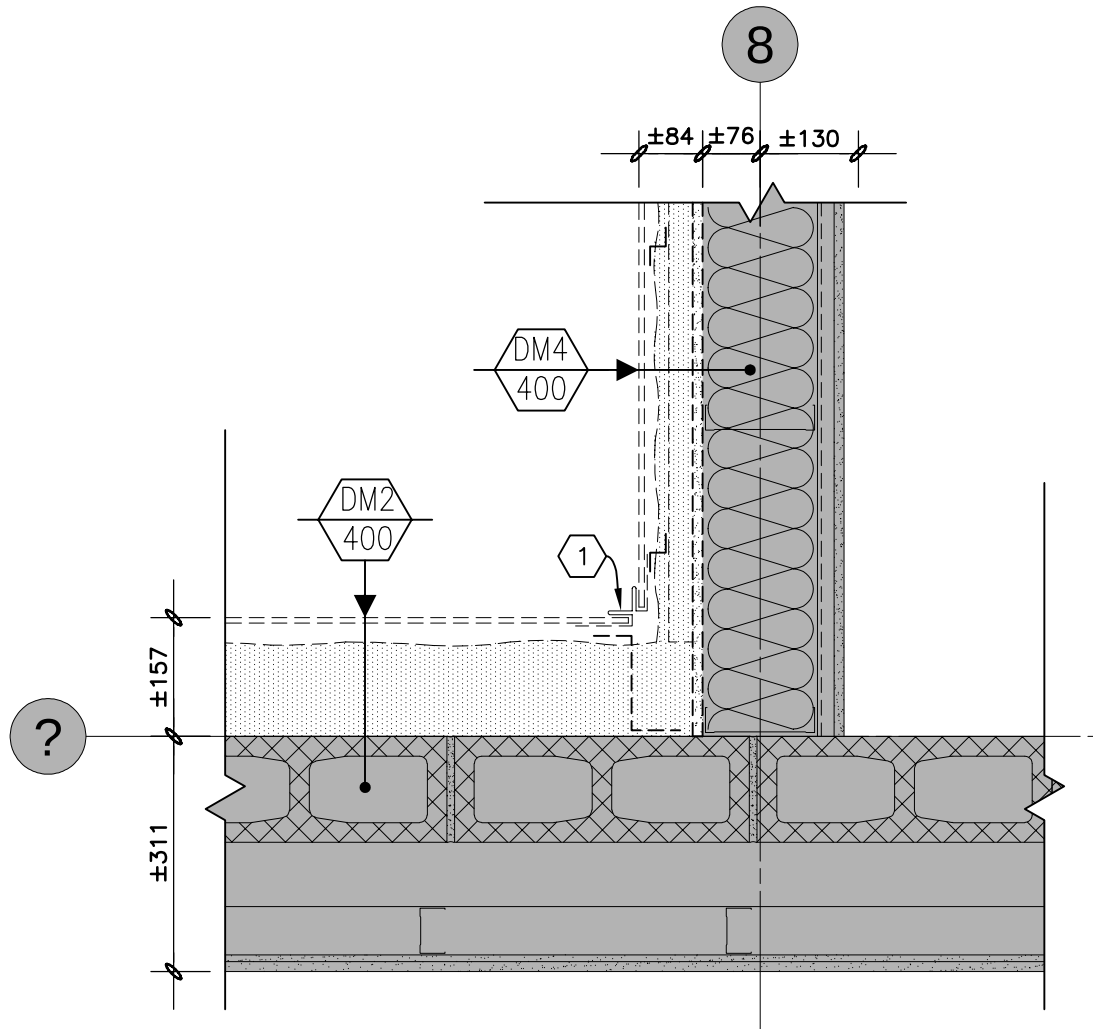


DÉMOLITION

15 VUE EN PLAN TYPE
052,102 453 1:10mm

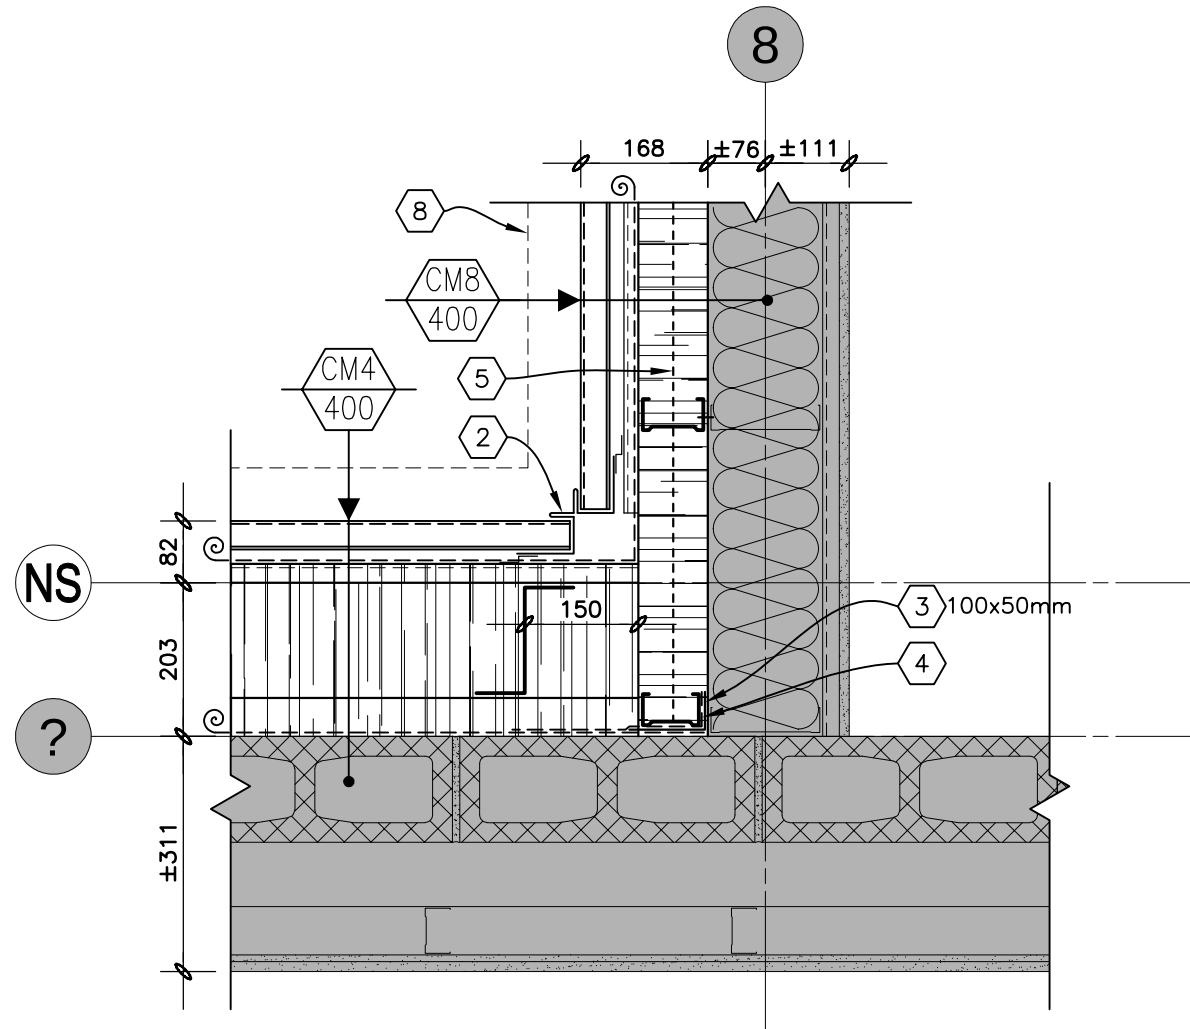


CONSTRUCTION

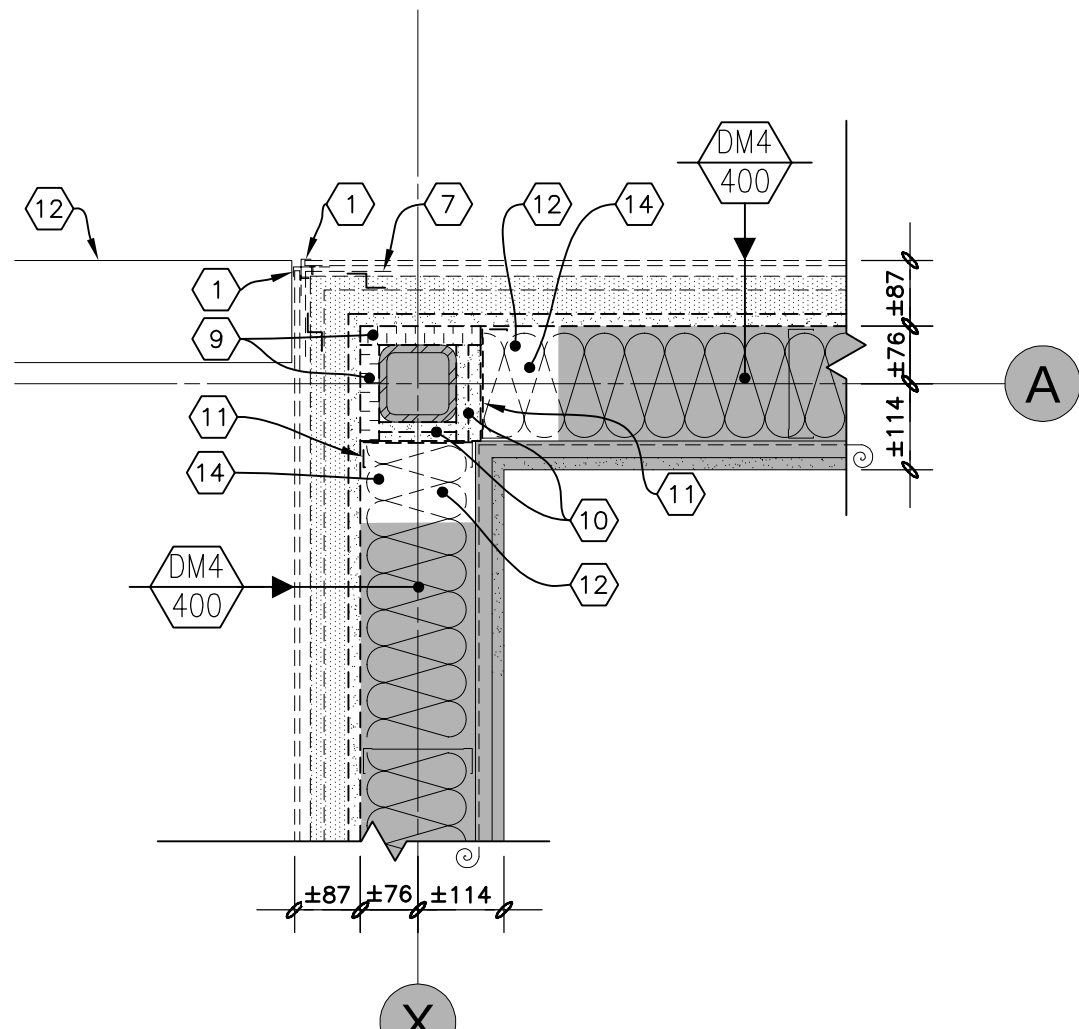


DÉMOLITION

16 VUE EN PLAN TYPE
052,102 453 1:10mm

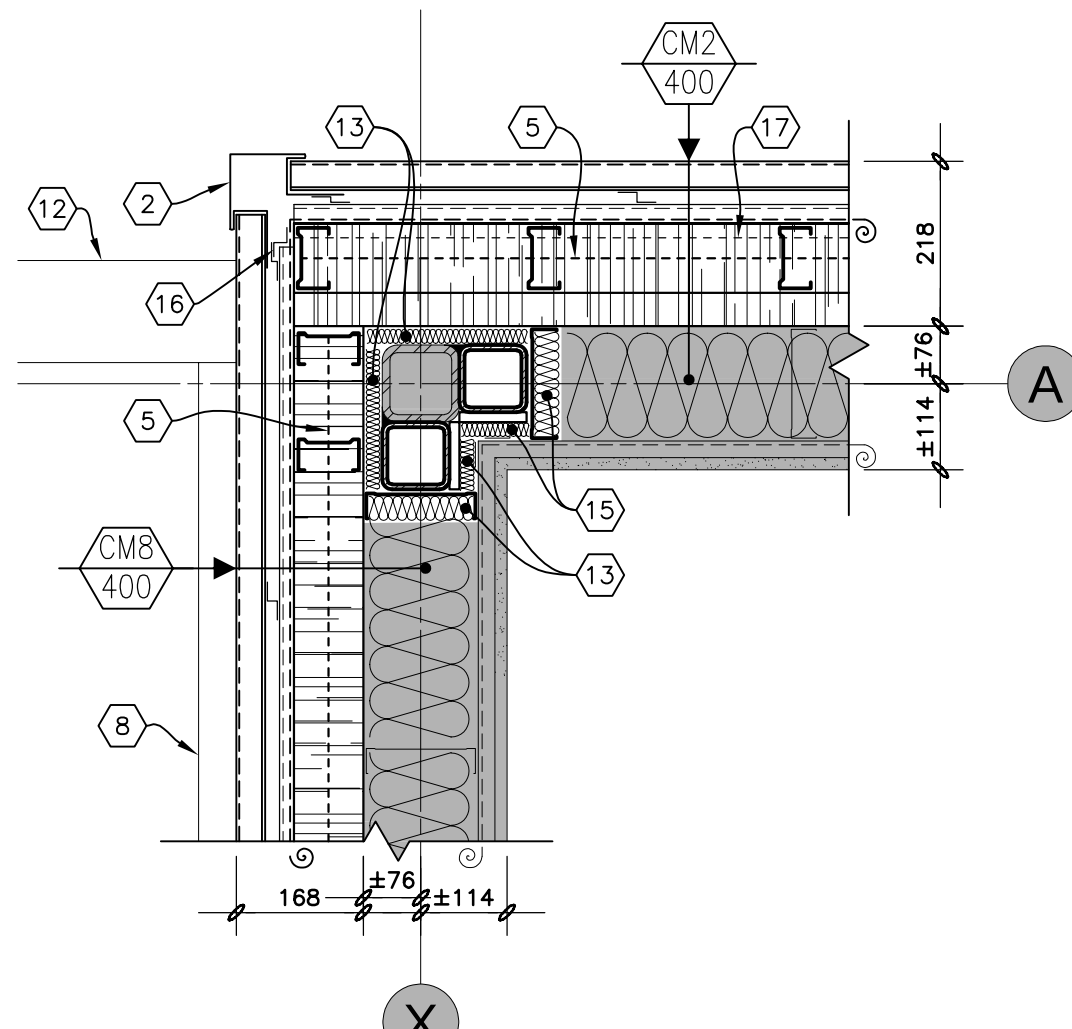


CONSTRUCTION

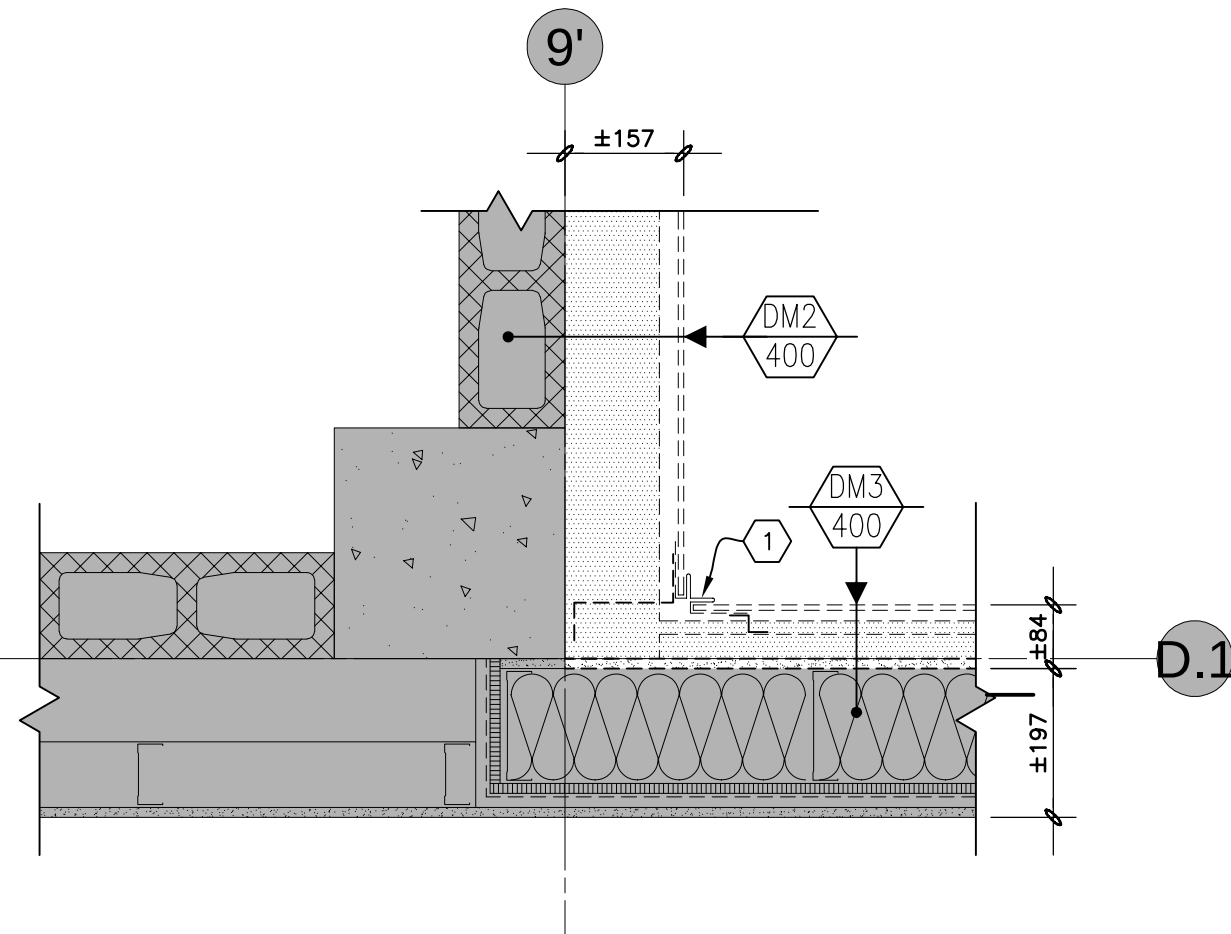


DÉMOLITION

17 VUE EN PLAN TYPE
052,102 453 1:10mm

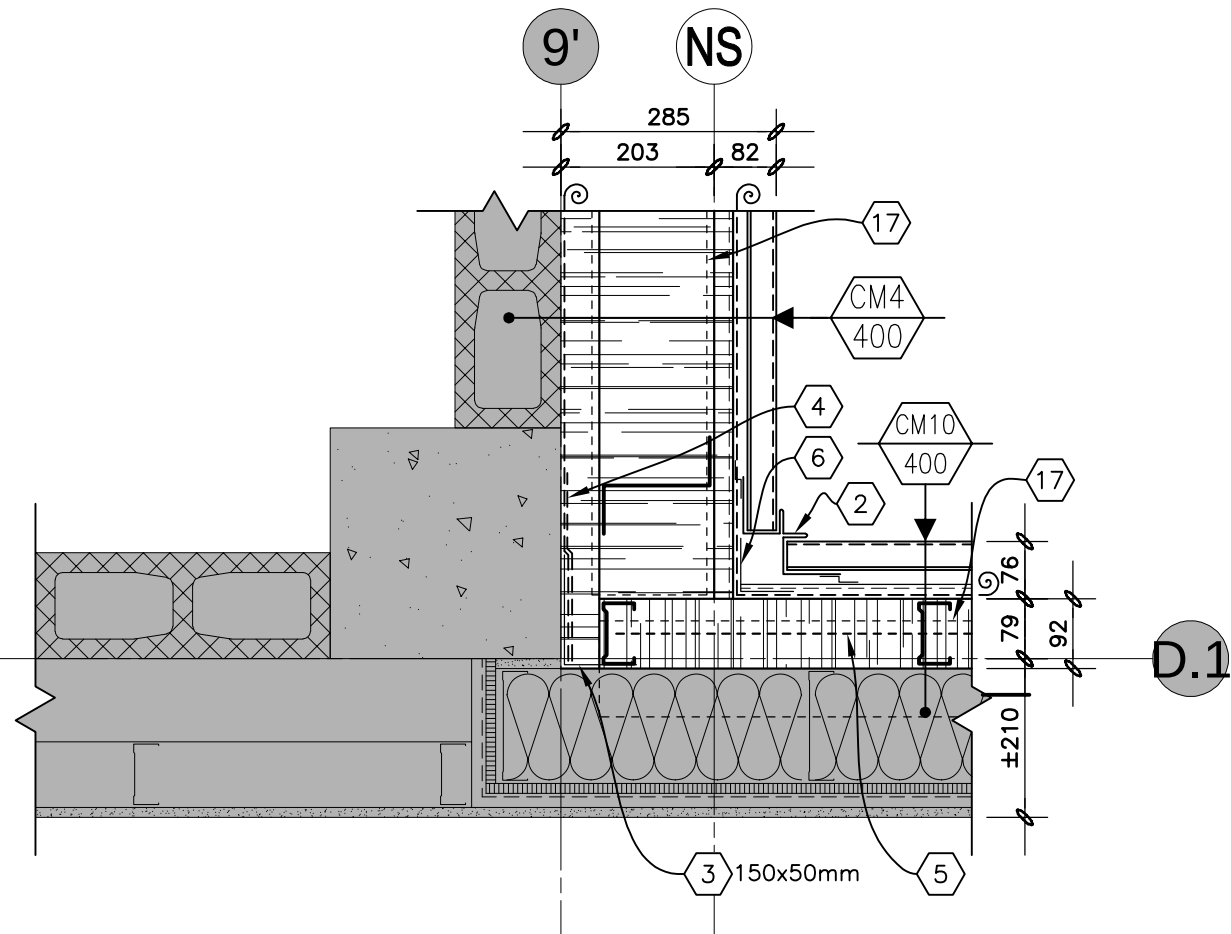


CONSTRUCTION

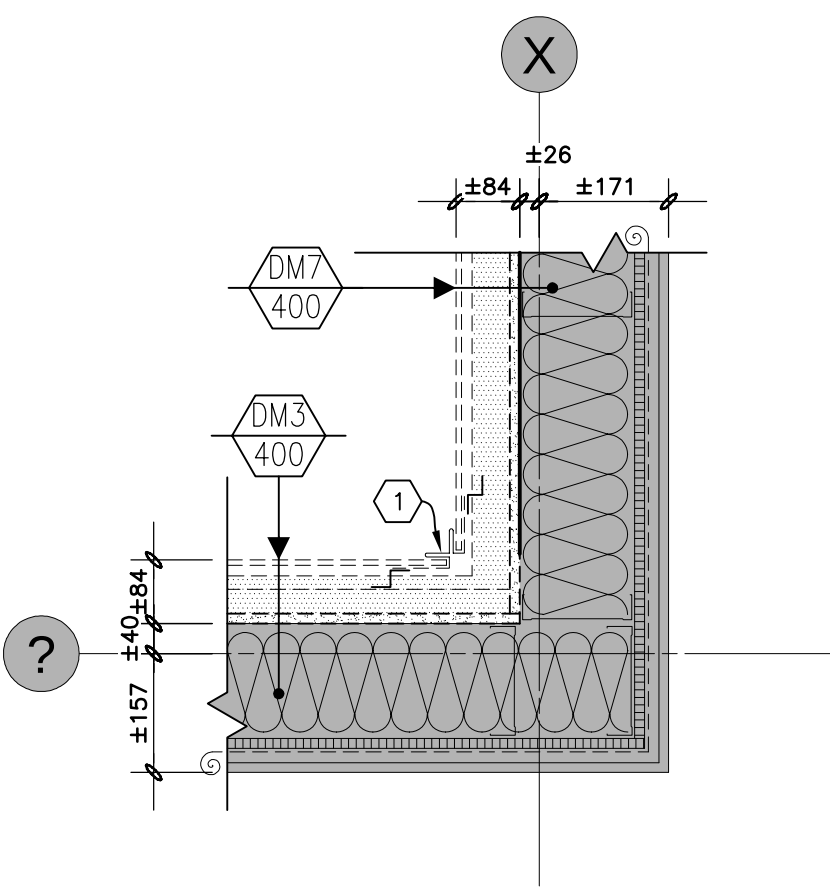

DÉMOLITION

18 VUE EN PLAN TYPE
052,102 453 1:10mm

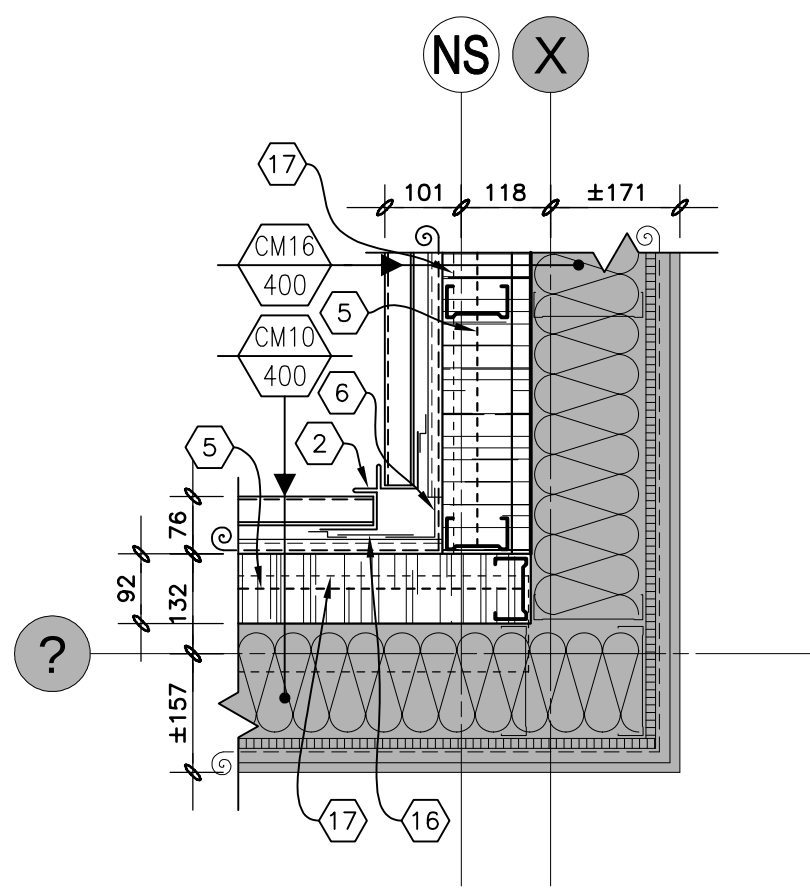

CONSTRUCTION

NOTES

- 1 MOULURE DE COIN EXISTANTE À DÉMOLIR.
- 2 MOULURE DE COIN DE PAREMENT EN ACIER ÉMAILLÉ, CAL.22.
- 3 PLIAGE EN ACIER GALVANISÉ EN "L", CAL.18.
- 4 MEMBRANE DE TYPE-1.
- 5 REMPLIR L'ENTREMISE ET LES ESPACES DE PART ET D'AUTRE D'ISOLANT DE FIBRE DE ROCHE FLEXIBLE, VOIR DÉTAIL #5.1 DE LA FEUILLE 411.
- 6 PLIAGE EN ACIER GALVANISÉ EN "L" 75x75mm, CAL.18 POUR RELIER LES BARRES "Z".
- 7 TOLE DE COIN À DÉMOLIR.
- 8 PROFIL DU PARAPET INTRAMURAL.
- 9 ISOLANT RIGIDE À DÉMOLIR.
- 10 DEUX (2) RANGS DE GYPSE À DÉMOLIR.
- 11 COUPER LES COLOMBAGES EXISTANTS AFIN DE NE CONSERVER EN PLACE QUE LES AILETTES INTÉRIEURES.
- 12 PROFIL DU PARAPET EXISTANT.
- 13 ISOLANT DE FIBRE DE VERRE À DÉMOLIR.
- 14 LISSES ET SABLIERES À COUPER DE CHAQUE CÔTÉ DES AILETTES INTÉRIEURES.
- 15 REMPLIR LES CAVITÉS D'ISOLANT DE LAINE DE FIBRE DE ROCHE.
- 16 PLIAGE EN ACIER GALVANISÉ DE COMPARTIMENTATION CONTINU SUR TOUTE LA HAUTEUR DE L'ÉTAGE, CAL.24.
- 17 LIMITE DU LITEAU DE STRUCTURE.




GLCRM | Proulx Savard |

GLCRM:
128, Avenue de la Cathédrale,
Bureau 201
Rimouski, QC, G5L 5H7
(418) 722-7555



2406, Ch. des Quatres-Bourgeois,
Bureau 100
Québec, QC, G1V 1W5
(418) 647-1700

Proulx Savard Architectes:
75, boul. Arthur-Buies Ouest,
Rimouski QC G5L 5C2
(418) 722-5543

ARCHITECTURE

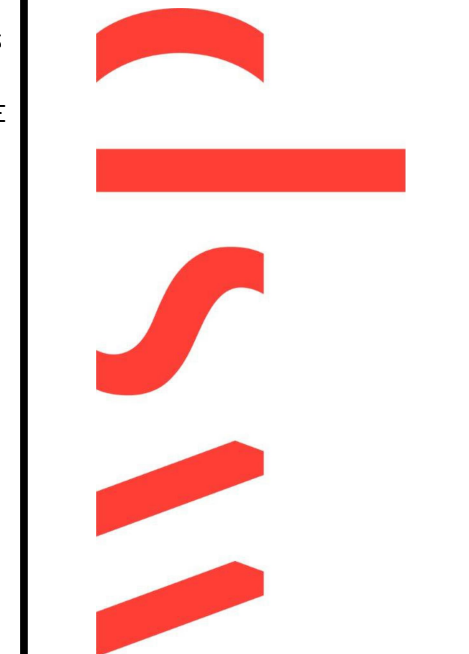

CONSULTANTS


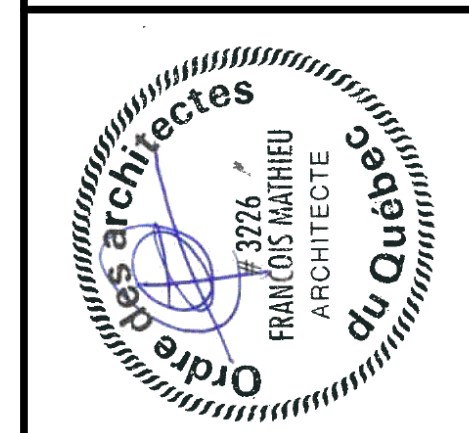
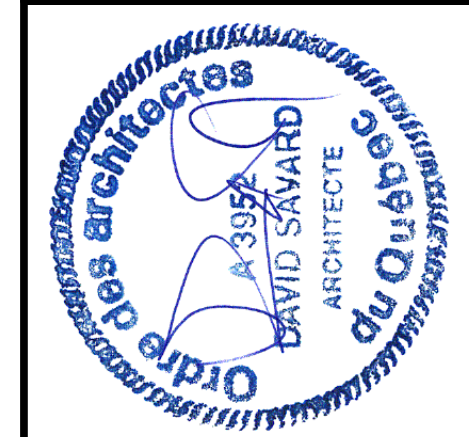


DESIGNATEUR (S)	AC.	ÉCHELLE	INDIQUÉE	DOSSIER No.		DATE	REVISIONS
				24-1087 / 1657-24	DATE		
DESIGN	AC.	ÉCHELLE	INDIQUÉE	05	2024-09-04	05	DÉFINITIVES POUR SOUMISSION
				06	2024-08-21	06	DÉFINITIVES 100% POUR APPROBATION
				03	2024-08-03	03	DÉFINITIVES 80% POUR APPROBATION
				02	2024-05-14	02	DÉFINITIVES 40% POUR APPROBATION
				01	2024-02-27	01	PRÉLIMINAIRES 20% POUR APPROBATION


DESIGN	AC.	ÉCHELLE	INDIQUÉE	DATE	REVISIONS				
DESIGN	AC.	ÉCHELLE	INDIQUÉE	DATE	REVISIONS				
PROJET					PROPRIÉTAIRE				
HÔPITAL DE CHANDLER, Chandler (Réfection de l'enveloppe)									
PROPRIÉTAIRE					Santé Québec				

NE DOIT PAS SERVIR À L'EXÉCUTION


Le présent document est émis pour la seule fin identifiée. Son contenu est protégé par les droits d'auteur et toute reproduction ou modification, partielle ou totale, est interdite sans l'autorisation écrite de gagnon, letellier, cyr, ricard, mathieu, proulx, savard consortium d'architectes.

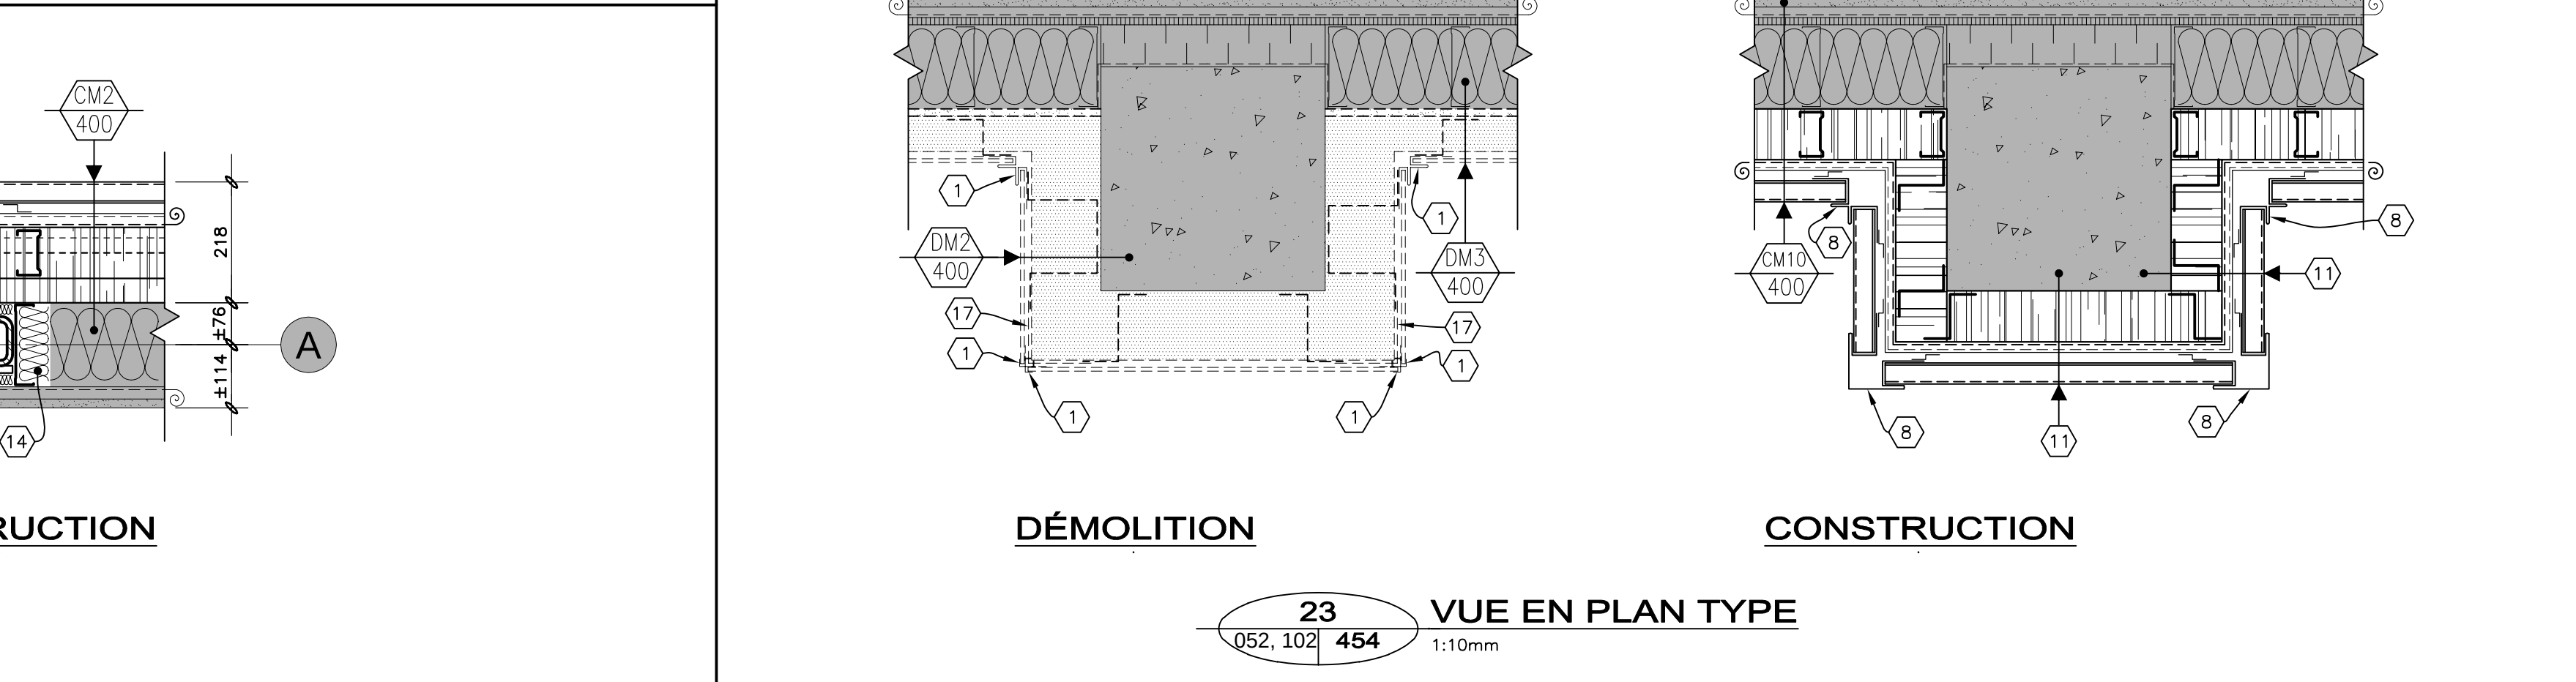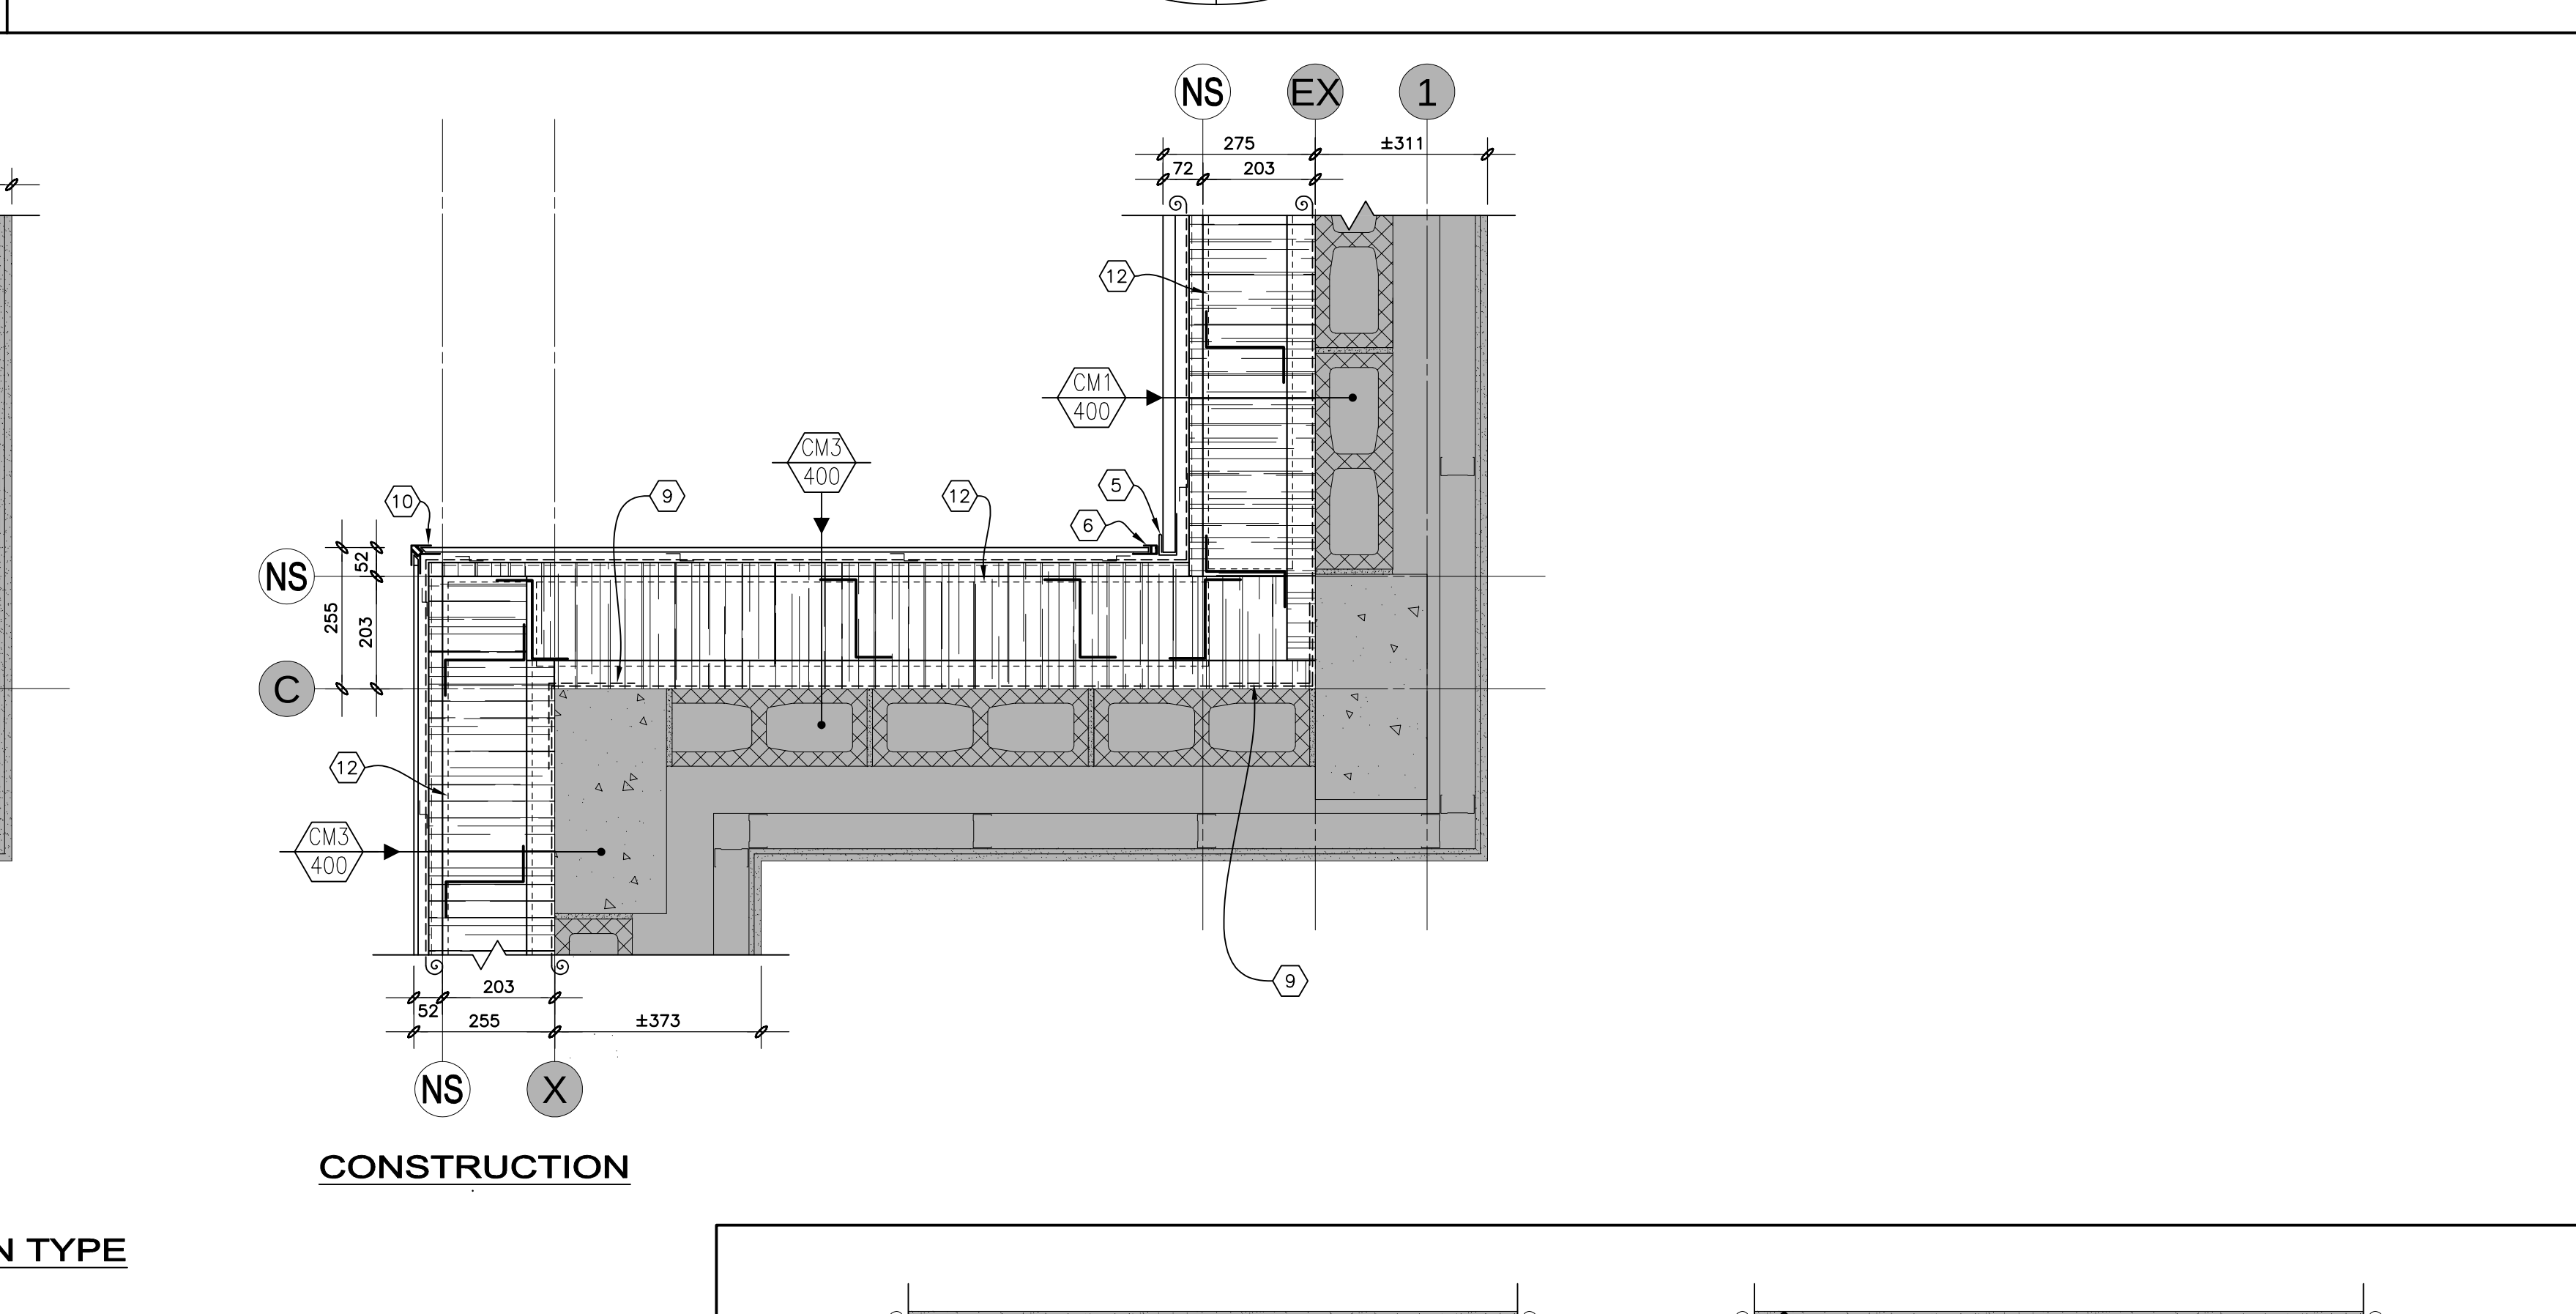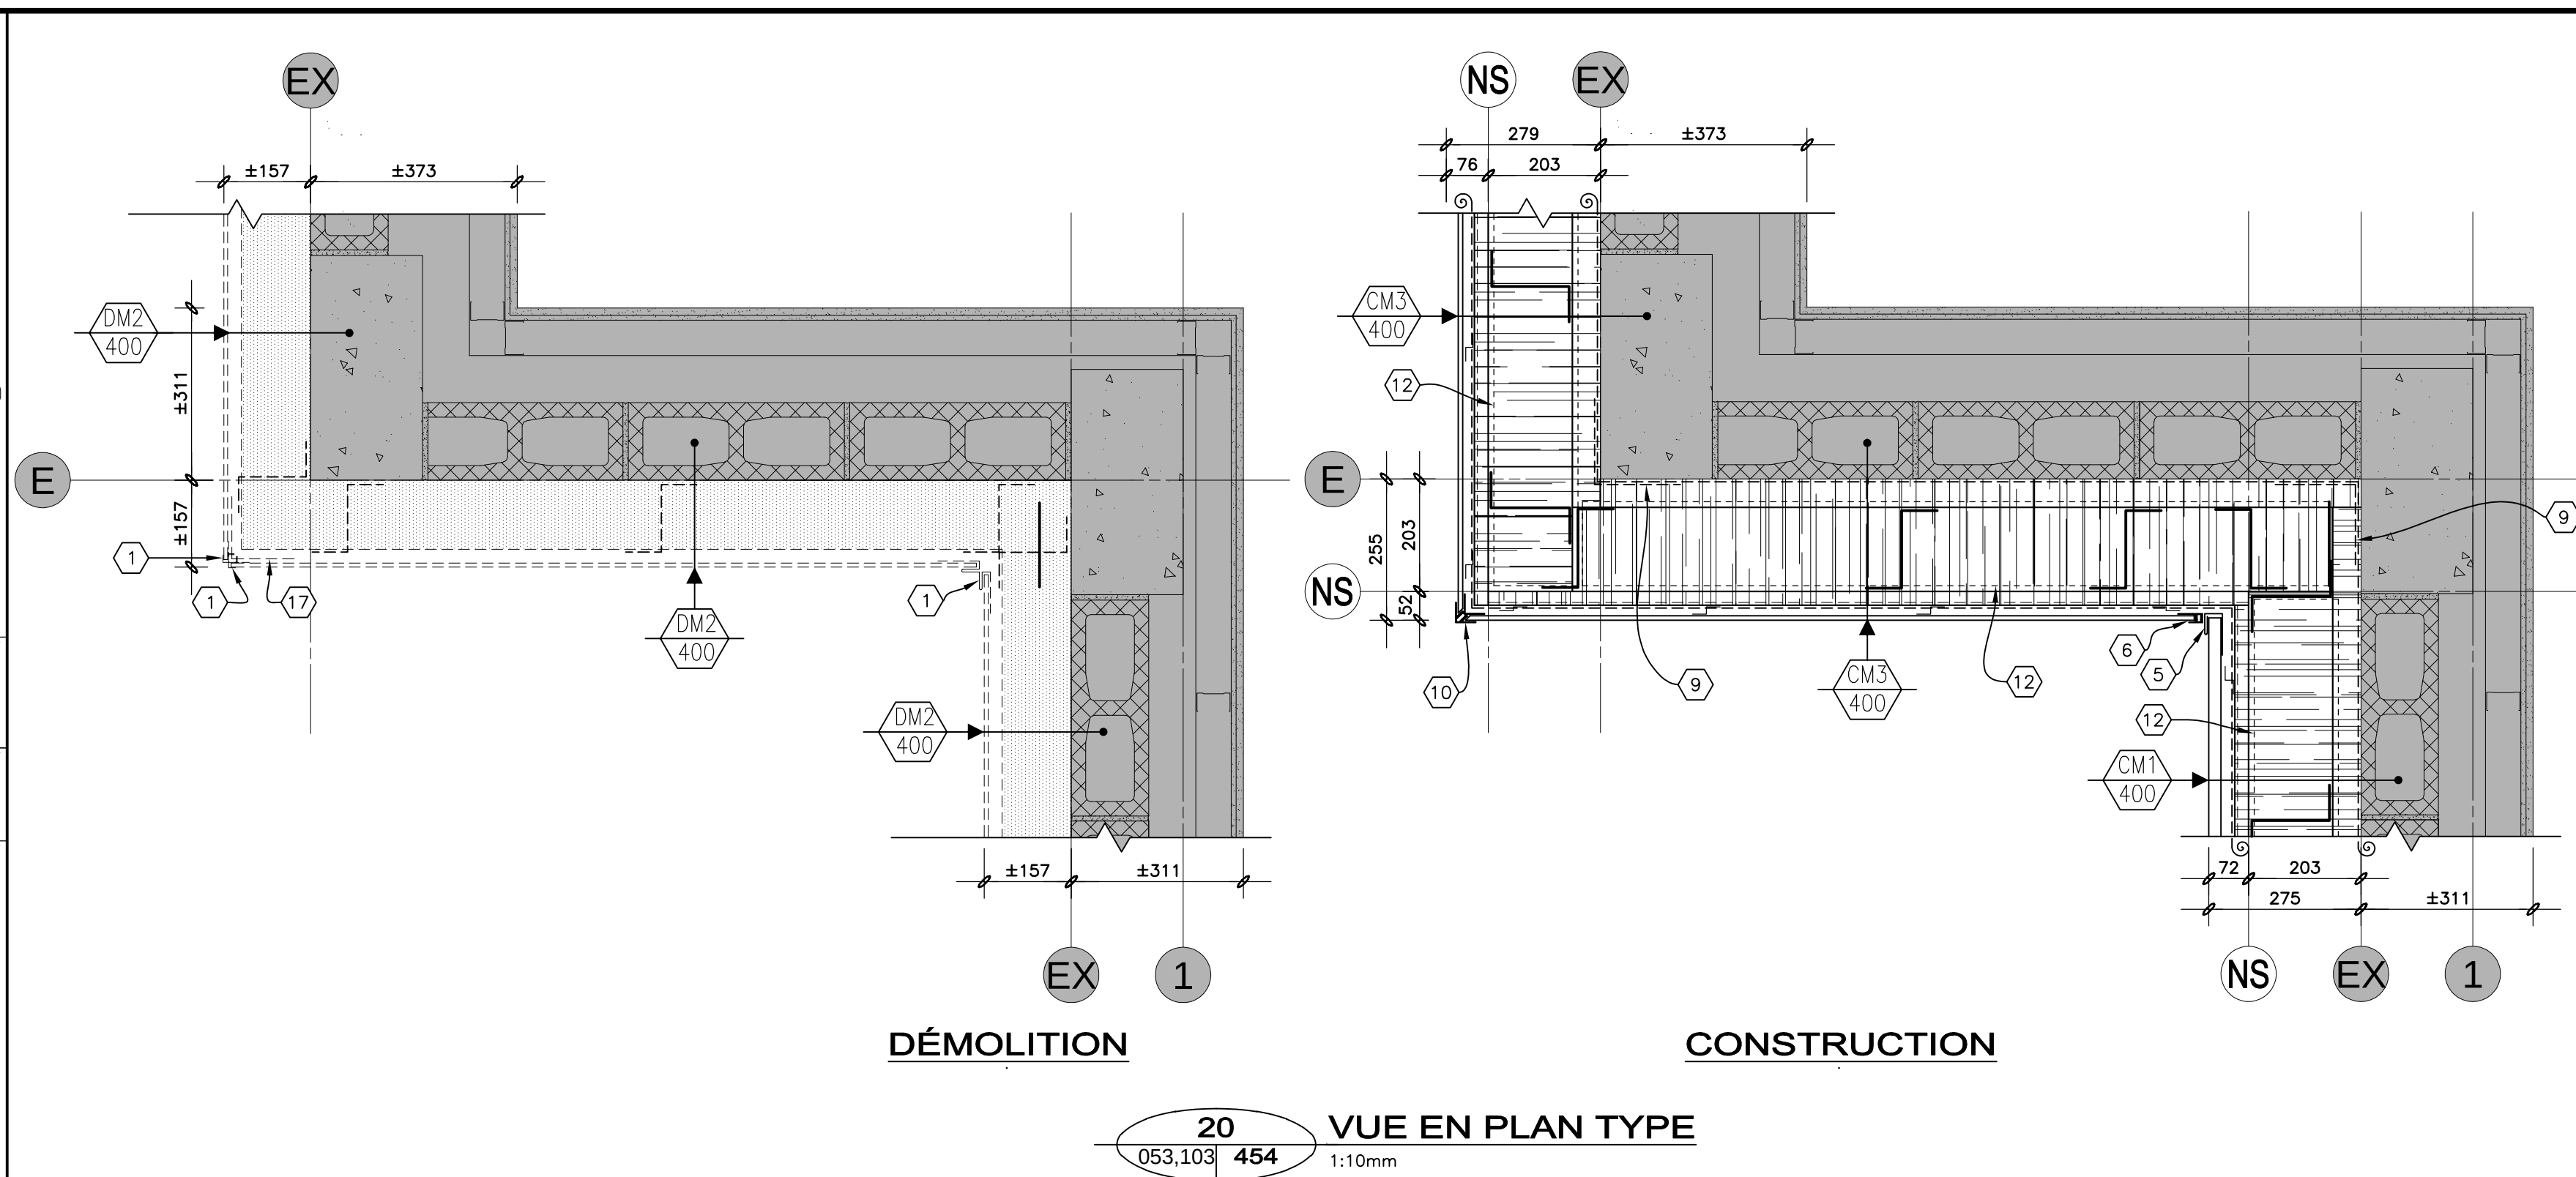


- # NOTES
- 1 MOULURE DE COIN EXISTANTE À DÉMOLIR.
 - 2 MOULURE EN "J" EXISTANTE À DÉMOLIR.
 - 3 PLAGE DE TÔLE EXISTANT À DÉMOLIR.
 - 4 CONDUIT DE MÉCANIQUE EXISTANT À DÉMOLIR, VOIR DOCUMENTS D'INGÉNIERIE.
 - 5 MOULURE EN ACIER ÉMAILLÉ CAL.22.
 - 6 MOULURE EN "J" PAR LE MANUFACTURIER DU PAREMENT DE DÉCLIN D'ALUMINIUM.
 - 7 ISOLANT DE FIBRE DE VERRE À DÉMOLIR.
 - 8 MOULURE DE COIN DE PAREMENT EN ACIER ÉMAILLÉ, CAL.22.
 - 9 MEMBRANE DE TYPE-1.
 - 10 MOULURE DE COIN EXTÉRIEUR PAR LE MANUFACTURIER DU PAREMENT DE DÉCLIN D'ALUMINIUM.
 - 11 NOUVELLE COMPOSITION :
 - PAREMENT D'ACIER, CAL.22, HORIZONTAL;
 - BARRE "Z" 19mm D'ÉPAISSEUR, CAL.16 @ 405mm C/C, VERTICALE;
 - BARRE "Z" 19mm D'ÉPAISSEUR, CAL.16 @ 405mm C/C, HORIZONTALE;
 - MEMBRANE PARE-INTÉMPIERIE (TYPE 3), JOINTS CAUVECHÀS;
 - BARRE "Z" 92mm, CAL.16;
 - COLONNE DE BÉTON EXISTANTE À CONSERVER.
 - 12 LIMITE DU LITEAU DE STRUCTURE.
 - 13 PLAGE EN ACIER GALVANISÉ "L" 75x75mm, CAL.18 POUR RELIER LES BARRES "Z".
 - 14 REMPLIR LA CAVITÉ D'ISOLANT LAINE DE FIBRE DE
 - 15 TÔLE EN ACIER GALVANISÉ COMPACTIONNEMENT CONTINU SUR TOUTE LA HAUTEUR DE L'ÉTAGE, CAL.24.
 - 16 REMPLIR L'ENTREMISE ET LES ESPACES DE PART ET D'AUTRE D'ISOLANT DE FIBRE DE ROCHE FLEXIBLE, VOIR DÉTAIL #8.1 DE LA FEUILLE 411.
 - 17 TÔLE DE COIN EXISTANT À DÉMOLIR.
 - 18 NOUVELLE COMPOSITION :
 - PAREMENT D'ACIER, CAL.22, HORIZONTAL;
 - BARRE "Z" 19mm D'ÉPAISSEUR, CAL.16 @ 405mm C/C, VERTICALE;
 - BARRE "Z" 19mm D'ÉPAISSEUR, CAL.16 @ 405mm C/C, HORIZONTALE;
 - MEMBRANE PARE-INTÉMPIERIE (TYPE 3), JOINTS CAUVECHÀS;
 - BARRE "Z" 92mm;
 - ISOLANT SEMI-RIGIDE DE FIBRE DE ROCHE 89mm D'ÉPAISSEUR;
 - COLOMBAGE MÉTALLIQUE EXISTANT À CONSERVER;
 - ISOLANT DE FIBRE DE VERRE EXISTANT À CONSERVER;
 - CARTON-FIBRE EXISTANT À CONSERVER;
 - PARE-VAPEUR EXISTANT À CONSERVER;
 - FOURRIÈRE MÉTALLIQUE EXISTANTE À CONSERVER;
 - PLAQUE DE PLÂTRE EXISTANTE À CONSERVER.
 - 19 PROFIL DU PARAPET INTRAMURAL.

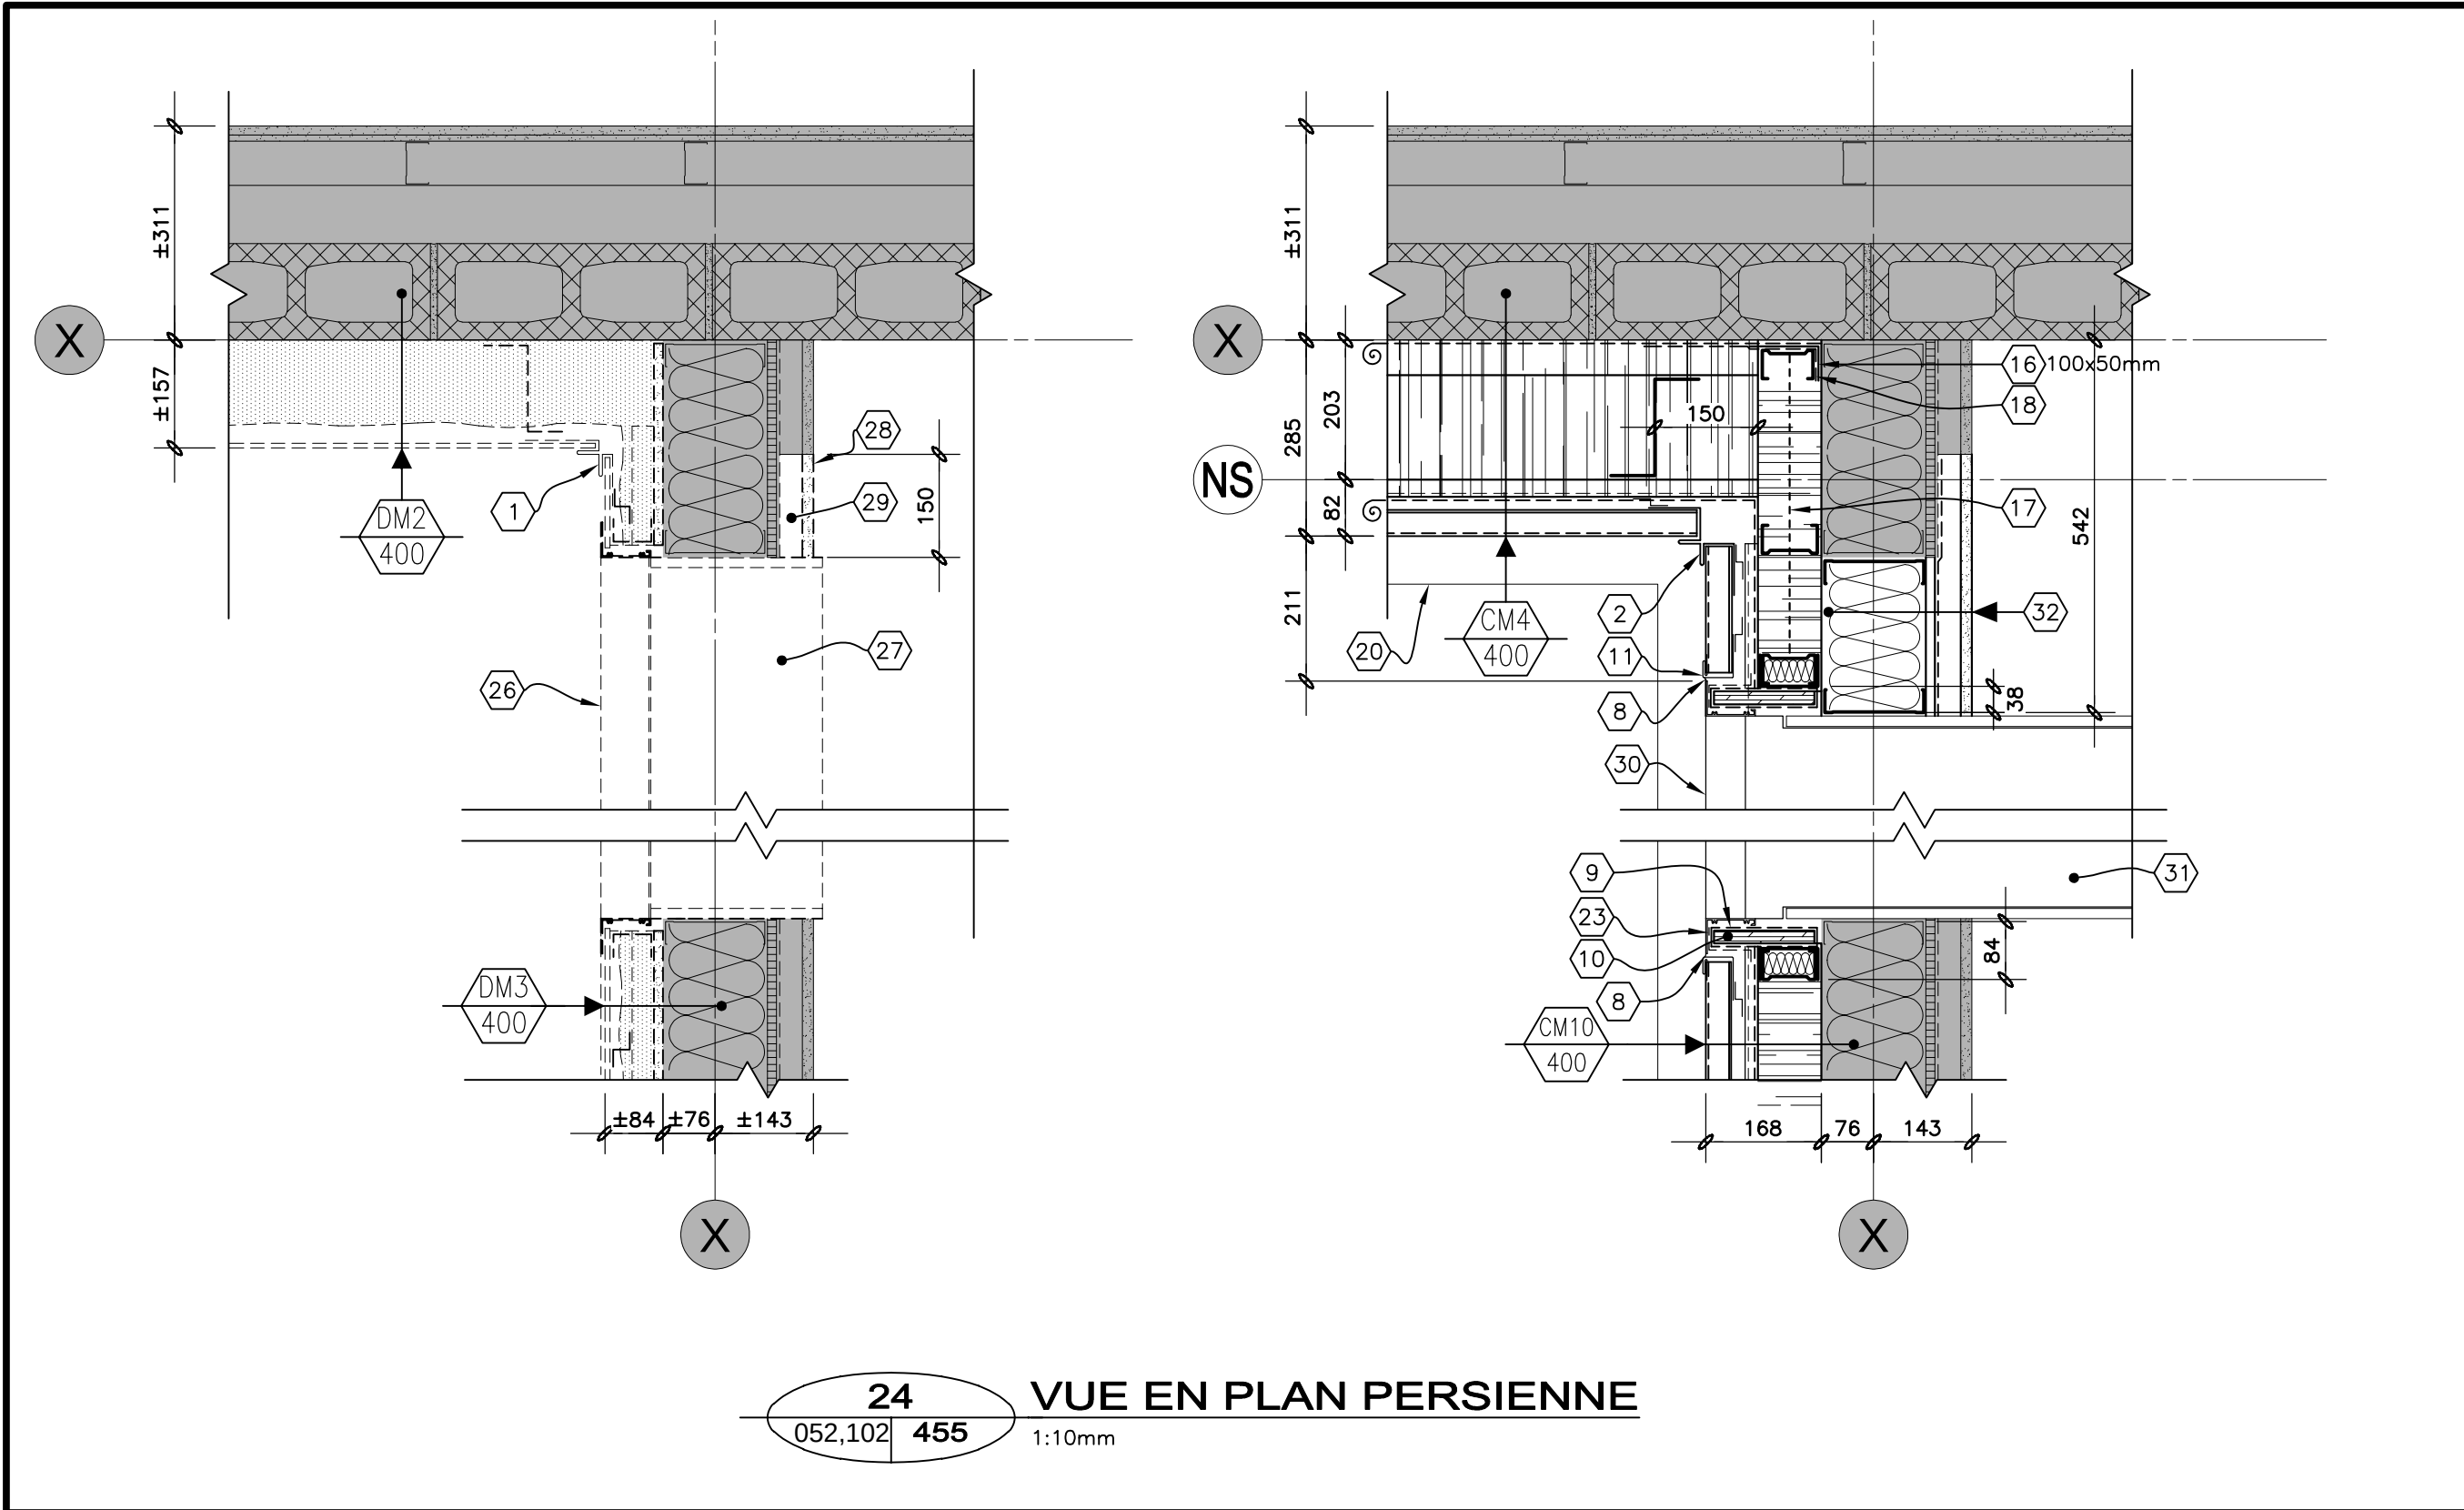


24 VUE EN PLAN PERSIENNE
052,102 455 1:10mm

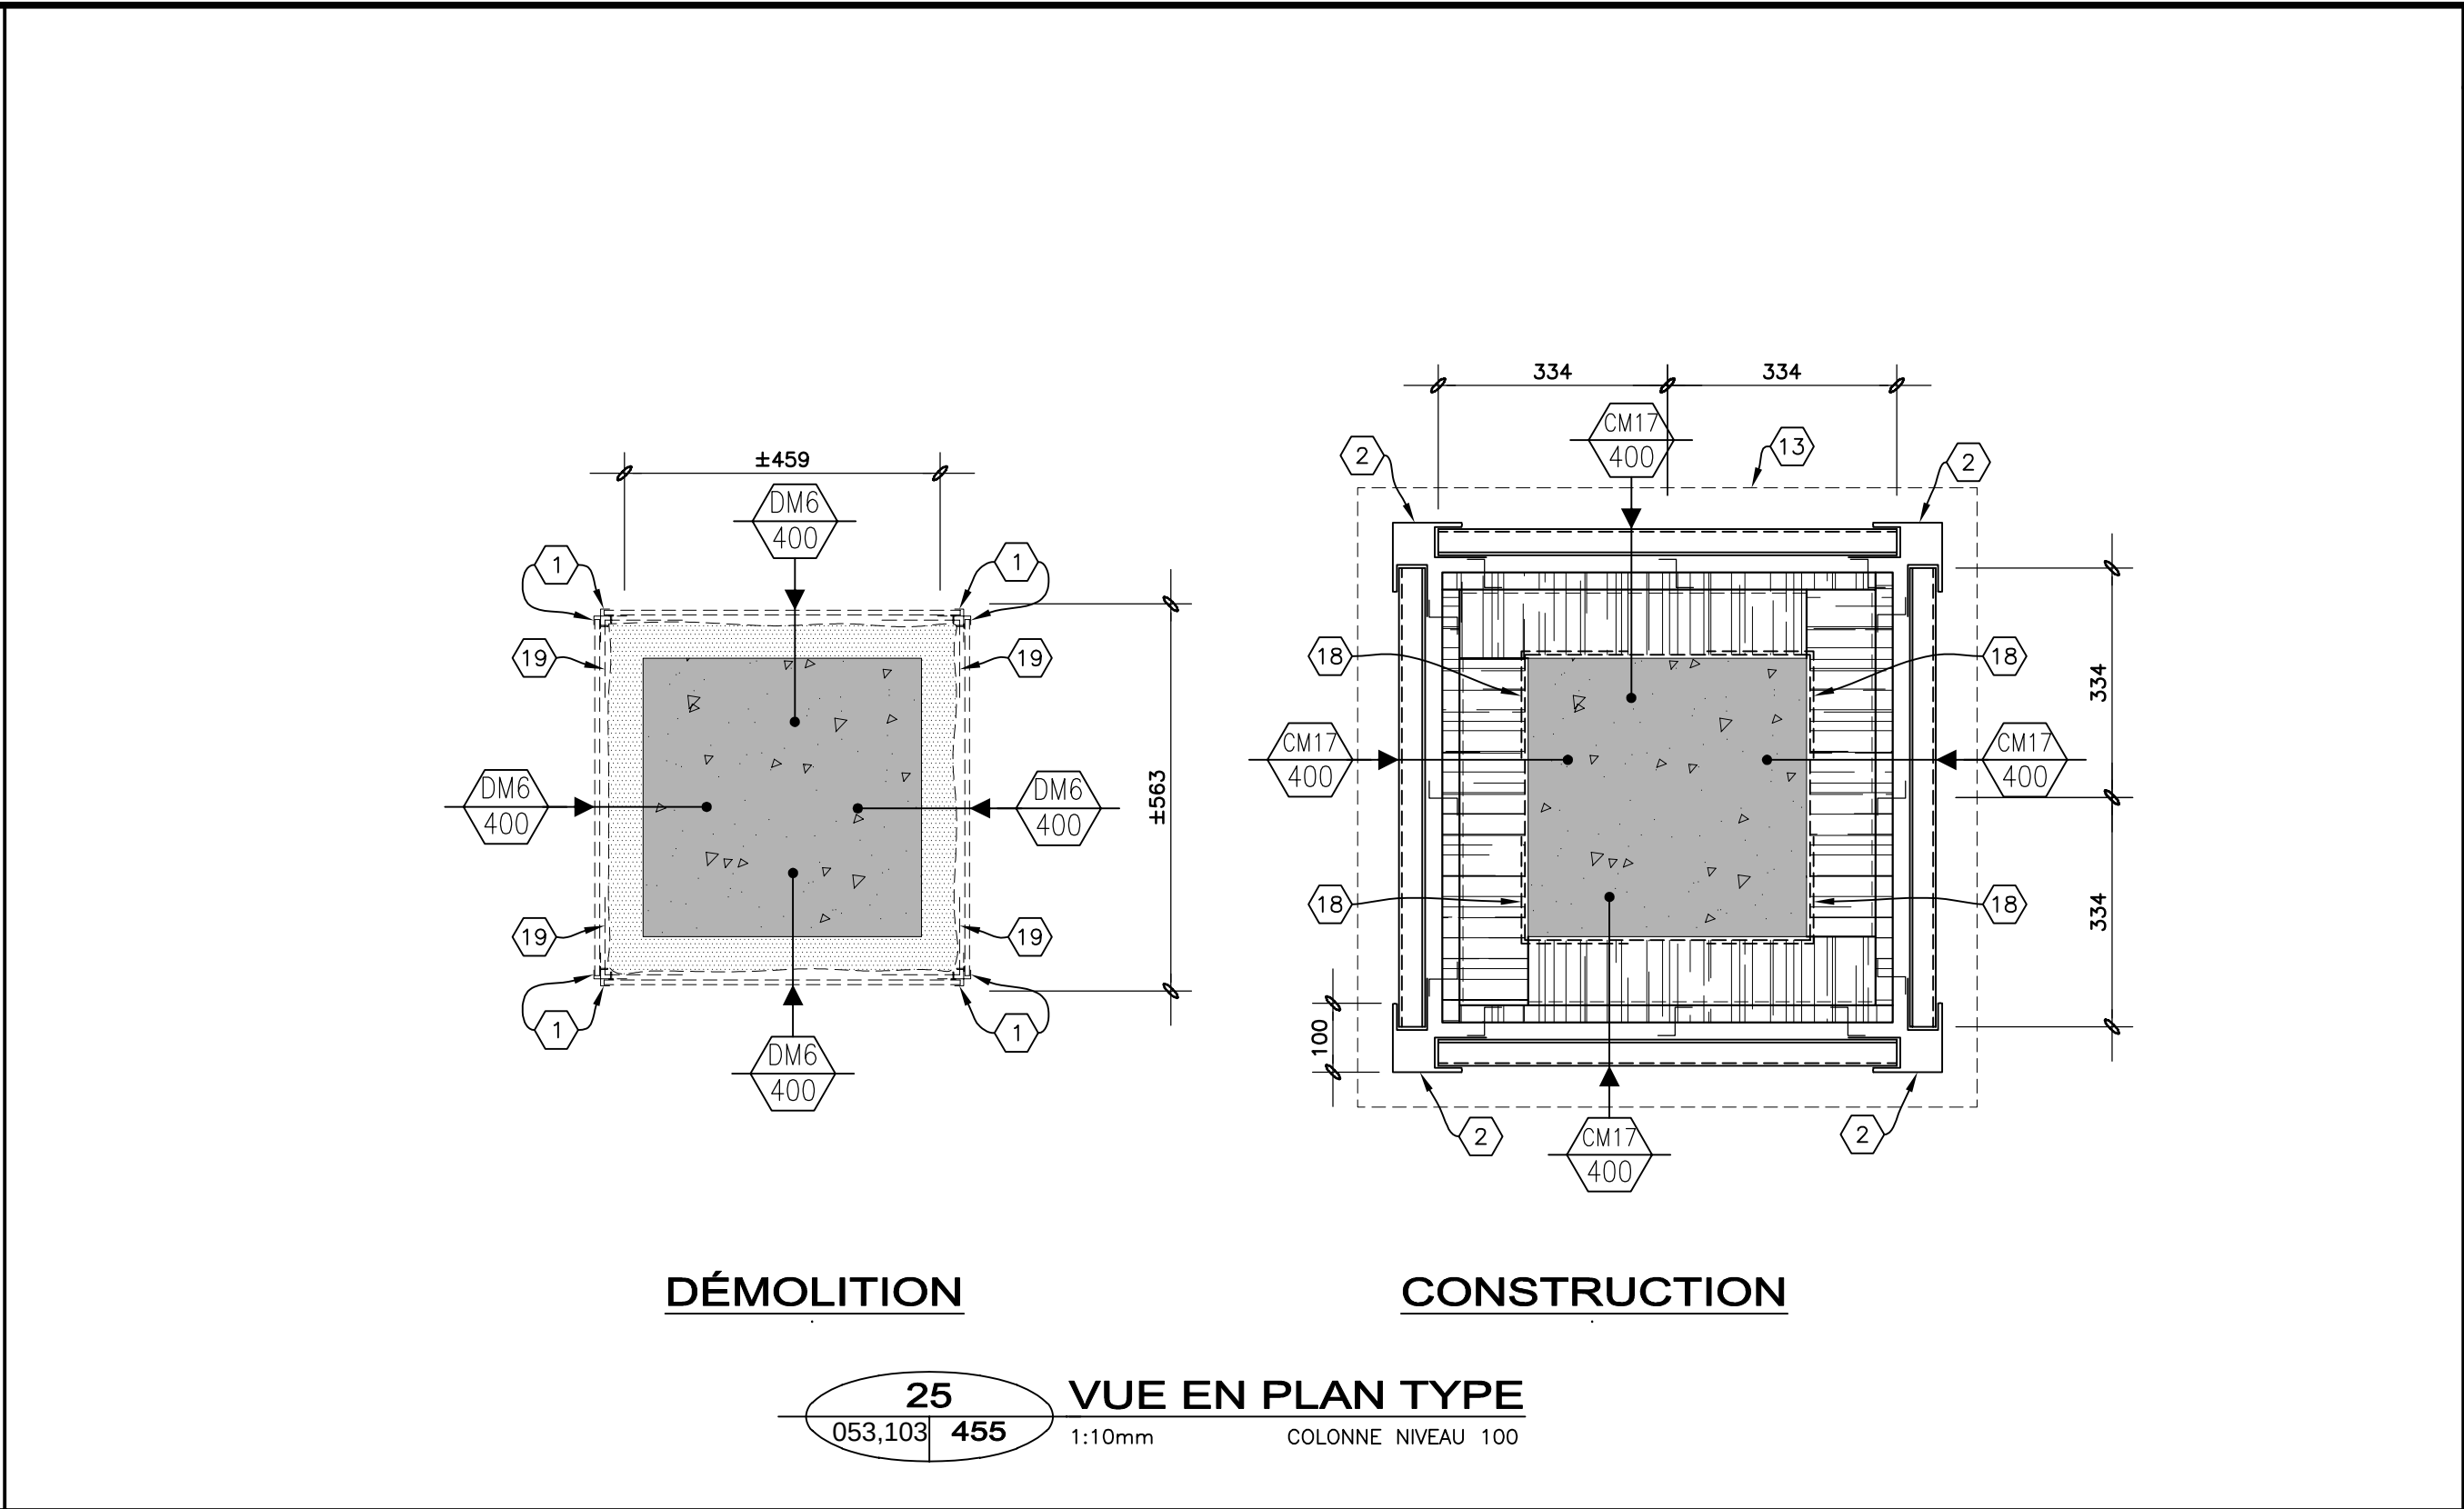


25 VUE EN PLAN TYPE
053,103 455 1:10mm COLONNE NIVEAU 100

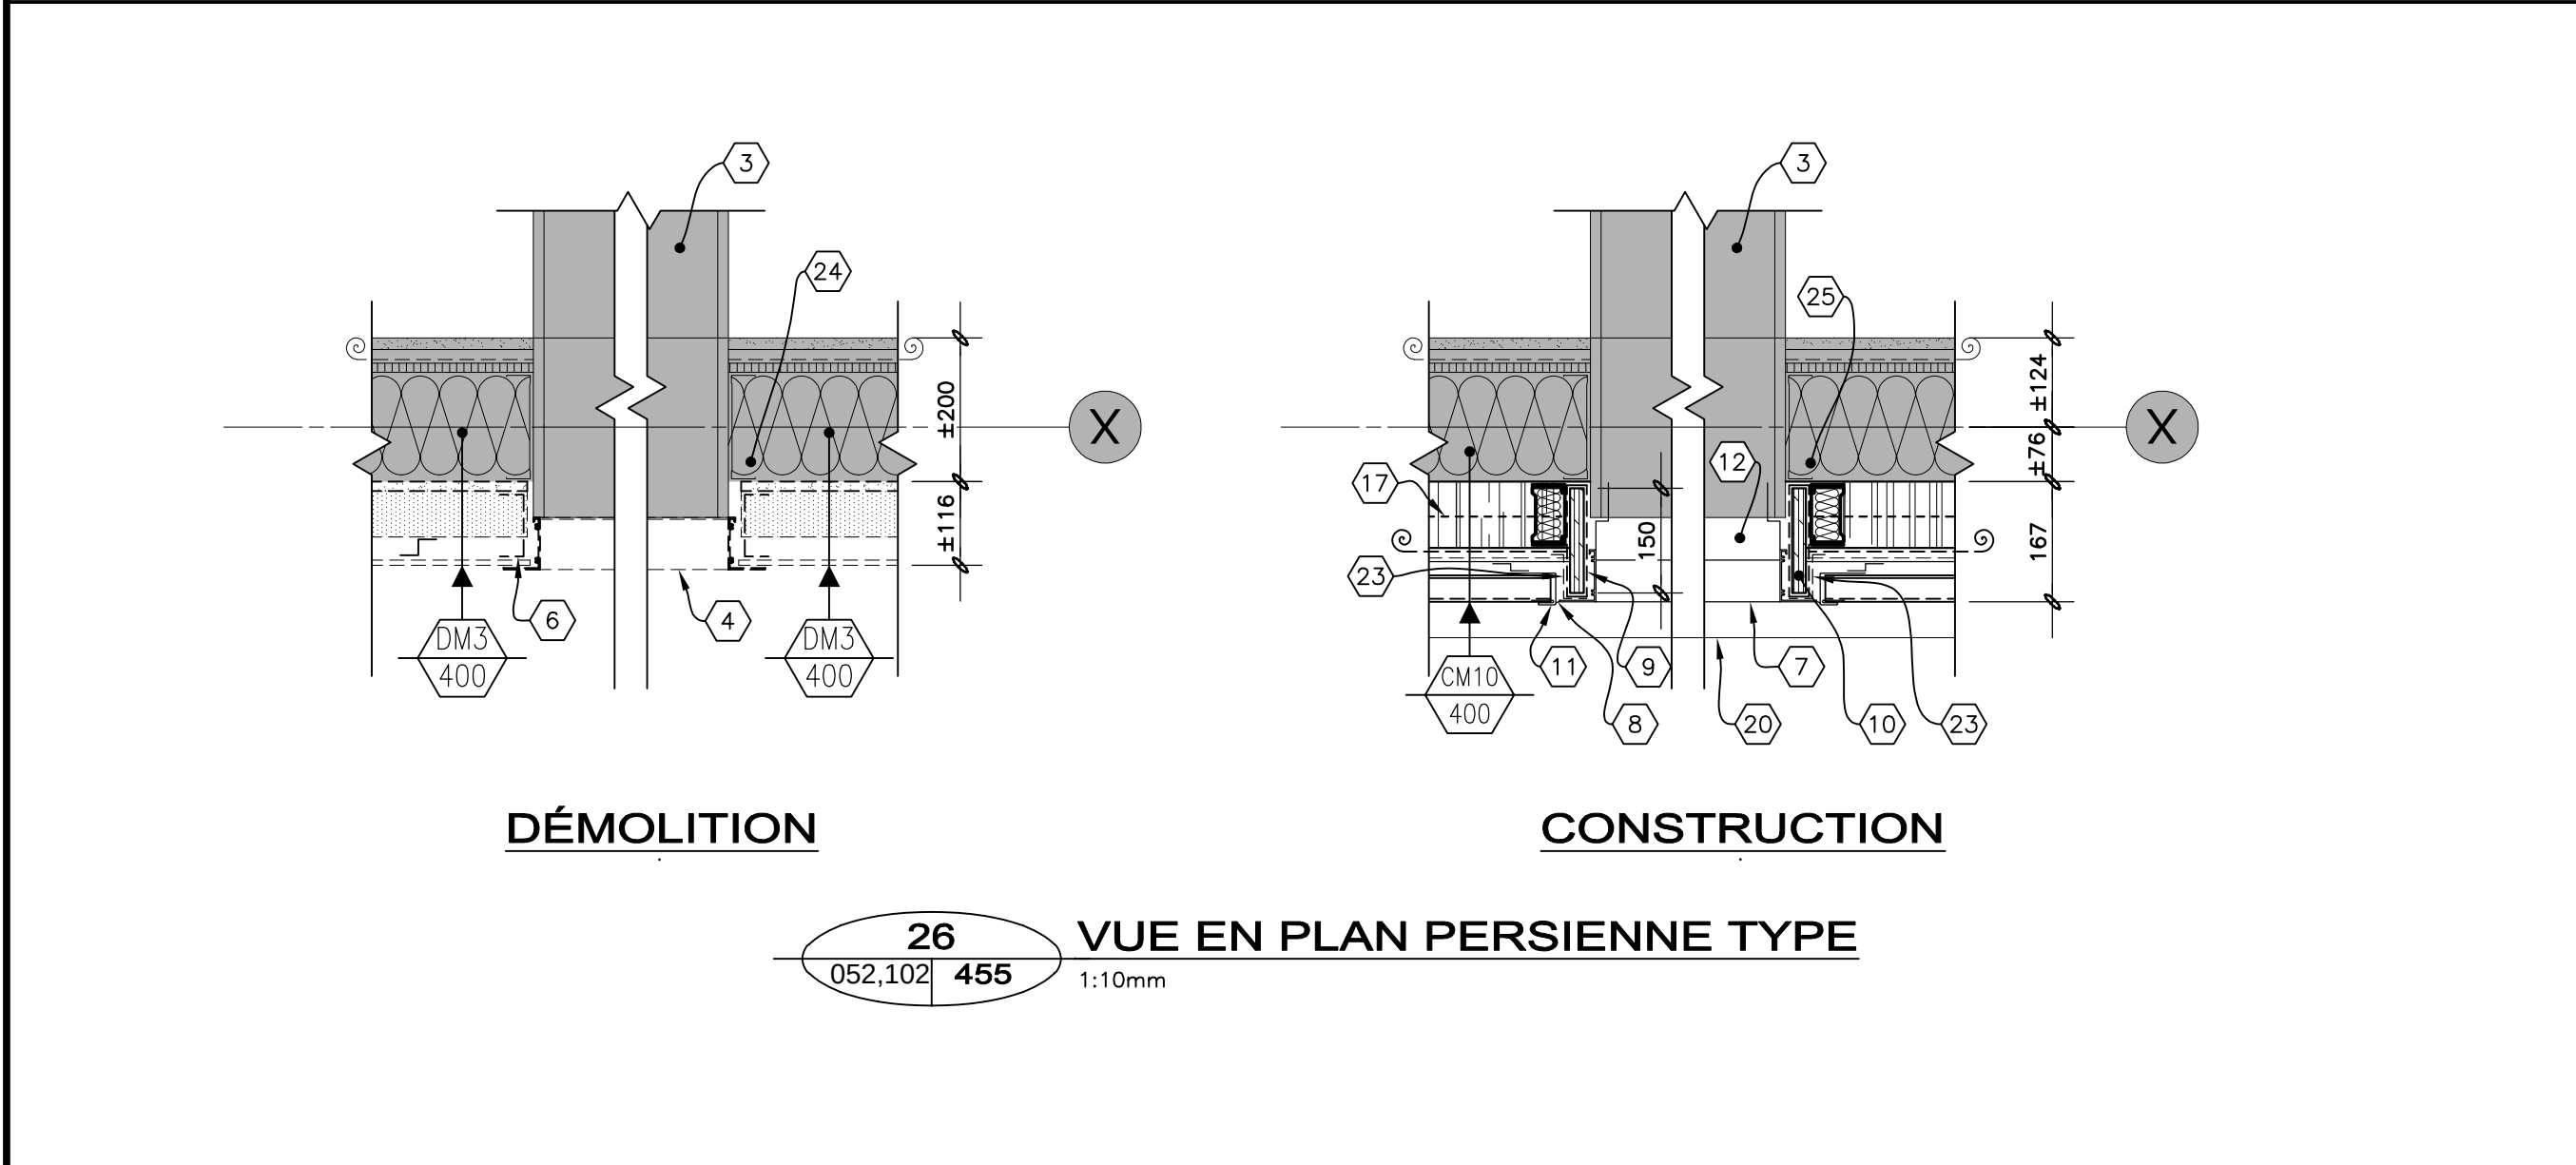


26 VUE EN PLAN PERSIENNE TYPE
052,102 455 1:10mm

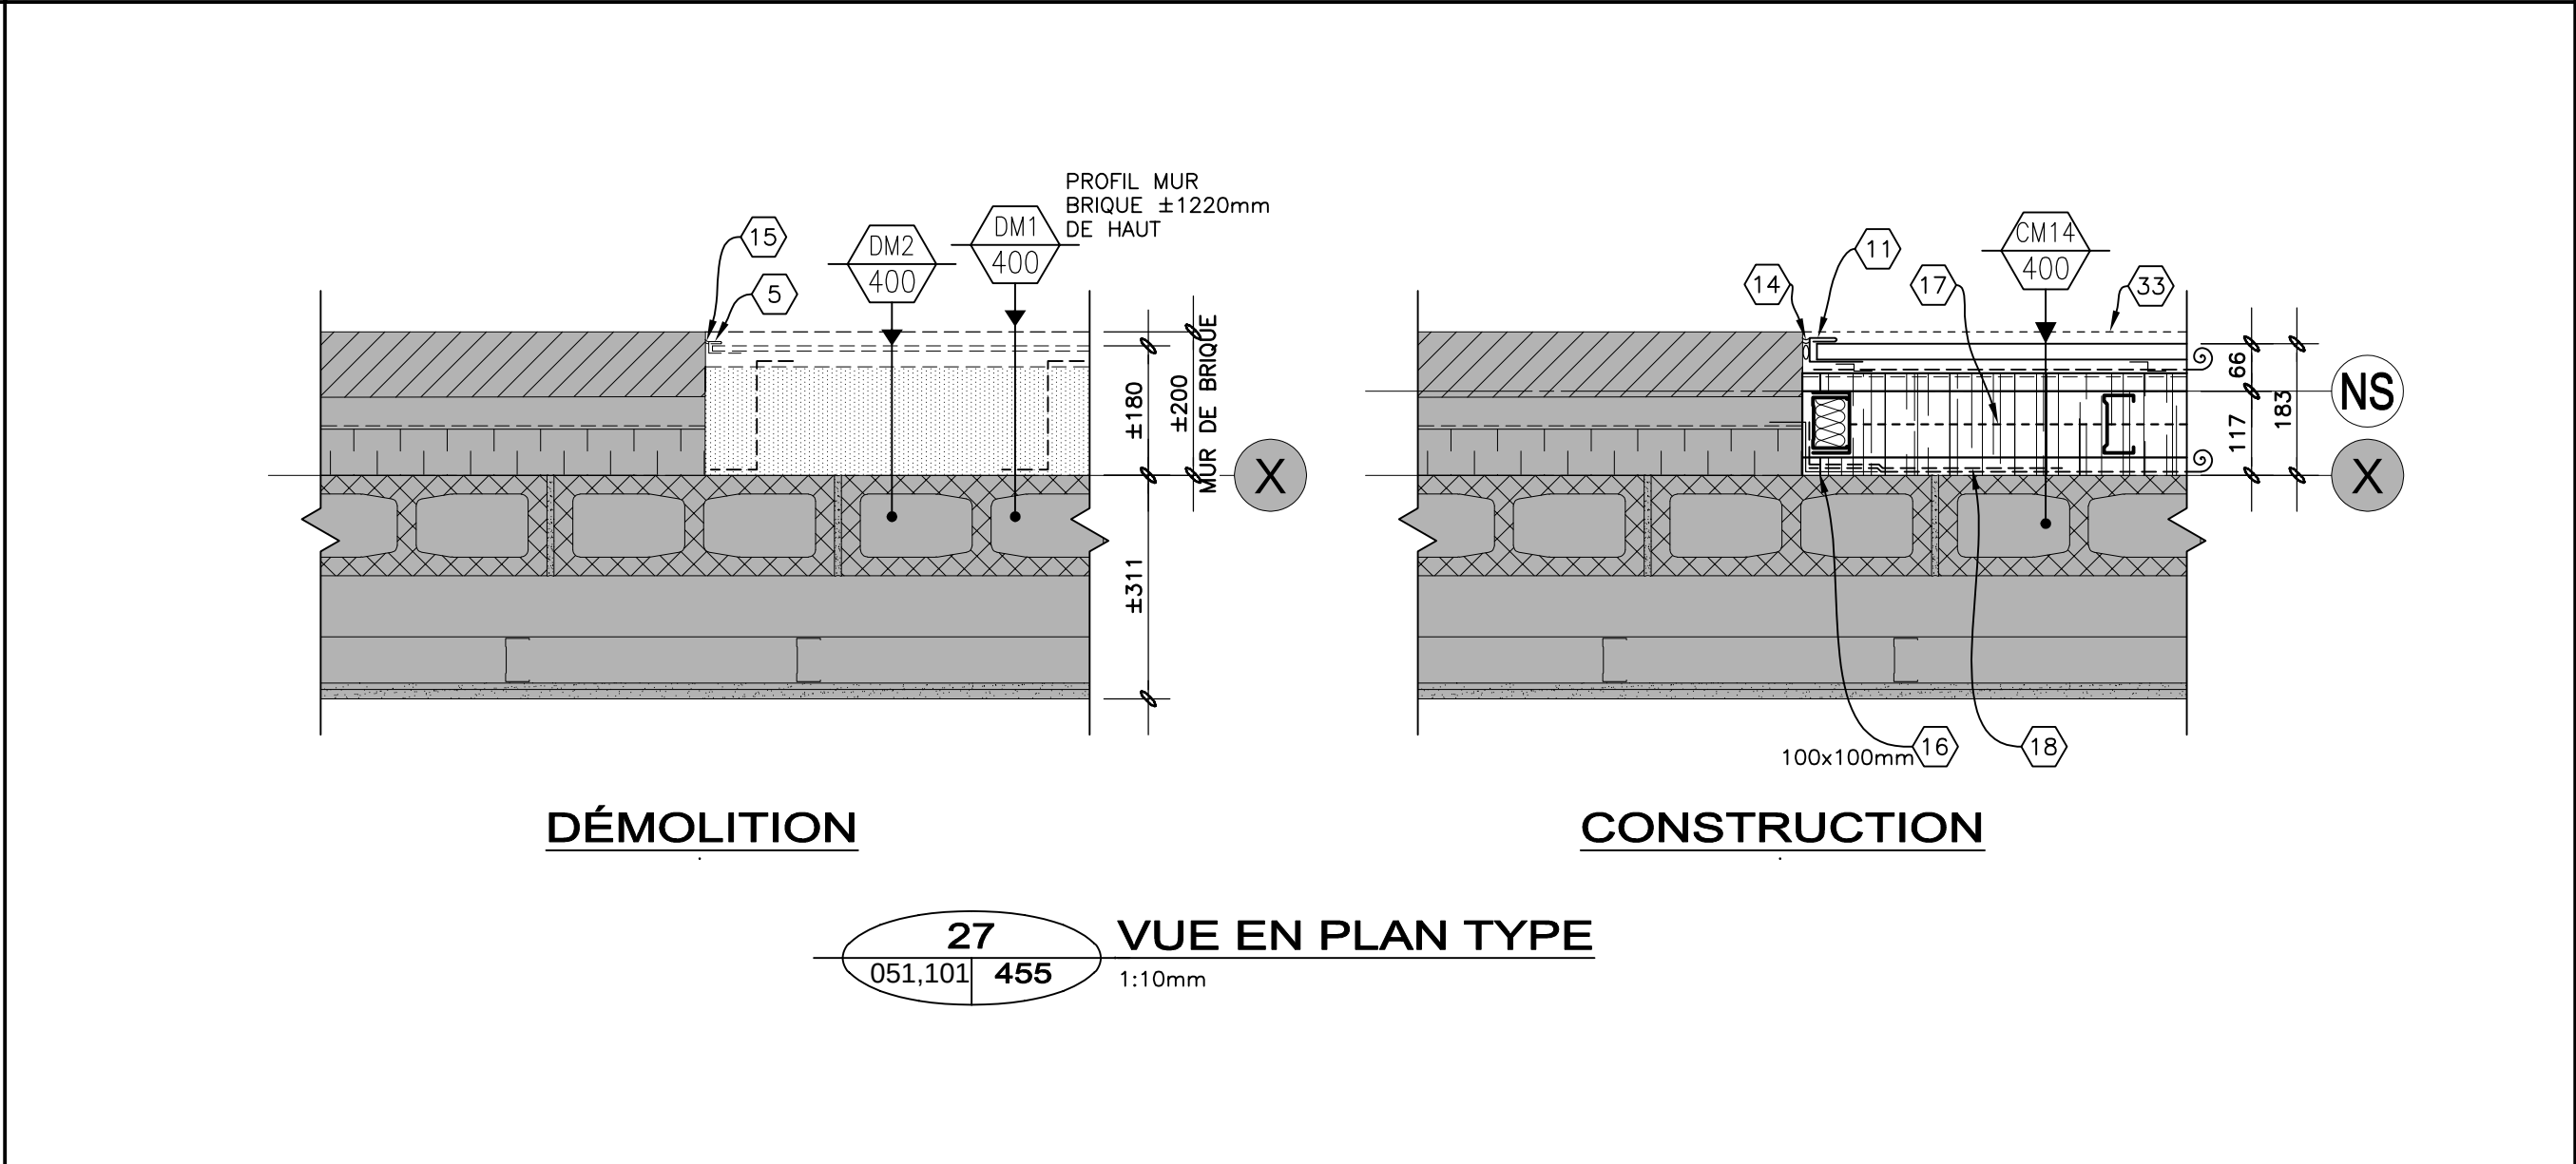

27 VUE EN PLAN TYPE
051,101 455 1:10mm

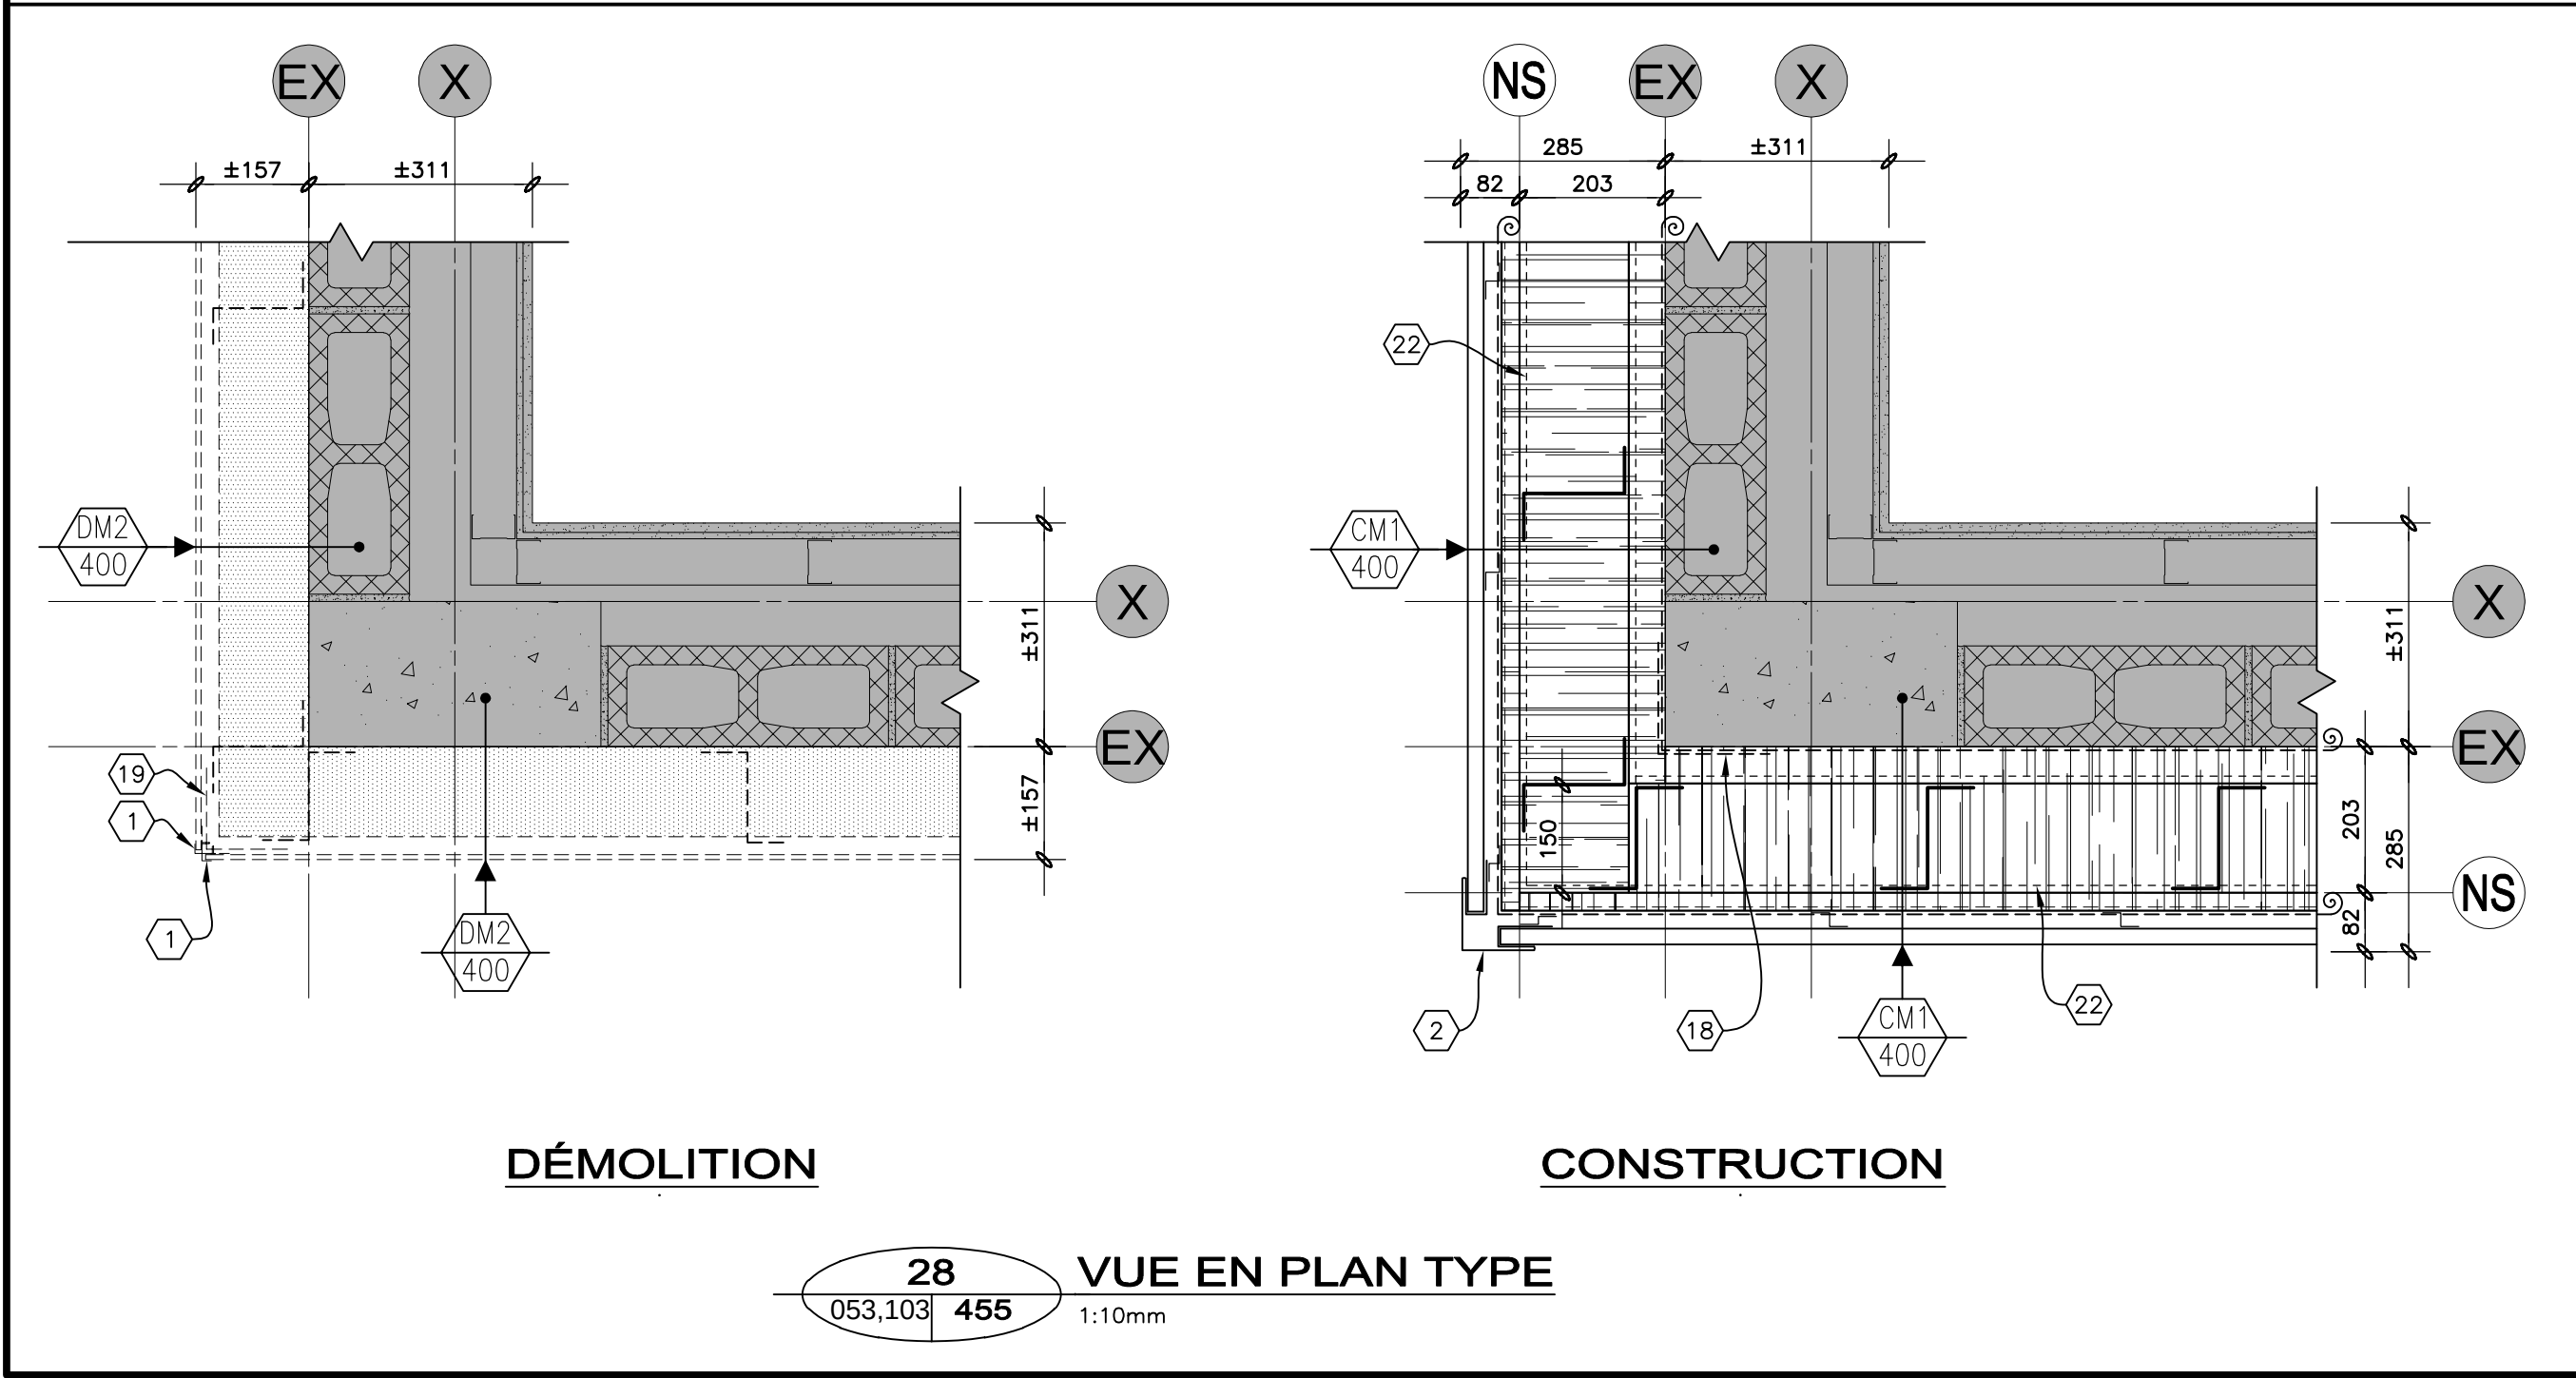

28 VUE EN PLAN TYPE
053,103 455 1:10mm

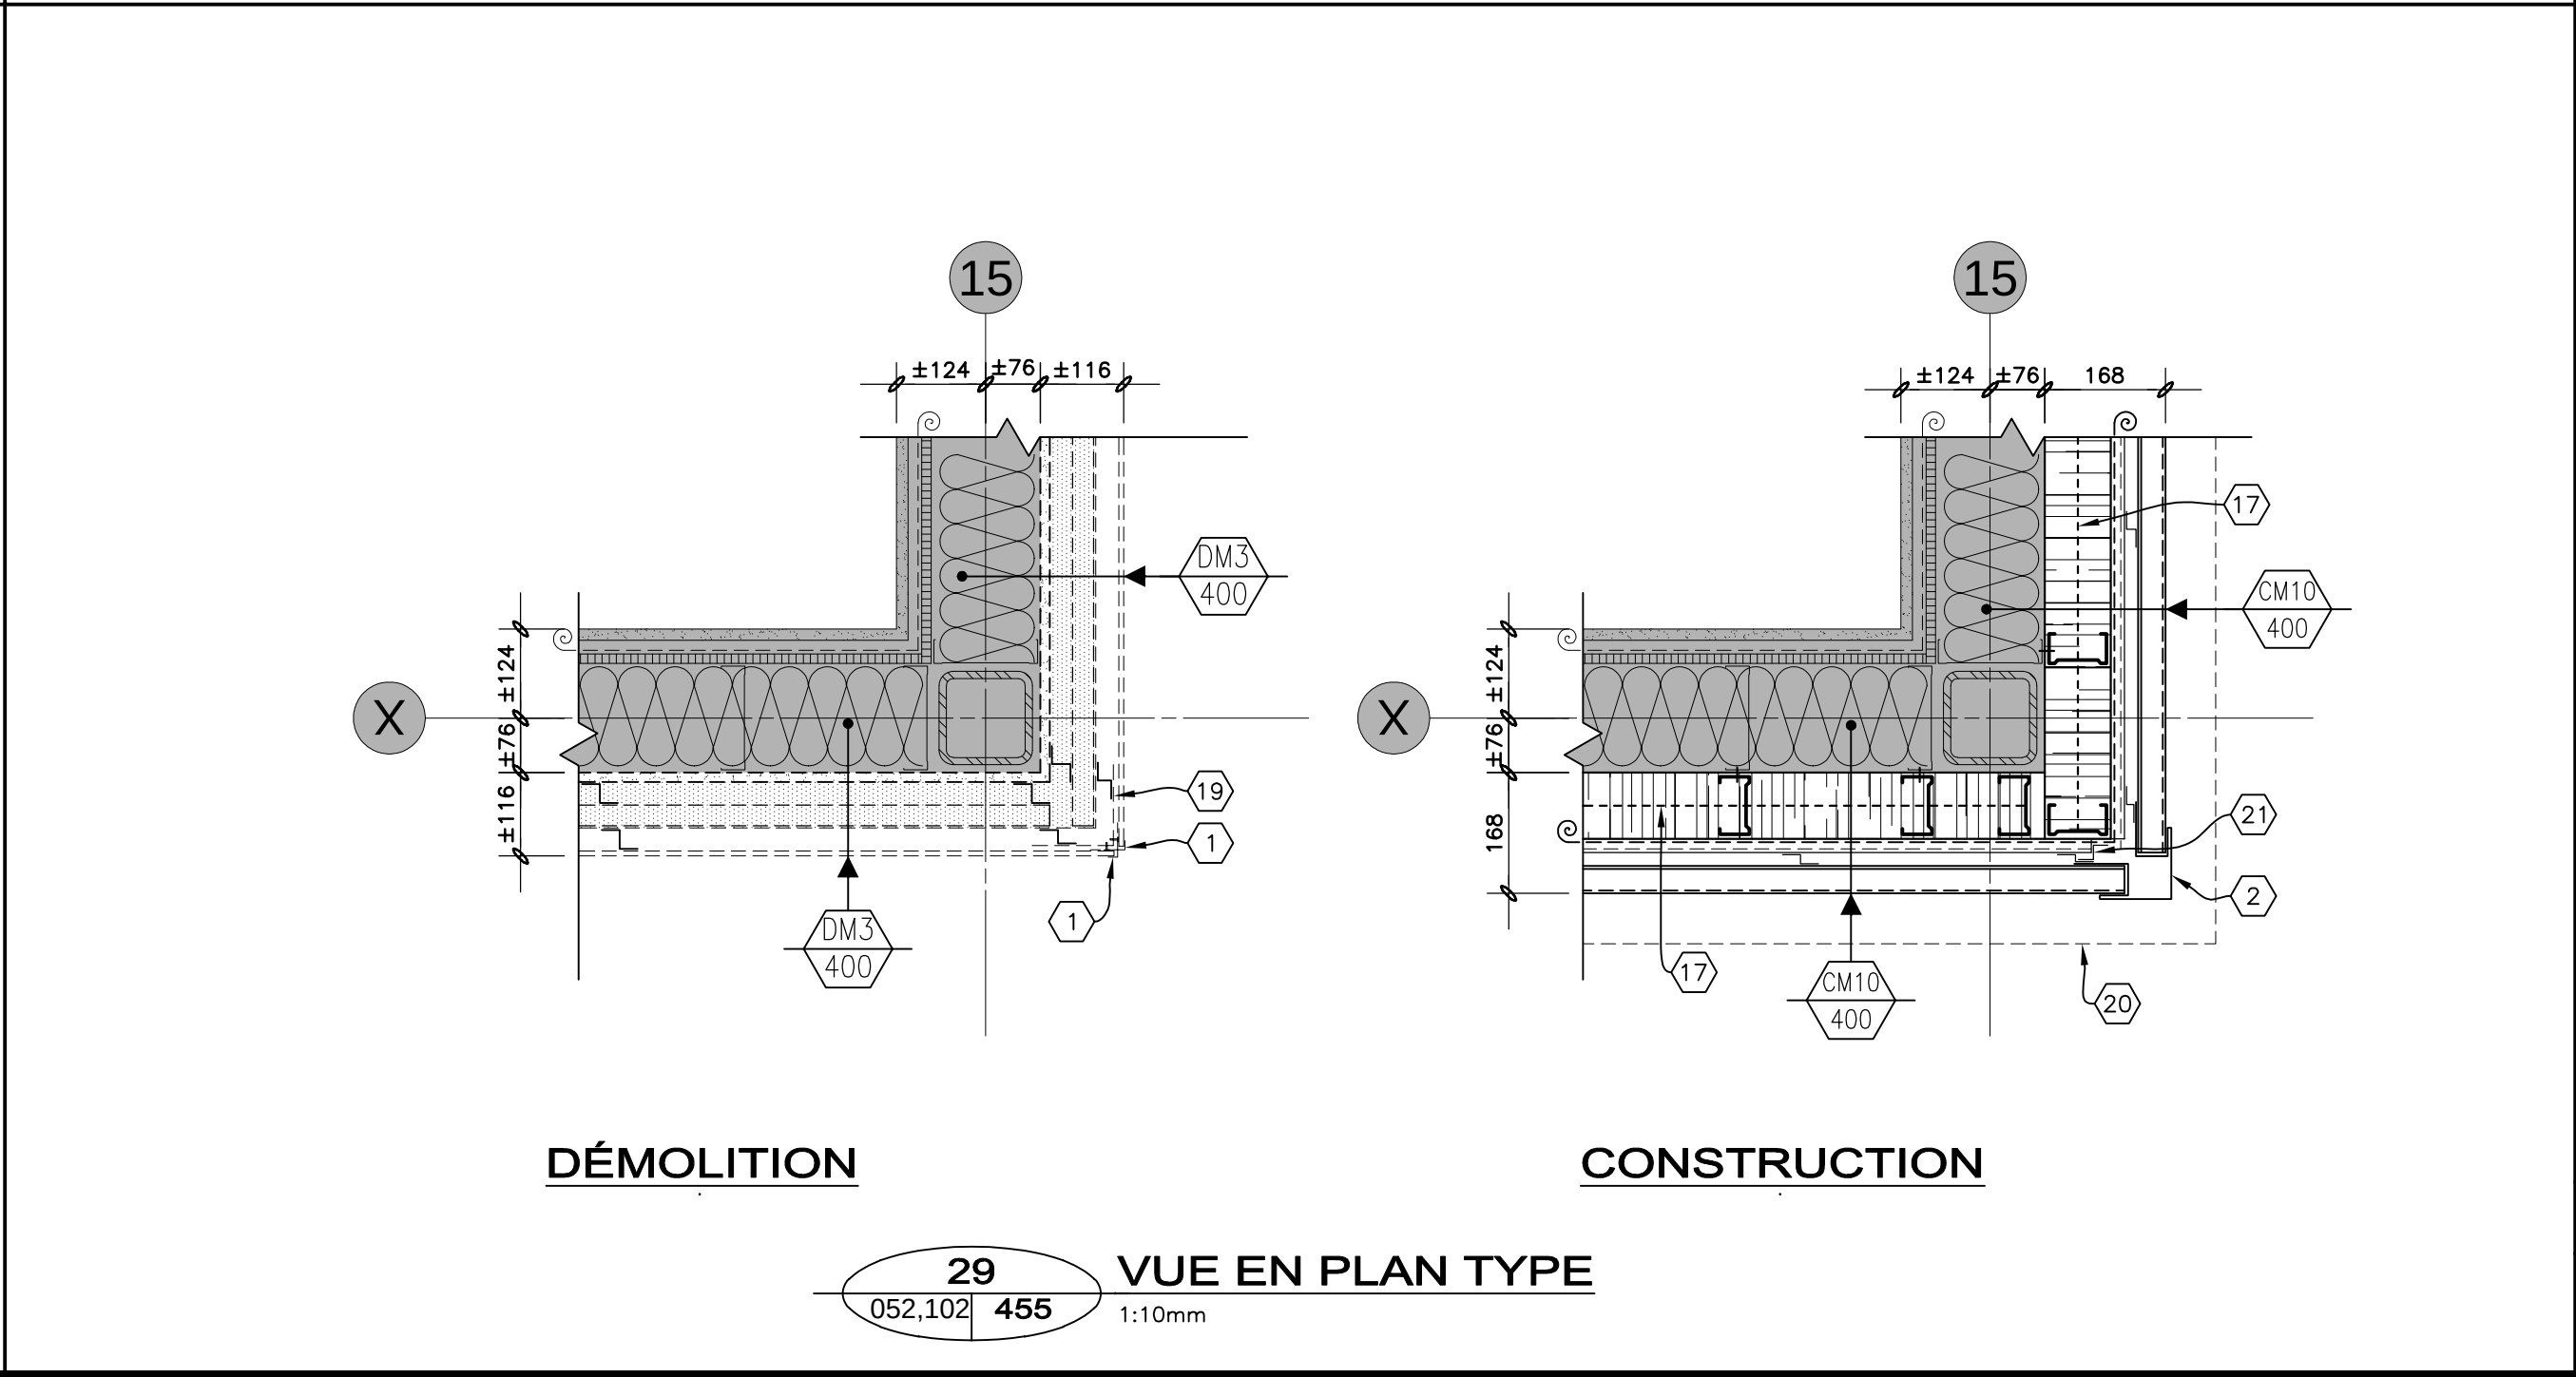

29 VUE EN PLAN TYPE
052,102 455 1:10mm

NOTES

1

MOULURE DE COIN EXISTANTE À DÉMOLIR.

2

MOULURE DE COIN DE PAREMENT EN ACIER ÉMAILLÉ, CAL.22.

3

CONDUIT DE MÉCANIQUE EXISTANT À CONSERVER, VOIR DOCUMENTS D'INGÉNIERIE.

4

PERSIENNE EXISTANTE À ENLEVER, GRATTER, PEINDRE ET REINSTALLER, COMPOSÉ DE 4 SECTIONS DE ± 1900 LARGEUR X 2440mm DE HAUTEUR CHACUNE.

5

MOULURE DE PAREMENT À DÉMOLIR.

6

FER C EXISTANT À DÉMOLIR.

7

PERSIENNE EXISTANTE REPEINTE À REINSTALLER.

8

SCÉLLANT CONTINUE.

9

MEMBRANE DE TYPE-3 SUR TOUT LE PÉRIMÈTRE DU CONTREPLAQUÉ.

10

CONTREPLAQUÉ À PLUS TYPE EXTÉRIEUR 19mm SUR TOUT LE PÉRIMÈTRE DE L'OUVERTURE.

11

MOULURE D'EXTREMITÉ DE PAREMENT EN ACIER ÉMAILLÉ, CAL.22.

12

PROLONGER LE CONDUIT DE LA PERSIENNE, VOIR MÉCANIQUE.

13

PROFIL DES NOUVEAUX PARAPETS.

14

SCÉLLANT CONTINUE SUR BOUDIN COMPRESSIBLE 10mm MINIMUM.

15

SCÉLLANT EXISTANT À DÉMOLIR.

16

PLIAGE EN ACIER GALVANISÉ EN "L", CAL.18.

17

REMPLIR L'ENTREMISE ET LES ESPACES DE PART ET D'AUTRE D'ISOLANT DE FIBRE DE ROCHE FLEXIBLE, VOIR DÉTAIL #6.1 DE LA FEUILLE 411.

18

MEMBRANE DE TYPE-1.

19

TÔLE DE COIN À DÉMOLIR.

20

PROFIL DU PARAPET INTRAMURAL.

21

TÔLE EN ACIER GALVANISÉ DE COMPARTIMENTATION CONTINU SUR TOUTE LA HAUTEUR DE L'ÉTAGE, CAL.24.

22

LIMITE DU LITEAU DE STRUCTURE.

23

RUBAN AUTOCOLLANT. SCÉLLER LA MEMBRANE PARE-INTÉMPÉRIES AVEC LA MEMBRANE AUTOADHÉSIVE.

24

ISOLANT DE FIBRE DE VERRE EXISTANT À ENLEVER TEMPORAIREMENT POUR LES TRAVAUX DE STRUCTURE.

25

ISOLANT DE FIBRE DE VERRE À REINSTALLER.

26

PERSIENNE EXISTANTE À DÉMOLIR.

27

CONDUIT DE MÉCANIQUE EXISTANT À DÉMOLIR, VOIR DOCUMENTS D'INGÉNIERIE.

28

SECTION DE GYPSE EXISTANT À DÉMOLIR.

29

BARRE "Z" EXISTANT À COUPER.

30

NOUVELLE PERSIENNE DE 950X400mm.

31

NOUVEAU CONDUIT DE MÉCANIQUE, VOIR DOCUMENTS D'INGÉNIERIE.

32

NOUVELLE SECTION DE MUR :

- GYPSE 13mm;
- FOURRURE MÉTALLIQUE;
- PARE-VAPEUR CHEVAUCHANT CELUI EXISTANT DE 150mm;
- ISOLANT EN NATTES 152mm;
- COLOMBAGE MÉTALLIQUE 152mm.

33

PROFIL DE LA FONDATION EXISTANTE.

GLCRM | Proulx Savard |

GLCRM:
128, Avenue de la Cathédrale,
Bureau 201
Rimouski, QC, G5L 5H7
(418) 722-7655

2404, Ch. des Quatres-Bourgeois,
Bureau 100
Québec, QC, G1V 1W5
(418) 647-1700

Proulx Savard Architectes:
75, boul. Arthur-Buies Ouest,
Rimouski QC G5L 5C2
(418) 723-5543

ARCHITECTURE

CONSULTANTS

Odre des architectes

A-3996

DAVID SAVARD

ARCHITECTE

du Québec

Odre des architectes

3276

FRANÇOIS MATHIEU

ARCHITECTE

du Québec

DOSSIER No. 24-1087 / 6857-24

DATE SEPTEMBRE 2024

DESIGNATEUR (S) A.C. INDICUÉE

05 2024-09-04 DÉFINITIVES POUR SOUMISSION

04 2024-08-21 DÉFINITIVES 100% POUR APPROBATION

03 2024-08-03 DÉFINITIVES 80% POUR APPROBATION

02 2024-05-14 DÉFINITIVES 40% POUR APPROBATION

01 2024-02-27 PRÉLIMINAIRES 20% POUR APPROBATION

REVISIONS

No DATE

DESSIN

DETAIL EN PLAN

DÉMOLITION / CONSTRUCTION

PROJET

HÔPITAL DE CHANDLER,
Chandler
(Réfection de l'enveloppe)


PROPRIÉTAIRE

Santé Québec


NE DOIT PAS SERVIR À L'EXÉCUTION

Le présent document est émis pour la seule fin identifiée. Son contenu est protégé par les droits d'auteur et toute reproduction ou modification, partielle ou totale, est interdite sans l'autorisation écrite de gagnon, letellier, cyr, ricard, mathieu, proulx, savard consortium d'architectes.

455

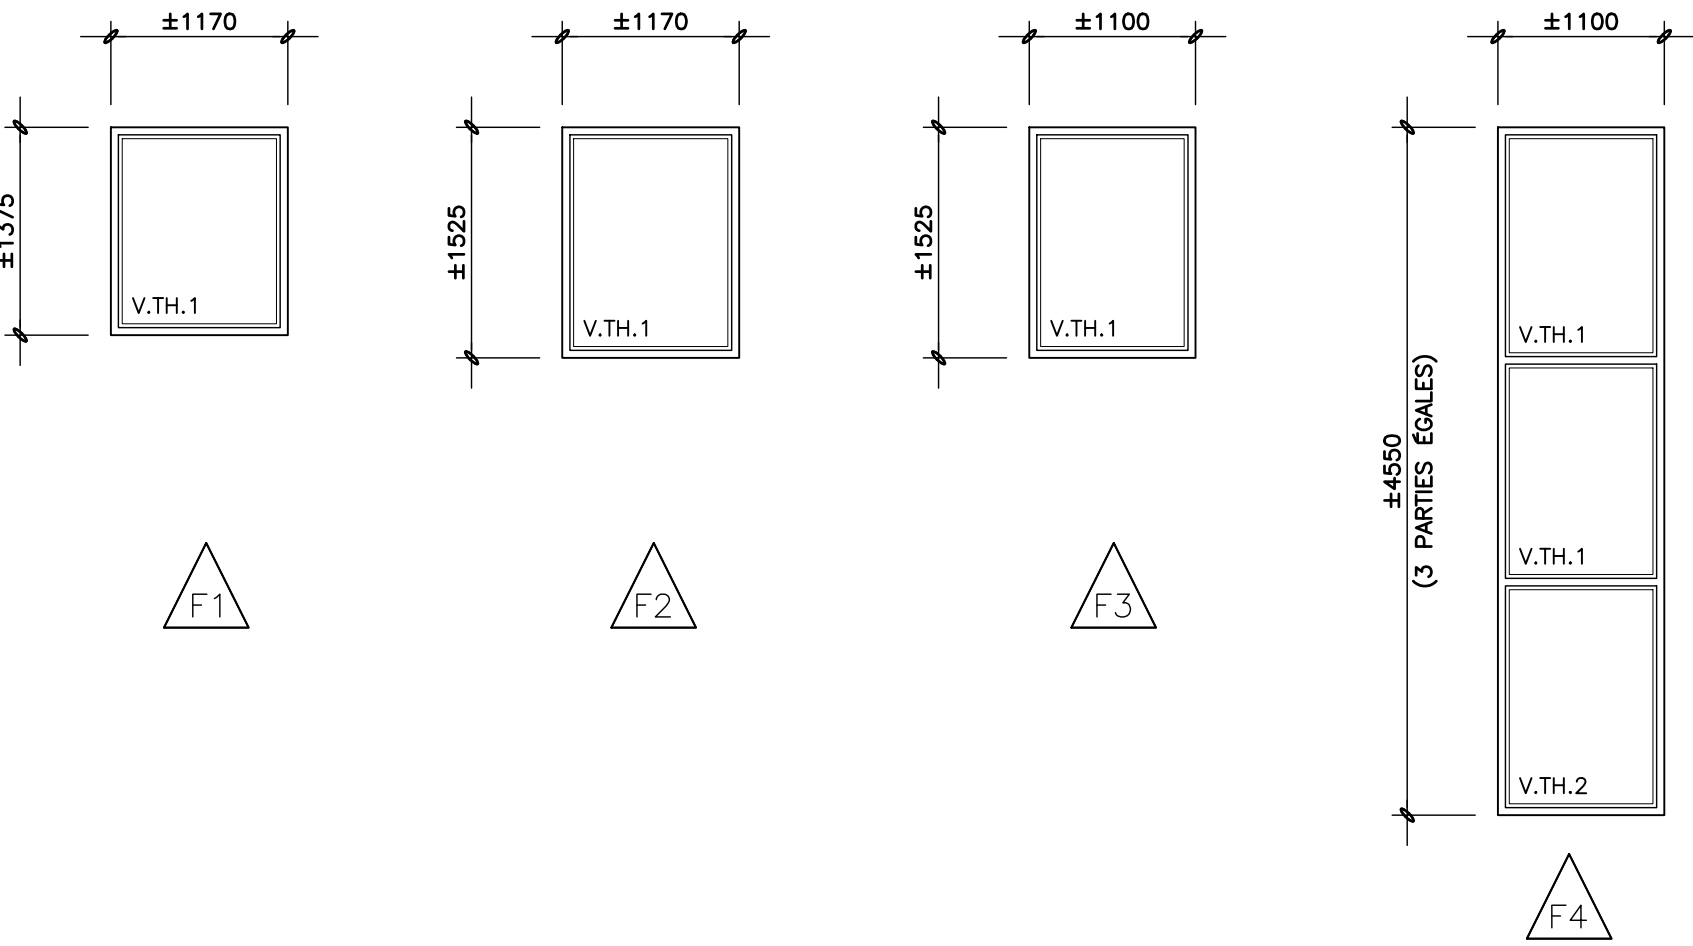

ÉLÉVATIONS TYPES DES FENÊTRES
1:50mm
(VUE DE L'EXTÉRIEUR)

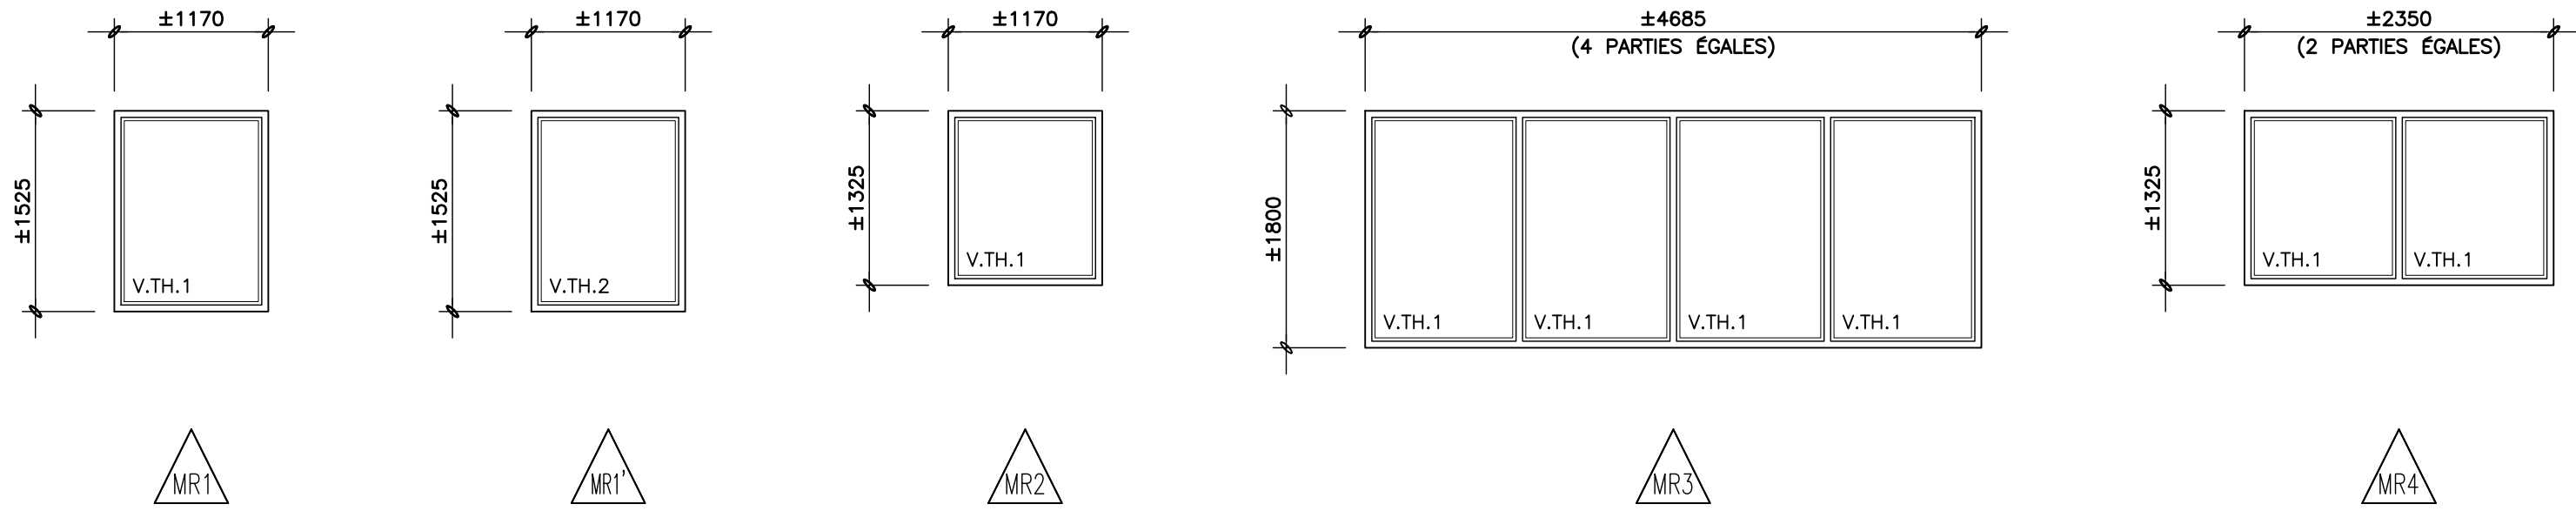

ÉLÉVATIONS TYPES DES MURS RIDEAUX
1:50mm
(VUE DE L'EXTÉRIEUR)

NOTE - MENEAU

1. MENEAU PÉRIMÉTRIQUE VERTICAL ET HORIZONTAL:
- 50,8mm X 140mm AVEC COUVERCLE À PRESSION DE 25mm.

LÉGENDE - TYPES DE VITRAGE

(VOIR DEVIS SECTION 08 80 50 POUR LE TYPE DE VITRAGE)

- V.TH.1.: VERRE THERMOS CLAIR
V.TH.2.: VERRE DE SÉRURITÉ THERMOS CLAIR.

PROFONDEUR DES ENCADREMENTS DE FINITION INTÉRIEURE EXISTANTES

REZ-DE-CHAUSSÉE		NIVEAU 100		NIVEAU 200		NIVEAU 300		NIVEAU 400		ESCALIER #5	
# LOCAL	PROFONDEUR	# LOCAL	PROFONDEUR	# LOCAL	PROFONDEUR	# LOCAL	PROFONDEUR	# LOCAL	PROFONDEUR	# LOCAL	PROFONDEUR
R04	340	101-D10-A	125	202	315	301	350	401	355	ESC#5-100	330
R07	335	101-D-11	125	202A	325	302	325	402	345		
	335	101-D4	125	203	320	303	315	403	340		
	325	101-D5	125	204	310	304	370	404	345		
R10-B	295	101-D6	125	205	310	305	360	405	350		
R10-B1	295	101-D7	125	206	325	306	355	406	330		
R10-I	340	101-D8	125	207	345	307	335	407	320		
	345	101-D9	125	208	405	308	325	408	330		
R10-J	350	101-D9	125	209	445	309	335	409	335		
R10-K	330	104-A1	205		435	310	360		330		
	340	104-A2	205	210	460	311	315	410A	325		
R10-M	295	104-C	150		420	311-A	365	410B	310		
R16	305		155	211	400	315	290	411	310		
	355	104-F	150		410	316	295	412	305		
R33-D	320		150	212	345	317	285		305		
	320	104-G	155	213	340	318	285	414	310		
R33-D2	310		160	214	360	319	285	415	310		
R34-B	300	105-B	120	215	390	320	275	416	305		
R34-C	305	105-C	110	216	395	321	220	417	315		
R36-B1	115	105-D	115	217	420	322	225	418	315		
R36-B2	115	105-E	110	218	400	323	220	419	305		
R36-F	310	107-A	105	219	385	324	205	420	310		
R36-J	330	107-C	110	220	360	331-A	310	421	305		
R44-B	300	109	120	221	335	332-A	305	422	295		
R44-C	310	110-A	120	222	315		300	423	280		
R44-D	315	110-B	125	223	290		295	431	305		
	310	110-C	140	224	285	332-B	295	432	315		
R44-E	315	112-B	240	230	315	332-C	285		320		
R44-G	305	112-C	235	231	315	332-D	300	434	330		
R44-I	315	113-A	175	231-A	310	332-H	310		310		
R44-K	330	113-B	175	232	345	337	270	436	310		
R44-M	325	119-A	115		340		265	438	315		
R44-N	325		115	233	385		240	439	365		
R46-G	340	121-A	130	235	290		240		365		
	350	122-A	180	236/237	300	338-A	335		305		
	355	122-B	175			339	340		305		
	345		180			348	310				
	345					380	270				
		122-C	175			381	245	439-A	365		
		122-D	125								
		123-A	250								
		123-B	135								
		123-D	130								
			130								
		123-H	115								
		124	65								
		124-A	155								
			240								
		124-B	170								

NOTE - ENCADREMENTS

- LES DIMENSIONS DANS LE TABLEAU SONT À TITRE INDICATIF SEULEMENT. TOUTES LES DIMENSIONS SONT À VALIDER SUR PLACE. LES DIMENSIONS REPRÉSENTENT LA PROFONDEUR EXISTANTE DES ENCADREMENTS SELON LES DIFFÉRENTS LOCAUX.

NOTES - HABILLAGES DES FENÊTRES EXISTANTES

- L'ENTREPRENEUR GÉNÉRAL DEVRA RETIRER LES TOILES, STORES VERTICAUX, STORES HORIZONTAUX, PÔLES À RIDEAU ET/OU VALENCE SUR CHAQUE FENÊTRE.
- L'ENTREPRENEUR GÉNÉRAL DEVRA INSTALLER TEMPORAIREMENT UN HABILLAGE DE FENÊTRE (TOILE OU STORE) POUR CHACUNE DES FENÊTRES PENDANT LES TRAVAUX. VOIR LES DÉTAILS EN ÉTAPES DE LA PAGE 505.
- REMETTRE TOUS LES HABILLAGES DE FENÊTRES EXISTANTS AU CLIENT À LA FIN DES TRAVAUX.
- L'ENTREPRENEUR GÉNÉRAL DEVRA FOURNIR ET INSTALLER DE NOUVELLES TOILES SOLAIRES POUR LES NIVEAUX 200, 300 ET 400. FOURNIR DES TOILES SOLAIRE 0% POUR LES CHAMBRES ET DES TOILES SOLAIRES 3% POUR LES AUTRES LOCAUX. VOIR LES VUES EN PLANS DES NIVEAUX POUR LES TYPES DE LOCAUX.
- VOIR DEVIS SECTION 12 24 00 POUR LE MODÈLE DE TOILE SOLAIRE À ROULEAU.

NOTES - CONTRÔLE QUALITÉ DES FENÊTRES ET MUR RIDEAUX
(TESTS IN SITU)

(VOIR ÉGALEMENT DEVIS SECTIONS 08 52 00 ET 08 44 13)

- DES ESSAIS "IN SITU" SERONT RÉALISÉS SUR UNE (1) FENÊTRE ET UN (1) MUR RIDEAU PENDANT LE DÉROULEMENT DES TRAVAUX PAR UNE FIRME EXTERNE ENGAGÉE PAR LE PROPRIÉTAIRE. LES COÛTS DE RÉALISATION DE CES ESSAIS SERONT ASSUMÉS PAR LE PROPRIÉTAIRE. CEPENDANT, LES COÛTS RELIÉS AUX TRAVAUX CORRECTIFS, LE CAS ÉCHÉANT, SERONT AU FRAIS DE L'ENTREPRENEUR. CE DERNIER DEVRA ÉGALEMENT FOURNIR LES ÉQUIPEMENTS REQUIS (ÉCHAUDAUFDAGE, NACELLE OU AUTRE) POUR LA RÉALISATION DES TESTS.
- LE PAREMENT EXTÉRIEUR DEVRA ÊTRE INSTALLÉ AU POURTOUR DE L'OUVERTURE CIBLÉE POUR LA RÉALISATION DES TESTS. DANS L'ÉVENTUALITÉ QUE CE DERNIER NE SOIT PAS INSTALLÉ LORS DES ESSAIS, L'ENTREPRENEUR DEVRA CONSTRUIRE EN PÉRIPHÉRIE DE L'OUVERTURE RETENUE UN ASSEMBLAGE TEMPORAIRE DE 610mm DE LARGEUR (4 CÔTÉS). CET ASSEMBLAGE SERA COMPOSÉ COMME SUIVIT:
 - PANNEAU DE BOIS DUR;
 - FOURNITURE MÉTALLIQUE;
 - MEMBRANE PARÉ-INTÉMPIERIE.
- RÉALISER LE SOLINAGE AINSI QUE LE SCÈLLEMENT EN PÉRIPHÉRIE DE L'OUVERTURE.
- LA FINITION INTÉRIEURE NE DOIT PAS ÊTRE RÉALISÉE LORS DES ESSAIS.

NOTES - FENÊTRES ET MURS RIDEAUX

(VOIR ÉGALEMENT DEVIS SECTIONS 08 52 00 ET 08 44 13)

- L'ENTREPRENEUR DEVRA VÉRIFIER LES DIMENSIONS DES FENÊTRES SUR PLACE EN TENANT COMPTE DE LA CONCEPTION DES DÉTAILS DE FENÊTRES/MURS RIDEAUX DANS CES MESURES (VOIR SÉRIE 500 DES PLANS D'ARCHITECTURE). FOURNIR LES DESSINS D'ATELIER SELON LES SECTIONS 08 52 00 ET 08 44 13 DU DEVIS D'ARCHITECTURE AVANT LA FABRICATION DE CES DERNIERS.
- TYPE DE VITRAGE: VOIR DEVIS, SECTION 08 80 50.
- LES DIMENSIONS DES FENÊTRES/MURS RIDEAUX SONT APPROXIMATIVES ET REPRÉSENTENT L'EXTÉRIEUR DES CADRES D'ALUMINIUM.
- LES FIXATIONS DES NOUVELLES FENÊTRES/MURS RIDEAUX DEVRONT RESPECTER LES EXIGENCES DU FABRICANT ET CELLES DU DEVIS D'ARCHITECTURE.
- LA PREMIÈRE FENÊTRE ET LE PREMIER MUR RIDEAUX DEVRONT ÊTRE INSTALLÉS OBLIGATOIREMENT EN COMPAGNIE DE L'ARCHITECTE À TITRE DE PROTOTYPE ET DE RÉFÉRENCE.
- CONSTRUIRE LES FAUX CADRES DES OUVERTURES D'ÉQUERRE ET D'APLOMB. AJUSTER LES FAUX-CADRES DE FAÇON À PERMETTRE L'ALIGNEMENT DES OUVERTURES, VERTICALEMENT ET HORIZONTALEMENT SUR LES FAÇADES.
- LAVÉES LES VITRAGES À LA FIN DES TRAVAUX, SELON LES PRESCRIPTIONS DE LA SECTION 08 52 00, ART. 3.5.

FENÊTRES:

- FOURNIR LES RAPPORTS D'ESSAIS EXIGÉS CONFORMES À LA NORME NAFS-11 ET AU SUPPLÉMENT CANADIEN CAS A44051-17 SELON L'ARTICLE 1.9 DE LA SECTION 08 52 00. VOIR LA SECTION DU DEVIS POUR LES CRITÈRES DE PERFORMANCE REQUIS DES FENÊTRES.
- L'INSTALLATEUR DES FENÊTRES DOIT FOURNIR TOUTES LES CALES D'AJUSTEMENT EN PVC (ÉPAISSEUR VARIABLE) POUR POSITIONNER CORRECTEMENT LES FENÊTRES, D'APLOMB ET DE NIVEAU. REMPLIR TOUS LES ESPACES VIDES D'URÉTHANE GICLÉ À FAIBLE EXPANSION.
- INSTALLER LES CALES D'AJUSTEMENT EN PVC, EN CONSERVANT UN ESPACE, CÔTÉS INTÉRIEUR ET EXTÉRIEUR POUR PERMETTRE D'AVOIR DE L'ISOLANT CONTINU DE POLYURÉTHANNE GICLÉ. LE JOINT DE SCELLANT ET LE BOUDIN PLACÉS DU CÔTÉ INTÉRIEUR DOIVENT ÊTRE CONTINUS. POSÉS SANS INTERRUPTION ET DE LARGEUR REQUISE SELON LES RECOMMANDATIONS DU FABRICANT.

NOTES

NE DOIT PAS SERVIR À L'EXÉCUTION

Le présent document est émis pour la seule fin identifiée. Son contenu est protégé par les droits d'auteur et toute reproduction ou modification, partielle ou totale, est interdite sans l'autorisation écrite de gagnon, letellier, cyr, ricard, mathieu, proulx, savard consortium d'architectes.




GLCRM | Proulx Savard |

GLCRM:
128, Avenue de la Cathédrale,
Bureau 201
Rimouski, QC, G5L 5H7
(418) 722-7655



2406, Ch. des Quatres-Bourgeois,
Bureau 100
Québec, QC, G1V 1W5
(418) 647-1700

Proulx Savard Architectes:
75, boul. Arthur-Buies Ouest,
Rimouski QC G5L 5C2
(418) 723-5543

ARCHITECTURE

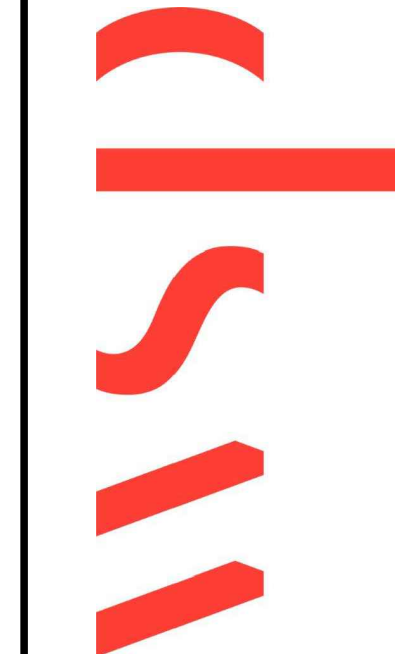

CONSULTANTS

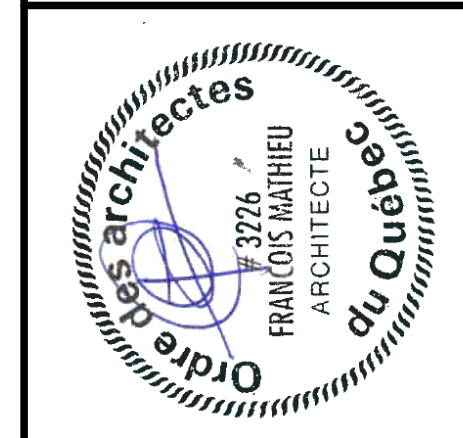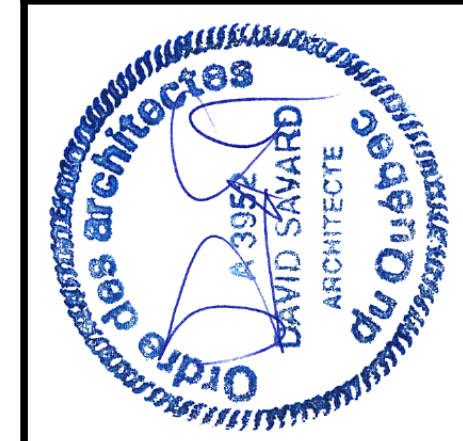

DESIGNÉ	DESIGNATEUR (S)	DOSSIER No.	DATE	ÉCHELLE	INDIQUÉE	DATE	RÉVISIONS
PROJET	HÔPITAL DE CHANDLER, Chandler (Refaction de l'enveloppe)	24-1087 / 6867-24	2024-09-04	05	04	03	02
PROPRIÉTAIRE	Santé Québec	24-1087 / 6867-24	2024-09-04	05	04	03	02

DESIGNÉ

MURS RIDEAUX

PROPRIÉTAIRE

PROPRIÉTAIRE

PROPRIÉTAIRE

PROPRIÉTAIRE