



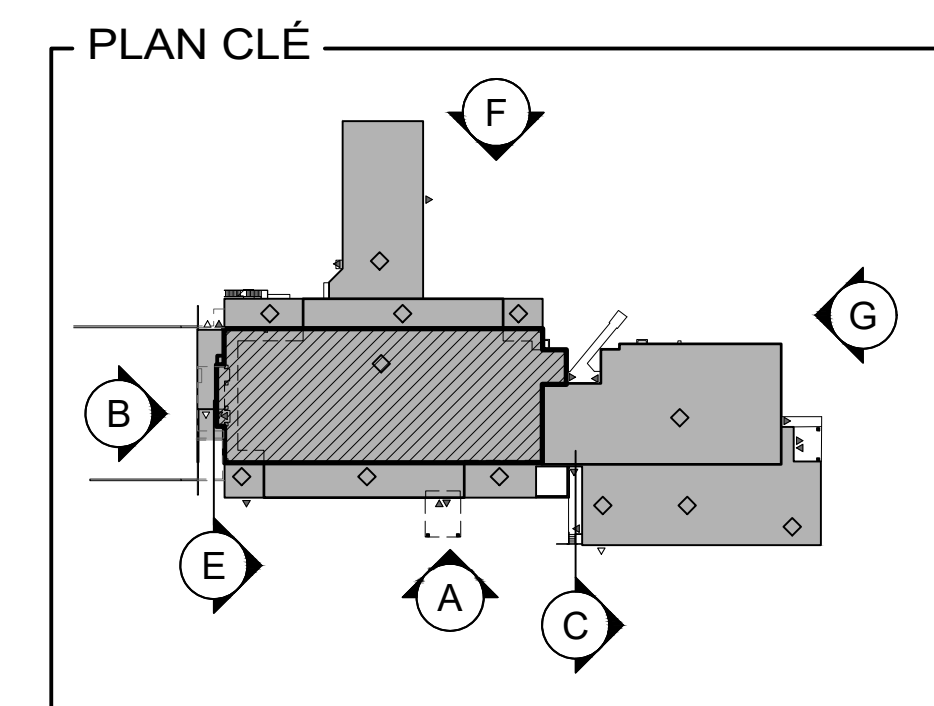


503


Le présent document est émis pour la seule fin identifiée. Son contenu est protégé par les droits d'auteur et toute reproduction ou modification, partielle ou totale, est interdite sans l'autorisation écrite de gagnon, letellier, cyr, ricard, mathieu, proulx, savard consortium d'architectes.

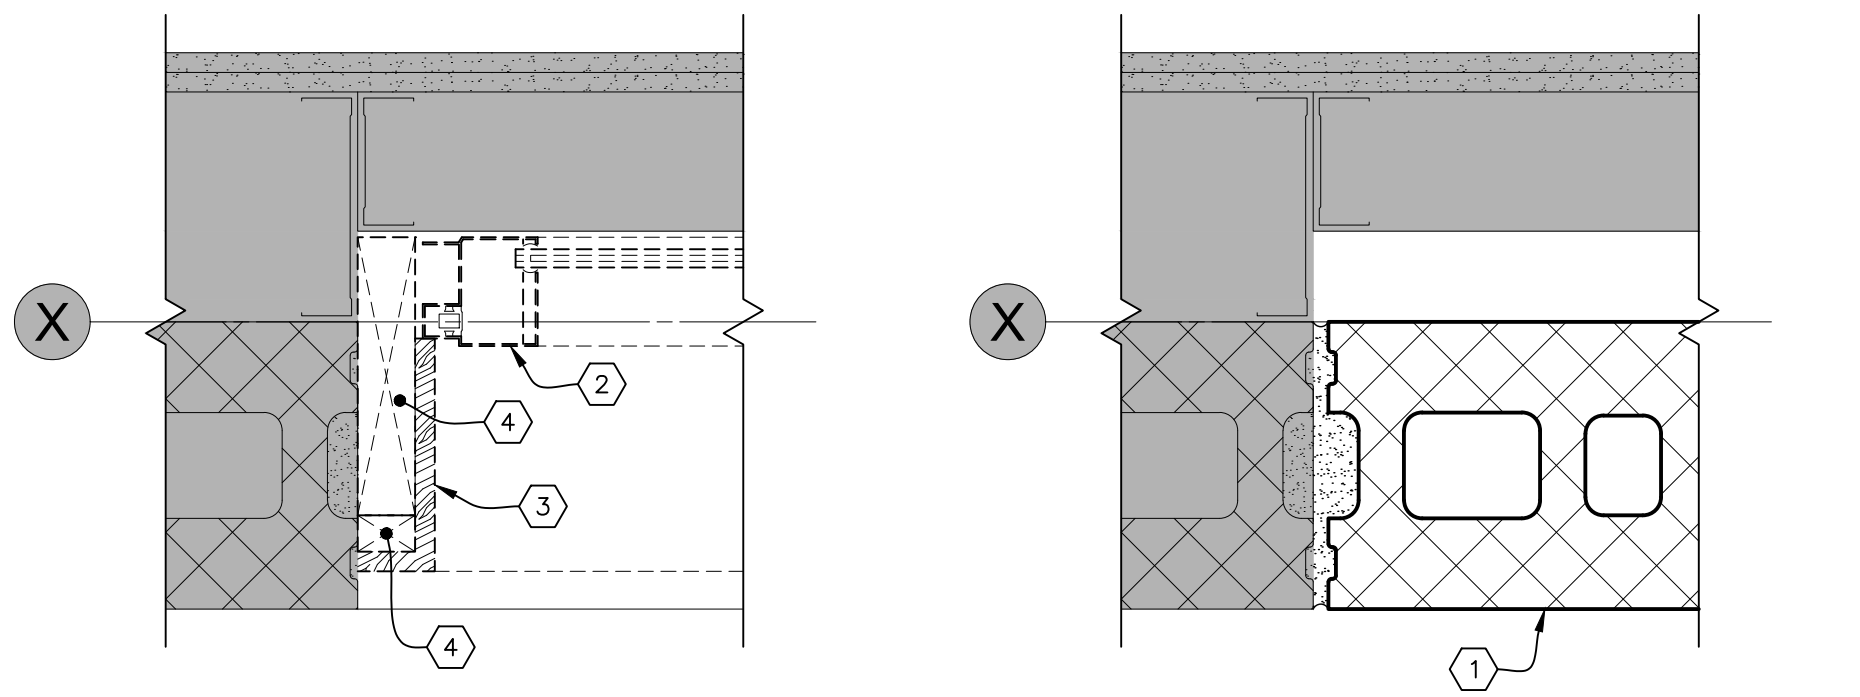

JAMBAGE

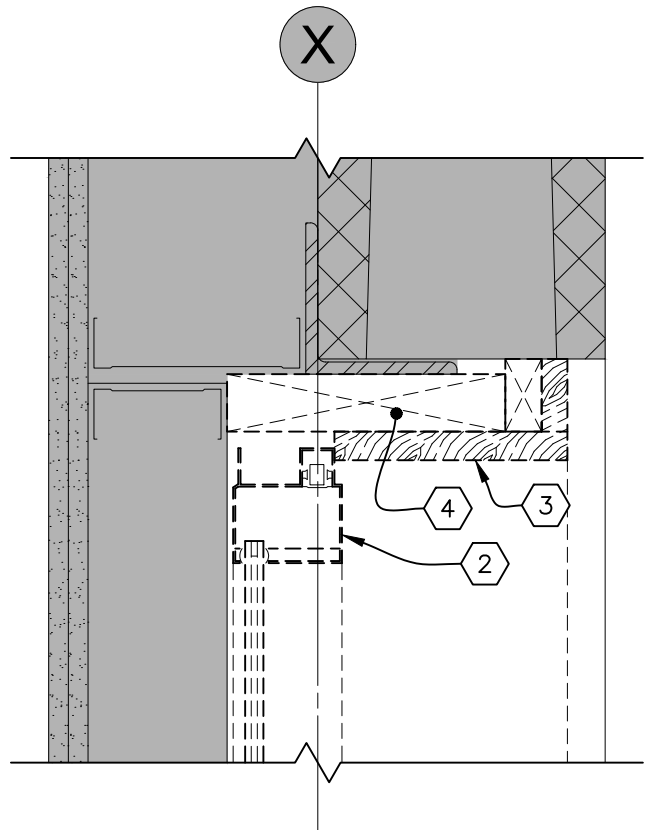

TÊTE

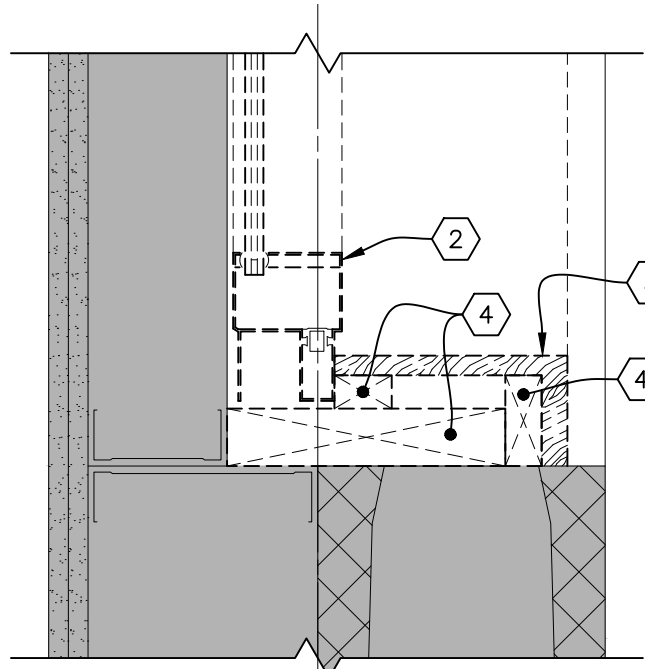


ALLÈGE

DÉMOLITION

1
052.103 | 504
1:5mm


DÉTAIL DE FENÊTRE À OBTURER
(NIVEAU 100)

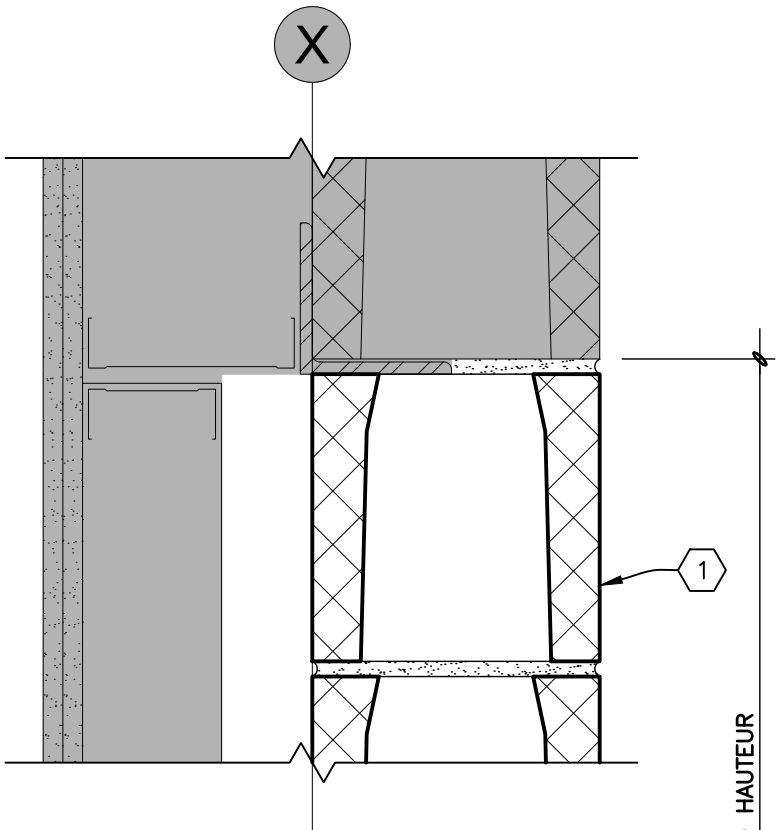


CONSTRUCTION

1
052.103 | 504
1:5mm


ALLÈGE

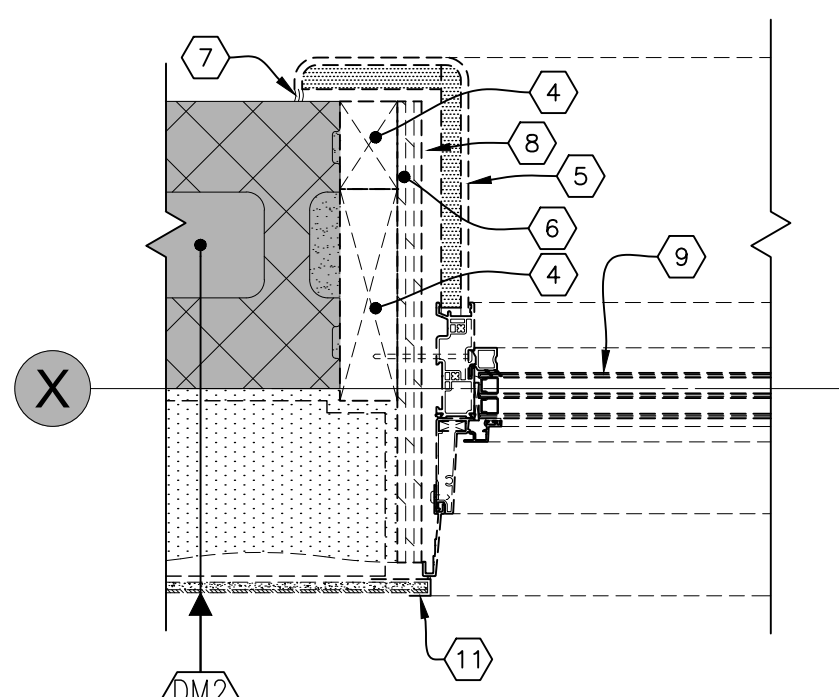

JAMBAGE

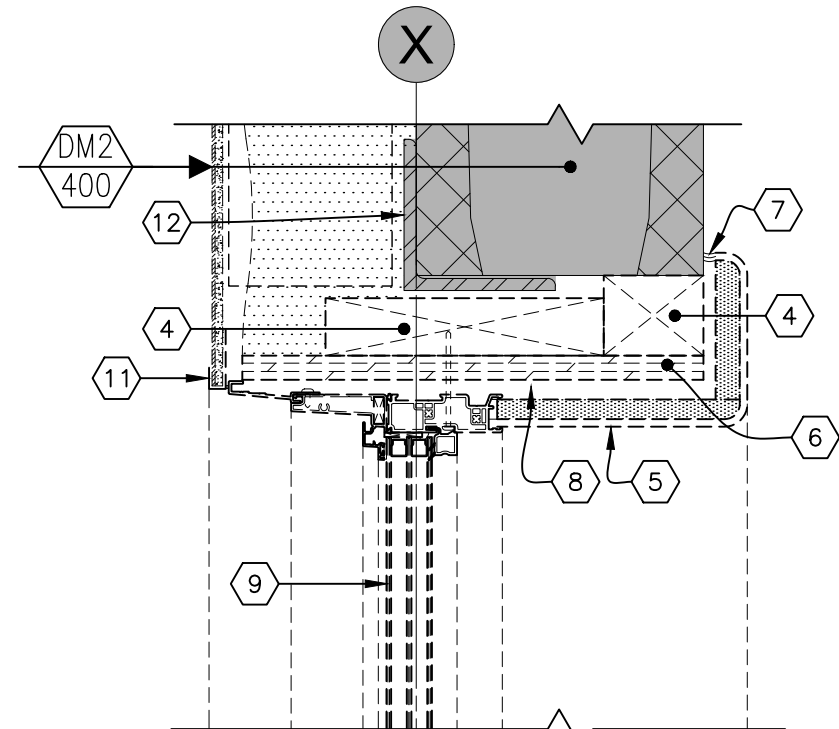

TÊTE

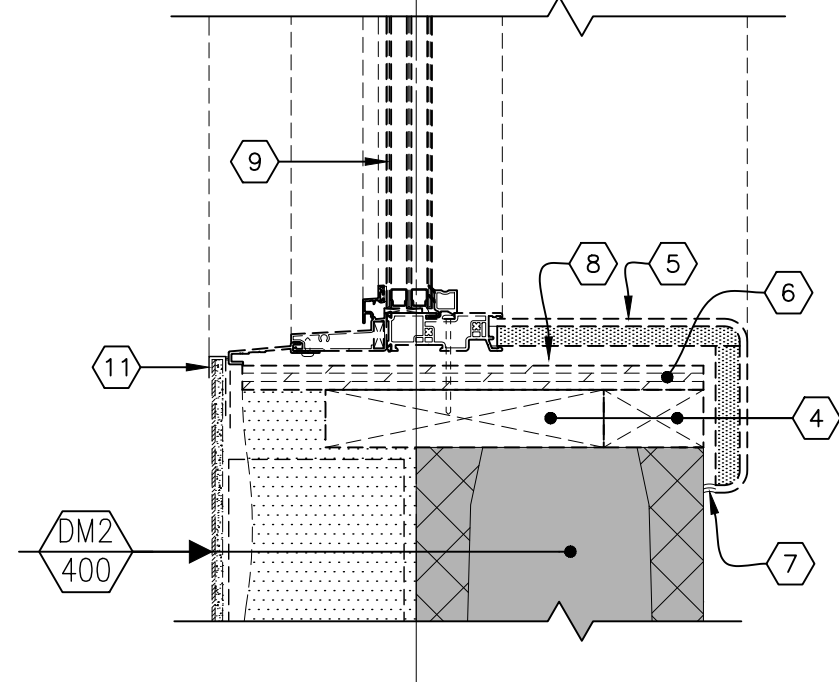


DÉMOLITION


2
502.503 | 504
1:5mm

DÉTAIL TYPE DE FENÊTRE À OBTURER
(NIVEAUX 200, 300 ET 400)


ALLÈGE

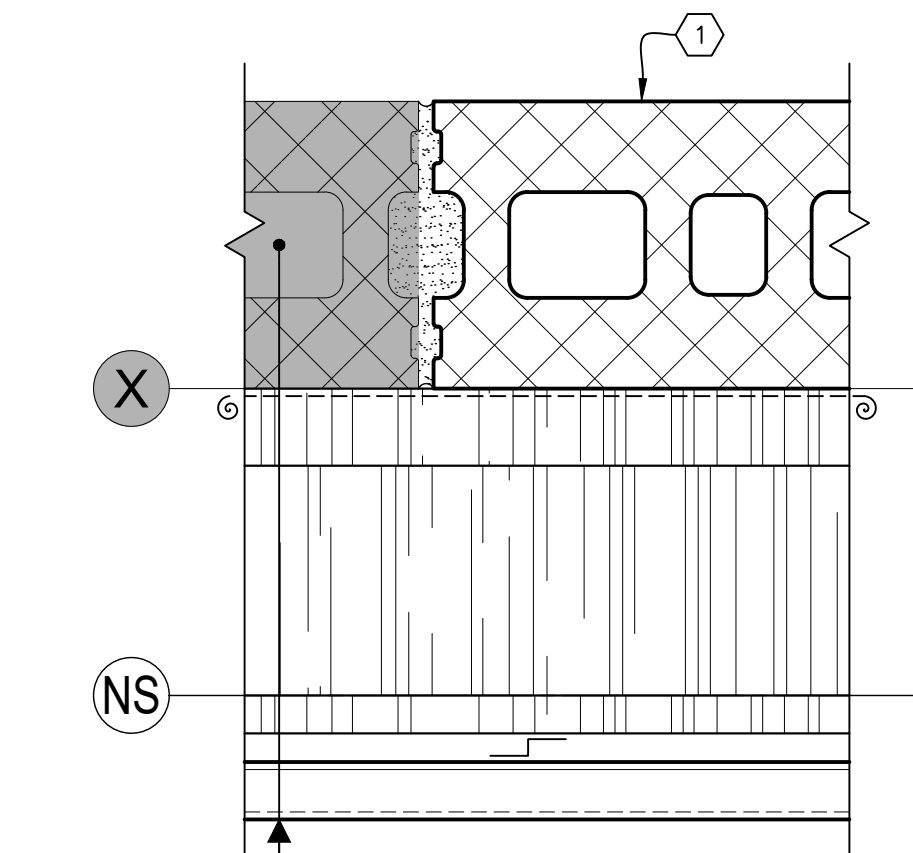

TÊTE

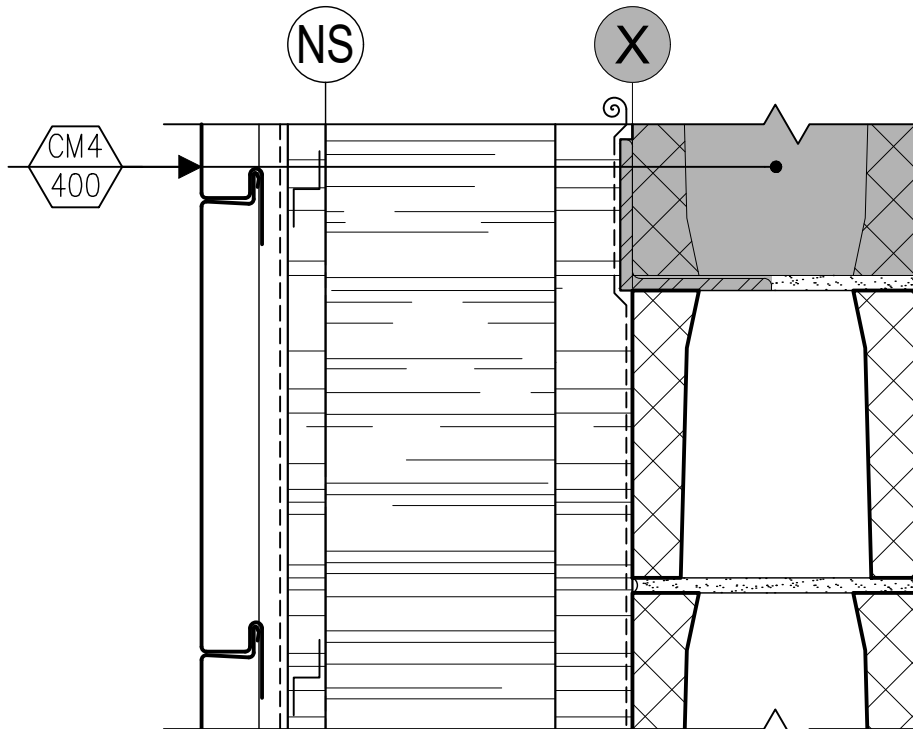


ALLÈGE

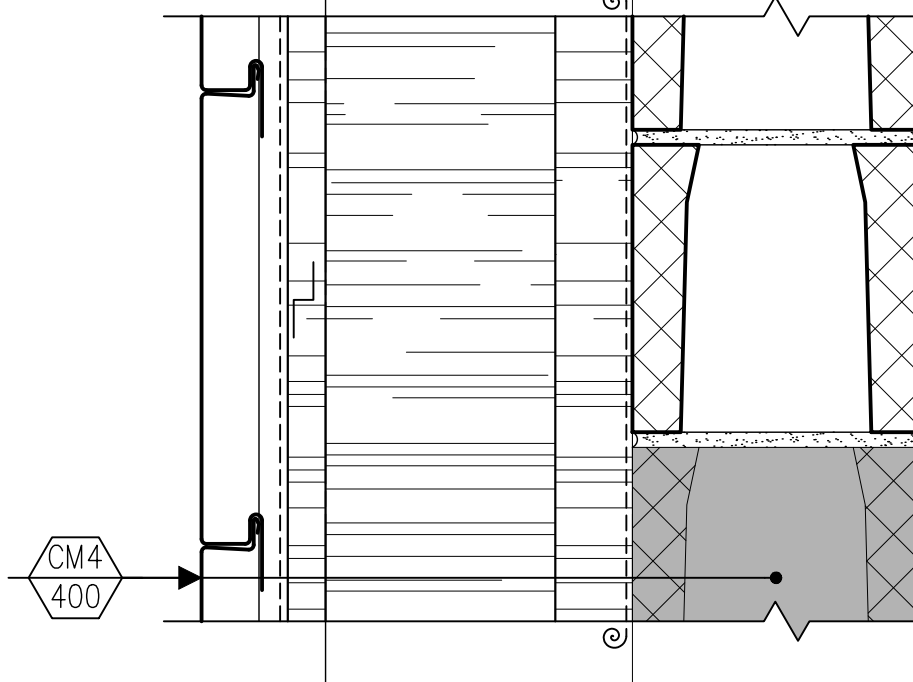

CONSTRUCTION


2
502.503 | 504
1:5mm

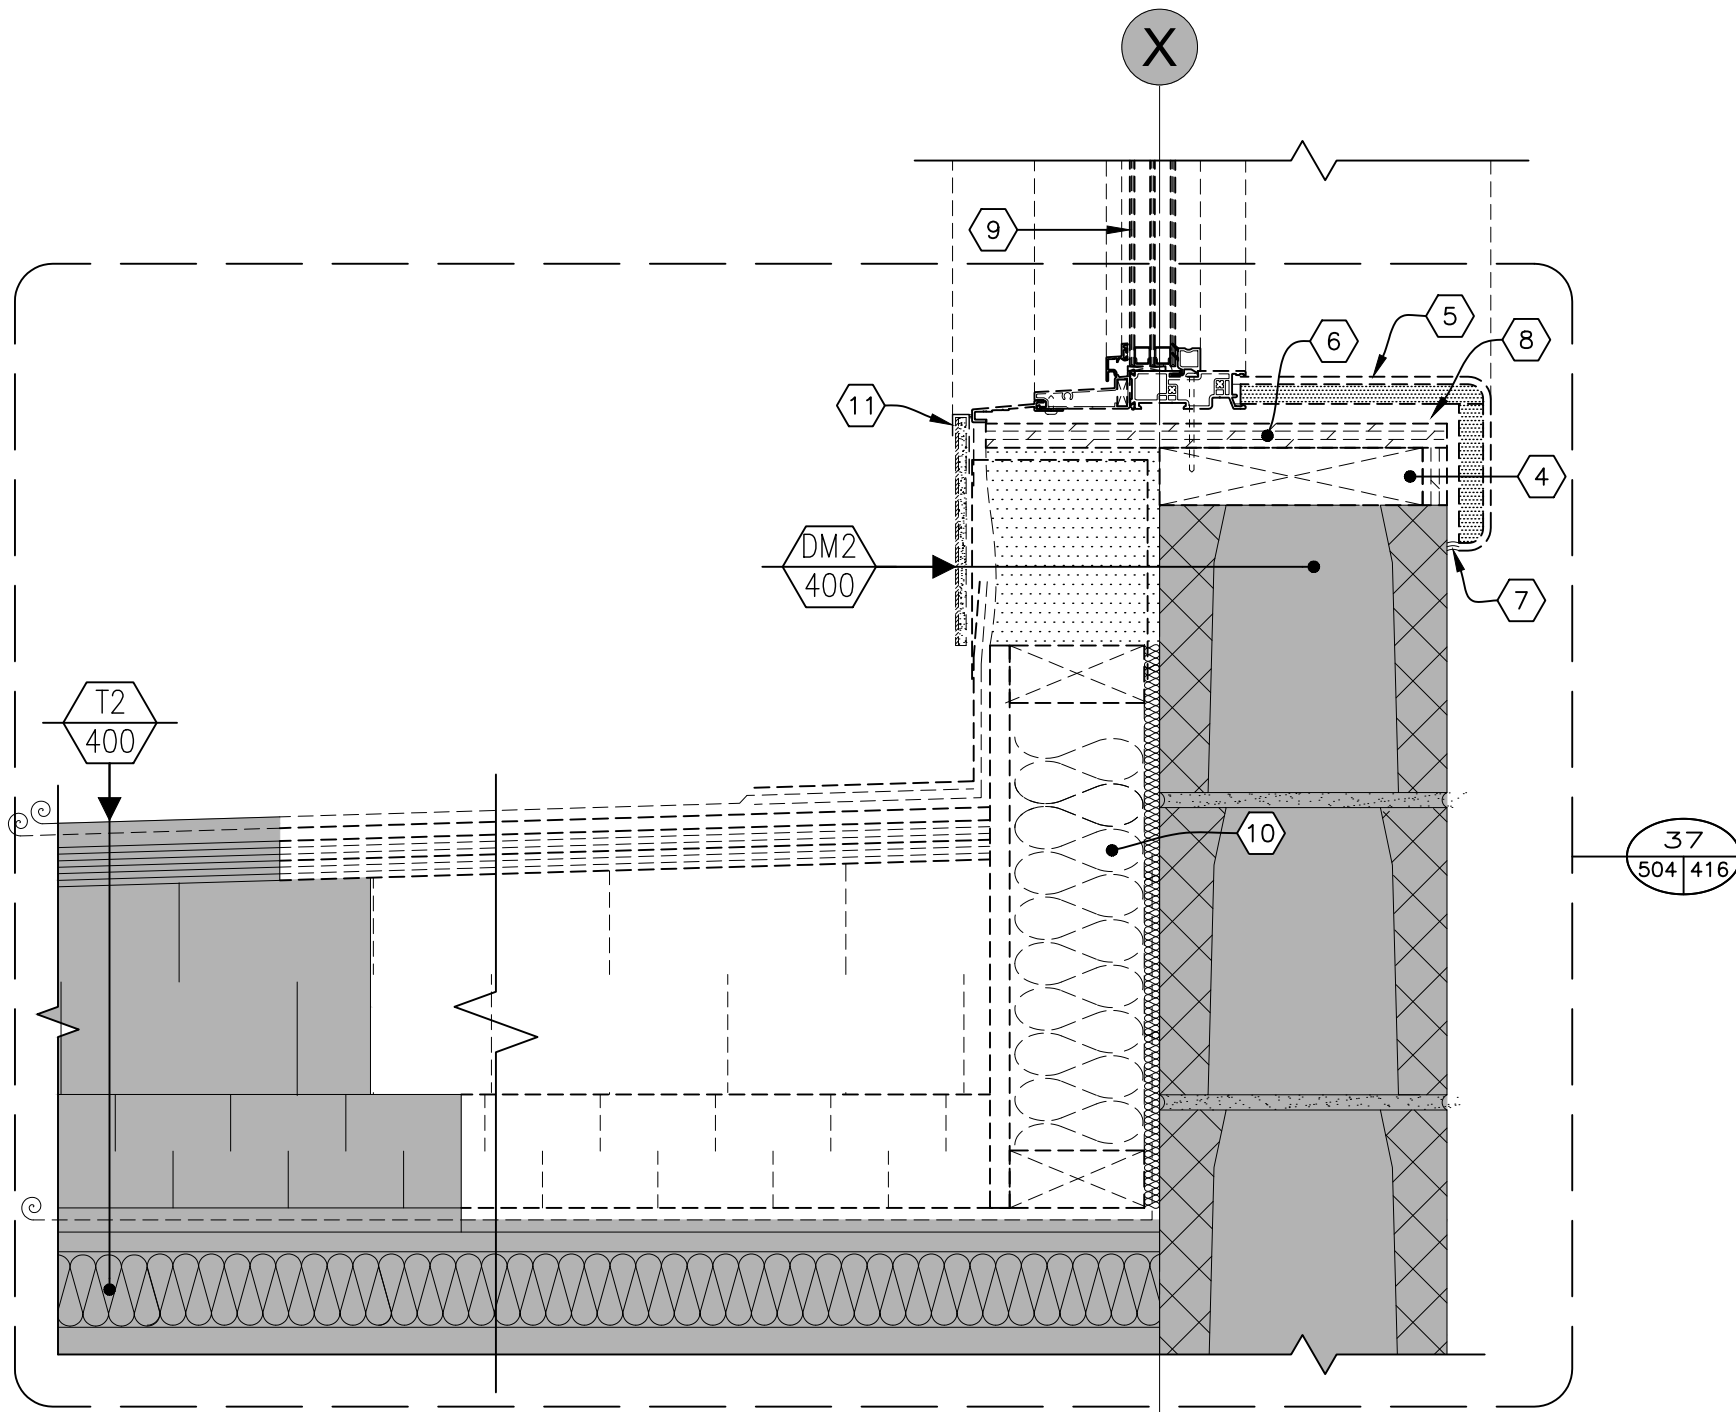

DÉMOLITION

3
502.503 | 504
1:5mm

DÉTAIL DE FENÊTRE À OBTURER
(NIVEAU 200)

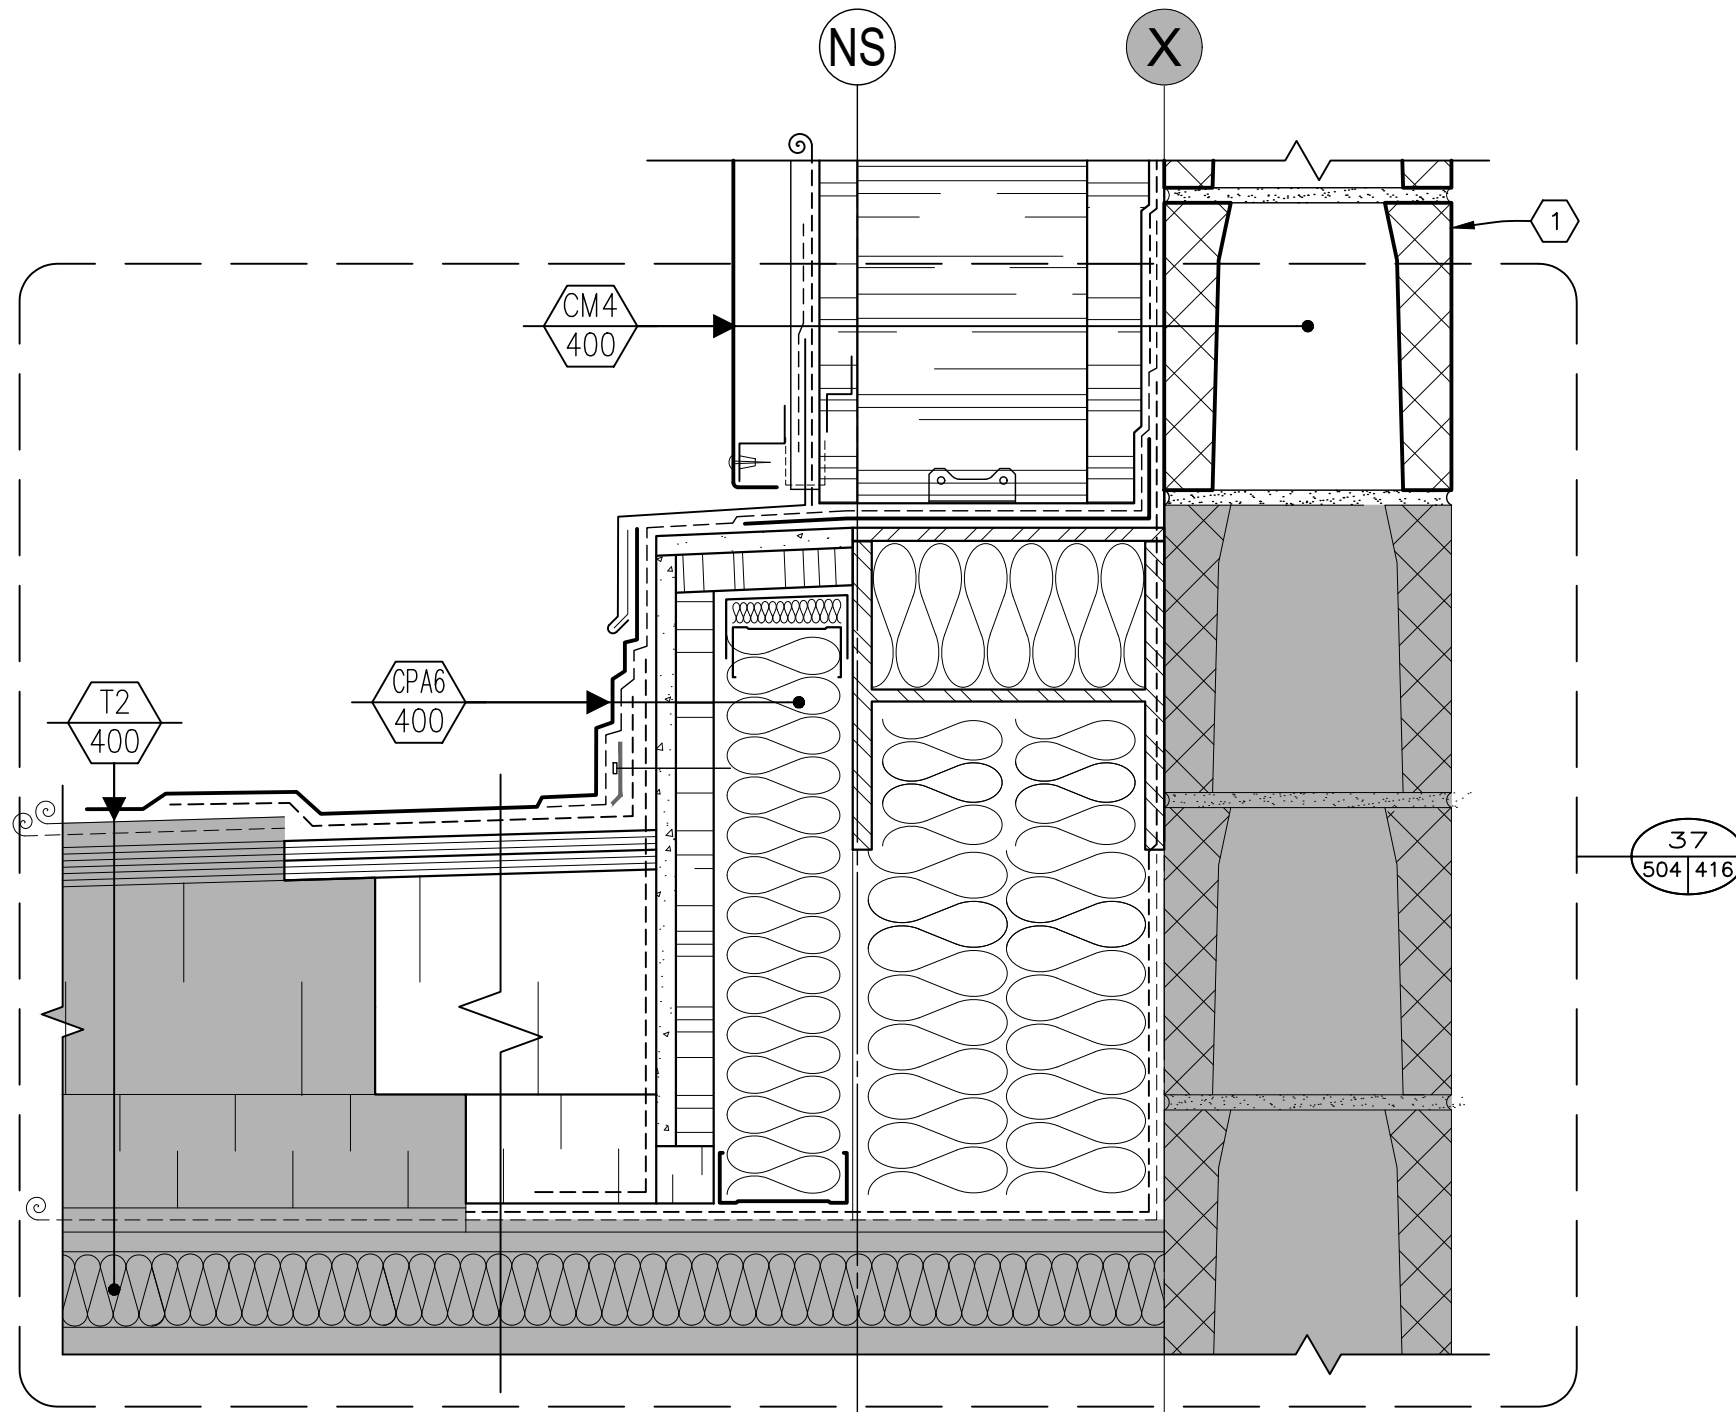

CONSTRUCTION

NOTES

- NOUVEAU BLOC DE MAÇONNERIE DE DIMENSION REQUISE. À PEINDRE.
- FENÊTRE EXISTANTE EN ALUMINIUM À ENLEVER.
- CADRE DE BOIS À ENLEVER.
- PIÈCE DE BOIS À DÉMOLIR.
- FINITION INTÉRIEURE EN CONTREPLAQUÉ RECOUVERT DE STRATIFIÉ À DÉMOLIR.
- CONTREPLAQUÉ EXISTANT À DÉMOLIR.
- SCELLANT EXISTANT À ENLEVER. NETTOYER LES SURFACES EXISTANTES CONSERVÉES DE TOUTES TRACES DE SCELLANT.
- MEMBRANE AUTOADHÉSIVE EXISTANTE À DÉMOLIR.
- FENÊTRE HYBRIDE (ALUMINIUM/PVC) EXISTANTE À DÉMOLIR.
- MURET EN COLOMBAGES DE BOIS Ø 400mm C/C. LAINE DE FIBRE DE VERRE ET CONTREPLAQUÉ À DÉMOLIR.
- MOULURE EN ALUMINIUM À DÉMOLIR.
- CORNÈRE EXISTANTE À CONSERVER.




GLCRM | Proulx Savard |

GLCRM:
178, Avenue de la Cathédrale,
Bureau 201
Rimouski, QC, G5L 5H7
(418) 722-7655


2406, Ch. des Quatres-Bourgeois,
Bureau 100
Québec, QC, G1V 1W5
(418) 647-1700

Proulx Savard Architectes:
75, boul. Arthur-Buies Ouest,
Rimouski QC G5L 5C2
(418) 723-5543

ARCHITECTURE

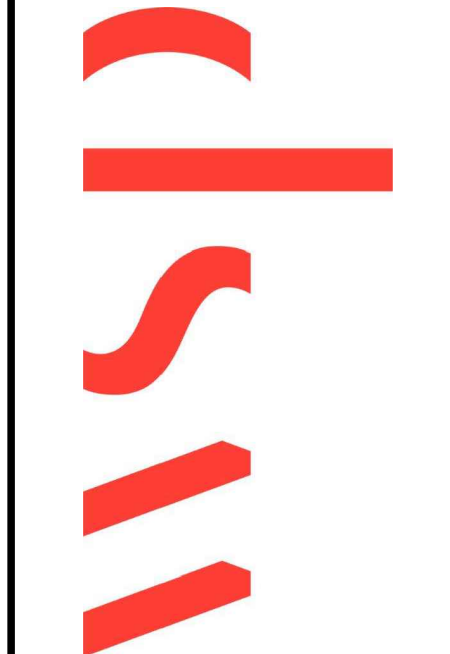

CONSULTANTS

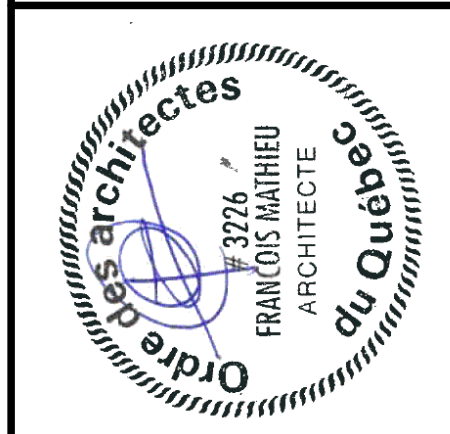

DESIGNATEUR (S)	DOSSIER NO.	DATE	REVISIONS
DB: ALL	24-1087 / 1687-24	SEPTEMBRE 2024	
ÉCHELLE			
INDIQUÉE			
05	2024-09-04	DÉFINITIVES POUR SOUMISSION	
06	2024-08-21	DÉFINITIVES 100% POUR APPROBATION	
03	2024-08-03	DÉFINITIVES 80% POUR APPROBATION	
02	2024-05-14	DÉFINITIVES 40% POUR APPROBATION	
01	2024-02-27	PRÉLIMINAIRES 20% POUR APPROBATION	
No	DATE		


DESIGN	PROJET	PROPRIÉTAIRE
DÉTAIL DE FENÊTRE (CAGE D'ESCALIER #3)	HÔPITAL DE CHANDLER, Chandler (Réfection de l'enveloppe)	Santé Québec
DÉMOLITION ET CONSTRUCTION		

LÉGENDE


- EXISTANT À CONSERVER.
- ÉLÉMENT À DÉMOLIR.
- AXE EXISTANT
- EX
- EXTÉRIEUR DE LA STRUCTURE DE BÉTON EXISTANTE DE LA TOUR.
- NS
- NOUVEL AXE: FACE EXTÉRIEURE DES BARRES Z ET COLOMBAGES DE LA TOUR. VOIR STRUCTURE.
- (*) VOIR NOTE GÉNÉRAL PAGE 400.

NE DOIT PAS SERVIR À L'EXÉCUTION


Le présent document est émis pour la seule fin identifiée. Son contenu est protégé par les droits d'auteur et toute reproduction ou modification, partielle ou totale, est interdite sans l'autorisation écrite de gagnon, letellier, cyr, ricard, mathieu, proulx, savard consortium d'architectes.

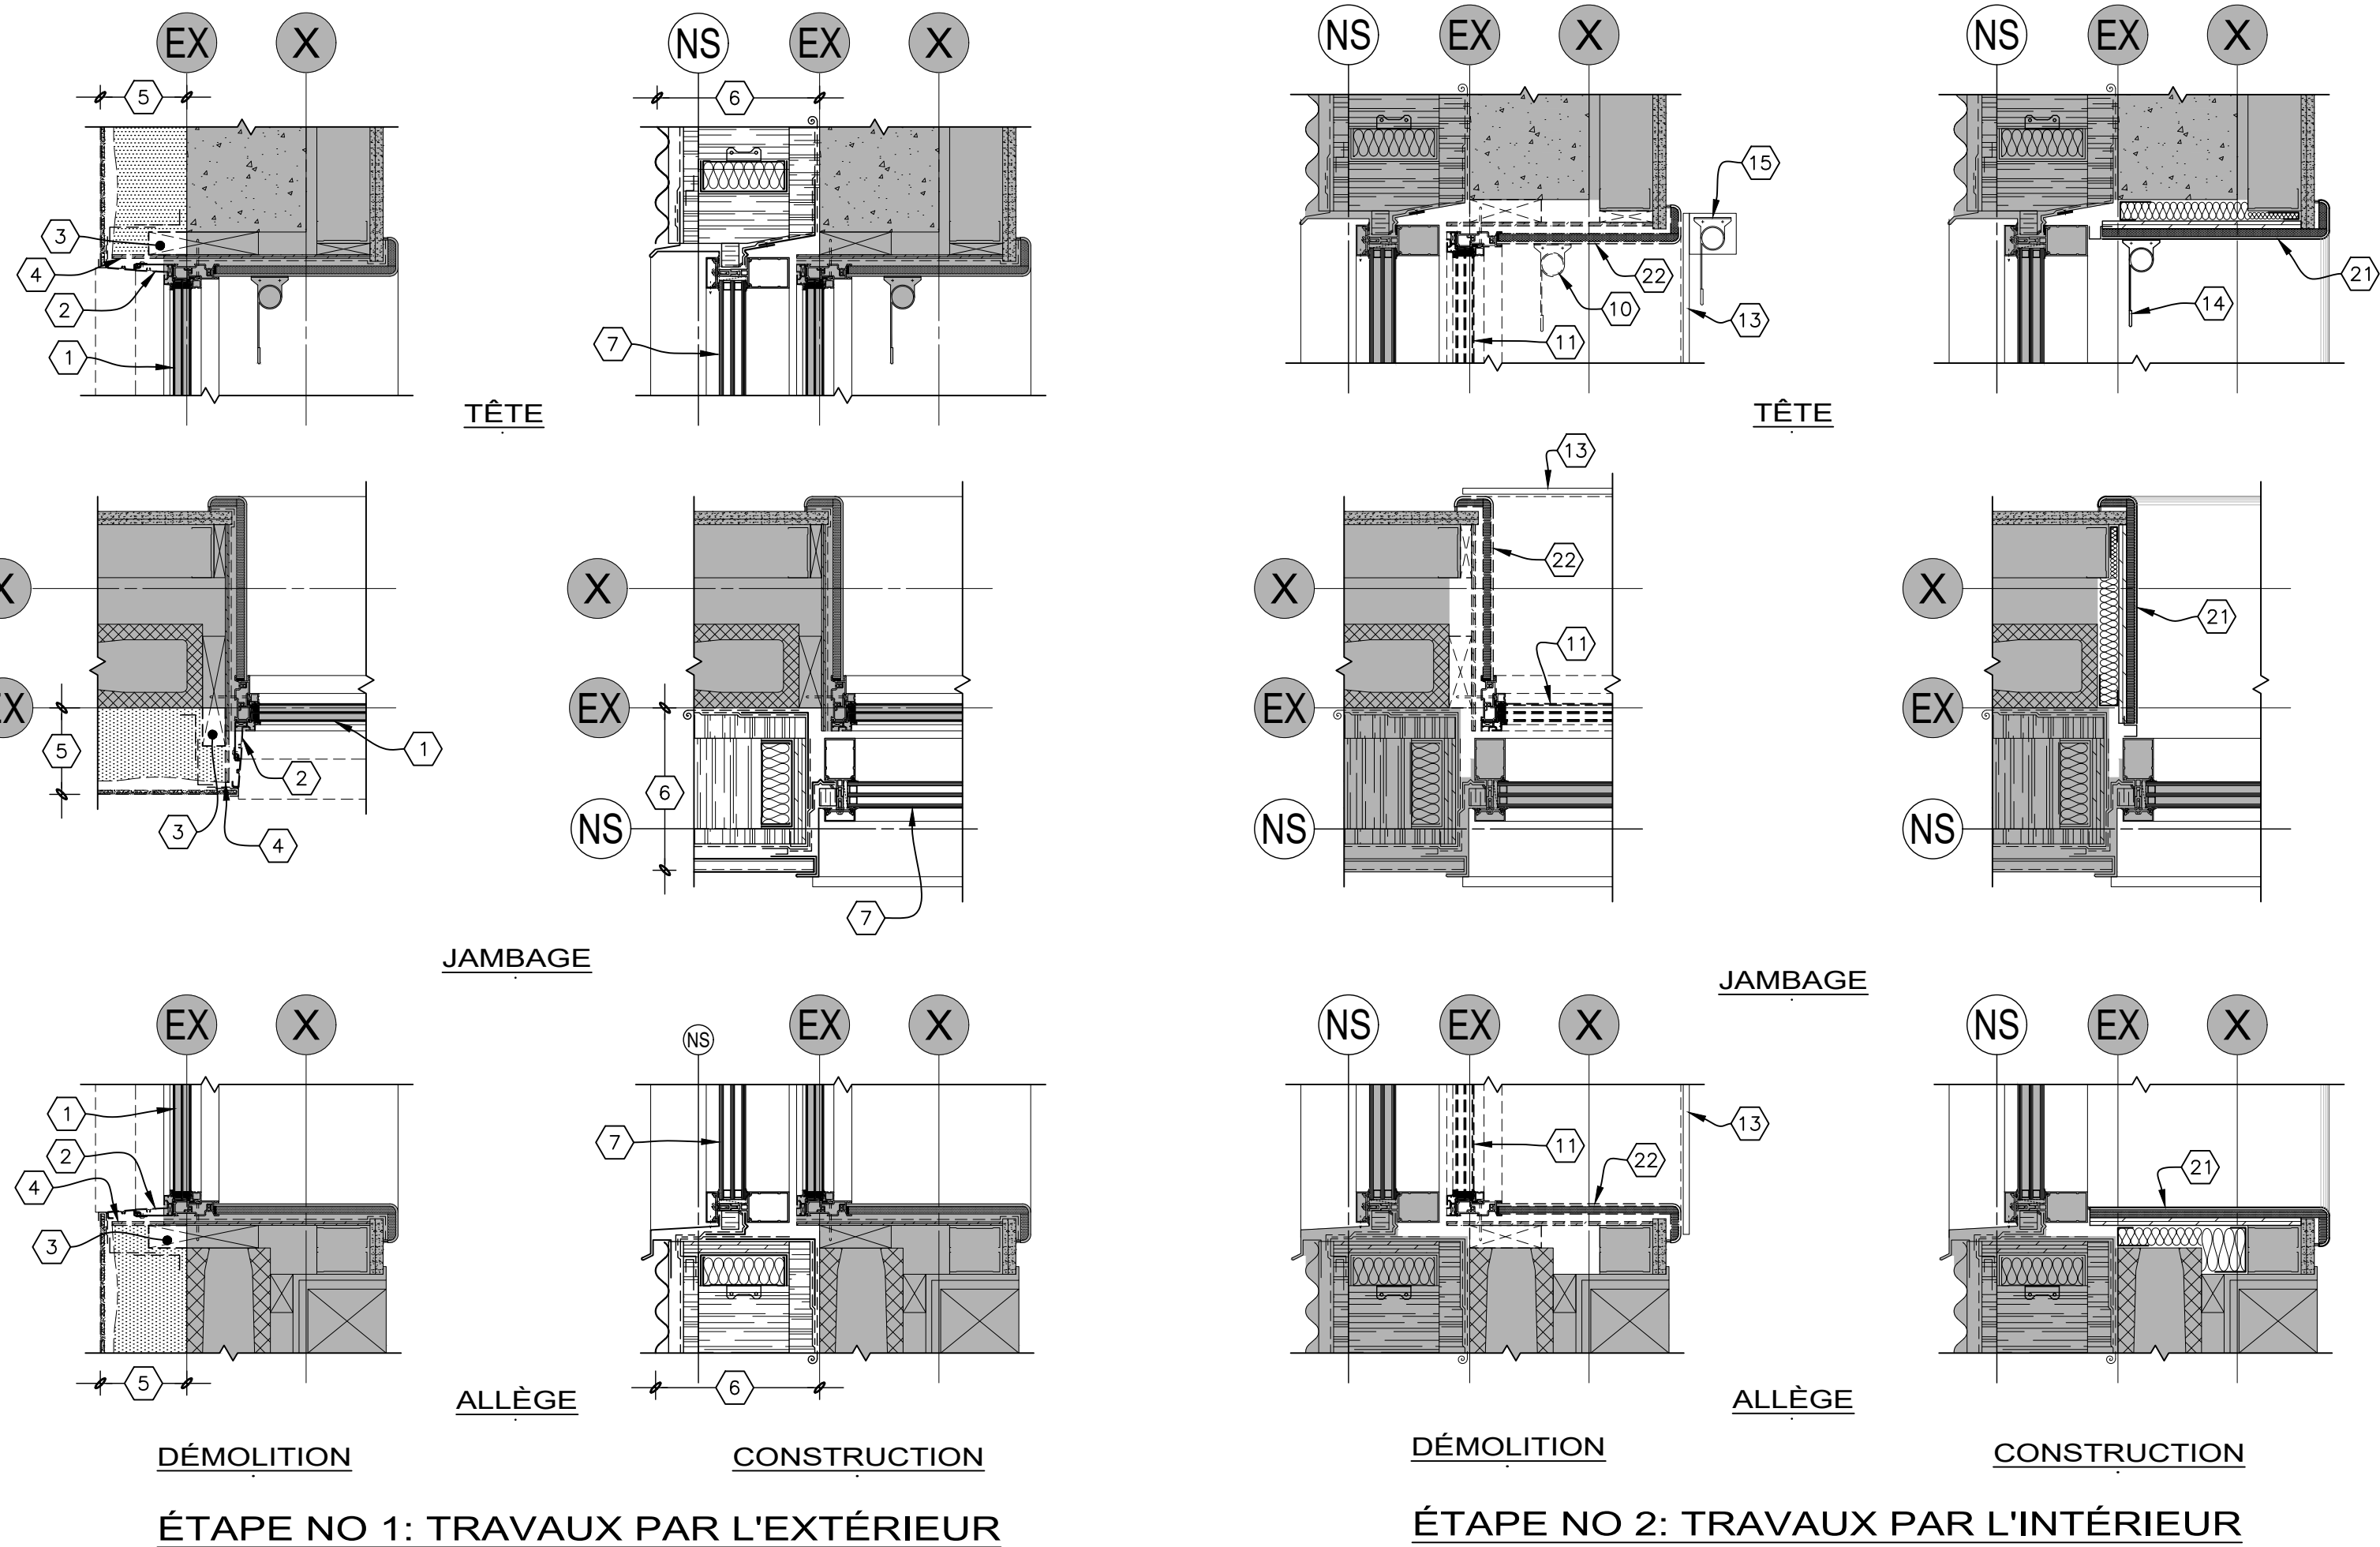

A
502,503 505
PRINCIPE DE REMPLACEMENT DES FENÊTRES DE LA TOUR
1:10mm
(NIVEAUX 200, 300 ET 400 - BLOCS DE BÉTON)

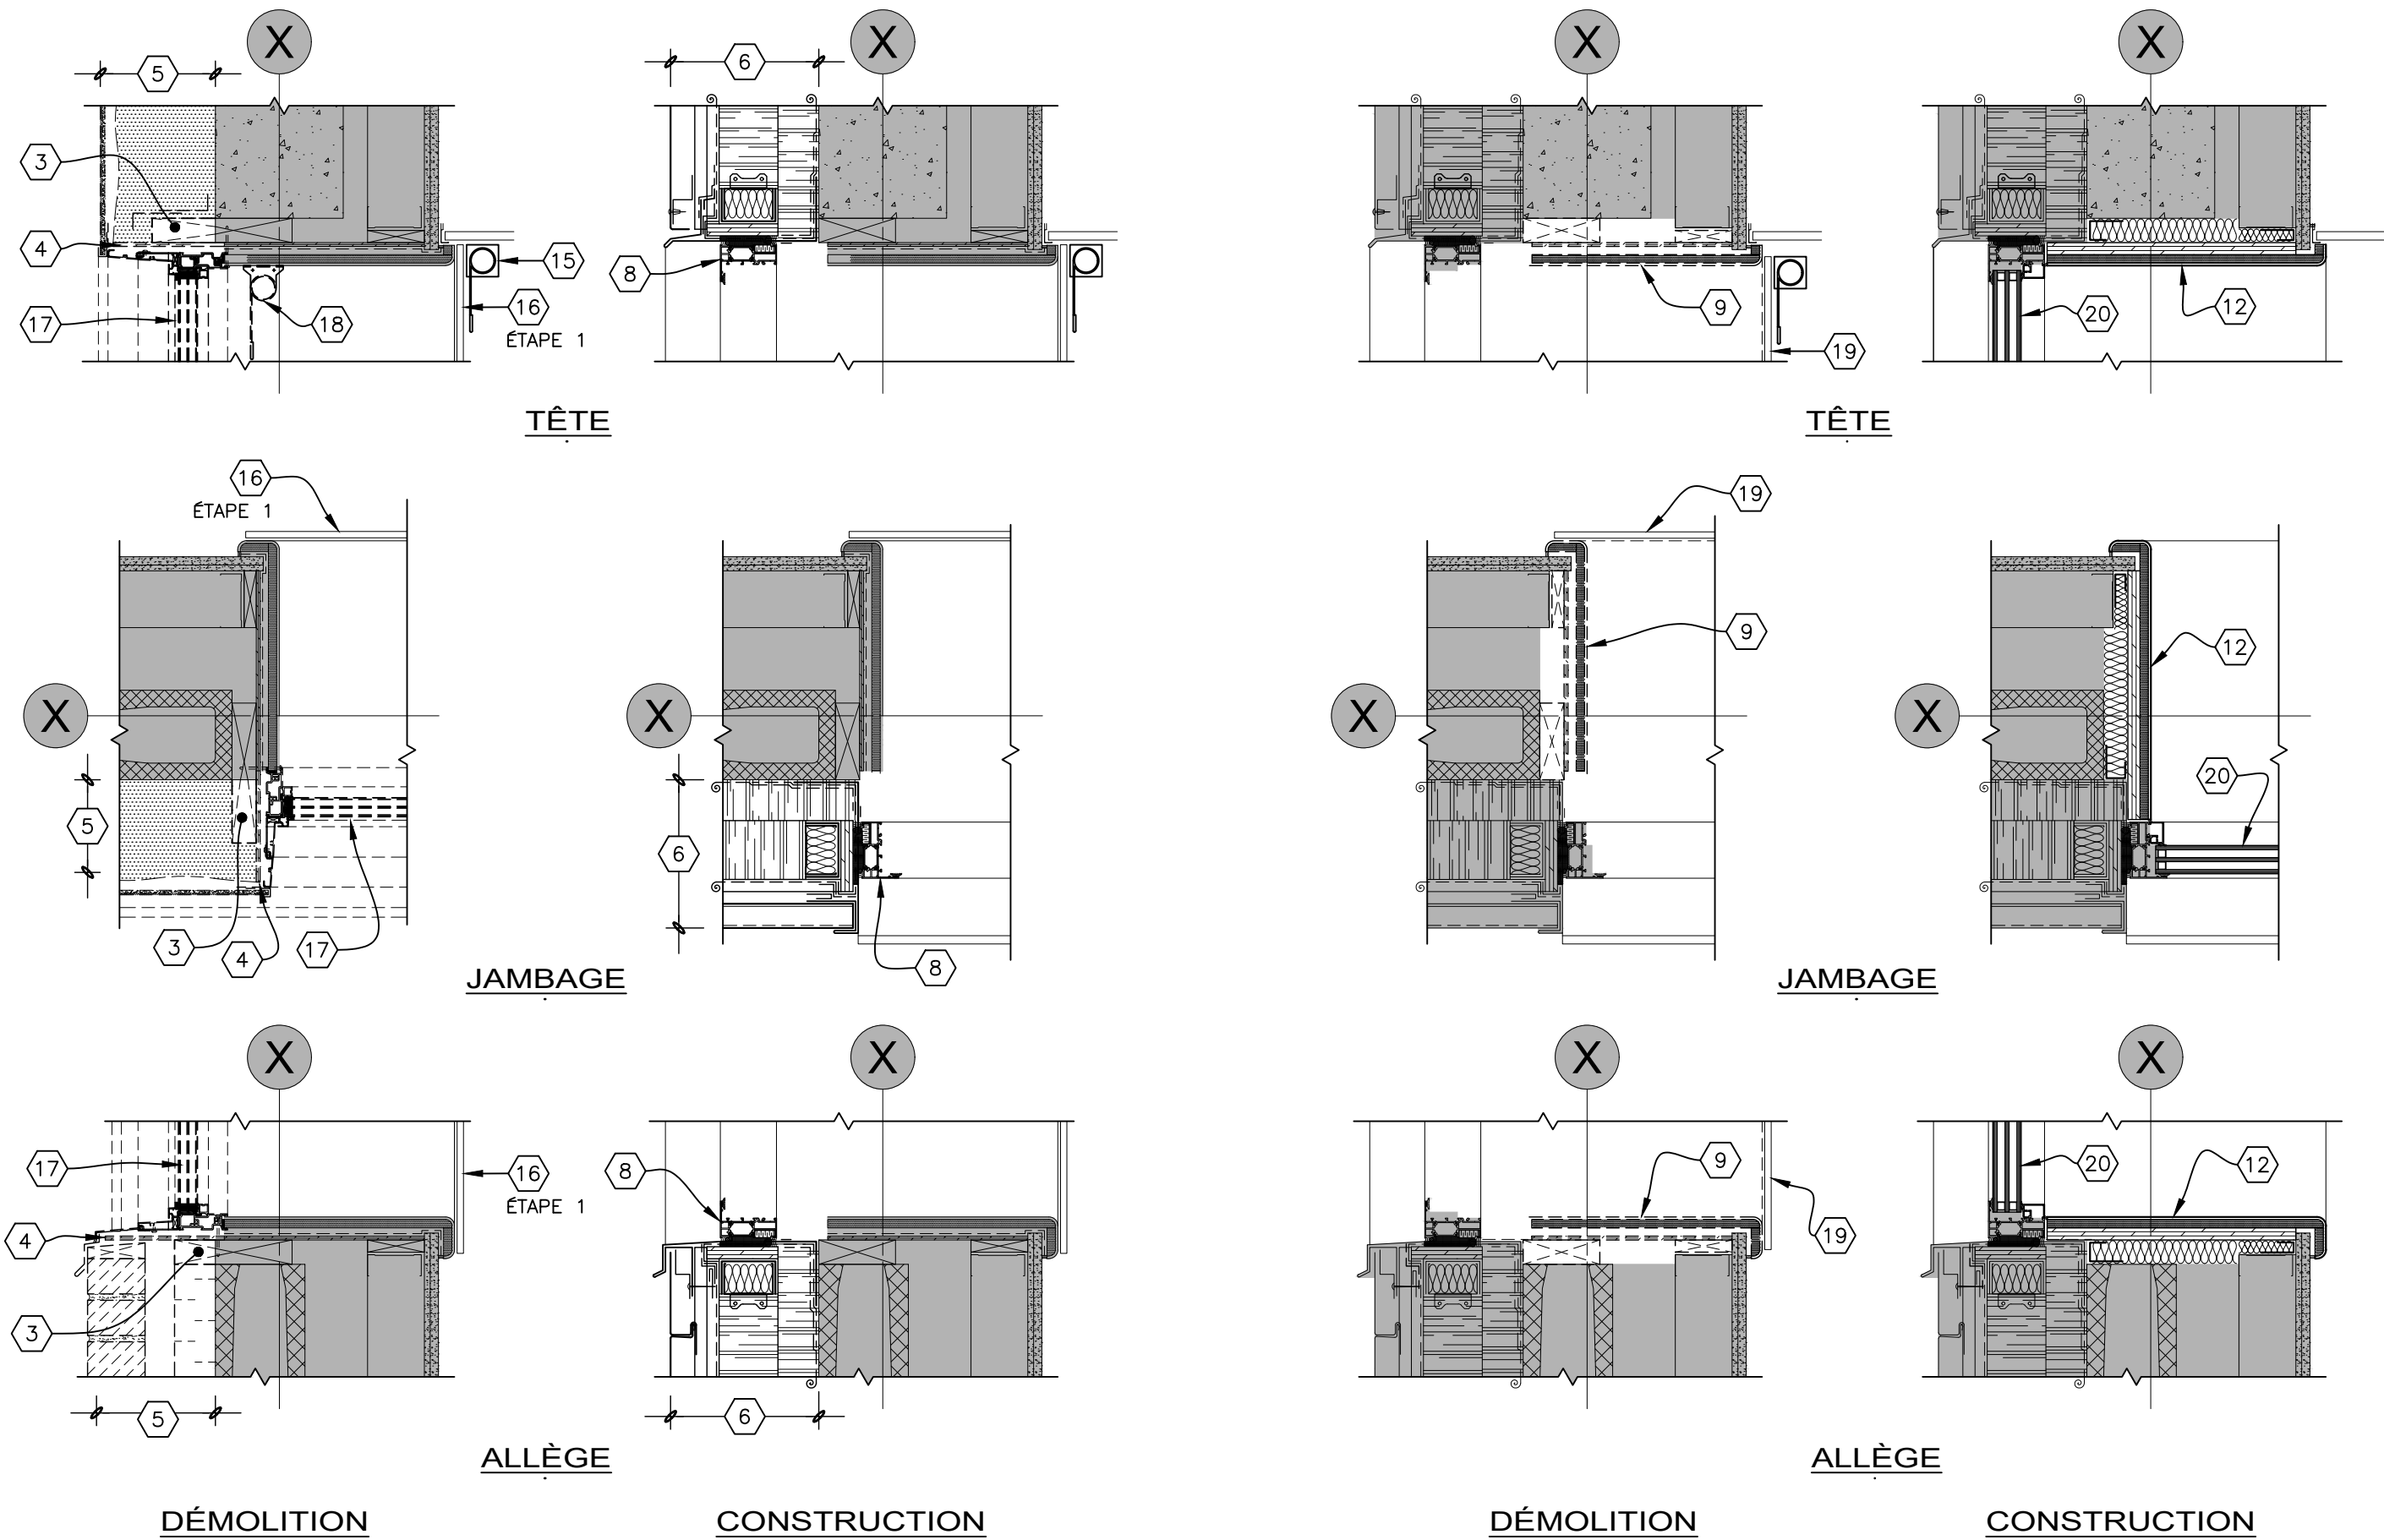

B
502,503 505
PRINCIPE DE REMPLACEMENT DES FENÊTRES DU BASILAIRE
1:10mm
(NIVEAU RDC - BLOCS DE BÉTON - EXCLUANT SECTEUR IRM)

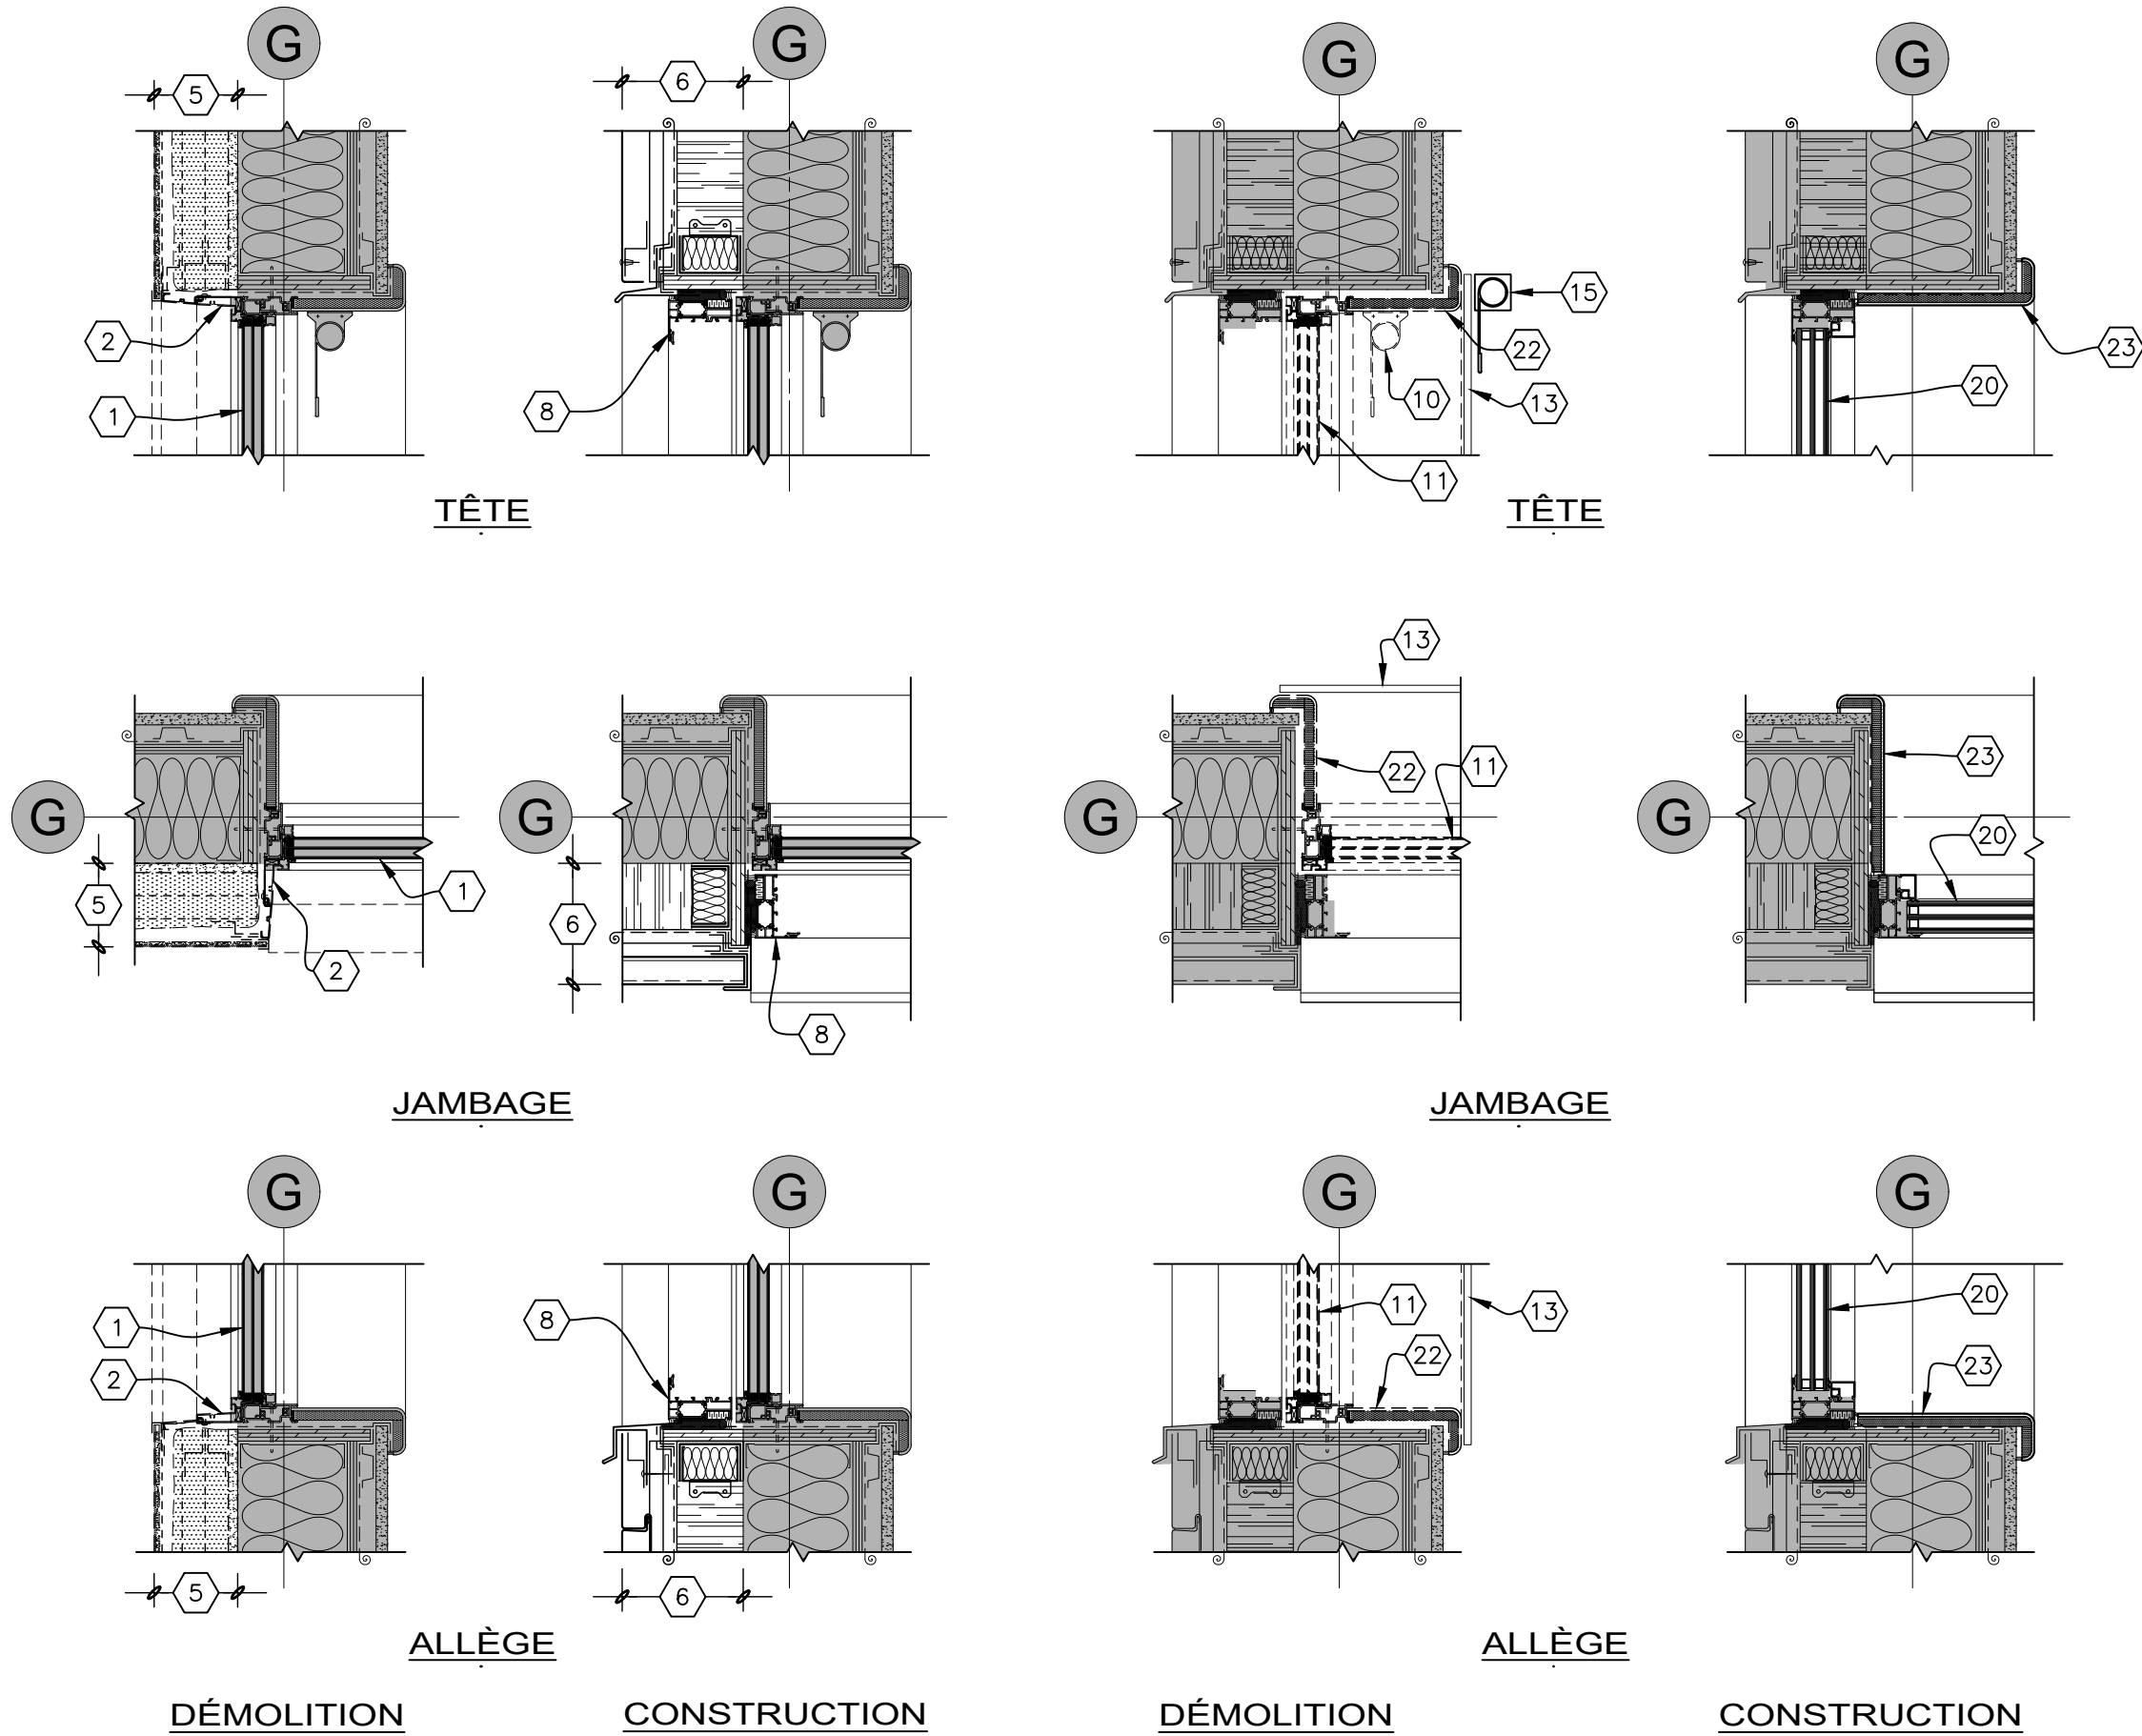

C
502,503 505
PRINCIPE DE REMPLACEMENT DES FENÊTRES DU BASILAIRE
1:10mm
(COLOMBAGES MÉTALLIQUES - SECTEUR IRM ET NIVEAU 100)

NOTE - FENÊTRES EXISTANTE

LES FENÊTRES SONT FIXÉS AU FAUX-CADRE EN CONTREPLAQUÉ À L'AIDE DE DEUX (2) ATTACHES MÉTALLIQUES SITUÉES SUR LES JAMBAGES DE L'OUVERTURE.

NOTES - PLEXIGLASS

APRÈS LE RETRAIT DE L'ENCADREMENT DE LA FINITION INTÉRIEURE EN PÉRIPHÉRIE DE L'OUVERTURE, DE LA TOILE SOLAIRE ET DE LA FENÊTRE, FOURNIR ET INSTALLER UN PANEAU DE PLEXIGLASS FIXÉ AU POURTOUR DE L'OUVERTURE JUSQU'AU MOMENT DE L'INSTALLATION DE LA NOUVELLE FINITION INTÉRIEURE. APPLIQUER UN RUBAN AUTOCOLLANT 2 CÔTÉS AU POURTOUR DE L'OUVERTURE AVANT L'INSTALLATION DES PANEaux DE PLEXIGLASS. REINSTALLER L'HABILLAGE DE LA FENÊTRE (TOILE OU STORE) TEMPORAIREMENT.

POUR LES FENÊTRES DU RDC ET LES 11 FENÊTRES IDENTIFIÉES PAR LA NOTE #4 SUR LA PAGE 502, DE NOVEMBRE À AVRIL, UN BATI ISOLÉ EN REMPLACEMENT DU PANEAU DE PLEXIGLASS EST REQUIS POUR LA DURÉE DES TRAVAUX À EFFECTUER PAR L'EXTÉRIEUR.

NOTE - FINITION INTÉRIEURE EXISTANTE EN PÉRIPHÉRIE DES FENÊTRES

LA FINITION DE STRATIFIÉ EXISTANTE EST PRÉ-ASSEMBLÉE (4 CÔTÉS) EN UN (1) SEUL MORCEAU AVANT SA MISE EN PLACE DANS L'OUVERTURE. ELLE A ÉTÉ COLLÉE AVEC DU SILICONE ET CLOUS DE FINITION. ELLE SE RETIRE EN UN (1) SEUL MORCEAU EN EXERÇANT UNE PRESSION À L'AIDE D'UN OUTIL SUR LES 4 CÔTÉS.

NOTES - THERMOS ET FINITION

APPLICABLE AU DÉTAIL B SEULEMENT

L'INSTALLATION DU THERMOS, CÔTÉ INTÉRIEUR, DEVRA ÊTRE RÉALISÉ EN MÊME TEMPS QUE LA DÉMOLITION DE LA FINITION INTÉRIEUR, PAR LA SUITE, LA POSE DU PANEAU DE PLEXIGLASS EST REQUISE JUSQU'AU MOMENT DE LA RÉALISATION DES TRAVAUX PAR L'ÉBÉNISTE.

APPLICABLE AU DÉTAIL C SEULEMENT

L'INSTALLATION DU THERMOS ET LA PRÉPARATION, CÔTÉ INTÉRIEUR, DEVRONT ÊTRE RÉALISÉ IMMÉDIATEMENT APRÈS LA DÉMOLITION DE LA FENÊTRE EXISTANTE PAR L'INTÉRIEUR. PAR LA SUITE, LA POSE DU PANEAU DE PLEXIGLASS EST REQUISE JUSQU'AU MOMENT DE LA RÉALISATION DES TRAVAUX PAR L'ÉBÉNISTE. APPLICABLE AU DÉTAIL C SEULEMENT.

NOTE - TOILE SOLAIRE

EN TOUT TEMPS, UNE TOILE SOLAIRE DEVRA ÊTRE INSTALLÉE ET OPÉRATIONNELLE DANS LES CHAMBRES. INSTALLER UN DISPOSITIF DE FIXATION SUR LE PANEAU DE PLEXIGLASS.

NOTES

- FENÊTRE EXISTANTE À CONSERVER LORS DE L'ÉTAPE 1.
- COUPER CETTE SECTION DU CADRE DE FENÊTRE À L'ÉTAPE 1, S'ASSURER QUE LE VERRE RESTE SOLIDEMENT EN PLACE.
- PIÈCE DE BOIS À COUPER À L'ÉTAPE 1.
- CONTREPLAQUÉ À COUPER À L'ÉTAPE 1.
- PAREMENT ET ISOLATION À DÉMOLIR À L'ÉTAPE 1. VOIR DÉTAILS DES PAGES SUIVANTES POUR LES COMPOSITIONS EXACTES.
- NOUVEAUX PAREMENTS ET ISOLATION À L'ÉTAPE 1. VOIR DÉTAILS DES PAGES SUIVANTES POUR LES COMPOSITIONS EXACTES.
- NOUVEAU MUR-RIDEAU À L'ÉTAPE 1.
- NOUVEAU CADRAGE DE FENÊTRE À L'ÉTAPE 1.
- FINITION INTÉRIEURE DE STRATIFIÉ À DÉMOLIR À L'ÉTAPE 3.
- TOILE SOLAIRE EXISTANTE À ENLEVER À L'ÉTAPE 2, VOIR NOTE GÉNÉRAL SUR CETTE PAGE.
- FENÊTRE EXISTANTE À DÉMOLIR À L'ÉTAPE 2.
- NOUVELLE FINITION EN PÉRIPHÉRIE DE LA FENÊTRE À L'ÉTAPE 3, VOIR NOTE "FINITION INTÉRIEURE" SUR CETTE PAGE.
- PANEAU DE PLEXIGLASS À INSTALLER TEMPORAIREMENT SUR L'OUVERTURE APRÈS LA DÉMOLITION DE LA FENÊTRE ET DU CADRAGE ET À RETIRER POUR L'INSTALLATION DE LA NOUVELLE FINITION INTÉRIEURE. VOIR NOTE "PLEXIGLASS" SUR CETTE PAGE.
- NOUVELLE TOILE SOLAIRE, VOIR NOTE HABILLAGE DE FENÊTRE PAGE 501.
- INSTALLATION TEMPORAIRE DE LA TOILE SOLAIRE OU STORE EXISTANTS, VOIR NOTE CI-CONTRE.
- AVANT TOUTE DÉMOLITION PAR L'EXTÉRIEUR, INSTALLER UN PLEXIGLASS DU CÔTÉ INTÉRIEUR (ÉTAPE 1), VOIR NOTE CI-CONTRE.
- FENÊTRE EXISTANTE À DÉMOLIR LORS DE L'ÉTAPE 2, DÉMOLITION PAR L'EXTÉRIEUR.
- TOILE SOLAIRE À ENLEVER AVANT L'INSTALLATION DU PLEXIGLASS.
- ENLEVER TEMPORAIREMENT LE PLEXIGLASS POUR LA DÉMOLITION DE L'ENCADREMENT, À REINSTALLER EN ATTENTE DE LA NOUVELLE FINITION.
- NOUVEAU THERMOS.
- NOUVELLE FINITION EN PÉRIPHÉRIE DU MUR RIDEAU À L'ÉTAPE 2, VOIR NOTE "FINITION INTÉRIEURE" SUR CETTE PAGE.
- FINITION INTÉRIEURE DE STRATIFIÉ À DÉMOLIR À L'ÉTAPE 2.
- NOUVELLE FINITION EN PÉRIPHÉRIE DE LA FENÊTRE À L'ÉTAPE 2, VOIR NOTE "FINITION INTÉRIEURE" SUR CETTE PAGE.




GLCRM | Proulx Savard |

GLCRM:
128, Avenue de la Cathédrale,
Bureau 201
Rimouski, QC, G5L 5H7
(418) 722-7655



2406, Ch. des Quatres-Bourgeois,
Bureau 100
Québec, QC, G1V 1W5
(418) 647-1700

Proulx Savard Architectes:
75, boul. Arthur-Buies Ouest,
Rimouski, QC G5L 5C2
(418) 723-5543

ARCHITECTURE

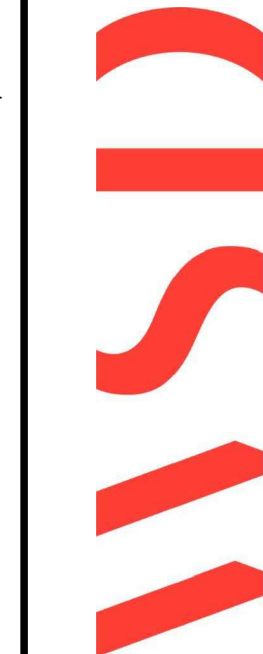

CONSULTANTS

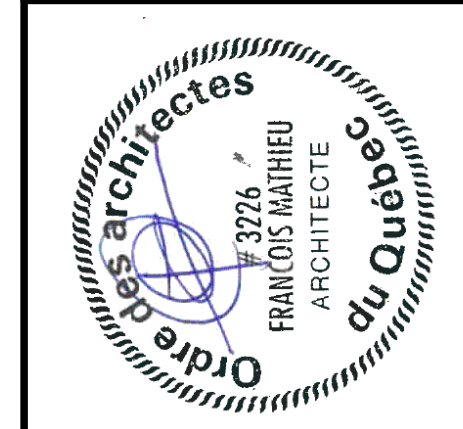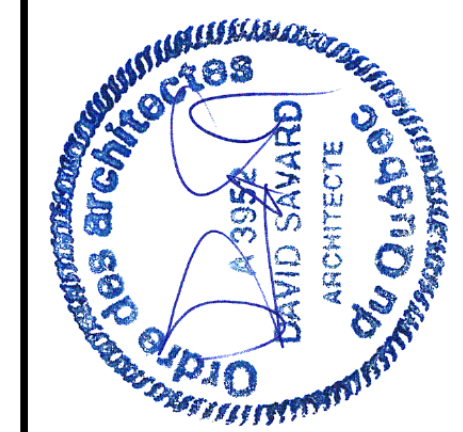

DESSIN	DESSINATEUR (S)	DOSSIER N°	DATE	DATE	RÉVISIONS
PROJET	HÔPITAL DE CHANDLER, Chandler (Redaction de l'enveloppe)	DB AL	ÉCHELLE	INDIQUÉE	No
PROPRIÉTAIRE	Santé Québec	2024-09-04	2024-08-21	2024-08-03	2024-05-14
PROPRIÉTAIRE	Santé Québec	2024-09-04	2024-08-21	2024-08-03	2024-05-14

— LÉGENDE —

- EXISTANT À CONSERVER.
- ÉLÉMENT À DÉMOLIR.
- AXE EXISTANT
- EXTÉRIEUR DE LA STRUCTURE DE BÉTON EXISTANTE DE LA TOUR.
- NOUVEL AXE, FACE EXTÉRIEURE DES BARRES Z ET COLOMBAGES DE LA TOUR, VOIR STRUCTURE.
- (*) VOIR NOTE GÉNÉRAL PAGE 400.

NE DOIT PAS SERVIR À L'EXÉCUTION

Le présent document est émis par la seule fin identifiée. Son contenu est protégé par les droits d'auteur et toute reproduction ou modification, partielle ou totale, est interdite sans l'autorisation écrite de gagnon, letellier, cyr, ricard, mathieu, proulx, savard consortium d'architectes.

