



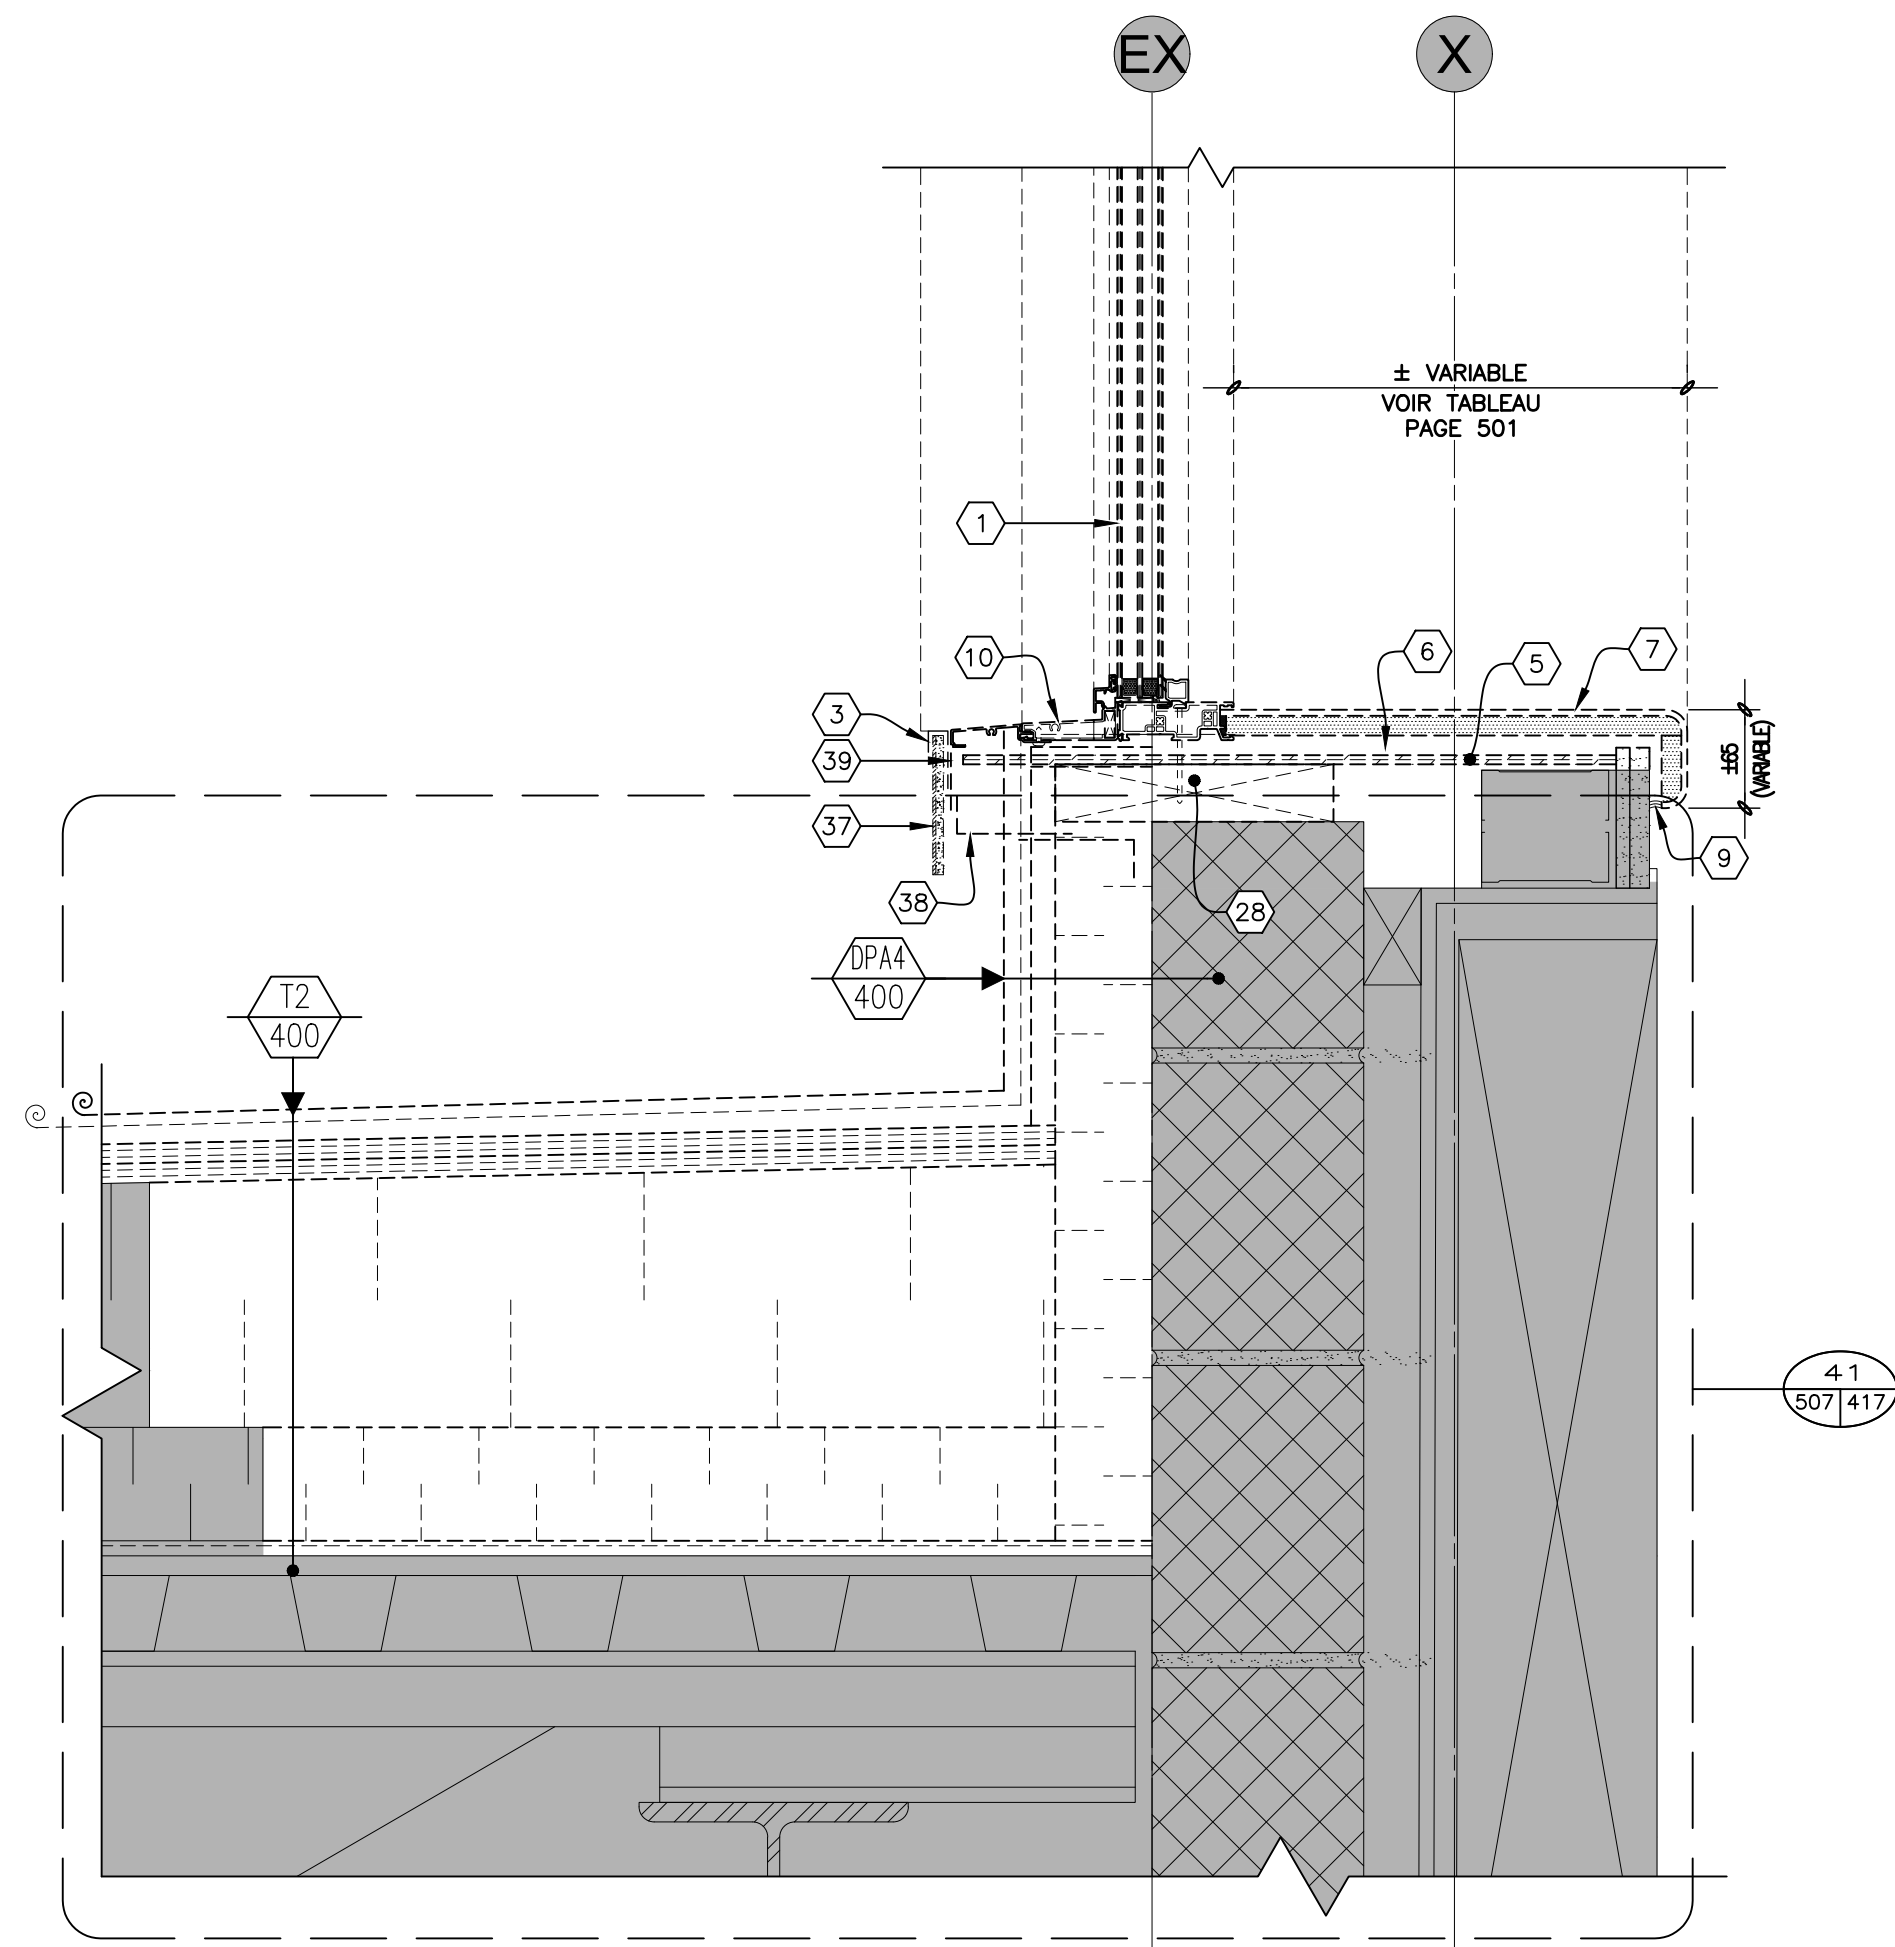


DÉMOLITION

8 DÉTAIL DE FENÊTRE
502.503 507 1:5mm (TOUR/CHIRURGIE)

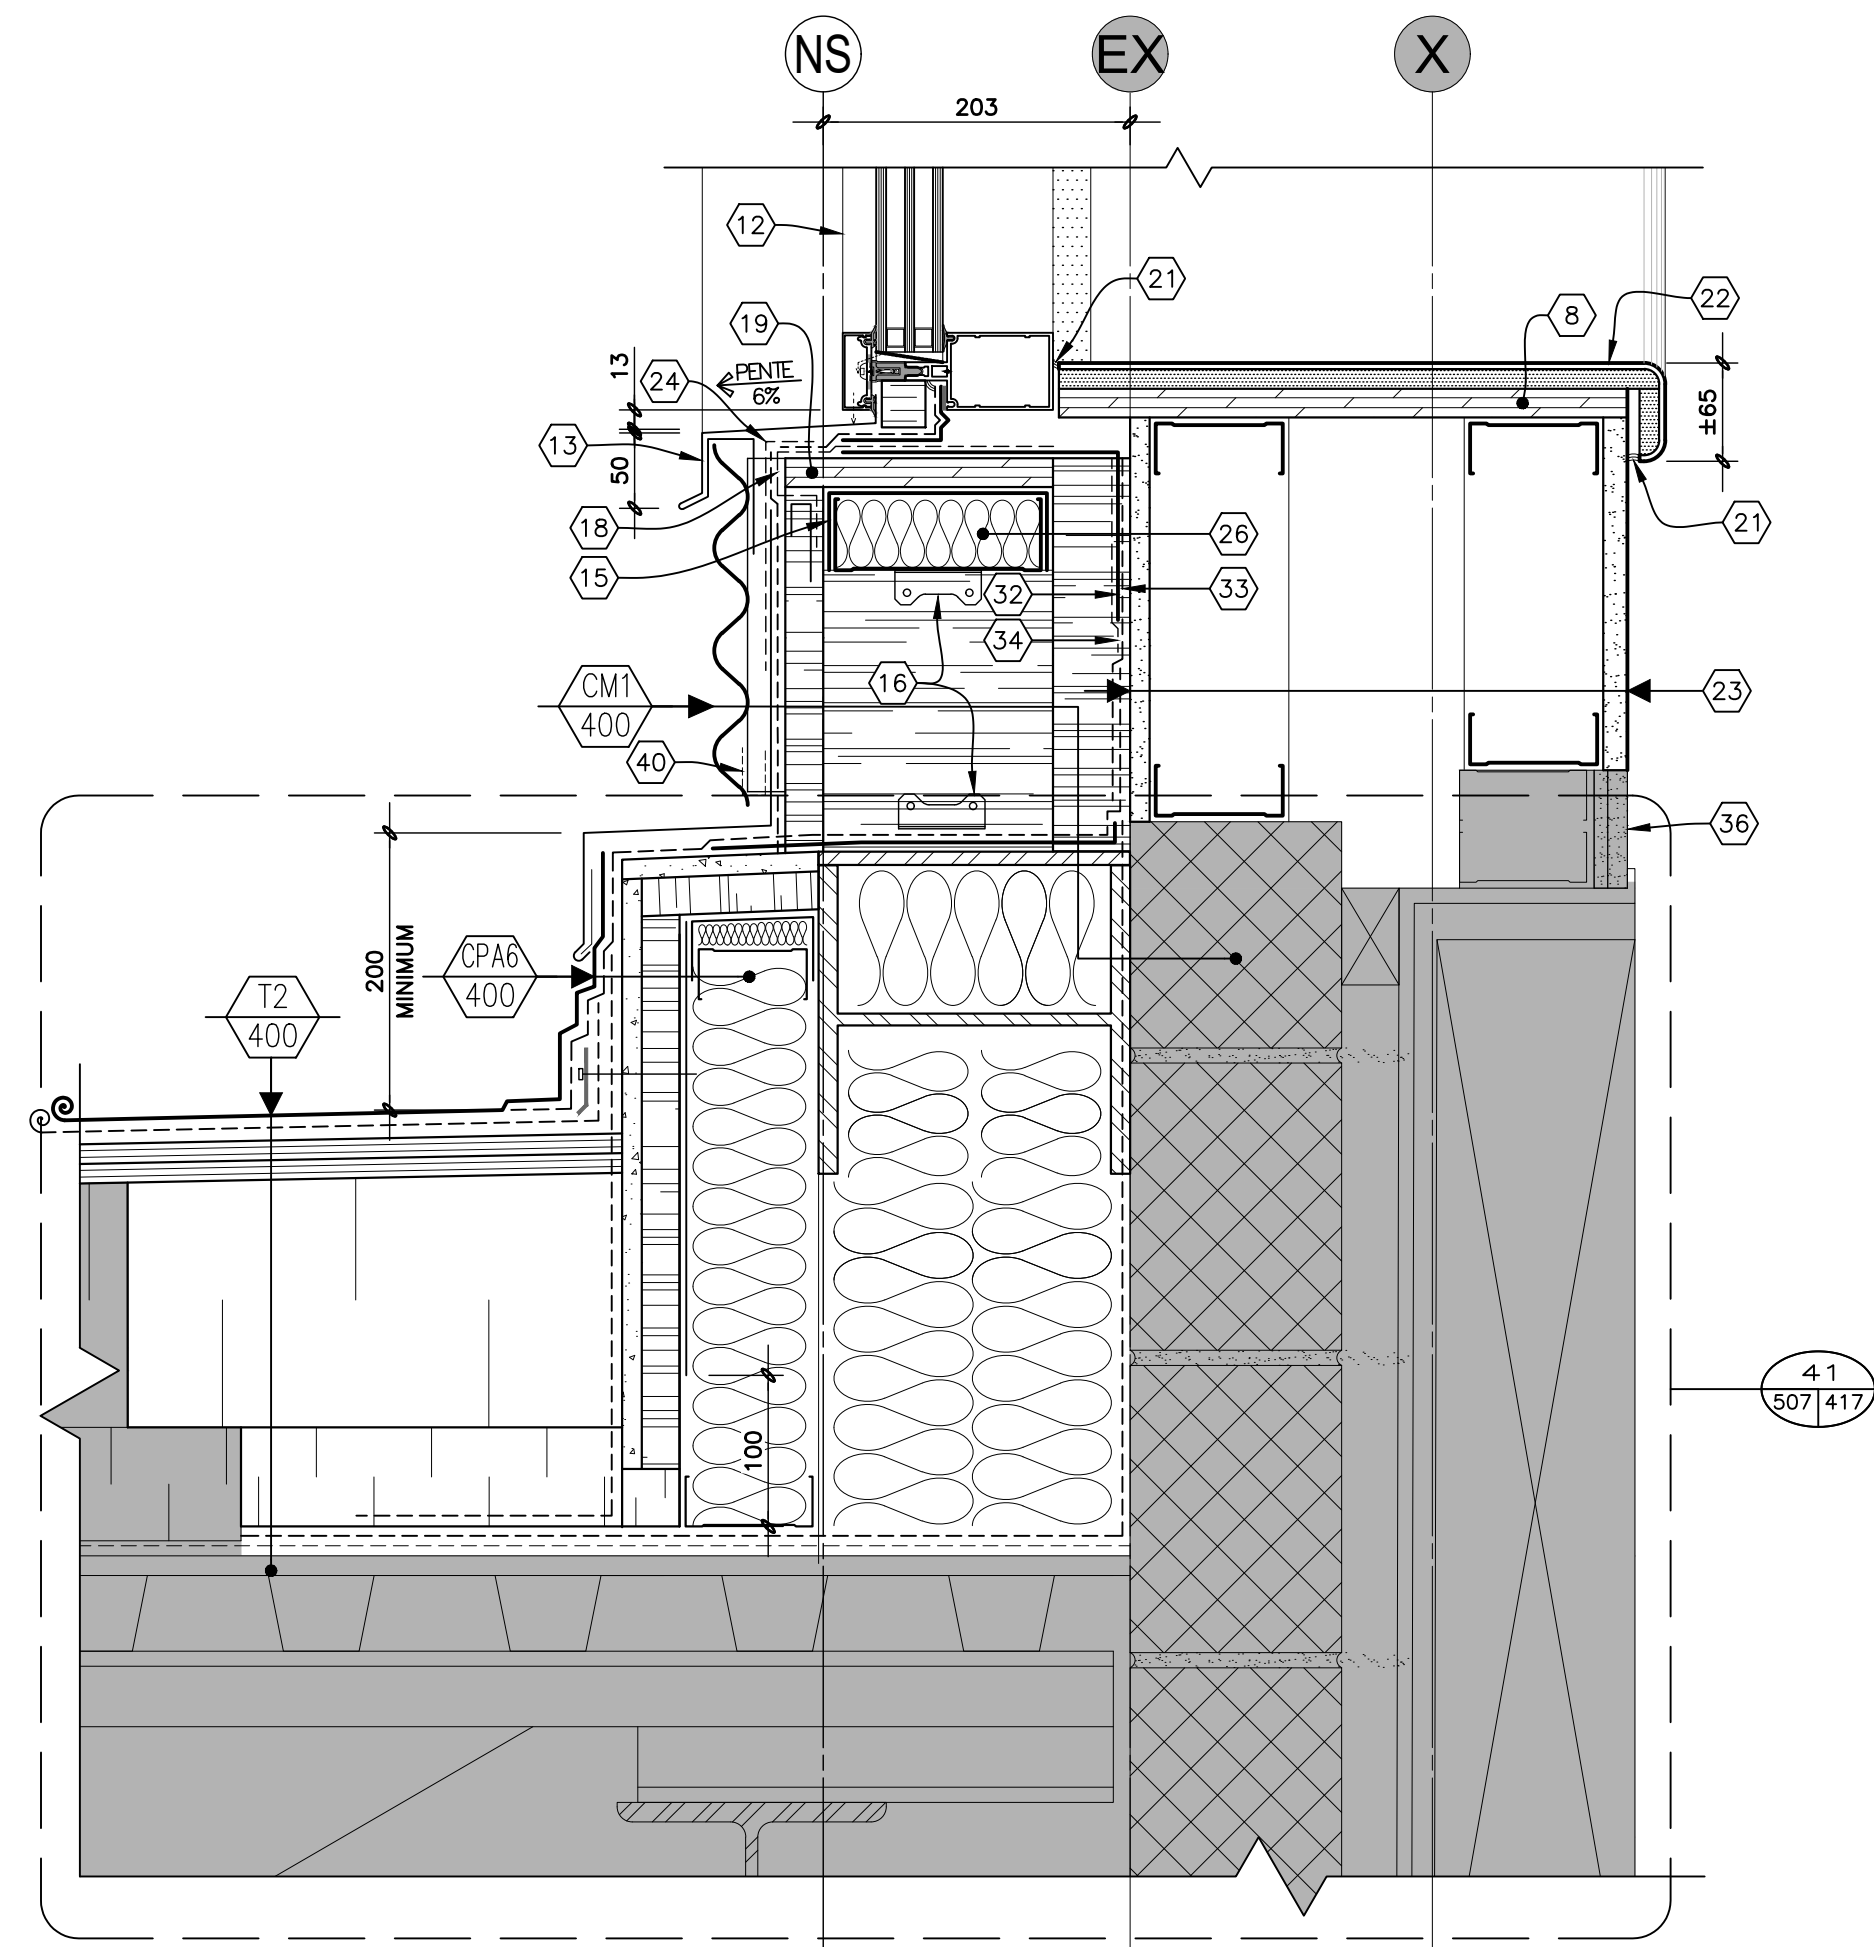


CONSTRUCTION

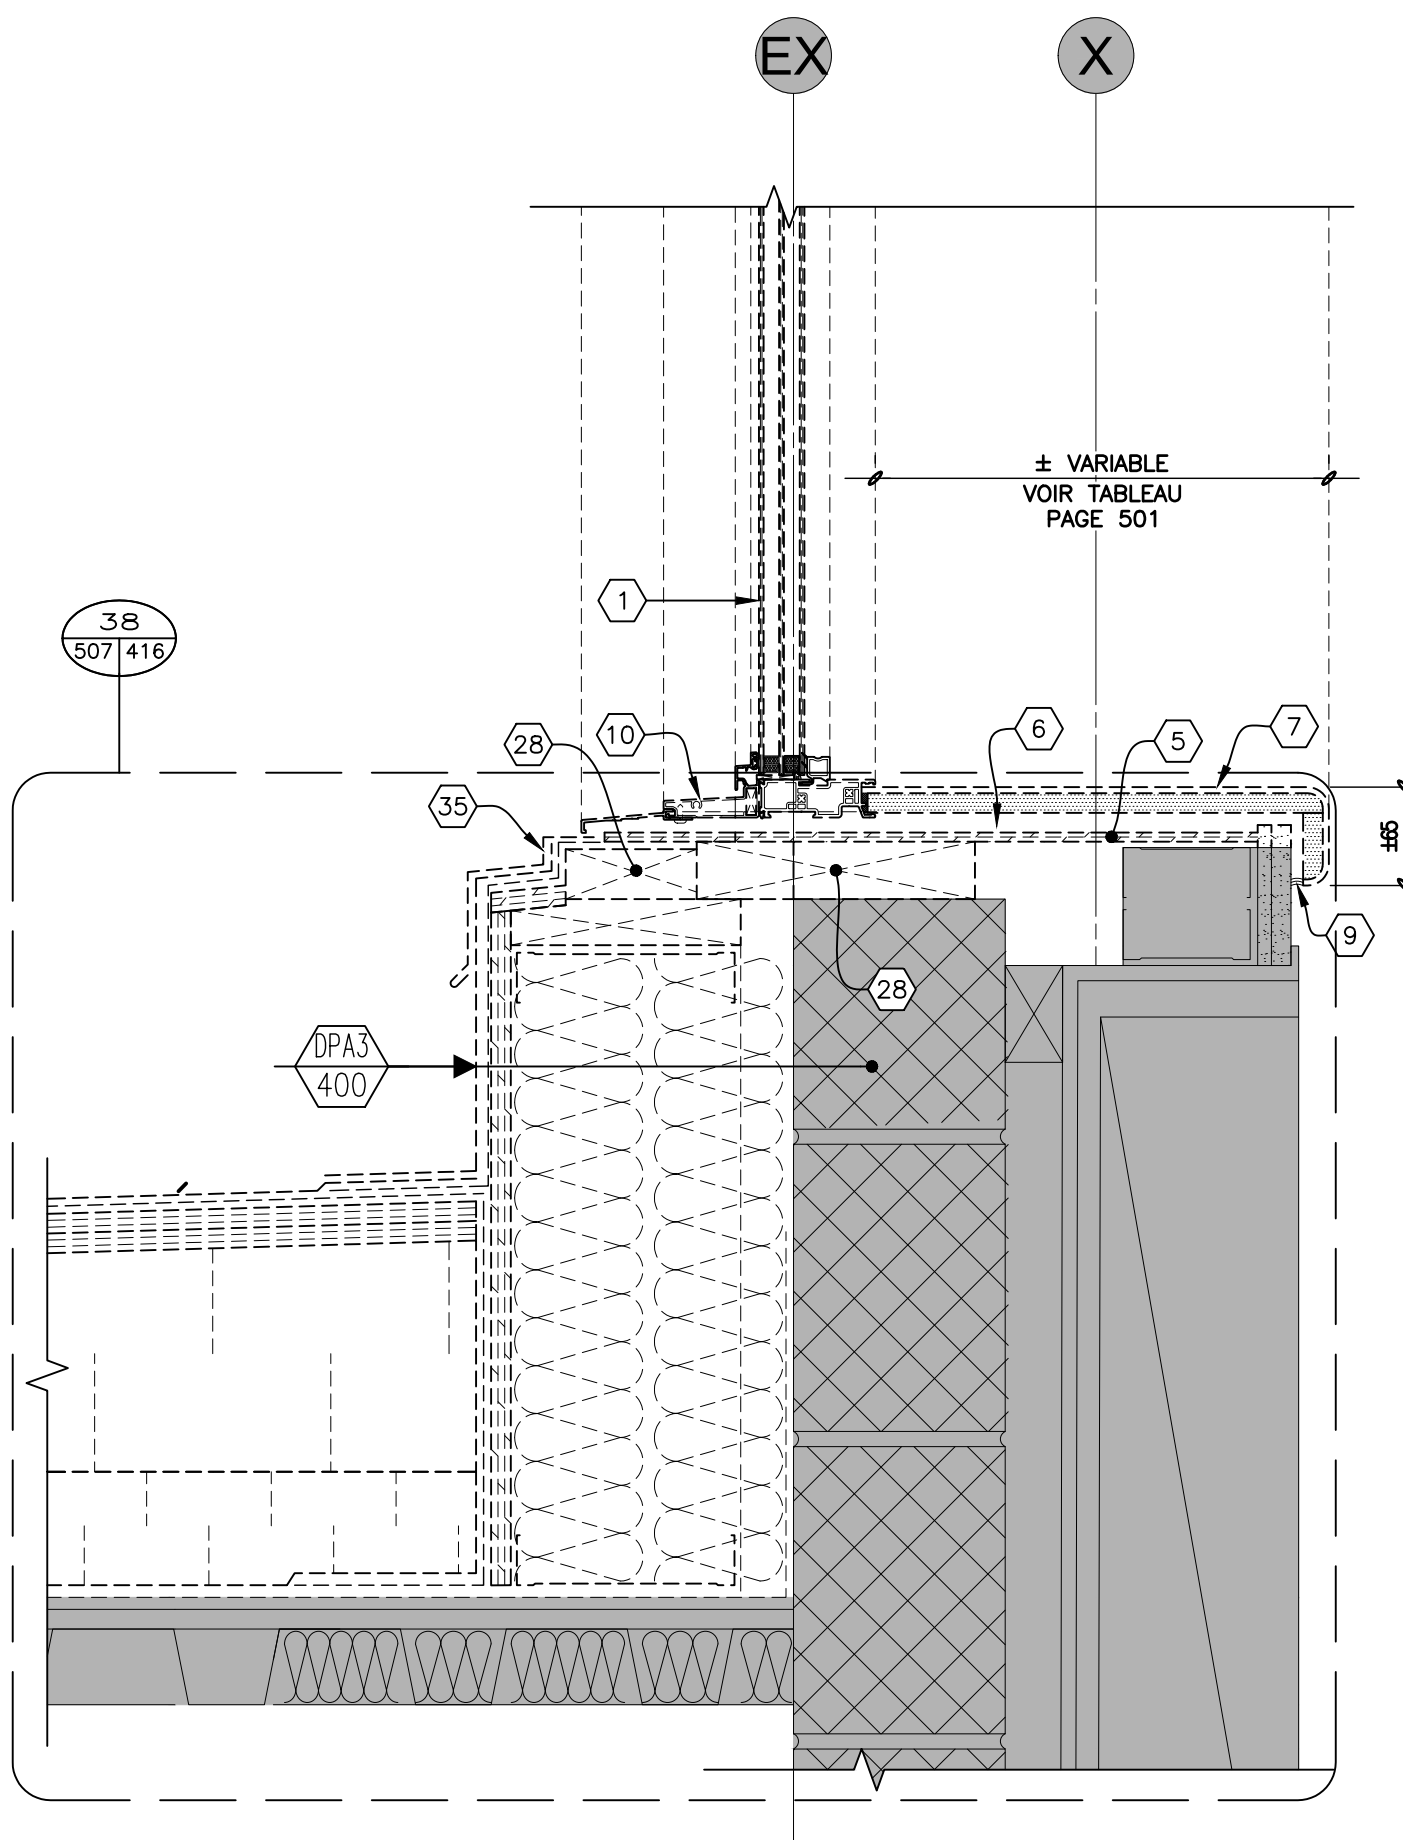


DÉMOLITION


9 DÉTAIL DE LA FENÊTRE
502.503 507 1:5mm (TOUR/ADMINISTRATION)

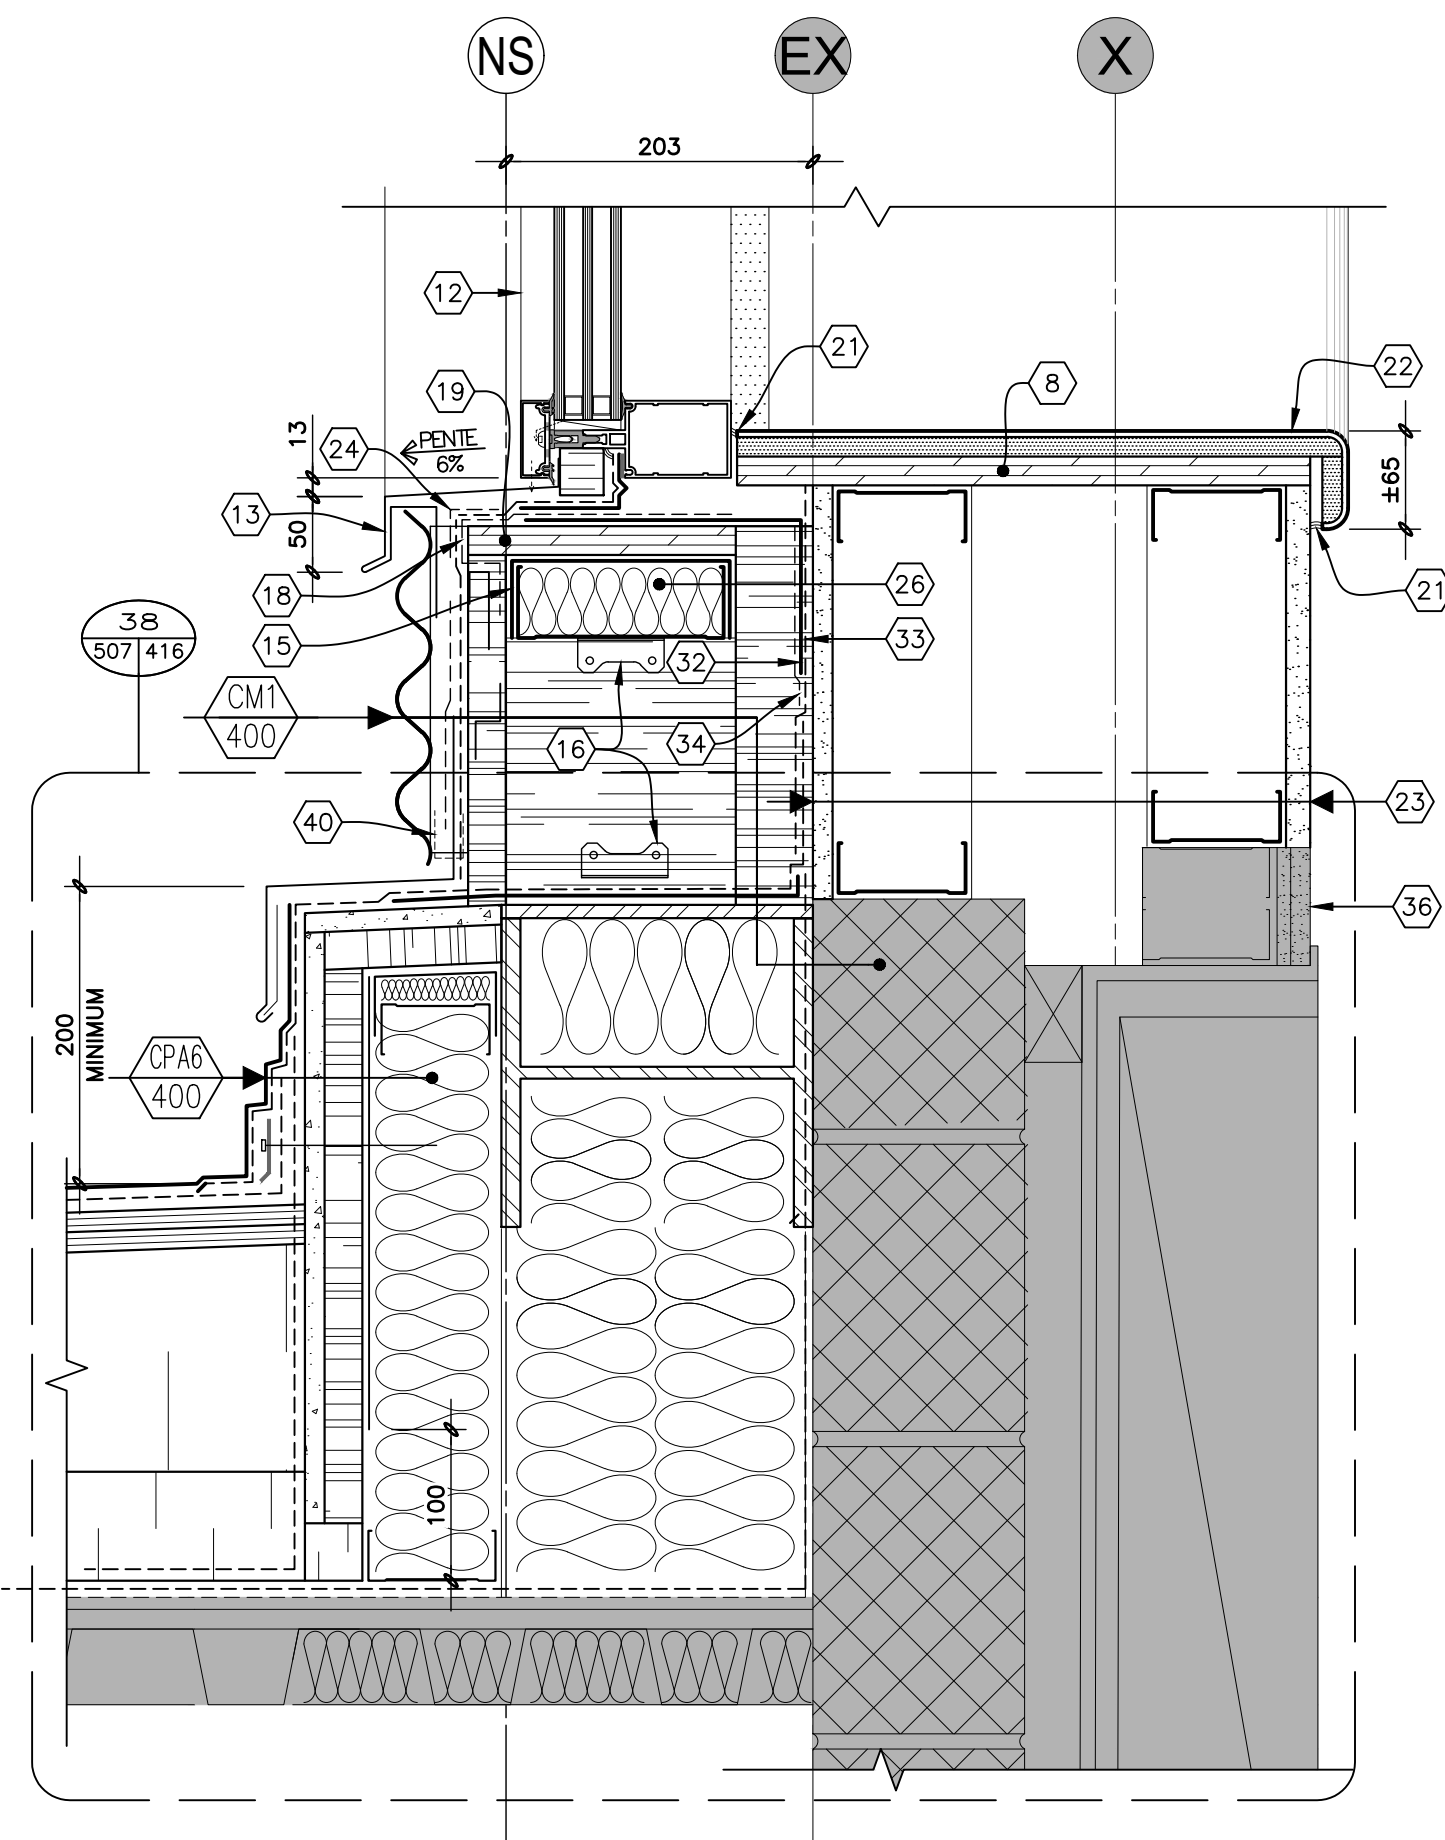

CONSTRUCTION


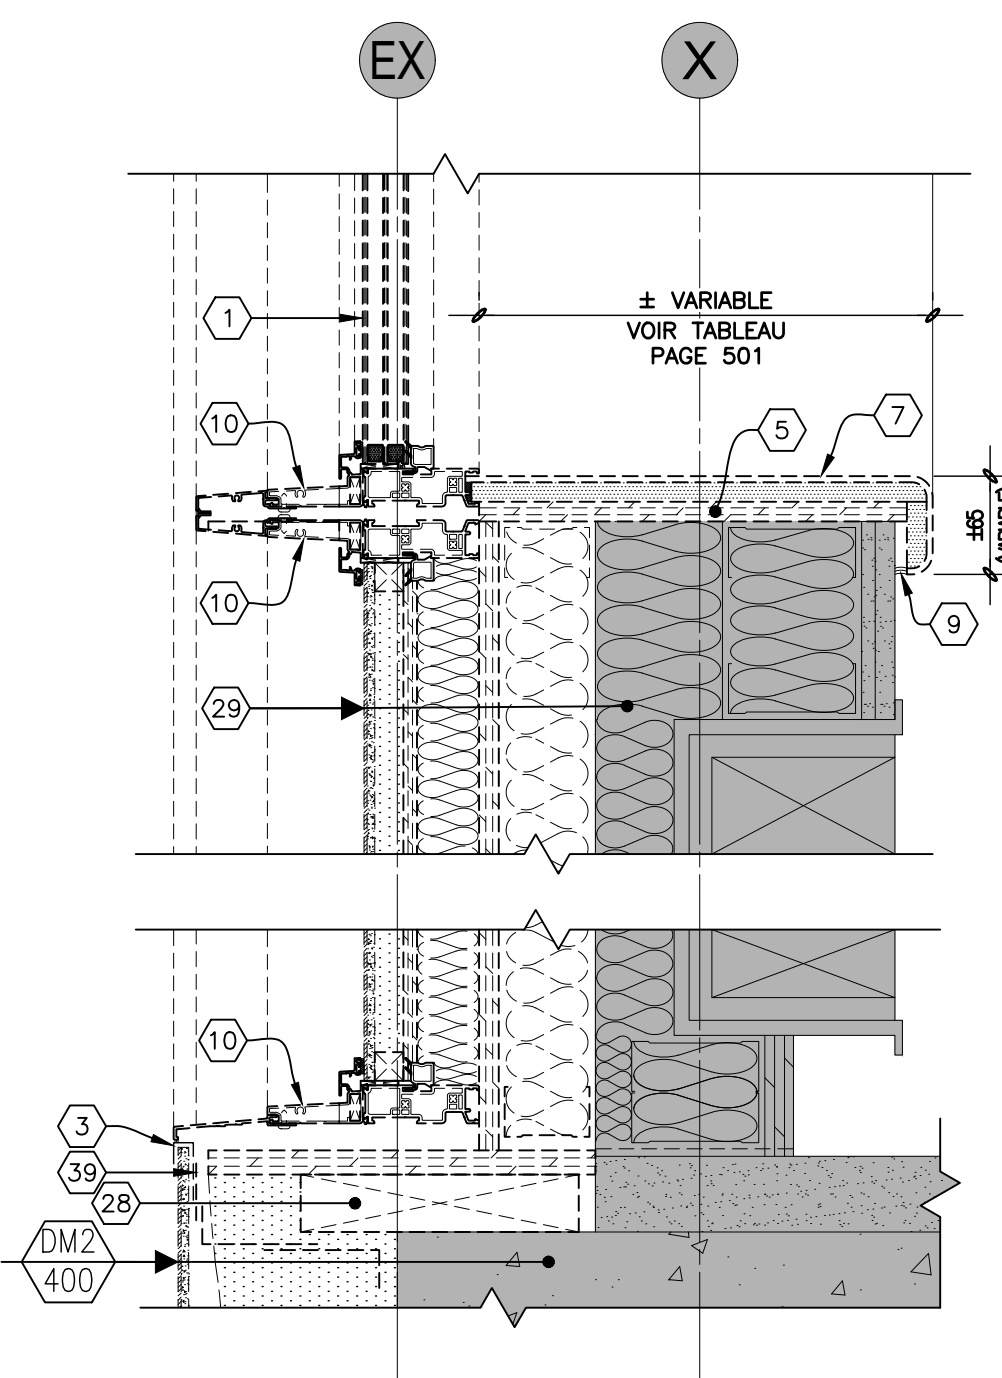


DÉMOLITION

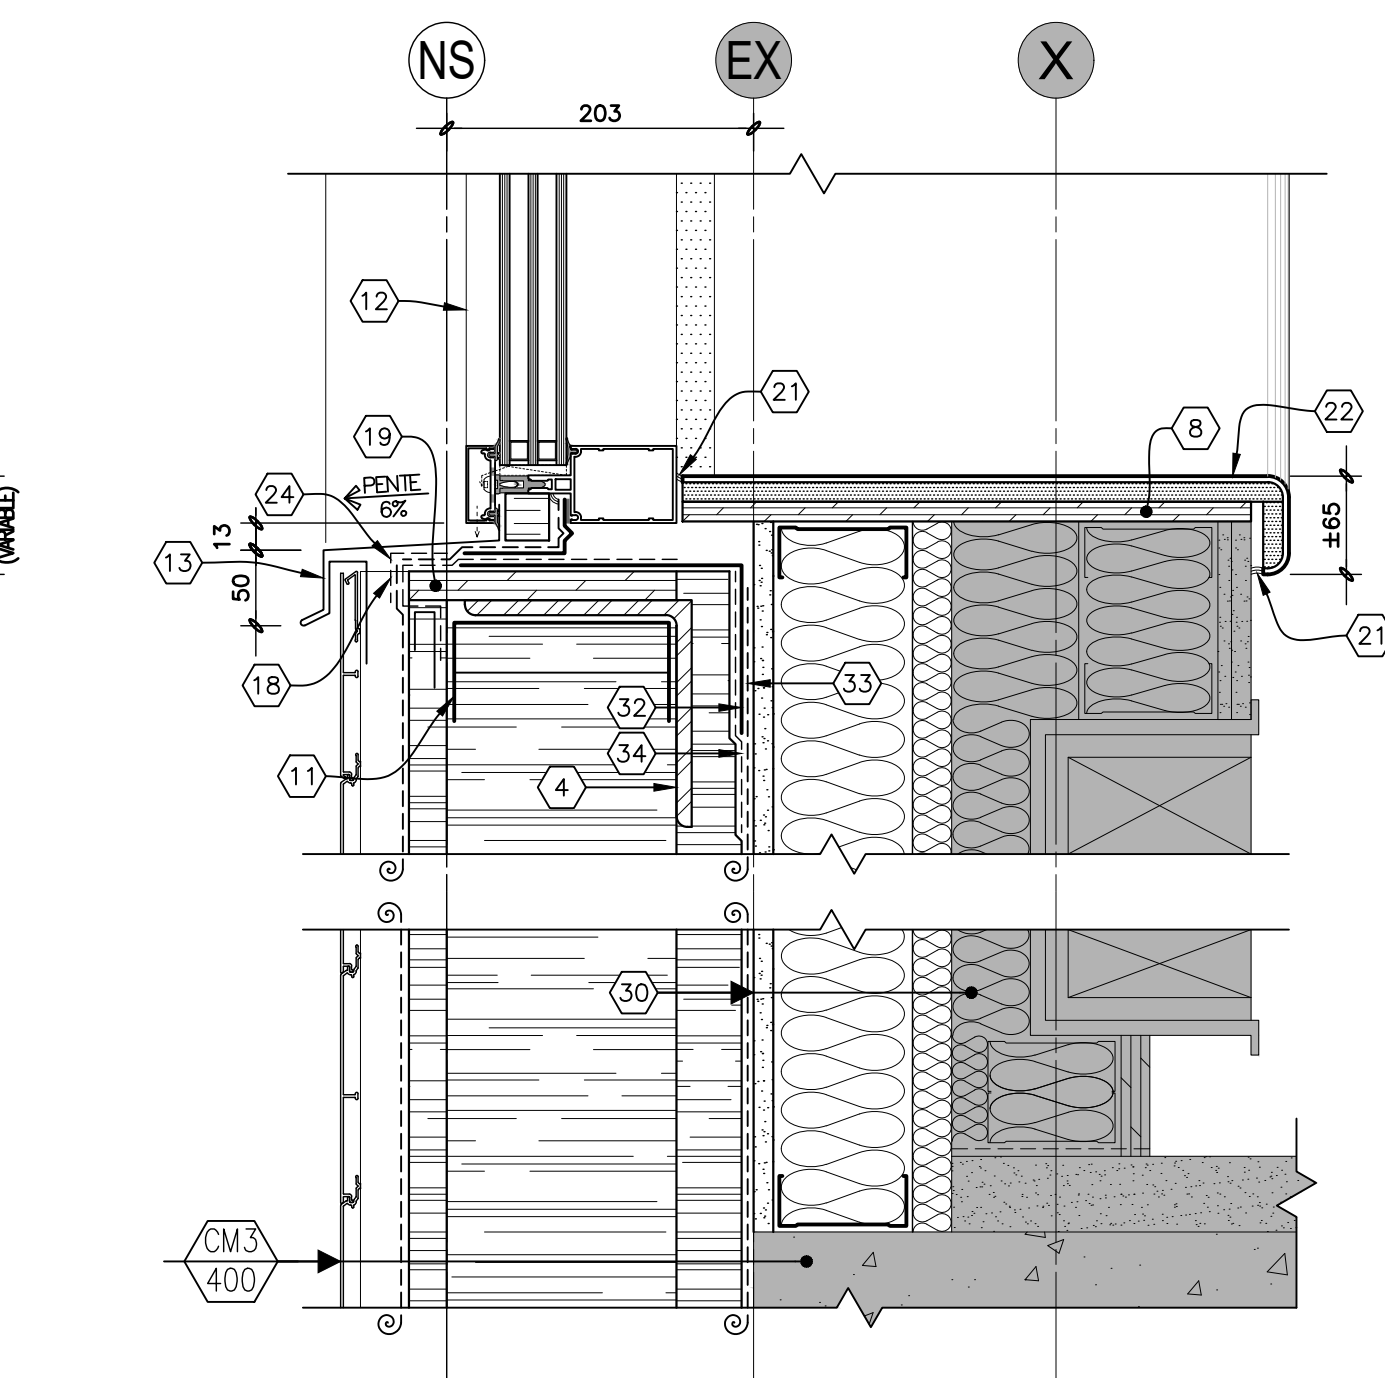

CONSTRUCTION

7 DÉTAIL DE FENÊTRE CONSTRUCTION
502.503 507 1:5mm (TOUR)

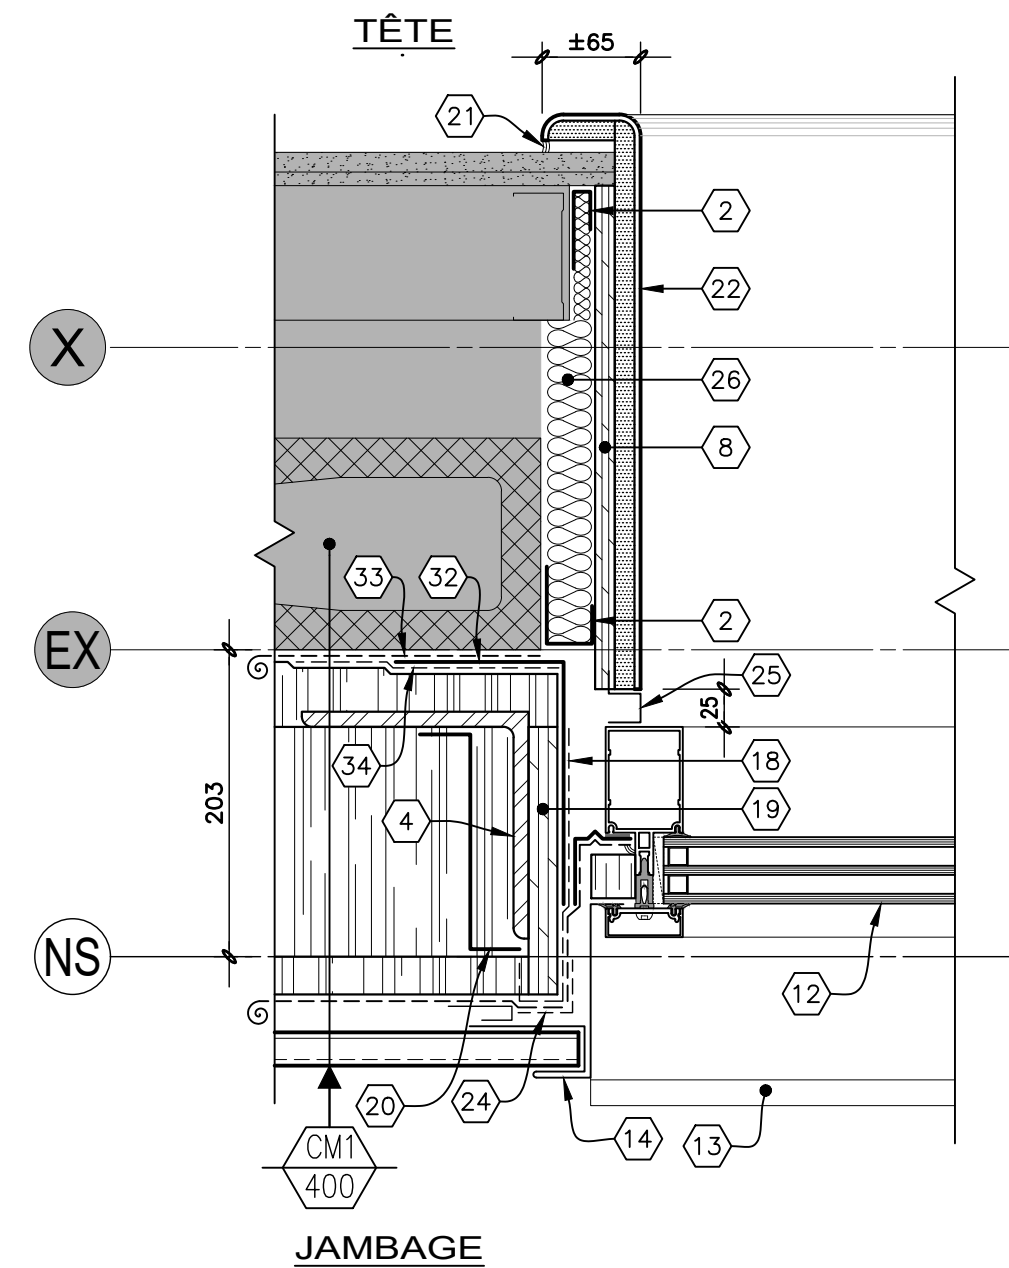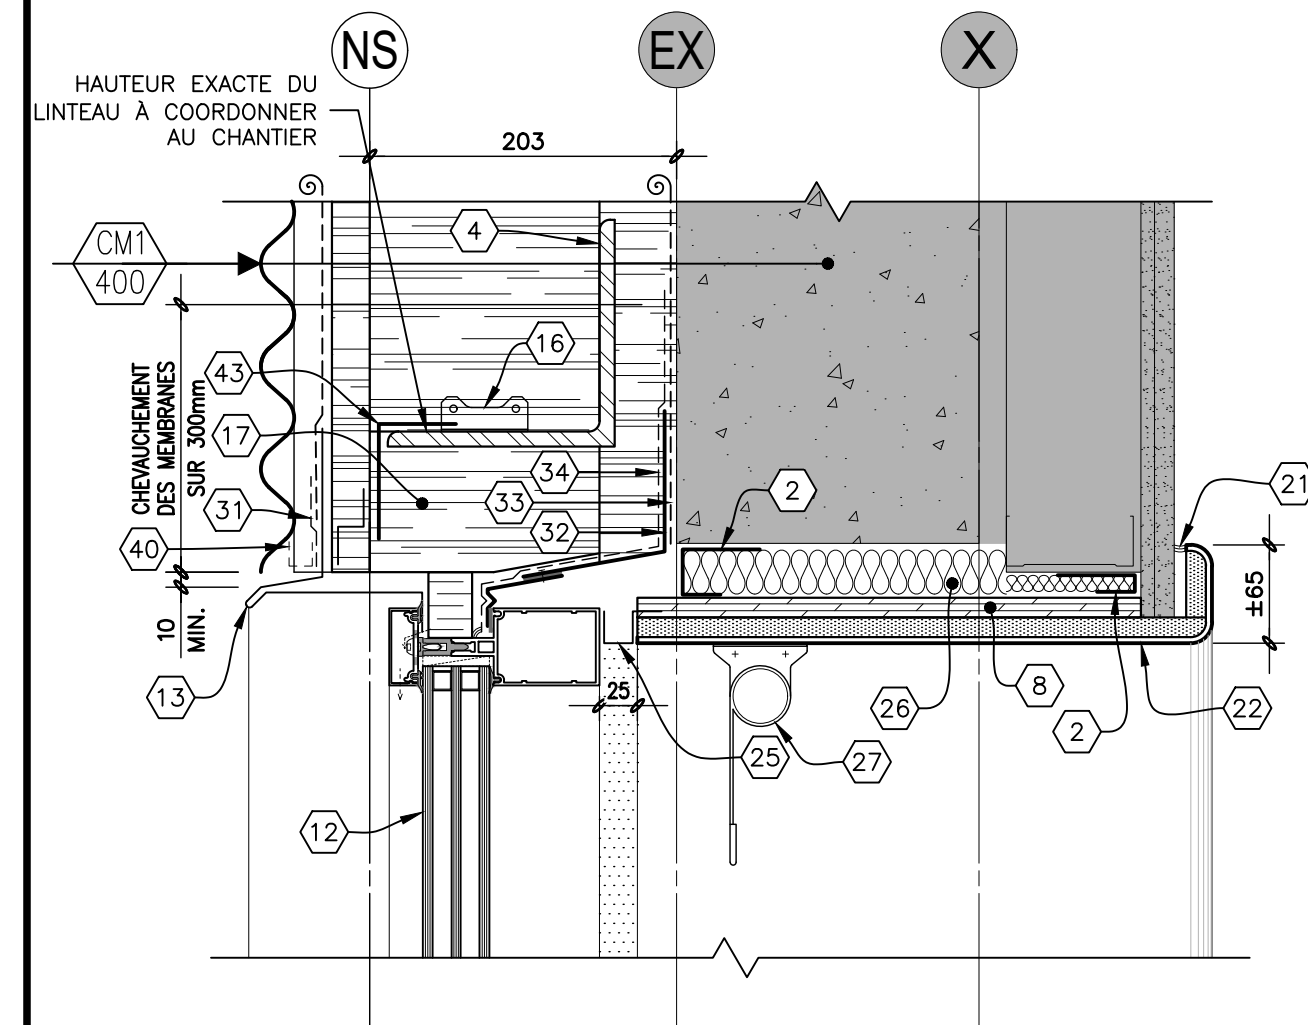

JAMBAGE

NOTES

- FENÊTRE HYBRIDE (ALUMINIUM/PVC) EXISTANTE À DÉMOLIR.
- PLIAGE DE TÔLE EN ACIER ÉMAILLÉ, CAL.18.
- MOULURE EN ALUMINIUM À DÉMOLIR.
- LINTEAU, VOIR STRUCTURE.
- CONTREPLAQUÉ EXISTANT À DÉMOLIR.
- MEMBRANE AUTOADHÉSIVE EXISTANTE À DÉMOLIR.
- FINITION INTÉRIEURE EN CONTREPLAQUÉ RECOUVRENT DE STRATIFIÉ À DÉMOLIR.
- CONTREPLAQUÉ 16mm D'ÉPAISSEUR.
- SCÉLLANT EXISTANT À ENLEVER. NETTOYER LES SURFACES EXISTANTES CONSERVÉES DE TOUTES TRACES DE SCÉLLANT.
- SECTION DU CADRE DE FENÊTRE À COUPER ET À DÉMOLIR. VOIR DÉTAILS EN ÉTAPES À LA PAGE 505.
- USSE DE DÉFLEXION, VOIR STRUCTURE.
- NOUVEAU MUR-RIDEAU, VOIR DEVIS.
- SOLIN EN ACIER ÉMAILLÉ, CAL. 24.
- MOULURE EN "J" EN ACIER ÉMAILLÉ, CAL.24.
- ASSEMBLAGE DE COLOMBAGE ET DE USSE SUR TOUT LE PÉRIMÈTRE DE L'OUVERTURE, VOIR PLAN DE STRUCTURE.
- CONNECTEUR, VOIR STRUCTURE.
- LAINE DE ROCHE SEMI-RIGIDE.
- MEMBRANE D'ÉTANCHÉITÉ AUTOADHÉSIVE SUR TOUT LE PÉRIMÈTRE DE L'OUVERTURE.
- CONTREPLAQUÉ À PLUS 19mm D'ÉPAISSEUR.
- BARRE "Z" STRUCTURALE, VOIR STRUCTURE.
- SCÉLLANT DE FINITION.
- FINITION EN CONTREPLAQUÉ À PLUS 19mm D'ÉPAISSEUR RECOUVRENT DE PLASTIQUE STRATIFIÉ, COIN ARRONDI SUR TOUT LE PÉRIMÈTRE DE L'OUVERTURE. COULEUR AU CHOIX DE L'ARCHITECTE.
- PLAQUE DE PLÂTRE, 16mm D'ÉPAISSEUR, À PEINDRE; - COLOMBAGE MÉTALLIQUE 92mm Ø 400mm C/C; - COLOMBAGE MÉTALLIQUE 92mm Ø 400mm C/C; - PANNEAU DE MÂT DE FIBRE DE VERRE, 13mm D'ÉPAISSEUR.
- RUBAN AUTOCOLLANT. SCÉLLER LA MEMBRANE PARE-INTÉMPÉRIES AVEC LA MEMBRANE AUTOADHÉSIVE.
- GRILLE DE VENTILATION CONTINUE (3 CÔTÉS) EN ALUMINIUM ÉMAILLÉ 0.8mm D'ÉPAISSEUR, PERFORÉ (POURCENTAGE D'OUVERTURE DE 40%). FINI TEL QUE LE MUR RIDEAU.
- REMPLIR L'ESPACE DE LAINE DE FIBRE DE ROCHE.
- NOUVELLE TOILE SOLAIRE, VOIR DEVIS.
- PIECE DE BOIS EXISTANTE À DÉMOLIR.
- PANNEAU DE POLYMÈRES RENFORCÉ DE FIBRES DE VERRE 7mm À DÉMOLIR; - CADRE DE BOIS 19X19mm AVEC MONTANTS VERTICAUX Ø ±400mm À DÉMOLIR; - ISOLANT DE POLYURÉTHANE GICLÉ À DÉMOLIR; - CONTREPLAQUÉ À DÉMOLIR; - ISOLANT EN NATTES À DÉMOLIR; - CONTREPLAQUÉ À DÉMOLIR; - ISOLANT EN NATTES À DÉMOLIR.
- PANNEAU DE MÂT DE FIBRE DE VERRE, 13mm D'ÉPAISSEUR; - COLOMBAGE MÉTALLIQUE 92mm Ø 400mm C/C; - LAINE DE FIBRE DE ROCHE 92mm; - REMPLIR L'ESPACE DE LAINE DE FIBRE DE ROCHE.
- RUBAN AUTOCOLLANT.
- TÔLE PLIÉE EN ACIER GALVANISÉ, CAL. 16, AU POURTOUR DE L'OUVERTURE.
- MEMBRANE AUTOCOLLANTE PARE-VAPEUR.
- MEMBRANE LIQUIDE PULVÉRISÉE PAR-DESSUS LA MEMBRANE AUTOADHÉSIVE.
- SOLIN EN ACIER ÉMAILLÉ EXISTANT À DÉMOLIR.
- MUR EXISTANT À RAGRÉER ET À PEINDRE DE COULEUR TEL QUE L'EXISTANT.
- PANNEAU DE POLYMÈRES RENFORCÉ DE FIBRE DE VERRE 7mm À DÉMOLIR.
- BARRE "Z" EXISTANTE À DÉMOLIR.
- TÔLE EXISTANTE RIVETÉE SUR LA BARRE EN "Z" ET AU CADRE DE LA FENÊTRE À DÉMOLIR.
- MOUSTOQUAIRE.
- SECTION DE MOULURE DE DÉPART POUR APPUI DU PAREMENT DE DÉCLIN D'ALUMINIUM, PAR LE MANUFACTURIER DU PAREMENT DE DÉCLIN D'ALUMINIUM.
- MOULURE EN "J" PAR LE MANUFACTURIER DU PAREMENT DE DÉCLIN D'ALUMINIUM.
- PLIAGE DE TÔLE, CAL.16.

LÉGENDE

- EXISTANT À CONSERVER.
- ÉLÉMENT À DÉMOLIR.
- X AXE EXISTANT
- EX EXTÉRIEUR DE LA STRUCTURE DE BÉTON EXISTANTE DE LA TOUR.
- NS NOUVEL AXE: FACE EXTÉRIÈRE DES BARRES Z ET COLOMBAGES DE LA TOUR. VOIR STRUCTURE. (*) VOIR NOTE GÉNÉRAL PAGE 400.

NE DOIT PAS SERVIR À L'EXÉCUTION

Le présent document est émis par la seule fin identifiée. Son contenu est protégé par les droits d'auteur et toute reproduction ou modification, partielle ou totale, est interdite sans l'autorisation écrite de gagnon, letellier, cyr, ricard, mathieu, proulx, savard consortium d'architectes.




GLCRM | Proulx Savard |

GLCRM:
128, Avenue de la Cathédrale,
Bureau 201
Rimouski, QC, G5L 5H7
(418) 722-7655


2406, Ch. des Quatres-Bourgeois,
Bureau 100
Québec, QC, G1V 1W5
(418) 647-1700

Proulx Savard Architectes:
75, boul. Arthur-Buies Ouest,
Rimouski QC G5L 5C2
(418) 723-5543

ARCHITECTURE

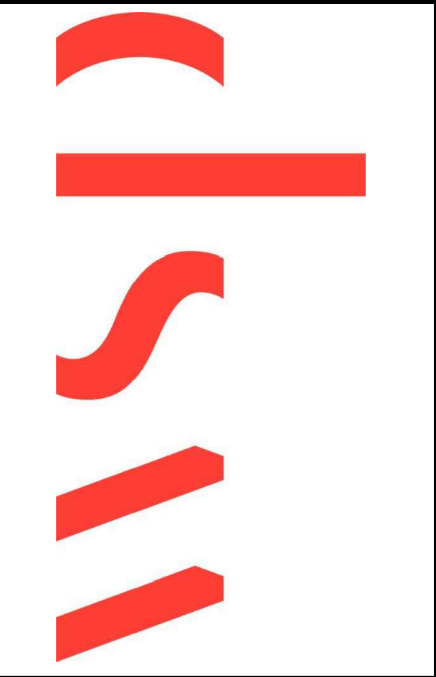

CONSULTANTS

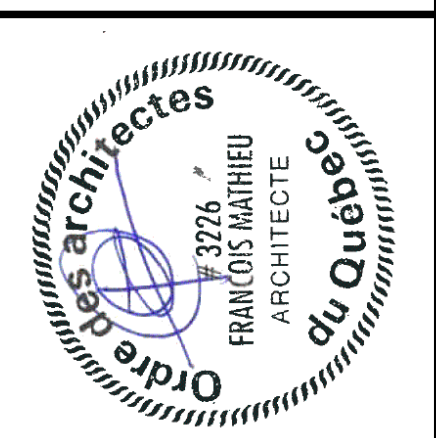

DOSSIER NO.		DATE		RÉVISIONS	
24-108 / R457-24		SEPTEMBRE 2024			
DESIGNATEUR (S)		DATE		RÉVISIONS	
D.B. A.L.					
ÉCHELLE		INDIQUÉE			

PROPRIÉTAIRE	DATE	REVISIONS
Santé Québec		

TÊTE

JAMBAGE

DÉMOLITION

ALLÈGE

CONSTRUCTION

10 DÉTAIL DE FENÊTRE TYPE (BASILAIRE)
502,503 508 1:5mm (CHIRURGIE/ADMINISTRATION - NIVEAU 100)

TÊTE

JAMBAGE

DÉMOLITION

CONSTRUCTION

ALLÈGE

11 DÉTAIL DE FENÊTRE TYPE (BASILAIRE)
502,503 508 1:5mm (CHIRURGIE - NIVEAU RDC)

DÉMOLITION

JAMBAGE

12
502,503 508

DÉTAIL DE FENÊTRE TYPE (BASILAIRE)

1:5mm (BRIQUE CONSERVÉE - NIVEAU RDC - URGENCE / ADMINISTRATION)

NOTES


- (1) FENÊTRE HYBRIDE (ALUMINIUM/PVC) EXISTANTE À DÉMOUR.
- (2) SOLIN EN ACIER EMAILLÉ EXISTANT À DÉMOUR.
- (3) MOULURE EN ALUMINIUM À DÉMOUR.
- (4) PLAGE DE TÔLE EN ACIER EMAILLÉ, CAL.18.
- (5) CONTREPLAQUÉ EXISTANT À DÉMOUR.
- (6) MEMBRANE AUTOADHÉSIVE EXISTANTE À DÉMOUR.
- (7) FINITION INTÉRIEURE EN CONTREPLAQUÉ RECOUVRET DE STRATIFIÉ À DÉMOUR.
- (8) ACIER EMAILLÉ EXISTANT À DÉMOUR.
- (9) SCELLANT EXISTANT À ENLEVER. NETTOYER LES SURFACES EXISTANTES CONSERVÉES DE TOUTES TRACES DE SCELLANT.
- (10) SECTION DU CADRE DE FENÊTRE À COUPER ET À DÉMOUR. VOIR DÉTAILS EN ÉTAPES À LA PAGE 505.
- (11) TÔLE, STROU ET/OU HAUBILLAGE DE FENÊTRE À ENLEVER ET À RETREMIER AU PROPRIÉTAIRE, VOIR NOTE PAGE 505.
- (12) NOUVELLE FENÊTRE EN ALUMINIUM.
- (13) SOLIN EN ACIER EMAILLÉ, CAL. 24.
- (14) MOULURE EN "J" EN ACIER EMAILLÉ, CAL.24.
- (15) ASSEMBLAGE DE COLOMBAGE ET DE LISSE SUR TOUT LE PÉRIMÈTRE DE L'OUVERTURE, VOIR STRUCTURE.
- (16) CONNECTEUR, VOIR STRUCTURE.
- (17) SCELLANT SUR FOND DE JOINT.
- (18) MEMBRANE D'ÉTANCHÉITÉ AUTOADHÉSIVE SUR TOUT LE PÉRIMÈTRE DE L'OUVERTURE.
- (19) CONTREPLAQUÉ À PLUS 19mm D'ÉPAISSEUR.
- (20) BOUDIN D'ÉCLAFFAGE DE DIAMÈTRE APPROPRIÉ ET SCELLANT CONTINU SUR TOUT LE PÉRIMÈTRE DE LA FENÊTRE POUR ASSURER LA CONTINUITÉ DE L'ÉTANCHÉITÉ ENTRE LA MEMBRANE ET LE CADRE DE LA FENÊTRE.
- (21) SCELLANT DE FINITION.
- (22) FINITION EN CONTREPLAQUÉ À PLUS 19mm D'ÉPAISSEUR RECOUVRET DE PLASTIQUE STRATIFIÉ, CERN ARRondi SUR TOUT LE PÉRIMÈTRE DE L'OUVERTURE. COULEUR AU CHOIX DE L'ARCHITECTE.
- (23) POLYURÉTHANE GICLÉ NON EXPANSIF SUR LE PÉRIMÈTRE DE LA FENÊTRE.
- (24) RUBAN AUTOCOLLANT. SCELLER LA MEMBRANE PAR-INTÉRIEURES AVEC LA MEMBRANE AUTOADHÉSIVE.
- (25) MEMBRANE AUTOADHÉSIVE PARÉ-VAPEUR SUR TOUT LE PÉRIMÈTRE DE L'OUVERTURE. SCELLER SUR LA NOUVELLE MEMBRANE SOUS LE CADRE DE FENÊTRE ET SUR LE POLYÉTHYLÈNE DU MUR EXISTANT.
- (26) REMPLIR L'ESPACE DE LAINE DE FIBRE DE ROCHE.
- (27) CALE D'AJUSTEMENT EN POLYVINYLE RIGIDE D'ÉPAISSEUR REQUISE.
- (28) PIÈCE DE BOIS EXISTANTE À DÉMOUR.
- (29) RIVET EN ACIER PRÉPÊTE, DE MÊME COULEUR QUE LE PAVEMENT.
- (30) PLAGE DE TÔLE EN ACIER GALVANISÉ CAL. 22.
- (31) RUBAN AUTOCOLLANT.
- (32) TÔLE PLIÉE EN ACIER GALVANISÉ 75mm x 75mm, CAL. 16, AU POURTOUR DE L'OUVERTURE.
- (33) MEMBRANE AUTOCOLLANTE PARÉ-VAPEUR.
- (34) CONTREPLAQUÉ À PLUS D'ÉPAISSEUR REQUISE.
- (35) CONTREPLAQUÉ À PLUS 19mm RECOUVRET D'UNE MEMBRANE AUTOCOLLANTE ET D'UNE TÔLE PLIÉE EN ACIER EMAILLÉ, CAL. 24, COULEUR AU CHOIX DE L'ARCHITECTE.
- (36) BOUT DU PANNEAU REPLIÉ VERS L'INTÉRIEUR.
- (37) MEMBRANE LIQUIDE PULVÉRISÉE PAR-DESSUS LA MEMBRANE AUTOADHÉSIVE.
- (38) PLAFOND SUSPENDU (HAUTEUR VARIABLE), À CONSERVER.
- (39) TÔLE EXISTANTE RIVETÉE SUR LA BARRE EN "Z" ET AU CADRE DE LA FENÊTRE À DÉMOUR.
- (40) MEMBRANE AUTOCOLLANTE EXISTANTE À DÉMOUR.
- (41) BARRE EN "Z" AJUSTABLE EXISTANTE À DÉMOUR.
- (42) MOUSTIQUEURE.

LÉGENDE

- | | |
|---|---|
|  | EXISTANT À CONSERVER. |
| ----- | ÉLÉMENT À DÉMOLIR. |
|  | AXE EXISTANT |
|  | EXTÉRIEUR DE LA STRUCTURE DE BÉTON EXISTANTE DE LA TOUR. |
|  | NOUVEL AXE: FACE EXTÉRIEURE DES BARRES Z ET COLOMBAGES DE LA TOUR.
VOIR STRUCTURE.
(*) VOIR NOTE GÉNÉRALE PAGE 400. |

NE DOIT PAS SERVIR À L'EXÉCUTION


Le présent document est émis pour la seule fin identifiée. Son contenu est protégé par les droits d'auteur et toute reproduction ou modification, partielle ou totale, est interdite sans l'autorisation écrite de gagnon, letellier, cyr, ricard, mathieu, proulx, savard consortium d'architectes.

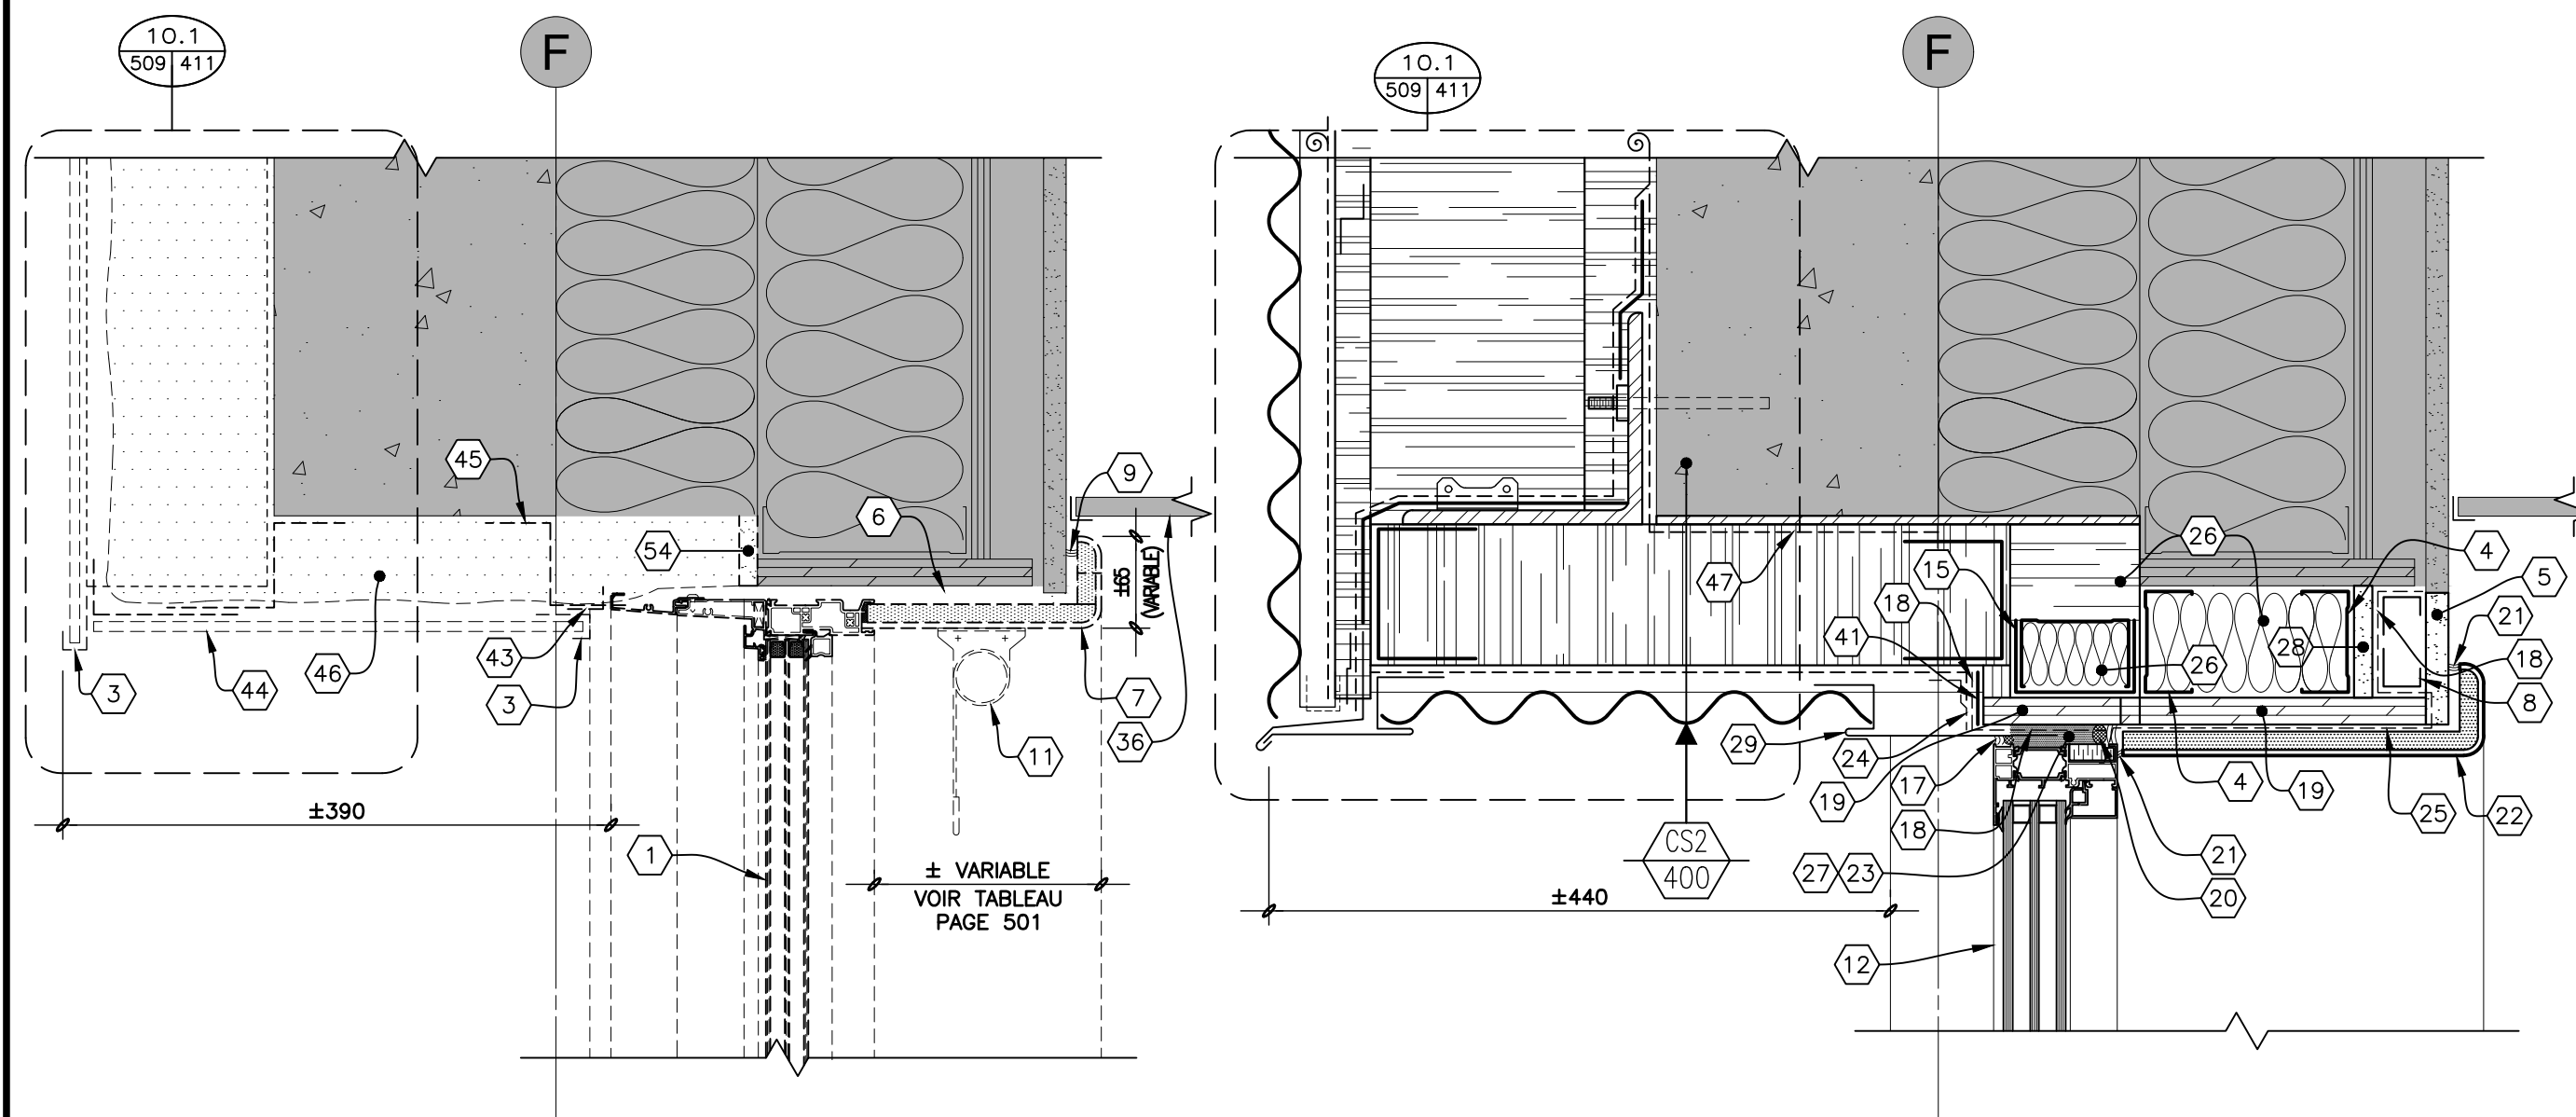


TÊTE

JAMBAGE

ALLÈGE

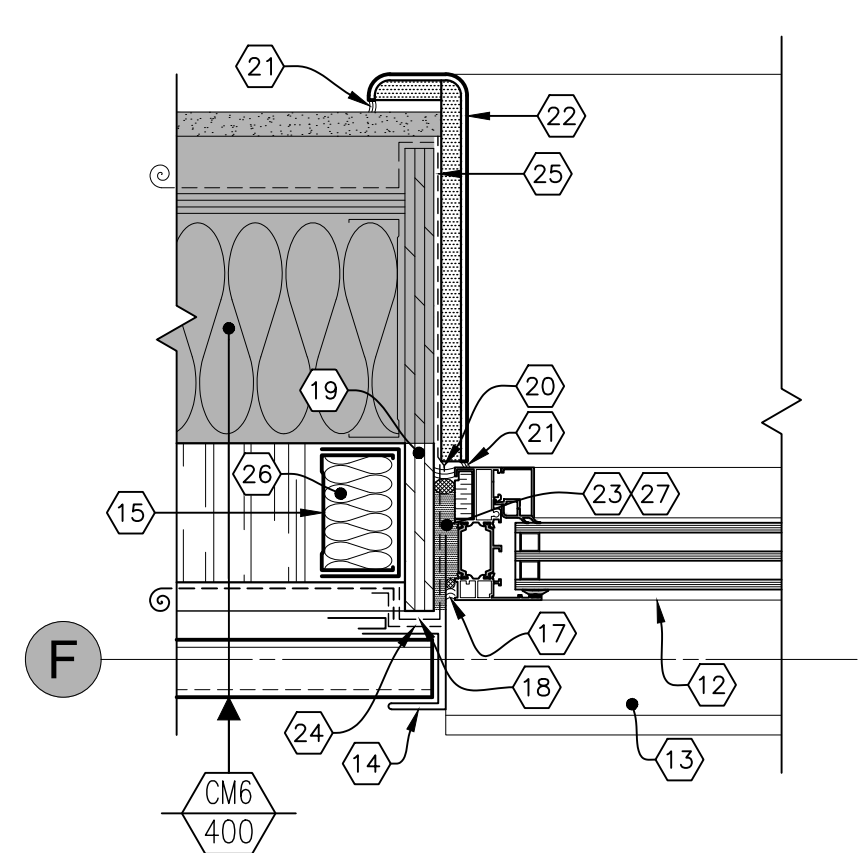


CONSTRUCTION

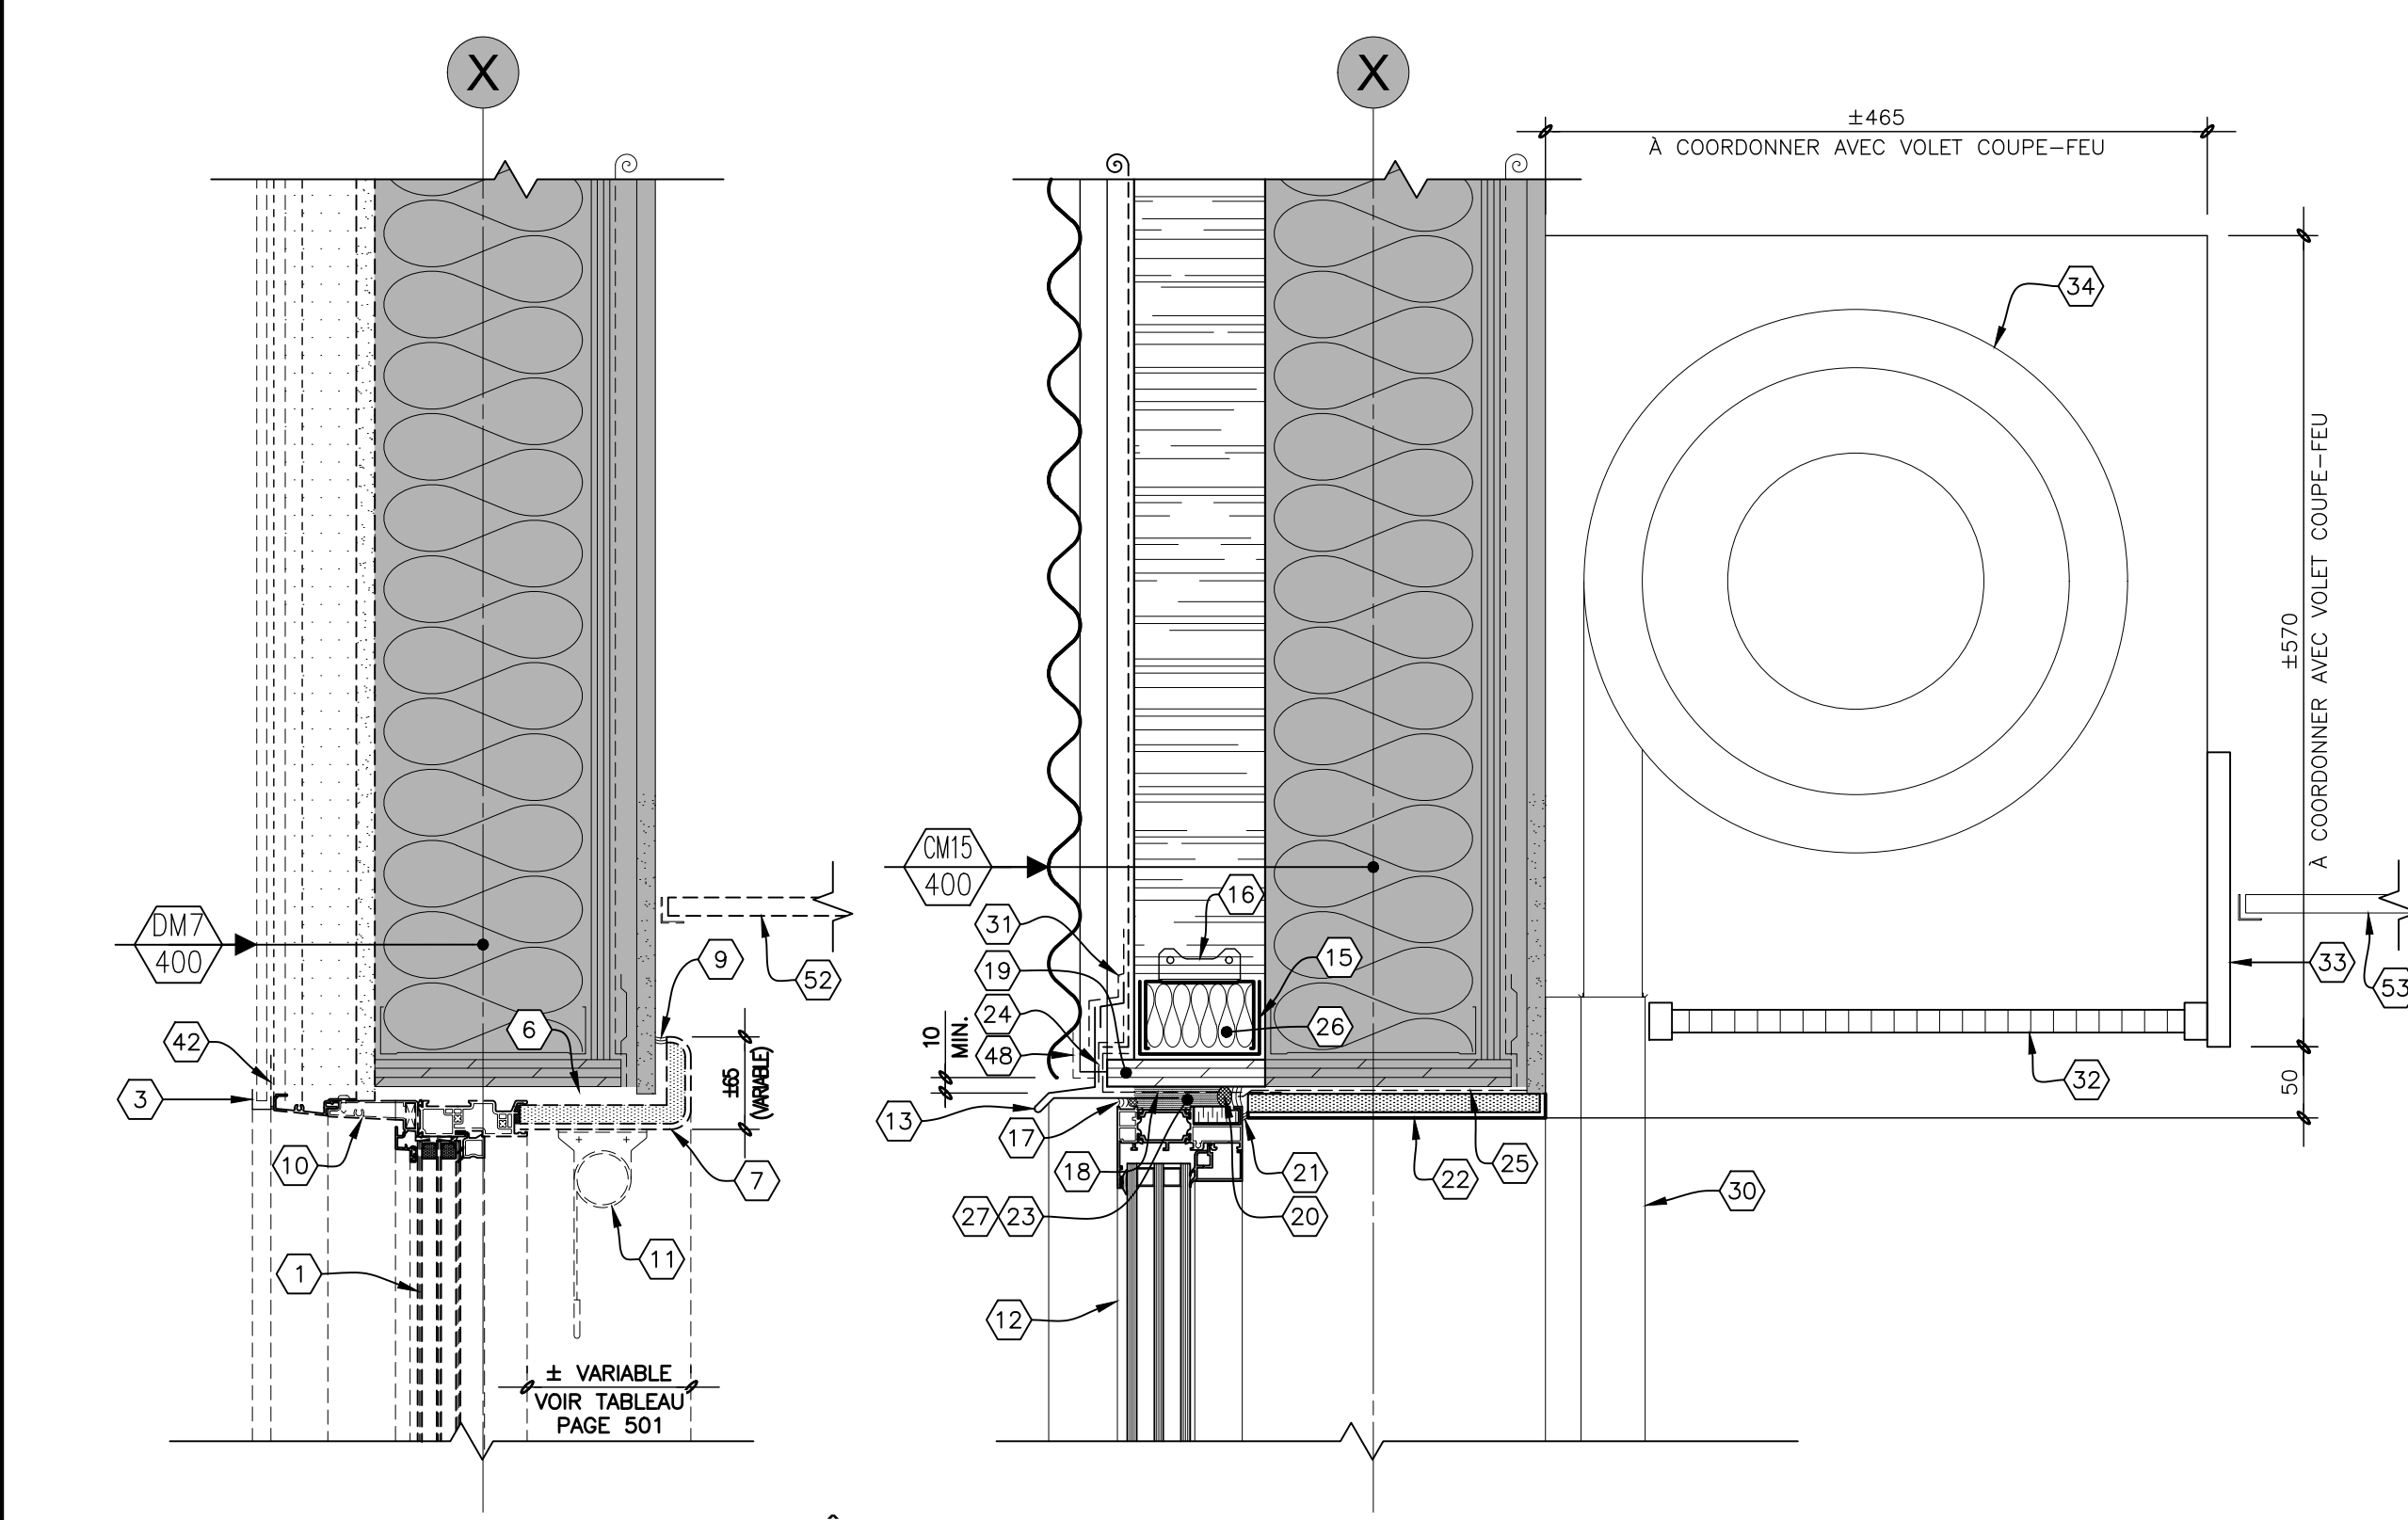

TÊTE

JAMBAGE

ALLÈGE

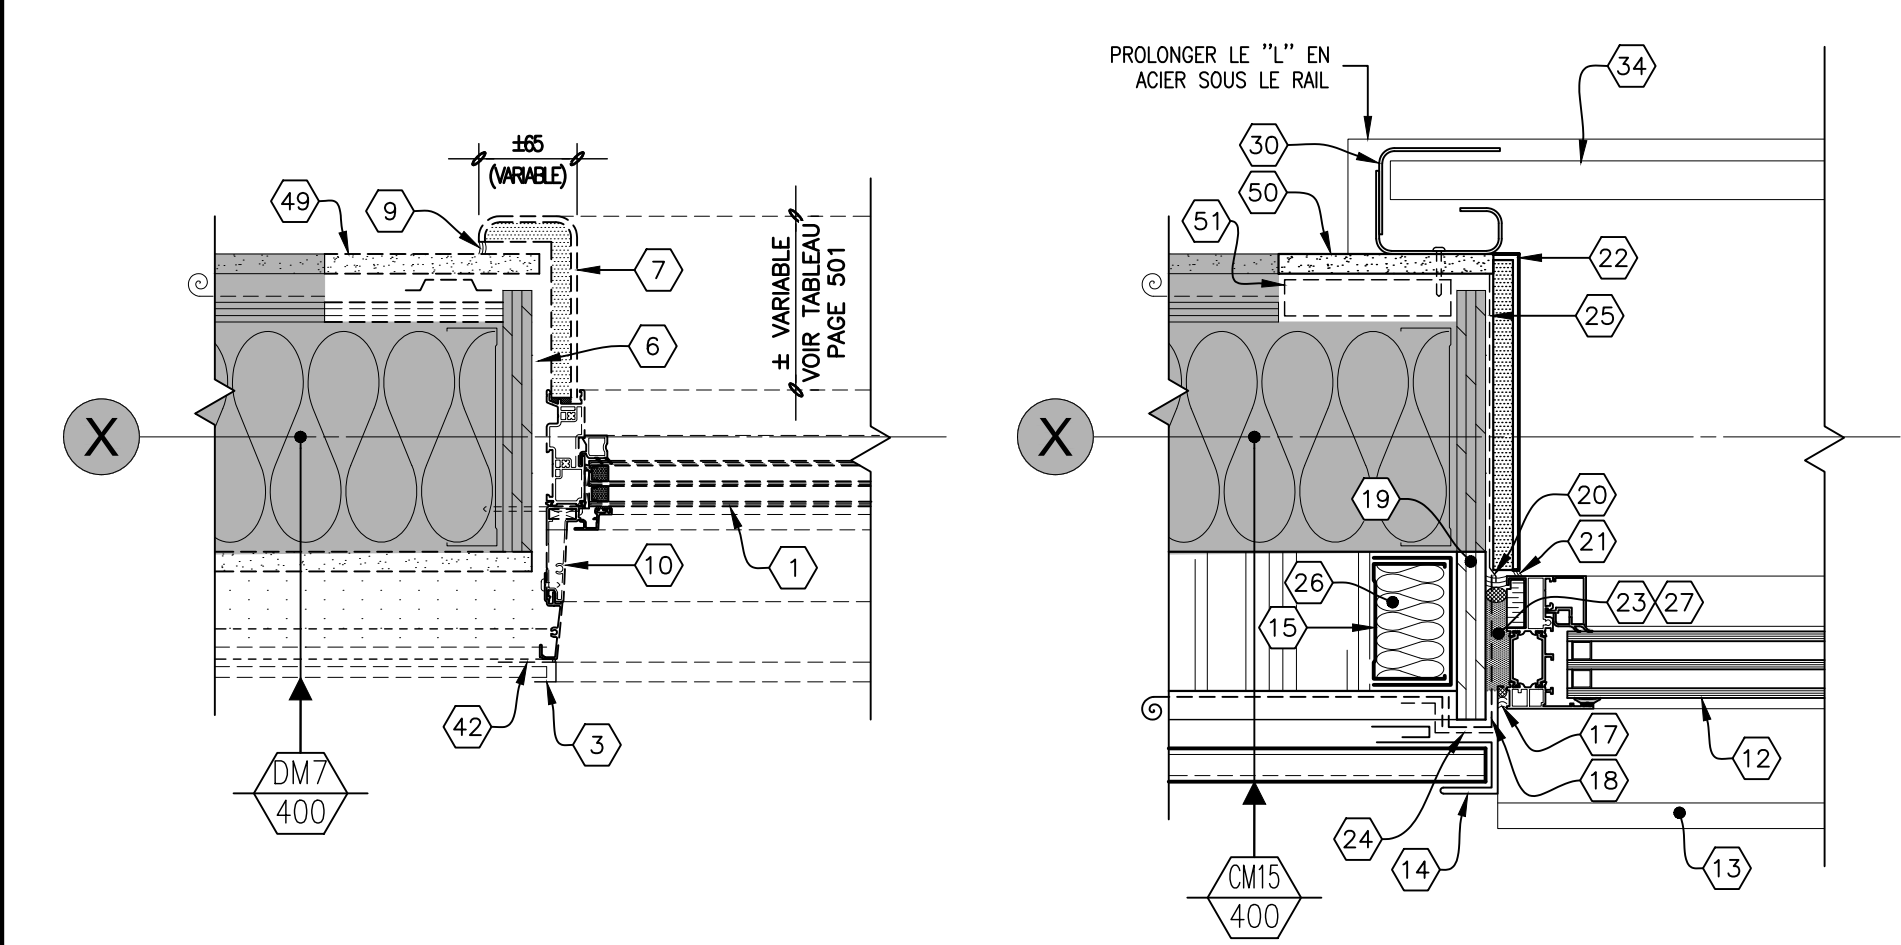

CONSTRUCTION

LÉGENDE	
	EXISTANT À CONSERVER.
	ÉLÉMENT À DÉMOLIR.
	AXE EXISTANT
	EXTÉRIEUR DE LA STRUCTURE DE BÉTON EXISTANTE DE LA TOUR.
	NOUVEL AXE; FACE EXTÉRIEURE DES BARRES Z ET COLOMBAGES DE LA TOUR. VOIR STRUCTURE.
(*) VOIR NOTE GÉNÉRAL PAGE 400.	

NOTES	
1	FENÊTRE HYBRIDE (ALUMINIUM/PVC) EXISTANTE À DÉMOLIR.
2	SOLIN EN ACIER ÉMAILLÉ EXISTANT À DÉMOLIR.
3	MOULURE EN ALUMINIUM À DÉMOLIR.
4	COLOMBAGE MÉTALLIQUE DE DIMENSIONS REQUISES.
5	PLAQUE DE PLÂTRE, 16mm D'ÉPAISSEUR, À PEINDRE.
6	MEMBRANE AUTOADHÉSIVE EXISTANTE À DÉMOLIR.
7	FINITION INTÉRIEURE EN CONTREPLAQUÉ RECOUVERT DE STRATIFIÉ À DÉMOLIR.
8	PLIAGE DE TÔLE EN ACIER GALVANISÉ CAL.16.
9	SCÉLLANT EXISTANT À ENLEVER. NETTOYER LES SURFACES EXISTANTES CONSERVÉES DE TOUTES TRACES DE SCÉLLANT.
10	SECTION DU CADRE DE FENÊTRE À COUPER ET À DÉMOLIR. VOIR DÉTAILS EN ÉTAPES À LA PAGE 505.
11	TÔLE, STORE ET/OU HABILLAGE DE FENÊTRE À ENLEVER ET À REMETTRE AU PROPRIÉTAIRE. VOIR NOTE PAGE 505.
12	NOUVELLE FENÊTRE EN ALUMINIUM.
13	SOLIN EN ACIER ÉMAILLÉ, CAL.24.
14	MOULURE EN "J" EN ACIER ÉMAILLÉ, CAL.24.
15	ASSEMBLAGE DE COLOMBAGE ET DE LISSE SUR TOUT LE PÉRIMÈTRE DE L'OUVERTURE, VOIR STRUCTURE.
16	CONNECTEUR, VOIR STRUCTURE.
17	SCÉLLANT SUR FOND DE JOINT.
18	MEMBRANE D'ÉTANCHÉITÉ AUTOADHÉSIVE SUR TOUT LE PÉRIMÈTRE DE L'OUVERTURE.
19	CONTREPLAQUÉ À PLUS 19mm D'ÉPAISSEUR.
20	BOUDIN D'ÉTAFOAM DE DIAMÈTRE APPROPRIÉ ET SCÉLLANT CONTINU SUR TOUT LE PÉRIMÈTRE DE LA FENÊTRE POUR ASSURER LA CONTINUITÉ DE L'ÉTANCHÉITÉ ENTRE LA MEMBRANE ET LE CADRE DE LA FENÊTRE.
21	SCÉLLANT DE FINITION.
22	FINITION EN CONTREPLAQUÉ À PLUS 19mm D'ÉPAISSEUR RECOUVERT DE PLASTIQUE STRATIFIÉ, COIN ARRONDÉ SUR TOUT LE PÉRIMÈTRE DE L'OUVERTURE. COULEUR AU CHOIX DE L'ARCHITECTE.
23	POLYURÉTHANE GICLÉ NON EXPANSIF SUR LE PÉRIMÈTRE DE LA FENÊTRE.
24	RUBAN AUTOCOLLANT. SCÉLLER LA MEMBRANE PARE-INTÉRIÈRES AVEC LA MEMBRANE AUTOADHÉSIVE.
25	MEMBRANE AUTOADHÉSIVE PARE-VAPEUR SUR TOUT LE PÉRIMÈTRE DE L'OUVERTURE. SCÉLLER SUR LA NOUVELLE MEMBRANE SOUS LE CADRE DE FENÊTRE ET SUR LE POLYÉTHYLÈNE DU MUR EXISTANT.
26	REMPLIR L'ESPACE DE LAINE DE FIBRE DE ROCHE.
27	CALE D'AJUSTEMENT EN POLYVINYLE RIGIDE D'ÉPAISSEUR REQUISE.
28	PLAQUE DE PLÂTRE, 13mm D'ÉPAISSEUR.
29	MOULURE EN ACIER ÉMAILLÉ, CAL.24.
30	RAIL DU VOLET COUPE-FEU À PEINTURER TEL QUE LE MUR.
31	RUBAN AUTOCOLLANT.
32	DIFFUSEUR D'ÉCLAIRAGE PERFORÉ AMOVIBLE, COULEUR CHROME.
33	PANNEAU DE PARTICULES AGLOMÉRÉES HAUTE DENSITÉ, 16mm, FINI MÉLAMINE, COULEUR AU CHOIX DE L'ARCHITECTE.
34	VOLET COUPE-FEU, VOIR DEVIS.
35	PIÈCE DE BOIS EXISTANTE À DÉMOLIR.
36	PLAFOND SUSPENDU (HAUTEUR VARIABLE), À CONSERVER.
37	"L" EN ACIER 76x89mm X 4mm D'ÉPAISSEUR À PEINDRE, COULEUR TEL QUE LE MUR.
38	LISSE DE DÉFLEXION VOIR STRUCTURE.
39	COLOMBAGE MÉTALLIQUE 92mm, VOIR STRUCTURE.
40	ISOLANT SEMI-RIGIDE DE FIBRE DE ROCHE 89mm D'ÉPAISSEUR.
41	TÔLE D'APPUI, CAL.18.
42	TÔLE EXISTANTE RIVETÉE SUR LA BARRE EN "Z" ET AU CADRE DE LA FENÊTRE À DÉMOLIR.
43	ACIER ÉMAILLÉ À DÉMOLIR.
44	URÉTHANE GICLÉ EXISTANT À DÉMOLIR. GRATTER ET NETTOYER TOUT RÉSIDUS SUR LE BÉTON.
45	BARRE EN "Z" EXISTANTE À DÉMOLIR.
46	PANNEAU DE POLYMÈRES RENFORCÉ DE FIBRES DE VERRE À DÉMOLIR.
47	PLAQUE D'ACIER STRUCTURALE, VOIR STRUCTURE.
48	MOUSTIQUAIRE.
49	OUVRIR LE MUR POUR L'INSTALLATION DU FOND DE CLOUAGE.
50	PLAQUE DE PLÂTRE DE MÊME ÉPAISSEUR QUE CELUI EXISTANT. À PLÂTRER ET À PEINDRE.
51	FOND DE CLOUAGE EN ACIER GALVANISÉ CAL.16, FIXÉ AU COLOMBAGE EXISTANT POUR LA FIXATION DU "L" EN ACIER.
52	PLAFOND SUSPENDU À DÉMANTÉLER SUR LA DIMENSION REQUISE POUR L'INSTALLATION DU VOLET COUPE-FEU DANS L'ENTREPLAFOND.
53	PLAFOND SUSPENDU EXISTANT À RÉINSTALLER AVEC NOUVELLE SUSPENSION EN ALUMINIUM ET NOUVELLES TUILLES.
54	PANNEAU DE GYPSE EXISTANT À DÉMOLIR.
55	BOULON D'ANCRAGE DE DIMENSION REQUISE À PEINDRE.

NE DOIT PAS SERVIR À L'EXÉCUTION

Le présent document est émis par la seule fin d'identifier. Son contenu est protégé par les droits d'auteur et toute reproduction ou modification, partielle ou totale, est interdite sans l'autorisation écrite de gagnon, letellier, cyr, ricard, mathieu, proulx, savard consortium d'architectes.

GLCRM | Proulx Savard |
GLCRM:
128, Avenue de la Cathédrale,
Bureau 201
Rimouski, QC, G5L 5H7
(418) 722-7655
2406, Ch. des Quatre-Bourgeois,
Bureau 100
Québec, QC, G1V 1W5
(418) 647-1700
Proulx Savard Architectes:
75, boul. Arthur-Buies Ouest,
Rimouski QC G5L 5C2
(418) 723-5543
ARCHITECTURE


DESSINATEUR (S)	DATE	REVISIONS
AL. D.B.	24-10-27 16:57-24	
INDICÉE	SEPTEMBRE 2024	
05	2024-09-04	DÉFINITIVES POUR SOUMISSION
04	2024-08-21	DÉFINITIVES 100% POUR APPROBATION
03	2024-08-03	DÉFINITIVES 80% POUR APPROBATION
02	2024-05-14	DÉFINITIVES 40% POUR APPROBATION
01	2024-02-27	PRÉLIMINAIRES 20% POUR APPROBATION

DESSIN
DÉTAIL TYPE DE FENÊTRE (BASILAIRE)
DÉMOLITION ET CONSTRUCTION



PROJET
HÔPITAL DE CHANDLER,
Chandler
(Réfection de l'enveloppe)

PROPRIÉTAIRE
Santé Québec



509

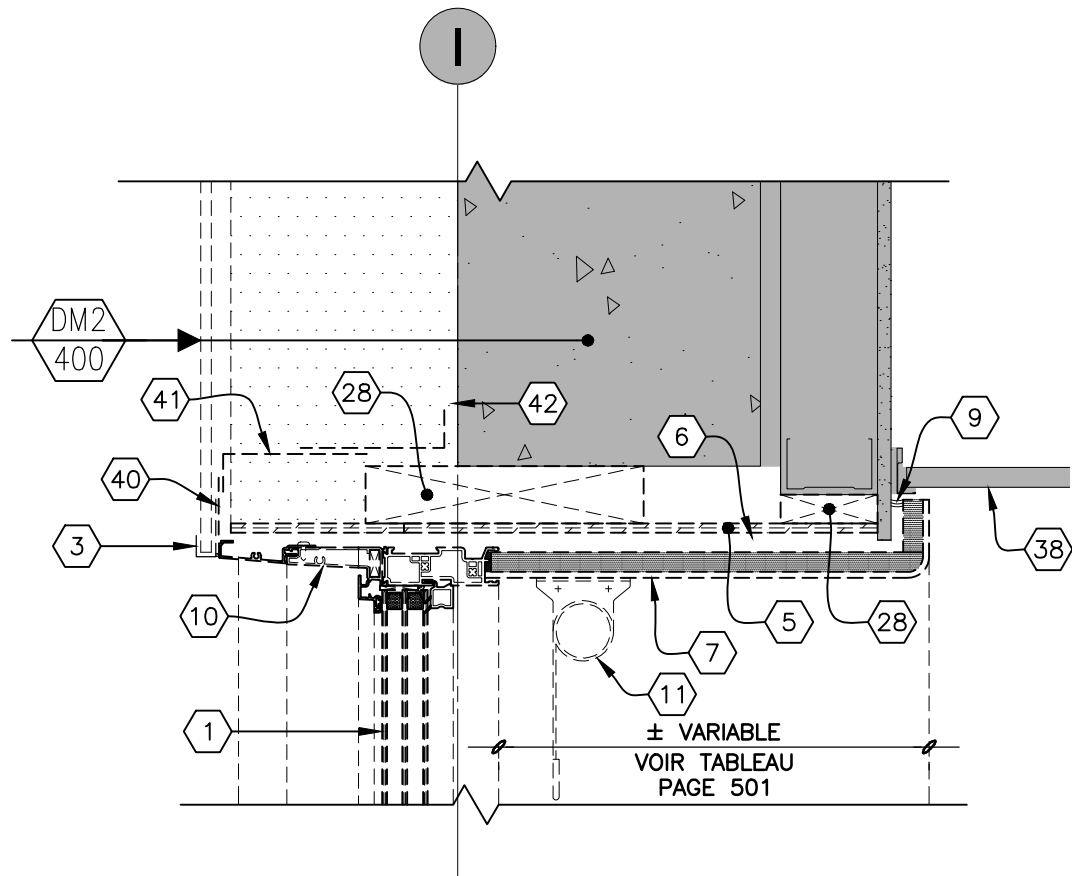

TÊTE

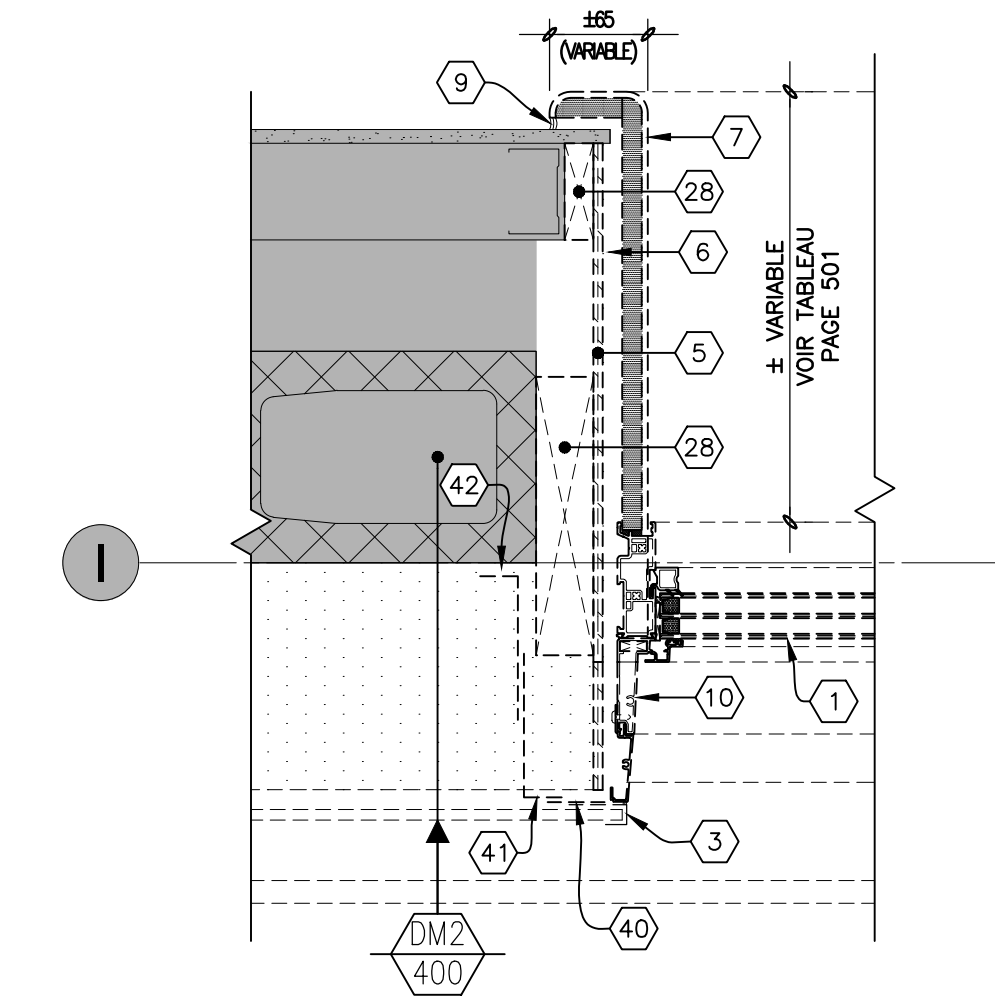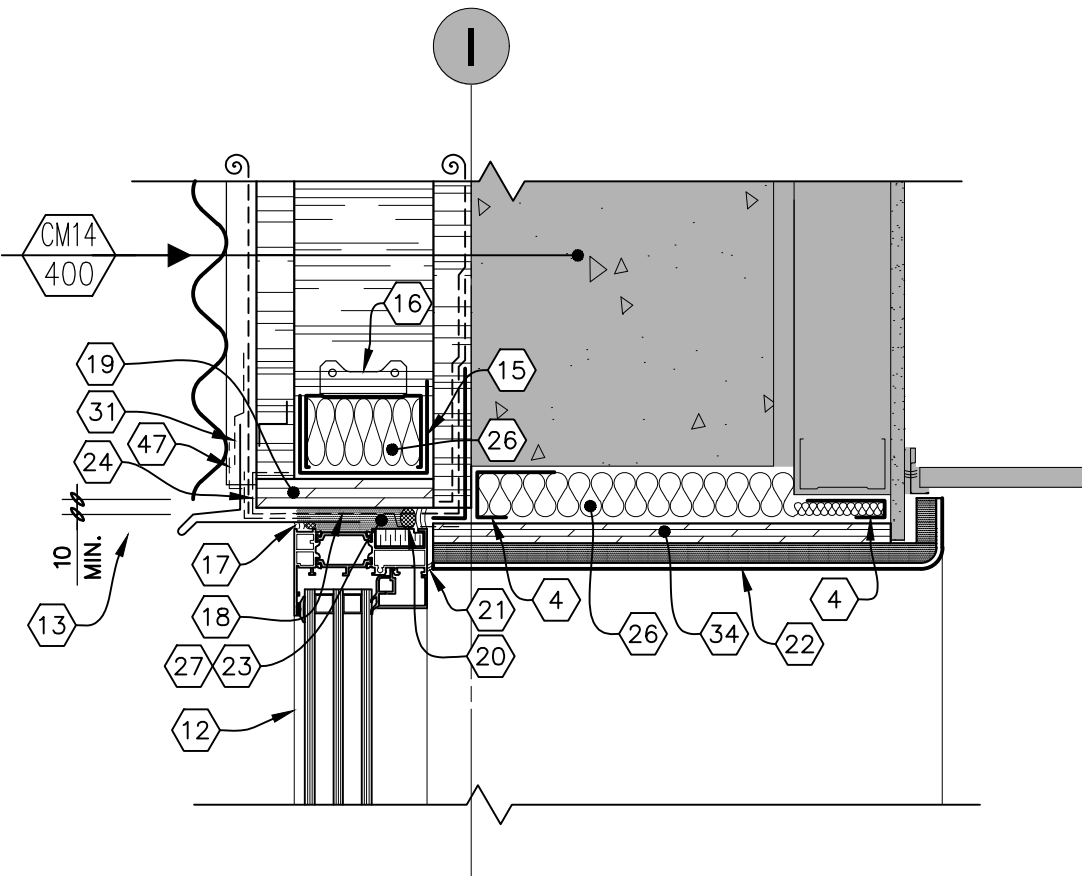

JAMBAGE

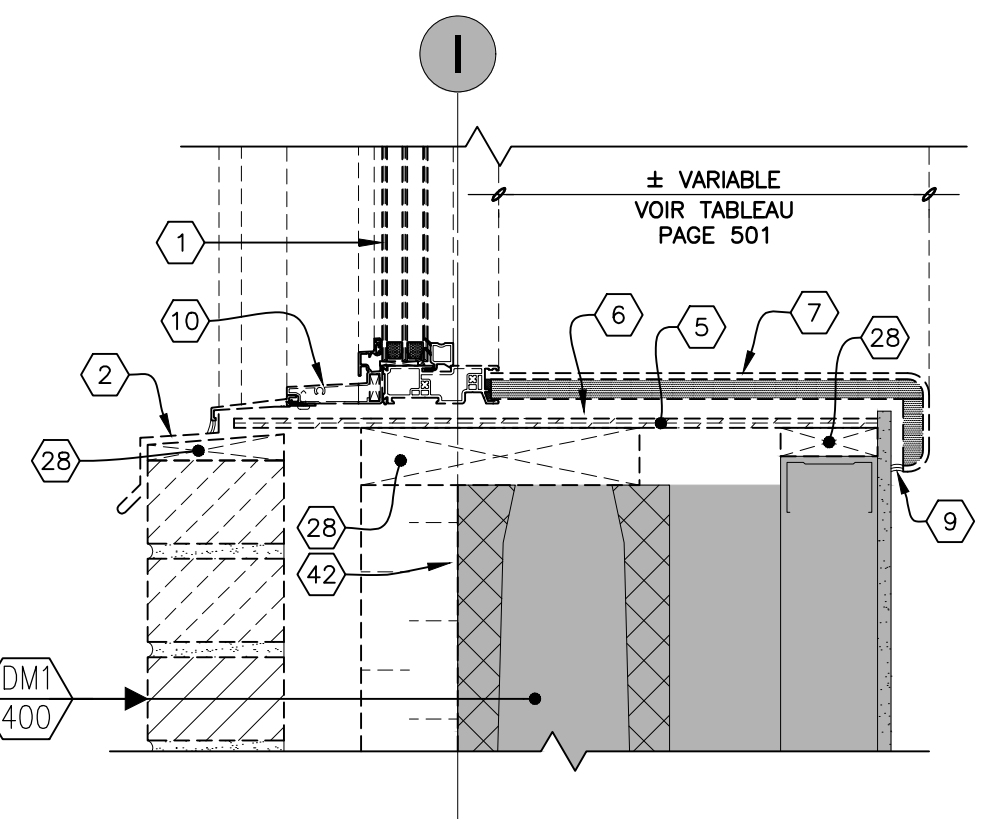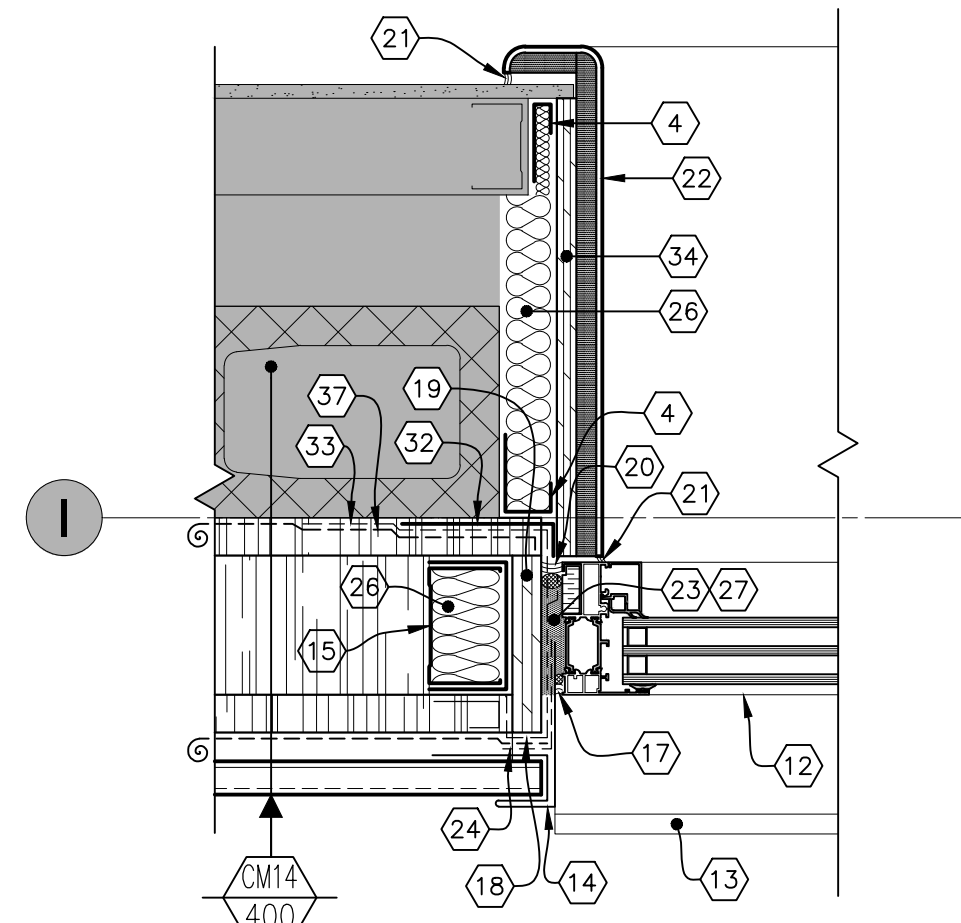


DÉMOLITION

15
502,503 510
1:5mm


DÉTAIL DE FENÊTRE TYPE (BASILAIRE)

(ONCOLOGIE 1974 - NIVEAU RDC)

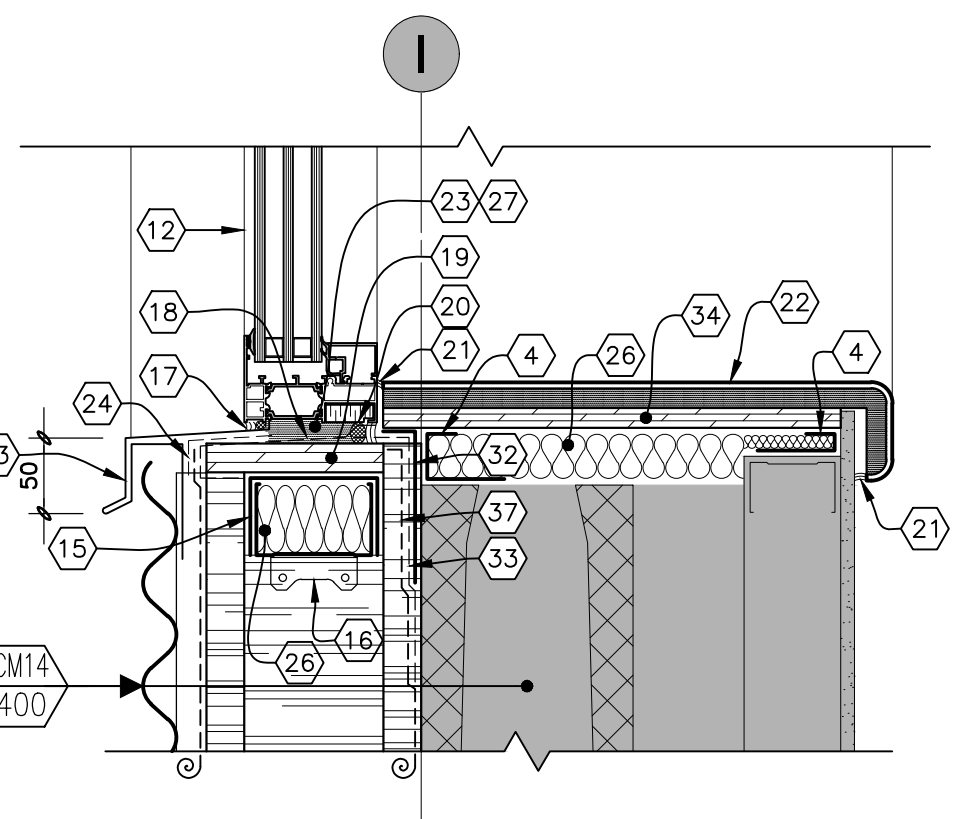


ALLÈGE



CONSTRUCTION

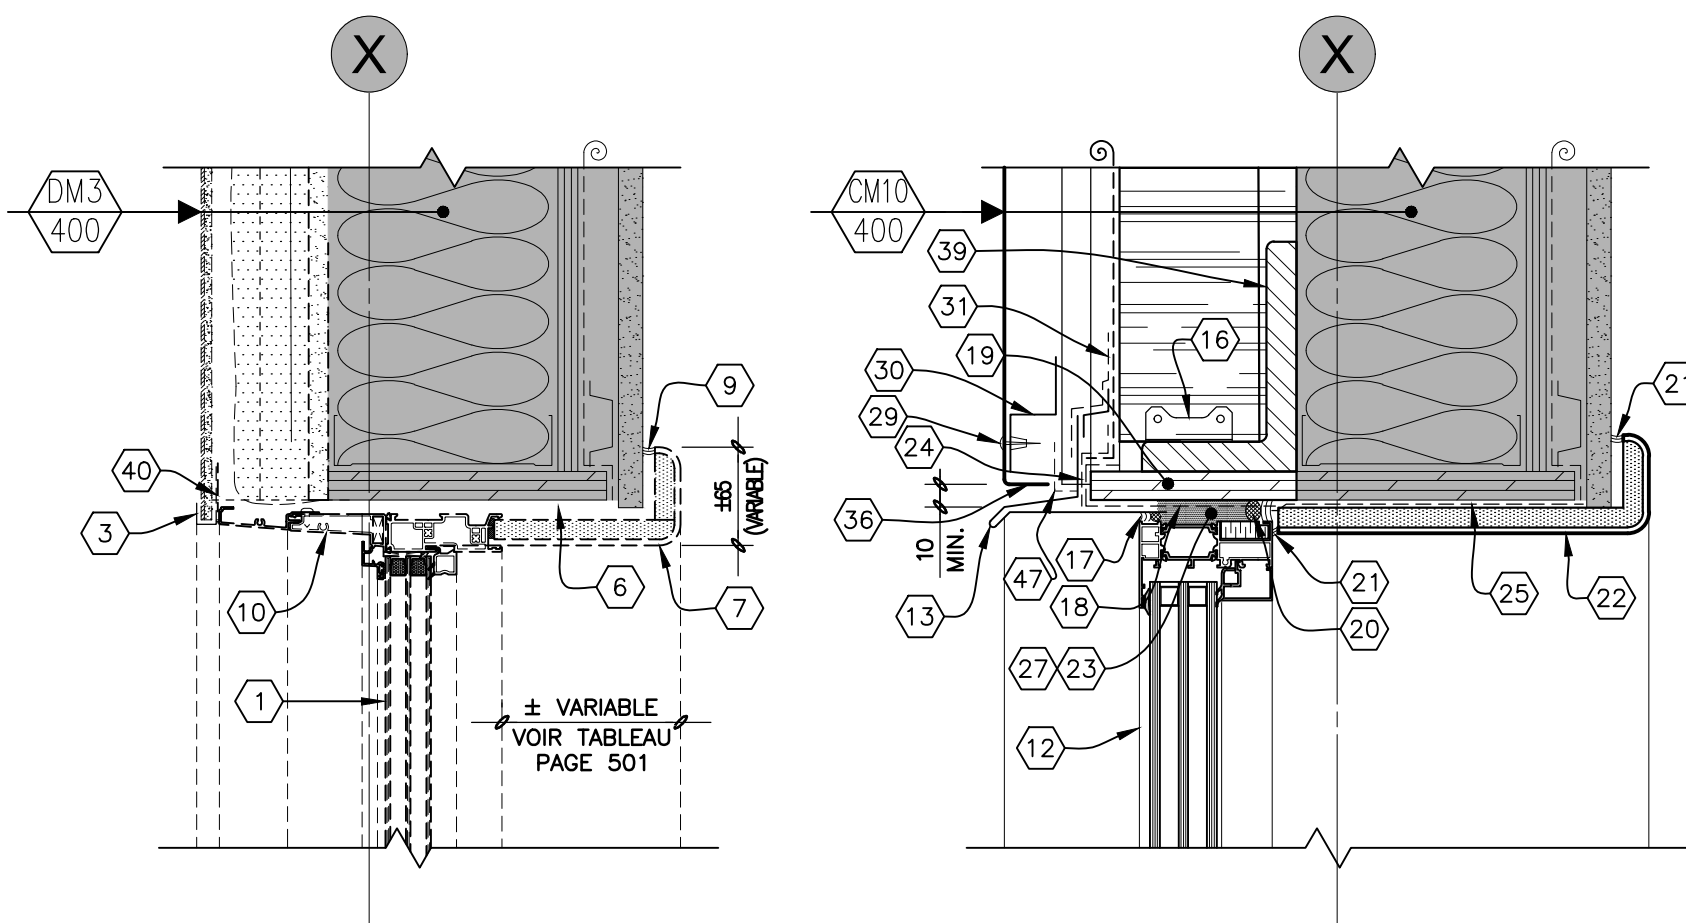

TÊTE

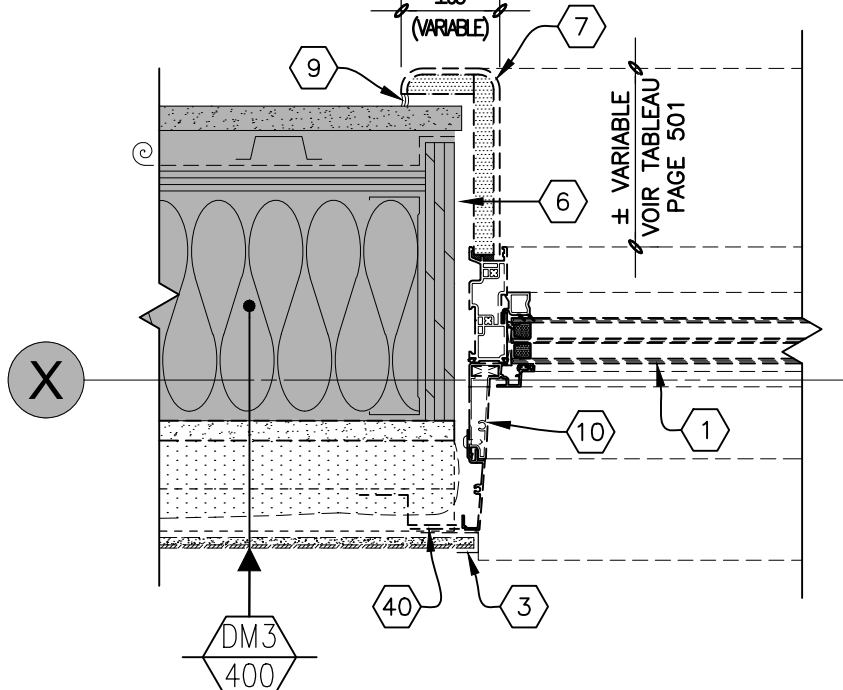

JAMBAGE

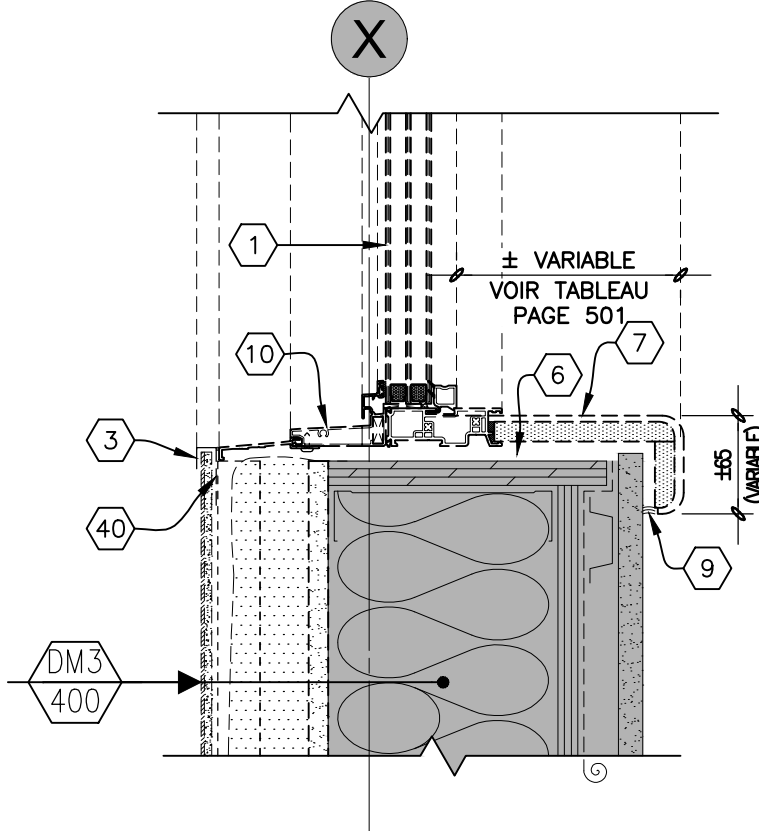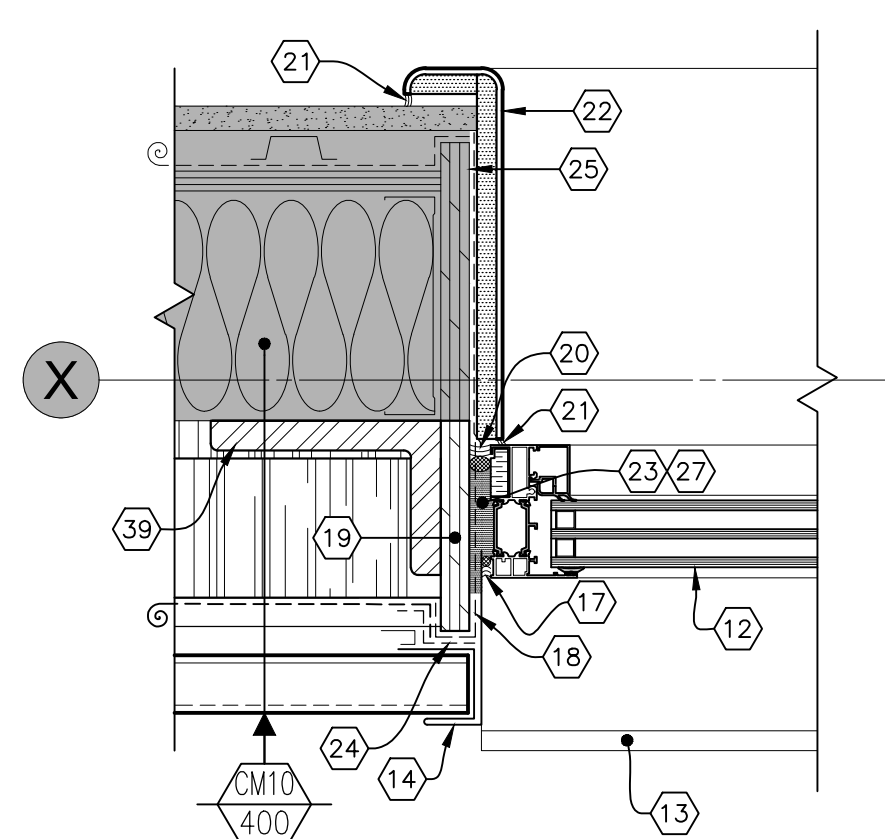


DÉMOLITION


17
502,503 510
1:5mm

DÉTAIL DE FENÊTRE - ESCALIER #6

ALLÈGE

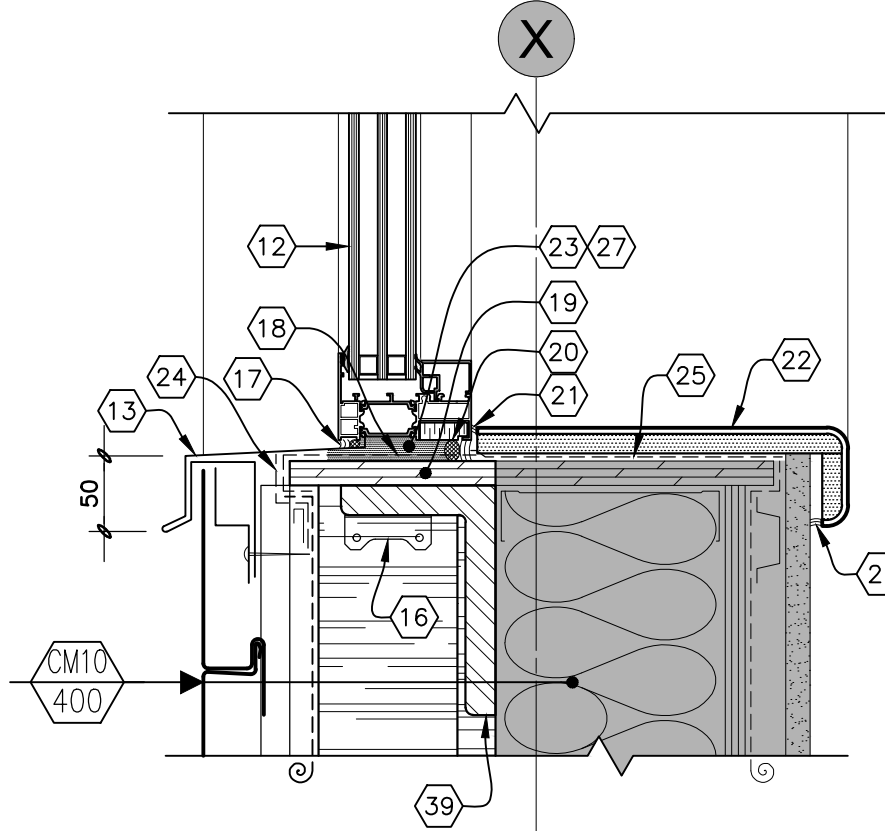

CONSTRUCTION

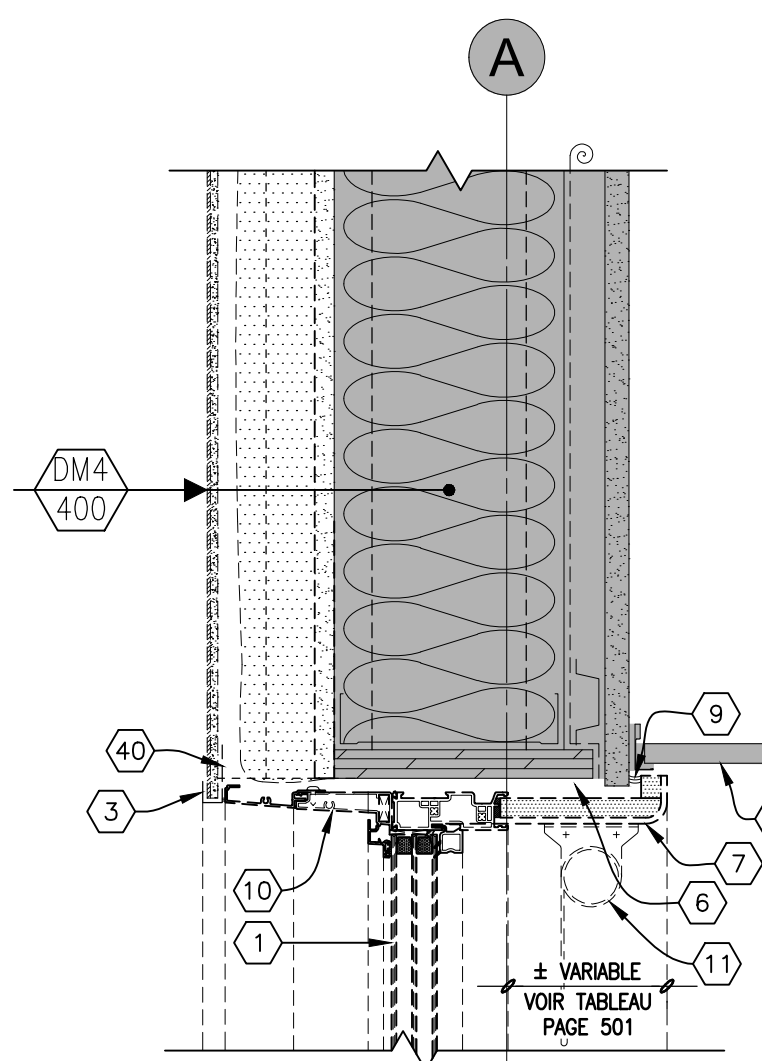


DÉMOLITION

16
502,503 510
1:5mm

DÉTAIL - TÊTE DE FENÊTRE

(LABORATOIRE - NIVEAU 100)

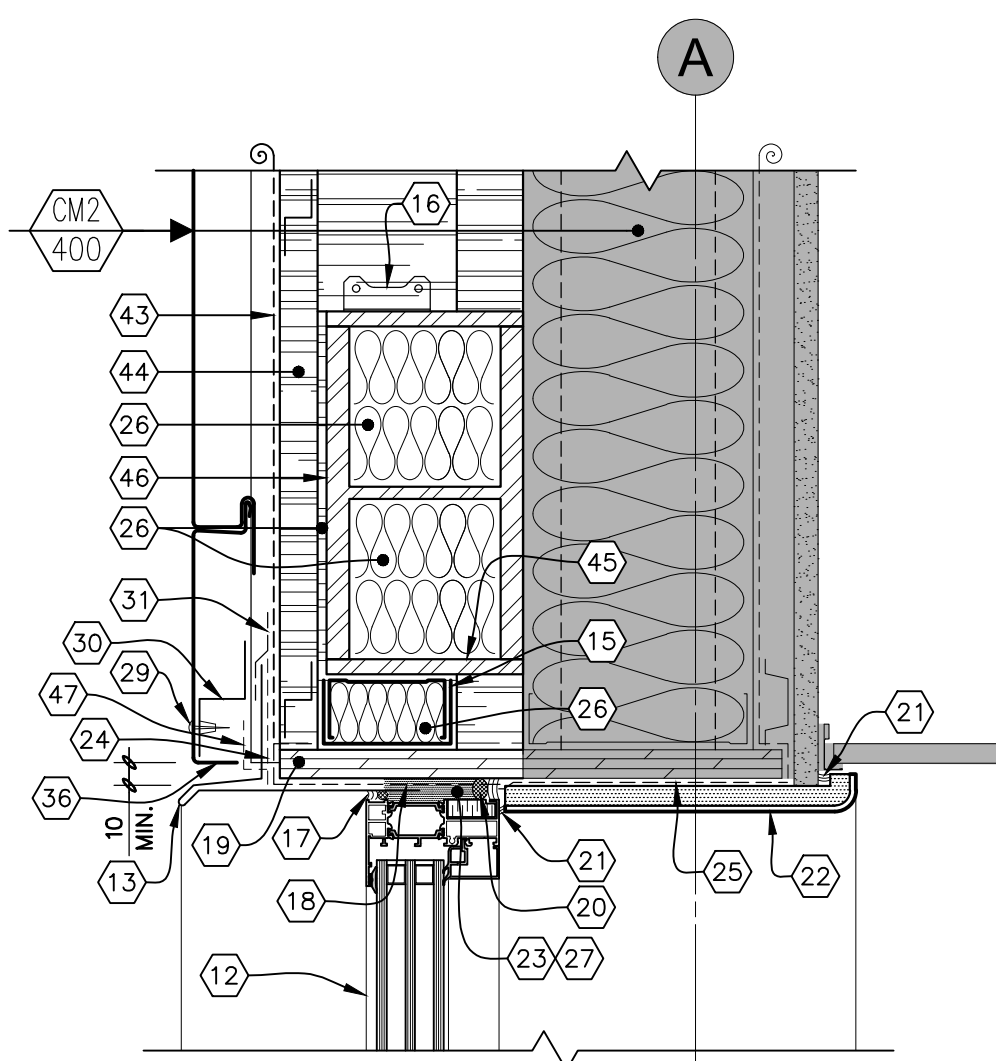

CONSTRUCTION

NOTES


- FENÊTRE HYBRIDE (ALUMINIUM/PVC) EXISTANTE À DÉMOLIR.
- SOLIN EN ACIER ÉMAILLÉ EXISTANT À DÉMOLIR.
- MOULURE EN ALUMINIUM À DÉMOLIR.
- PLIAGE DE TOLE EN ACIER ÉMAILLÉ, CAL.18.
- CONTREPLAQUÉ EXISTANT À DÉMOLIR.
- MEMBRANE AUTOADHESIVE EXISTANTE À DÉMOLIR.
- FINITION INTÉRIEURE EN CONTREPLAQUÉ RECOUVRENT DE STRATIFIÉ À DÉMOLIR.
- TOLE PLIÉE EXISTANTE À DÉMOLIR.
- SCÉLANT EXISTANT À ENLEVER. NETTOYER LES SURFACES EXISTANTES CONSERVÉES DE TOUTES TRACES DE SCÉLANT.
- SECTION DU CADRE DE FENÊTRE À COUPER ET À DÉMOLIR. VOIR DÉTAILS EN ÉTAPES À LA PAGE 505.
- TOILE, STORE ET/OU HABILLAGE DE FENÊTRE À ENLEVER ET À REMETTRE AU PROPRIÉTAIRE. VOIR NOTE PAGE 505.
- NOUVELLE FENÊTRE EN ALUMINIUM.
- SOLIN EN ACIER ÉMAILLÉ, CAL.24.
- MOULURE EN "J" EN ACIER ÉMAILLÉ, CAL.24.
- ASSEMBLAGE DE COLOMBAGE ET DE LISSE SUR TOUT LE PÉRIMÈTRE DE L'OUVERTURE. VOIR STRUCTURE.
- CONNECTEUR. VOIR STRUCTURE.
- SCÉLANT SUR FOND DE JOINT.
- MEMBRANE D'ÉTANCHÉITÉ AUTOADHESIVE SUR TOUT LE PÉRIMÈTRE DE L'OUVERTURE.
- CONTREPLAQUÉ À PLUS 19mm D'ÉPAISSEUR.
- BOUDIN D'ÉTAFOAM DE DIAMÈTRE APPROPRIÉ ET SCÉLANT CONTINU SUR TOUT LE PÉRIMÈTRE DE LA FENÊTRE POUR ASSURER LA CONTINUITÉ DE L'ÉTANCHÉITÉ ENTRE LA MEMBRANE ET LE CADRE DE LA FENÊTRE.
- SCÉLANT DE FINITION.
- FINITION EN CONTREPLAQUÉ À PLUS 19mm D'ÉPAISSEUR RECOUVRENT DE PLASTIQUE STRATIFIÉ. COIN ARRONDI SUR TOUT LE PÉRIMÈTRE DE L'OUVERTURE. COULEUR AU CHOIX DE L'ARCHITECTE.
- POLYURÉTHANE GICLÉ NON EXPANSIF SUR LE PÉRIMÈTRE DE LA FENÊTRE.
- RUBAN AUTOCOLLANT. SCÉLER LA MEMBRANE PARE-INTÉRIÈRES AVEC LA MEMBRANE AUTOADHESIVE.
- MEMBRANE AUTOADHESIVE PARE-VAPEUR SUR TOUT LE PÉRIMÈTRE DE L'OUVERTURE. SCÉLER SUR LA NOUVELLE MEMBRANE SOUS LE CADRE DE FENÊTRE ET SUR LE POLYÉTHYLENE DU MUR EXISTANT.
- REMPLIR L'ESPACE DE LAINE DE FIBRE DE ROCHE.
- CALE D'AJUSTEMENT EN POLYVINYLE RIGIDE D'ÉPAISSEUR REQUISE.
- PIÈCE DE BOIS EXISTANTE À DÉMOLIR.
- RIVET EN ACIER PRÉPEINT, DE MÊME COULEUR QUE LE PAREMENT.
- PLIAGE DE TOLE EN ACIER GALVANISÉ CAL. 22.
- RUBAN AUTOCOLLANT.
- TOLE PLIÉE EN ACIER GALVANISÉ 75mm X 75mm, CAL. 16, AU POURTOUR DE L'OUVERTURE.
- MEMBRANE AUTOCOLLANTE PARE-VAPEUR.
- CONTREPLAQUÉ À PLUS D'ÉPAISSEUR REQUISE.
- CONTREPLAQUÉ À PLUS 19mm RECOUVRENT D'UNE MEMBRANE AUTOCOLLANTE ET D'UNE TOLE PLIÉE EN ACIER ÉMAILLÉ, CAL. 24, COULEUR AU CHOIX DE L'ARCHITECTE.
- BOUT DU PANNEAU REPLIÉ VERS L'INTÉRIEUR.
- MEMBRANE LIQUIDE PULVÉRISÉE PAR-DESSUS LA MEMBRANE AUTOADHESIVE.
- PLAFOND SUSPENDU (HAUTEUR VARIABLE), À CONSERVER.
- CORNIERE 102X152X19mm, VOIR INGÉNIEUR.
- TOLE EXISTANTE RIVETÉE SUR LA BARRE EN "Z" ET AU CADRE DE LA FENÊTRE À DÉMOLIR.
- BARRE EN "Z" AJUSTABLE EXISTANTE À DÉMOLIR.
- MEMBRANE AUTOCOLLANTE EXISTANTE À DÉMOLIR.
- MEMBRANE PARE-INTÉRIÈRE (TYPE 3), JOINTS CHEVAUCHÉS.
- ISOLANT SEMI-RIGIDE DE FIBRE DE ROCHE 25mm D'ÉPAISSEUR.
- PLAQUE PONCTUELLE, VOIR STRUCTURE.
- POUTRE D'ACIER, VOIR STRUCTURE.
- MOUSTIQUEAIRE.

LÉGENDE

- EXISTANT À CONSERVER.
- ÉLÉMENT À DÉMOLIR.
- X AXE EXISTANT
- EX EXTÉRIEUR DE LA STRUCTURE DE BÉTON EXISTANTE DE LA TOUR.
- NS NOUVEL AXE: FACE EXTÉRIÈRE DES BARRES Z ET COLOMBAGES DE LA TOUR. VOIR STRUCTURE. (*) VOIR NOTE GÉNÉRAL PAGE 400.

NE DOIT PAS SERVIR À L'EXÉCUTION

Le présent document est émis pour la seule fin identifiée. Son contenu est protégé par les droits d'auteur et toute reproduction ou modification, partielle ou totale, est interdite sans l'autorisation écrite de gagnon, letellier, cyr, ricard, mathieu, proulx, savard consortium d'architectes.

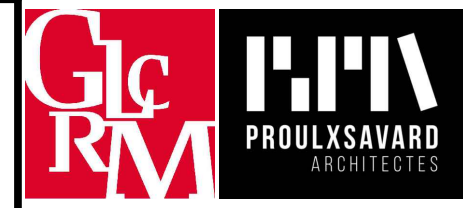


GLCRM | Proulx Savard |

GLCRM:
128, Avenue de la Cathédrale,
Bureau 201
Rimouski, QC, G5L 5H7
(418) 722-7655


2406, Ch. des Quatres-Bourgeois,
Bureau 100
Québec, QC, G1V 1W5
(418) 647-1700

Proulx Savard Architectes:
75, boul. Arthur-Buies Ouest,
Rimouski QC G5L 5C2
(418) 722-5543

ARCHITECTURE

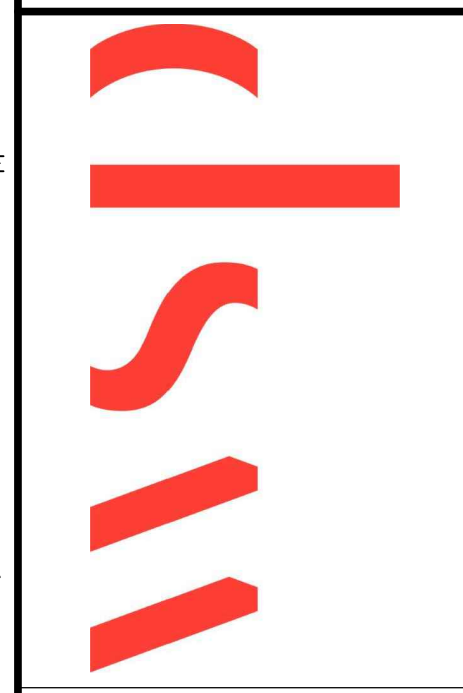


CONSULTANTS

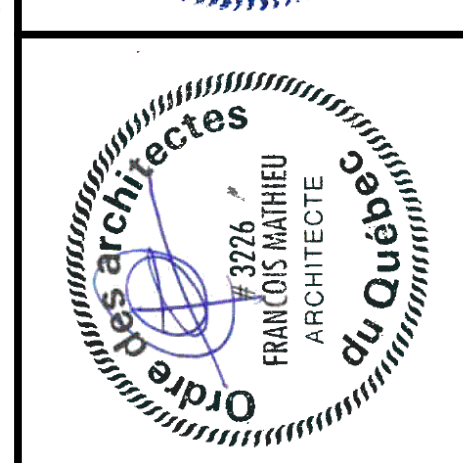


DESSINATEUR (S)		DOSSIER No.
ALL. D.B.		24-1087 / 1687-24
ÉCHELLE		DATE
INDIQUÉE		SEPTEMBRE 2026
05	2026-09-04	DÉFINITIFS POUR SOUMISSION
04	2026-08-21	DÉFINITIFS 100% POUR APPROBATION
03	2026-08-03	DÉFINITIFS 80% POUR APPROBATION
02	2026-05-14	DÉFINITIFS 40% POUR APPROBATION
01	2026-02-27	PRÉLIMINAIRES 20% POUR APPROBATION
No	DATE	REVISIONS


DESSIN	PROJET	PROPRIÉTAIRE
DÉTAIL TYPE DE FENÊTRE (BASILAIRE) DÉMOLITION ET CONSTRUCTION	HÔPITAL DE CHANDLER, Chandler (Redaction de l'enveloppe)	Santé Québec

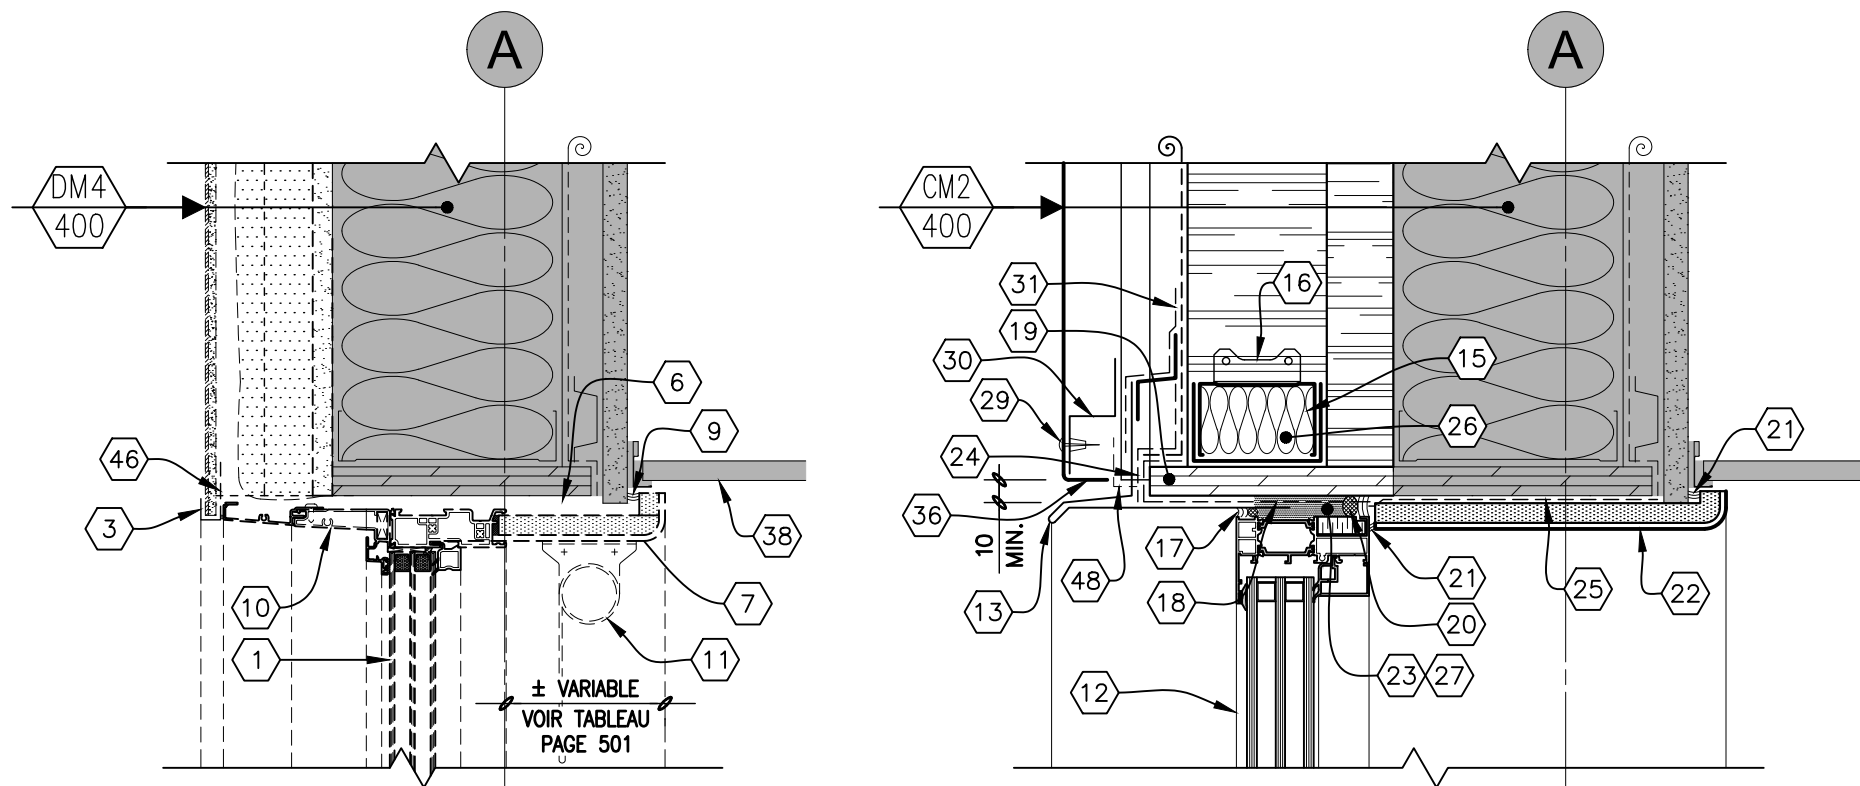

TÊTE

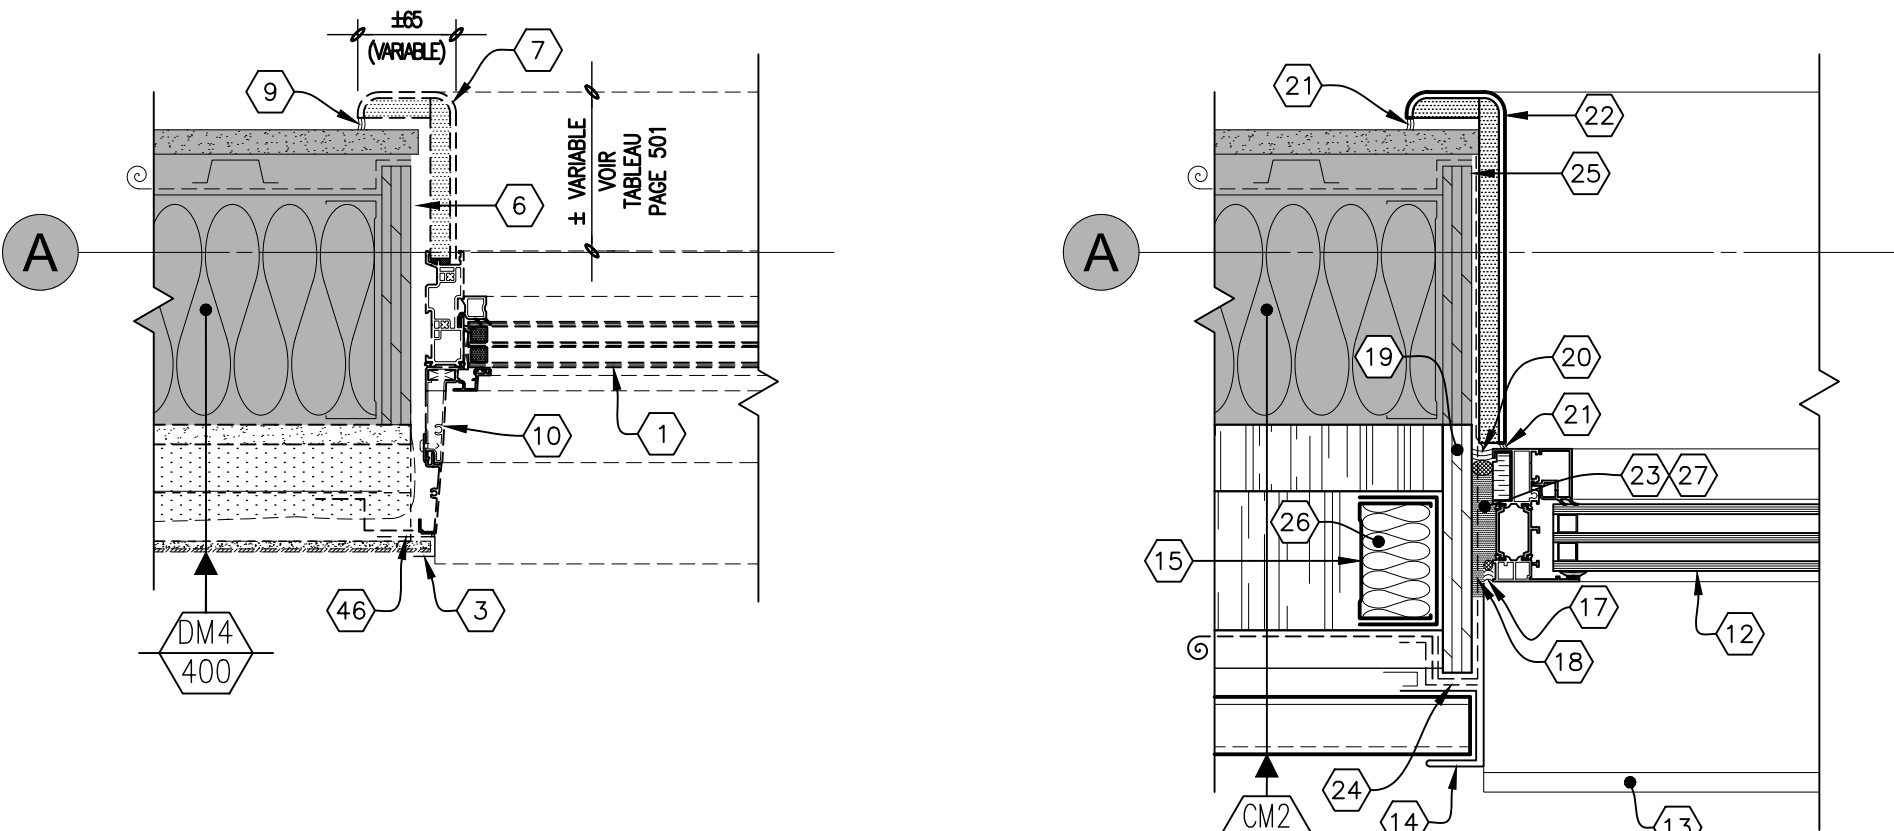

JAMBAGE

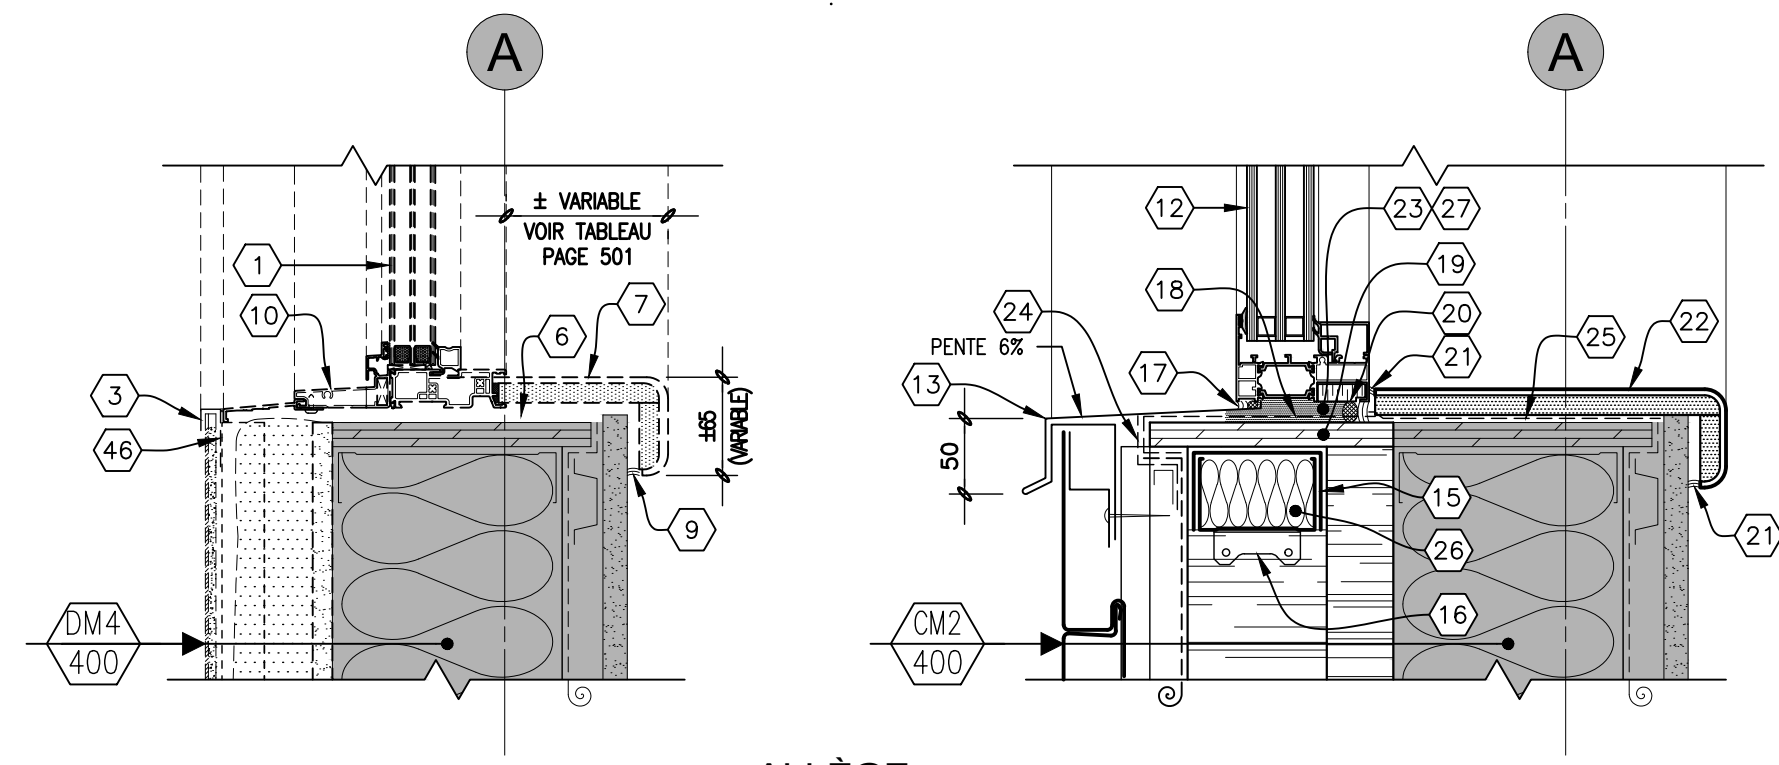


DÉMOLITION


ALLÈGE

CONSTRUCTION


18 DÉTAIL DE FENÊTRE TYPE (BASILAIRE)
502.503 511 1:5mm (LABORATOIRE - NIVEAU 100)

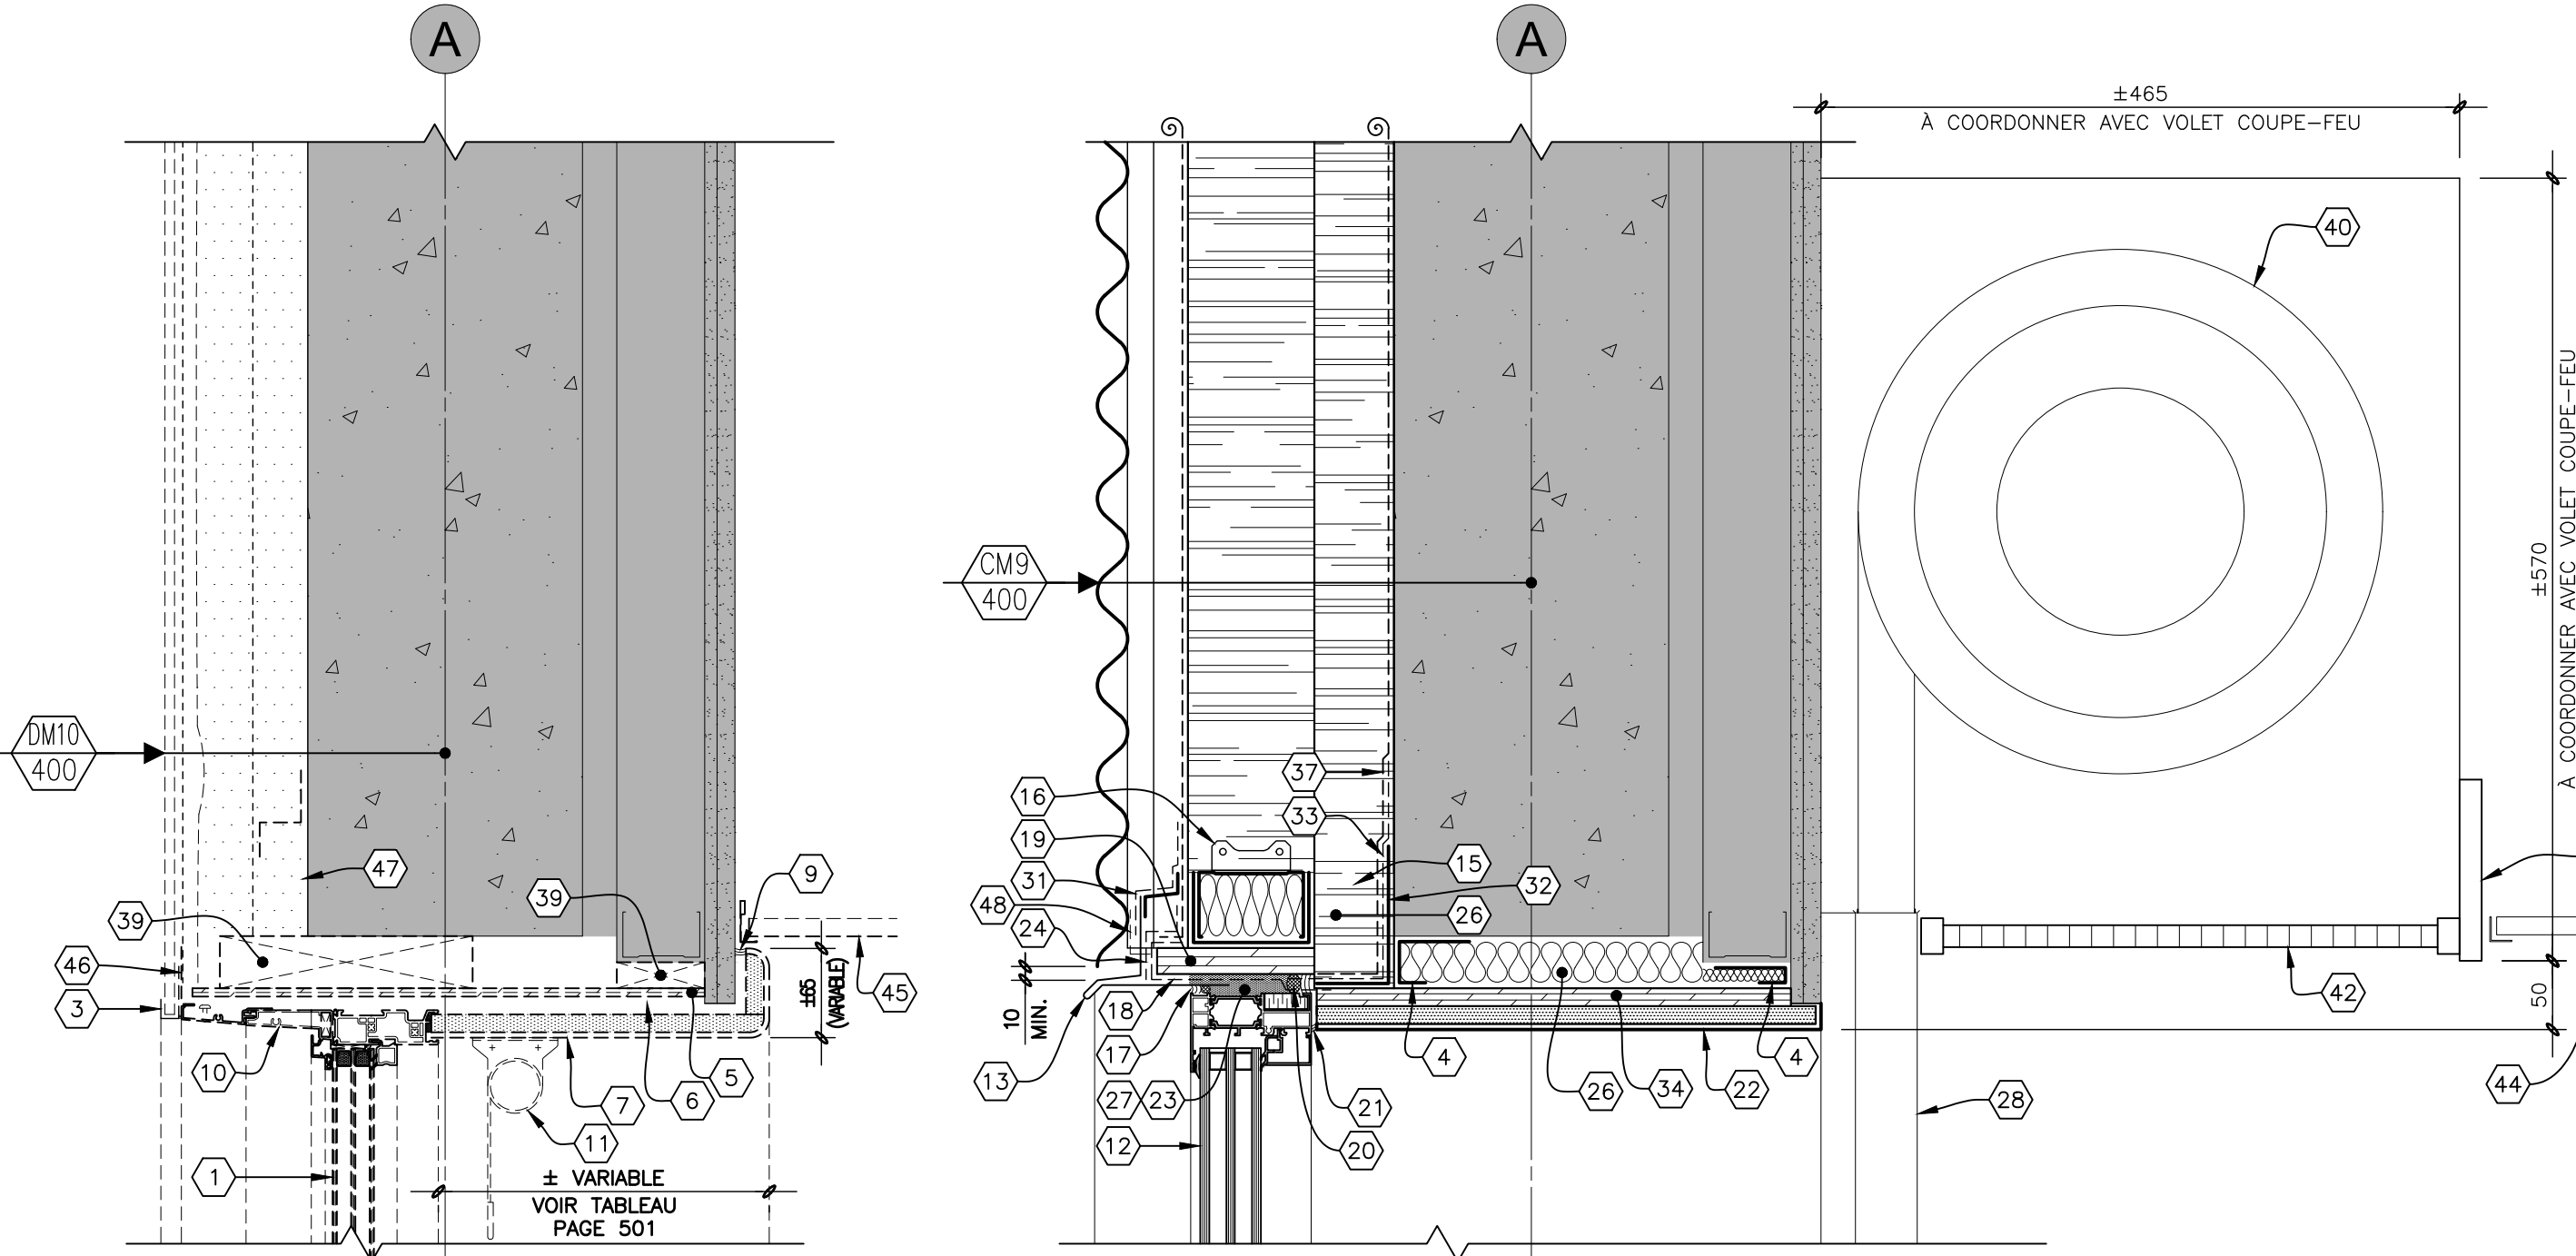

TÊTE

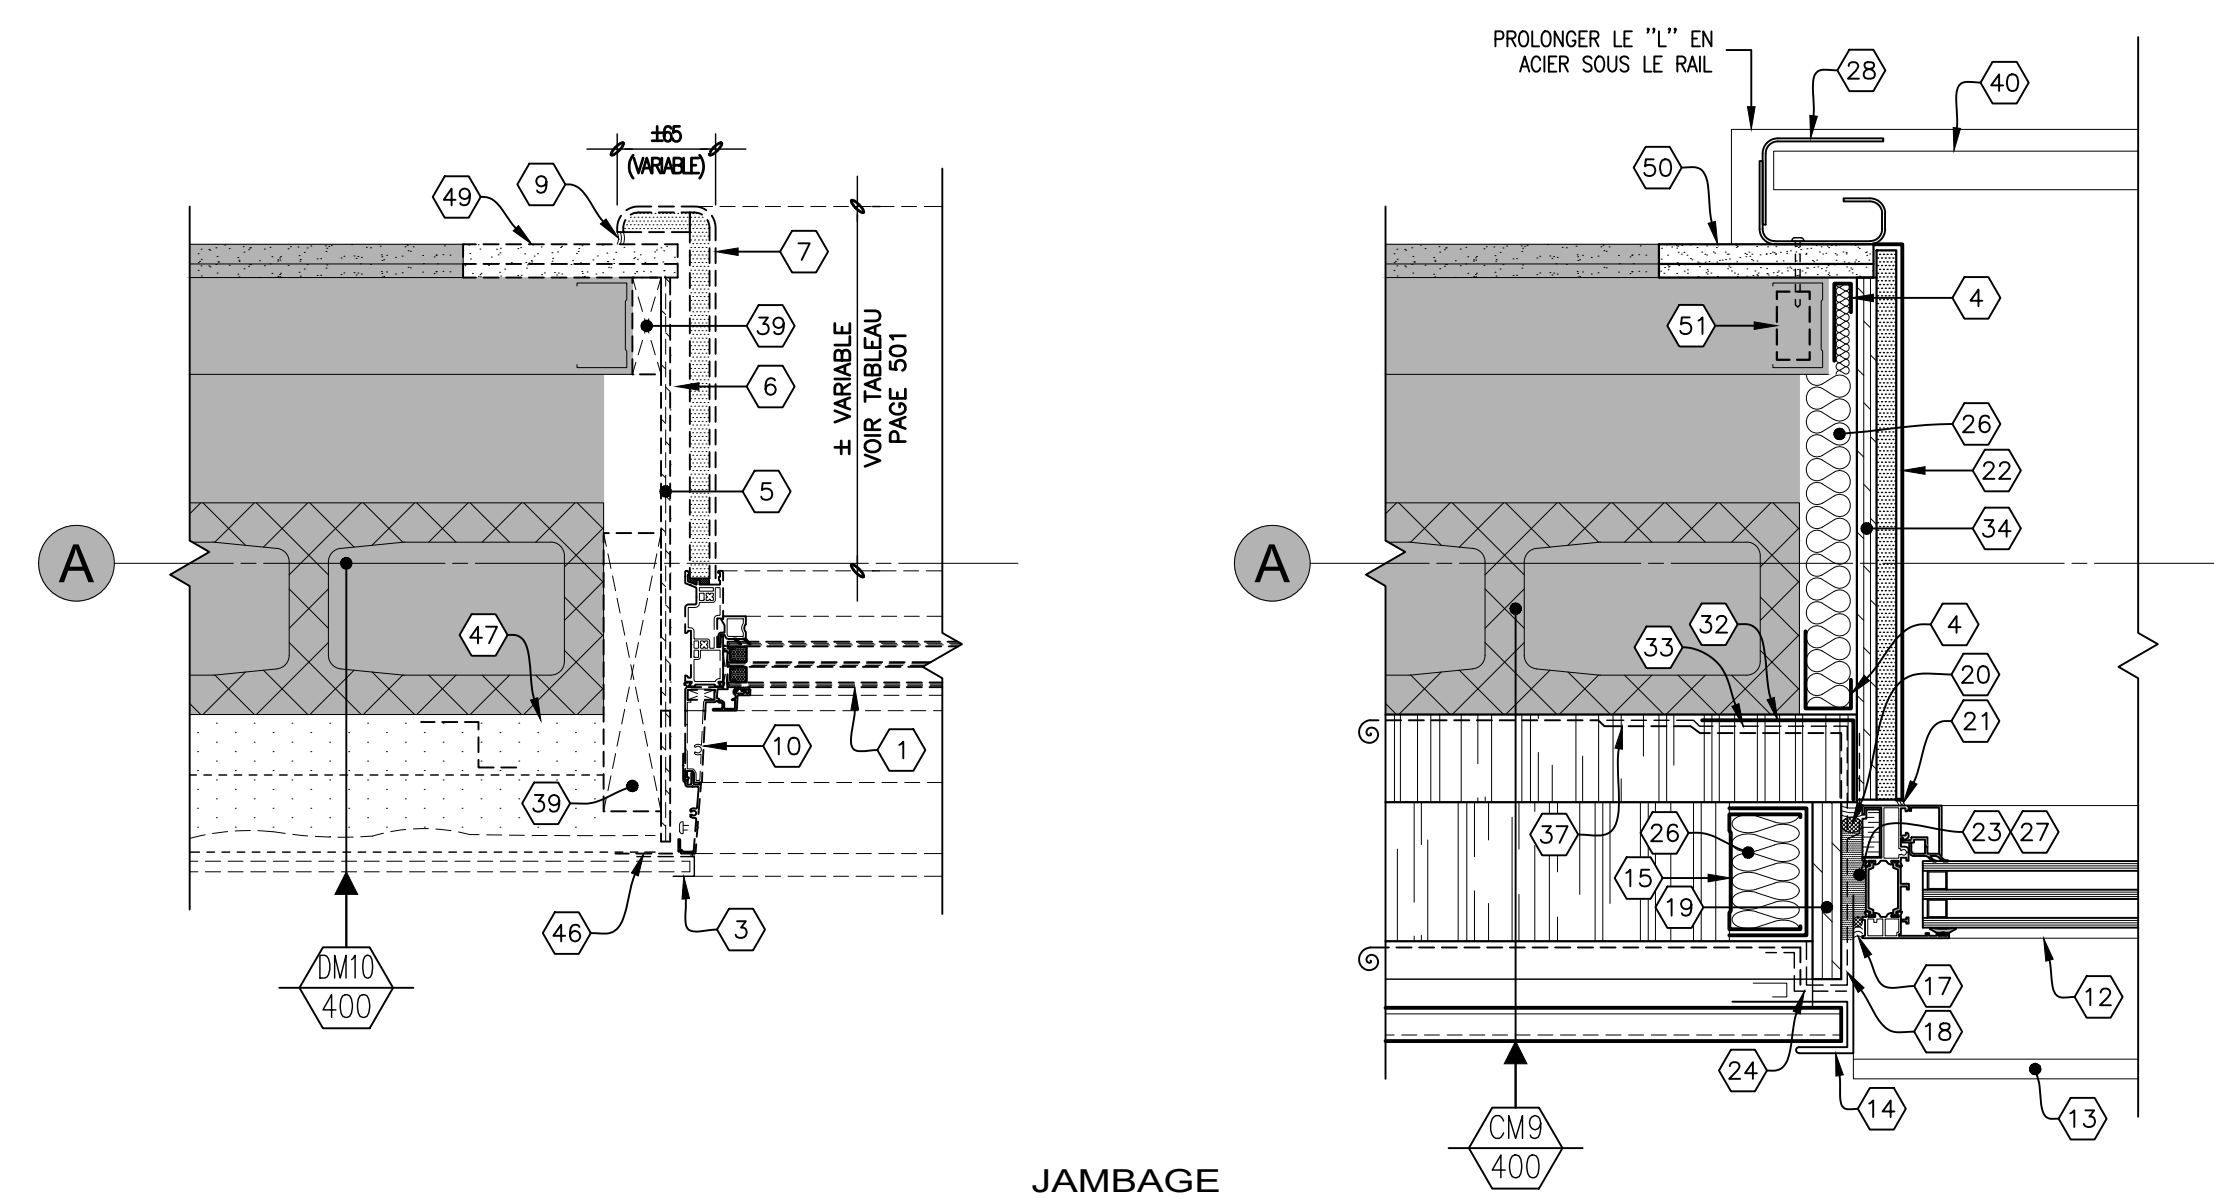

JAMBAGE

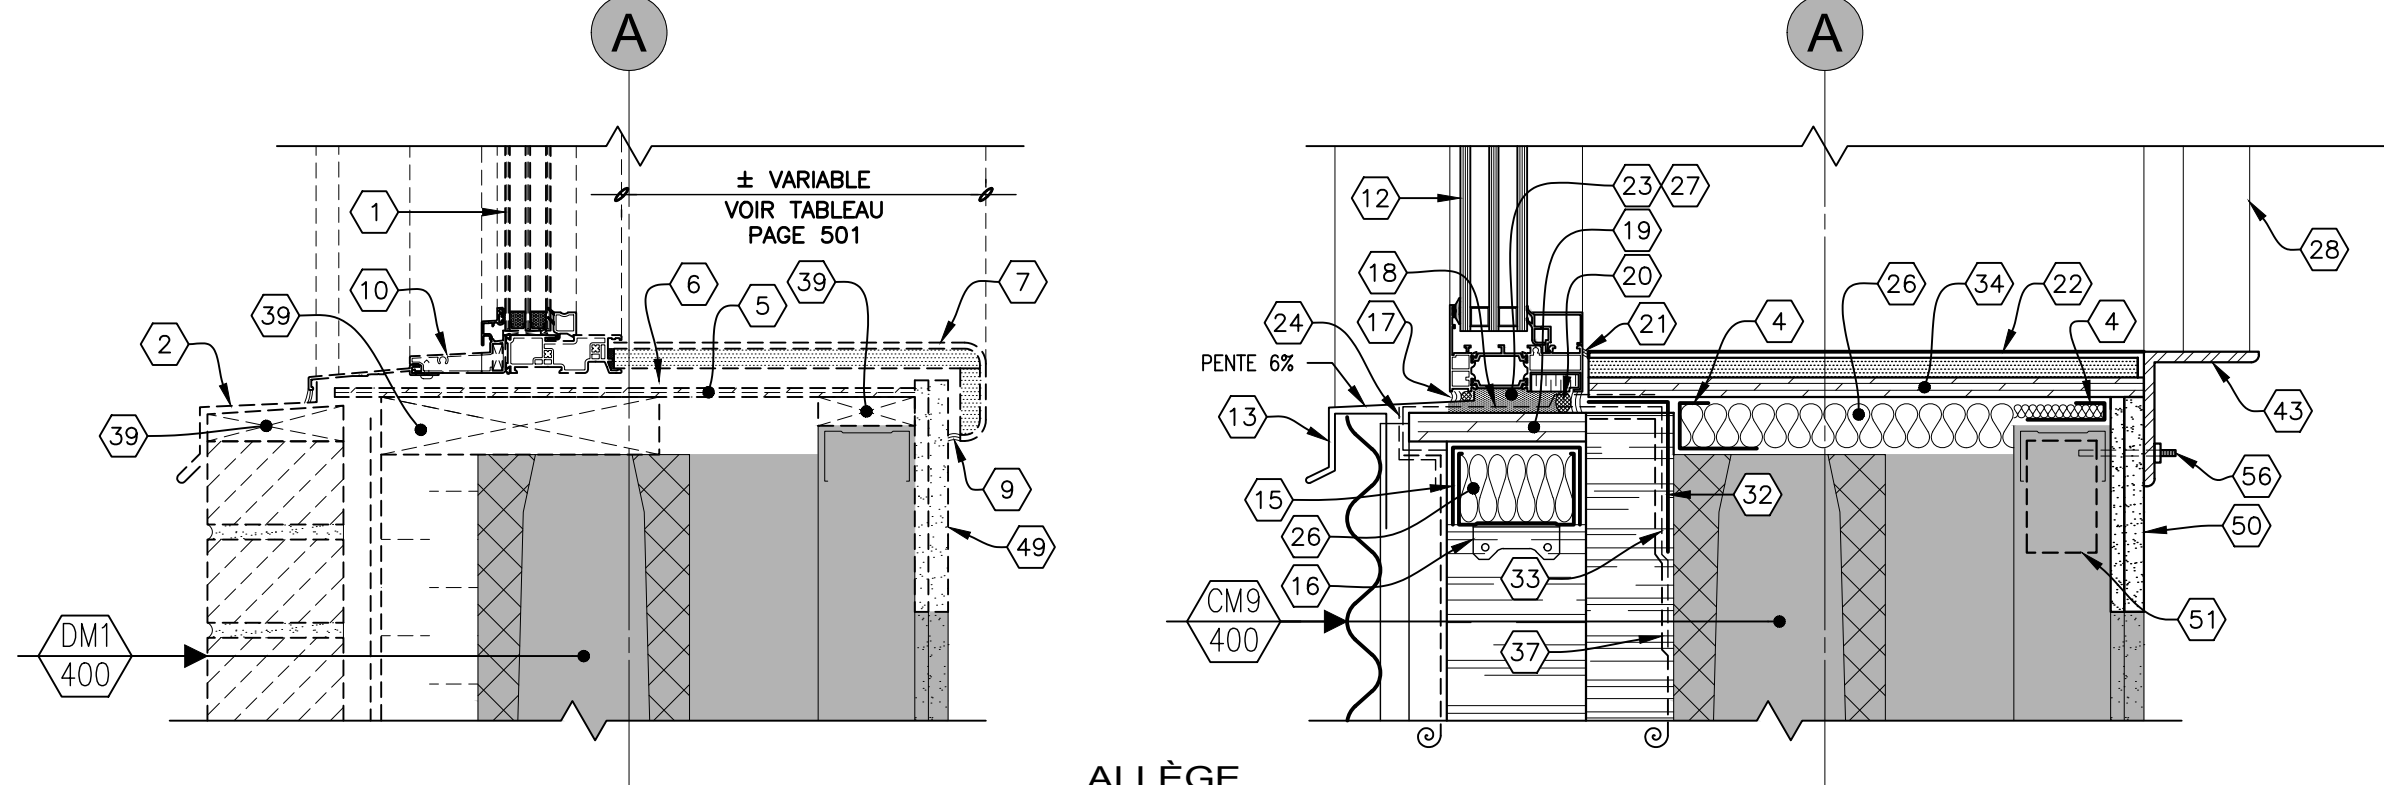

DÉMOLITION

ALLÈGE

CONSTRUCTION

19 DÉTAIL DE FENÊTRE TYPE (BASILAIRE)
502.503 511 1:5mm (URGENCE FAÇADE NORD - NIVEAU RDC)

LÉGENDE

- EXISTANT À CONSERVER.
- ÉLÉMENT À DÉMOLIR.
- X AXE EXISTANT
- EX EXTÉRIEUR DE LA STRUCTURE DE BÉTON EXISTANTE DE LA TOUR.
- NS NOUVEL AXE: FACE EXTÉRIEURE DES BARRES Z ET COLOMBAGES DE LA TOUR. VOIR STRUCTURE. (*) VOIR NOTE GÉNÉRAL PAGE 400.

NOTES (SUITE)

- BOULON D'ANCRAGE DE DIMENSIONS REQUISES À PEINDRE.
- MEMBRANE D'ÉTANCHÉITÉ AUTO-ADHÉSIVE.
- PANNEAU DE MÂT DE FIBRE DE VERRE 13mm D'ÉPAISSEUR.
- PLIAGE EN ALUMINIUM ANODISÉ CLAIR.
- ISOLANT SEMI-RIGIDE DE LAINE DE ROCHE ±70MM D'ÉPAISSEUR.
- ACCESSOIRE EXISTANT À CONSERVER.
- CABINET DE GAZ MÉDICAUX EXISTANT À CONSERVER.

NOTES

- FENÊTRE HYBRIDE (ALUMINIUM/PVC) EXISTANTE À DÉMOLIR.
- SOLIN EN ACIER ÉMAILLÉ EXISTANT À DÉMOLIR.
- MOULURE EN ALUMINIUM À DÉMOLIR.
- PLIAGE DE TOLE EN ACIER ÉMAILLÉ, CAL.18.
- CONTREPLAQUÉ EXISTANT À DÉMOLIR.
- MEMBRANE AUTOADHÉSIVE EXISTANTE À DÉMOLIR.
- FINITION INTÉRIEURE EN CONTREPLAQUÉ RECOUVRENT DE STRATIFIÉ À DÉMOLIR.
- TOLE PLIÉE EXISTANTE À DÉMOLIR.
- SCÉLLANT EXISTANT À ENLEVER. NETTOYER LES SURFACES EXISTANTES CONSERVÉES DE TOUTES TRACES DE SCÉLLANT.
- SECTION DU CADRE DE FENÊTRE À COUPER ET À DÉMOLIR. VOIR DÉTAILS EN ÉTAPES À LA PAGE 505.
- TOLE, STORE ET/OU HABILLAGE DE FENÊTRE À ENLEVER ET À REMETTRE AU PROPRIÉTAIRE. VOIR NOTE PAGE 505.
- NOUVELLE FENÊTRE EN ALUMINIUM.
- SOLIN EN ACIER ÉMAILLÉ, CAL.24.
- MOULURE EN "J" EN ACIER ÉMAILLÉ, CAL.24.
- ASSEMBLAGE DE COLOMBAGE ET DE LISSE SUR TOUT LE PÉRIMÈTRE DE L'OUVERTURE. VOIR STRUCTURE.
- CONNECTEUR. VOIR STRUCTURE.
- SCÉLLANT SUR FOND DE JOINT.
- MEMBRANE D'ÉTANCHÉITÉ AUTOADHÉSIVE SUR TOUT LE PÉRIMÈTRE DE L'OUVERTURE.
- CONTREPLAQUÉ À PLUS 19mm D'ÉPAISSEUR.
- BOUDIN D'ÉTAFOAM DE DIAMÈTRE APPROPRIÉ ET SCÉLLANT CONTINU SUR TOUT LE PÉRIMÈTRE DE LA FENÊTRE. POUR ASSURER LA CONTINUITÉ DE L'ÉTANCHÉITÉ ENTRE LA MEMBRANE ET LE CADRE DE LA FENÊTRE.
- SCÉLLANT DE FINITION.
- FINITION EN CONTREPLAQUÉ À PLUS 19mm D'ÉPAISSEUR RECOUVRENT DE PLASTIQUE STRATIFIÉ. COIN ARRONDI SUR TOUT LE PÉRIMÈTRE DE L'OUVERTURE. COULEUR AU CHOIX DE L'ARCHITECTE.
- POLYURÉTHANE GICLÉ NON EXPANSIF SUR LE PÉRIMÈTRE DE LA FENÊTRE.
- RUBAN AUTOCOLLANT. SCÉLLER LA MEMBRANE PARE-INTÉRIÈRES AVEC LA MEMBRANE AUTOADHÉSIVE.
- MEMBRANE AUTOADHÉSIVE PARE-VAPEUR SUR TOUT LE PÉRIMÈTRE DE L'OUVERTURE. SCÉLLER SUR LA NOUVELLE MEMBRANE SOUS LE CADRE DE FENÊTRE ET SUR LE POLYÉTHYLENE DU MUR EXISTANT.
- REMPUR L'ESPACE DE LAINE DE FIBRE DE ROCHE.
- CALE D'AJUSTEMENT EN POLYVINYLE RIGIDE D'ÉPAISSEUR REQUISE.
- RAIL DU VOLET COUPE-FEU À PEINTURER, COULEUR TEL QUE LE MUR.
- RIVET EN ACIER PRÉPINT, DE MÊME COULEUR QUE LE PAREMENT.
- PLIAGE DE TOLE EN ACIER GALVANISÉ CAL. 22.
- RUBAN AUTOCOLLANT.
- TOLE PLIÉE EN ACIER GALVANISÉ 75mm X 75mm, CAL. 16, AU POURTOUR DE L'OUVERTURE.
- MEMBRANE AUTOCOLLANTE PARE-VAPEUR.
- CONTREPLAQUÉ À PLUS D'ÉPAISSEUR REQUISE.
- CONTREPLAQUÉ À PLUS 19mm RECOUVRENT D'UNE MEMBRANE AUTOCOLLANTE ET D'UNE TOLE PLIÉE EN ACIER ÉMAILLÉ, CAL. 24, COULEUR AU CHOIX DE L'ARCHITECTE.
- BOUT DU PANNEAU REPLIÉ VERS L'INTÉRIEUR.
- MEMBRANE LIQUIDE PULVÉRISÉE PAR-DESSUS LA MEMBRANE AUTOADHÉSIVE.
- PLAFOND SUSPENDU (HAUTEUR VARIABLE), À CONSERVER.
- PIÈCE DE BOIS EXISTANTE À DÉMOLIR.
- VOLET COUPE-FEU. VOIR DEVIS.
- PANNEAU DE PARTICULES AGGLOMÉRÉES HAUTE DENSITÉ 16mm, FINI MÉLAMINE, COULEUR AU CHOIX DE L'ARCHITECTE.
- DIFFUSEUR D'ÉCLAIRAGE PERFORÉ AMOVIBLE, COULEUR CHROME.
- "L" EN ACIER 76X89MM X 4MM D'ÉPAISSEUR À PEINDRE, COULEUR TEL QUE LE MUR.
- PLAFOND SUSPENDU EXISTANT À RÉINSTALLER AVEC NOUVELLE SUSPENSION EN ALUMINIUM ET NOUVELLES TUILLES.
- PLAFOND SUSPENDU À DÉMANTÉLER SUR LA DIMENSION REQUISE. POUR L'INSTALLATION DU VOLET COUPE-FEU DANS L'ENTREPLAFOND.
- TOLE EXISTANTE RIVETÉE SUR LA BARRE EN "Z" ET AU CADRE DE LA FENÊTRE À DÉMOLIR.
- MEMBRANE AUTOCOLLANTE EXISTANTE À DÉMOLIR.
- MOUSTQUAIRE.
- OUVRIR LE MUR POUR L'INSTALLATION DU FOND DE CLOUAGE.
- PLAQUE DE PLÂTRE DE MÊME ÉPAISSEUR QUE CEUX EXISTANTS (2 RANGS), À PEINDRE.
- FOND DE CLOUAGE EN ACIER GALVANISÉ CAL.16, FIXÉ AU COLOMBAGE EXISTANT POUR LA FIXATION DU "L" EN ACIER.
- ACIER ÉMAILLÉ COLLÉ CAL.24, COULEUR BLANCHE.
- SCÉLLANT COUPE-FEU.
- PLAQUE DE PLÂTRE 16mm TYPE X.
- PLAQUE DE PLÂTRE 16mm TYPE X; -COLOMBAGE "CH" 64mm CAL.16; -PLAQUE DE PLÂTRE 25mm.

NE DOIT PAS SERVIR À L'EXÉCUTION

Le présent document est émis pour la seule fin identifiée. Son contenu est protégé par les droits d'auteur et toute reproduction ou modification, partielle ou totale, est interdite sans l'autorisation écrite de gagnon, letellier, cyr, ricard, mathieu, proulx, savard consortium d'architectes.




GLCRM | Proulx Savard |

GLCRM:
128, Avenue de la Cathédrale,
Bureau 201
Rimouski, QC, G5L 5H7
(418) 722-7655



2406, Ch. des Quatres-Bourgeois,
Bureau 100
Québec, QC, G1V 1W5
(418) 647-1700

Proulx Savard Architectes:
75, boul. Arthur-Buies Ouest,
Rimouski QC G5L 5C2
(418) 723-5543

ARCHITECTURE

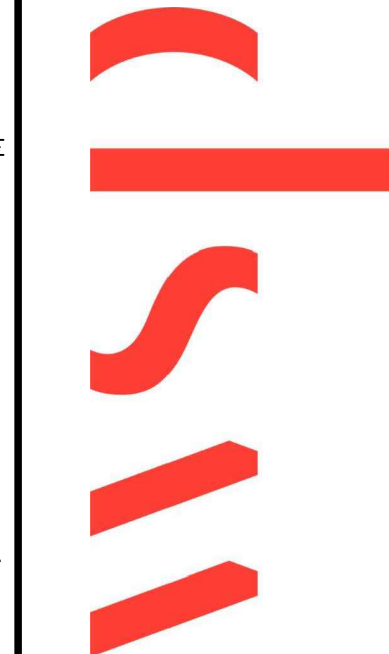

CONSULTANTS

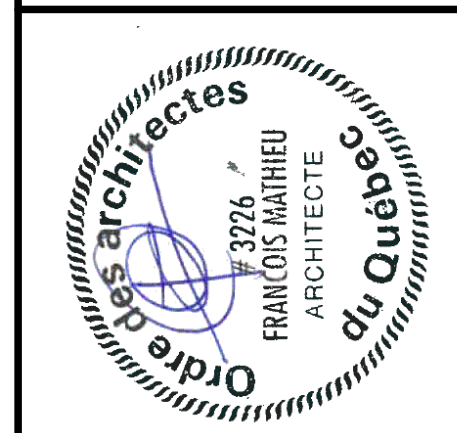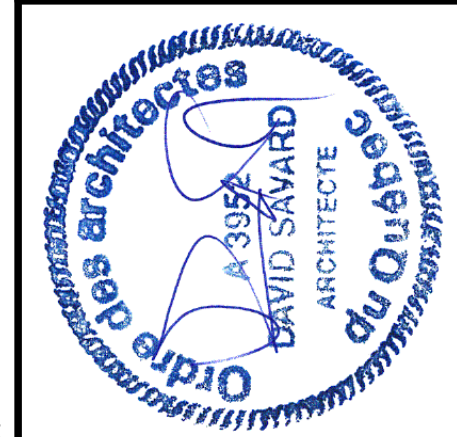

DESSINATEUR(S)		DOSSIER No.
A.L. D.B.		24-107 / 687-24
ÉCHELLE		DATE
INDIQUÉE		SEPTEMBRE 2024
05	2024-09-04	DÉFINITIVES POUR SOUMISSION
04	2024-08-21	DÉFINITIVES 100% POUR APPROBATION
03	2024-08-03	DÉFINITIVES 80% POUR APPROBATION
02	2024-05-14	DÉFINITIVES 40% POUR APPROBATION
01	2024-02-27	PRÉLIMINAIRES 20% POUR APPROBATION
No	DATE	REVISIONS

DÉTAIL TYPE DE FENÊTRE (BASILAIRE)
DÉMOLITION ET CONSTRUCTION

PROJET
HÔPITAL DE CHANDLER,
Chandler
(Redaction de l'enveloppe)

PROPRIÉTAIRE
Santé Québec

511