
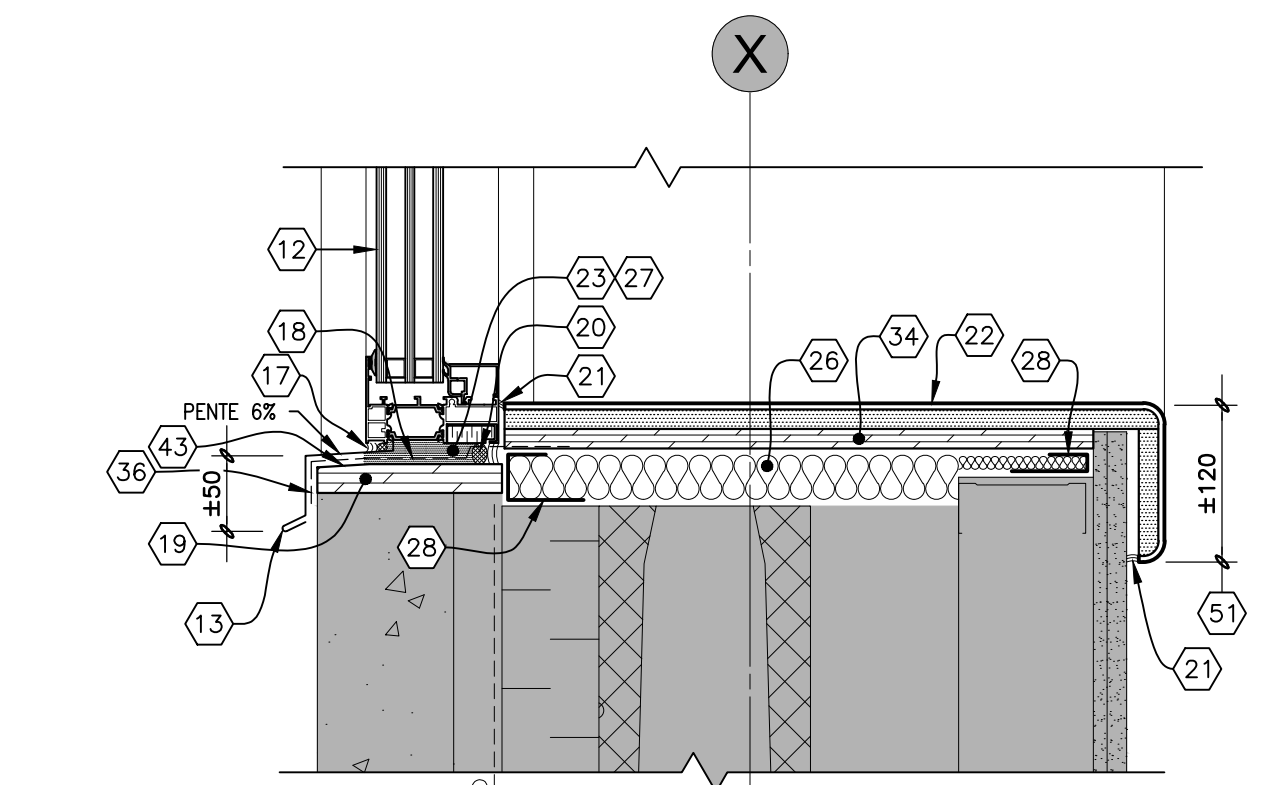


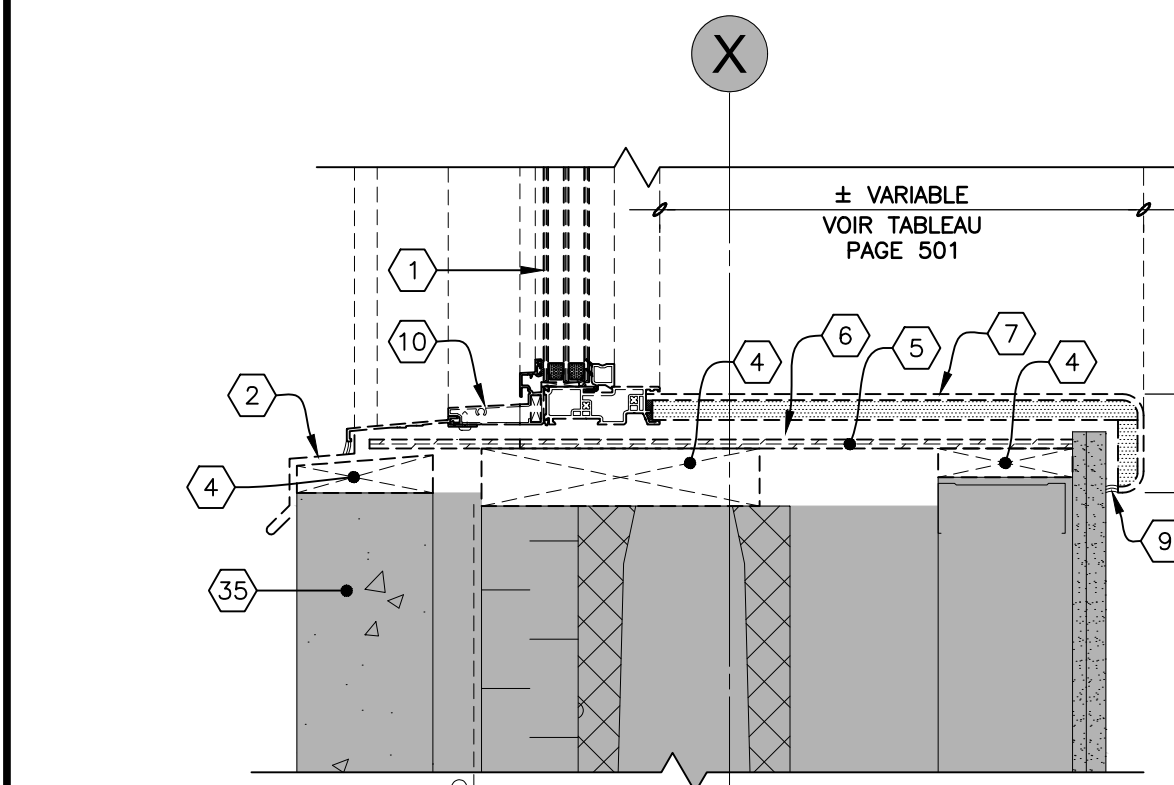

TÊTE

JAMBAGE


ALLÈGE

DÉMOLITION

21	
502,503	512

DÉTAIL DE FENÊTRE TYPE (BASILAIRE)

(ENTRÉE AMBULANCE – NIVEAU RDC)

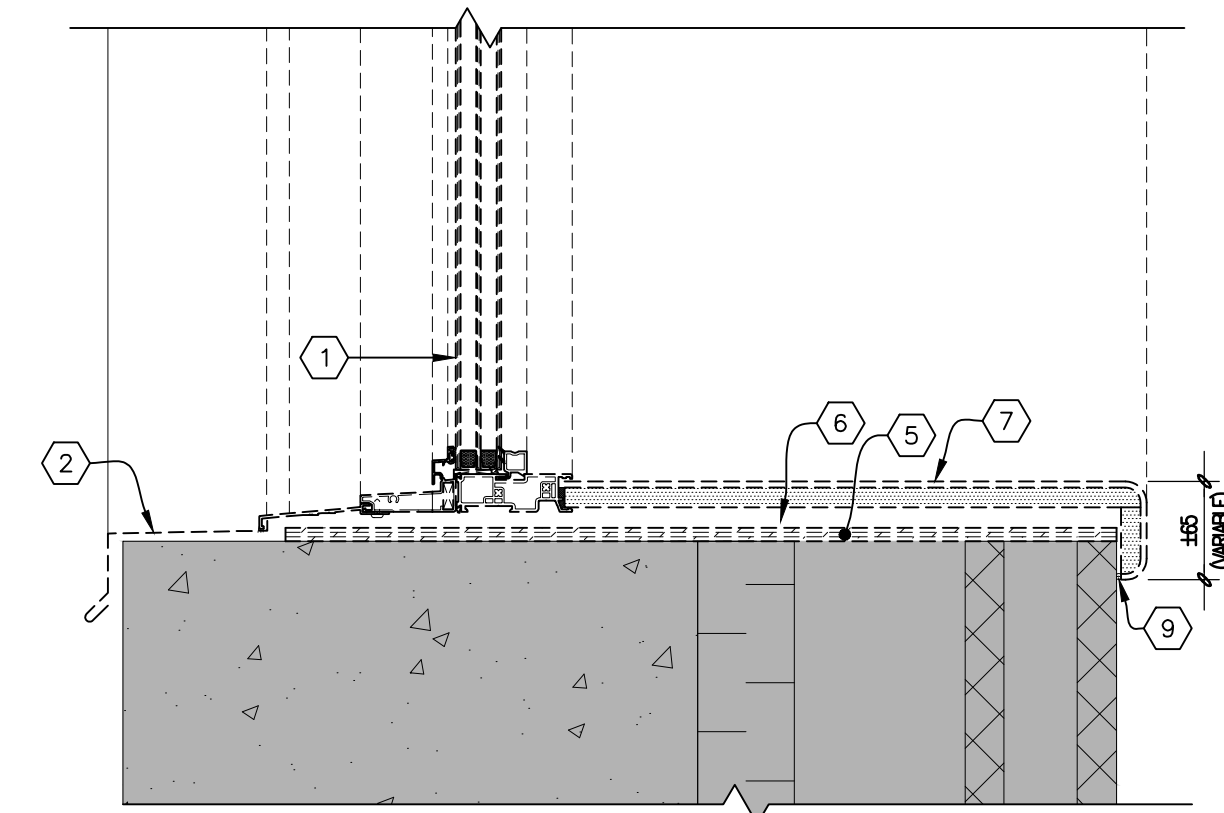


TÊTE

JAMBAGE

ALLÈGE

DÉMOLITION

100,204,502,503

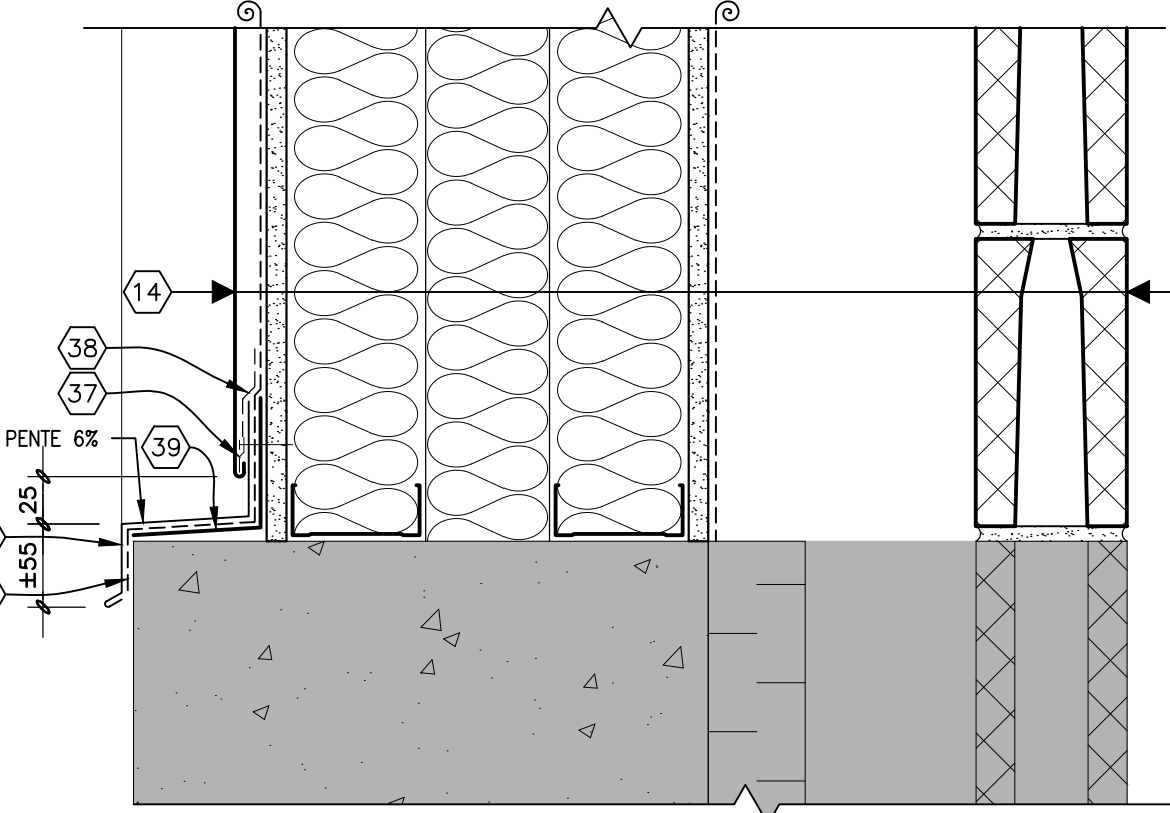

CONSTRUCTION

22 DÉ

(SOUS-SOL FAÇADE NORD)

(SOUS-SOL FAÇADE NORD)

NOTES (SUITE)

- (44) PLIAGE EN ALUMINIUM ANODISÉ CLAIR.
- (45) À RÉALISER DE MÊME DIMENSIONS SUR TROIS (3) CÔTÉS DE LA FENÊTRE.
- (46) MEMBRANE D'ÉTANCHÉITÉ AUTO-ADHÉSIVE.
- (47) PLAQUE DE PLÂTRE (2 RANGS) D'ÉPAISSEUR TEL QUE CELUI EXISTANT
- (48) PANNEAU DE MÂT DE FIBRE DE VERRE 13mm D'ÉPAISSEUR.
- (49) ISOLANT SEMI-RIGIDE DE LAINE DE ROCHE ±70mm D'ÉPAISSEUR.
- (50) COLOMBAGE D'ACIER 33X92mm.

NOTES


- (1) FENÊTRE HYBRIDE (ALUMINIUM/PVC) EXISTANTE À DÉMOUR.
- (2) SOLIN EN ACIER ÉMAILLÉ EXISTANT À DÉMOUR.
- (3) MOULURE EN ALUMINIUM À DÉMOUR.
- (4) PIÈCE DE BOIS EXISTANTE À DÉMOUR.
- (5) CONTREPLAQUE EXISTANT À DÉMOUR.
- (6) MEMBRANE AUTOADHÉSIVE EXISTANTE À DÉMOUR.
- (7) FINITION INTÉRIEURE EN CONTREPLAQUE RECOUVERT DE STRATIFIÉ À DÉMOUR.
- (8) TÔLE PLUÉE EXISTANTE À DÉMOUR.
- (9) SCELLANT EXISTANT À ENLEVER, NETTOYER LES SURFACES EXISTANTES CONSERVÉES DE TOUTES TRACES DE SCELLANT.
- (10) SECTION DU CADRE DE FENÊTRE À COUPER ET À DÉMOUR. VOIR DÉTAILS EN ÉTAPES À LA PAGE 505.
- (11) TÔLE, STORE ET/OU HABILLAGE DE FENÊTRE À ENLEVER ET À REMETTRE AU PROPRIÉTAIRE. VOIR NOTE PAGE 505.
- (12) NOUVELLE FENÊTRE EN ALUMINIUM.
- (13) SOLIN EN ACIER ÉMAILLÉ, CAL.24.
- (14)
 - TÔLE EN ACIER ÉMAILLÉ COLLÉE, CAL.24. COULEUR AU CHOIX DE L'ARCHITECTE;
 - MEMBRANE PARÉ-AIR/INTÉMPIÈRES (TYPE 4) PERMEABLE À LA VAPEUR D'EAU AUTO-ADHÉSIVE, JOINTS CEAUCHES;
 - PANNEAU DE MÂT DE FIBRE DE VERRE 13mm;
 - COLOMBAGE D'ACIER 92mm, VOIR STRUCTURE;
 - ISOLANT DE FIBRE DE ROCHE 89mm D'ÉPAISSEUR;
 - REMPLIR L'ESPACE D'ISOLANT DE FIBRE DE ROCHE;
 - COLOMBAGE D'ACIER 92mm VOIR STRUCTURE;
 - ISOLANT DE FIBRE DE ROCHE 89mm D'ÉPAISSEUR;
 - PANNEAU DE MÂT DE FIBRE DE VERRE 13mm;
 - NOUVEAU BLOC DE MAÇONNERIE DE DIMENSION REQUISE, À FINIR.
- (15) ASSEMBLAGE DE COLOMBAGE ET DE L'USSE SUR TOUT LE PÉRIMÈTRE DE L'OUVERTURE, VOIR STRUCTURE.
- (16) CONNECTEUR, VOIR STRUCTURE.
- (17) SCELLANT SUR FOND DE JOINT.
- (18) MEMBRANE D'ÉTANCHÉITÉ AUTOADHÉSIVE SUR TOUT LE PÉRIMÈTRE DE L'OUVERTURE.
- (19) CONTREPLAQUE À PLUS 19mm D'ÉPAISSEUR.
- (20) BOUDIN D'ÉTAFOAM DE DIAMÈTRE APPROPRIÉ ET SCELLANT CONTINU SUR TOUT LE PÉRIMÈTRE DE LA FENÊTRE POUR ASSURER LA CONTINUÏTÉ DE L'ÉTANCHÉITÉ ENTRE LA MEMBRANE ET LE CADRE DE LA FENÊTRE.
- (21) SCELLANT DE FINITION.
- (22) FINITION EN CONTREPLAQUE À PLUS 19mm D'ÉPAISSEUR RECOUVERT DE PLASTIQUE STRATIFIÉ, COIN ARRondi SUR TOUT LE PÉRIMÈTRE DE L'OUVERTURE. COULEUR AU CHOIX DE L'ARCHITECTE.
- (23) POLYURÉTHANE GICLÉ NON EXPANSIF SUR LE PÉRIMÈTRE DE LA FENÊTRE.
- (24) RUBAN AUTOCOLLANT. SCELLER LA MEMBRANE PARÉ-INTÉMPIÈRES AVEC LA MEMBRANE AUTOADHÉSIVE.
- (25) CORNIÈRE EXISTANTE À CONSERVER.
- (26) REMPLIR L'ESPACE DE LAINE DE FIBRE DE ROCHE.
- (27) CALE D'AJUSTEMENT EN POLYNYLÈ REIGIDE D'ÉPAISSEUR REQUISE.
- (28) PLAGE DE TÔLE EN ACIER GALVANISÉ, CAL.18.
- (29) PLAFOND SUSPENDU (HAUTEUR VARIABLE), À CONSERVER.
- (30) MEMBRANE LIQUIDE PULVÉRISÉE PAR-DESSUS LA MEMBRANE AUTOADHÉSIVE.
- (31) CONTREPLAQUE À PLUS 19mm RECOUVERT D'UNE MEMBRANE AUTOCOLLANTE ET D'UNE TÔLE PLUÉE EN ACIER ÉMAILLÉ, CAL. 24, COULEUR AU CHOIX DE L'ARCHITECTE.
- (32) TÔLE PLUÉE EN ACIER GALVANISÉ 1575mm X 75mm, CAL. 16, AU POURTOUR DE L'OUVERTURE.
- (33) MEMBRANE AUTOCOLLANTE PARÉ-VAPEUR.
- (34) CONTREPLAQUE À PLUS 19mm D'ÉPAISSEUR REQUISE.
- (35) BÉTON EXISTANT À CONSERVER.
- (36) RETOURNER LA MEMBRANE SUR LA FACE DU MUR DE FONDATION.
- (37) AGRAFE, CAL.24.
- (38) RUBAN AUTOCOLLANT.
- (39) PLAGE DE TÔLE CAL.18, EN PENTE 6%.
- (40) TÔLE EXISTANTE RIVETÉE SUR LA BARRE EN "Z" ET AU CADRE DE LA FENÊTRE À DÉMOUR.
- (41) MEMBRANE AUTOCOLLANTE EXISTANTE À DÉMOUR.
- (42) BARRE EN "Z" AJUSTABLE EXISTANTE À DÉMOUR.
- (43) CONTREPLAQUE BISEAUTÉ.

-LÉGENDE



-  EXISTANT À CONSERVER.
- ÉLÉMENT À DÉMOLIR.
-  AXE EXISTANT
-  EXTÉRIEUR DE LA STRUCTURE DE BÉTON EXISTANTE DE LA TOUR.
-  NOUVEAU AXE: FACE EXTÉRIEURE DES BARRES Z ET COLOMBAGES DE LA 1^{re} VOIR STRUCTURE.
- (*) VOIR NOTE GÉNÉRAL PAGE 400.

NE DOIT PAS SERVIR À L'EXÉCUTION


Le présent document est émis pour la seule fin identifiée. Son contenu est protégé par les droits d'auteur et toute reproduction ou modification, partielle ou totale, est interdite sans l'autorisation écrite de gagnon, letellier, cyr, ricard, mathieu, proulx, savard consortium d'architectes.

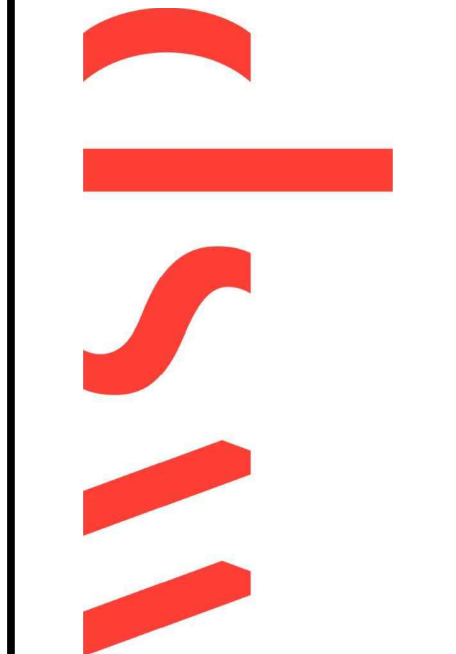


CONSULTANTS

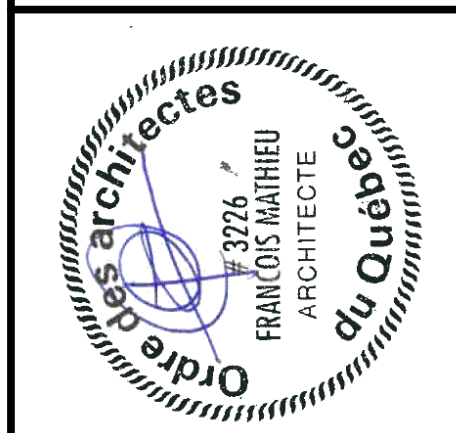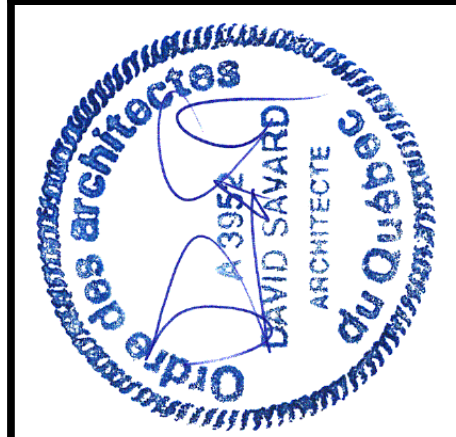


PROJET	HÔPITAL DE CHANDLER, Chandler (Rédaction de l'enveloppe)		PROPRIÉTAIRE	 Santé Québec
DESSIN	DÉTAIL TYPE DE FENÊTRE (BASILAIRE)		DEMOLITION ET CONSTRUCTION	
PERSONNEL(S)	DOSSIER No. 24-108 / 1687-24		DATE SEPTEMBRE 2024	
	A.L. D.B. ECELLE INDIVIDUE			
PROJET	05	2024-09-04	DÉFINITIFS POUR SOUMISSION	
	04	2024-08-21	DÉFINITIFS 100% POUR APPROBATION	
	03	2024-08-03	DÉFINITIFS 80% POUR APPROBATION	
	02	2024-05-14	DÉFINITIFS 60% POUR APPROBATION	
	01	2024-02-27	PRÉLIMINAIRES 30% POUR APPROBATION	
	No	DATE	REVISIONS	

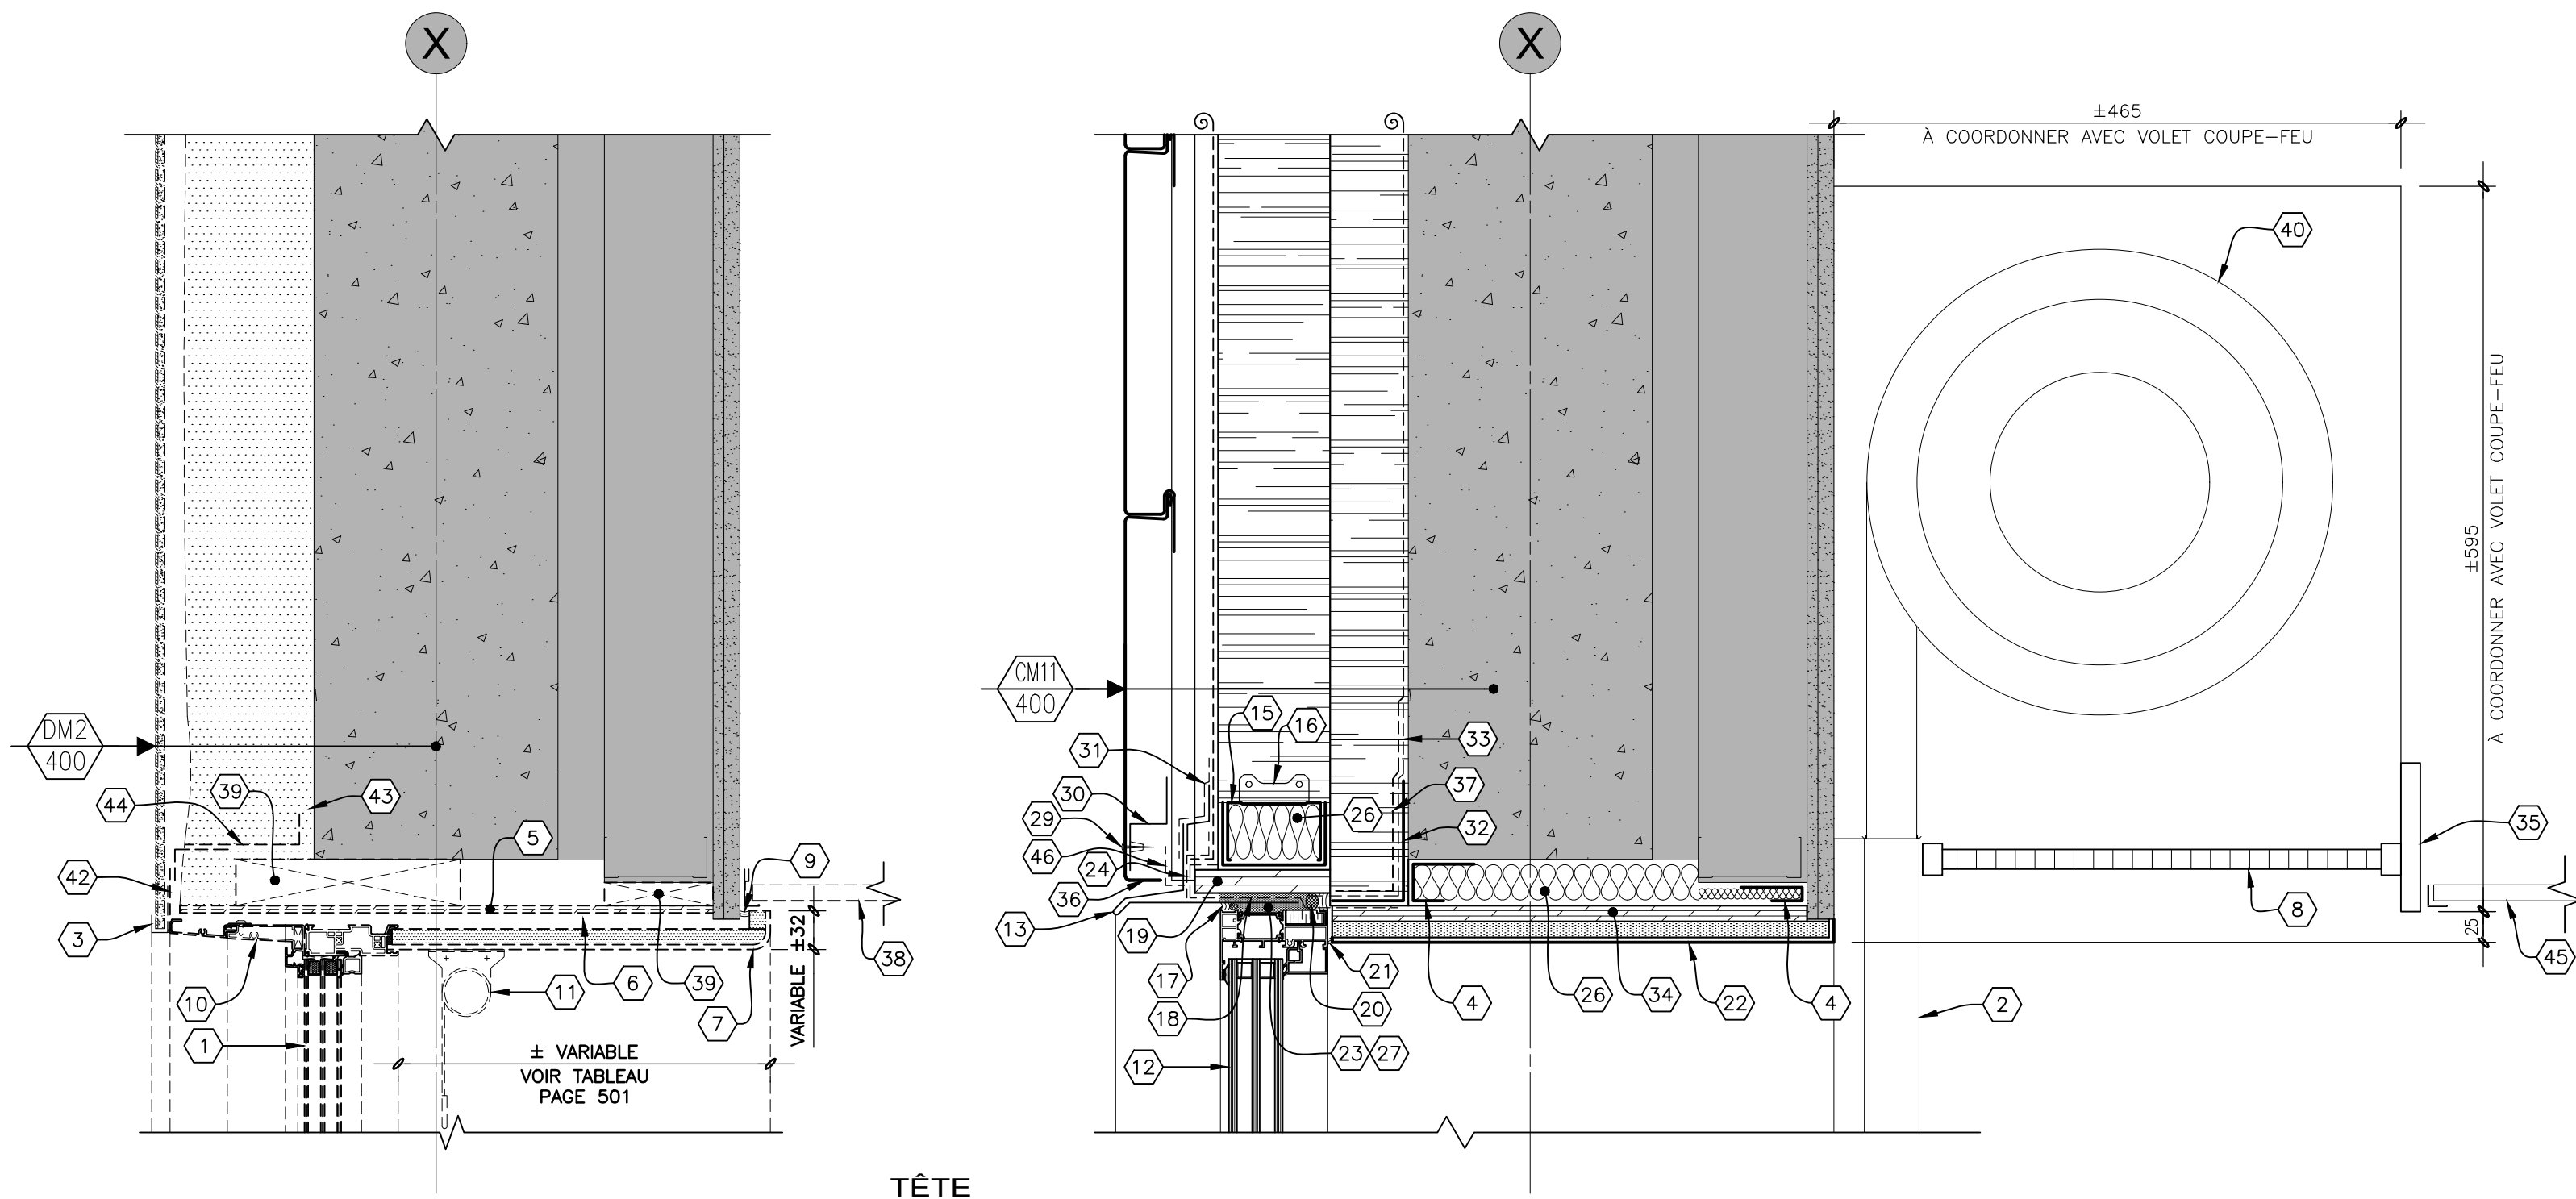

TÊTE

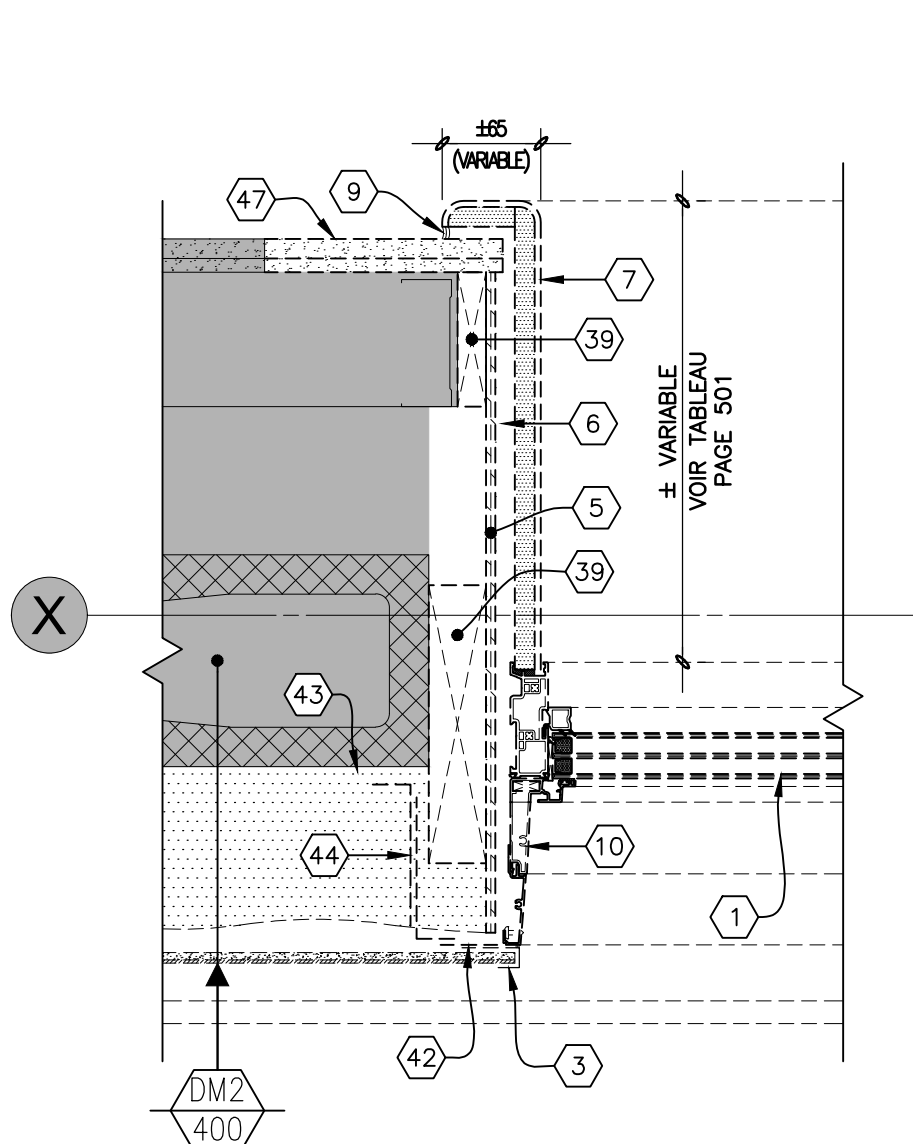

JAMBAGE

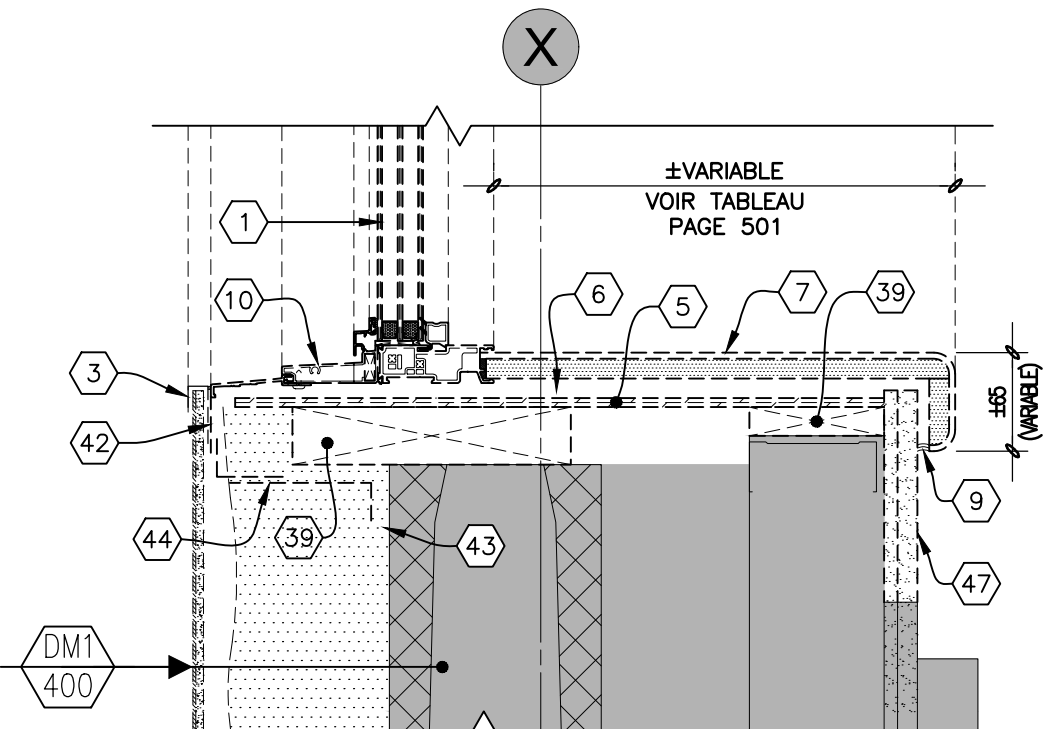


DÉMOLITION

ALLÈGE

CONSTRUCTION


23 DÉTAIL DE FENÊTRE TYPE (BASILAIRE)
502,503 513 1:5mm
(NIVEAU RDC – ADMINISTRATION FAÇADE NORD)

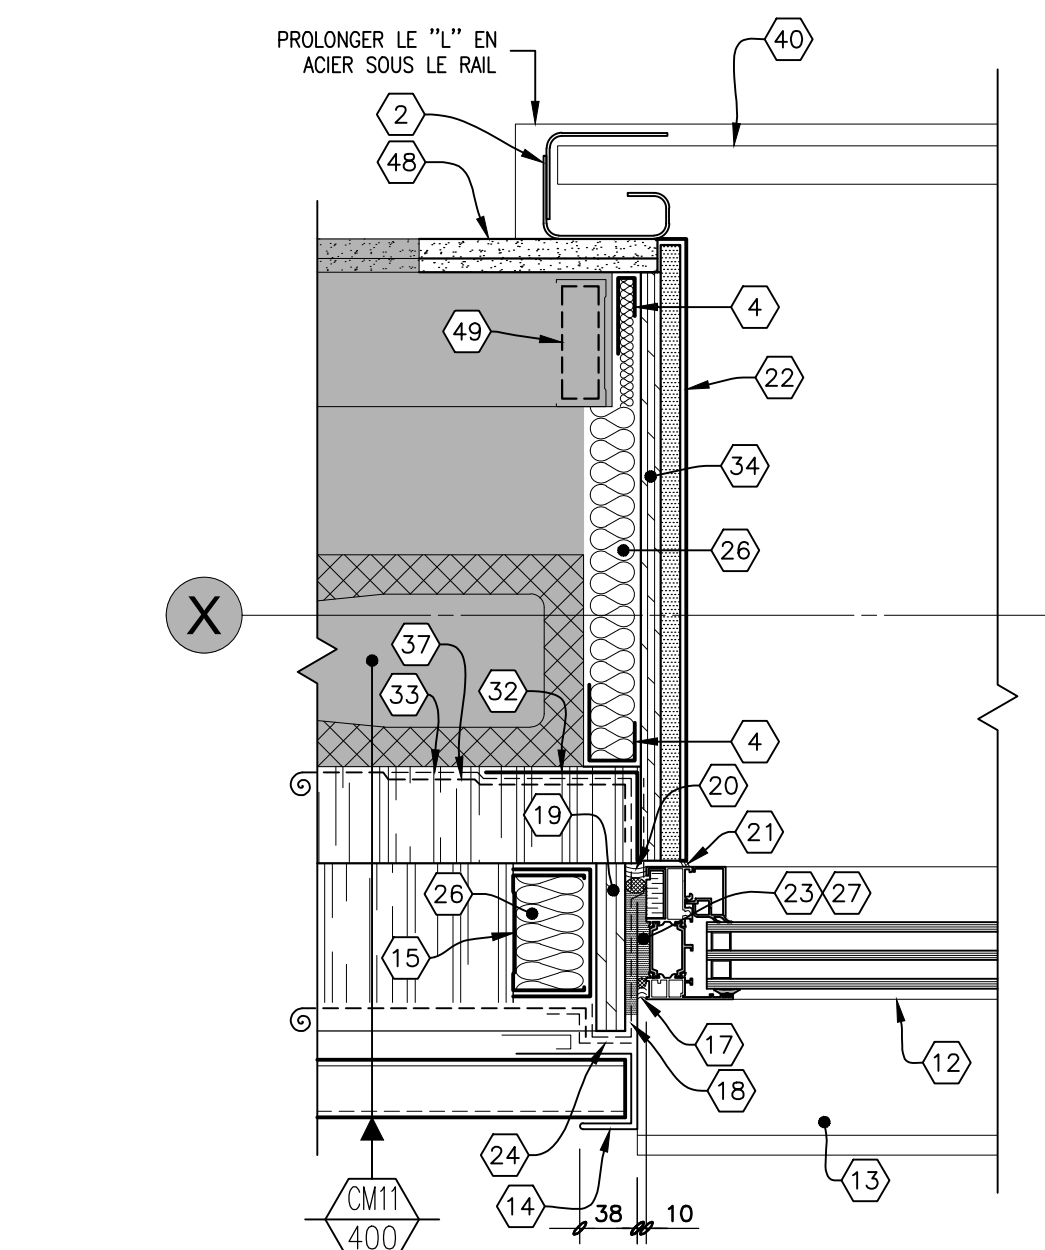

ALLÈGE

CONSTRUCTION

24 DÉTAIL DE FENÊTRE TYPE (BASILAIRE)
502,503 513 1:5mm
(NIVEAU RDC – ADMINISTRATION FAÇADE NORD)

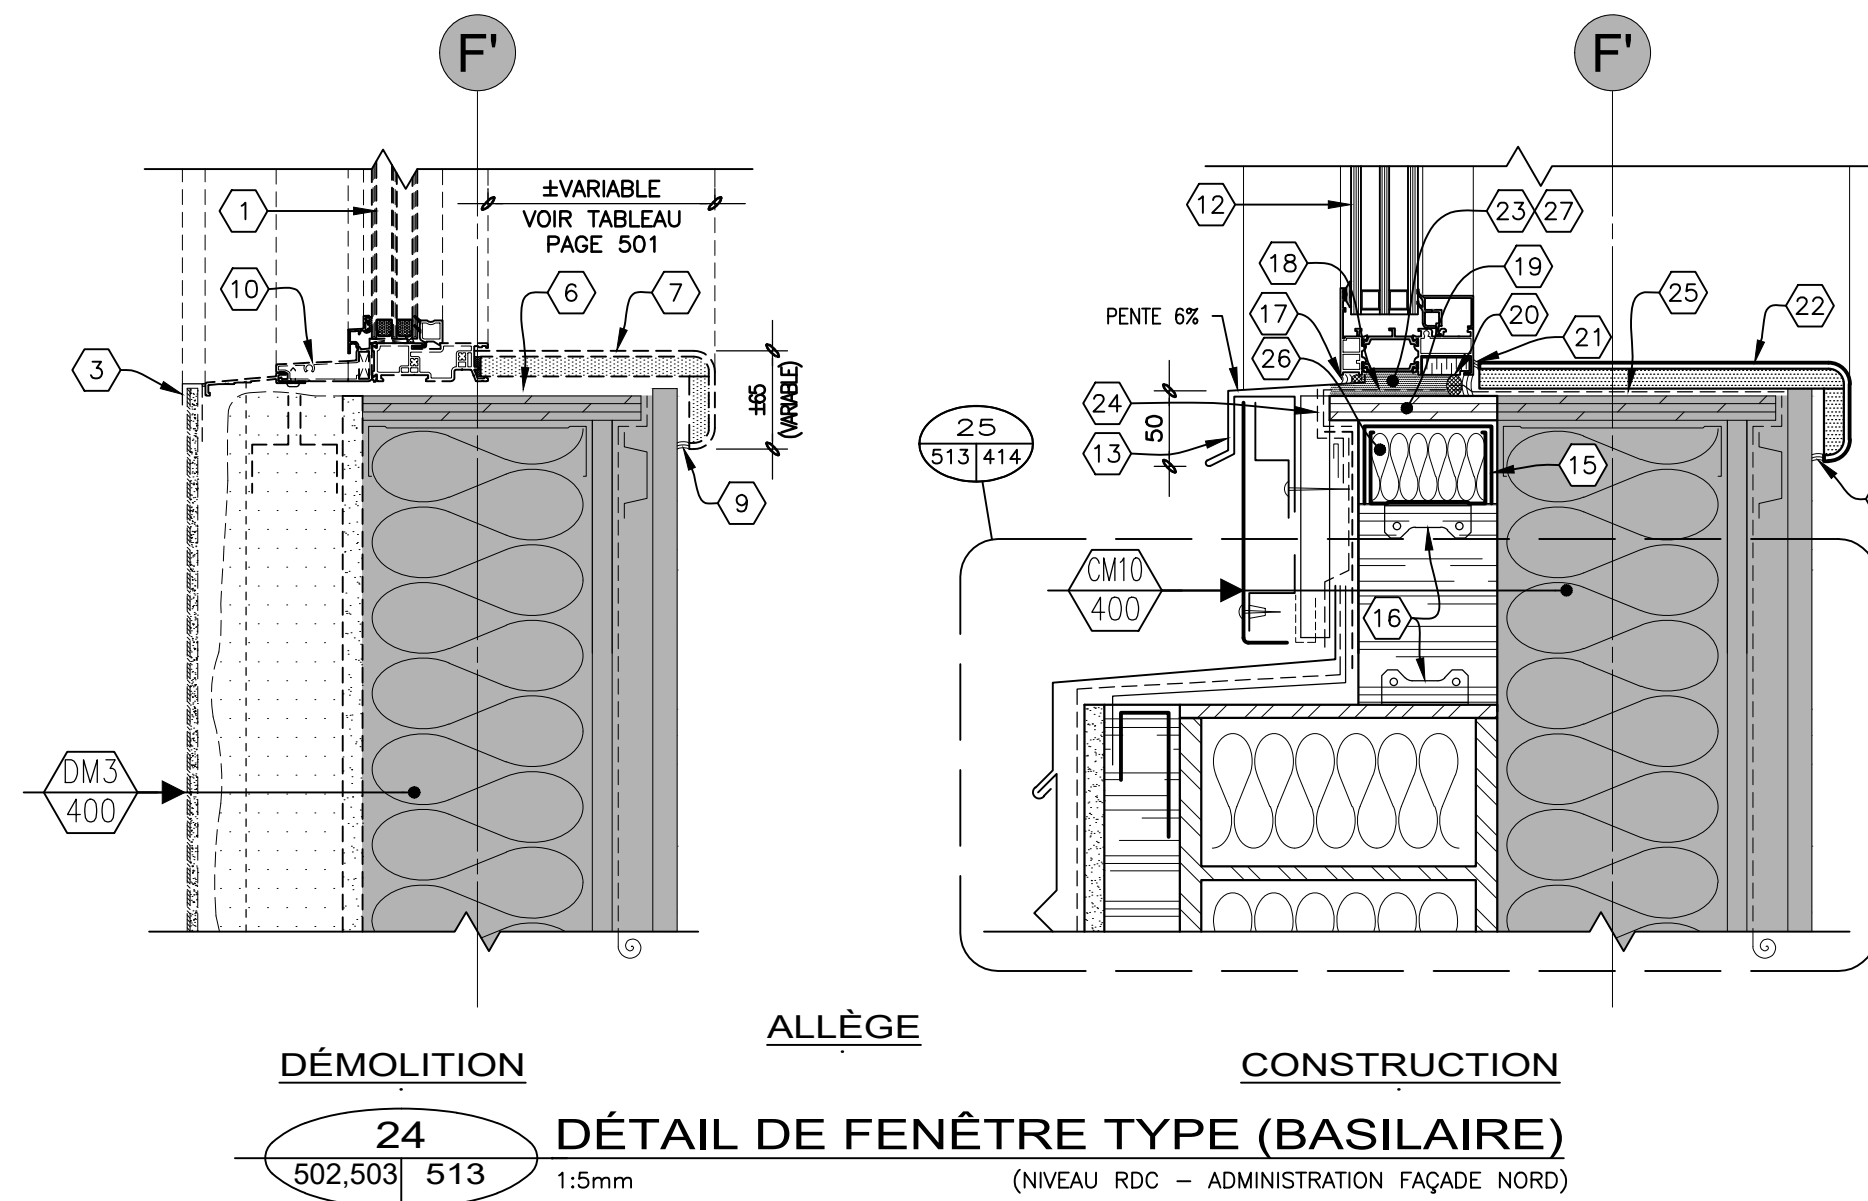


DÉMOLITION

ALLÈGE

CONSTRUCTION

24 DÉTAIL DE FENÊTRE TYPE (BASILAIRE)
502,503 513 1:5mm
(NIVEAU RDC – ADMINISTRATION FAÇADE NORD)

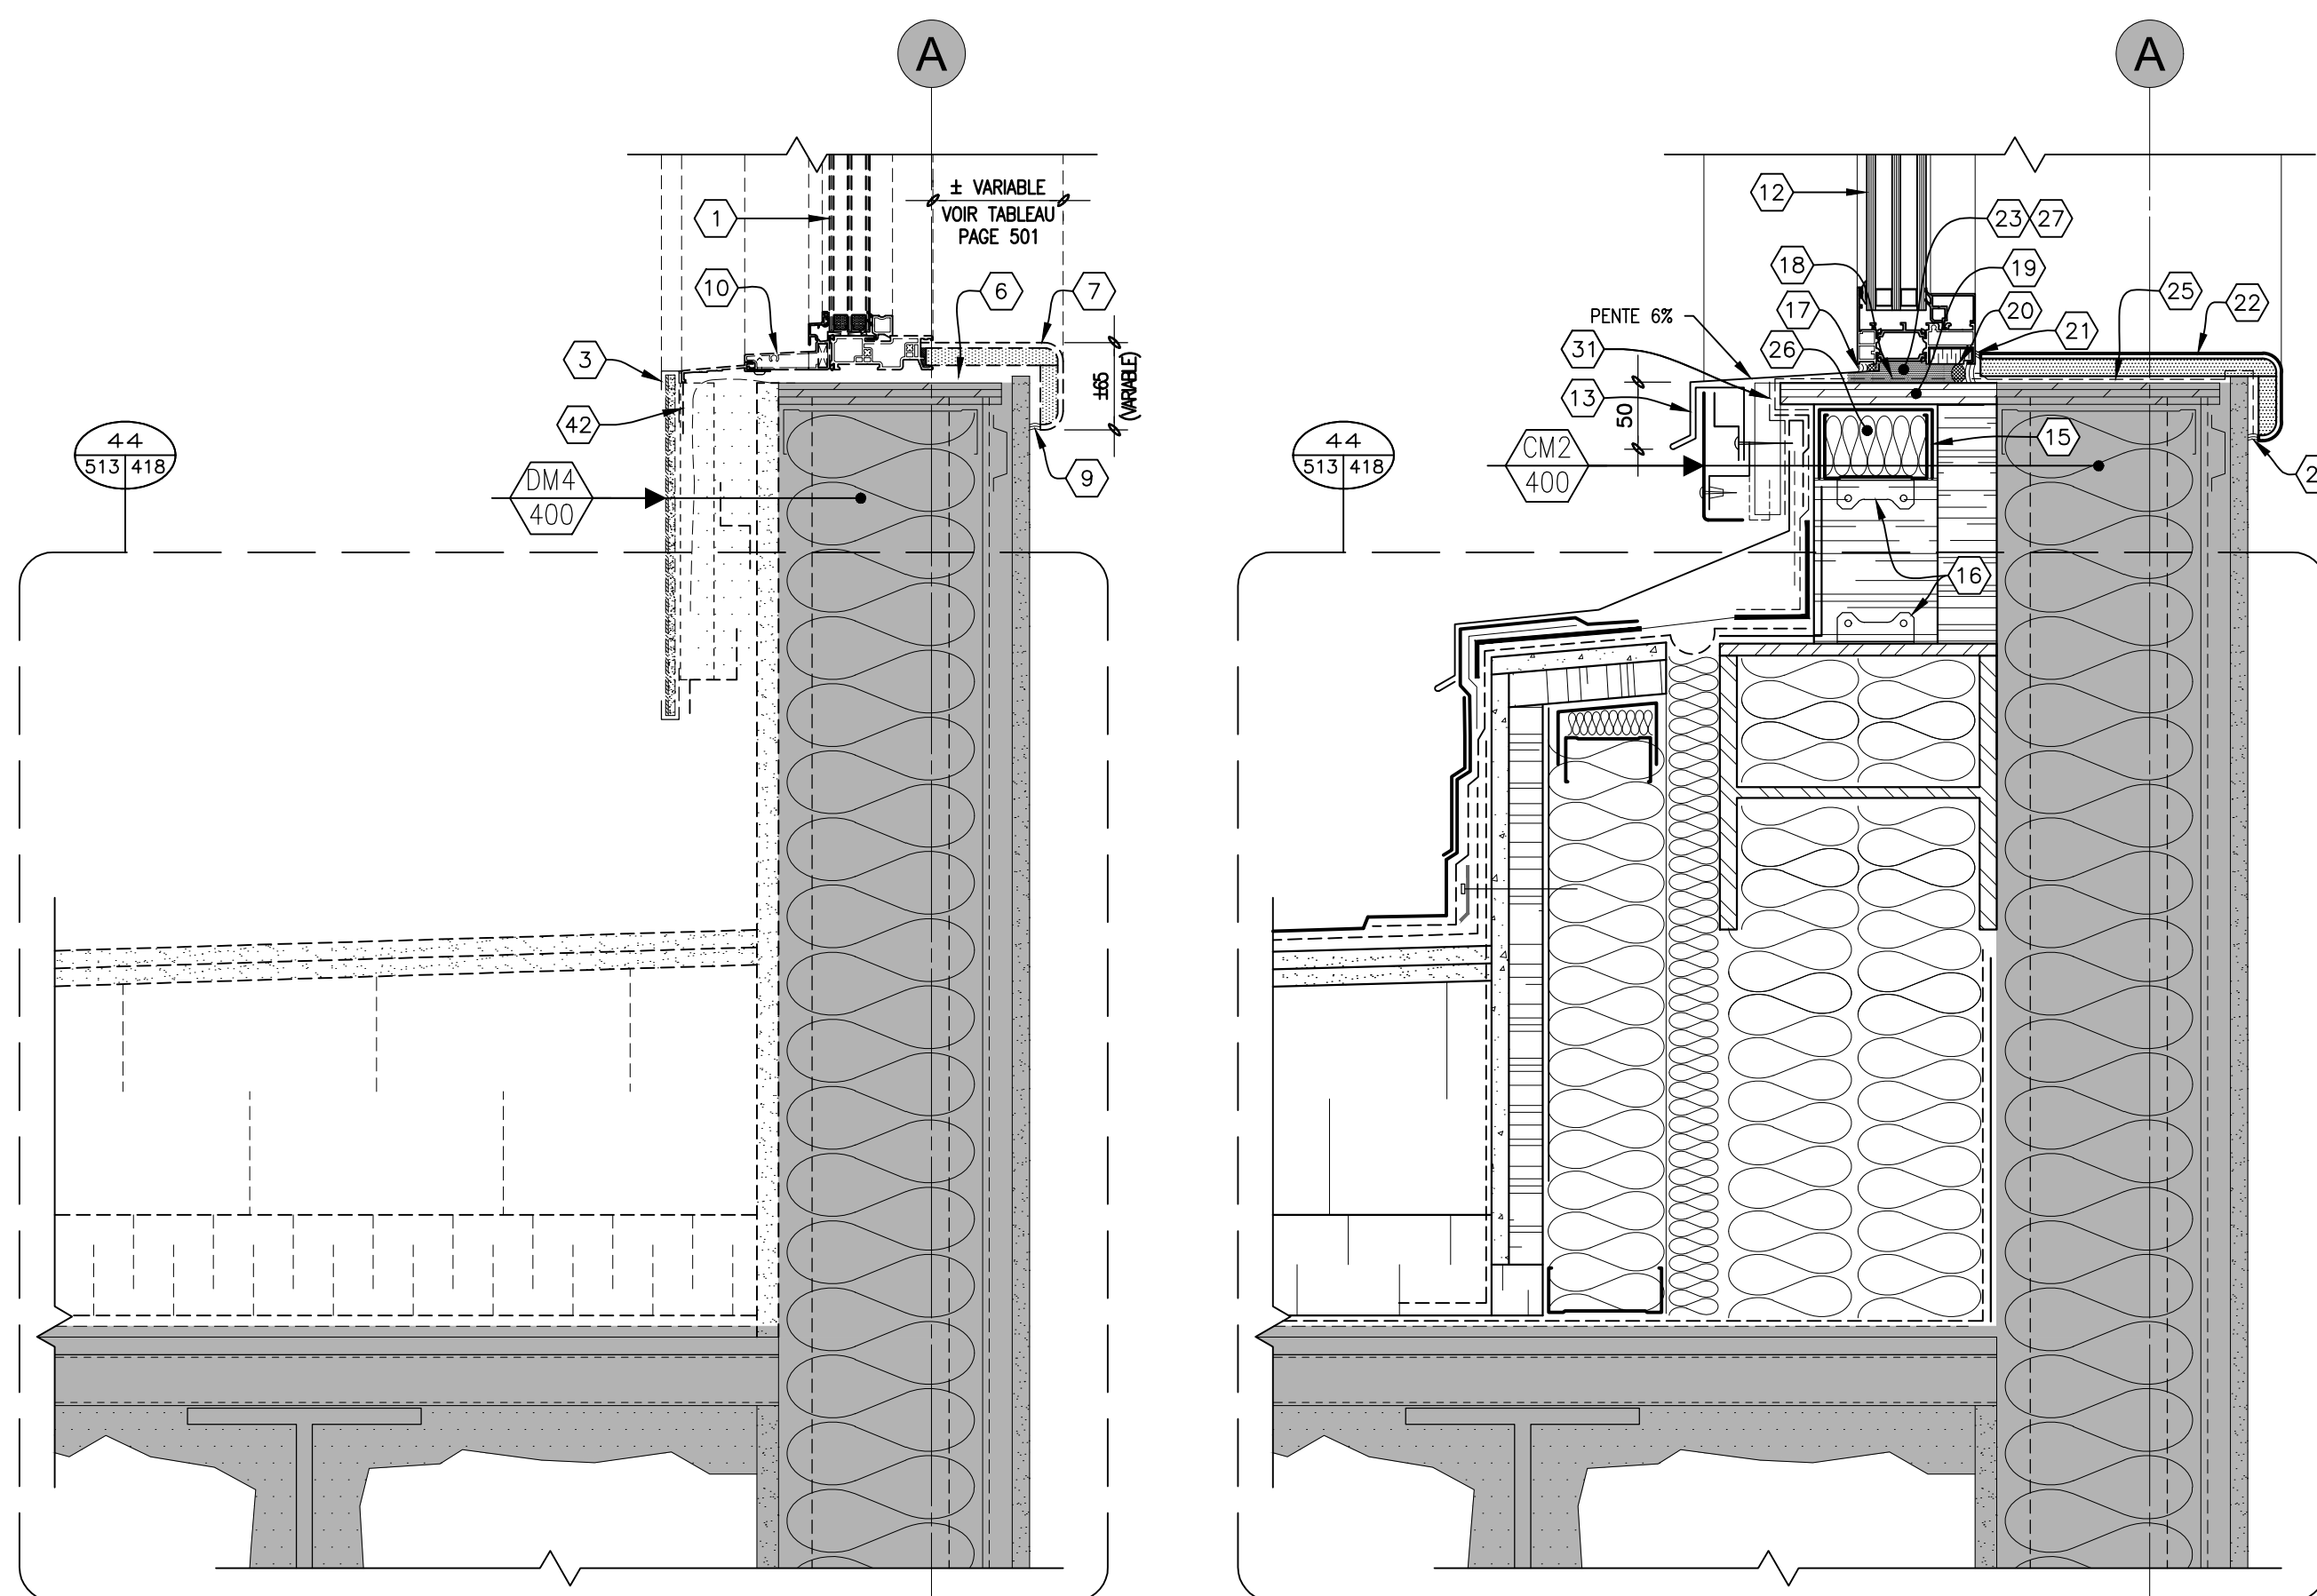

DÉMOLITION

ALLÈGE

CONSTRUCTION

25 DÉTAIL DE FENÊTRE TYPE (BASILAIRE)
502,503 513 1:5mm
(LABORATOIRE/FAÇADE NORD)

LÉGENDE

- EXISTANT À CONSERVER.
- ÉLÉMENT À DÉMOLIR.
- AXE EXISTANT
- EXTÉRIEUR DE LA STRUCTURE DE BÉTON EXISTANTE DE LA TOUR.
- NOUVEL AXE: FACE EXTÉRIEURE DES BARRES Z ET COLOMBAGES DE LA TOUR. VOIR STRUCTURE.
- NOUVEL AXE: FACE EXTÉRIEURE DES BARRES Z ET COLOMBAGES DE LA TOUR. VOIR STRUCTURE.

NOTES

- FENÊTRE HYBRIDE (ALUMINIUM/PVC) EXISTANTE À DÉMOLIR.
- RAIL DU VOLET COUPE-FEU À PEINTURER, COULEUR TEL QUE LE MUR.
- MOULURE EN ALUMINIUM À DÉMOLIR.
- RAIL DU VOLET COUPE-FEU À PEINTURER, COULEUR AU CHOIX DE L'ARCHITECTE.
- CONTREPLAQUÉ EXISTANT À DÉMOLIR.
- MEMBRANE AUTOADHÉSIVE EXISTANTE À DÉMOLIR.
- FINITION INTÉRIEURE EN CONTREPLAQUÉ RECOUVERT DE STRATIFIÉ À DÉMOLIR.
- DIFFUSEUR D'ÉCLAIRAGE PERFORÉ AMOVIBLE, COULEUR CHROME.
- SCÉLLANT EXISTANT À ENLEVER. NETTOYER LES SURFACES EXISTANTES CONSERVÉES DE TOUTES TRACES DE SCÉLLANT.
- SECTION DU CADRE DE FENÊTRE À COUPER ET À DÉMOLIR. VOIR DÉTAILS EN ÉTAPES À LA PAGE 505.
- TOILE, STORE ET/OU HABILLAGE DE FENÊTRE À ENLEVER ET À REMETTRE AU PROPRIÉTAIRE. VOIR NOTE PAGE 505.
- NOUVELLE FENÊTRE EN ALUMINIUM.
- SOLIN EN ACIER ÉMAILLÉ, CAL.24.
- MOULURE EN "J" EN ACIER ÉMAILLÉ, CAL.24.
- ASSEMBLAGE DE COLOMBAGE ET DE LISSE SUR TOUT LE PÉRIMÈTRE DE L'OUVERTURE, VOIR STRUCTURE.
- CONNECTEUR, VOIR STRUCTURE.
- SCÉLLANT SUR FOND DE JOINT.
- MEMBRANE D'ÉTANCHÉITÉ AUTOADHÉSIVE SUR TOUT LE PÉRIMÈTRE DE L'OUVERTURE.
- CONTREPLAQUÉ À PLUS 19mm D'ÉPAISSEUR.
- BOUDIN D'ÉTAFOAM DE DIAMÈTRE APPROPRIÉ ET SCÉLLANT CONTINU SUR TOUT LE PÉRIMÈTRE DE LA FENÊTRE POUR ASSURER LA CONTINUITÉ DE L'ÉTANCHÉITÉ ENTRE LA MEMBRANE ET LE CADRE DE LA FENÊTRE.
- SCÉLLANT DE FINITION.
- FINITION EN CONTREPLAQUÉ À PLUS 19mm D'ÉPAISSEUR RECOUVERT DE PLASTIQUE STRATIFIÉ, COIN ARRONDI SUR TOUT LE PÉRIMÈTRE DE L'OUVERTURE. COULEUR AU CHOIX DE L'ARCHITECTE.
- POLYURÉTHANE GICLÉ NON EXPANSIF SUR LE PÉRIMÈTRE DE LA FENÊTRE.
- RUBAN AUTOCOLLANT. SCÉLLER LA MEMBRANE PARE-INTÉRIÈRES AVEC LA MEMBRANE AUTOADHÉSIVE.
- MEMBRANE AUTOADHÉSIVE PARE-VAPEUR SUR TOUT LE PÉRIMÈTRE DE L'OUVERTURE. SCÉLLER SUR LA NOUVELLE MEMBRANE SOUS LE CADRE DE FENÊTRE ET SUR LE POLYÉTHYLÈNE DU MUR EXISTANT.
- REMPUR L'ESPACE DE LAINE DE FIBRE DE ROCHE.
- CALE D'AJUSTEMENT EN POLYVINYLE RIGIDE D'ÉPAISSEUR REQUISE.
- "L" EN ACIER 76X89MM X 4MM D'ÉPAISSEUR À PEINDRE, COULEUR TEL QUE LE MUR.
- RIVET EN ACIER PRÉPÊTÉ, DE MÊME COULEUR QUE LE PAREMENT.
- PLIAGE DE TÔLE EN ACIER GALVANISÉ CAL. 22.
- RUBAN AUTOCOLLANT.
- TÔLE PLIÉE EN ACIER GALVANISÉ 75mm X 75mm, CAL. 16, AU POURTOUR DE L'OUVERTURE.
- MEMBRANE AUTOCOLLANTE PARE-VAPEUR.
- CONTREPLAQUÉ À PLUS D'ÉPAISSEUR REQUISE.
- PANNEAU DE PARTICULES AGGLOMÉRÉES HAUTE DENSITÉ 16mm, FINI MÉLAMINE, COULEUR AU CHOIX DE L'ARCHITECTE.
- BOUT DU PANNEAU REPLIÉ VERS L'INTÉRIEUR.
- MEMBRANE LIQUIDE PULVÉRISÉE PAR-DESSUS LA MEMBRANE AUTOADHÉSIVE.
- PLAFOND SUSPENDU À DÉMANTÉLER SUR LA DIMENSION REQUISE POUR L'INSTALLATION DU VOLET COUPE-FEU DANS L'ENTREPLAFOND.
- PIÈCE DE BOIS EXISTANTE À DÉMOLIR.
- VOLET COUPE-FEU, VOIR DEVIS.
- PANNEAU DE PARTICULES AGGLOMÉRÉES HAUTE DENSITÉ 16mm, FINI MÉLAMINE, COULEUR AU CHOIX DE L'ARCHITECTE.
- TÔLE EXISTANTE RIVETÉE SUR LA BARRE EN "Z" ET AU CADRE DE LA FENÊTRE À DÉMOLIR.
- MEMBRANE AUTOCOLLANTE EXISTANTE À DÉMOLIR.
- BARRE EN "Z" AJUSTABLE EXISTANTE À DÉMOLIR.
- PLAFOND SUSPENDU EXISTANT À RÉINSTALLER AVEC NOUVELLE SUSPENSION EN ALUMINIUM ET NOUVELLES TUILLES.
- MOUSTIQUEAIRE.
- OUVRIR LE MUR POUR L'INSTALLATION DU FOND DE CLOUAGE.
- PLAQUE DE PLÂTRE DE MÊME ÉPAISSEUR QUE CEUX EXISTANTS (2 RANGS) À PEINDRE.
- FOND DE CLOUAGE EN ACIER GALVANISÉ CAL.16, FIXÉ AU COLOMBAGE EXISTANT POUR LA FIXATION DU "L" EN ACIER.
- BOULON D'ANCRAGE DE DIMENSION REQUISE À PEINDRE.

NE DOIT PAS SERVIR À L'EXÉCUTION

Le présent document est émis pour la seule fin identifiée. Son contenu est protégé par les droits d'auteur et toute reproduction ou modification, partielle ou totale, est interdite sans l'autorisation écrite de gagnon, letellier, cyr, ricard, mathieu, proulx, savard consortium d'architectes.




GLCRM | Proulx Savard |

GLCRM:
128, Avenue de la Cathédrale,
Bureau 201
Rimouski, QC, G5L 5H7
(418) 722-7655



2406, Ch. des Quatres-Bourgeois,
Bureau 100
Québec, QC, G1V 1W5
(418) 647-1700

Proulx Savard Architectes:
75, boul. Arthur-Buies Ouest,
Rimouski QC G5L 5C2
(418) 723-5543

ARCHITECTURE

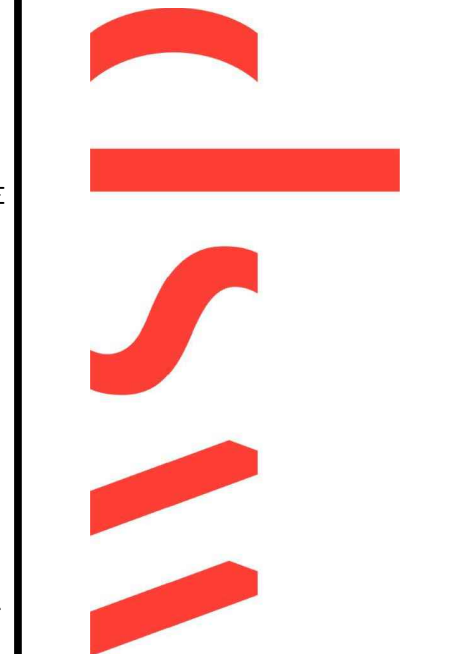

CONSULTANTS

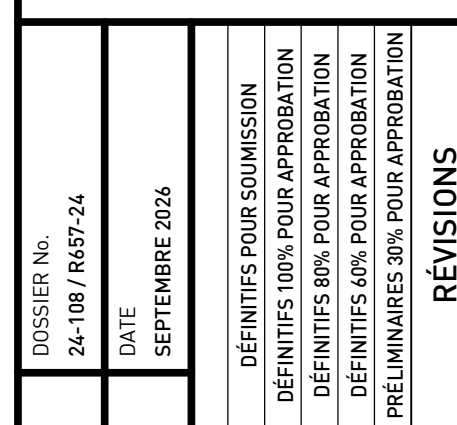
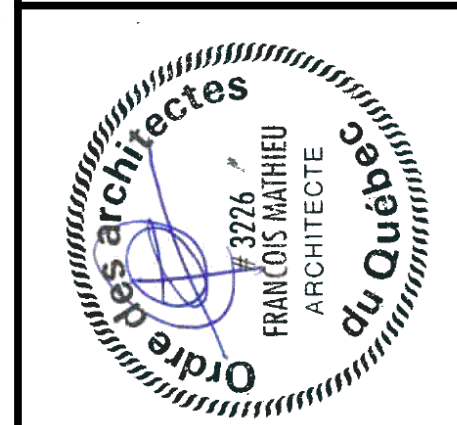


DESSIN	PROJET	PROPRIÉTAIRE
DETAIL TYPE DE FENÊTRE (BASILAIRE) DÉMOLITION ET CONSTRUCTION	HÔPITAL DE CHANDLER, Chandler (Réfection de l'enveloppe)	Santé Québec

513

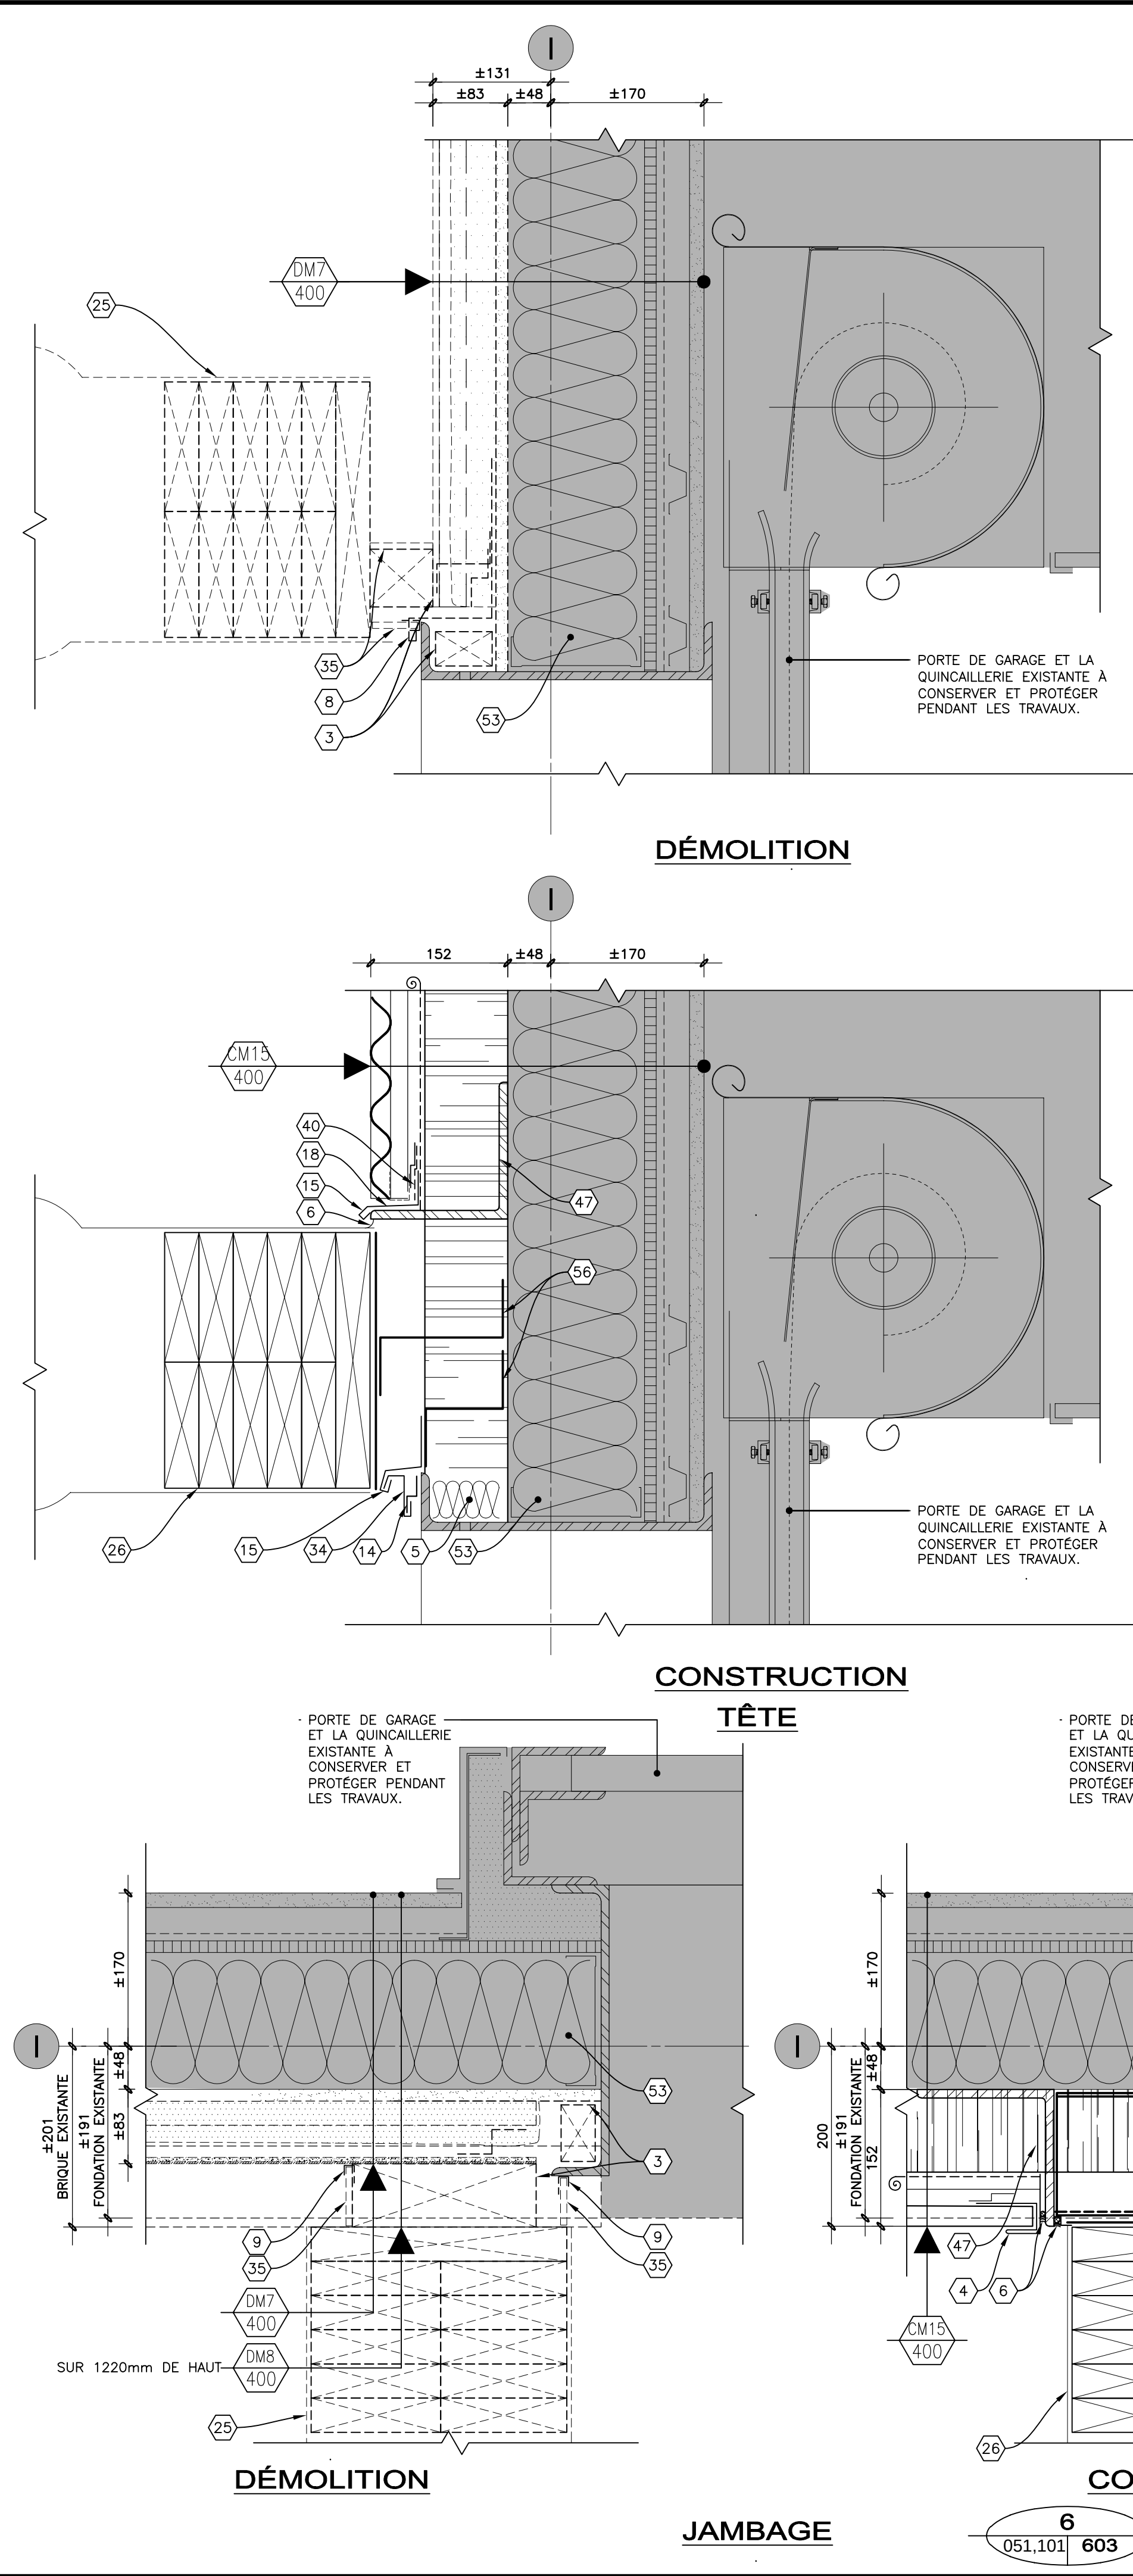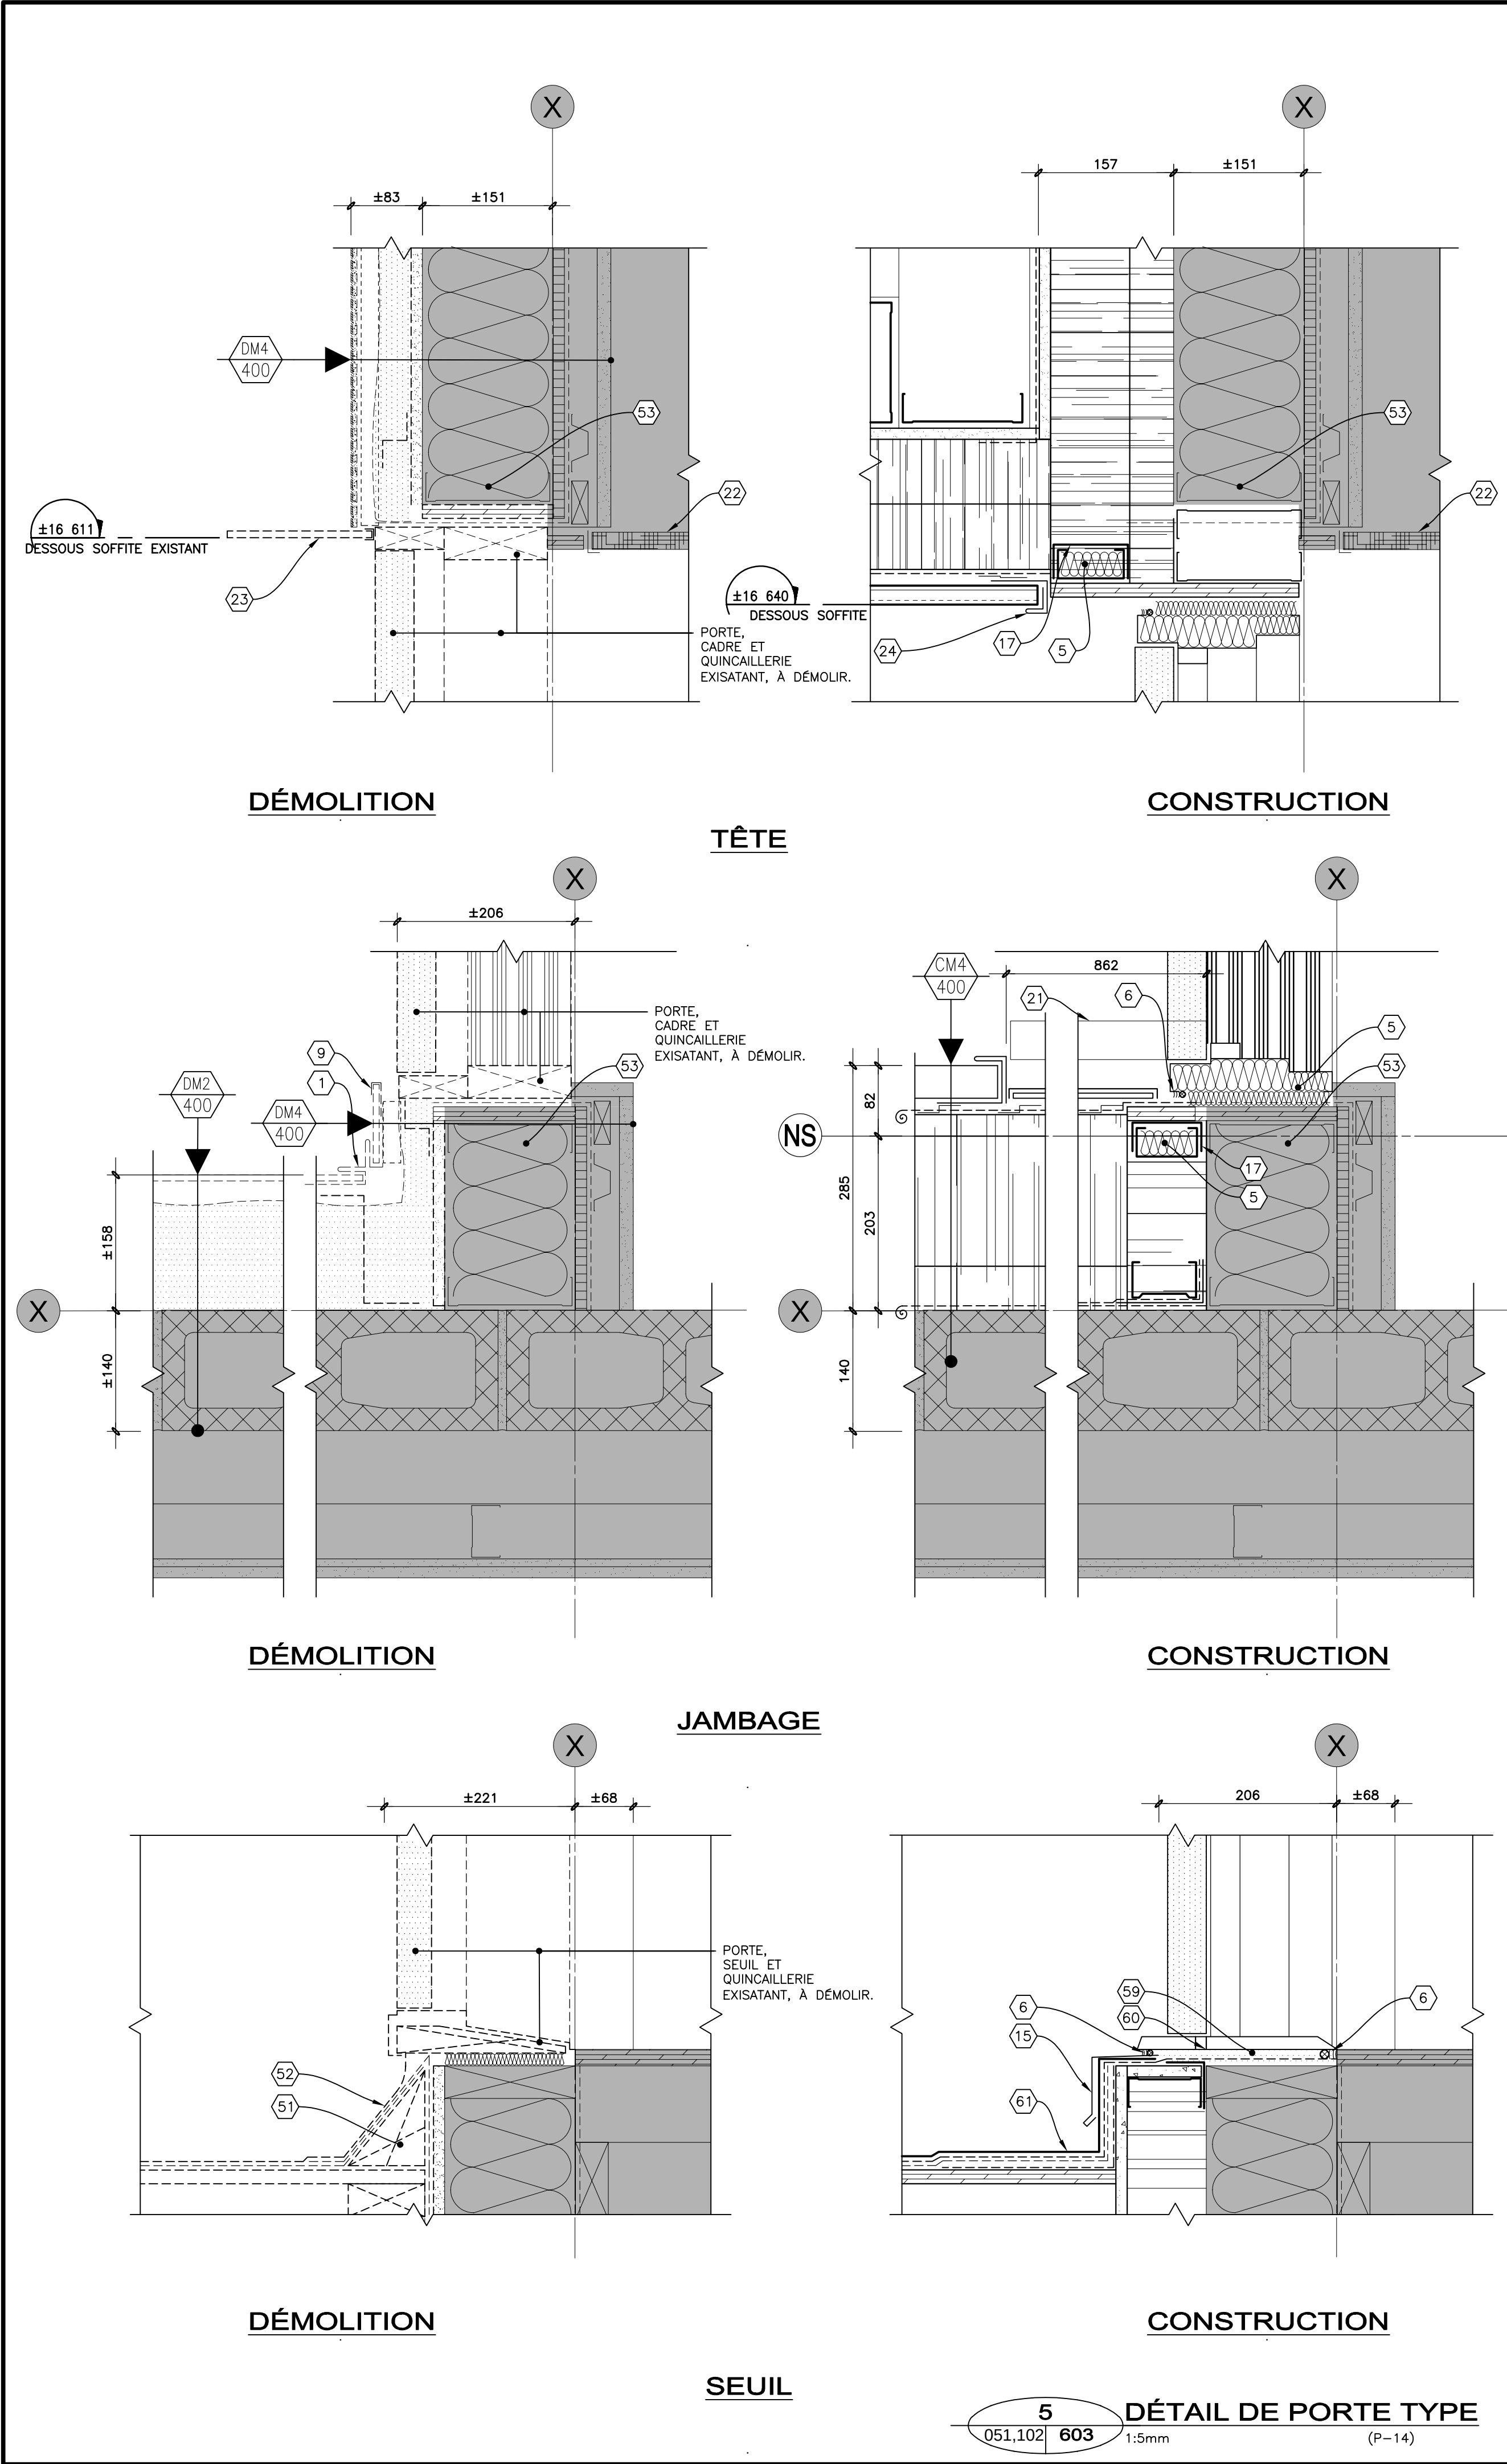

NOTES	NOTES
(51) FAINE DE BOIS À DÉMOLIR. (52) MEMBRANE DE BITUME MODIFIÉE BI-COUCHE À DÉMOLIR. (53) PRÉVOIR LE RETRAIT TEMPORAIRE DE L'ISOLANT EXISTANT POUR LA FIXATION DES ASSEMBLAGES DE STRUCTURE. (54) PLAQUE D'ACIER PLIÉE EN 1 MORCEAU. (55) PRÉVOIR UN PERCEMENT DANS LA PLAQUE POUR LE PASSAGE DU FILAGE DU LECTEUR DE CARTE, VOIR INGÉNIERIE. (56) BARRE EN "Z" HORIZONTALE. (57) PLAQUE STRIÉE PLIÉE DE 6mm. (58) PLIAGE EN PLAQUE STRIÉE À RETIRER. (59) LIT DE SCELLANT. (60) SEUL DE PORTE AVEC BRIS THERMIQUE. (61) MEMBRANE DE FINITION GRANULÉ.	(1) MOULURE DE COIN EXISTANTE À DÉMOLIR. (2) MOULURE EN "J" EXISTANTE À DÉMOLIR. (3) PIÈCE DE BOIS EXISTANTE À DÉMOLIR. (4) MOULURE EN "J" EN ACIER ÉMAILLÉ, CAL.22. (5) REMPLIR L'ESPACE D'ISOLANT DE FIBRE DE ROCHE EN MATELAS. (6) SCELLANT CONTINU SUR BOUDIN COMPRESSIBLE 10mm MINIMUM. (7) VIS À TÊTE FRAISÉE. (8) SOLIN MÉTALLIQUE À DÉMOLIR. (9) MOULURE EN ALUMINIUM DES PANNEAUX À DÉMOLIR. (10) TÔLE D'ÉTANCHÉITÉ EN L, CAL.22 EN ACIER GALVANISÉ. (11) SCELLANT ET BOUDIN EXISTANT À DÉMOLIR. (12) CONNECTEUR À CHAQUE COLOMBAGES OU BARRE EN "Z" SELON LE CAS, VOIR STRUCTURE. (13) RIVET EN ACIER INOXYDABLE. (14) PLIAGE EN TÔLE EN ACIER GALVANISÉ, CAL.22. (15) SOLIN EN ACIER ÉMAILLÉ, CAL.22. (16) MEMBRANE DE TYPE 1. (17) LITEAU OU JAMBAGE RENFORCÉ EN COLOMBAGES MÉTALLIQUES, VOIR DOCUMENTS D'INGÉNIERIE. (18) MOUSTQUAIRE. (19) CONTREPLAQUÉ DE TYPE EXTÉRIEUR ±16mm. (20) CADRE DE LA PORTE RECOUVERT D'UN PLIAGE EN ALUMINIUM. (21) PROFIL D'OUVERTURE DE LA PORTE. (22) PLAFOND EXISTANT. (23) SOFFITE EXISTANT À DÉMOLIR. (24) NOUVEAU SOFFITE EN PAREMENT D'ACIER CORRUGUÉ. (25) COUSSINS GONFLABLES EXISTANT À DÉMONTÉLER ET ENTREPOSER POUR LA PÉRIODE DE TRAVAUX, VOIR DOCUMENTATIONS D'INGÉNIERIE POUR LE RACCORDEMENT ÉLECTRIQUE. (26) COUSSINS GONFLABLES EXISTANT À REINSTALLER AU POURTOUR DE LA PORTE, VOIR DOCUMENTS D'INGÉNIERIE POUR LE RACCORDEMENT ÉLECTRIQUE. (27) PLIAGE DE TÔLE EXISTANT À DÉMOLIR. (28) SECTION DE CONTREPLAQUÉ EXISTANT À DÉMOLIR. (29) BÂTI COMPOSÉ DE 2 CONTREPLAQUÉS DE TYPE EXTÉRIEUR 19mm ép. PRÉ-MEMBRANE D'UNE MEMBRANE DE TYPE 1 AUTOCOLLANTE. (30) SCELLANT. (31) REMPLIR LES EXTRÉMITÉS DE L'ALLÈGE VERS LE HAUT SOUS LE PLIAGE DES JAMBAGES. (32) PIÈCE DE BOIS BISEAUTÉ DE DIMENSIONS APPROPRIÉES. (33) PLANCHER DE CÉRAMIQUE EXISTANT À CONSERVER. (34) AGRAFFE EN ACIER ÉMAILLÉ CAL.22. (35) PANNEAU DE POLYMERES RENFORCÉ DE FIBRES DE VERRE 7mm D'ÉPAISSEUR À DÉMOLIR. (36) CONTREPLAQUÉ À PLUS 16mm RECOUVERT D'UNE MEMBRANE DE TYPE 1 ET D'UNE TÔLE PLIÉE EN ACIER ÉMAILLÉ CAL.24. (37) COUPER SOIGNEUSEMENT LE CONTREPLAQUÉ ET OU LA PIÈCE DE BOIS DE MANIÈRE À CE QUE CEUX-CI ARRIVENT EN ALIGNEMENT AVEC LA FACE DE L'ÉLÉMENT STRUCTURAL DU MUR (MONTANT D'ACIER, BLOCS DE BÉTON OU POUTRE DE BÉTON). (38) ISOLANT DE FIBRE DE VERRE EXISTANT DANS LE CADRE DE PORTE À CONSERVER ET PROTÉGER PENDANT LA PÉRIODE DE TRAVAUX. DANS LE CAS OÙ L'ISOLANT EST ABIMÉ, QU'IL PRÉSENTE DES TRACES D'HUMIDITÉ OU DE MOISSISURE, RETIRER L'ISOLANT EXISTANT ET LE REMPLACER PAR UN NOUVEL ISOLANT DE FIBRE MINÉRALE EN MATELAS. (39) MEMBRANE DE TYPE 1. COLLER LA MEMBRANE SUR LA SURFACE DU MUR EXISTANT ET LAISSER LE RESTE DE LA MEMBRANE EN ATTENTE DE L'INSTALLATION DES COLOMBAGES MÉTALLIQUES. LORSQUE LES COLOMBAGES MÉTALLIQUES SONT INSTALLÉS, REMONTER LA MEMBRANE SOUS LES LISSES MÉTALLIQUES ET FIXER LE BÂTI DE CONTREPLAQUÉ PRÉ-MEMBRANE AUX LISSES. ASSURER LA PLEINE ADHÉRENCE DE LA MEMBRANE SUR LE BÂTI DE CONTREPLAQUÉS. COLLER LE RESTE DE LA MEMBRANE PAR-DESSUS LE NOUVEAU SOLIN MÉTALLIQUE. (40) SCELLER LA MEMBRANE DE TYPE 3 SUR LA MEMBRANE DE TYPE 1 AVEC UN RUBAN AUTOCOLLANT. (41) TÔLE EN ACIER ÉMAILLÉE EXISTANTE À CONSERVER. (42) SECTION DU CADRE DE FENÊTRES À COUPER ET À DÉMOLIR. VOIR DÉTAILS EN ÉTAPES À LA PAGE 505. (43) MEMBRANE AUTODHÉSIVE EXISTANTE À DÉMOLIR. (44) FINITION INTÉRIEUR EN CONTREPLAQUÉ RECOUVERT DE STRATIFIÉ À DÉMOLIR. (45) FENÊTRE HYBRIDE (ALUMINIUM/PVC) EXISTANTE À DÉMOLIR. (46) SCELLANT EXISTANT À ENLEVER, NETTOYER LES SURFACES EXISTANTES CONSERVÉES DE TOUTES TRACES DE SCELLANT. (47) CORNIÈRE, VOIR STRUCTURE. (48) PERSIENNE EXISTANTE À CONSERVER. (49) COUPE-FROID EXISTANT À DÉMONTÉLER ET ENTREPOSER POUR REINSTALLATION FUTUR. (50) COUPE-FROID EXISTANT REINSTALLÉ.
NOTE GÉNÉRALE: VOIR LA FEUILLE «GESTION DE CHANTIER DÉTAILLÉE» POUR LES PRÉCAUTIONS À PRENDRE LORS DES TRAVAUX POUR MAINTENIR LES ISSUES ET LES CHEMINS D'ÉVACUATION OPÉRATIONNELS DURANT LE CHANTIER	
NE DOIT PAS SERVIR À L'EXÉCUTION	
Le présent document est émis pour la seule fin identifiée. Son contenu est protégé par les droits d'auteur et toute reproduction ou modification, partielle ou totale, est interdite sans l'autorisation écrite de gagnon, letellier, cyr, ricard, mathieu, proulx, savard consortium d'architectes.	

GLCRM | Proulx Savard |
GLCRM:
128, Avenue de la Cathédrale,
Bureau 201
Rimouski, QC, G5L 5H7
(418) 722-7455
2406, Ch. des Quatres-Bourgeois,
Bureau 100
Québec, QC, G1V 1W5
(418) 647-1700
Proulx Savard Architectes:
75, boul. Arthur-Buis Ouest,
Rimouski QC G5L 5C2
(418) 722-5543
ARCHITECTURE

CONSULTANTS

DOSSIER No.	24-102 / 1637-24	DATE	SEPTEMBRE 2024	
DÉSIGNATEUR (S)	A.B.	ÉCHELLE	INDIQUÉE	
DÉTAILS DE PORTE DÉMOLITION ET CONSTRUCTION	DESIGN HÔPITAL DE CHANDLER, Chandler (Réfection de l'enveloppe)	PROJET CHANDLER (Réfection de l'enveloppe)	PROPRIÉTAIRE Santé Québec	
RÉVISIONS		DATE	No	