




PROJET:	
HÔPITAL DE CHANDLER (RÉFECTION DE L'ENVELOPPE)	
TITRE:	
PLAN CLÉ	
NUMÉRO DU FEUILLET:	REV:
S200	0

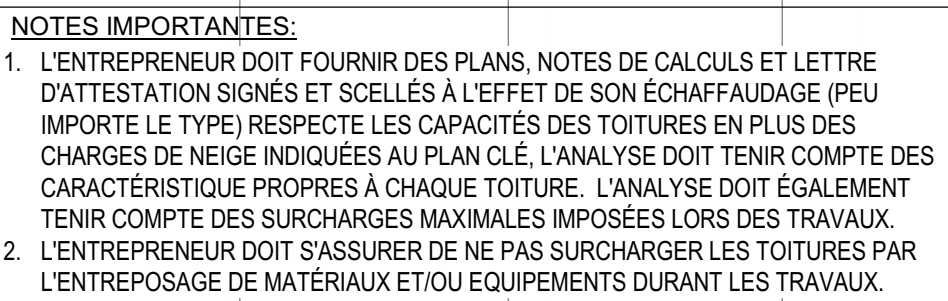

1 : 200

ARCHITECTURE



MÉCANIQUE:



RÉVISIONS:

0	2026-09-04	DÉFINITIFS POUR SOUMISSION	JLB
REV	DATE	DESCRIPTION	PAR

SCEAU:



AVERTISSEMENT: CE DESSIN EST LA PROPRIÉTÉ INTELLECTUELLE DE WSP CANADA INC. AUCUNE RÉVISION, REPRODUCTION OU TOUT AUTRE USAGE N'EST PERMIS SANS L'AUTORISATION ÉCRITE DE WSP CANADA INC. L'ENTREPRENEUR DEVRA VÉRIFIER TOUTES LES DIMENSIONS AUX PLANS ET FAIRE LOCALISER TOUTS LES SERVICES UTILITÉS PUBLIQUES ET RAPPORTER TOUTES ERREURS OU OMISSIONS AVANT DE

DROIT D'AUTEUR:

ÉCHELLE ORIGINALE:
Comme indiqué

PRÉPARÉ PAR:
JOANIE ROBILLARD, ing.
CHARLOTTE ALLARD, CPI
NATHAN SCHMITT, ing. PR

VÉRIFIÉ PAR:
JEAN-LUC BOUFFARD, ing

DESSINÉ PAR:
GLORIA GILDA SIMIREA, te

DATE:
2026-09-04

SI CETTE BARRE NE
MESURE PAS 25 mm,
AJUSTER VOTRE ÉCHELLE
DE TRAÇAGE.


25mm

DISCIPLINE:	STRUCTURE
-------------	-----------



NO PROJET: CA0062562.5541

CLIENT:



RÉF. CLIENT: R674-24 / 24-108

PROJET:

HÔPITAL DE CHANDLER
(RÉFECTION DE L'ENVELOPPE)

TITRE


VUE EN PLAN DU
REZ-DE-CHAUSSÉE -
CONSTRUCTION

NUMÉRO DU FEUILLET:

S201

REV

0

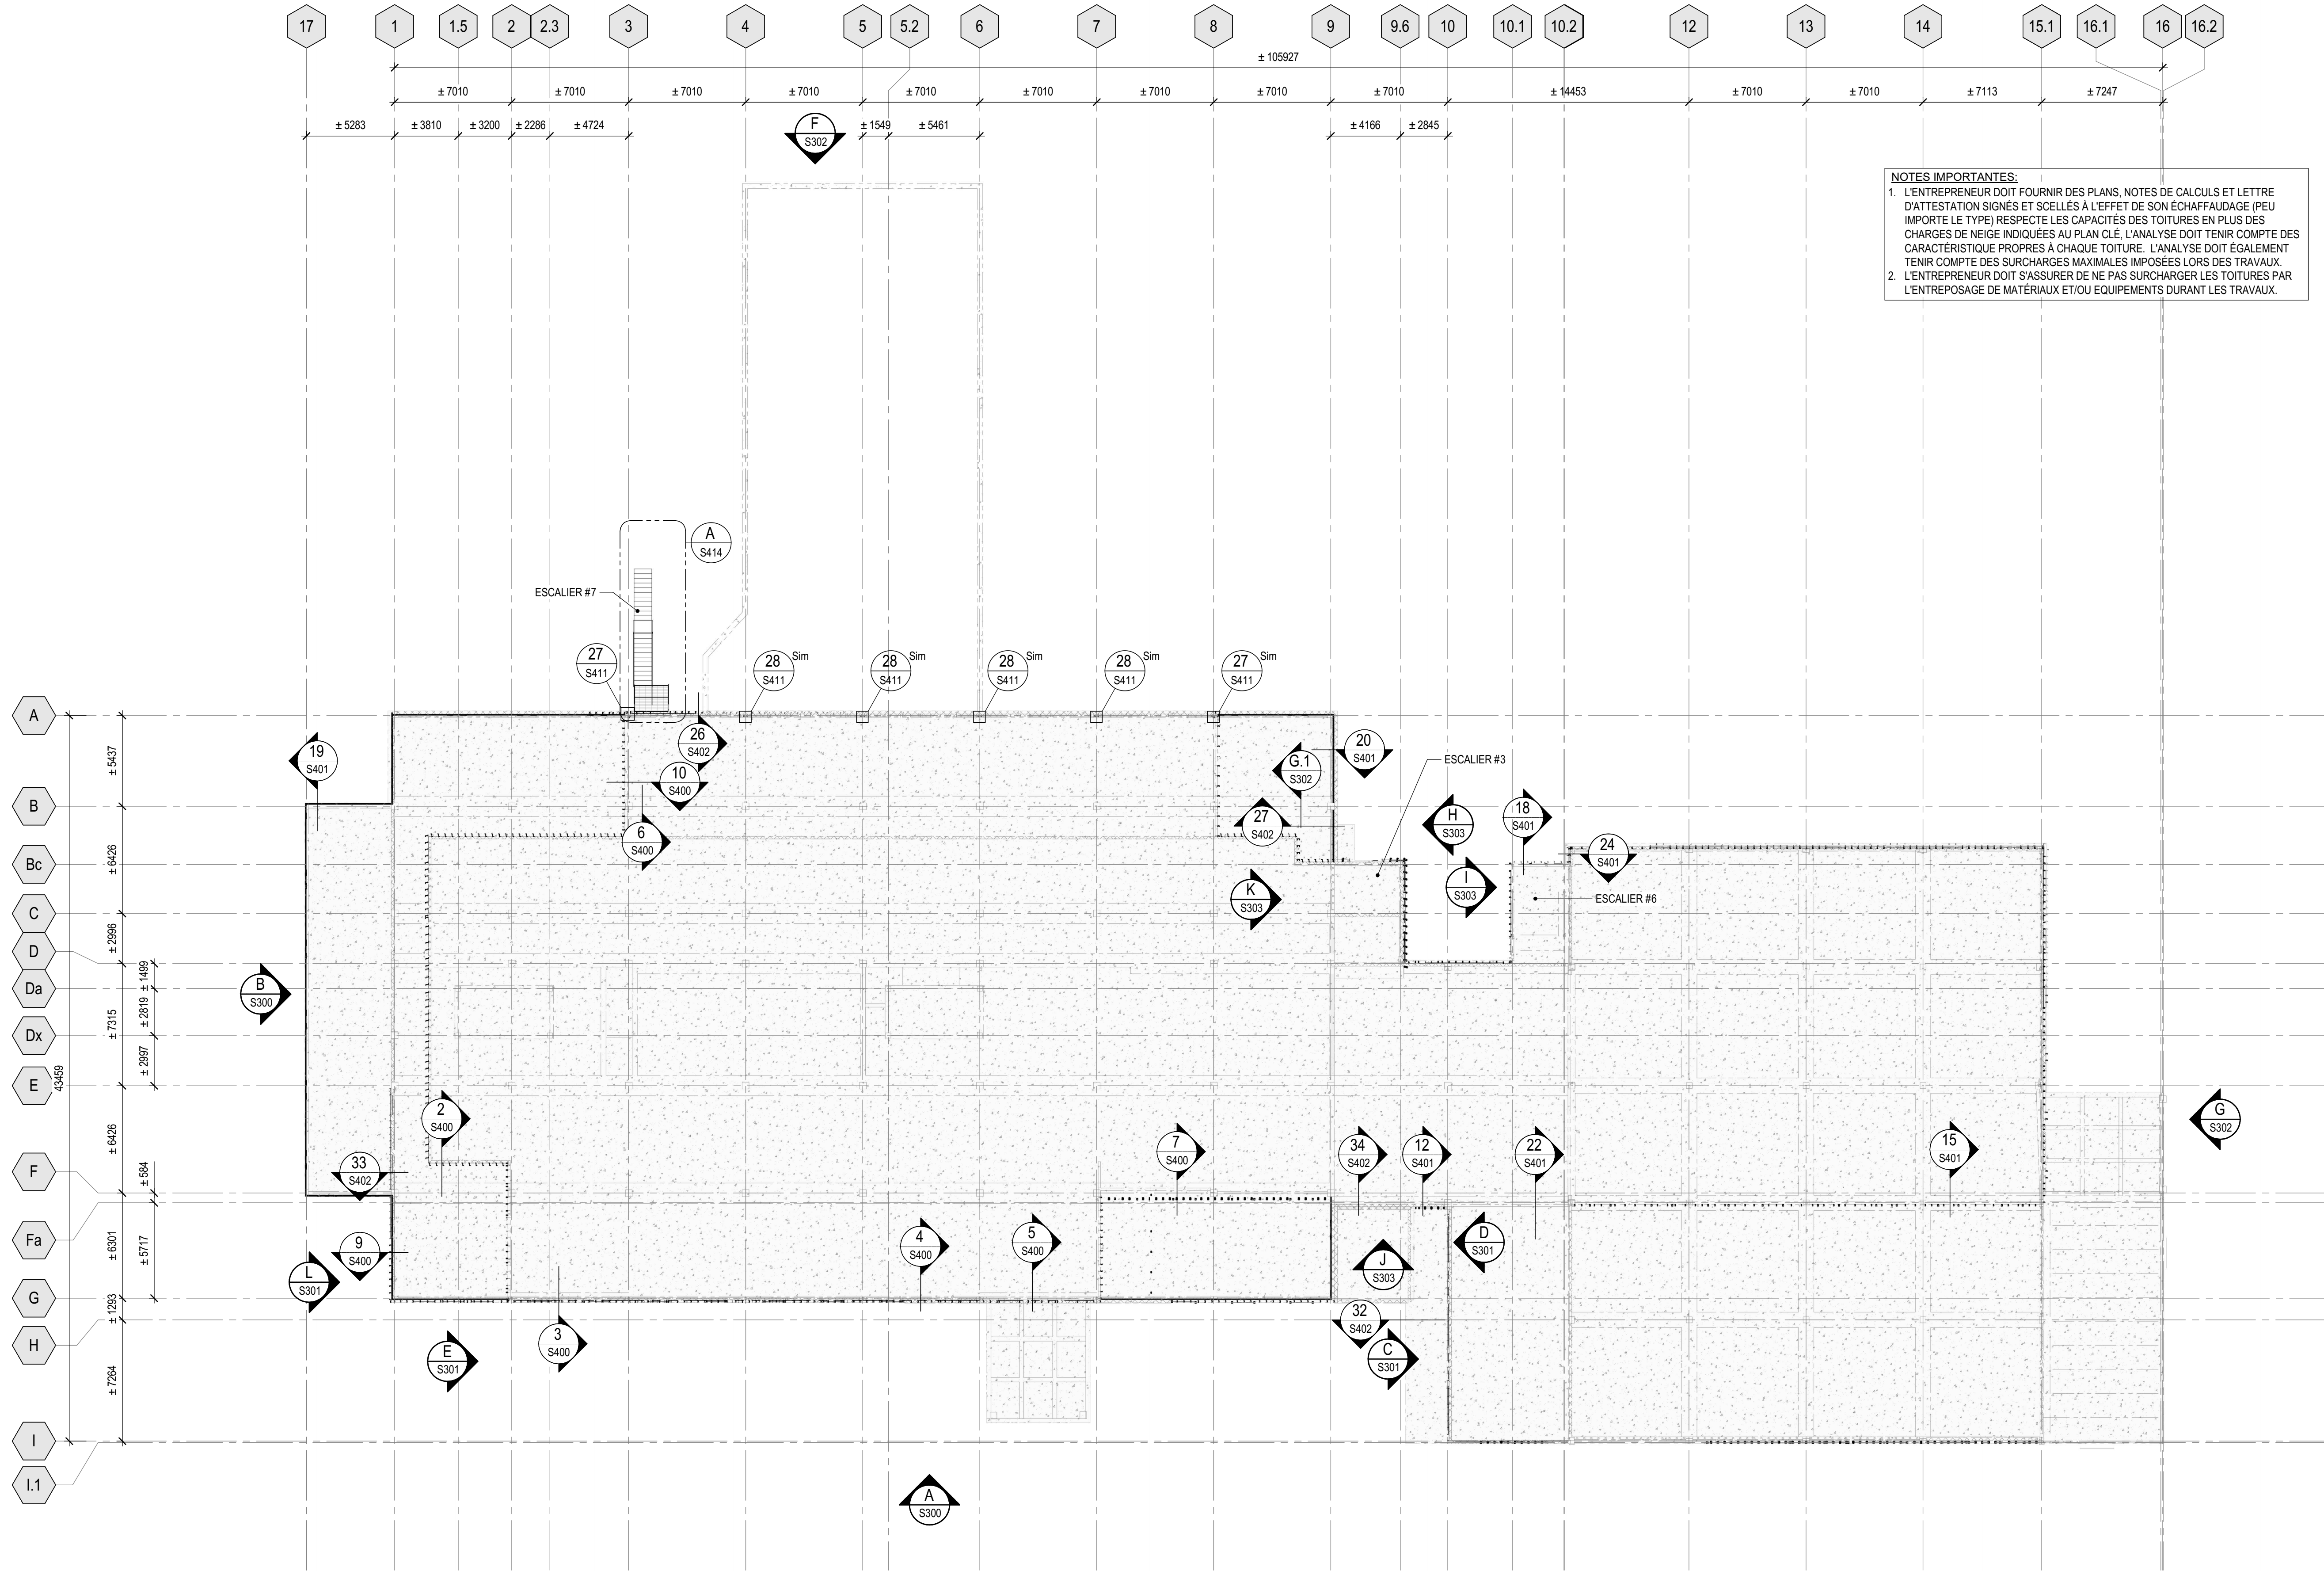

VUE EN PLAN NIVEAU 100 - CONSTRUCTION

1 : 200

CE DOCUMENT NE DOIT PAS ÊTRE UTILISÉ
À DES FINS DE CONSTRUCTION

ARCHITECTURE:



MÉCANIQUE:



RÉVISIONS:

REV	DATE	DESCRIPTION	PAR
0	2026-09-04	DÉFINITIFS POUR SOUMISSION	JLB

SCEAU:



AVERTISSEMENT: CE DROIT D'AUTEUR: L'ENTREPRENEUR DOIT FOURNIR DES PLANS, NOTES DE CALCULS ET LETTRE D'ATTENTION SIGNÉS ET SCÉLÉS À L'EFFET DE SON ÉCHAFFAUDAGE (PEU IMPORTANTE LE TYPE) RESPECTE LES CAPACITÉS DES TOITURES EN PLUS DES CHARGES DE NEIGE INDICÉES AU PLAN CLÉ. L'ANALYSE DOIT TENIR COMPTE DES CARACTÉRISTIQUES PROPRES À CHAQUE TOITURE. L'ANALYSE DOIT ÉGALEMENT TENIR COMPTE DES SURCHARGES MAXIMALES IMPOSÉES LORS DES TRAVAUX. L'ENTREPRENEUR DOIT S'ASSURER DE NE PAS SURCHARGER LES TOITURES PAR L'ENTREPOSAGE DE MATÉRIAUX ET/OU ÉQUIPEMENTS DURANT LES TRAVAUX.

ÉCHELLE ORIGINALE: Comme indiqué	DATE: 2026-09-04
PRÉPARÉ PAR: JOANIE ROBILLARD, ing.	SI CETTE BARRE NE MESURE PAS 25 mm, AJUSTER VOTRE ÉCHELLE DE TRAÇAGE.
CHARLOTTE ALLARD, CPI	
NATHAN SCHMITT, ing. PRT	
VÉRIFIÉ PAR: JEAN-LUC BOUFFARD, ing.	
DESSINÉ PAR: GLORIA GILDA SIMIREAU, tech.	

DISCIPLINE: STRUCTURE



WSP Canada Inc.
1135 Boulevard Lebourgneuf
Ville de Québec, Québec, G2K 0M5
T +1 418-623-2254 | www.wsp.com

NO PROJET: CA0062562.5541

CLIENT:



RÉF. CLIENT: R674-24 / 24-108

PROJET:

HÔPITAL DE CHANDLER
(RÉFECTION DE L'ENVELOPPE)

TITRE:

VUE EN PLAN NIVEAU 100 -
CONSTRUCTION


NUMÉRO DU FEUILLET:

S202

REV:


0

Autodesk Docs/Reflexion Env Hôpital Chandler/CA0062562.5541_STR_P26.rvt
2026-09-04 11:17:19

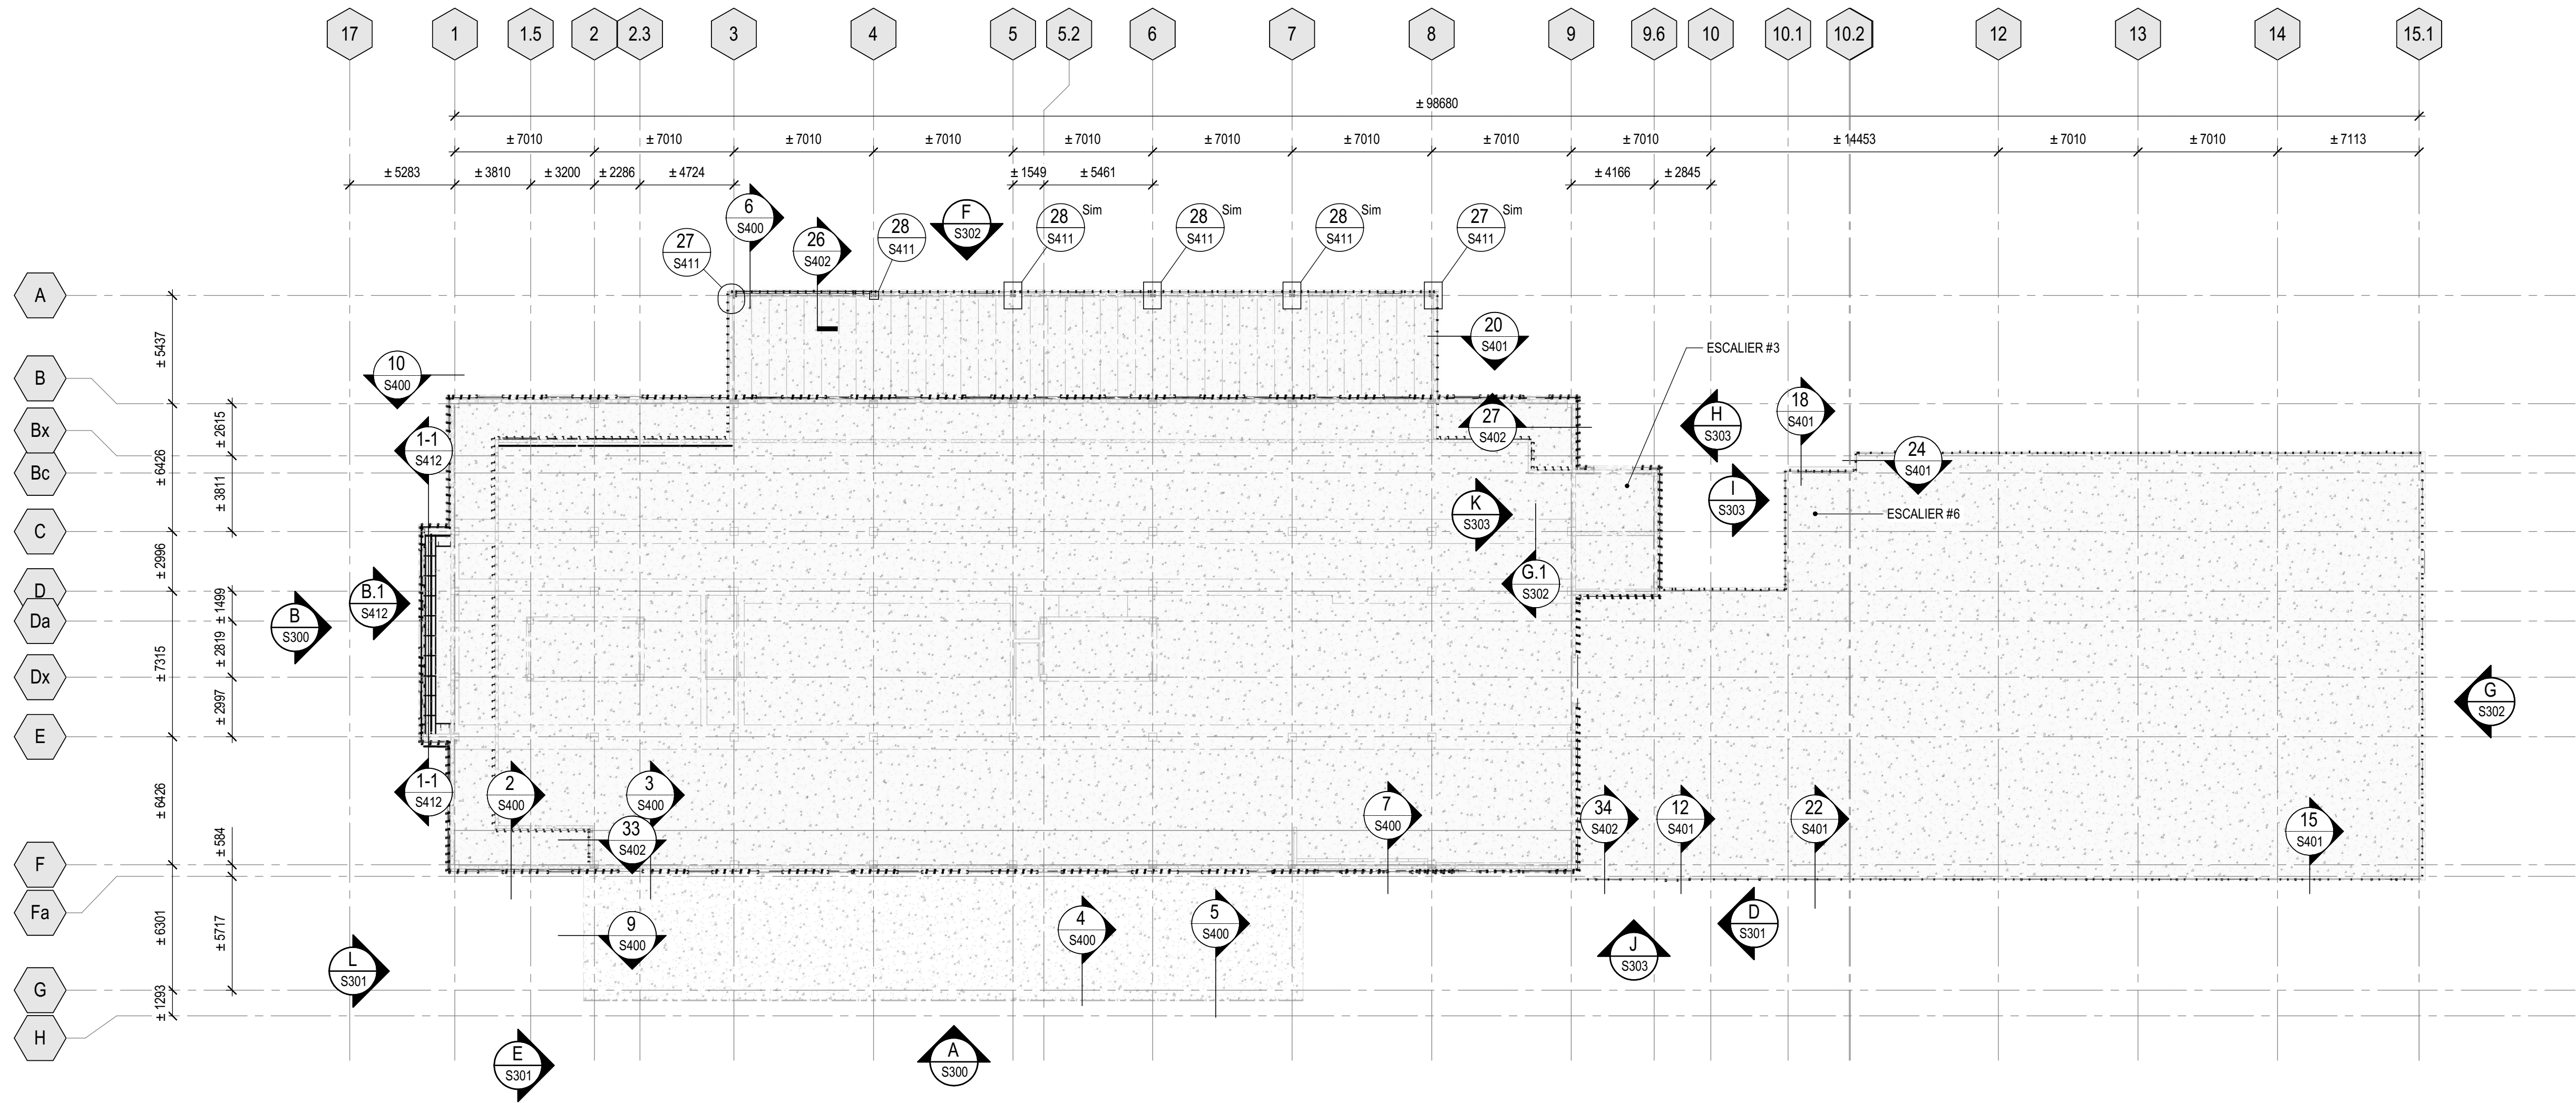

VUE EN PLAN NIVEAU 200 - CONSTRUCTION

1 : 200

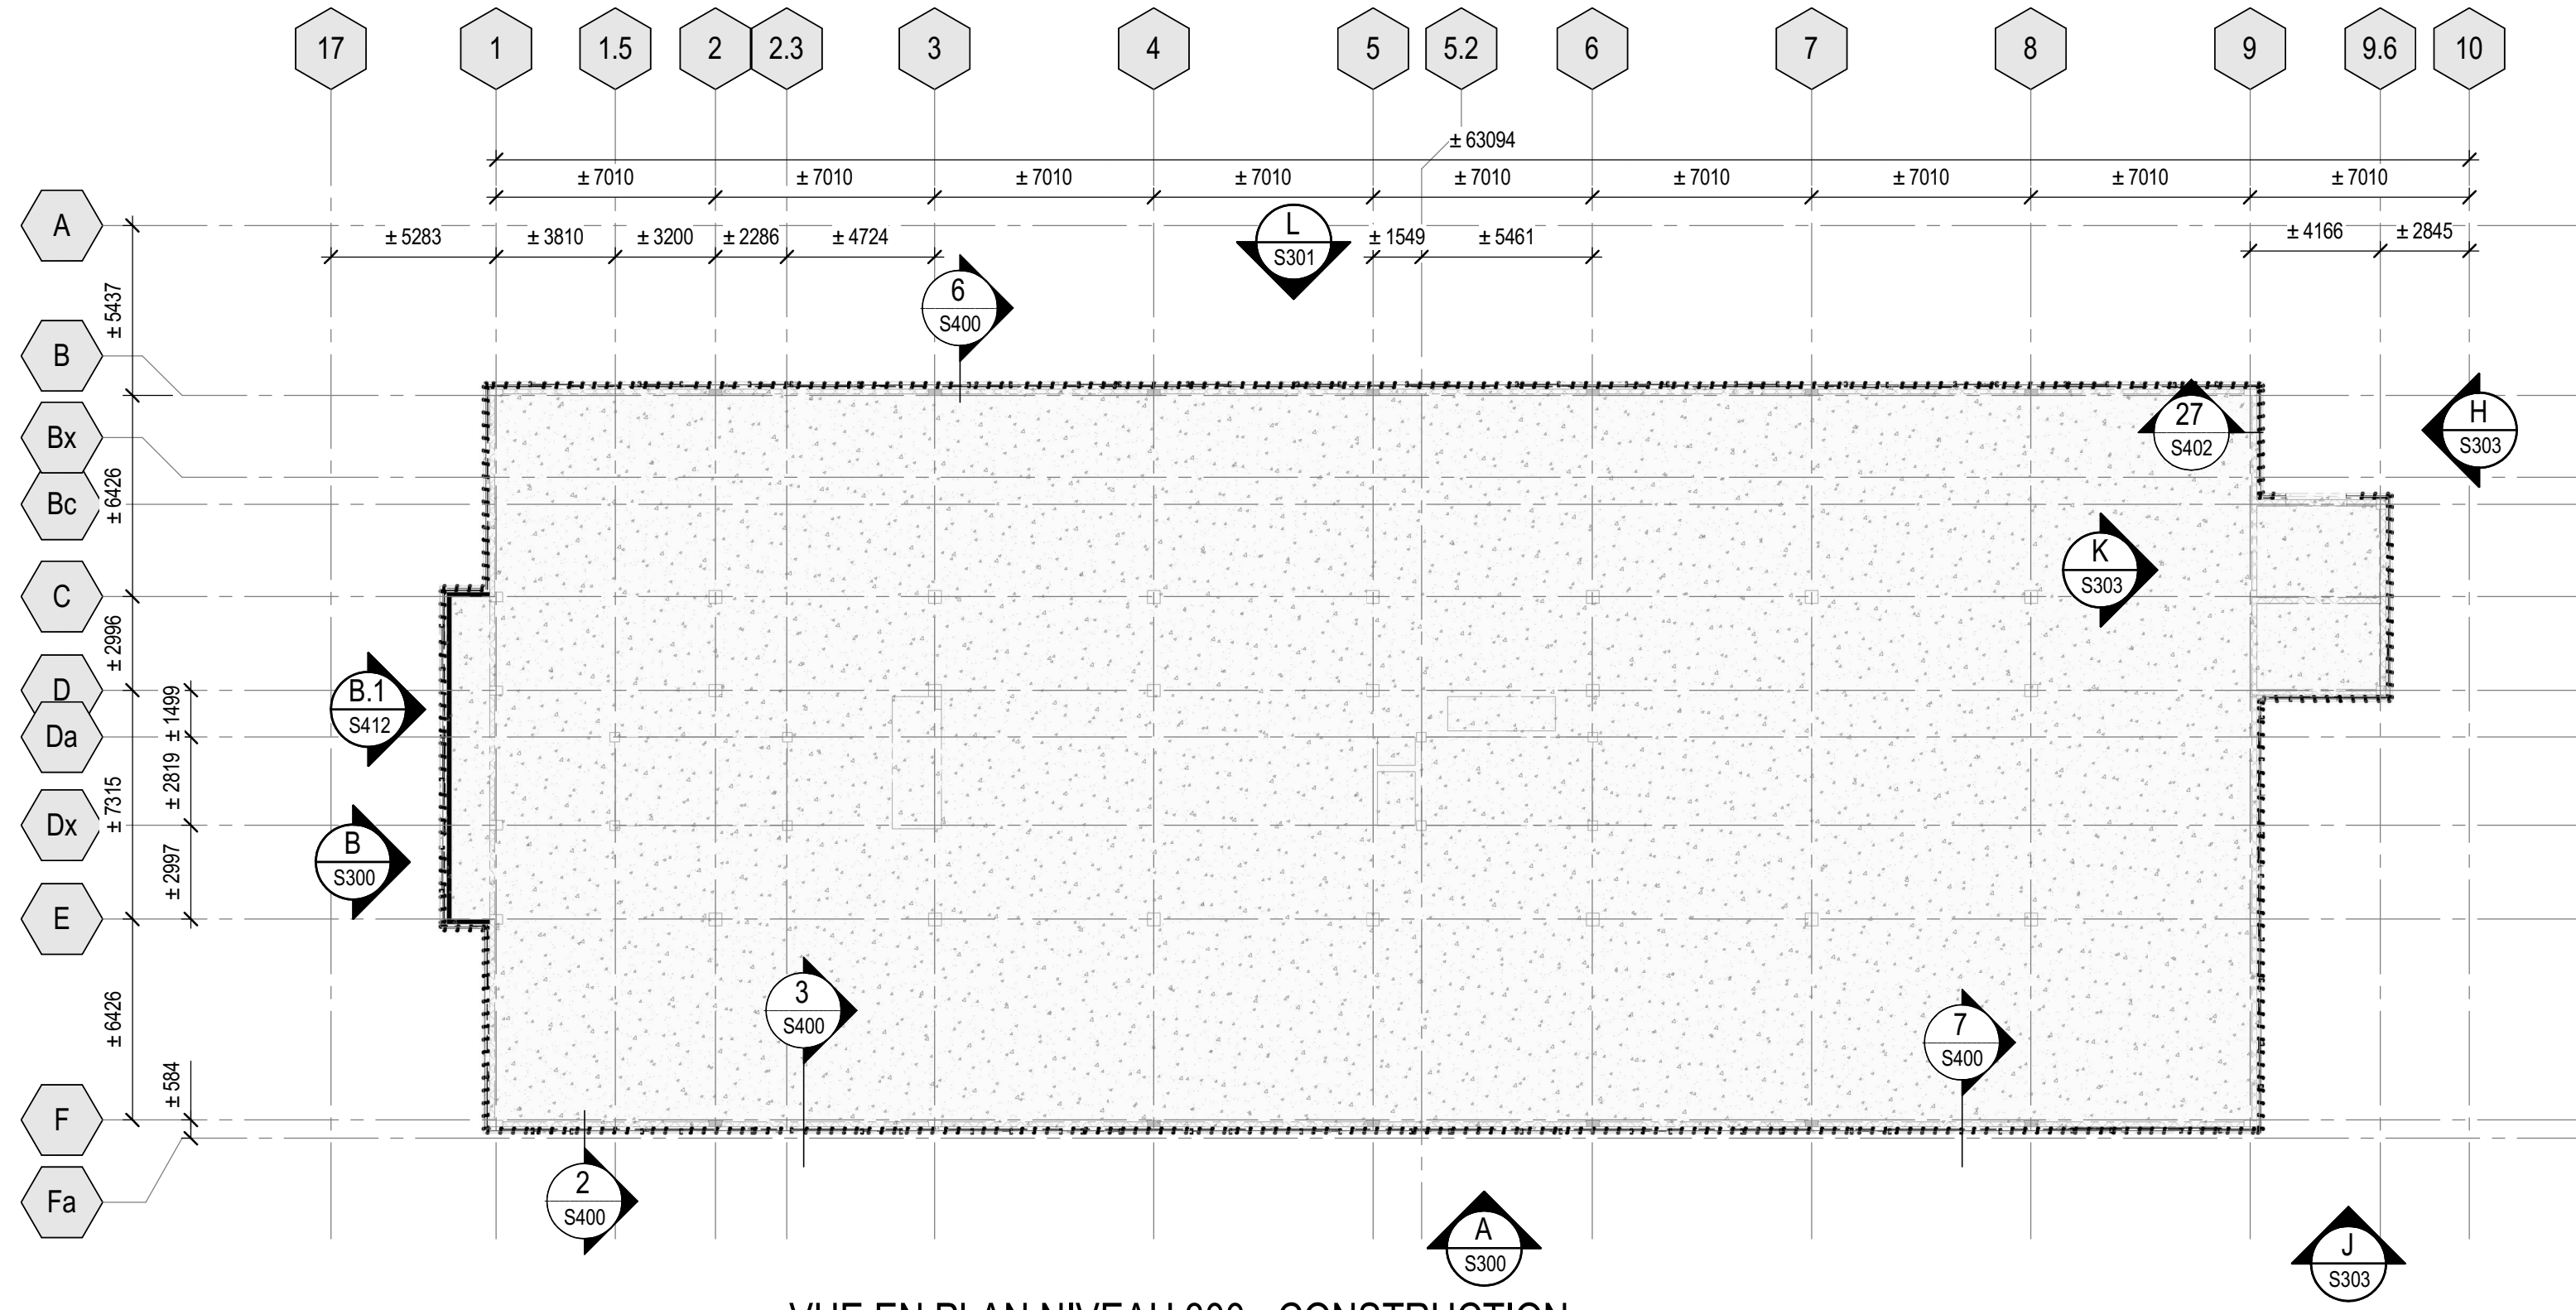

VUE EN PLAN NIVEAU 300 - CONSTRUCTION

1 : 200

NOTES IMPORTANTES:

1. L'ENTREPRENEUR DOIT FOURNIR DES PLANS, NOTES DE CALCULS ET LETTRE D'ATTTESTATION SIGNÉS ET SCÉLLÉS À L'EFFET DE SON ÉCHAFFAUDAGE (PEU IMPORTÉ LE TYPE) RESPECTE LES CAPACITÉS DES TOITURES EN PLUS DES CHARGES DE NEIGE INDICUÉES AU PLAN CLÉ. L'ANALYSE DOIT TENIR COMPTE DES CARACTÉRISTIQUES PROPRES À CHAQUE TOITURE. L'ANALYSE DOIT ÉGALEMENT TENIR COMPTE DES SURCHARGES MAXIMALES IMPOSÉES LORS DES TRAVAUX.
2. L'ENTREPRENEUR DOIT S'ASSURER DE NE PAS SURCHARGER LES TOITURES PAR L'ENTREPOSAGE DE MATÉRIAUX ET/OU ÉQUIPEMENTS DURANT LES TRAVAUX.

CE DOCUMENT NE DOIT PAS ÊTRE UTILISÉ
À DES FINS DE CONSTRUCTION

ARCHITECTURE:



MÉCANIQUE:



RÉVISIONS:

REV	DATE	DESCRIPTION	PAR
0	2026-09-04	DÉFINITIFS POUR SOUMISSION	JLB

SCEAU:



AVERTISSEMENT:
CE DESIN EST LA PROPRIÉTÉ INTELLECTUELLE DE WSP CANADA INC. AUCUNE RÉVISION, REPRODUCTION OU TOUT AUTRE USAGE N'EST PERMIS SANS L'AUTORISATION ÉCRITE DE WSP CANADA INC. L'ENTREPRENEUR DOIT VÉRIFIER TOUTES LES DIMENSIONS AUX PLANS ET FAIRE LOCALISER TOUTES LES SERVICES D'UTILITÉS PUBLIQUES ET RAPPORTER TOUTES ERREURS OU OMISSIONS AVANT DE COMMENCER LES TRAVAUX.

ÉCHELLE ORIGINALE: Comme indiqué	DATE: 2026-09-04
PRÉPARÉ PAR: JOANIE ROBILARD, ing. CHARLOTTE ALLARD, CPI NATHAN SCHMITT, ing. PRT	SI CETTE BARRE NE MESURE PAS 25 mm, AJUSTER VOTRE ÉCHELLE DE TRAÇAGE.
VÉRIFIÉ PAR: JEAN-LUC BOUFFARD, ing.	25mm
DESSINÉ PAR: GLORIA GILDA SIMIREA, tech.	

DISCIPLINE: STRUCTURE



WSP Canada Inc.
1135 Boulevard Lebourgneuf
Ville de Québec, Québec, G2K 0M5
T +1 418-623-2254 | www.wsp.com

NO PROJET: CA0062562.5541

CLIENT:



RÉF. CLIENT: R874-24 / 24-108

PROJET:

HÔPITAL DE CHANDLER
(RÉFECTION DE L'ENVELOPPE)

TITRE:

VUE EN PLAN NIVEAUX 200 &
300 - CONSTRUCTION


NUMÉRO DU FEUILLET:

S203

REV:


0

Autodesk Docs/Reflexion Enr Hôpital ChandlerCA0002562.5541_STR_P26.rvt
2026-09-04 11:17:27

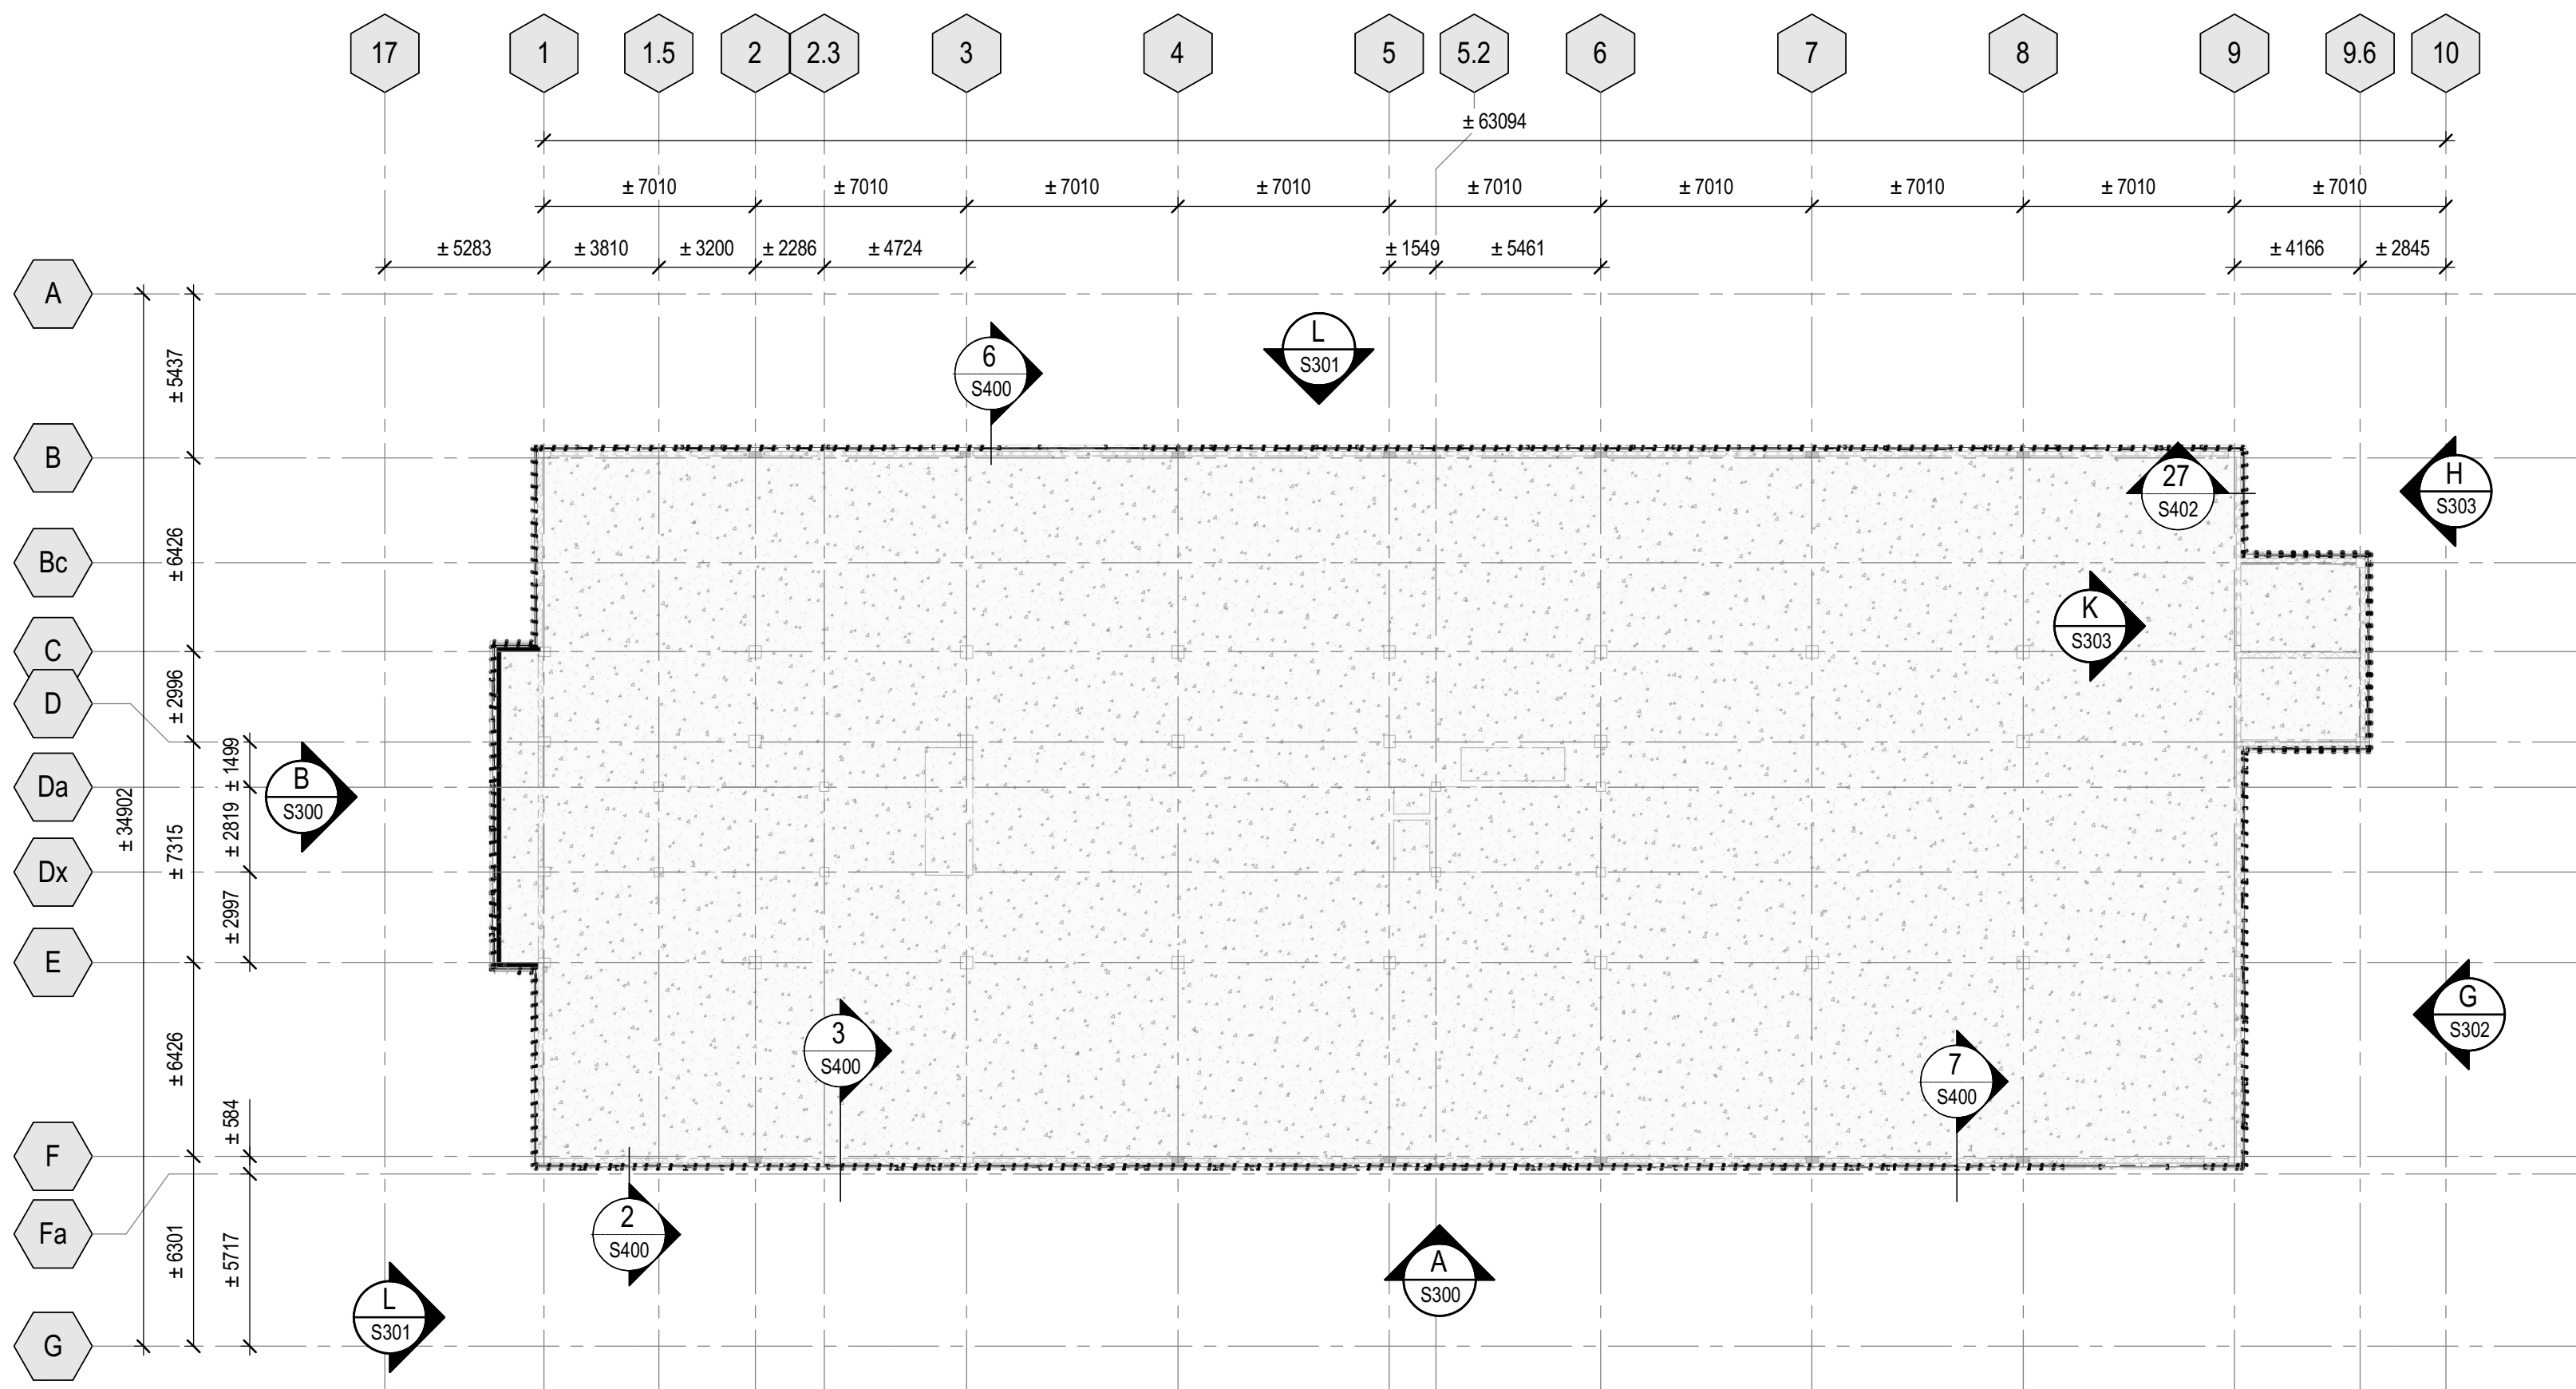

VUE EN PLAN NIVEAU 400 - CONSTRUCTION

1 : 200

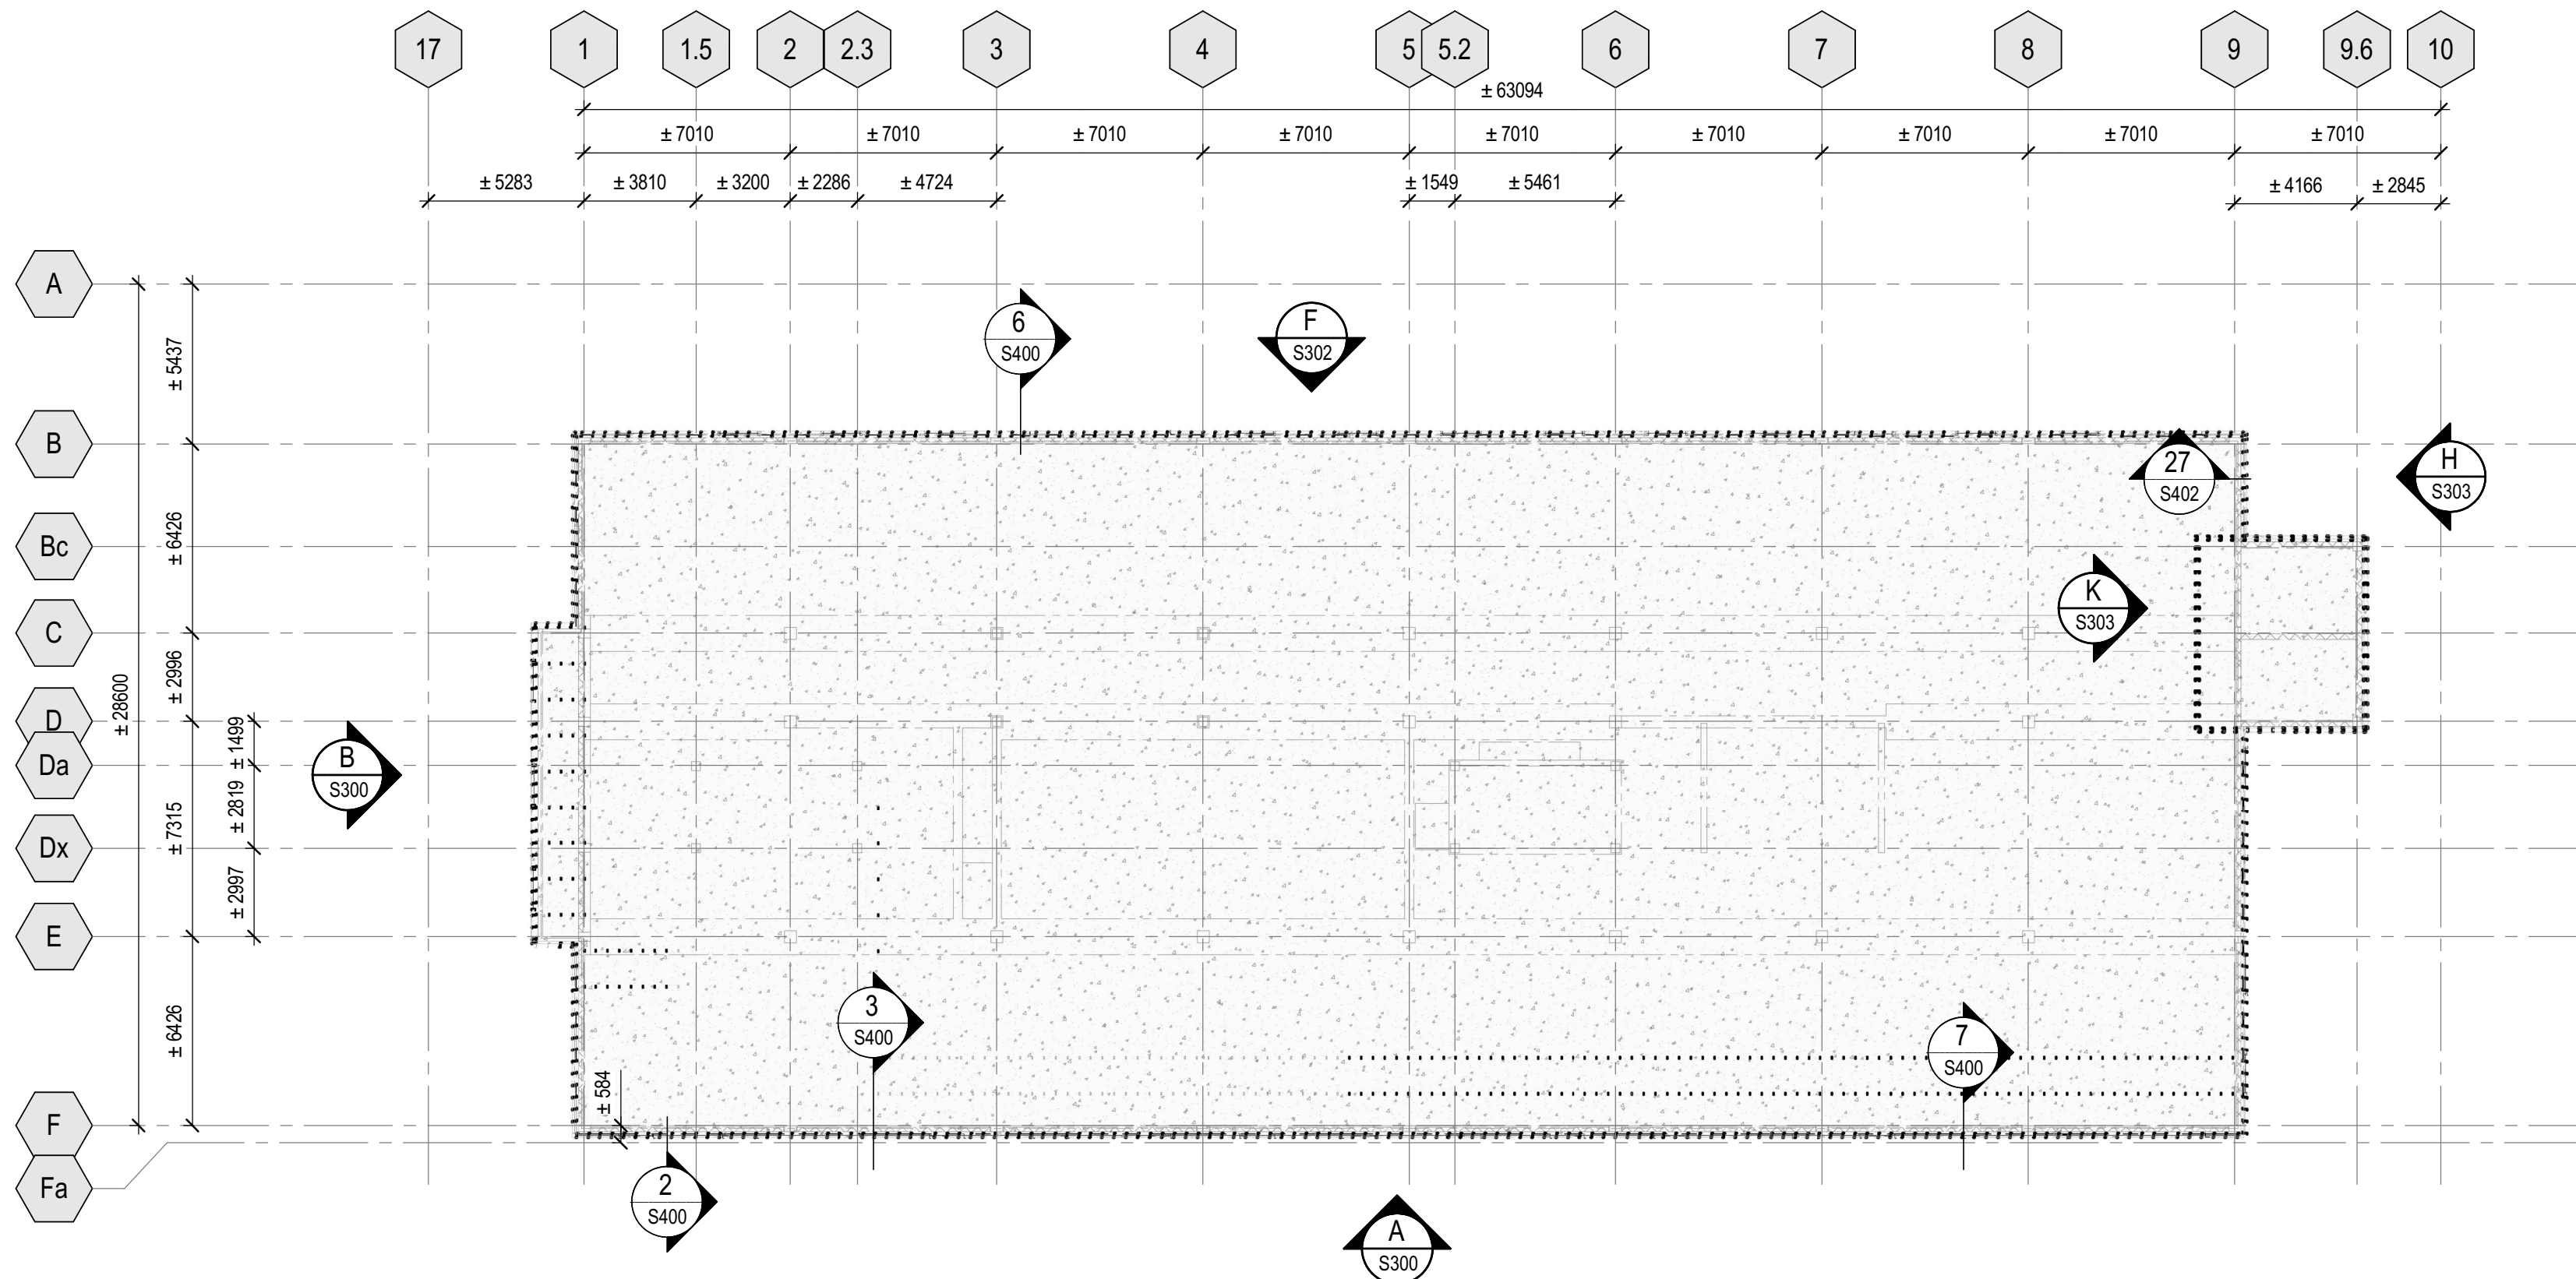

VUE EN PLAN NIVEAU 500 - CONSTRUCTION

1 : 200

NOTES IMPORTANTES:

1. L'ENTREPRENEUR DOIT FOURNIR DES PLANS, NOTES DE CALCULS ET LETTRE D'ATTESTATION SIGNÉS ET SCÉLLÉS À L'EFFET DE SON ÉCHAFFAUDAGE (PEU IMPORTE LE TYPE) RESPECTE LES CAPACITÉS DES TOITURES EN PLUS DES CHARGES DE NEIGE INDICUÉES AU PLAN CLÉ. L'ANALYSE DOIT TENIR COMPTE DES CARACTÉRISTIQUE PROPRES À CHAQUE TOITURE. L'ANALYSE DOIT ÉGALEMENT TENIR COMPTE DES SURCHARGES MAXIMALES IMPOSÉES LORS DES TRAVAUX. L'ENTREPRENEUR DOIT S'ASSURER DE NE PAS SURCHARGER LES TOITURES PAR L'ENTREPOSAGE DE MATÉRIAUX ET/OU ÉQUIPEMENTS DURANT LES TRAVAUX.

ARCHITECTURE:



MÉCANIQUE:



RÉVISIONS:

REV	DATE	DESCRIPTION	PAR
0	2026-09-04	DÉFINITIFS POUR SOUMISSION	JLB

SCEAU:



AVERTISSEMENT: CE Dessin est la propriété intellectuelle de WSP Canada Inc. Aucune réimpression, reproduction ou tout autre usage n'est permis sans l'autorisation écrite de WSP Canada Inc. L'ENTREPRENEUR DOIT VÉRIFIER TOUTES LES DIMENSIONS AUX PLANS ET FAIRE LOCALISER TOUTES LES SERVICES D'UTILITÉS PUBLIQUES ET RAPPORTER TOUTES ERREURS OU OMISSIONS AVANT DE COMMENCER LES TRAVAUX.

ECHÉLLE ORIGINALE: Comme indiqué	DATE: 2026-09-04
PRÉPARÉ PAR: JOANIE ROBILLARD, ing. CHARLOTTE ALLARD, CPI NATHAN SCHMITT, ing. PRT	SI CETTE BARRE NE MESURE PAS 25 mm, AJUSTER VOTRE ÉCHELLE DE TRAÇAGE.
VÉRIFIÉ PAR: JEAN-LUC BOUFFARD, ing.	25mm
DESSINÉ PAR: GLORIA GILDA SIMIREA, tech.	

DISCIPLINE: STRUCTURE



WSP Canada Inc.
1135 Boulevard Lebourgneuf
Ville de Québec, Québec, G2K 0M5
T +1 418-623-2254 | www.wsp.com

NO PROJET: CA0062562.5541

CLIENT:



RÉF. CLIENT: R674-24 / 24-108

PROJET:

HÔPITAL DE CHANDLER
(RÉFECTION DE L'ENVELOPPE)

TITRE:

VUE EN PLAN NIVEAUX 400 &
500 - CONSTRUCTION

NUMÉRO DU FEUILLET:

S204

REV:

0

CE DOCUMENT NE DOIT PAS ÊTRE UTILISÉ
À DES FINS DE CONSTRUCTION