



Autodesk Docs/Reflexion Env Hôpital Chandler/CA0062562.5541\_STR\_P26.rvt  
2026-09-04 11:17:26

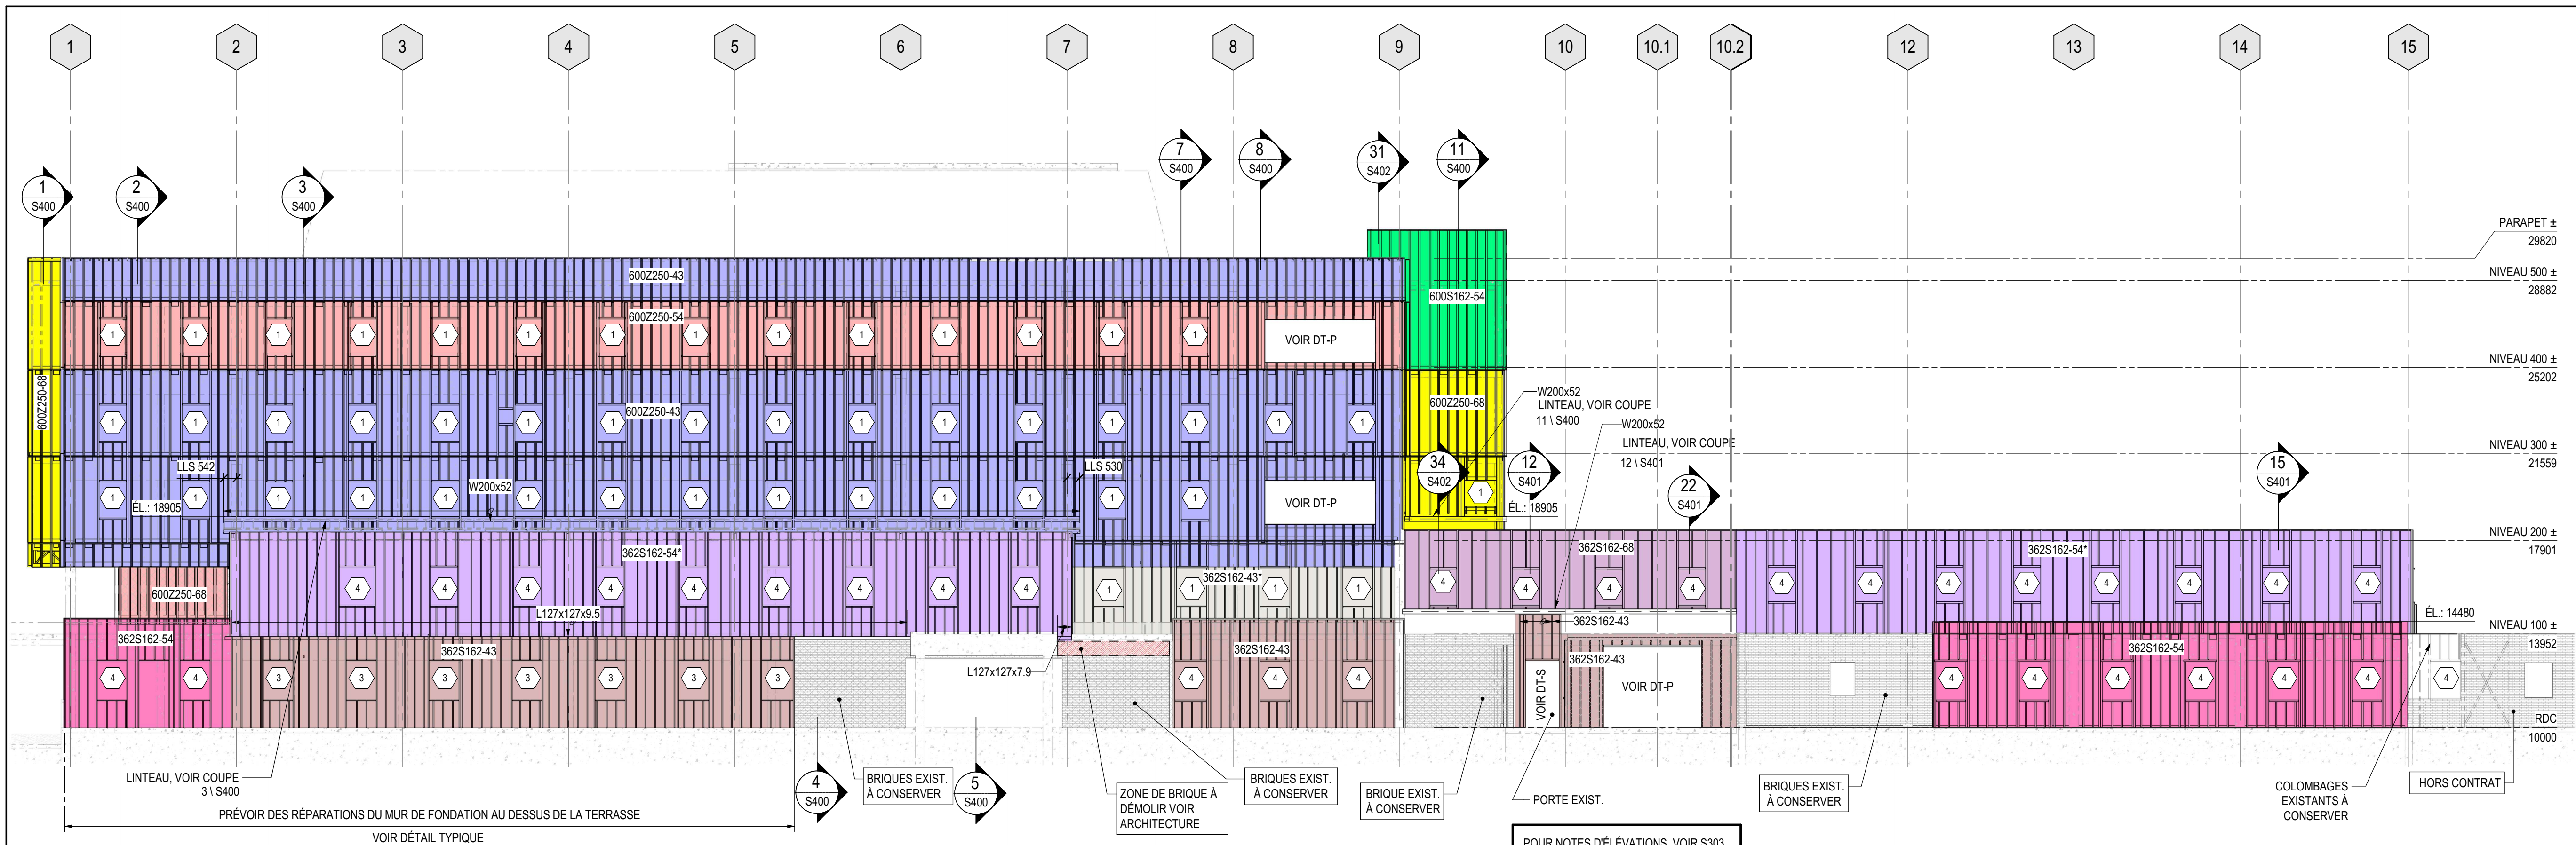

A  
S200 1:150  
ÉLEVATION SUD

- NOTES - TRAITEMENT DU MUR DE FONDATION EXISTANT :
1. PRÉVOIR RETIRER TOUS LES DÉBRIS, MORTIER, ASPÉRITÉS ET PRÉSENCE INDÉSIRABLE AU DESSUS DU MUR DE FONDATION.
  2. EFFECTUER LA PRÉPARATION DE SURFACE DU MUR DE FONDATION AFIN D'OBTENIR UNE RUGOSITÉ DE TYPE CSP-05.
  3. PRÉVOIR L'APPLICATION D'UN MORTIER DE RÉPARATION AFIN D'OBTENIR UN MUR DE FONDATION DE NIVEAU, ALIGÉE ET UNIFORME.
  4. AUX ENDROITS REQUIS, PRÉVOIR LA RÉPARATION DU MUR DE FONDATION SELON LE DÉTAIL TYPE SUR FEUILLE S102 (PRÉVOIR UN TOTAL DE 17 INTERVENTIONS POUR UN TOTAL DE 1,6 M2 DE SURFACE).
  5. LE TRAITEMENT DU MUR DE FONDATION EST APPLICABLE SUR LA FAÇADE SUD ET NORD.

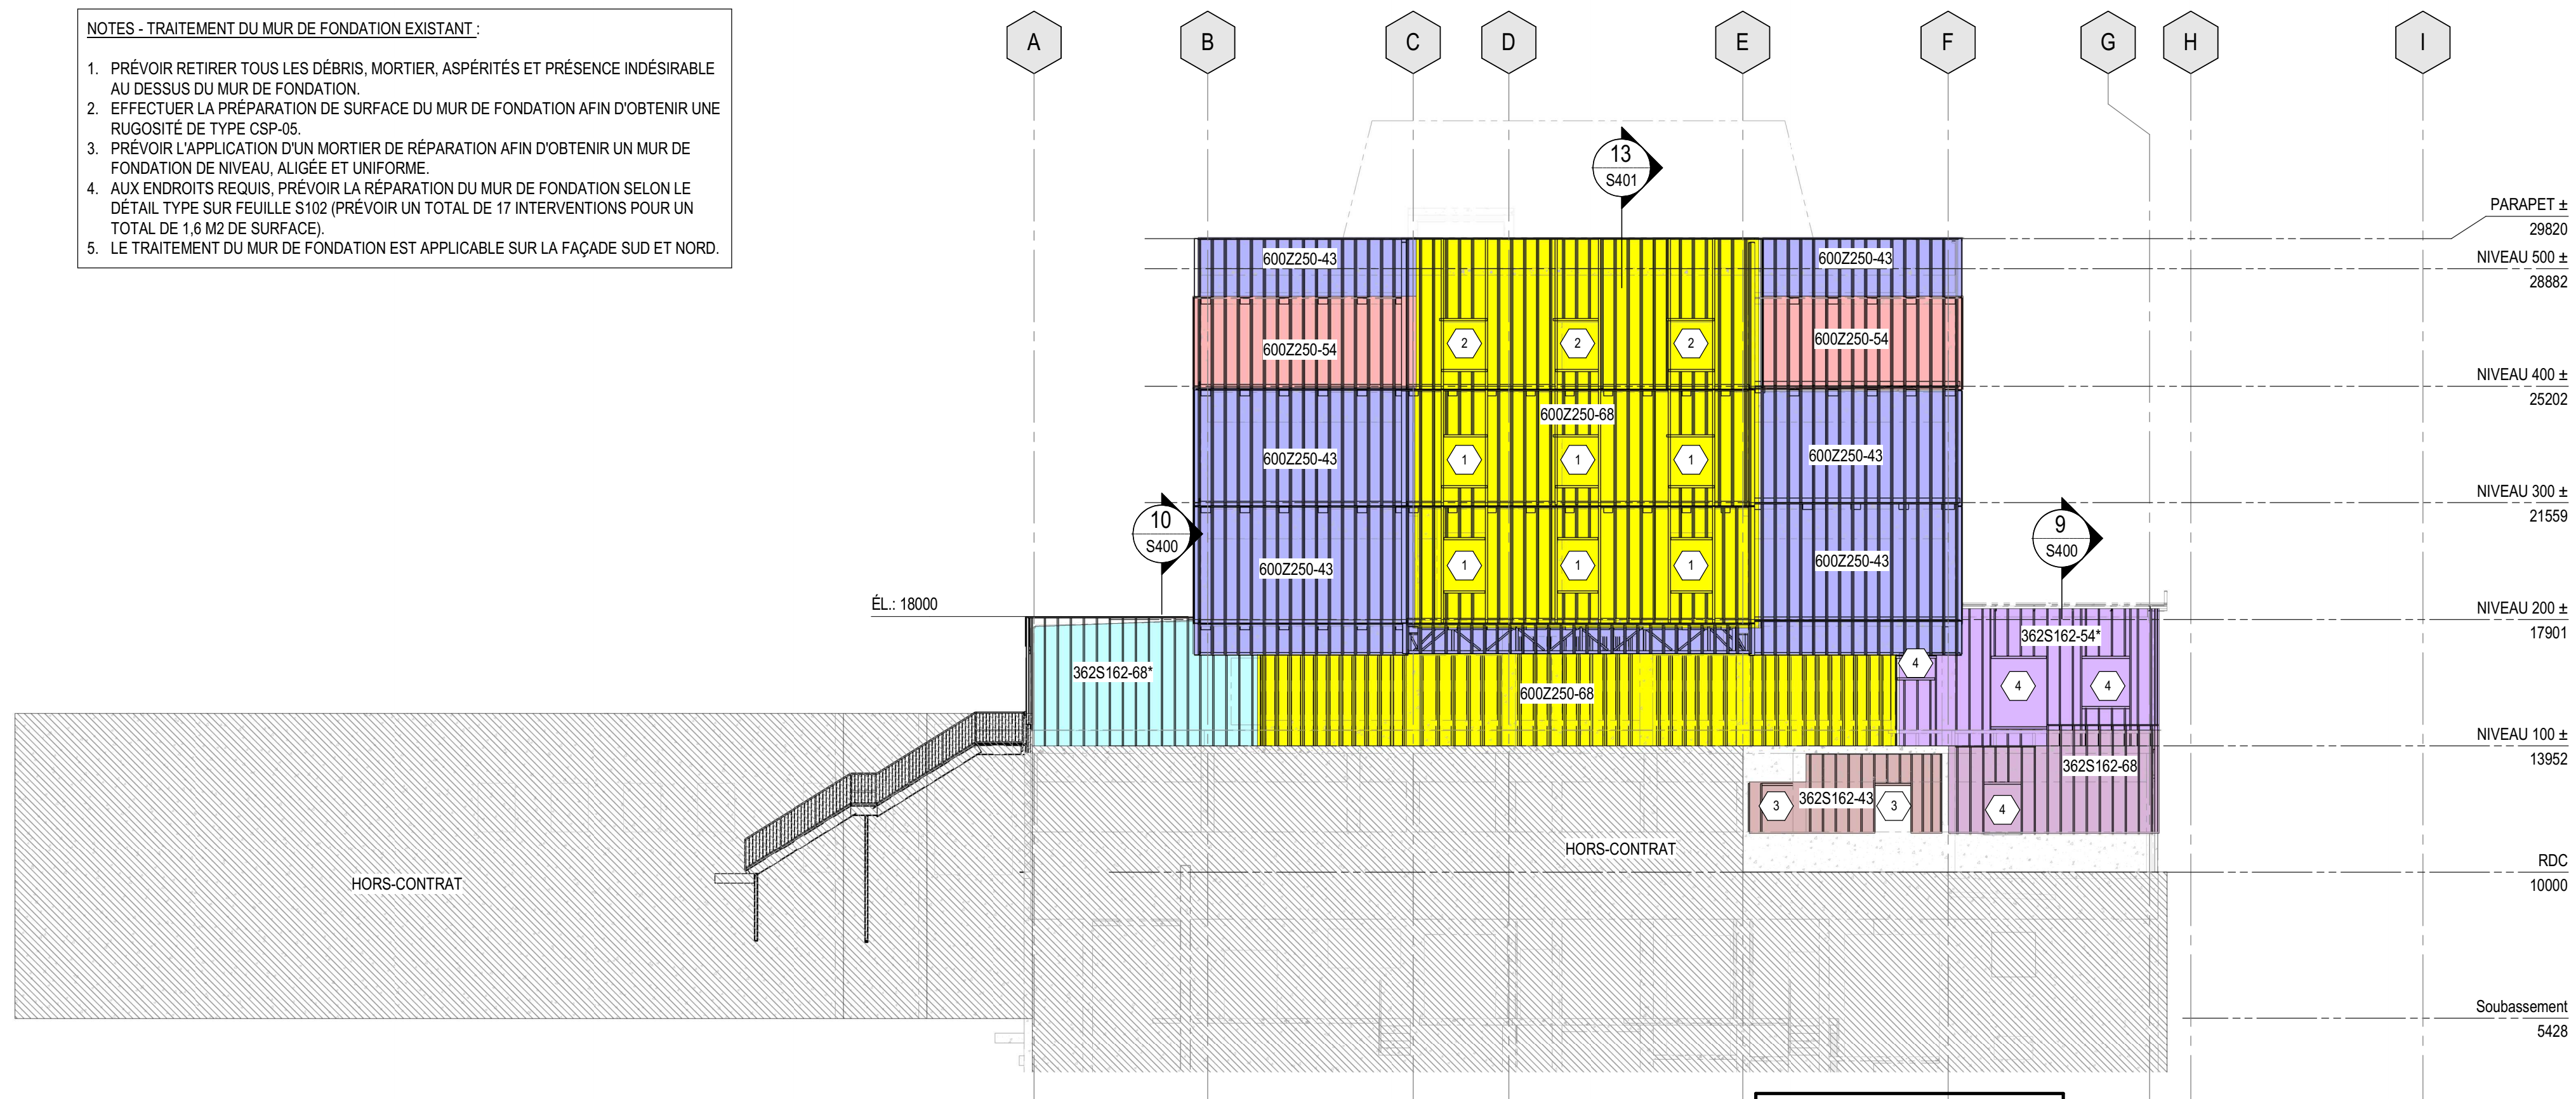

B  
S200 1:150  
ÉLEVATION OUEST

LÉGENDE DE LA  
STRUCTURE D'ACIER

- 600Z250-43 @ 400 c/c
- 600Z250-54 @ 400 c/c
- 600Z250-68 @ 400 c/c
- 362S162-43 @ 400 c/c
- 362S162-43\* @ 400 c/c
- 362S162-54 @ 400 c/c
- 362S162-54\* @ 400 c/c
- 600S162-54 @ 400 c/c
- 362S162-68 @ 400 c/c
- 362S162-68\* @ 600 c/c

- \* = EN RENFORT AUX COLOMBAGES EXISTANTS
- (X) = OUVERTURE TYPE, VOIR DÉTAIL DT-F \ S100 POUR DIMENSIONS BRUTES VOIR ARCHITECTURE
- LLS = LIMITE LINTEAU STRUCTURAL, À COORDONNER AVEC ARCHITECTURE

CE DOCUMENT NE DOIT PAS ÊTRE UTILISÉ  
À DES FINS DE CONSTRUCTION

ARCHITECTURE:



MÉCANIQUE:



RÉVISIONS:

| REV | DATE       | DESCRIPTION                | PAR |
|-----|------------|----------------------------|-----|
| 0   | 2026-09-04 | DÉFINITIFS POUR SOUMISSION | JLB |

SCEAU:



AVERTISSEMENT: CE Dessin EST LA PROPRIÉTÉ INTELLECTUELLE DE WSP CANADA INC. AUCUNE RÉVISION, REPRODUCTION OU TOUT AUTRE USAGE N'EST PERMIS SANS L'AUTORISATION ÉCRITE DE WSP CANADA INC. L'ENTREPRENEUR DOIT VÉRIFIER TOUTES LES DIMENSIONS AUX PLANS ET FAIRE LOCALISER TOUTES LES SERVICES D'UTILITÉS PUBLIQUES ET RAPPORTER TOUTES ERREURS OU OMISSIONS AVANT DE COMMENCER LES TRAVAUX.

ÉCHELLE ORIGINALE: Comme indiqué  
PRÉPARÉ PAR: JOANIE ROBILLARD, ing.  
CHARLOTTE ALLARD, CPI  
NATHAN SCHMITT, ing. PRT  
VÉRIFIÉ PAR: JEAN-LUC BOUFFARD, ing.  
Dessiné PAR: GLORIA GILDA SIMIREA, tech.  
DATE: 2026-09-04  
SI CETTE BARRE NE MESURE PAS 25 mm, AJUSTER VOTRE ÉCHELLE DE TRAÇAGE.  
25mm

DISCIPLINE: STRUCTURE



WSP Canada Inc.  
1135 Boulevard Lebourgneuf  
Ville de Québec, Québec, G2K 0M5  
T +1 418-623-2254 | www.wsp.com

NO PROJET: CA0062562.5541

CLIENT:



# RÉF. CLIENT: R674-24 / 24-108

PROJET:

HÔPITAL DE CHANDLER  
(RÉFECTION DE L'ENVELOPPE)

TITRE:


ÉLÉVATIONS -  
CONSTRUCTION

NUMÉRO DU FEUILLET:


S300

REV:


0

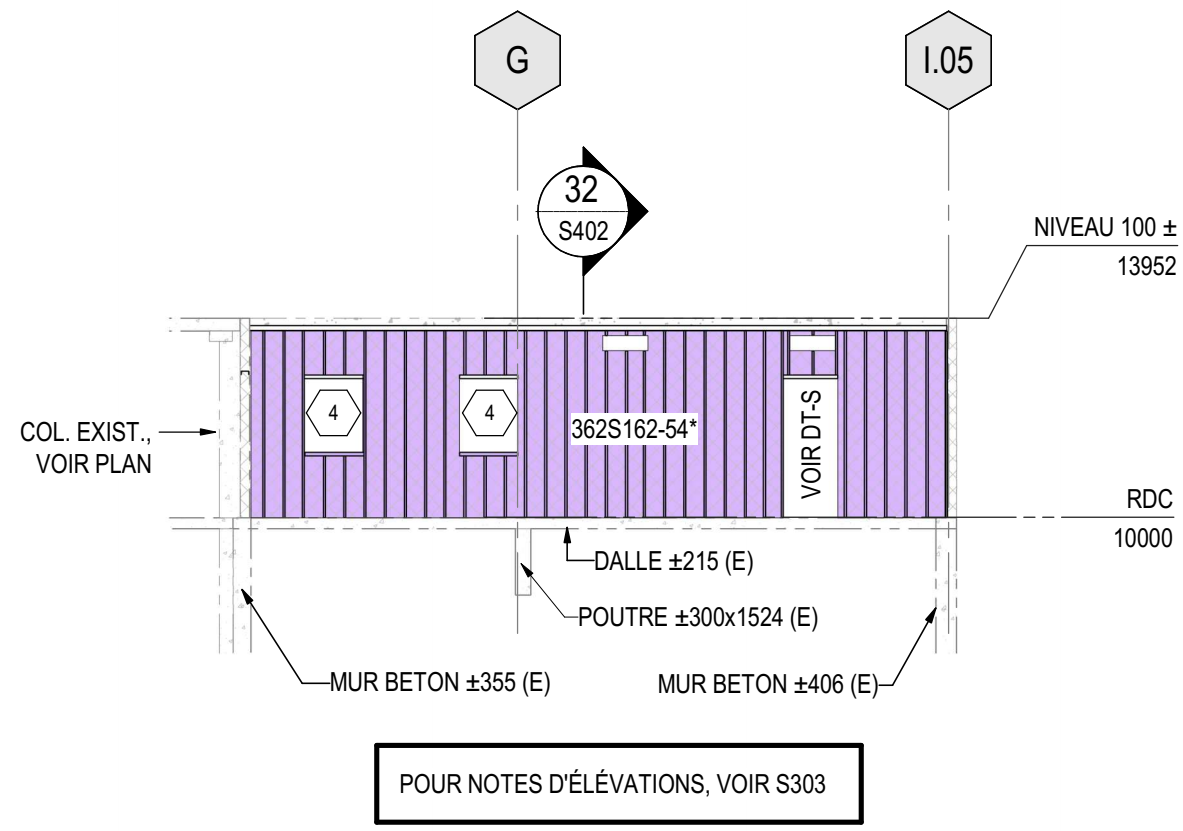

C ÉLEVATION OUEST PARTIELLE  
S200 1:150

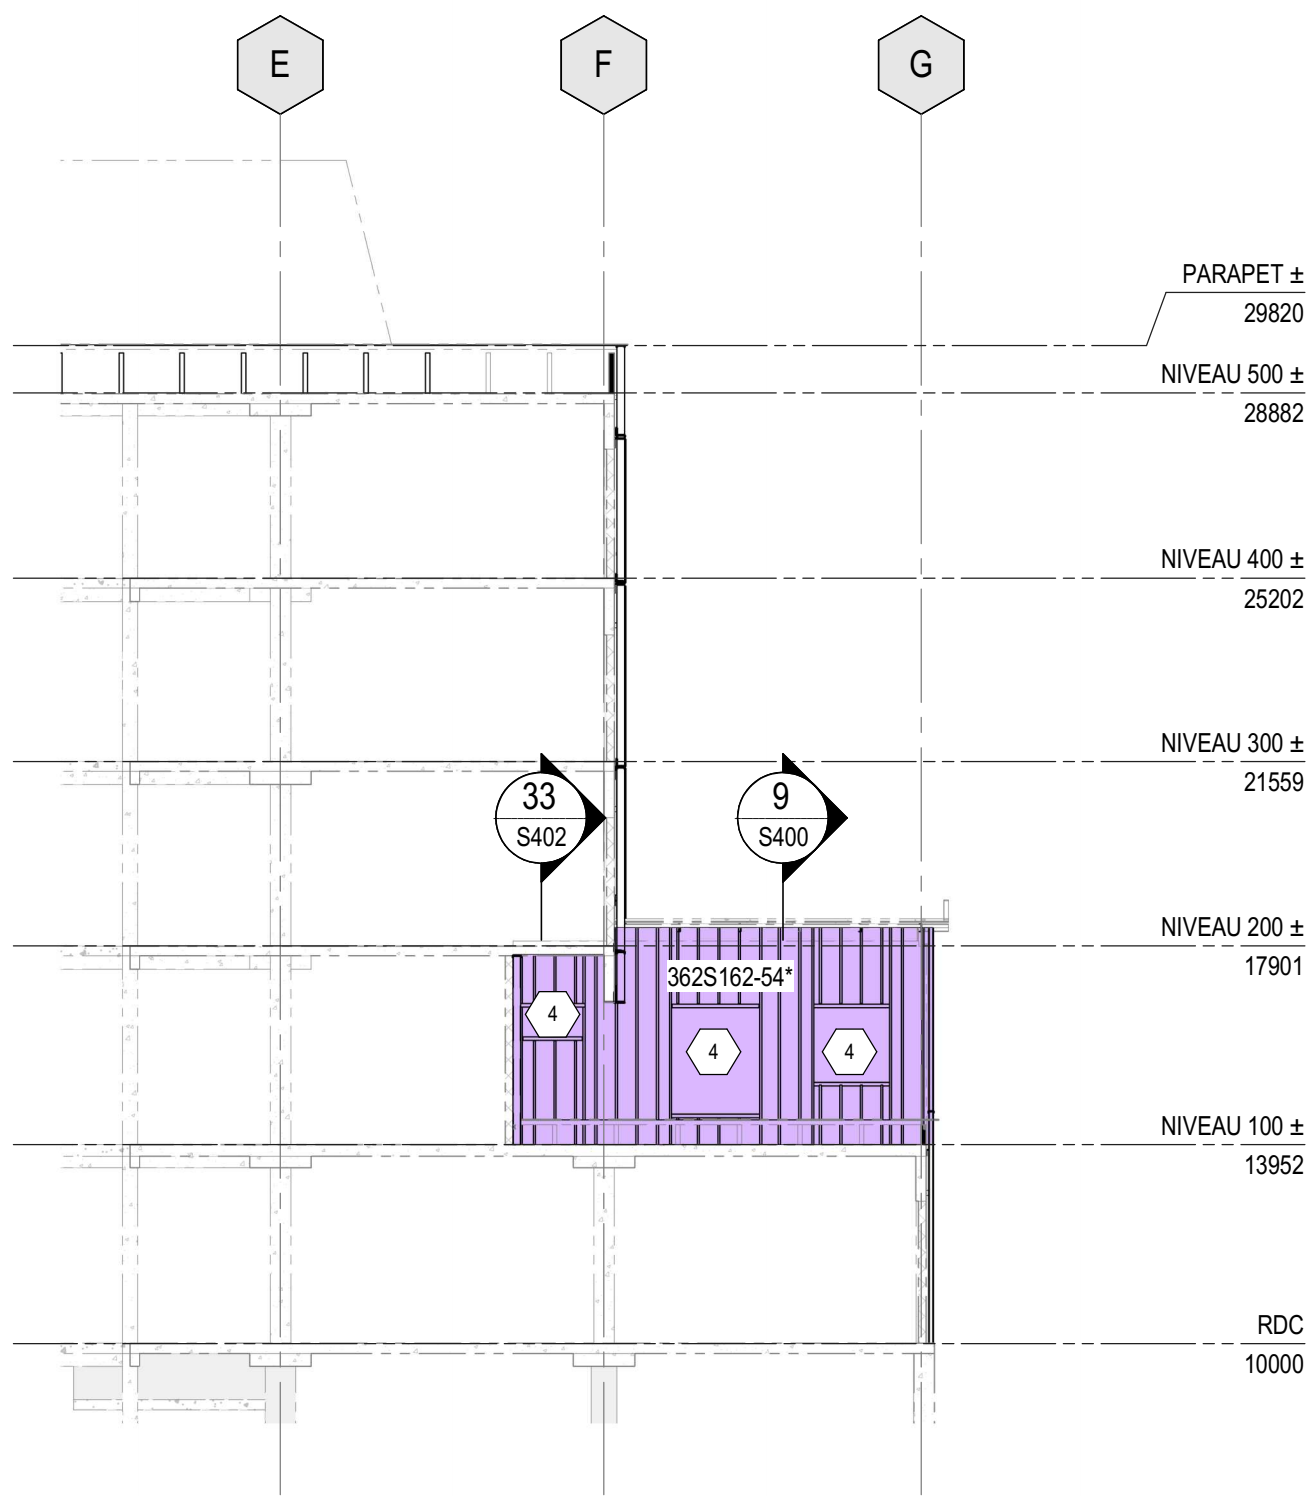

E ÉLEVATION OUEST PARTIELLE  
S200 1:150

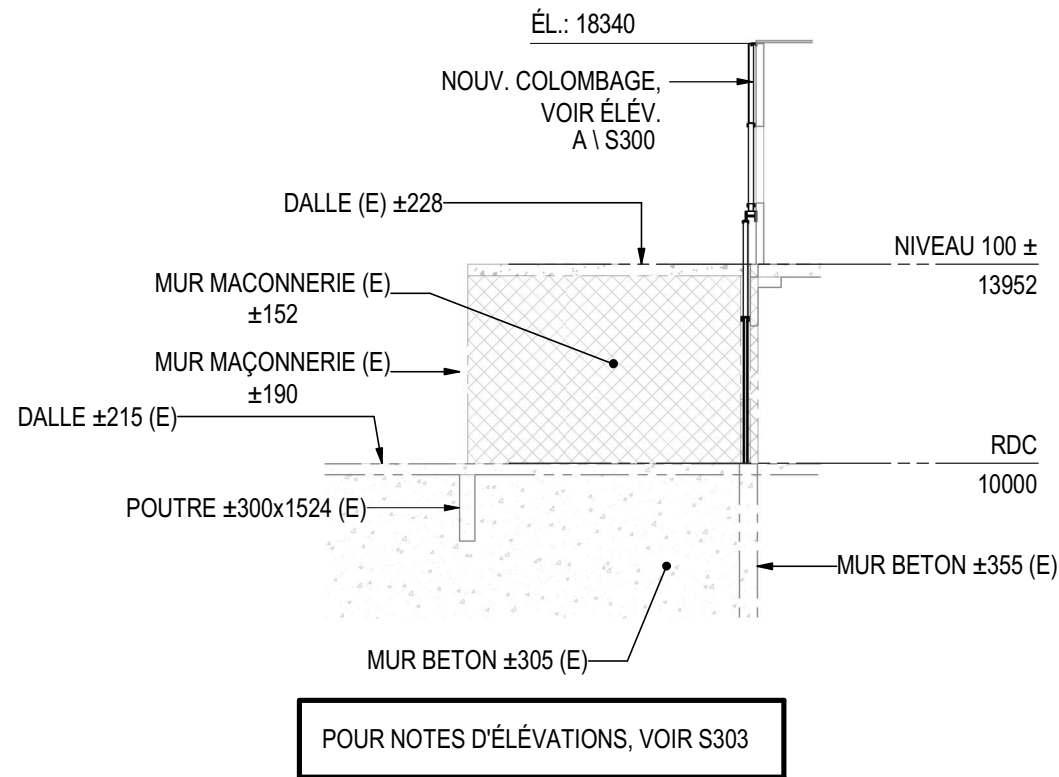

D ÉLEVATION EST PARTIELLE  
S200 1:150



L ÉLEVATION OUEST PARTIELLE - EST  
S200 1:150

#### LÉGENDE DE LA STRUCTURE D'ACIER

|             |           |
|-------------|-----------|
| 600Z250-43  | @ 400 c/c |
| 600Z250-54  | @ 400 c/c |
| 600Z250-68  | @ 400 c/c |
| 362S162-43  | @ 400 c/c |
| 362S162-43* | @ 400 c/c |
| 362S162-54  | @ 400 c/c |
| 362S162-54* | @ 400 c/c |
| 600S162-54  | @ 400 c/c |
| 362S162-68  | @ 400 c/c |
| 362S162-68* | @ 600 c/c |

\* = EN RENFORT AUX  
COLOMBAGES EXISTANTS

(X) = OUVERTURE TYPE, VOIR  
DÉTAIL DT-F \ S100  
POUR DIMENSIONS BRUTES  
VOIR ARCHITECTURE

LLS = LIMITE LINTEAU STRUCTURAL,  
À COORDONNER AVEC  
ARCHITECTURE

ARCHITECTURE:



MÉCANIQUE:



RÉVISIONS:

| REV | DATE       | DESCRIPTION                | PAR |
|-----|------------|----------------------------|-----|
| 0   | 2026-09-04 | DÉFINITIFS POUR SOUMISSION | JLB |

SCEAU:



AVERTISSEMENT:  
CE Dessin EST LA PROPRIÉTÉ INTELLECTUELLE DE WSP CANADA INC. AUCUNE RÉVISION,  
REPRODUCTION OU TOUT AUTRE USAGE N'EST PERMIS SANS L'AUTORISATION ÉCRITE DE WSP CANADA  
INC. L'ENTREPRENEUR DOIT VÉRIFIER TOUTES LES DIMENSIONS AUX PLANS ET FAIRE LOCALISER TOUTES  
LES SERVICES D'UTILITÉS PUBLIQUES ET RAPPORTER TOUTES ERREURS OU OMISSIONS AVANT DE  
COMMENCER LES TRAVAUX.

|                                                                                             |                                                                                 |
|---------------------------------------------------------------------------------------------|---------------------------------------------------------------------------------|
| ÉCHELLE ORIGINALE:<br>1 : 150                                                               | DATE:<br>2026-09-04                                                             |
| PRÉPARÉ PAR:<br>JOANIE ROBILLARD, ing.<br>CHARLOTTE ALLARD, CPI<br>NATHAN SCHMITT, ing. PRT | SI CETTE BARRE NE<br>MESURE PAS 25 mm,<br>AJUSTER VOTRE ÉCHELLE<br>DE TRACÉAGE. |
| VÉRIFIÉ PAR:<br>JEAN-LUC BOUFFARD, ing.                                                     | 25mm                                                                            |
| DESSINÉ PAR:<br>GLORIA GILDA SIMIREA, tech.                                                 |                                                                                 |

DISCIPLINE: STRUCTURE



WSP Canada Inc.  
1135 Boulevard Lebourgneuf  
Ville de Québec, Québec, G2K 0M5  
T +1 418-623-2254 | www.wsp.com

NO PROJET: CA0062562.5541

CLIENT:



# RÉF. CLIENT: R874-24 / 24-108

PROJET:

HÔPITAL DE CHANDLER  
(RÉFECTION DE L'ENVELOPPE)

TITRE:

ÉLEVATIONS -  
CONSTRUCTION

NUMÉRO DU FEUILLET:



S301

REV:

0

CE DOCUMENT NE DOIT PAS ÊTRE UTILISÉ  
À DES FINS DE CONSTRUCTION



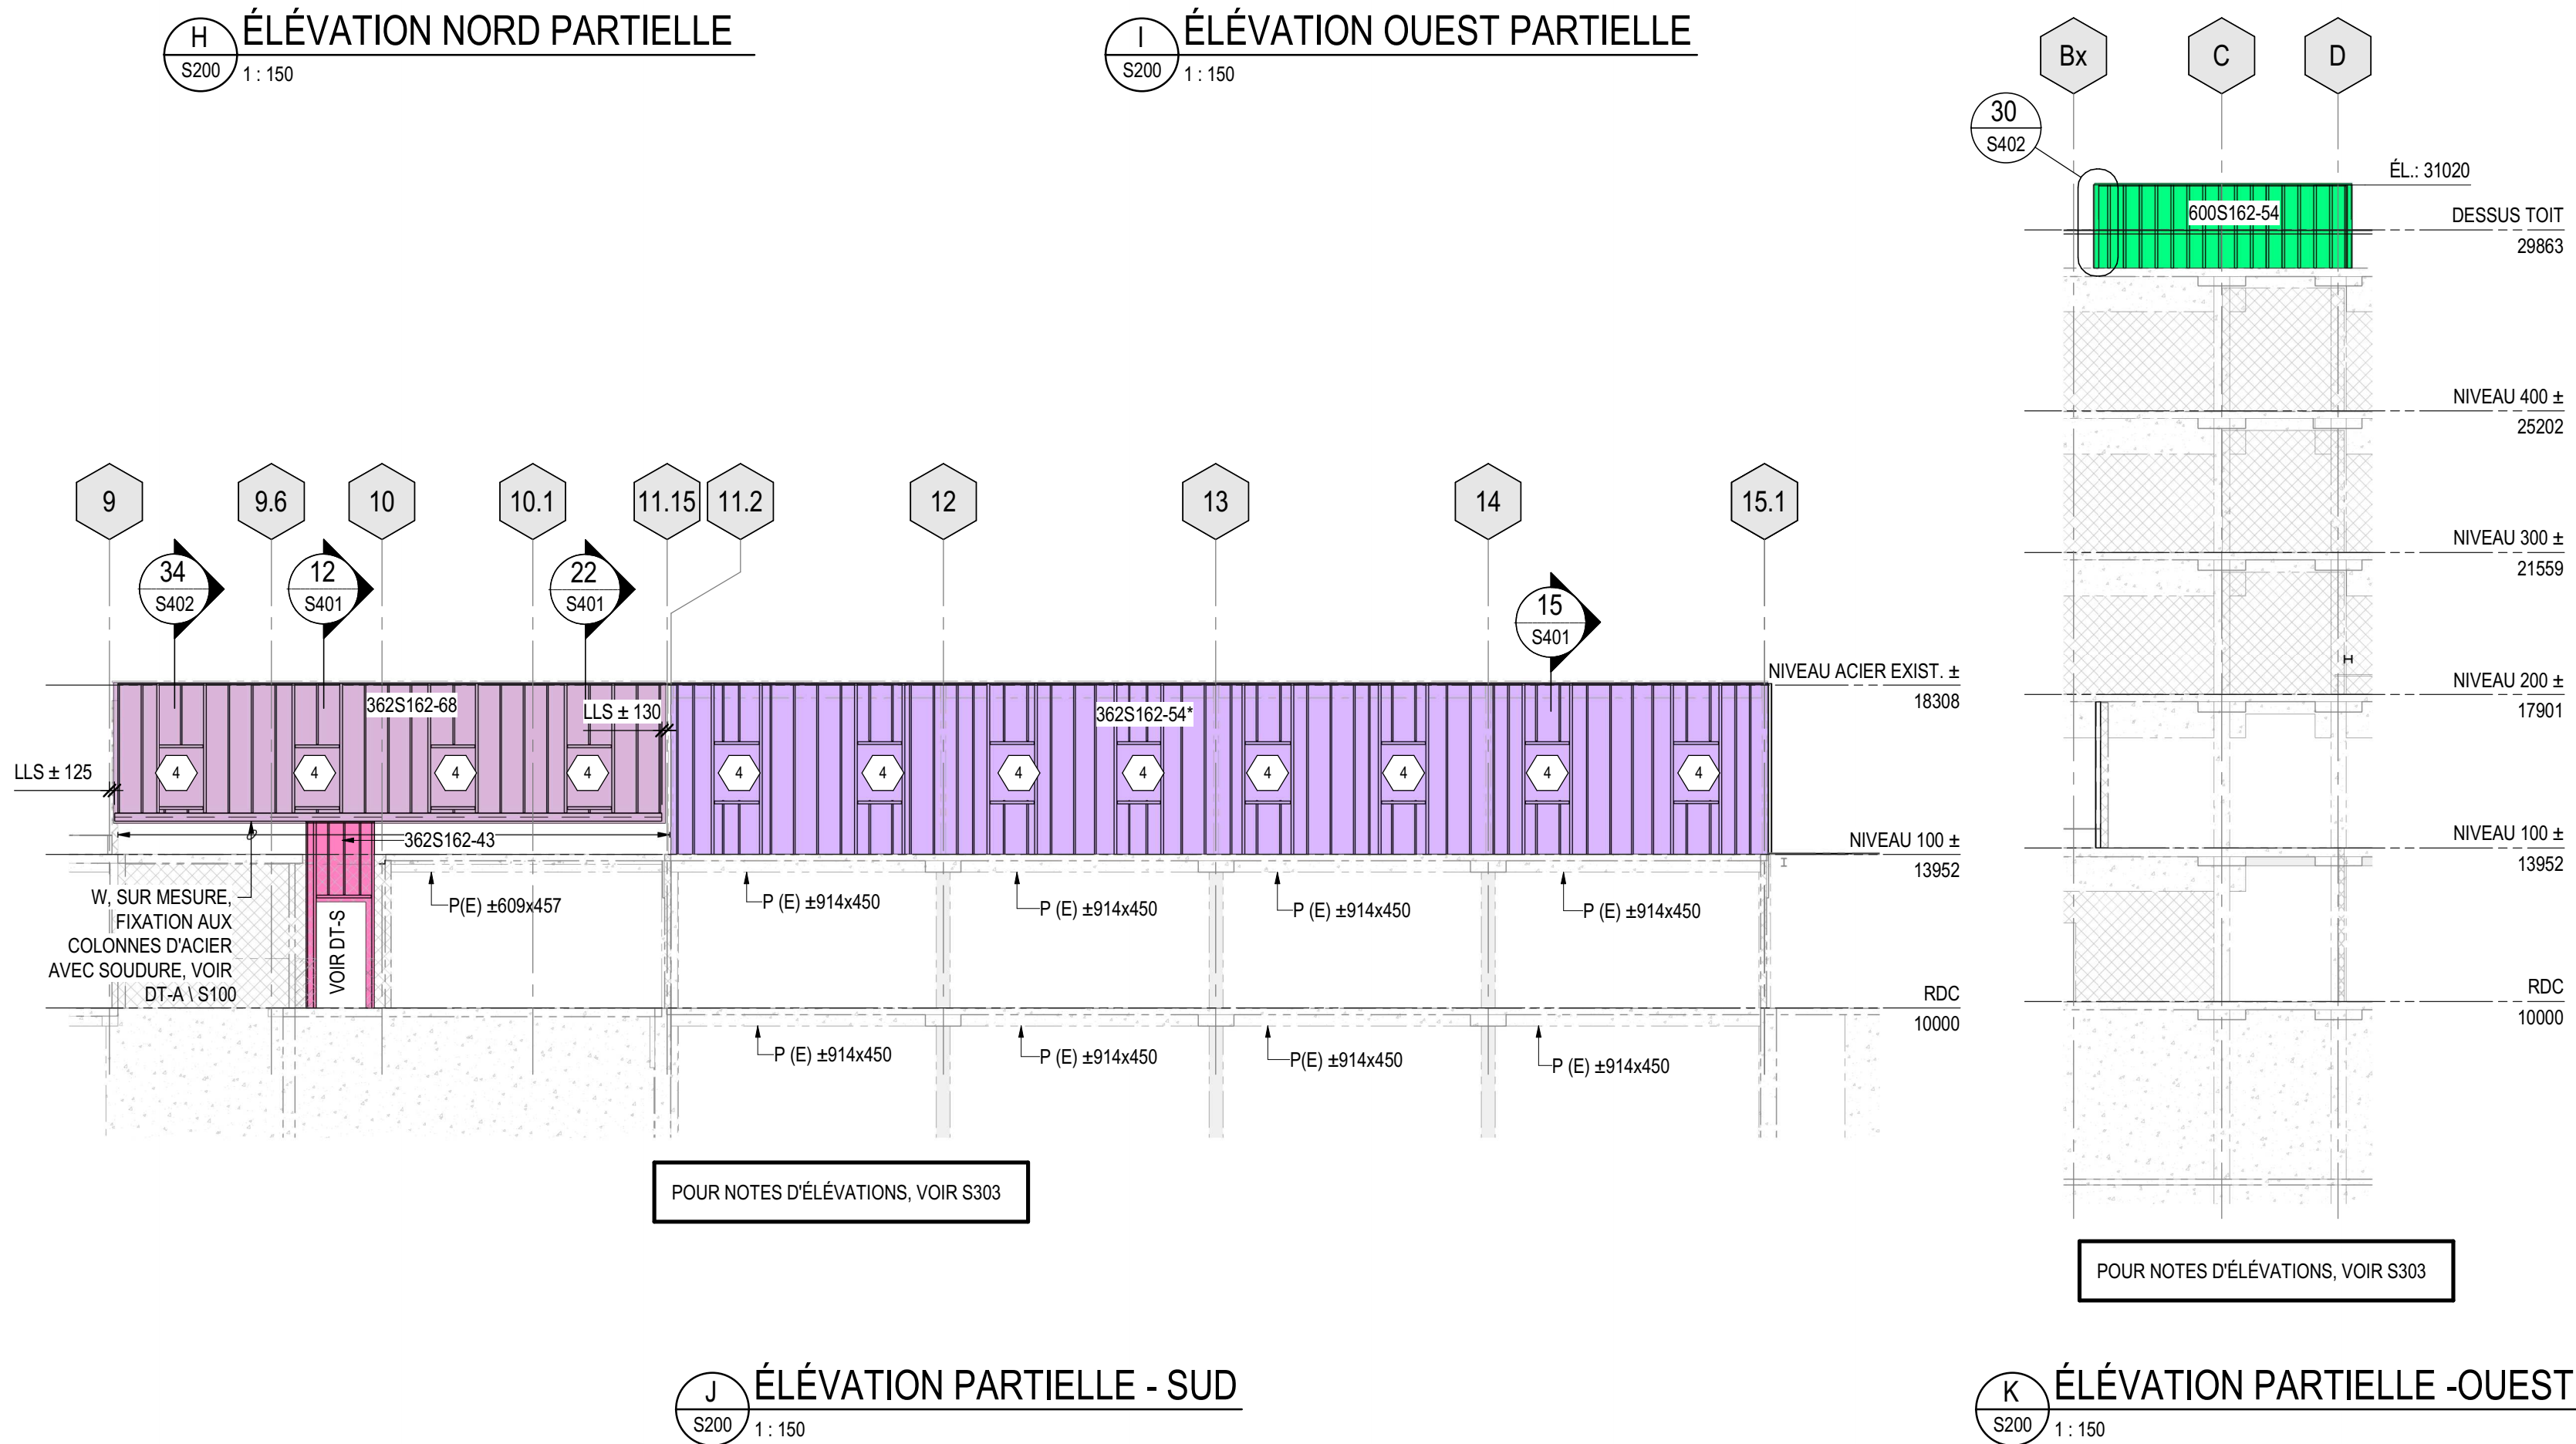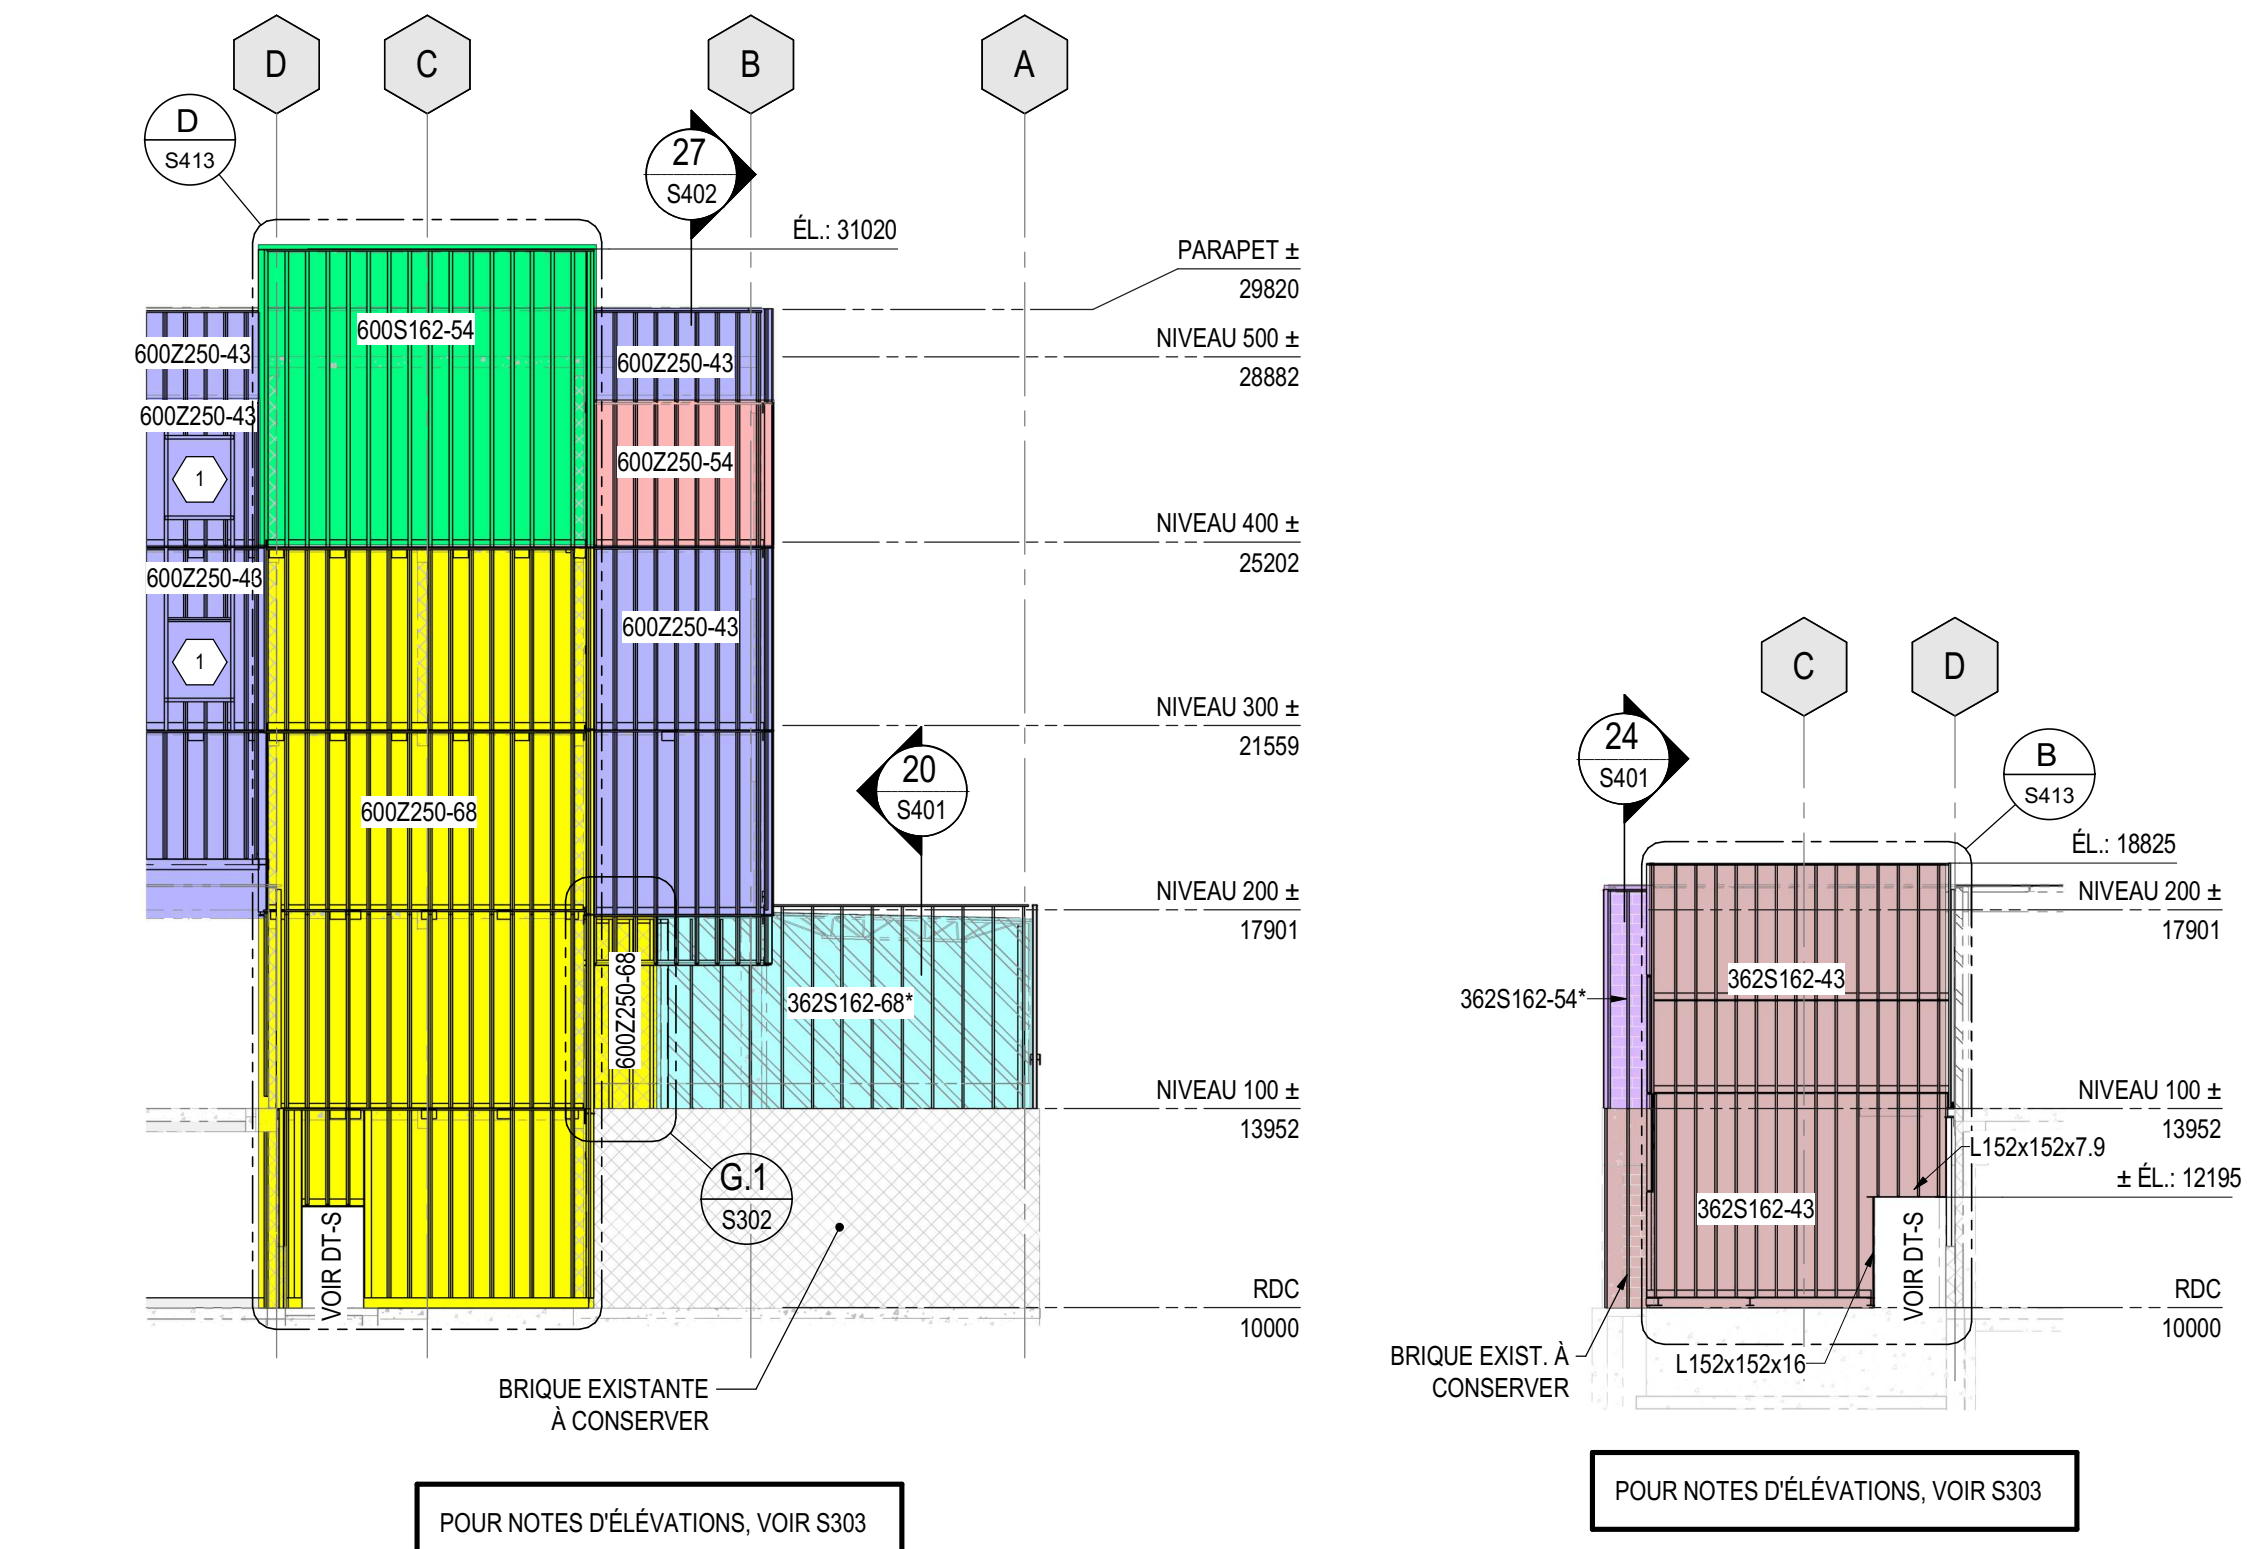

#### LÉGENDE DE LA STRUCTURE D'ACIER

- 600Z250-43 @ 400 c/c
- 600Z250-54 @ 400 c/c
- 600Z250-68 @ 400 c/c
- 362S162-43 @ 400 c/c
- 362S162-43\* @ 400 c/c
- 362S162-54 @ 400 c/c
- 362S162-54\* @ 400 c/c
- 600S162-54 @ 400 c/c
- 362S162-68 @ 400 c/c
- 362S162-68\* @ 600 c/c

\* = EN RENFORT AUX COLOMBAGES EXISTANTS

(X) = OUVERTURE TYPE, VOIR DÉTAIL DT-F \ S100 POUR DIMENSIONS BRUTES VOIR ARCHITECTURE

LLS = LIMITE LINÉAIRE STRUCTURALE, À COORDONNER AVEC ARCHITECTURE

#### NOTES D'ÉLÉVATION IMPORTANTES :

- L'ENTREPRENEUR DOIT PRÉVOIR DES ANCRAGES TEMPORAIRES AU NIVEAU DES DALLES POUR VENIR SUPPORTER SON ÉCHAFAUDAGE OU FOURNIR DES PLANS, NOTES DE CALCULS ET LETTRE D'ATTESTATION SIGNÉS ET SCELLÉS À L'EFFET QUE SON ÉCHAFAUDAGE (PEU IMPORTE LE TYPE) RESPECTE LES CAPACITÉS DES TOITURES EN PLUS DE LA CHARGE DE NEIGE ( $S_s = 3,8 \text{ kPa}$  ;  $S_f = 0,6 \text{ kPa}$  ;  $I_s \text{ (ULS)} = 1,25$  ; CHARGE DE NEIGE MINIMUM NON PONDERÉE  $= 3,64 \text{ kPa} \times I_s$ ). L'ANALYSE DOIT TENIR COMPTE DES CARACTÉRISTIQUES PROPRES À CHAQUE TOITURE. L'ANALYSE DOIT ÉGALEMENT TENIR COMPTE DES SURCHARGES MAXIMALES IMPOSÉES LORS DES TRAVAUX.
- L'ENTREPRENEUR DOIT S'ASSURER DE NE PAS SURCHARGER LES TOITURES PAR L'ENTREPOSAGE DE MATÉRIEL ET D'ÉQUIPEMENT DURANT LES TRAVAUX. AUCUNE CHARGE PONCTUELLE NE DOIT ÊTRE DÉPOSÉE SUR LES TOITURES VENTILÉES.
- TOUT L'ACIER DE CHARPENTE DU PROJET, INCLUANT LES PLAQUES, LES ANCRAGES ET LES CORNIÈRES, DOIT ÊTRE GALVANISÉ À CHAUD.
- AVANT LA FABRICATION, L'ENTREPRENEUR DOIT VALIDER TOUTES LES DIMENSIONS DES ÉLÉMENTS STRUCTURAUX AU CHANTIER. LES VARIATIONS DES DIMENSIONS DES ÉLÉMENTS STRUCTURAUX POUR S'ADAPTER AUX CONDITIONS EXISTANTES DOIT ÊTRE INCLUS À LA SOUMISSION.
- PRÉVOIR DES TROUS DE PRÉPERÇAGE DE 3mm Ø OU SCANNER TOUS LES ÉLÉMENTS EN BÉTON POUR LA LOCALISATION DE L'ARMATURE AVANT L'INSTALLATION DE LA CHARPENTE EN ACIER. DANS LE CAS DE CONFLIT ENTRE LES PERCEMENTS ET L'ARMATURE, PRÉVOIR DÉPLACER LES ANCRAGES ET AJUSTER LES PLAQUES D'ASSEMBLAGE. LA VÉRIFICATION DES CONFLITS POTENTIELS AVEC L'ARMATURE DOIT ÊTRE VALIDER AVANT LA FABRICATION DES ÉLÉMENTS EN ACIER.
- PRÉVOIR L'ENSEMBLE DES CALES EN ACIER GALVANISÉ ENTRE LA CHARPENTE EN BÉTON ET LES ÉLÉMENTS D'ANCRAGE DE LA CHARPENTE EN ACIER. PRÉVOIR METTRE EN PLACE UN COULIS SANS RETRAIT DERRIÈRE TOUS LES ÉLÉMENTS D'ANCRAGE.
- TOUTES LES CÔTES SONT EXPRIMÉES EN ± ET DOIVENT ÊTRE COORDONNÉES AVEC LES PLANS D'ARCHITECTURE.
- SUIVANT LES TRAVAUX DE DÉMOLITION (VOIR PLANS D'ARCHITECTURE) ET AVANT LA FABRICATION DE LA CHARPENTE D'ACIER, DES COLOMBAGES ET DES BARRES EN Z PRÉVOIR LE RELEVÉ COMPLET DES FAÇADES, COORDONNER L'ALIGNEMENT FINAL DE LA NOUVELLE ENVELOPPE AVEC L'ARCHITECTE ET INFORMER L'INGÉNIEUR DES AJUSTEMENTS REQUIS AUX TRAVAUX DE STRUCTURE (SI REQUIS).

#### NOUVEAU MUR EN BARRES EN Z

- BARRE EN Z :
  - 600Z250-43 (CALIBRE 18) @ 400 mm c/c OU
  - 600Z250-54 (CALIBRE 16) @ 400 mm c/c OU
  - 600Z250-68 (CALIBRE 14) @ 400 mm c/c, SELON INDICATIONS AUX ÉLÉVATIONS
- ENTREMISE : FEUILLARD MÉTALLIQUE CS DE SIMPSON STRONG TIE @ 800 mm c/c DE CALIBRE IDENTIQUE AUX BARRES EN Z FIXÉ SUR L'AILE INTÉRIEURE DES BARRES EN Z À L'AIDE DE 1 VIS #10 ET AUX BLOCAGES À L'AIDE DE 2 VIS #10, VOIR DT-O
- SABLIÈRE : LISSE MULTIFENTE 362MST250 DE CALIBRE IDENTIQUE AUX BARRES EN Z

#### NOUVEAU MUR EN COLOMBAGES MÉTALLIQUES

- COLOMBAGE :
  - 362S162-43 (CALIBRE 18) @ 400 mm c/c OU
  - 362S162-54 (CALIBRE 16) @ 400 mm c/c OU
  - 362S162-68 (CALIBRE 14) @ 400 mm c/c OU
  - 600S162-54 (CALIBRE 16) @ 400 mm c/c, SELON INDICATIONS AUX ÉLÉVATIONS
- ENTREMISE : 150U50-54 (CALIBRE 16) @ 1200 mm c/c FIXÉE À CHAQUE COLOMBAGE À L'AIDE DE CONNECTEURS LSUBH 3,25 DE SIMPSON STRONG TIE LORSQUE LES COLOMBAGES SONT DE CALIBRE 18 ET 16 OU MUSBH 3,25 DE SIMPSON STRONG TIE LORSQUE LES COLOMBAGES SONT DE CALIBRE 14, UTILISER 2 VIS #10
- SABLIÈRE : LISSE MULTIFENTE 362MST250 OU 600MST250 DE CALIBRE IDENTIQUE AUX COLOMBAGES

#### NOUVEAU MUR EN COLOMBAGES MÉTALLIQUES EN RENFORT AUX COLOMBAGES EXISTANTS

- COLOMBAGE :
  - 362S162-43 (CALIBRE 18) @ 400 mm c/c OU
  - 362S162-54 (CALIBRE 16) @ 400 mm c/c OU
  - 362S162-68 (CALIBRE 14) @ 600 mm c/c, SELON INDICATIONS AUX ÉLÉVATIONS
- ENTREMISE : 150U50-54 (CALIBRE 16) @ 1200 mm c/c FIXÉE À CHAQUE COLOMBAGE À L'AIDE DE CONNECTEURS LSUBH 3,25 DE SIMPSON STRONG TIE LORSQUE LES COLOMBAGES SONT DE CALIBRE 18 ET 16 OU MUSBH 3,25 DE SIMPSON STRONG TIE LORSQUE LES COLOMBAGES SONT DE CALIBRE 14, UTILISER 2 VIS #10
- SABLIÈRE : LISSE MULTIFENTE 362MST250 DE CALIBRE IDENTIQUE AUX COLOMBAGES

#### FIXATION TYPIQUE DES LISSES ET SABLIÈRES AUX PROFILÉS ACIER :

- 2 VIS AUTOPERCEUSES #1/4-20 DE TYPE KWIK-FLEX BIMÉTALLIQUE (UTILISER UNE POINTE No 5) DE HILTI @ 400 mm c/c. EN PRÉSENCE D'UNE LISSE ET D'UNE SABLIÈRE SITUÉE DE PART ET D'AUTRE DE LA CORNIÈRE, FIXER LES DEUX (2) PIÈCES EN MÊME TEMPS EN S'ASSURANT QUE TOUTS LES ÉLÉMENTS SOIENT PARFAITEMENT APPUYÉS. PRÉVOIR DES VIS ASSEZ LONGUES ET ALTERNER LES VIS HAUT ET BAS. ESPACER LES VIS D'AU MOINS 19 mm ET RESPECTER UNE DISTANCE DE RIVE MINIMALE DE 13 mm. VOIR DT-D.
- TOUS LES COLOMBAGES, LES BARRES EN Z, LES SABLIÈRES ET LES LISSES DOIVENT AVOIR UNE FINITION DE ZINC TYPE Z125 (G90) CONFORMÉMENT À LA NORME ASTM A653M.
- PRÉVOIR L'ENCOCHE DANS LES SABLIÈRES AUX EMPLACEMENTS DES CONSOLES.

CE DOCUMENT NE DOIT PAS ÊTRE UTILISÉ À DES FINS DE CONSTRUCTION

ARCHITECTURE:



MÉCANIQUE:



RÉVISIONS:

| REV | DATE       | DESCRIPTION                | PAR |
|-----|------------|----------------------------|-----|
| 0   | 2026-09-04 | DÉFINITIFS POUR SOUMISSION | JLB |

SCEAU:



AVERTISSEMENT: CE DRESSIN EST LA PROPRIÉTÉ INTELLECTUELLE DE WSP CANADA INC. AUCUNE RÉVISION, REPRODUCTION OU TOUT AUTRE USAGE N'EST PERMIS SANS L'AUTORISATION ÉCRITE DE WSP CANADA INC. L'ENTREPRENEUR DOIT VÉRIFIER TOUTES LES DIMENSIONS AUX PLANS ET FAIRE LOCALISER TOUT LES SERVICES D'UTILITÉS PUBLIQUES ET RAPPORTER TOUTES ERREURS OU OMISSIONS AVANT DE COMMENCER LES TRAVAUX.

|                                                                                    |                                                                       |
|------------------------------------------------------------------------------------|-----------------------------------------------------------------------|
| ÉCHELLE ORIGINALE: Comme indiqué                                                   | DATE: 2026-09-04                                                      |
| PRÉPARÉ PAR: JOANIE ROBILLARD, ing. CHARLOTTE ALLARD, CPI NATHAN SCHMITT, ing. PRT | SI CETTE BARRE NE MESURE PAS 25 mm, AJUSTER VOTRE ÉCHELLE DE TRAÇAGE. |
| VÉRIFIÉ PAR: JEAN-LUC BOUFFARD, ing.                                               |                                                                       |
| DRESSÉ PAR: GLORIA GILDA SIMIREA, tech.                                            |                                                                       |

DISCIPLINE: STRUCTURE



WSP Canada Inc.  
1135 Boulevard Lebourgneuf  
Ville de Québec, Québec, G2K 0M5  
T +1 418-623-2254 | www.wsp.com

NO PROJET: CA0062562.5541

CLIENT:



# RÉF. CLIENT: R674-24 / 24-108

PROJET:

HÔPITAL DE CHANDLER  
(RÉFECTION DE L'ENVELOPPE)

TITRE:


ÉLÉVATIONS -  
CONSTRUCTION

NUMÉRO DU FEUILLET:

S303

REV.

0

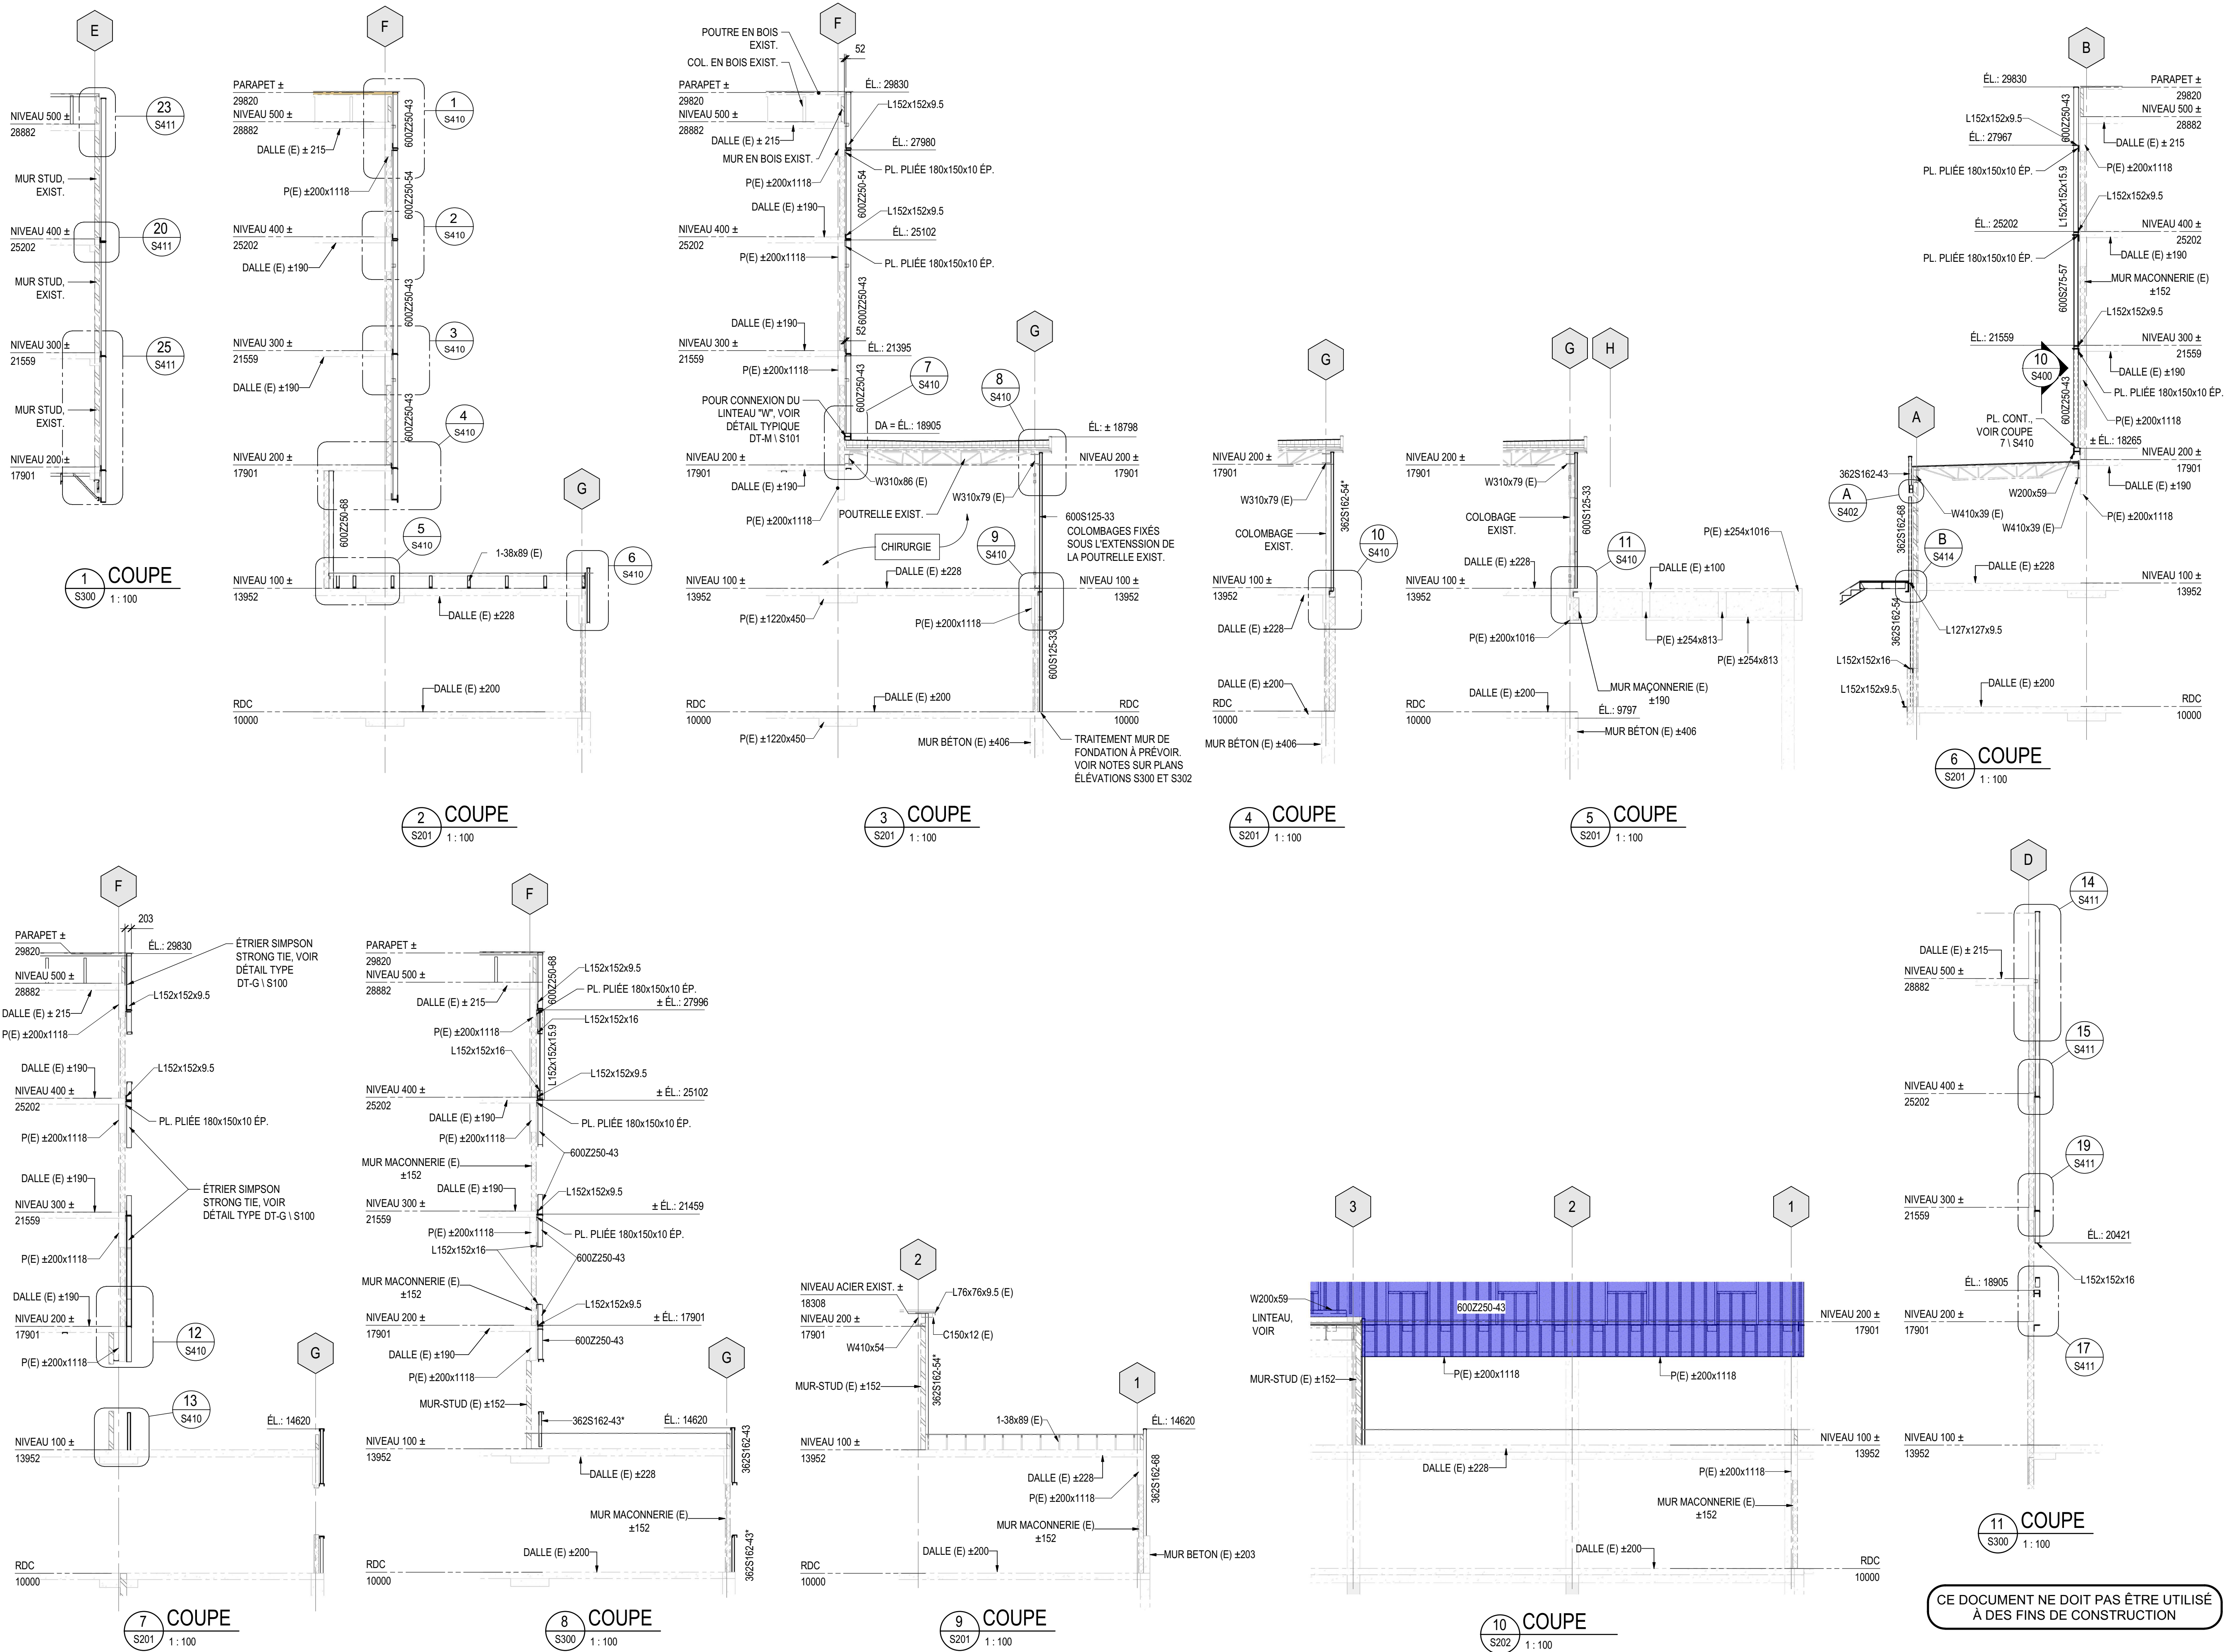

ARCHITECTURE:



MÉCANIQUE:



RÉVISIONS:

| REV | DATE       | DESCRIPTION                | PAR |
|-----|------------|----------------------------|-----|
| 0   | 2026-09-04 | DÉFINITIFS POUR SOUMISSION | JLB |

SCEAU:



AVERTISSEMENT:  
CE DOCUMENT EST LA PROPRIÉTÉ INTELLECTUELLE DE WSP CANADA INC. AUCUNE RÉVISION, REPRODUCTION OU TOUT AUTRE USAGE N'EST PERMIS SANS L'AUTORISATION ÉCRITE DE WSP CANADA INC. L'UTILISATEUR DOIT VÉRIFIER TOUS LES DIMENSIONS AUX PLANS ET FAIRE LOCALISER TOUS LES SERVICES D'UTILITÉS PUBLIQUES ET RAPPORTER TOUTES ERREURS OU OMISSIONS AVANT DE COMMENCER LES TRAVAUX.

|                                                                                             |                                                                        |
|---------------------------------------------------------------------------------------------|------------------------------------------------------------------------|
| ÉCHELLE ORIGINALE:<br>1 : 100                                                               | DATE:<br>2026-09-04                                                    |
| PRÉPARÉ PAR:<br>JOANIE ROBILLARD, ing.<br>CHARLOTTE ALLARD, CPI<br>NATHAN SCHMITT, ing. PRT | SI CETTE BARRE NE MESURE PAS 25 mm, AJUSTER VOTRE ÉCHELLE DE TRACÉAGE. |
| VÉRIFIÉ PAR:<br>JEAN-LUC BOUFFARD, ing.                                                     |                                                                        |
| DESSINÉ PAR:<br>GLORIA GILDA SIMIREA, tech.                                                 |                                                                        |
| DISCIPLINE:                                                                                 | STRUCTURE                                                              |



WSP Canada Inc.  
1135 Boulevard Lebourgneuf  
Ville de Québec, Québec, G2K 0M5  
T +1 418-623-2254 | www.wsp.com

NO PROJET: CA0062562.5541

CLIENT:



# RÉF. CLIENT: R674-24 / 24-108

PROJET:

HÔPITAL DE CHANDLER  
(RÉFECTION DE L'ENVELOPPE)

TITRE:

COUPES DE MURS

NUMÉRO DU FEUILLET:

S400

REV.

0

CE DOCUMENT NE DOIT PAS ÊTRE UTILISÉ  
À DES FINS DE CONSTRUCTION