



SANTÉ QUÉBEC GASPÉSIE

HÔPITAL DE CHANDLER (RÉFECTION DE L'ENVELOPPE)

451 RUE MGR - ROSS, CHANDLER, QC

LISTE DES PLANS


MÉCANIQUE / ÉLECTRICITÉ

GÉNÉRALITÉS	
G001	NOTES GÉNÉRALES ET LÉGENDE MÉCANIQUE
G002	NOTES GÉNÉRALES ET LÉGENDE ÉLECTRIQUE
G003	TABLEAU DE COORDINATION DES ÉQUIPEMENTS ÉLECTROMÉCANIQUES (À VENIR)
G004	DÉTAILS
ÉLÉVATIONS EXTÉRIEURES	
ME001(D)	ÉLÉVATIONS NORD / OUEST - DÉMOLITION
ME001	ÉLÉVATIONS NORD / OUEST - CONSTRUCTION
ME002(D)	ÉLÉVATIONS SUD / EST - DÉMOLITION
ME002	ÉLÉVATIONS SUD / EST - CONSTRUCTION
ME003(D)	ÉLÉVATIONS PARTIELLES - DÉMOLITION
ME003	ÉLÉVATIONS PARTIELLES - CONSTRUCTION
TOITURES	
ME004(D)	TOITURES ET SOFFITES - DÉMOLITION
ME004	TOITURES ET SOFFITES - CONSTRUCTION
ME005(D)	TOITURES - PARATONNERRE - DÉMOLITION
PLANS DE LOCALISATION	
ME006	SOUS-SOL ET REZ-DE-CHAUSSÉE - EXISTANT - LOCALISATION DES TRAVAUX INTÉRIEURS
ME007	NIVEAU 100, 200, 300 ET 400 - EXISTANT - LOCALISATION DES TRAVAUX INTÉRIEURS
VUES AGRANDIES ET DÉTAILS SPÉCIFIQUES	
ME008	VUES AGRANDIES ET DÉTAILS - QUAI DES AMBULANCES
ME009	VUES AGRANDIES ET DÉTAILS - TOITURE COIN NORD-OUEST
ME010	VUES AGRANDIES ET DÉTAILS - PRISE D'AIR DU BLOC OPÉRATOIRE
ME011	TRAVAUX TEMPORAIRES - PRISE D'AIR DU BLOC OPÉRATOIRE
ME012	VUES AGRANDIES ET DÉTAILS - MÉCANIQUE - AJOUT ISSUE LABORATOIRE
ME013	VUES AGRANDIES ET DÉTAILS - ÉLECTRICITÉ - AJOUT ISSUE LABORATOIRE
ME014	VUES AGRANDIES ET DÉTAILS - UNITÉ DE VENTILATION HÉMODIALYSE / LABORATOIRE
ME015	VUES AGRANDIES ET DÉTAILS - SALLE MÉCANIQUE CHIRURGIE D'UN JOUR ET PRISE D'AIR SERVICE ALIMENTAIRE
ME016	VUES AGRANDIES ET DÉTAILS - DIVERS TRAVAUX AU REZ-DE-CHAUSSÉE

MÉCANIQUE ET ÉLECTRICITÉ
HÔPITAL DE CHANDLER
(RÉFECTION DE L'ENVELOPPE)

DATE : 2026/09/04
NO DE RÉFÉRENCE :CA0066110.3235

DÉFINITIFS POUR
SOUSSION

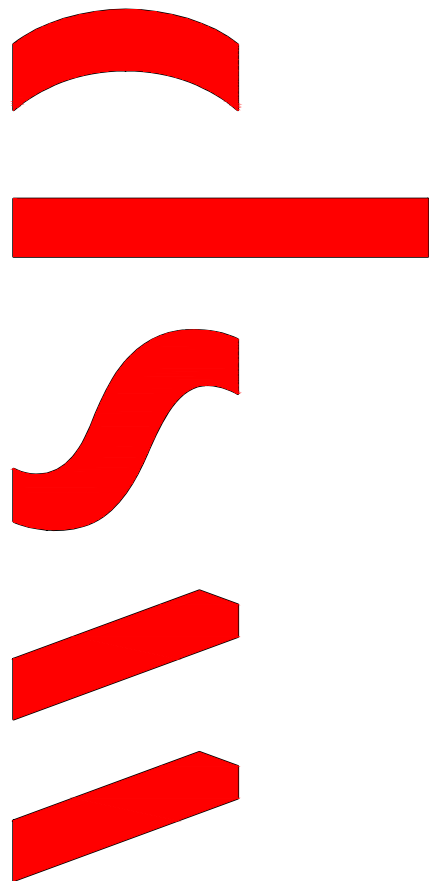

LISTE DES PROFESSIONNELS AU DOSSIER

LÉGENDE GÉNÉRALE

	ZONE HORS CONTRAT
	ÉLÉMENT EXISTANT
	ÉLÉMENT DÉMOLI
	ÉLÉMENT NOUVEAU
	ÉLÉMENT MODIFIÉ OU RELOCALISÉ
	ÉLÉMENT FOURNI ET INSTALLÉ PAR D'AUTRES
	ÉLÉMENT CACHÉ
	LIMITE DE CONTRAT
	IDENTIFICATION DES NOTES - CONSTRUCTION
	IDENTIFICATION DES NOTES - DÉMOLITION
	IDENTIFICATION CONCERNANT UNE AUTRE DISCIPLINE
	IDENTIFICATION CONCERNANT UNE AUTRE DISCIPLINE
	À COUPER ET BOUCHER ÉTANCHE
	POINT LIMITE DE DÉMOLITION
	POINT DE RACCORDEMENT À L'EXISTANT
	SOUFFLAGE
	RÉVISION
	IDENTIFICATION DES ÉQUIPEMENTS ET DES ACCESSOIRES
	IDENTIFICATION - POINT DE VUE PHOTO

ACRONYMES APPAREILS EXISTANTS

ACRONYME	EXPLICATION
EX	APPAREIL EXISTANT À CONSERVER
AE	APPAREIL EXISTANT À ENLEVER
AD	APPAREIL EXISTANT À DÉBRANCHER
AR	APPAREIL EXISTANT À RELOCALISER
R	APPAREIL EXISTANT RELOCALISÉ
AR*	APPAREIL EXISTANT À ENLEVER ET RÉINSTALLER AU MÊME ENDROIT
R*	APPAREIL EXISTANT ENLEVÉ ET RÉINSTALLÉ AU MÊME ENDROIT
AN	APPAREIL EXISTANT À ENLEVER ET À REMPLACER PAR UN NOUVEAU (CONSERVER LA FILERIE)
N	NOUVEL APPAREIL (FILIERE CONSERVÉE)
EAM	APPAREIL EXISTANT À MODIFIER
EM	APPAREIL EXISTANT MODIFIÉ

ACRONYMES GÉNÉRAUX

ACRONYME	EXPLICATION
EB	EN BAS
EH	EN HAUT
EL	ÉLEVATION
EP	CONDUIT OU ÉQUIPEMENT LOCALISÉ ENTRE LES POUTRELLES
PL	INSTALLÉ DANS L'ENTREPLAFOND
EPL	INSTALLÉ DANS L'ENTREPLAFOND C/A SUPPORT FIXE
HM	HAUTEUR DE MONTAGE
PA	PORTE D'ACCÈS
BPC	BAS DE PORTE COUPÉ

LÉGENDE ÉLECTRIQUE

ÉCLAIRAGE

GÉNÉRALITÉ:
LORSQUE L'ON RETROUVE UNE HACHURE QUADRILLÉE DANS UN SYMBOLE D'APPAREIL D'ÉCLAIRAGE, CEI INDIQUE QUE CE DERNIER EST NON CONTRÔLÉ, ALLUMÉ 24H PAR JOUR OU SUR URGENCE.

24H ET/OU SUR URGENCE: LUMINAIRE TEL QUE SYMBOLE ILLUSTRÉ (SANS CONTRÔLE)

EX: ou

	LUMINAIRE RECTANGULAIRE ENCASTRÉ AU PLAFOND (VOIR DIMENSION EN PLAN)
	LUMINAIRE RECTANGULAIRE SURFACE AU PLAFOND (VOIR DIMENSION EN PLAN)
	LUMINAIRE RECTANGULAIRE MURAL (VOIR DIMENSION EN PLAN)
	LUMINAIRE RECTANGULAIRE SUSPENDU (VOIR DIMENSION EN PLAN)
	LUMINAIRE ENCASTRÉ AU PLAFOND
	LUMINAIRE EN SURFACE AU PLAFOND
	LUMINAIRE SUSPENDU AU PLAFOND
	LUMINAIRE MURAL EN SURFACE
	LUMINAIRE MURAL EN SURFACE DE TYPE 'WALLPACK'

ÉCLAIRAGE D'URGENCE

	INDICATEUR DE SORTIE PERPENDICULAIRE AU MUR
	INDICATEUR DE SORTIE PARALLÈLE AU MUR
	INDICATEUR DE SORTIE AU PLAFOND
	PROJECTEUR D'ÉCLAIRAGE D'URGENCE AU PLAFOND SIMPLE OU DOUBLE
	PROJECTEUR D'ÉCLAIRAGE D'URGENCE MURAL SIMPLE OU DOUBLE
	BATTERIE D'ÉCLAIRAGE D'URGENCE AVEC PROJECTEURS
	BATTERIE D'ÉCLAIRAGE D'URGENCE

CONTRÔLE D'ÉCLAIRAGE

	INTERRUPTEUR SIMPLE
	INTERRUPTEUR 3 VOIES
	INTERRUPTEUR BASSE TENSION
	GRADATEUR À TENSION DE LIGNE
	GRADATEUR 0-10V
	CELLULE PHOTOÉLECTRIQUE

ALARME INCENDIE

	PANNEAU DE CONTRÔLE D'ALARME INCENDIE
	ANNONCIATEUR
	COMMUNICATEUR POUR CENTRALE DE SURVEILLANCE
	STATION MANUELLE
	DÉTECTEUR DE FUMÉE
	DÉTECTEUR DE FUMÉE DE GAINÉ
	DÉTECTEUR THERMIQUE ÉLEVATION DE TEMPÉRATURE
	KLAXON

PRISES ET SERVICES

GÉNÉRALITÉS:
LORSQU'UNE BARRE PERPENDICULAIRE TRAVERSE LE SYMBOLE D'UNE PRISE DE COURANT, CEI INDIQUE QUE CETTE DERNIÈRE DOIT ÊTRE INSTALLÉE À UNE HAUTEUR DE 1067mm (3'-6") DU PLANCHER OU 152mm (6") AU-DESSUS D'UN COMPTOIR EX.

EX: ou

	PRISE DE COURANT 15A-120V
	PRISE DE COURANT 15/20A-120V
	PRISE DE COURANT 15A-120V DDFT
	PRISE DE COURANT 15/20A-120V DDFT
	PRISE DE COURANT 15A-120V BATTERIE D'ÉCLAIRAGE D'URGENCE
	PRISE DE COURANT 15A-120V POUR EXTÉRIEUR
	PRISE DE COURANT 15/20A-120V POUR EXTÉRIEUR
	PRISE DE COURANT 15/20A-120V DE TOITURE EXTÉRIEURE SUR POTEAU
	PRISE DE COURANT SUR URGENCE (SYMBOLE ILLUSTRÉ SELON LÉGENDE DES PRISES)
	BOÎTE DE JONCTION OU DE TIRAGE

COMMUNICATION

GÉNÉRALITÉ:
LORSQU'UNE BARRE PERPENDICULAIRE TRAVERSE LE SYMBOLE D'UNE SORTIE, CEI INDIQUE QUE CETTE DERNIÈRE DOIT ÊTRE INSTALLÉE À UNE HAUTEUR DE 1067mm (3'-6") DU PLANCHER OU 152mm (6") AU-DESSUS D'UN COMPTOIR EX. ou (3) = 3 CÂBLES

	SORTIE INFORMATIQUE
	SORTIE TÉLÉPHONIQUE
	SORTIE DE TÉLÉCOMMUNICATION
	SORTIE INFORMATIQUE AU PLAFOND POUR RÉSEAU SANS FIL (Wi-Fi)

DISTRIBUTION

	PANNEAU 120/208V 120/240V SURFACE
	PANNEAU 120/208V 120/240V ENCASTRÉ
	PANNEAU 347/600V SURFACE
	PANNEAU 347/600V ENCASTRÉ
	PANNEAU À RELAIS SURFACE
	PANNEAU À RELAIS ENCASTRÉ
	SECTIONNEUR 250V ET MOINS
	SECTIONNEUR PLUS DE 250V
	TRANSFORMATEUR

RACCORDEMENT D'ÉQUIPEMENT

	MOTEUR MONOPHASÉ FRACTIONNEL (MOINS DE 1/10HP)
	MOTEUR MONOPHASÉ PUISSANCE 1/4 HP
	MOTEUR TRIPHASÉ PUISSANCE DE 2HP
	MINI-SECTIONNEUR D'ENTRETIEN
	DÉMARREUR MAGNÉTIQUE
	DÉMARREUR MAGNÉTIQUE COMBINÉ AVEC SECTIONNEUR
	ENTRAÎNEMENT À FRÉQUENCE VARIABLE
	ENTRAÎNEMENT À FRÉQUENCE VARIABLE COMBINÉ AVEC SECTIONNEUR
	DÉMARREUR MANUEL
	CONTACTEUR MAGNÉTIQUE C/A BOÎTIER
	RACCORD DIRECT 120V, 1 PHASE
	RACCORD DIRECT 208V OU 240V, 1 PHASE
	RACCORD DIRECT 208V, 3 PHASES OU 120/208V, 3 PHASES, 4 FILS
	RACCORD DIRECT 347V OU 600V, 1 PHASE
	RACCORD DIRECT 600V, 3 PHASES OU 347/600V, 3 PHASES, 4 FILS
	REGISTRE COUPE-FEU / COUPE-FUMÉE

CHAUFFAGE

	PLINTHE CHAUFFANTE ÉLECTRIQUE
	CABINET DE CHAUFFAGE ÉLECTRIQUE EN SURFACE À CONVECTION

CHAUFFAGE

	CABINET DE CHAUFFAGE ÉLECTRIQUE ENCASTRÉ À CONVECTION
	CABINET DE CHAUFFAGE ÉLECTRIQUE EN SURFACE À AIR FORCÉ
	CABINET DE CHAUFFAGE ÉLECTRIQUE ENCASTRÉ À AIR FORCÉ
	SERPENTIN ÉLECTRIQUE

CONTRÔLE D'ACCÈS

	PANNEAU DE CONTRÔLE D'ACCÈS
	CONTRÔLEUR DE SURVEILLANCE DE PORTES
	CONTRÔLEUR DE COMMUNICATIONS RÉSEAU
	BLOC D'ALIMENTATION QUINQUALLERIE ÉLECTRIFIÉE
	CLAVIER NUMÉRIQUE
	LECTEUR DE CARTES
	LECTEUR DE CARTES C/A CLAVIER NUMÉRIQUE
	LECTEUR DE CARTES LONGUE PORTÉE
	SERRURE ÉLECTRIFIÉE
	BOUTON / BARRE PANIQUE ÉLECTRIFIÉ
	CONTACT MAGNÉTIQUE DE PORTE
	ÉLECTRO-AIMANT (SERRURE ÉLECTROMAGNÉTIQUE)
	GÂCHE ÉLECTRIQUE
	GÂCHE MONITRICE
	TRANSFERT DE COURANT
	OPÉRATEUR DE PORTE
	RETENUE MAGNÉTIQUE DE PORTE
	REQUÊTE DE SORTIE
	BOUTON REQUÊTE DE SORTIE
	INTERRUPTEUR D'ÉVITEMENT À CLÉ
	BOUTON D'OUVERTURE DE PORTE
	BOUTON DE SONNETTE

VIDÉO SURVEILLANCE

	CAMÉRA DE SURVEILLANCE, ANGLE DE VUE SIMPLE
	CAMÉRA DE SURVEILLANCE, ANGLE DE VUE MULTIPLE
	CAMÉRA DE SURVEILLANCE À L'EXTÉRIEUR AVEC BOÎTIER DE PROTECTION
	MONITEUR SYSTÈME CAMÉRAS
	ENREGISTREUR NUMÉRIQUE DE SURVEILLANCE

INTERCOMMUNICATION

	CONSOLE PRINCIPALE SYSTÈME INTERCOMMUNICATION
	POSTE MAÎTRE
	POSTE SECONDAIRE ENCASTRÉ

	TROMPETTE INTÉRIEURE
	TROMPETTE EXTÉRIEURE
	INTERCOM MURAL EXTÉRIEUR C/A CAMÉRA
	RÉCEPTEUR DE L'INTERCOM
	HAUT-PARLEUR ENCASTRÉ AU PLAFOND
	HAUT-PARLEUR EN SURFACE AU PLAFOND C/A BOÎTIER
	HAUT-PARLEUR ENCASTRÉ AU MUR
	HAUT-PARLEUR INSTALLÉ EN SURFACE AU MUR C/A BOÎTIER
	COLONNE DE SON
	AMPLIFICATEUR
	MONITEUR / ÉCRAN MURAL POUR INTERCOM
	PRISE POUR ÉCOUTE-AUDIO
	PRISE POUR MICRO
	HORLOGE AU PLAFOND
	HORLOGE AU MUR

SONORISATION / APPEL GÉNÉRAL

	CONSOLE PRINCIPALE DU SYSTÈME DE SON
	AMPLIFICATEUR DU SYSTÈME DE SON
	HAUT-PARLEUR ENCASTRÉ AU PLAFOND
	HAUT-PARLEUR EN SURFACE AU PLAFOND C/A BOÎTIER
	HAUT-PARLEUR ENCASTRÉ AU MUR
	HAUT-PARLEUR INSTALLÉ EN SURFACE AU MUR C/A BOÎTIER
	COLONNE DE SON
	PRISE POUR ÉCOUTE-AUDIO
	PRISE POUR MICRO
	CONTRÔLE DE VOLUME

ACRONYMES

BJ	BOÎTE DE JONCTION
CD	CANDELAS (STROBE ALARME INCENDIE)
DDFT	AVEC DISPOSITIF DE DÉTECTION DE FUITE À LA TERRE
F:30A	AVEC FUSIBLE DE 30A
K	ÉQUIPEMENT MANIPULÉ À CLÉ
MALT	MISE À LA TERRE
MALTI	MISE À LA TERRE ISOLÉE
SF	SANS FUSIBLE
TL	VERROUILLABLE ('TWIST-LOCK')
TV	TÉLÉVISION

IDENTIFICATIONS

NOTE IMPORTANTE CONCERNANT LES TRAVAUX RÉALISÉS PAR PHASE

L'ENSEMBLE DES TRAVAUX CONTENUS DANS LES PLANS SERONT EXÉCUTÉS EN PLUSIEURS PHASES. CES PHASES SONT DÉCRITES AUX DOCUMENTS D'ARCHITECTURE. LE PRÉSENT ENTREPRENEUR DOIT PRENDRE CONNAISSANCE DE CES PHASES ET EN TENIR COMPTE DANS SON PRIX DE SOUMISSION. LE PRÉSENT ENTREPRENEUR DOIT ÉGALEMENT INCLURE TOUT LE MATÉRIEL, LA MAIN D'ŒUVRE, LES TRAVAUX TEMPORAIRES, ETC. NÉCESSAIRE AFIN QUE TOUT CE QUI EST À L'EXTÉRIEUR DE LA ZONE DES TRAVAUX, ET CE, À CHACUNE DES PHASES, DOIT TOUJOURS DEMEURER FONCTIONNEL ET OPÉRATIONNEL.

DOCUMENTS GÉNÉRAUX IMPORTANTS

LE PRÉSENT ENTREPRENEUR DOIT OBLIGATOIREMENT CONSULTER LES DOCUMENTS GÉNÉRAUX, PRÉPARÉS PAR LE PROPRIÉTAIRE ET/OU L'ARCHITECTE, QUI TRAITENT ENTRE AUTRE : DE LA GESTION DES REBUTS, DE LA PROTECTION DES INFECTIONS, DES HEURES DE TRAVAUX, DES HEURES POUR LES PERCEMENTS, LES INTERRUPTIONS DE SERVICES, ETC. LE PRÉSENT ENTREPRENEUR DOIT INCLURE DANS SON PRIX DE SOUMISSION, TOUT LE MATÉRIEL, LA MAIN D'ŒUVRE, ETC. RELATIFS AUX EXIGENCES DE CES DOCUMENTS.

NOTES GÉNÉRALES DE CONSTRUCTION

LES NOUVELLES FAÇADES SONT PLUS ÉPAISSES. POUR CHAQUE ÉQUIPEMENTS À INSTALLER OU RÉINSTALLER, FOURNIR TOUT LE MATÉRIEL REQUIS À L'ÉPAISSISSEMENT DES MURS. TELQUE, MAIS SANS S'Y LIMITER, EXTENSION DE BOÎTE, BOÎTE DE JONCTION, FILAGE, ETC.

CLIENT



SANTÉ QUÉBEC GASPÉSIE

RÉF. CLIENT:
PROJET

HÔPITAL DE CHANDLER
(RÉFECTION DE L'ENVELOPPE)

Architecte



CE DOCUMENT NE DOIT PAS SERVIR À LA CONSTRUCTION

REV	DATE	DESCRIPTION	PAR
RÉVISIONS PARTIELLES			
1	2026/09/04	DÉFINITIFS POUR SOUMISSION	JD-JA
B	2026/08/21	DÉFINITIFS 100% POUR APPROBATION	JD-VS
A	2026/05/14	DÉFINITIFS 60% POUR APPROBATION	JD-VS
REV	DATE	DESCRIPTION	PAR

SCEAU:	
MÉCANIQUE	ÉLECTRICITÉ
AVERTISSEMENT: DROIT D'AUTEUR: CE DESSIN EST LA PROPRIÉTÉ INTELLECTUELLE DE WSP CANADA INC. AUCUNE RÉVISION, REPRODUCTION OU TOUT AUTRE USAGE N'EST PERMIS SANS L'AUTORISATION ÉCRITE DE WSP CANADA INC. L'ENTREPRENEUR DEVRA VÉRIFIER TOUTES LES DIMENSIONS AUX PLANS ET FAIRE LOCALISER TOUS LES SERVICES D'UTILITÉS PUBLIQUES ET RAPPORTER TOUTES ERREURS OU OMISSIONS AVANT DE COMMENCER LES TRAVAUX.	
ÉCHELLE ORIGINALE: INDIQUÉE DESSINÉ PAR : A. CASTONGUAY PRÉPARÉ SOUS SUPERVISION PAR : J. D'AMOURS ET V. STOCKMEYER, ing. PRÉPARÉ PAR : J. D'AMOURS ET J. ALCINDOR, ing. APPROUVÉ ADMINISTRATIVEMENT PAR : S. LAVOIE	DATE: AVRIL 2026 SI CETTE BARRE NE MESURE PAS 25 mm, AJUSTER VOTRE ÉCHELLE DE TRAVAUX. 25mm
DISCIPLINE: MÉCANIQUE / ÉLECTRIQUE	

Mécanique / Électricité



NO PROJET: CA0066110.3235


TITRE:

NOTES GÉNÉRALES ET
LÉGENDE ÉLECTRIQUE

NUMÉRO DU
FEUILLET:


G002

\\corp.phn.qc.ca\data\shared\can11\PEP\projets\2026\11CA0661\10.3235\Bâtiment05 TECH04.1 CAO

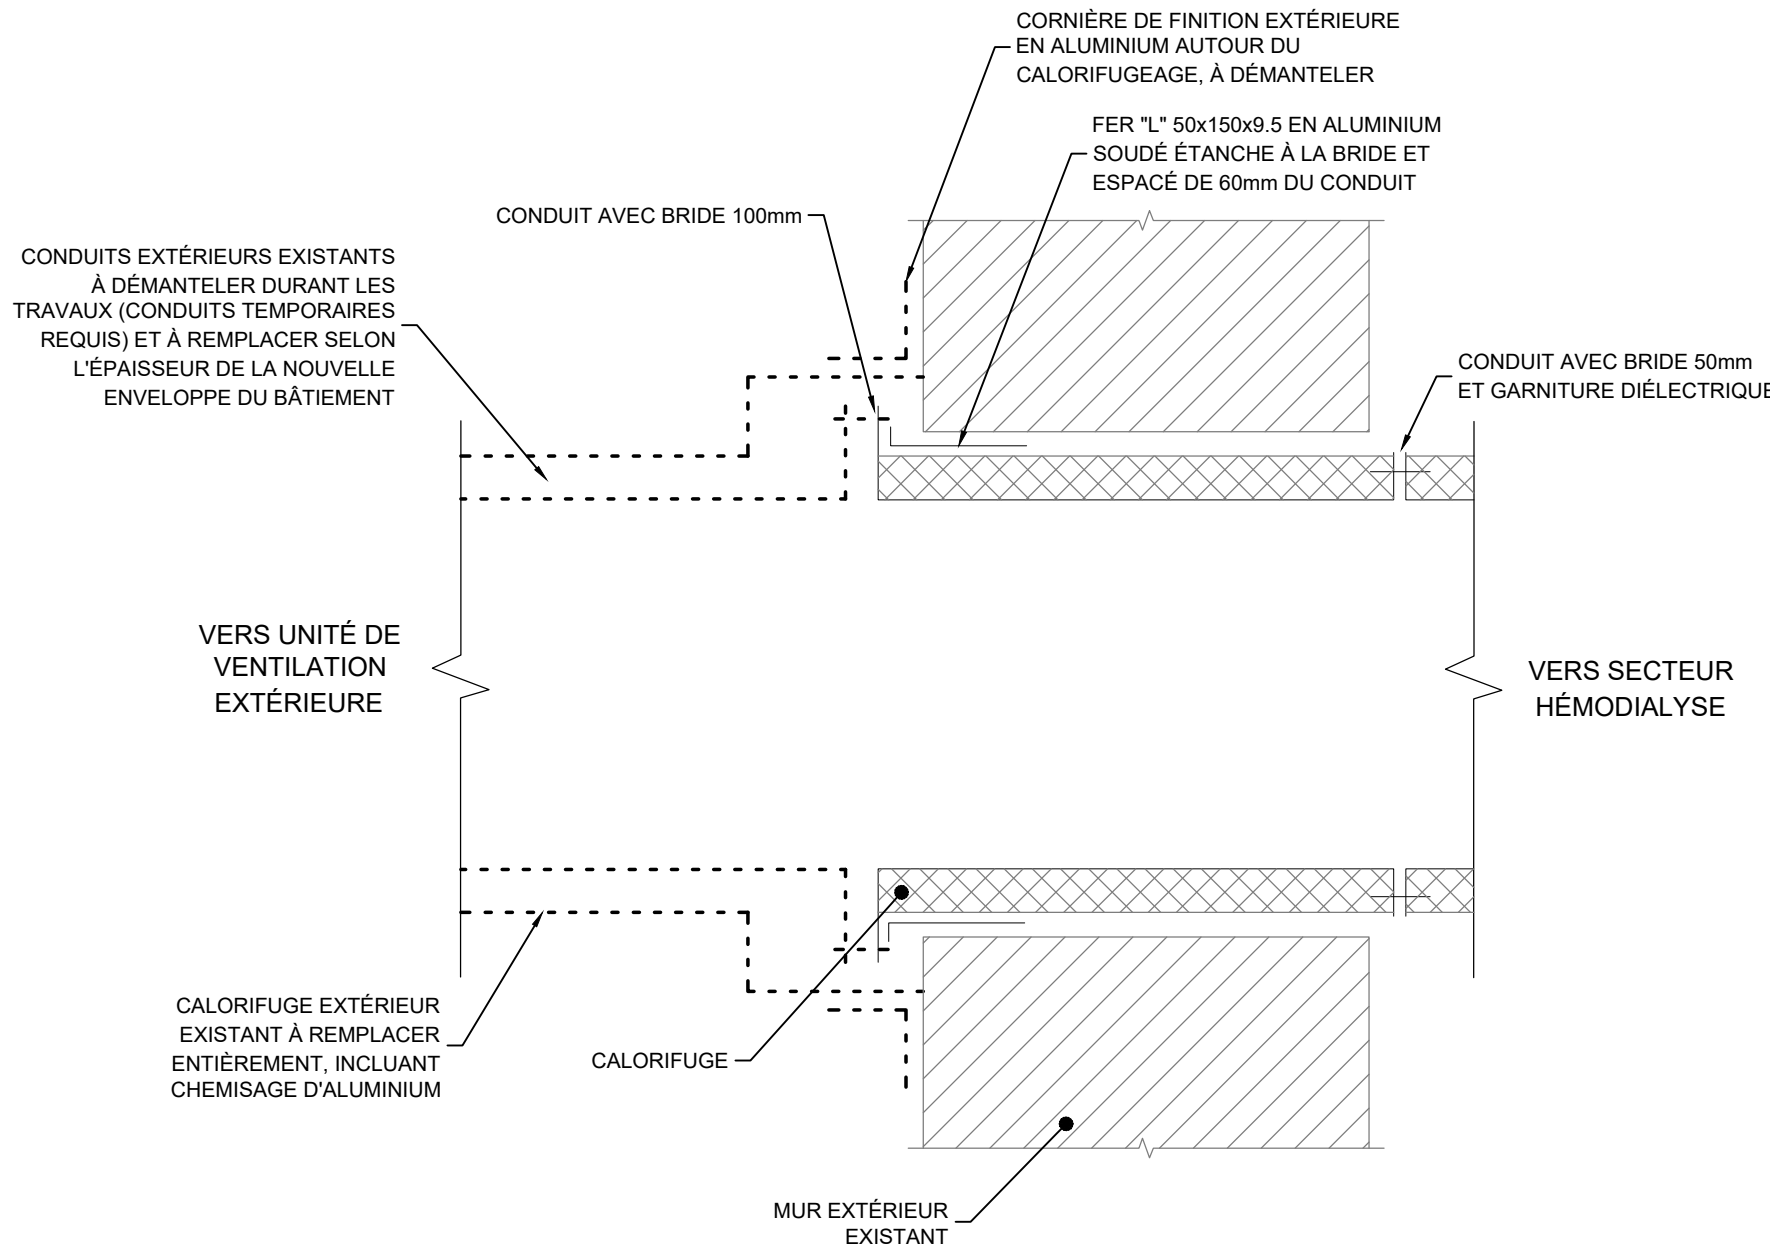


DÉTAIL DE TRAVERSÉE DE MUR EXTÉRIEUR - CONDUITS DU SECTEUR HÉMODIALYSE - DÉMOLITION

ÉCHELLE: AUCUNE

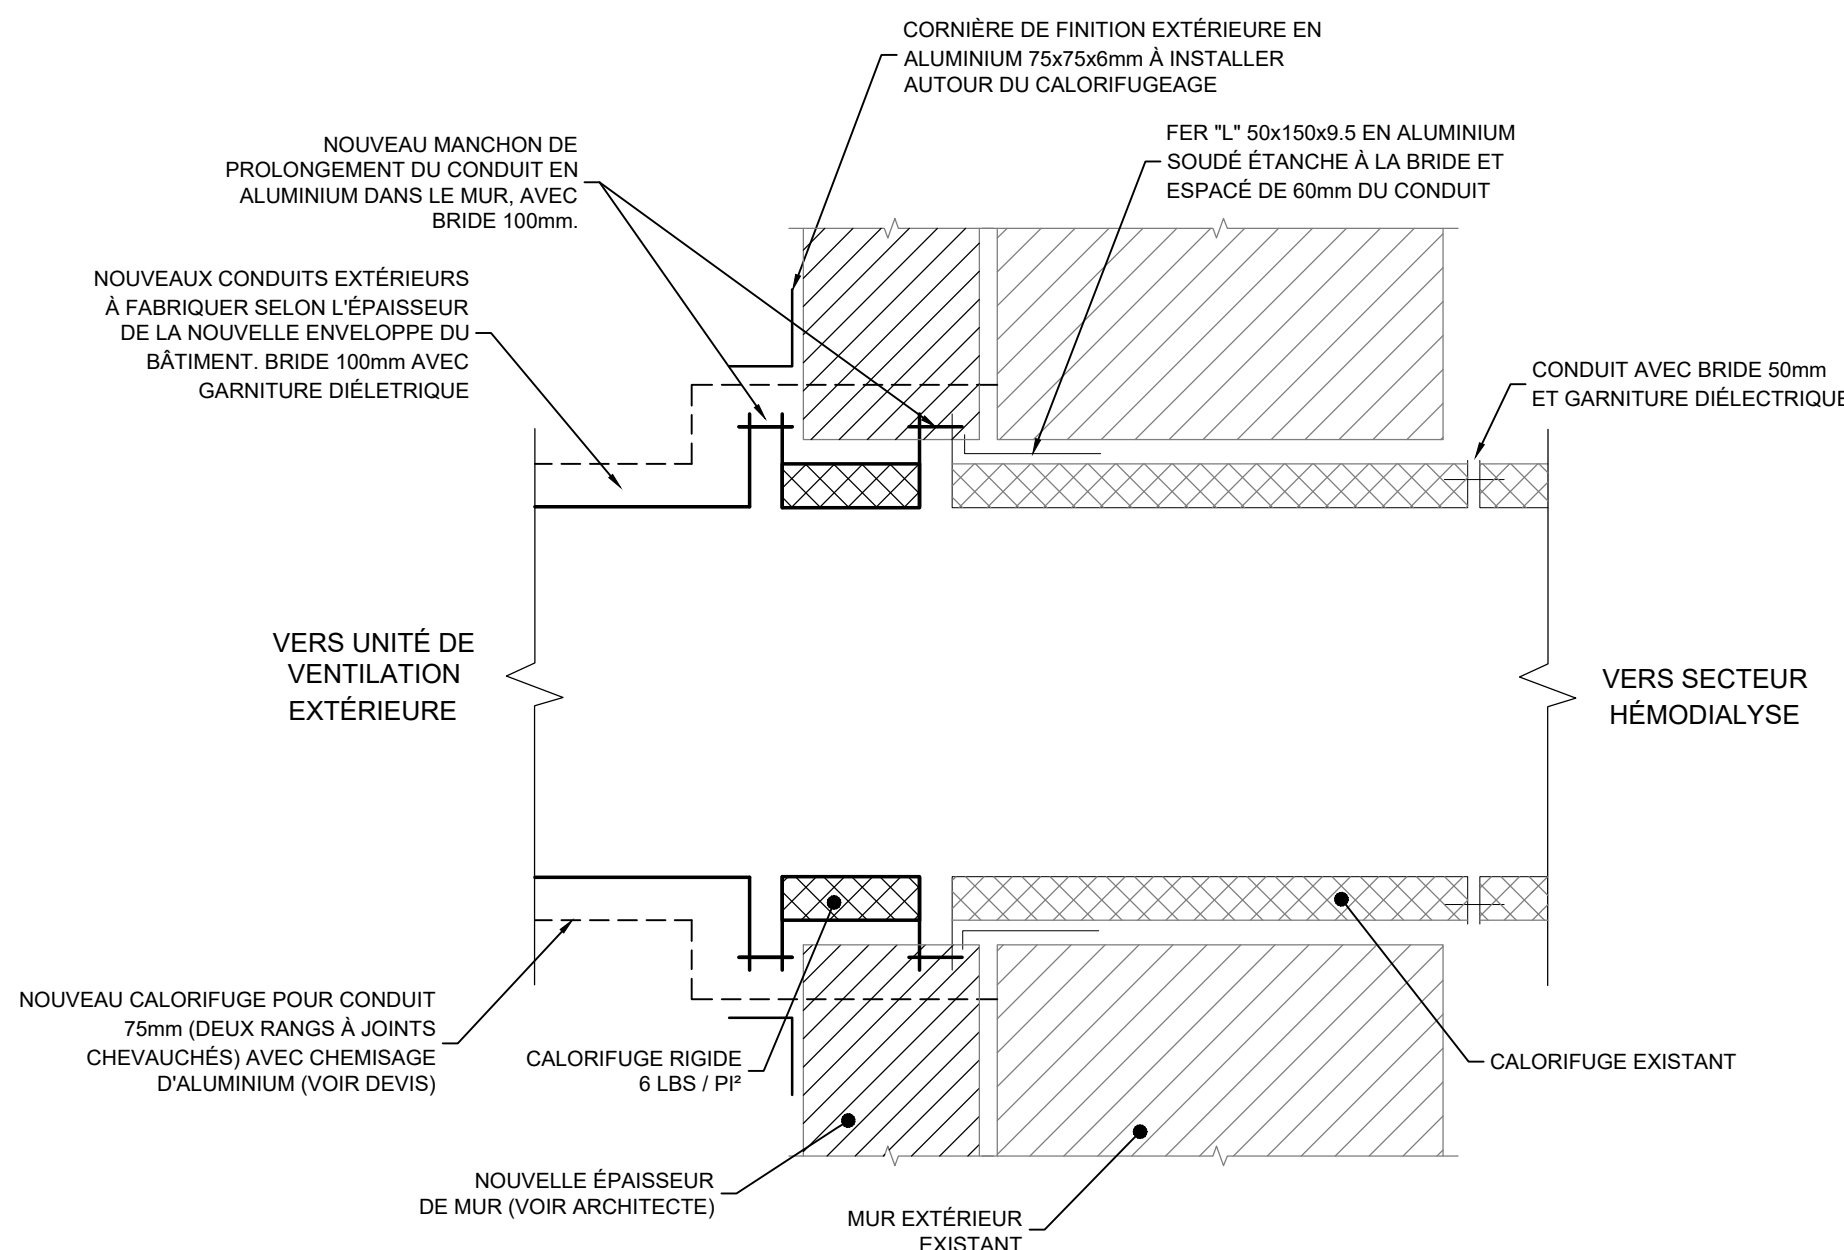


DÉTAIL DE TRAVERSÉE DE MUR EXTÉRIEUR - CONDUITS DU SECTEUR HÉMODIALYSE - DÉMOLITION

ÉCHELLE: AUCUNE

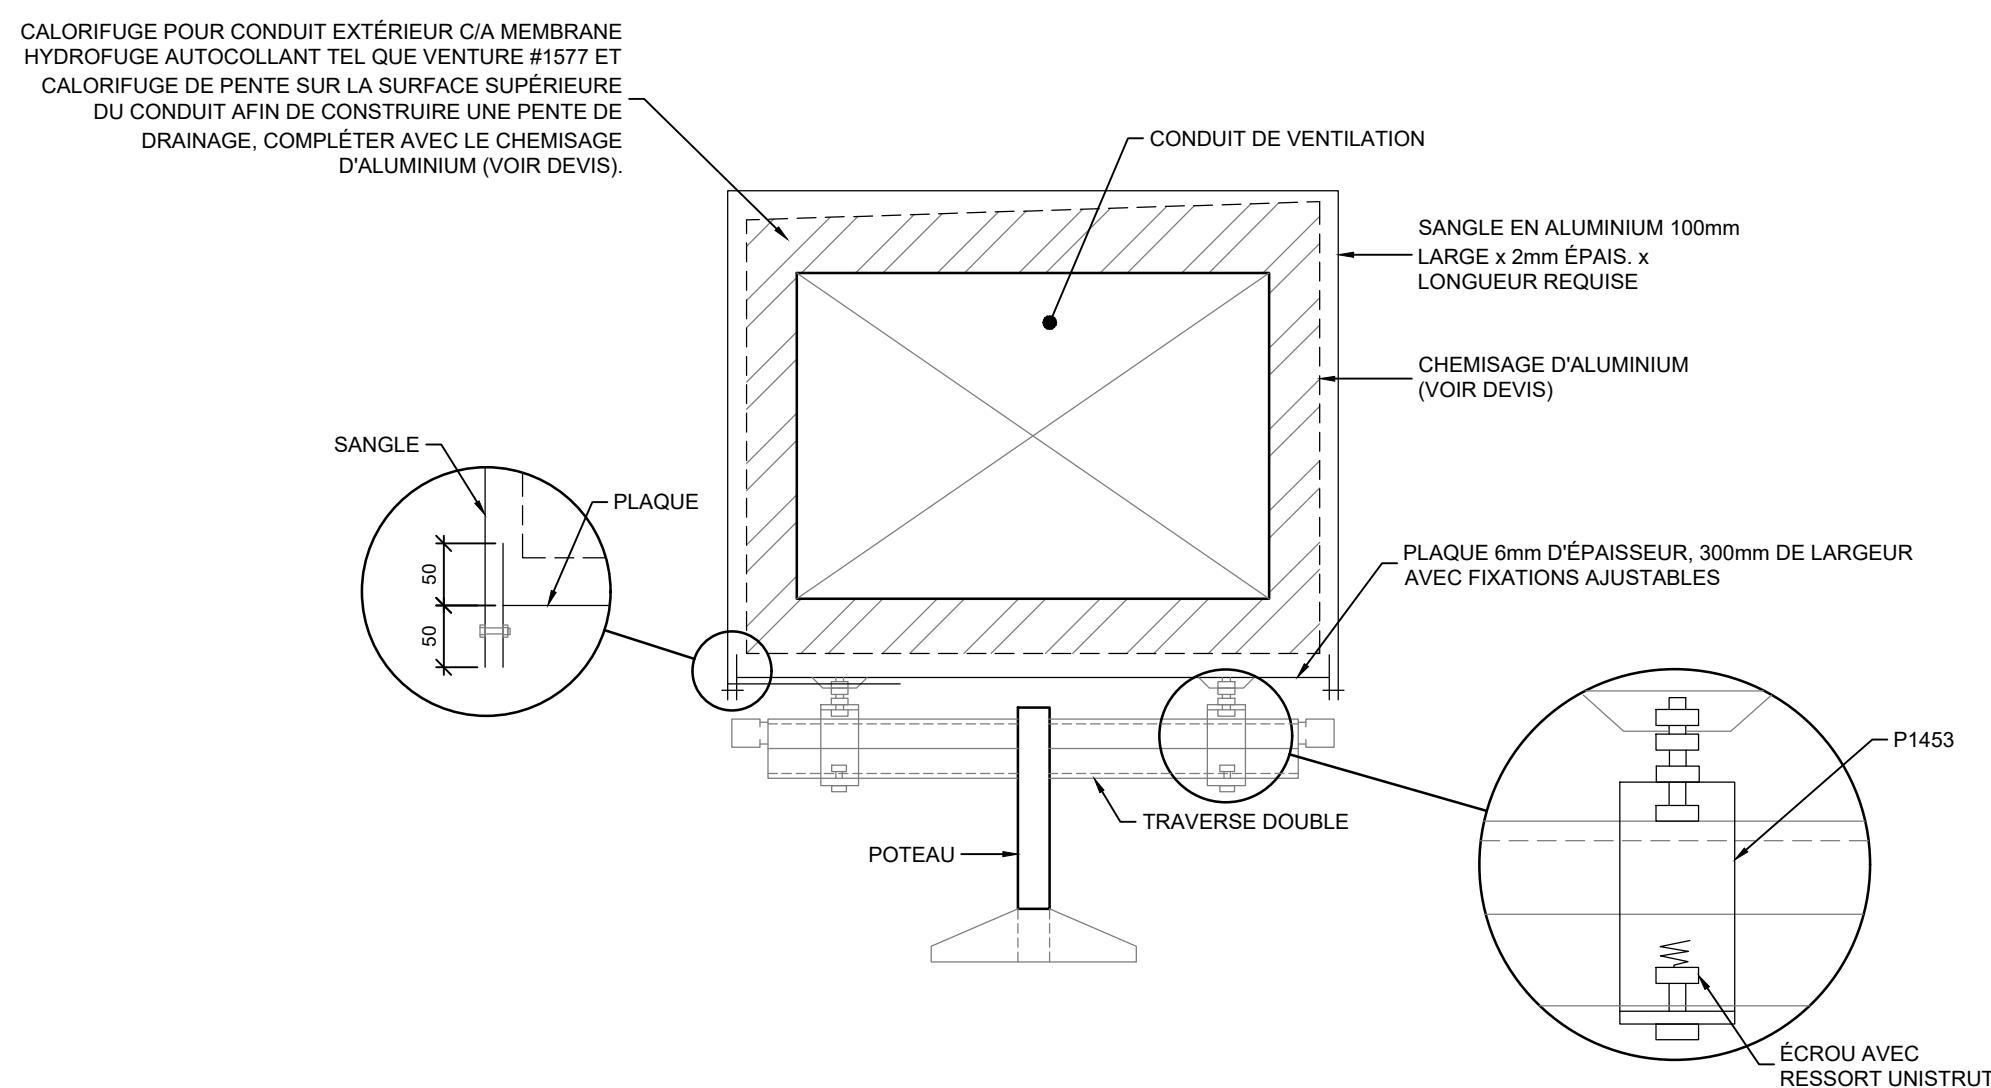


DÉTAIL D'INSTALLATION DES CONDUITS EXTÉRIEURS D'HÉMODIALYSE DÉPOSÉS AU TOIT #1

ÉCHELLE: AUCUNE

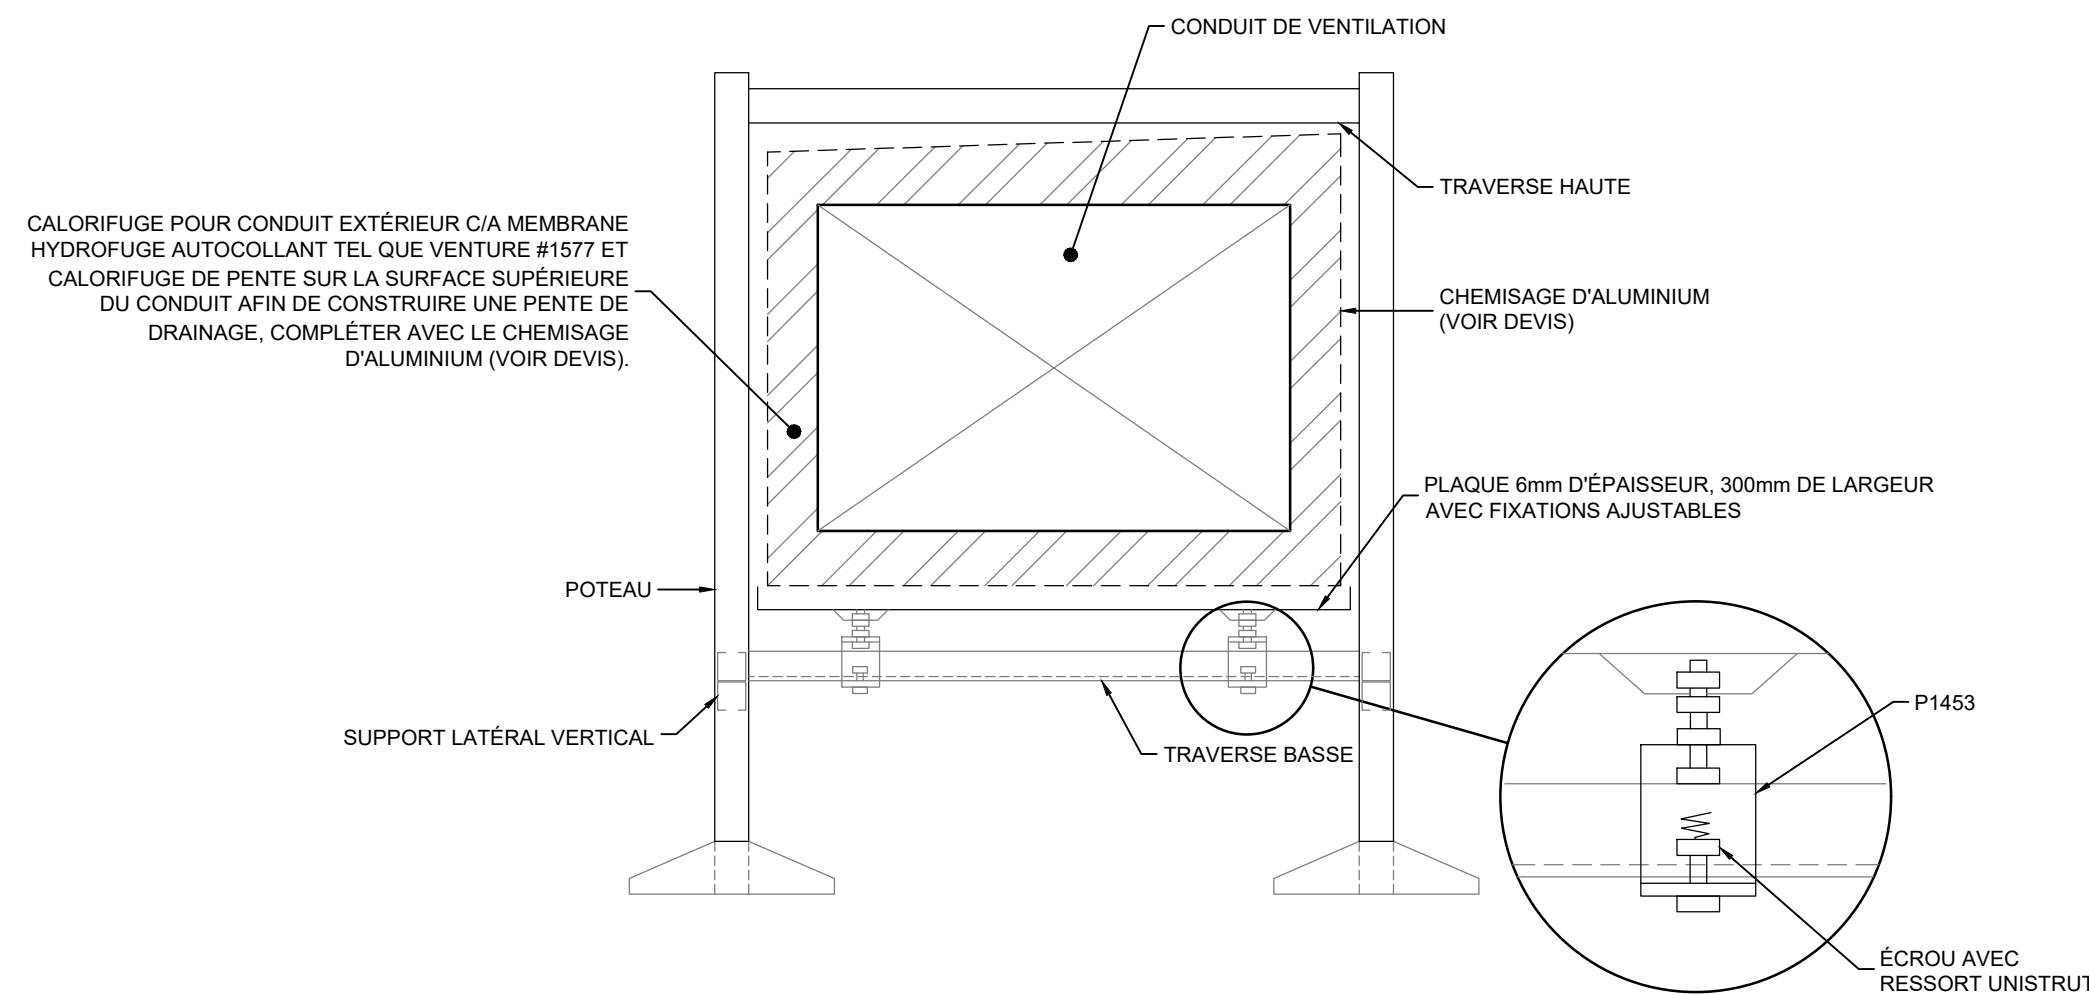

DÉTAIL D'INSTALLATION DES CONDUITS EXTÉRIEURS D'HÉMODIALYSE DÉPOSÉS AU TOIT #2

ÉCHELLE: AUCUNE

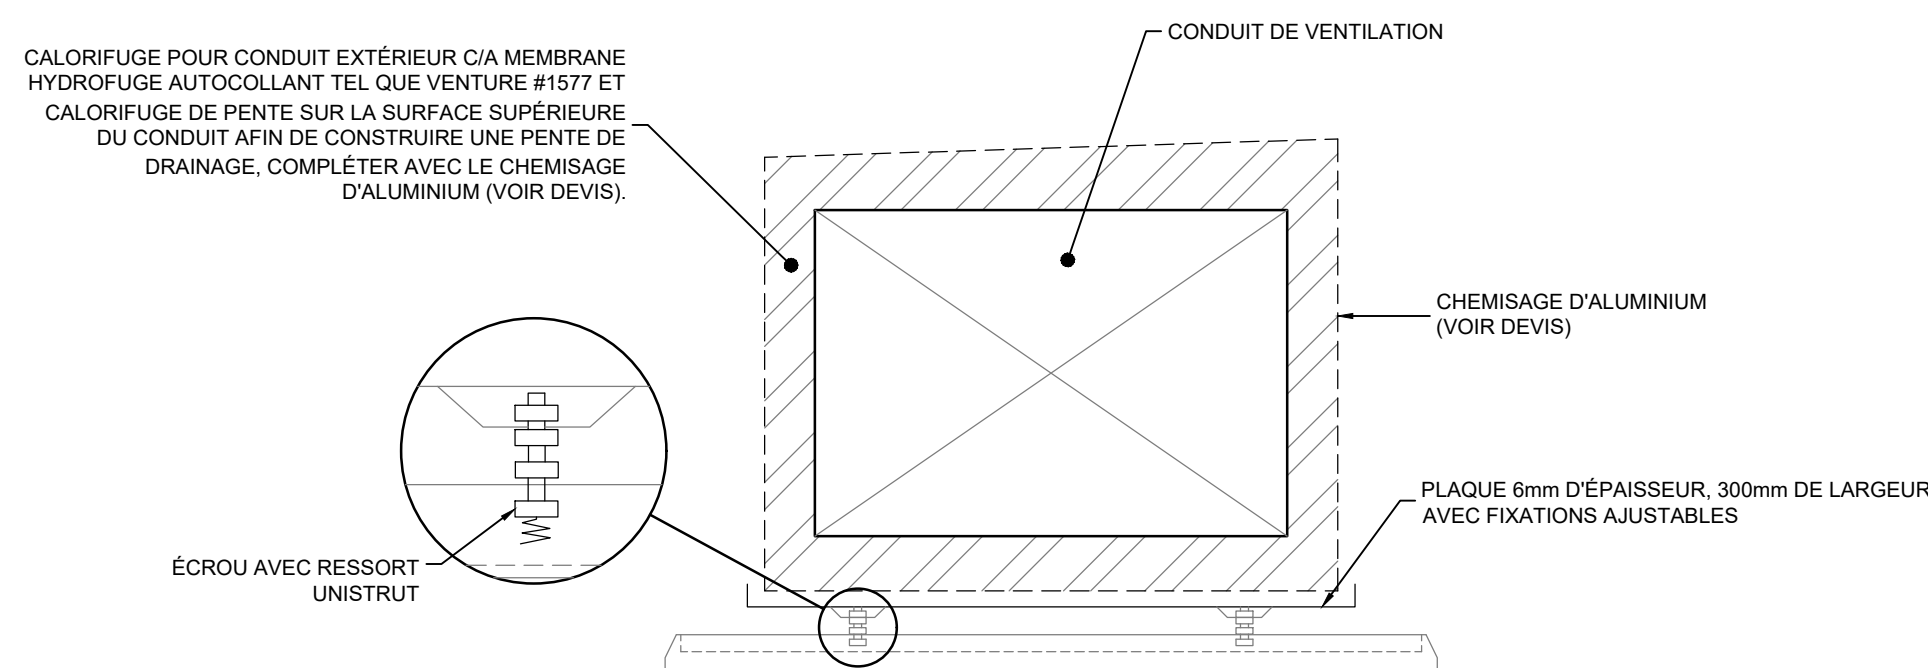

DÉTAIL D'INSTALLATION DES CONDUITS EXTÉRIEURS D'HÉMODIALYSE DÉPOSÉS AU TOIT #3

ÉCHELLE: AUCUNE

CLIENT



SANTÉ QUÉBEC GASPÉSIE

RÉF. CLIENT:

PROJET

HÔPITAL DE CHANDLER
(RÉFECTION DE L'ENVELOPPE)

Architecte



CE DOCUMENT NE DOIT PAS SERVIR À
LA CONSTRUCTION

REV	DATE	DESCRIPTION	PAR
RÉVISIONS PARTIELLES			
1	2026/09/04	DÉFINITIFS POUR SOUMISSION	JD-JA
B	2026/08/21	DÉFINITIFS 100% POUR APPROBATION	JD-VS
A	2026/05/14	DÉFINITIFS 60% POUR APPROBATION	JD-VS
REV	DATE	DESCRIPTION	PAR

SCEAU:



MÉCANIQUEÉLECTRICITÉ

AVERTISSEMENT:

CE DESSIN EST LA PROPRIÉTÉ INTELLECTUELLE DE WSP CANADA INC. AUCUNE RÉVISION, REPRODUCTION OU TOUT AUTRE USAGE N'EST PERMIS SANS L'AUTORISATION ÉCRITE DE WSP CANADA INC. L'ENTREPRENEUR DEVRA VÉRIFIER TOUTES LES DIMENSIONS AUX PLANS ET FAIRE LOCALISER TOUS LES SERVICES D'UTILITÉS PUBLIQUES ET RAPPORTER TOUTES ERREURS OU OMISSIONS AVANT DE COMMENCER LES TRAVAUX.

ÉCHELLE: ORIGINALE:

INDIQUÉE

DATE: AVRIL 2026

DESSINÉ PAR:

A. CASTONGUAY & A. HALLÉ

SI CETTE BARRE NE MESURE PAS 25 mm, AJUSTER VOTRE ÉCHELLE DE TRACÉ.

PRÉPARÉ SOUS SUPERVISION PAR:

J. D'AMOURS ET V. STOCKMEYER, ing.

25mm

PRÉPARÉ PAR:

J. D'AMOURS ET V. STOCKMEYER, ing.

APPROUVÉ ADMINISTRATIVEMENT PAR:

S. LAVOIE

DISCIPLINE:

MÉCANIQUE / ÉLECTRICITÉ

Mécanique / Électricité



NO PROJET: CA0066110.3235


TITRE:

DÉTAILS


NUMÉRO DU FEUILLET:

G004

ÉCHELLE: AUCUNE

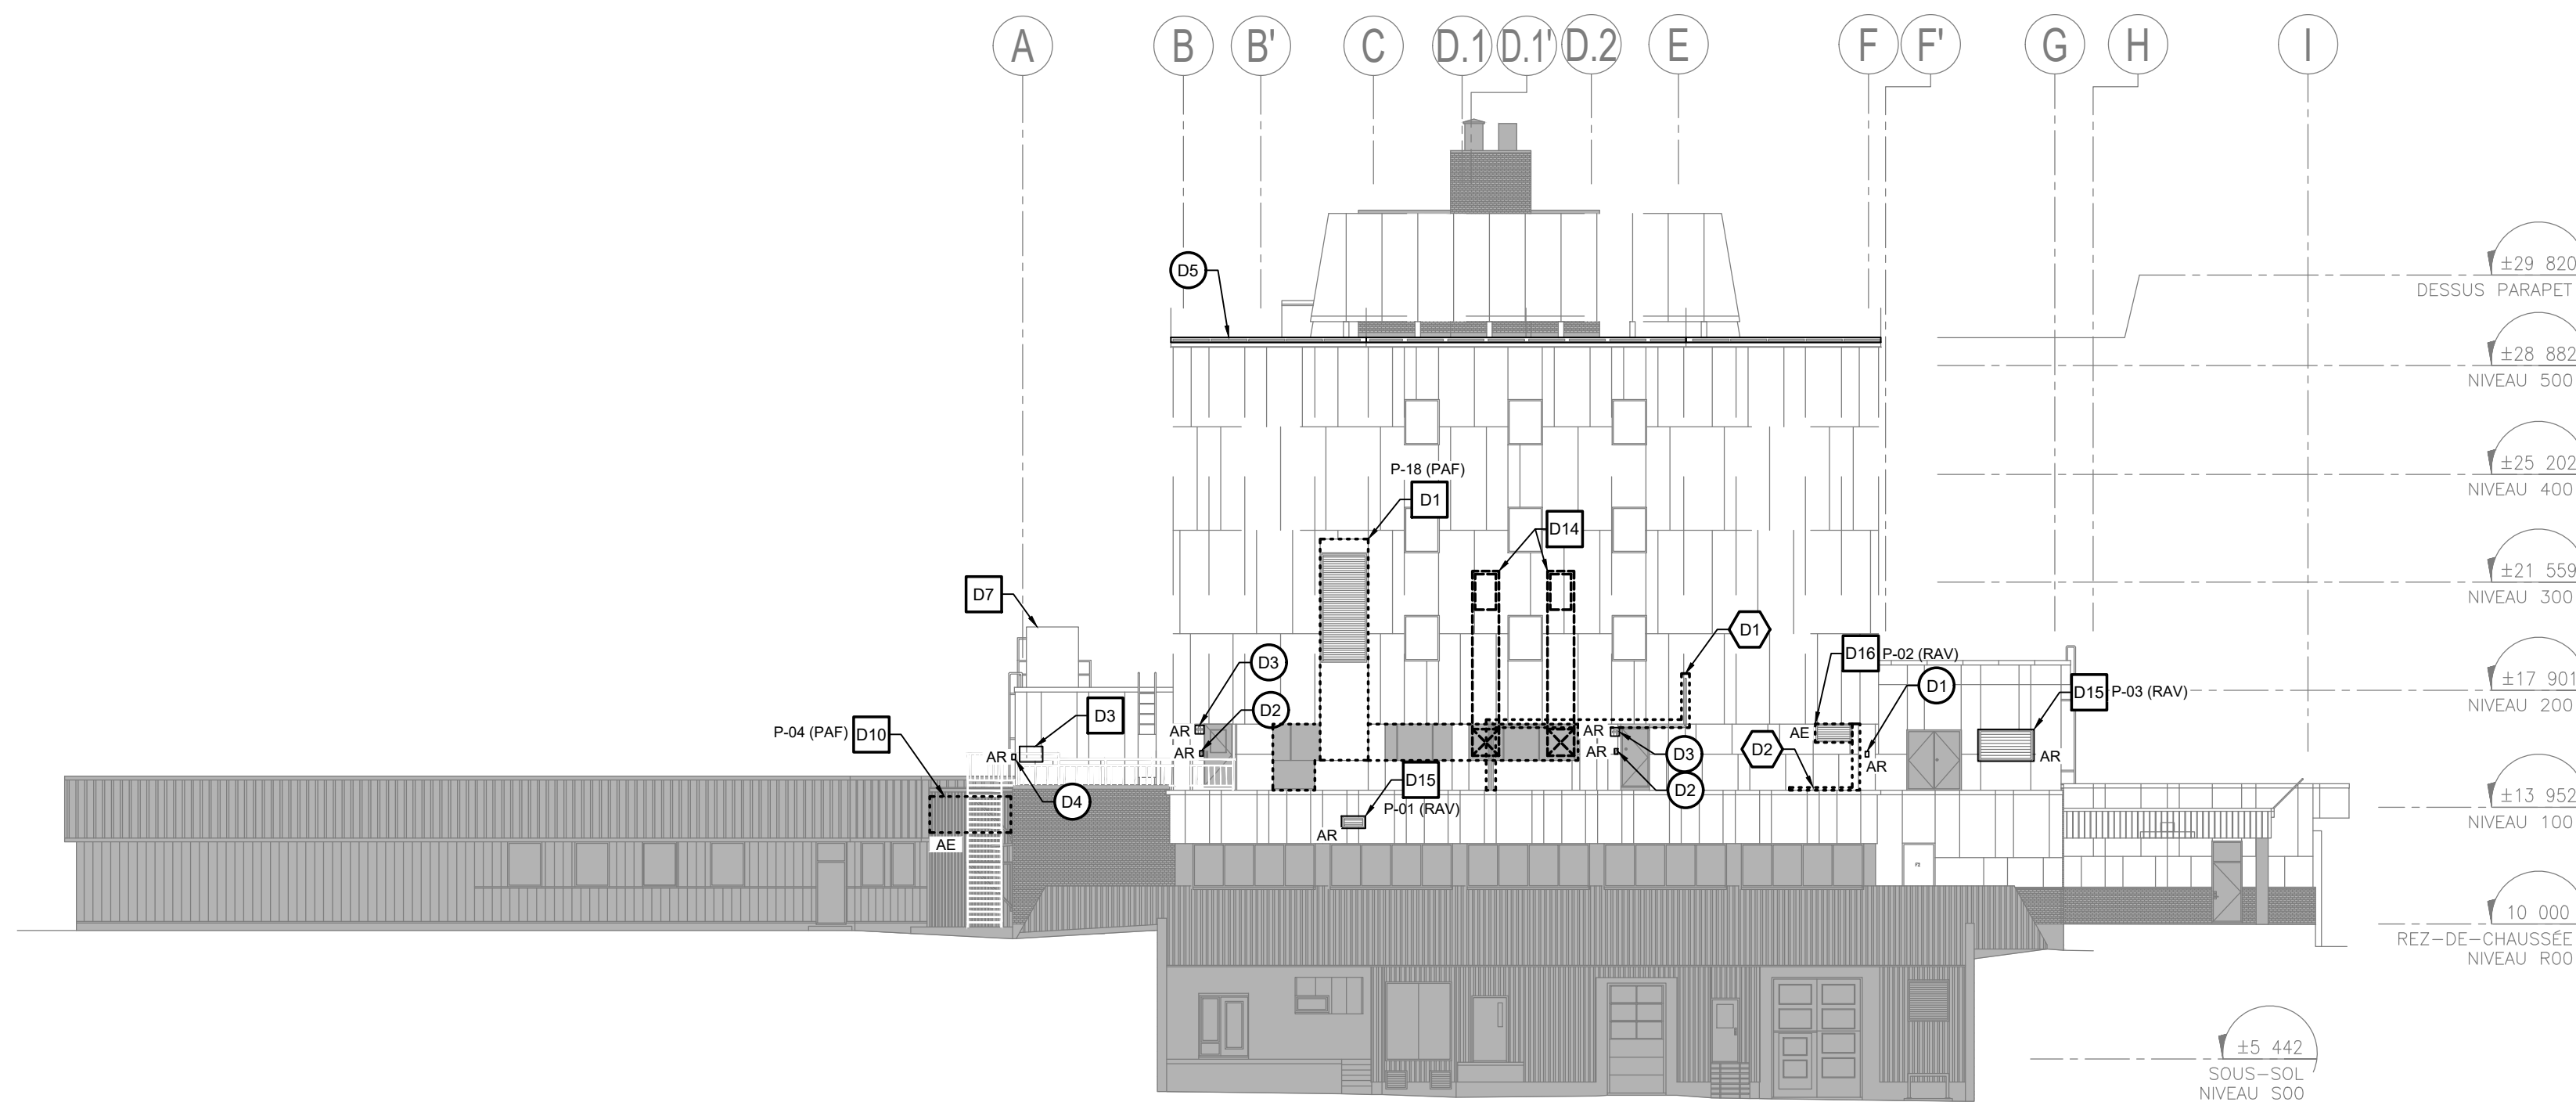

ÉCHELLE: 1:200

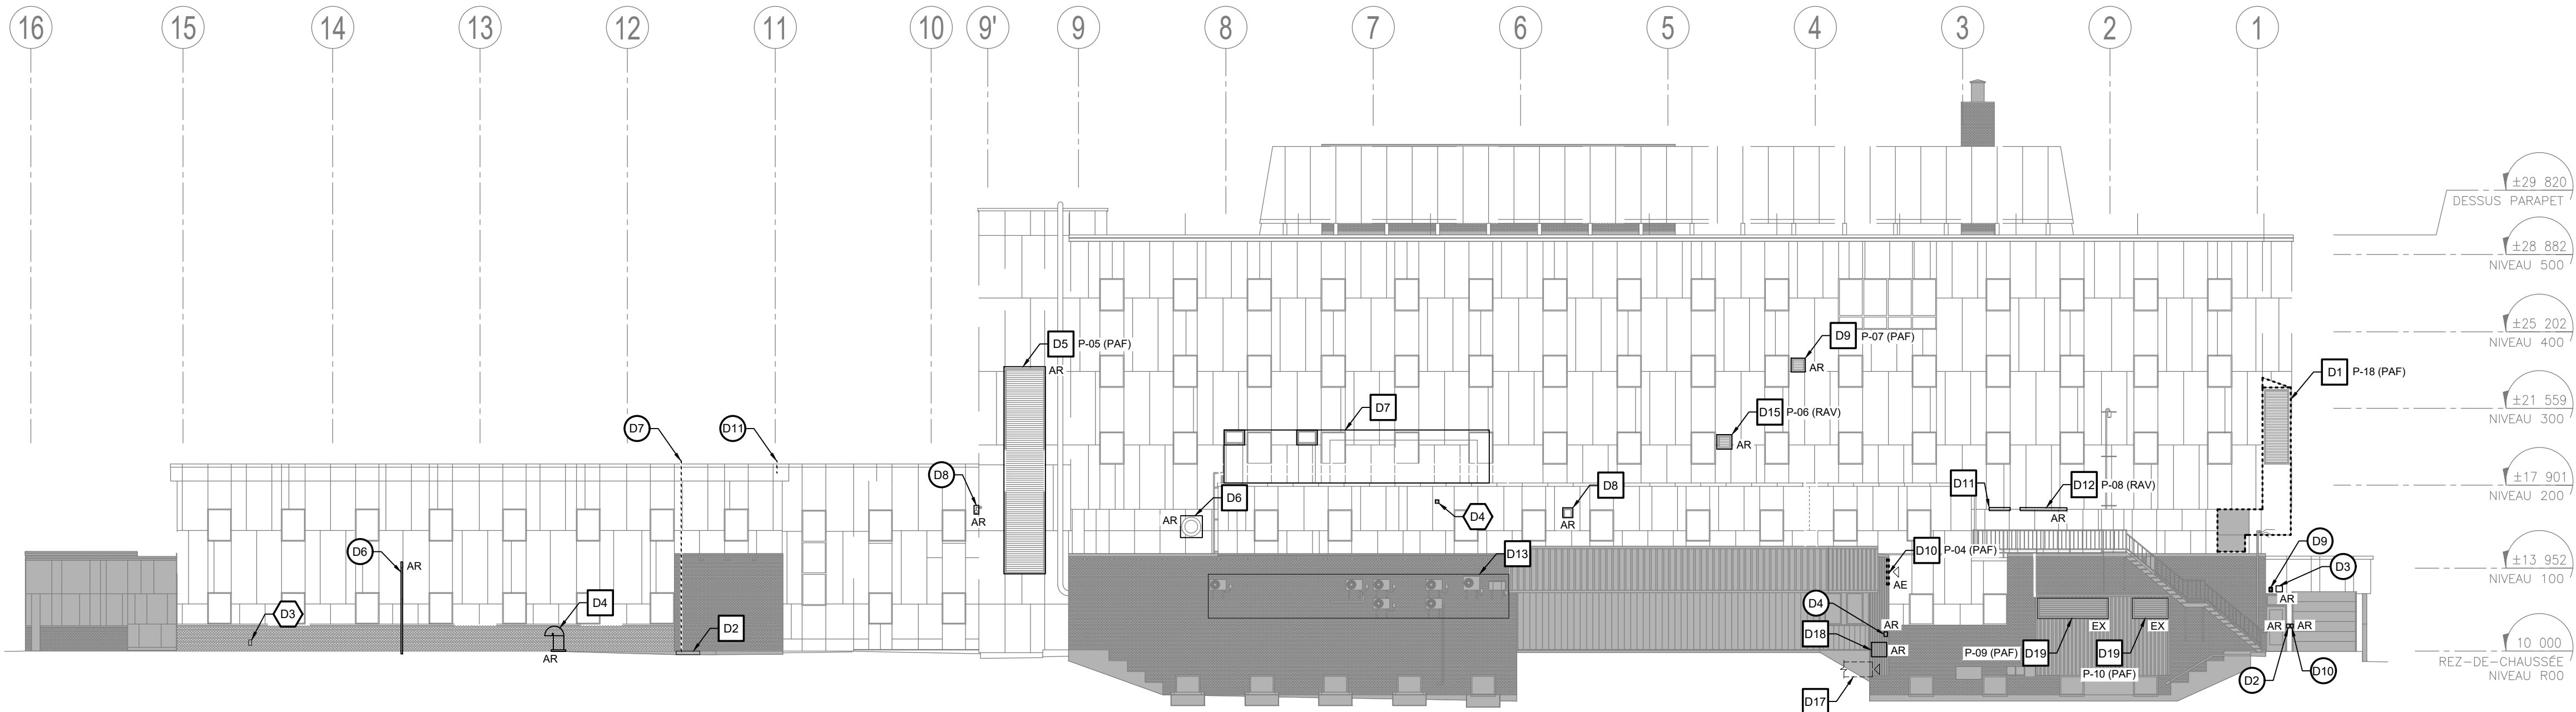

ÉCHELLE: 1:200

- (D1) THERMOSTAT POUR CÂBLES CHAUFFANTS À ENLEVER TEMPORAIREMENT LE TEMPS DES TRAVAUX ET À RÉINSTALLER SUR LA COLONNE APRÈS LES TRAVAUX DE RÉVÊTEMENT. CONDUIT ENT À REMPLACER ET À DISSIMULER AU-DESSUS DU SOFFITE JUSQU'À L'ENTRÉE DE LA SALLE DE MÉCANIQUE.
- (D2) LECTEURS DE CARTE À ENLEVER TEMPORAIREMENT LE TEMPS DES TRAVAUX. ENTREPOSER ADÉQUATEMENT.
- (D3) LUMINAIRES MURAUX À ENLEVER TEMPORAIREMENT LE TEMPS DES TRAVAUX. ENTREPOSER ADÉQUATEMENT.
- (D4) SECTIONNEUR THERMOPOMPE 208V/1P À ENLEVER TEMPORAIREMENT LE TEMPS DES TRAVAUX.
- (D5) LUMINAIRE MURAL LINÉAIRE C/A SUPPORT À ENLEVER TEMPORAIREMENT LE TEMPS DES TRAVAUX. ENTREPOSER ADÉQUATEMENT.
- (D6) LAMPADAIRE STATIONNEMENT À ENLEVER TEMPORAIREMENT LE TEMPS DES TRAVAUX DU SECTEUR. LE LAMPADAIRE DOIT ÊTRE EN FONCTION À TOUS LES SOIRS.
- (D7) ANTENNE AU TOIT C/A CONDUIT PVC À ENLEVER.
- (D8) CAMÉRA EXTÉRIEURE À RÉLOCALISER TEMPORAIREMENT LE TEMPS DES TRAVAUX. LE CHAMP DE LA CAMÉRA DOIT RESTER LE MÊME. LA COUPURE DE SERVICE DOIT ÊTRE LE PLUS COURT POSSIBLE. COORDONNER LE TOUT AVEC LE PROPRIÉTAIRE.
- (D9) PRISE ÉLECTRIQUE EXTÉRIEURE À DÉMANTÉLER. CIRCUIT EXISTANT À COORDONNER AVEC LES ÉQUIPEMENTS EXISTANTS ENCORE RACCORDÉS DANS LE GARAGE DES AMBULANCES.
- (D10) CLAVIER DE PORTE DE GARAGE À ENLEVER TEMPORAIREMENT LE TEMPS DES TRAVAUX. ENTREPOSER ADÉQUATEMENT.
- (D11) CÂBLE DE PARATONNERRE À ENLEVER.

D1 CONDUIT DE PRISE D'AIR FRAIS EN SURFACE À L'EXTÉRIEUR DU BÂTIMENT, DESSERVANT LA VENTILATION DU BLOC OPÉRATOIRE, À GARDER EN FONCTION DURANT TOUTE LA DURÉE DES TRAVAUX. AFIN DE RÉALISER LES TRAVAUX DE RÉFÉCTION DE FAÇADE DERRIÈRE LE CONDUIT EXISTANT, UNE INSTALLATION DE CONDUITS TEMPORAIRES D'AIR FRAIS DOIT ÊTRE MISE EN PLACE PAR L'ENTREPRENEUR EN PARALLÈLE DU CONDUIT EXISTANT ET DES TRAVAUX EN PLUSIEURS ÉTAPES SONT À PLANIFIER. VOIR VOS AGRANDISSEMENTS EN PLANS.

D2 PERSIENNE DE RENOVI D'AIR FRAIS EXISTANTE À CONSERVER, LOCALISÉE À L'INTÉRIEUR D'UN SAUT-DE-LOUP EN BÉTON. LE SYSTÈME D'ÉVACUATION DE L'ATELIER DE MENUISERIE SERA MIS À L'ARRÊT DURANT TOUTE LA DURÉE DES TRAVAUX DE CE SECTEUR.

D3 UNITÉ EXTÉRIEURE SYSTÈME BI-BLOC DE LA SALLE D'OBSERVATION, INSTALLÉE SUR LE GARDE-CORPS EXISTANT, À ENLEVER TEMPORAIREMENT ET À REINSTALLER SUR LE GARDE-CORPS MODIFIÉ À LA FIN DES TRAVAUX.

D4 COC DE CYGNE EXTÉRIEUR SERVANT À L'ÉVACUATION DE L'ATELIER GBM À ENLEVER TEMPORAIREMENT ET À REINSTALLER APRÈS LES TRAVAUX DE RÉFÉCTION DE FAÇADE.

D5 PERSIENNE DE PRISE D'AIR FRAIS EXISTANTE À RELOCALISER ET PLENUM À PROLONGER SELON L'ÉPAISSEUR DE L'ENVELOPPE EXTÉRIÈRE.

D6 VENTILATEUR D'ÉVACUATION MURAL EXTÉRIEUR (CLOCHE) DESSERVANT LA SALLE DE MÉCANIQUE DE STÉRILISATION, À ENLEVER TEMPORAIREMENT ET À REINSTALLER APRÈS LES TRAVAUX DE RÉFÉCTION DE FAÇADE. PROLONGER LE CONDUIT À L'INTÉRIEUR DU MUR EXTÉRIEUR.

D7 UNITÉ DE VENTILATION AU TOIT EXISTANTE À CONSERVER, DESSERVANT LE SECTEUR D'HEMODYALYSE ET DU LABORATOIRE. TROIS CONDUITS TRAVERSANT LE PAREMENT À MODIFIER DE FAÇON À GARDER L'UNITÉ EN FONCTION DURANT LES TRAVAUX. STRUCTURE DE PARSERELLE D'ACCÈS EN ALUMINIUM À ENLEVER TEMPORAIREMENT ET À MODIFIER POUR REINSTALLATION PAR L'ENTREPRENEUR GÉNÉRAL. UNE INSTALLATION DE CONDUITS TEMPORAIRES D'ALIMENTATION ET DE RETOUR D'AIR FRAIS DOIT ÊTRE MISE EN PLACE AVANT LES TRAVAUX DE DÉMOLITION DE L'ENVELOPPE.

D8 SORTIE D'AIR MURALE DU SECTEUR DU LABORATOIRE, À REMPLACER. UN CONDUIT D'ÉVACUATION TEMPORAIRE DOIT ÊTRE INSTALLÉ ET PROLONGÉ JUSQU'À L'EXTÉRIEUR DES ÉCHAFFAUDAGES POUR CONSERVER LA SORTIE EN FONCTION.

D9 PERSIENNE DE PRISE D'AIR FRAIS DU SYSTÈME D'APPORT D'AIR FRAIS SUPPLÉMENTAIRE DU SECTEUR DES SOINS INTENSIFS, À ENLEVER TEMPORAIREMENT ET À RELOCALISER.

D10 PERSIENNE DE PRISE D'AIR FRAIS DU SERVICE ALIMENTAIRE AU SOUS-SOL, À REMPLACER. LA PERSIENNE EST LOCALISÉE DANS UN SOUFFLAGE DE TÔLE À REMPLACER PAR L'ENTREPRENEUR GÉNÉRAL (VOIR ARCHITECTE).

D11 TRAPPES D'ACCÈS POUR MÉCANIQUE, À REMPLACER.

D12 PERSIENNE SOUS PORTE-A-FAUX, DESSERVANT DES ÉVACUATIONS DU NIVEAU 100, ÉVACUATION DES LABORATOIRES ET ÉVACUATION DU SYSTÈME DU BLOC OPÉRATOIRE, À ENLEVER TEMPORAIREMENT ET À RELOCALISER.

D13 UNITÉS EXTÉRIEURES DE DIVERS SYSTÈMES BI-BLOCS EXISTANTS À CONSERVER ET À GARDER EN FONCTION DURANT TOUTE LA DURÉE DES TRAVAUX.

D14 PROFIL DES CONDUITS DE PRISE D'AIR TEMPORAIRE DU BLOC OPÉRATOIRE À TITRE INFORMATIF (Z 900X90MM) À FOURNIR, INSTALLER ET RACCORDER AU PLENUM DE PRISE D'AIR FRAIS MÔS LE SOFFITE PAR L'ENTREPRENEUR (EN PLUSIEURS ÉTAPES) AFIN DE PERMETTRE LES TRAVAUX DE REVÊTEMENT DERRIÈRE LE CONDUIT EXISTANT SUR LA FAÇADE DE LA TOUR. VOIR VOS AGRANDISSEMENTS EN PLANS.

D15 PERSIENNE DE RENOVI D'AIR FRAIS EXISTANTE À RELOCALISER ET PLENUM À PROLONGER SELON L'ÉPAISSEUR DE L'ENVELOPPE EXTÉRIÈRE.

D16 PERSIENNE DE RENOVI D'AIR FRAIS EXISTANTE À REMPLACER PAR UNE NOUVELLE PERSIENNE MOINS LAIDE POUR LIBÉRER L'ESPACE REQUIS AUX TRAVAUX DE L'ENVELOPPE EXTÉRIÈRE.


D17 EMPLOIEMENT DE CENTRE D'AIR DU SERVICE ALIMENTAIRE AU SOUS-SOL DERRIÈRE LE SOUFFLAGE DE TÔLE EXISTANT. LE CONDUIT SERA À MODIFIER POUR L'AJOUT D'UN REGISTRE COUPE-FLU (VOIR VOS AGRANDISSEMENTS EN PLANS).

D18 UNITÉ EXTÉRIÈRE DU SYSTÈME BI-BLOC DE LA SALLE DE MAMMOGRAPHIE, À ENLEVER TEMPORAIREMENT ET À REINSTALLER AU MEME ENDROIT APRÈS LES TRAVAUX DE MODIFICATION DU SOUFFLAGE DE TÔLE (VOIR ARCHITECTE).

D19 PERSIENNES DE PRISE D'AIR FRAIS, NON TOUCHÉES PAR LES TRAVAUX, À ENLEVER AVEC PRÉ-FITTE TEMPORAIRE DURANT LES TRAVAUX SUR CETTE FAÇADE.


D1	ÉVÉNEMENTS DE VAPEUR POUR AUTOCLAVE LOCALISÉ AU SOUS-SOL, À RELOCALISER AVANT LE DÉBUT DES TRAVAUX DE LA FAÇADE OUEST. PROLONGER LA TYPAUTERIE EXTERIEURE SUR DES SUPPORTS TEMPORAIRES DÉPOSÉS EN TOITURE JUSQU'AU SUD-OUEST DU BÂTIMENT. VOIR VOS AGRANDISSEMENTS EN PLAN.
D2	ÉVÉNEMENTS DE VAPEUR EN INOX AVEC DRAIN DE CONDENSATS À MODIFIER.
D3	SORTIE D'ARRASAGE EXTERIEURE À CONSERVER ET À PROTÉGER.
D4	SORTIE D'ÉVENT MURALE DE LABORATOIRE AVEC COLÈNE VERS LE BAS #500. TYPAUTERIE EN ACIER INOXYDABLE À PROLONGER SELON L'ÉPAISSEUR DU REVÊTEMENT.

\\corp.phon.net\cadda5\cant1\PEP\projets\2026\11\CA0066110\3236\Bailment05 TECH04.1 CAO

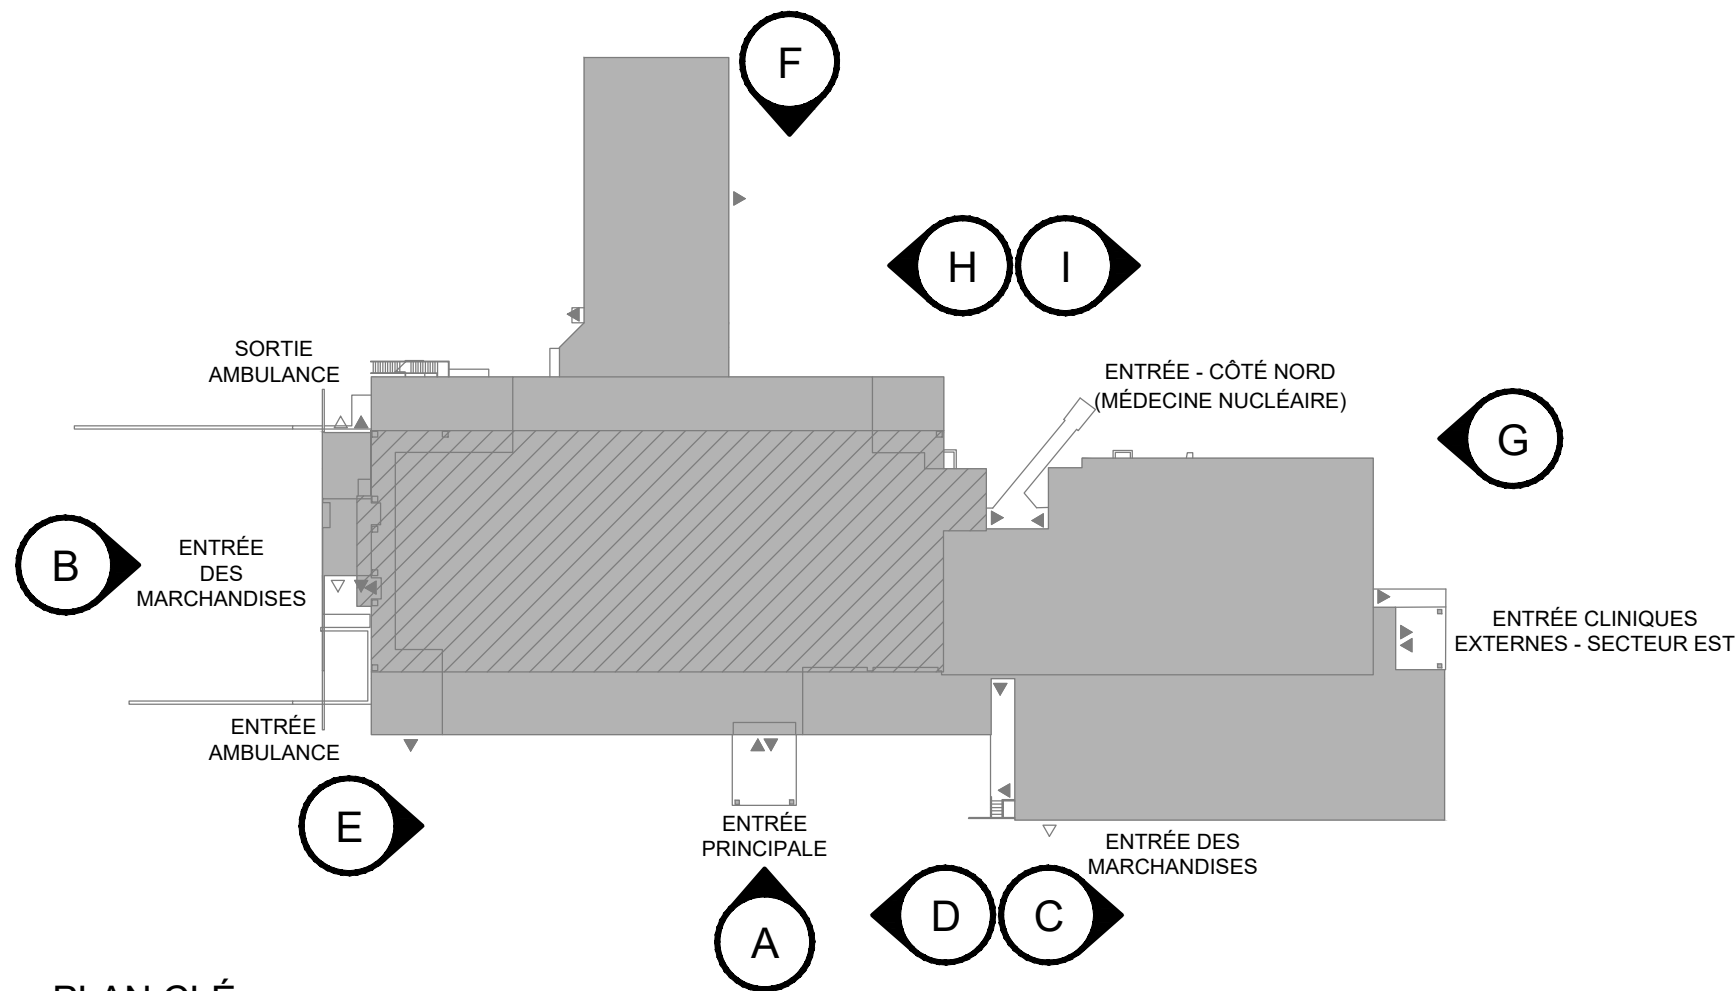


PLAN CLÉ

ÉCHELLE: AUCUNE

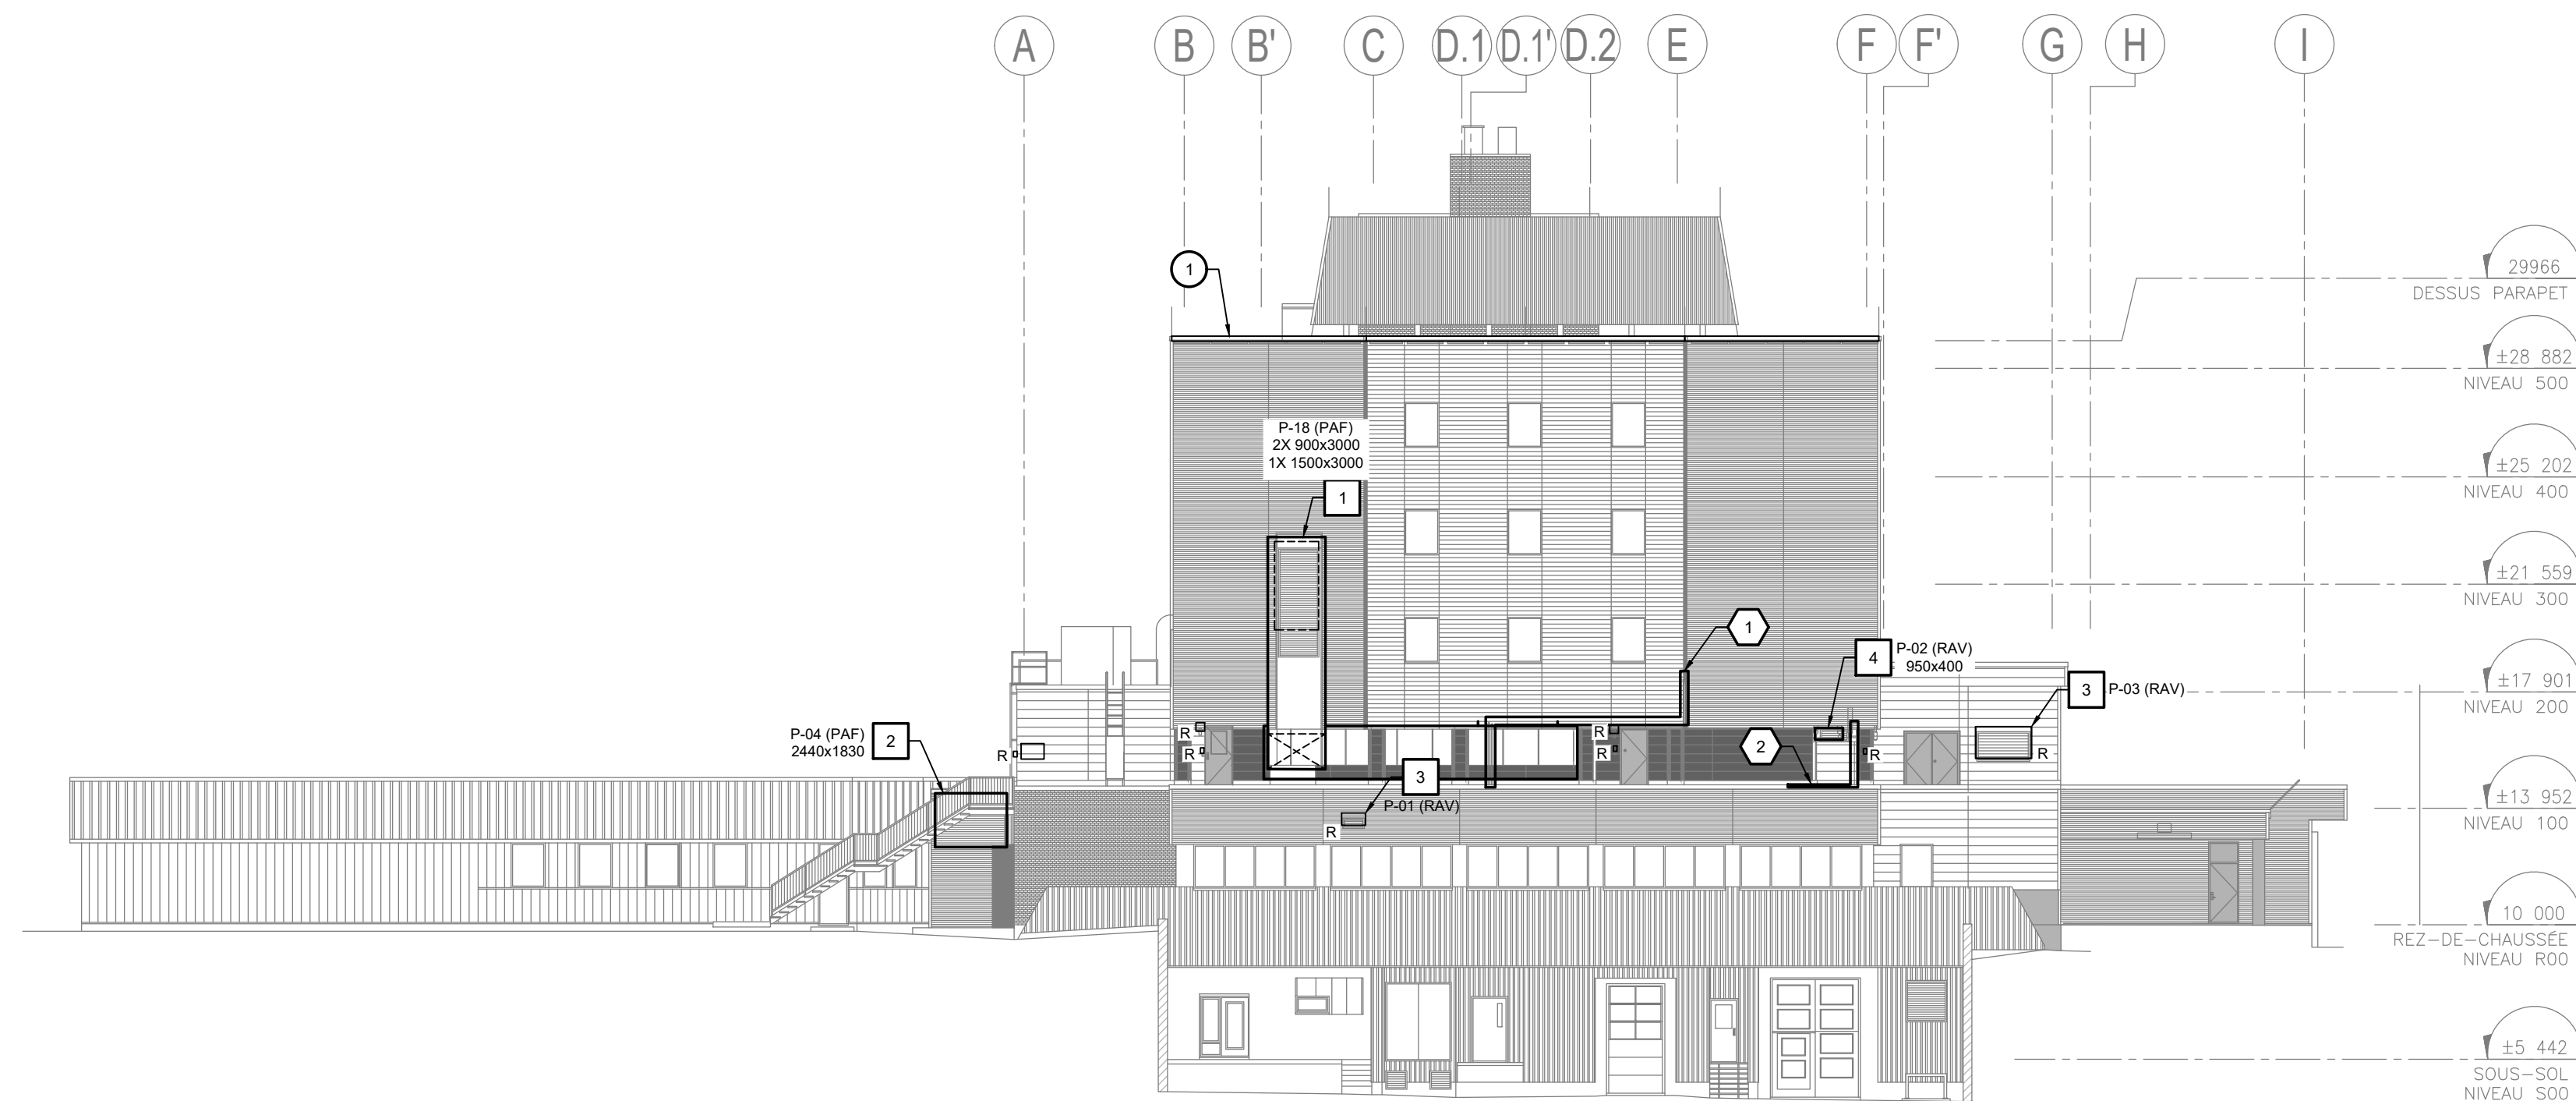

ÉLEVATION OUEST - CONSTRUCTION

ÉCHELLE: 1:200

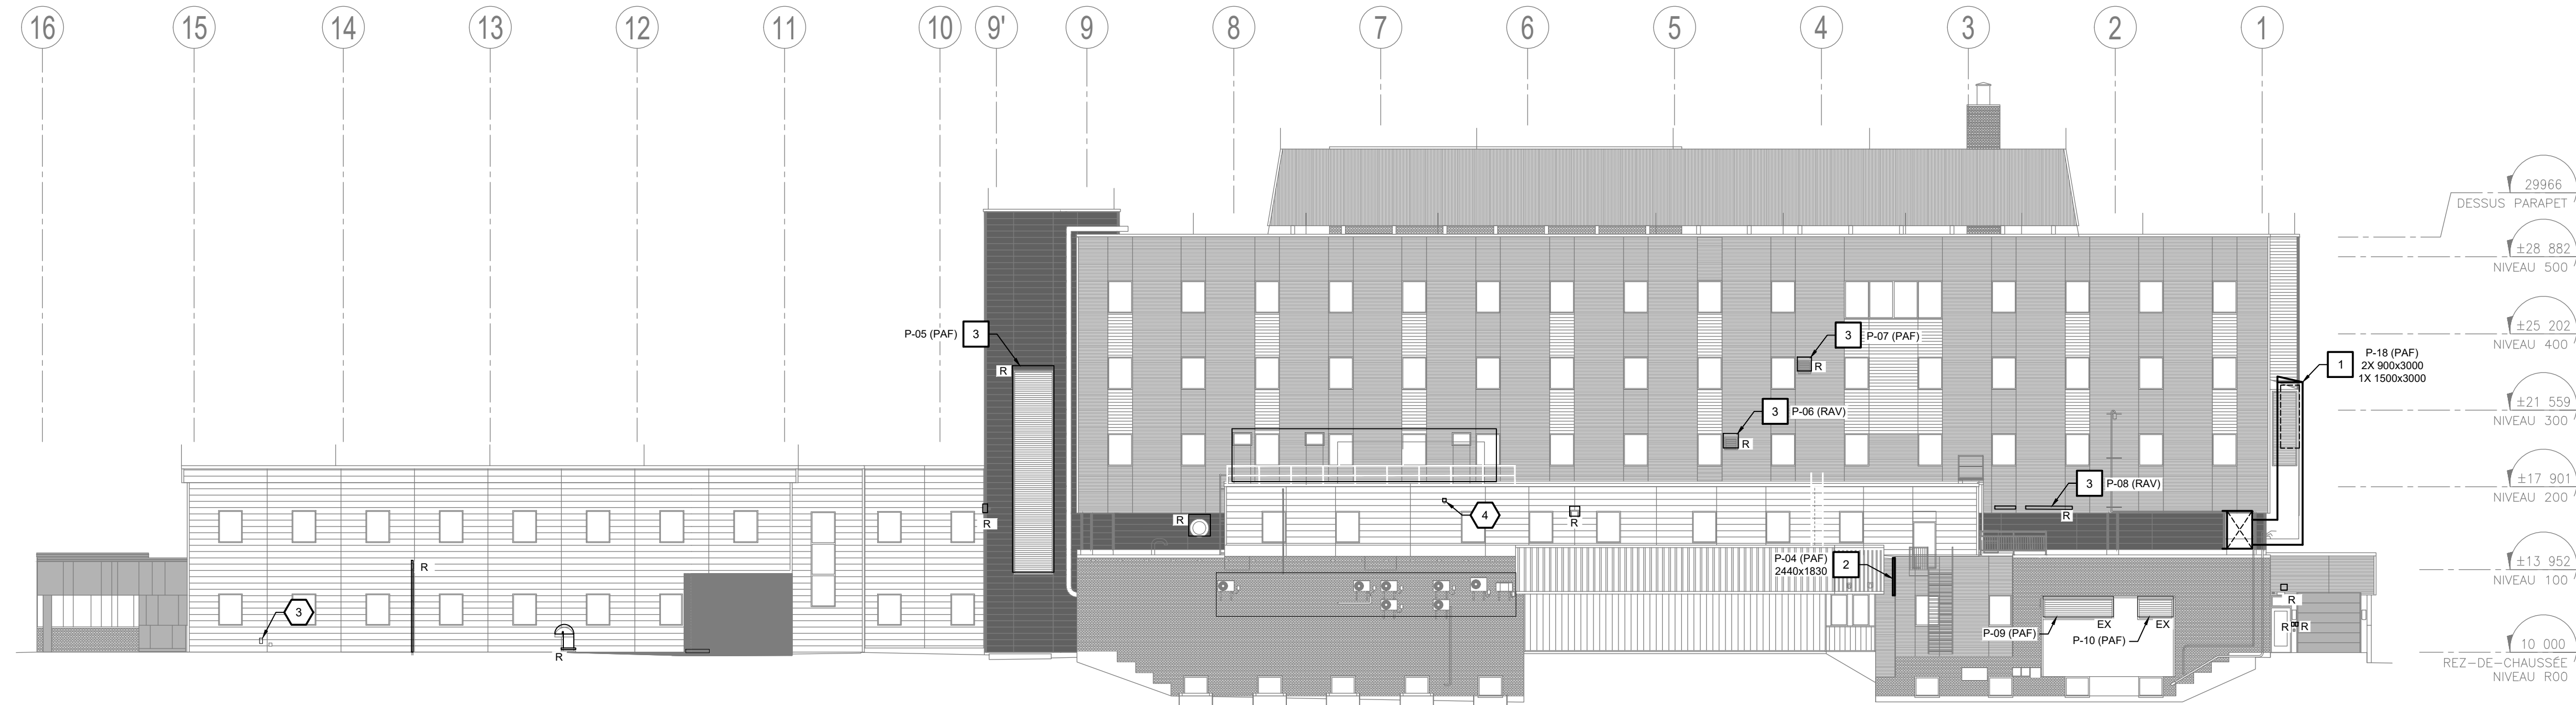

ÉLEVATION NORD - CONSTRUCTION

ÉCHELLE: 1:200

NOTE CONSTRUCTION - ÉLECTRICITÉ

- SÉRIE DE LUMINAIRES MURAUX À RÉINSTALLER AU MÊME ENDROIT SUR LE CÔTÉ DU NOUVEAU PARAPET OU SUR LE MUR EXTÉRIEUR (SELON LE CAS) APRÈS LES TRAVAUX DE REVÊTEMENT. CONSERVER L'AJUSTEMENT DE L'ANGLE DES LUMINAIRES.

NOTES CONSTRUCTION - VENTILATION

- NOUVEAU CONDUIT DE PRISE D'AIR FRAIS DU BLOC OPÉRAITOIRE. 1950X1200MM. À MONTER JUSQU'À UNE HAUTEUR DE 8.5M AU-DESSUS DU NIVEAU DU TOIT. CONSERVER UN ESPACE DE 200MM ENTRE LE CONDUIT ET LE MUR DERRIÈRE. INSTALLER LE CONDUIT APRÈS QUE LA FIN DES TRAVAUX DE REVÊTEMENT DERRIÈRE LE CONDUIT. CONSERVER LES CONDUITS TEMPORAIRES EN PARALLÈLE JUSQU'À LA MISE EN SERVICE DU NOUVEAU CONDUIT. VOIR VUES AGRANDIES EN PLANS.
- NOUVELLE PERSIENNE D'AIR NEUF DU SERVICE ALIMENTAIRE DE DIMENSIONS DIFFÉRENTES À INSTALLER DANS LE SOUFFLAGE DE TÔLE CONSTRUIT PAR L'ENTREPRENEUR GÉNÉRAL (VOIR ARCHITECTE). L'ENTRÉE D'AIR DU CONDUIT DANS LE BÂTIMENT SE FAIT AU SOUS-SOL (VOIR VUES AGRANDIES).
- PERSIENNE EXISTANTE À RÉINSTALLER APRÈS LES TRAVAUX DE REVÊTEMENT.
- NOUVELLE PERSIENNE D'AIR VICIÉE DE DIMENSIONS DIFFÉRENTES AVEC NOUVEAU PLENUM ET VOLET MOTORISÉ (VOIR VUES AGRANDIES EN PLANS).

NOTES CONSTRUCTION - PLOMBERIE

- ÉVÉNEMENTS DE VAPEUR POUR AUTOCLAVE LOCALISÉ AU SOUS-SOL. À RÉINSTALLER AU MÊME ENDROIT À LA FIN DES TRAVAUX. MODIFIER LES LONGUEURS DE TUYAUTERIE SELON LA NOUVELLE ÉPAISSEUR DE L'ENVELOPPE EXTÉRIEURE.
- ÉVÉNEMENTS DE VAPEUR EN INOX AVEC DRAIN DE CONDENSATS. PROLONGÉS SELON LA NOUVELLE ÉPAISSEUR DE L'ENVELOPPE EXTÉRIEURE. DRAIN DE CONDENSATS À RÉPARER EN NEUF JUSQU'AU DRAIN DE TOITURE LE PLUS PRÈS (EN SURFACE TEL QUE L'EXISTANT).
- SORTIE D'ARROSAGE EXTÉRIEURE CONSERVÉE EMBOÎTÉE DANS UNE ALCÔVE DANS LE NOUVEAU REVÊTEMENT (PAR L'ENTREPRENEUR GÉNÉRAL. VOIR ARCHITECTE).
- SORTIE MURALE D'ÉVÉNEMENT DE LABORATOIRE PROLONGÉE.



SANTÉ QUÉBEC GASPÉSIE

RÉF. CLIENT:

PROJET

HÔPITAL DE CHANDLER
(RÉFECTION DE L'ENVELOPPE)

Architecte




CE DOCUMENT NE DOIT PAS SERVIR À
LA CONSTRUCTION

REV	DATE	DESCRIPTION	PAR
RÉVISIONS PARTIELLES			
1	2026/09/04	DÉFINITIFS POUR SOUMISSION	JD/JA
B	2026/08/21	DÉFINITIFS 100% POUR APPROBATION	JD/VS
A	2026/05/14	DÉFINITIFS 60% POUR APPROBATION	JD/VS
REV	DATE	DESCRIPTION	PAR

SCEAU:	
MÉCANIQUE	ÉLECTRICITÉ
AVERTISSEMENT: DROIT D'AUTEUR: CE DESSIN EST LA PROPRIÉTÉ INTELLECTUELLE DE WSP CANADA INC. AUCUNE RÉVISION, REPRODUCTION OU TOUT AUTRE USAGE N'EST PERMIS SANS L'AUTORISATION ÉCRITE DE WSP CANADA INC. L'ENTREPRENEUR DEVRA VÉRIFIER TOUTES LES DIMENSIONS AUX PLANS ET FAIRE LOCALISER TOUS LES SERVICES D'UTILITÉS PUBLIQUES ET RAPPORTER TOUTES ERREURS OU OMISSIONS AVANT DE COMMENCER LES TRAVAUX.	
ÉCHELLE: ORIGINALE: INDIQUÉE DESSINÉ PAR: A. CASTONGUAY & A. HALLÉ PRÉPARÉ SOUS SUPERVISION PAR: J. D'AMOURS ET V. STOCKMEYER, ing. PRÉPARÉ PAR: J. D'AMOURS ET J. ALCINDOR, ing. APPROUVÉ ADMINISTRATIVEMENT PAR: S. LAVOIE	DATE: AVRIL 2026 SI CETTE BARRE NE MESURE PAS 25 mm, AJUSTER VOTRE ÉCHELLE DE TRAPAGE: 25mm
DISCIPLINE: MÉCANIQUE / ÉLECTRIQUE	


Mécanique / Électricité
NO PROJET: CA0066110.3235
TITRE: ÉLEVATIONS NORD / OUEST CONSTRUCTION
NUMÉRO DU FEUILLET: ME001

\\corp.phwan.net\caddas\cant1\PRJ\projets\2026\11\CA00661\10-3236\Bâtiment05 TECH04.1 CAO

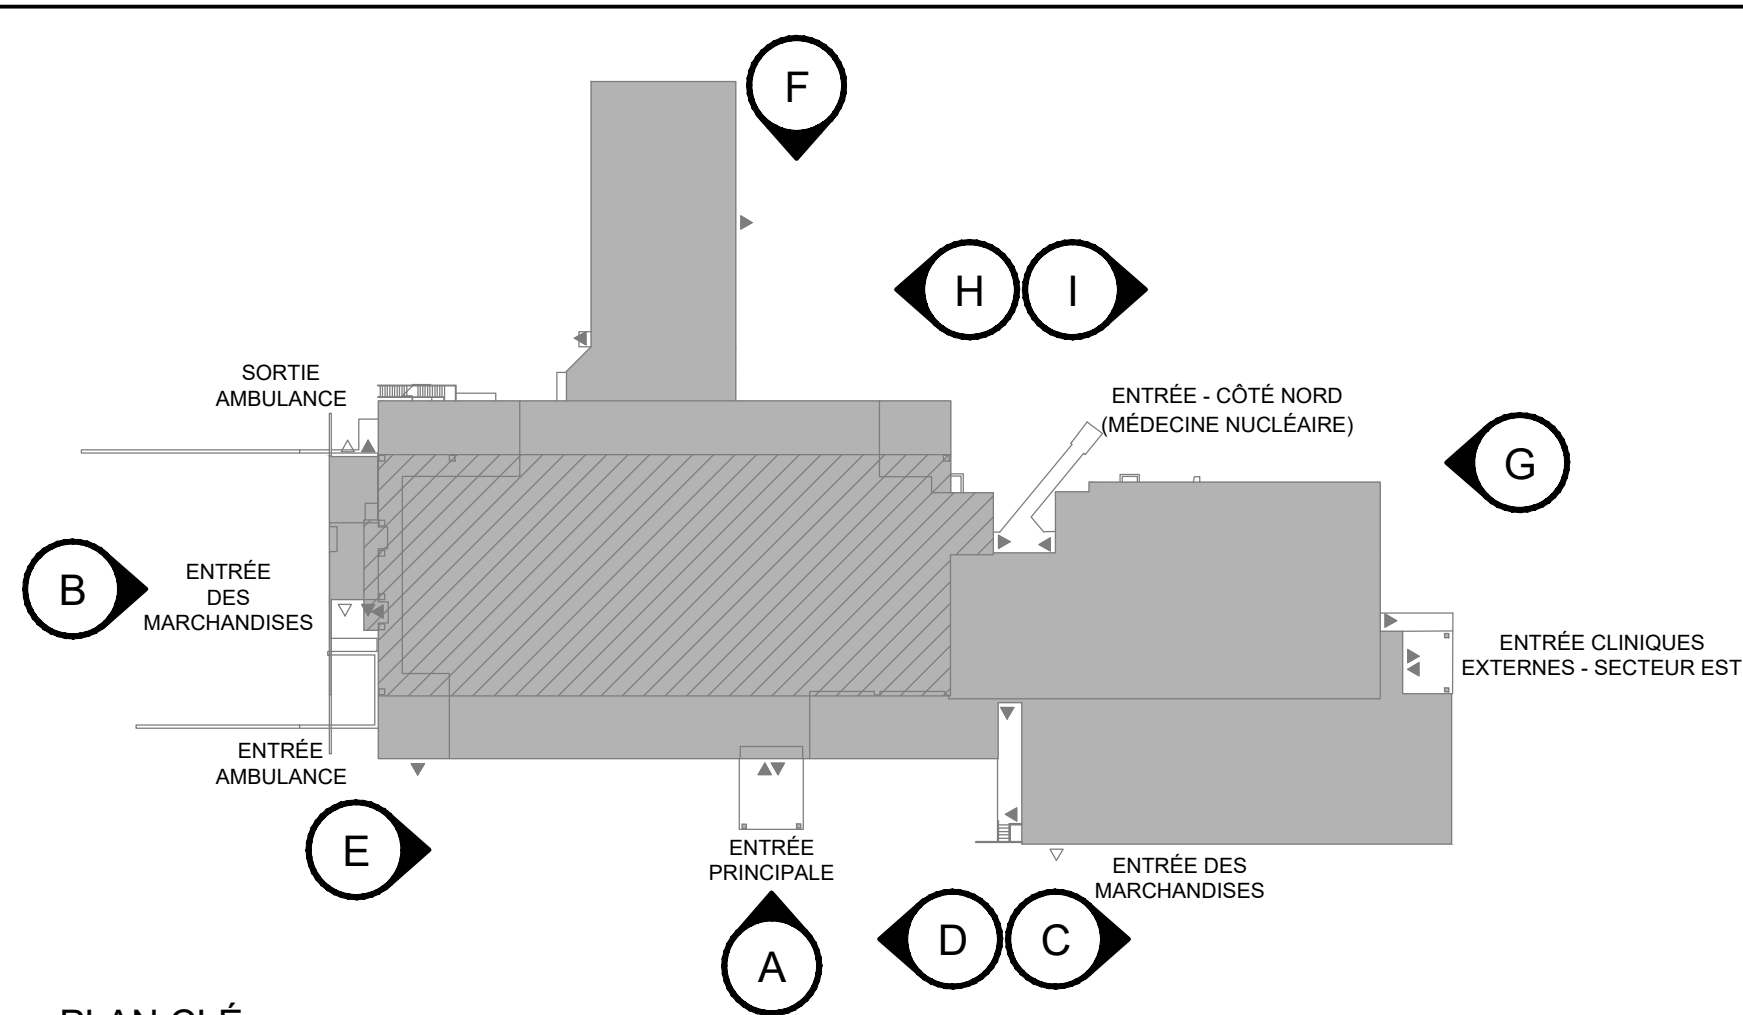


PLAN CLÉ

ÉCHELLE: AUCUNE

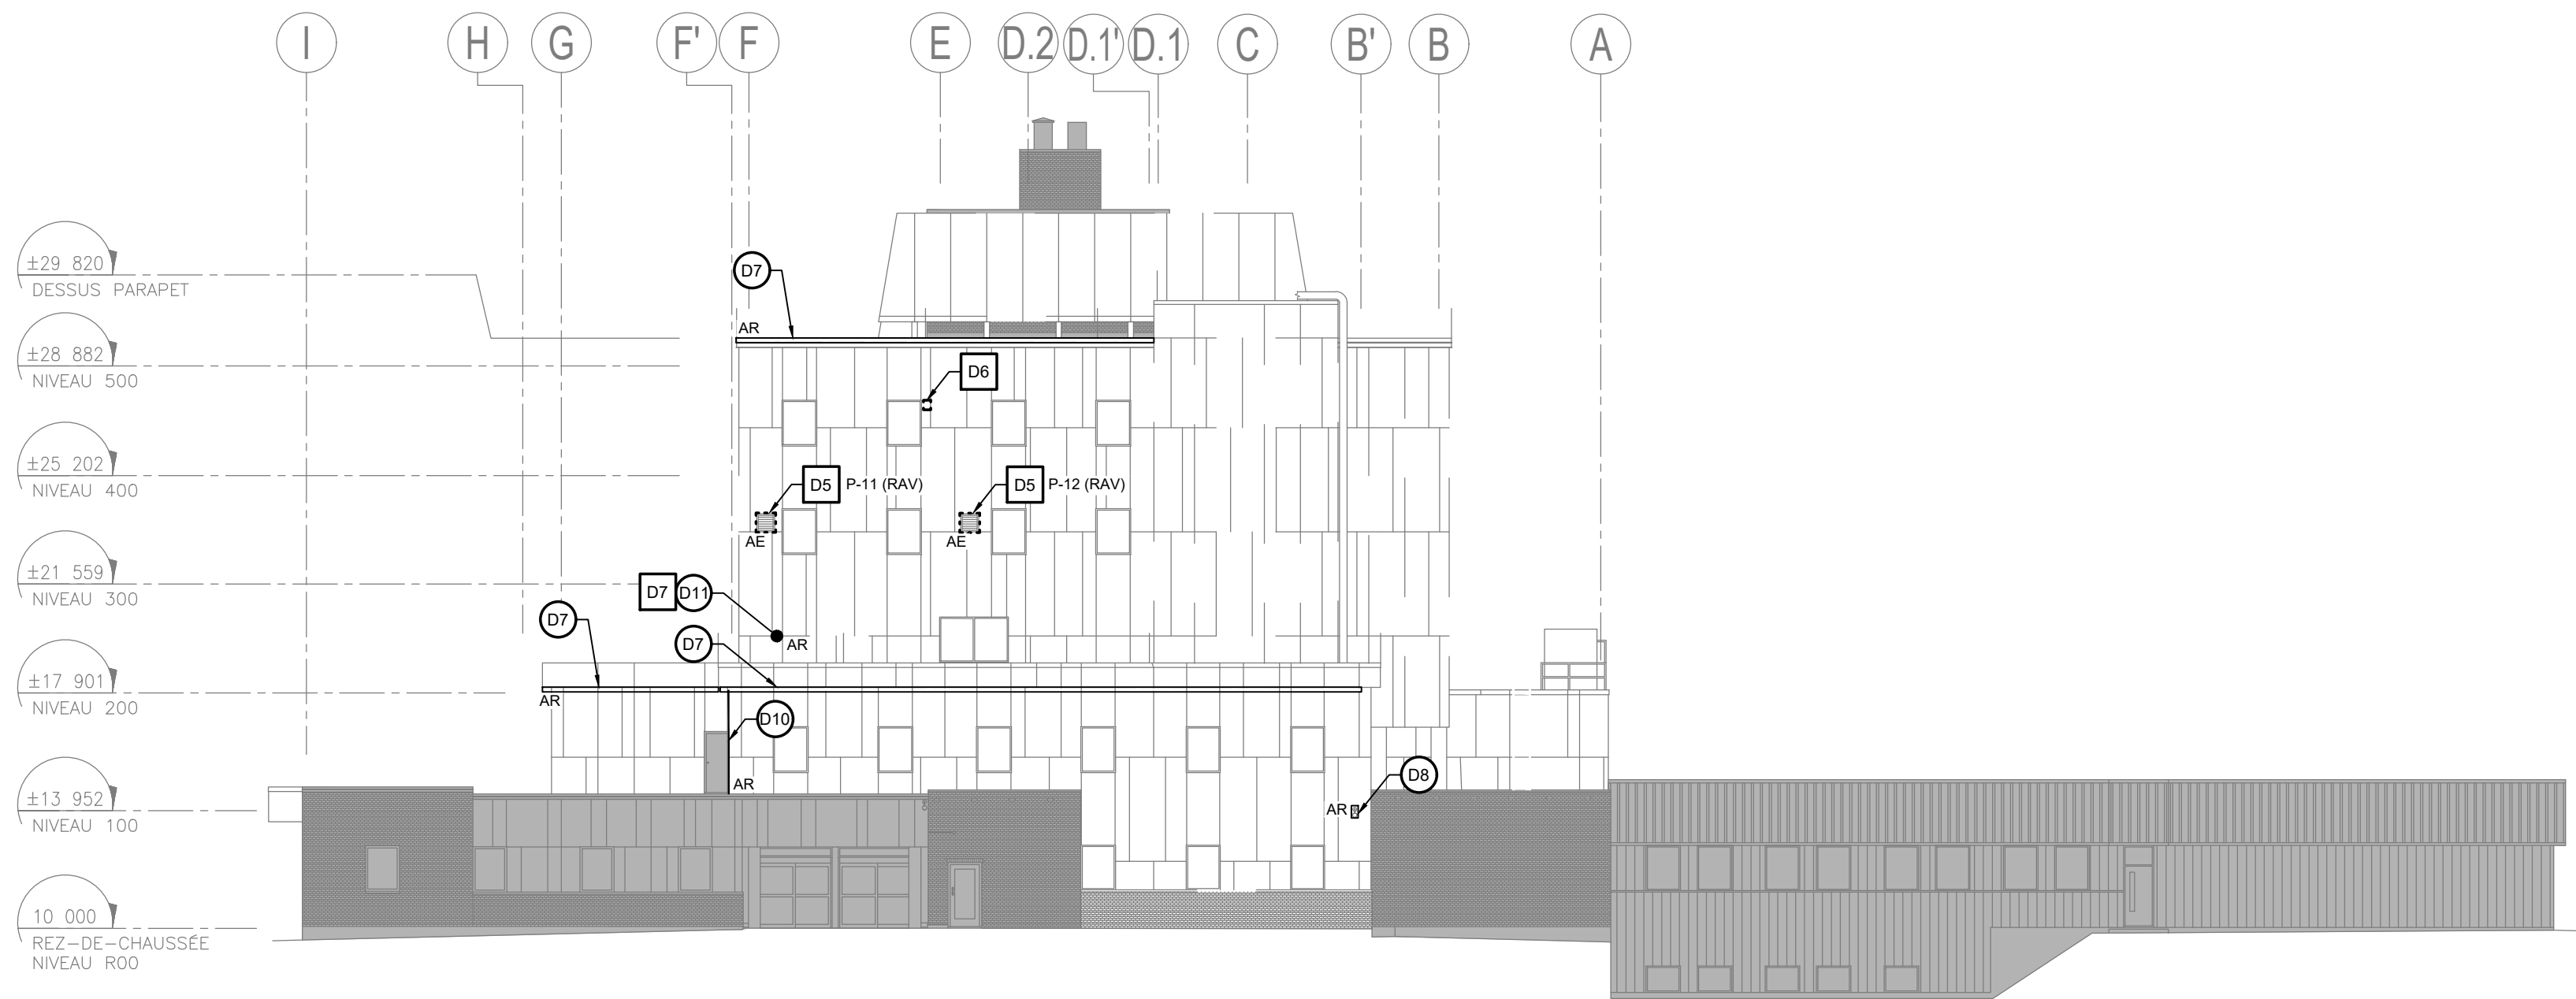

ÉLEVATION EST - DÉMOLITION

ÉCHELLE: 1:200

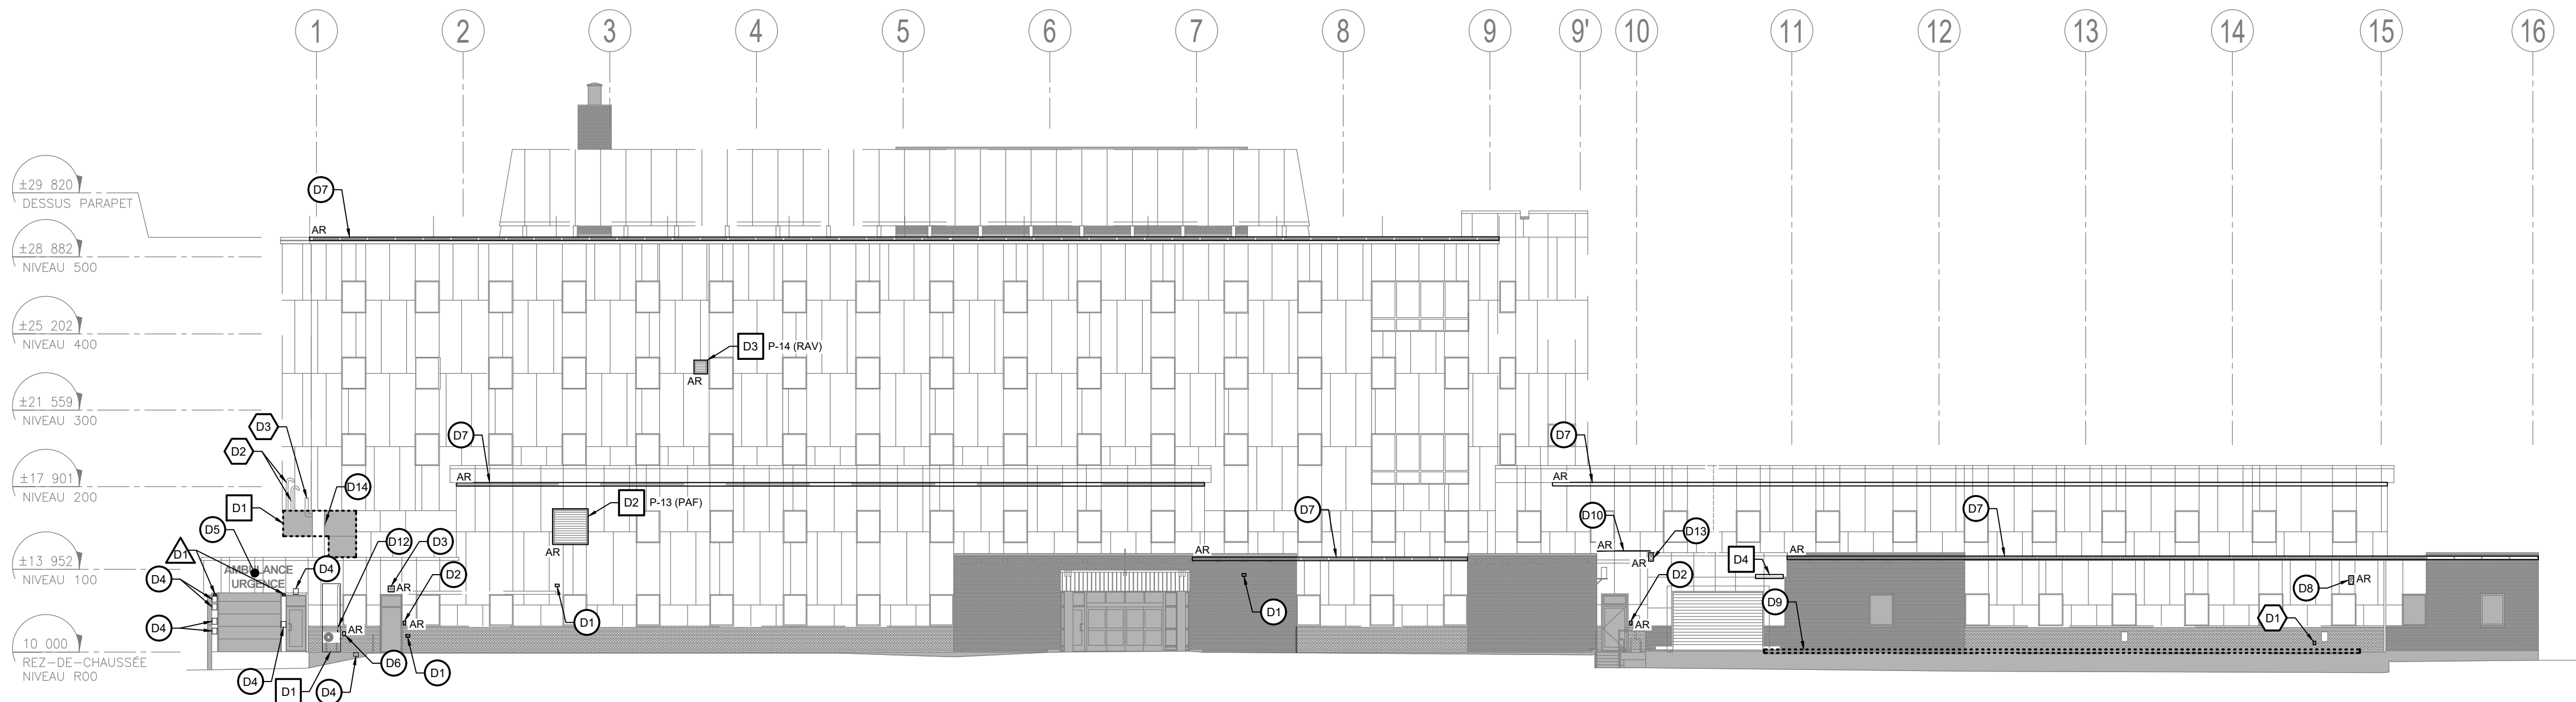

ÉLEVATION SUD - DÉMOLITION

ÉCHELLE: 1:200

NOTES DÉMOLITION - ÉLECTRICITÉ

- D1 PRISES ÉLECTRIQUES À REMPLACER. CONSERVER LE CIRCUIT.
- D2 LECTEURS DE CARTE À ENLEVER TEMPORAIREMENT LE TEMPS DES TRAVAUX. ENTREPOSER ADEQUATEMENT.
- D3 LUMINAIRES MURAUX À ENLEVER TEMPORAIREMENT LE TEMPS DES TRAVAUX. ENTREPOSER ADEQUATEMENT.
- D4 EQUIPEMENT (EX) EXISTANT À CONSERVER.
- D5 ENSEIGNE AMBULANCE URGENCE À DÉBRANCHER PAR L'ÉLECTRICIEN ET À ENLEVER PAR L'ENTREPRENEUR GÉNÉRAL LE TEMPS DES TRAVAUX. VOIR VUES AGRANDIES EN PLAN.
- D6 SECTIONNEUR THERMOPOMPE 208V/1P À ENLEVER TEMPORAIREMENT LE TEMPS DES TRAVAUX.
- D7 LUMINAIRE MURAL LINÉAIRE C/A SUPPORT À ENLEVER TEMPORAIREMENT LE TEMPS DES TRAVAUX. ENTREPOSER ADEQUATEMENT.
- D8 CAMÉRA EXTÉRIEURE À ENLEVER TEMPORAIREMENT LE TEMPS DES TRAVAUX. ENTREPOSER ADEQUATEMENT.
- D9 CONDUIT ET CÂBLAGE DE TÉLÉCOMMUNICATION DÉSUEU NE SERVANT PLUS, À ENLEVER.
- D10 CONDUIT EMT C/A FILAGE POUR LES LUMINAIRES MURAUX LINÉAIRES À ENLEVER TEMPORAIREMENT LE TEMPS DES TRAVAUX.
- D11 CÂBLAGE UNITÉ EXTÉRIEURE BI-BLOC À ENLEVER TEMPORAIREMENT LE TEMPS DES TRAVAUX. ENTREPOSER ADEQUATEMENT.
- D12 CÂBLAGE DÉSUEU NE SERVANT PLUS À ENLEVER (ANCIENNE ENSEIGNE ILLUMINÉE DÉJÀ RETIRÉE).
- D13 CAMÉRA EXTÉRIEURE À RELOCALISER TEMPORAIREMENT LE TEMPS DES TRAVAUX. LE CHAMP DE LA CAMÉRA DOIT RESTER LE MÊME. LA COUPURE DE SERVICE DOIT ÊTRE LE PLUS COURT POSSIBLE. COORDONNER LE TOUT AVEC LE PROPRIÉTAIRE.
- D14 THERMOSTAT POUR CÂBLES CHAUFFANTS À ENLEVER TEMPORAIREMENT LE TEMPS DES TRAVAUX ET À RÉINSTALLER SUR LA COLONNE APRÈS LES TRAVAUX DE REVÊTEMENT. CONDUIT EMT À REMPLACER ET À DISSIMULER AU-DESSUS DU SOFFITE JUSQU'À L'ENTRÉE DE LA SALLE DE MÉCANIQUE.

NOTES DÉMOLITION - VENTILATION

- D1 UNITÉ EXTÉRIEURE SYSTÈME BIBLOC GREE AU R410A DE 12 MBH EXISTANTE, AVEC SON SUPPORT MURAL, À DÉMANTÉLER TEMPORAIREMENT. RÉCUPÉRER LE RÉFRIGÉRANT, PROLONGER LE TUBAGE, LE PROTÉGER ET EFFECTUER UNE REMISE EN MARCHE AFIN DE MAINTENIR L'UNITÉ EN OPÉRATION DURANT LES TRAVAUX. PRÉVOIR UN SUPPORT TEMPORAIRE.
- D2 PERSIENNE DE PRISE D'AIR FRAIS DE L'UNITÉ UT-2 EXISTANTE (± 1 600 × 1 500 MM) À DÉMANTÉLER TEMPORAIREMENT LORS D'UNE COUPURE RAPIDE (NUIT OU FIN DE SEMAINE) AVEC LE REGISTRE MOTORISÉ FERMÉ. PRÉVOIR LA MISE EN PLACE D'UNE FILTRATION ET D'UN GRILLAGE AVIAIRE TEMPORAIRES AFIN DE MAINTENIR LE SYSTÈME EN FONCTION DURANT LES TRAVAUX. LA PERSIENNE EST À RÉCUPÉRER ET RÉINSTALLER.
- D3 PERSIENNE DE RENVOI D'AIR VICIÉ DE LA CHAMBRE À PRESSION NÉGATIVE #307 EXISTANTE (± 500 × 500 MM) À DÉMANTÉLER TEMPORAIREMENT LORSQUE LA CHAMBRE EST INNOUPÉE. PRÉVOIR LA PROLONGATION TEMPORAIRE DU CONDUIT À L'EXTÉRIEUR DES ÉCHAFAUDAGES ET UN GRILLAGE AVIAIRE TEMPORAIRE AFIN DE MAINTENIR LE SYSTÈME EN FONCTION DURANT LES TRAVAUX. LA PERSIENNE EST À RÉCUPÉRER ET RÉINSTALLER.
- D4 GRILLE D'ENTRÉE D'AIR EXISTANTE SOUS LA MARQUISE DE LA PORTE DE GARAGE POUR IRI MOBILE (SYSTÈME DE SOUFFLAGE DES COUSSINS DE PROTECTION DE LA PORTE DE GARAGE), À ENLEVER TEMPORAIREMENT ET À RÉINSTALLER AU MÊME ENDROIT APRÈS LES TRAVAUX.
- D5 PERSIENNE EXISTANTE (± 600 × 600 MM) À DÉMANTÉLER COMPLÈTEMENT. AUCUNE REMISE EN SERVICE NI MESURE TEMPORAIRE REQUISE. TRAVAIL EN COURS. VENTILATEUR D'ÉVACUATION (FUMOIR) DÉJÀ ENLEVÉ À L'INTÉRIEUR. DÉMANTÉLER COMPLÈTEMENT LE PLENUM DANS LE MUR DERRIÈRE LA PERSIENNE.
- D6 CAPOTIN MURAL DE RENVOI D'AIR VICIÉ DE LA HOTTE DE CUISINE DE LA SALLE COMMUNAUTAIRE, À REMPLACER. CONDUIT D'ÉVACUATION À PROLONGER SELON L'ÉPAISSEUR DE L'ENVELOPPE EXTÉRIEURE.
- D7 UNITÉ EXTÉRIEURE SYSTÈME BIBLOC LG AU R410A DE 18 MBH EXISTANTE, AVEC SON SUPPORT AU TOIT, À DÉMANTÉLER TEMPORAIREMENT. RÉCUPÉRER LE RÉFRIGÉRANT, PROLONGER LE TUBAGE, LE PROTÉGER ET EFFECTUER UNE REMISE EN MARCHE AFIN DE MAINTENIR L'UNITÉ EN OPÉRATION DURANT LES TRAVAUX. PRÉVOIR UN SUPPORT TEMPORAIRE.
- D8 CONDUIT DE PRISE D'AIR FRAIS EN SURFACE À L'EXTÉRIEUR DU BÂTIMENT, DESSERVANT LA VENTILATION DU BLOC OPÉATOIRE, À GARDER EN FONCTION DURANT TOUTE LA DURÉE DES TRAVAUX. AFIN DE RÉALISER LES TRAVAUX DE RÉFECTION DE FAÇADE DERRIÈRE LE CONDUIT EXISTANT, UNE INSTALLATION DE CONDUITS TEMPORAIRES D'AIR FRAIS DOIT ÊTRE MISE EN PLACE PAR L'ENTREPRENEUR EN PARALLÈLE DU CONDUIT EXISTANT ET DES TRAVAUX EN PLUSIEURS ÉTAPES SONT À PLANIFIER. VOIR VUES AGRANDIES EN PLANS.

NOTES DÉMOLITION - PLOMBERIE

- D1 SORTIE D'ARROSAGE EXTÉRIEURE EXISTANTE À CONSERVER ET À PROTÉGER.
- D2 ÉVÉNENTS DE VAPEUR POUR AUTOCLAVE LOCALISÉ AU SOUS-SOL, À RELOCALISER AVANT LE DÉBUT DES TRAVAUX DE LA FAÇADE OUEST. PROLONGER LA TUYAUTERIE EXTÉRIEURE SUR DES SUPPORTS TEMPORAIRES DÉPOSÉS EN TOITURE JUSQU'AU COIN SUD-OUEST DU BÂTIMENT. VOIR VUES AGRANDIES EN PLAN.
- D3 ÉVÉNENTS DE VAPEUR (3X) EN ACIER INOXYDABLE 1500, 1500 ET 2000 PROVENANT DE LA CHAUFFERIE, AVEC DRAIN DE CONDENSATS À MODIFIER.

NOTE DÉMOLITION - GICLEURS

- D1 GICLEURS EXISTANTS ET TUYAUTERIE ASSOCIÉE EXISTANTE (Ø 32 MM / 1 1/4 PO) SITUÉE SOUS LE TOIT DE L'ENTRÉE DES AMBULANCES (SUD), À DÉMANTÉLER TEMPORAIREMENT. PRÉVOIR LA MISE HORS-SERVICE DE CETTE ZONE DU SYSTÈME DE PROTECTION INCENDIE ET L'OBTURATION TEMPORAIRE DE LA TUYAUTERIE. PRÉVOIR LA RÉCUPÉRATION DU GLYCOL. LA TUYAUTERIE ET LES SUPPORTS SONT À RÉCUPÉRER ET MODIFIER. REMPLACER LES GICLEURS TEL QUE L'EXISTANT. VOIR VUES AGRANDIES EN PLAN.

CLIENT



SANTÉ QUÉBEC GASPÉSIE

RÉF. CLIENT:

PROJET

HÔPITAL DE CHANDLER
(RÉFECTION DE L'ENVELOPPE)


Architecte



CE DOCUMENT NE DOIT PAS SERVIR À
LA CONSTRUCTION

REV	DATE	DESCRIPTION	PAR
RÉVISIONS PARTIELLES			
1	2026/09/04	DÉFINITIFS POUR SOUMISSION	JD/JA
B	2026/08/21	DÉFINITIFS 100% POUR APPROBATION	JD/VS
A	2026/05/14	DÉFINITIFS 60% POUR APPROBATION	JD/VS
REV	DATE	DESCRIPTION	PAR

SCEAU:

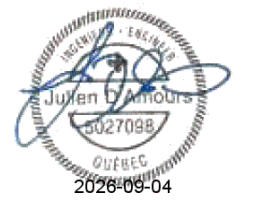

MÉCANIQUEÉLECTRICITÉ

AVERTISSEMENT:

CE DESSIN EST LA PROPRIÉTÉ INTELLECTUELLE DE WSP CANADA INC. AUCUNE RÉVISION, REPRODUCTION OU TOUT AUTRE USAGE N'EST PERMIS SANS L'AUTORISATION ÉCRITE DE WSP CANADA INC. L'ENTREPRENEUR DEVRA VÉRIFIER TOUTES LES DIMENSIONS AUX PLANS ET FAIRE LOCALISER TOUS LES SERVICES D'UTILITÉS PUBLIQUES ET RAPPORTER TOUTES ERREURS OU OMISSIONS AVANT DE COMMENCER LES TRAVAUX.

INDIQUÉE

DATE: AVRIL 2026

DESSINÉ PAR:

A. CASTONGUAY & A. HALLÉ

PRÉPARÉ SOUS SUPERVISION PAR:

J. D'AMOURS ET V. STOCKMEYER, ing.

PRÉPARÉ PAR:

J. D'AMOURS ET J. ALCINDOR, ing.

APPROUVÉ ADMINISTRATIVEMENT PAR:

G. LAVOIE

SI CETTE BARRE NE MESURE PAS 25 mm, AJUSTER VOTRE ÉCHELLE DE TRAPAGE.

25mm

DISCIPLINE:

MÉCANIQUE / ÉLECTRIQUE

Mécanique / Électricité



NO PROJET: CA0066110.3235


TITRE:

ÉLÉVATIONS
SUD / EST
DÉMOLITION

NUMÉRO DU
FEUILLET:


ME002D

\\corp.phwan.net\cadda5\cant1\PEP\projets\2026\11\CA0066110.3236\Bâtiment05 - TECH04.1 - CAO

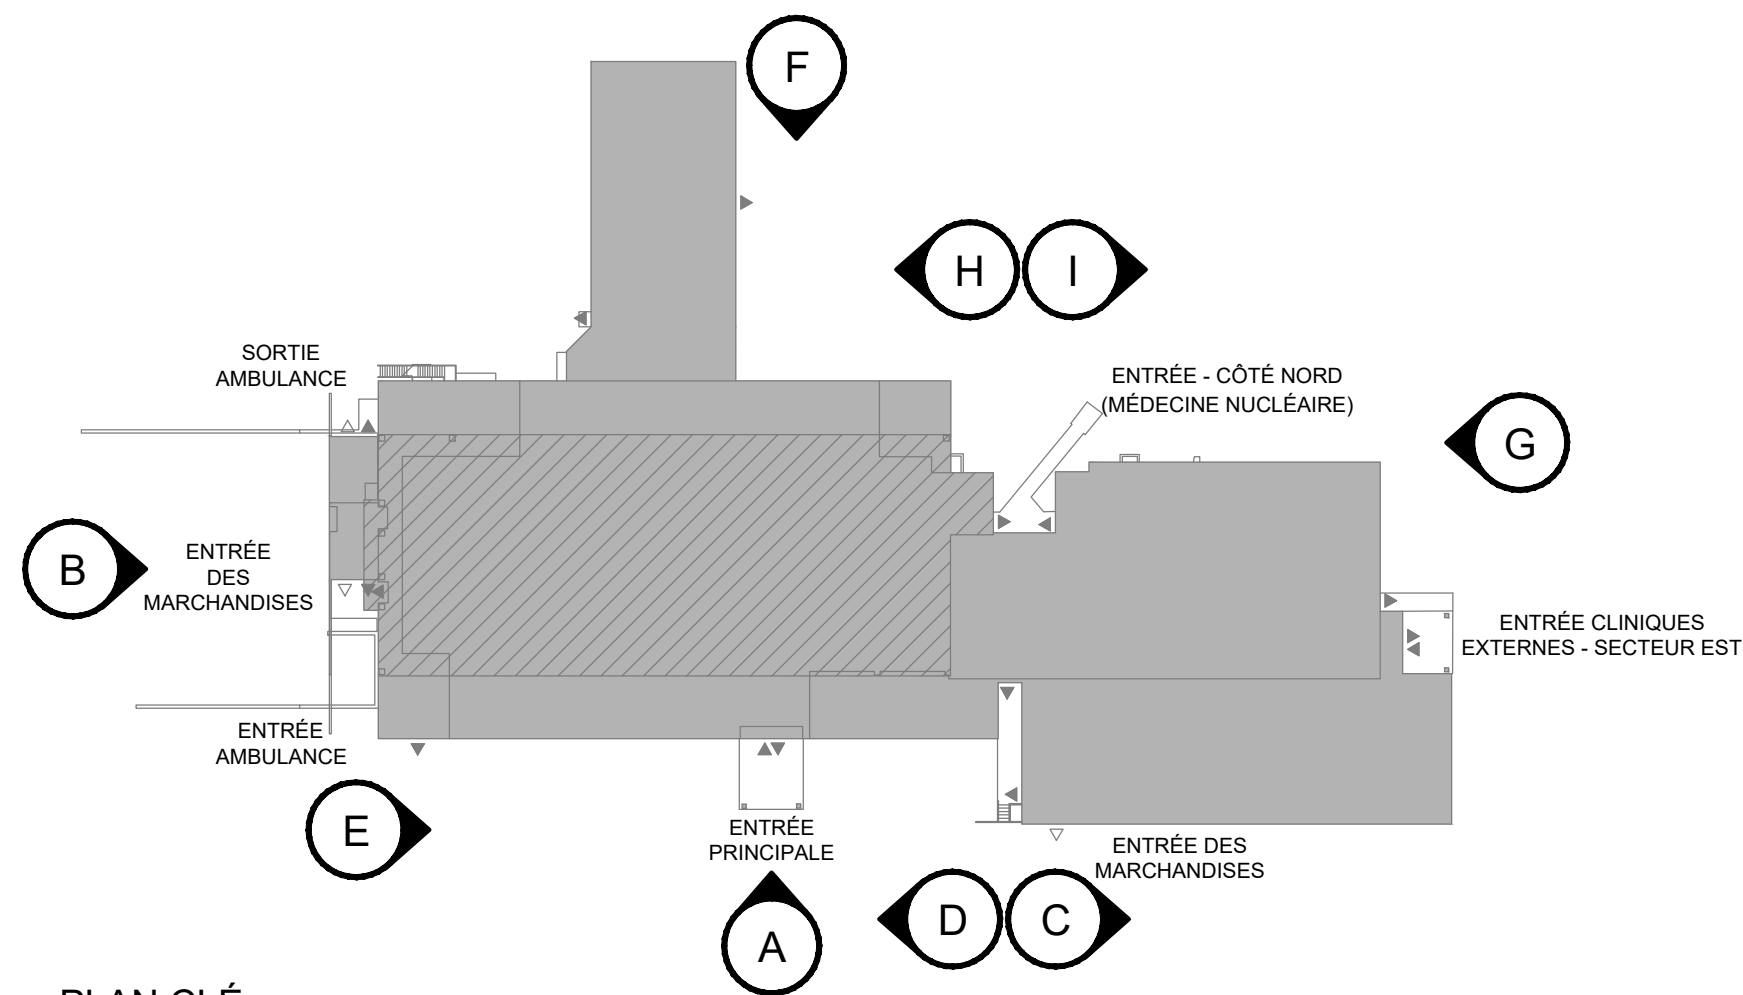


PLAN CLÉ

ÉCHELLE: AUCUNE

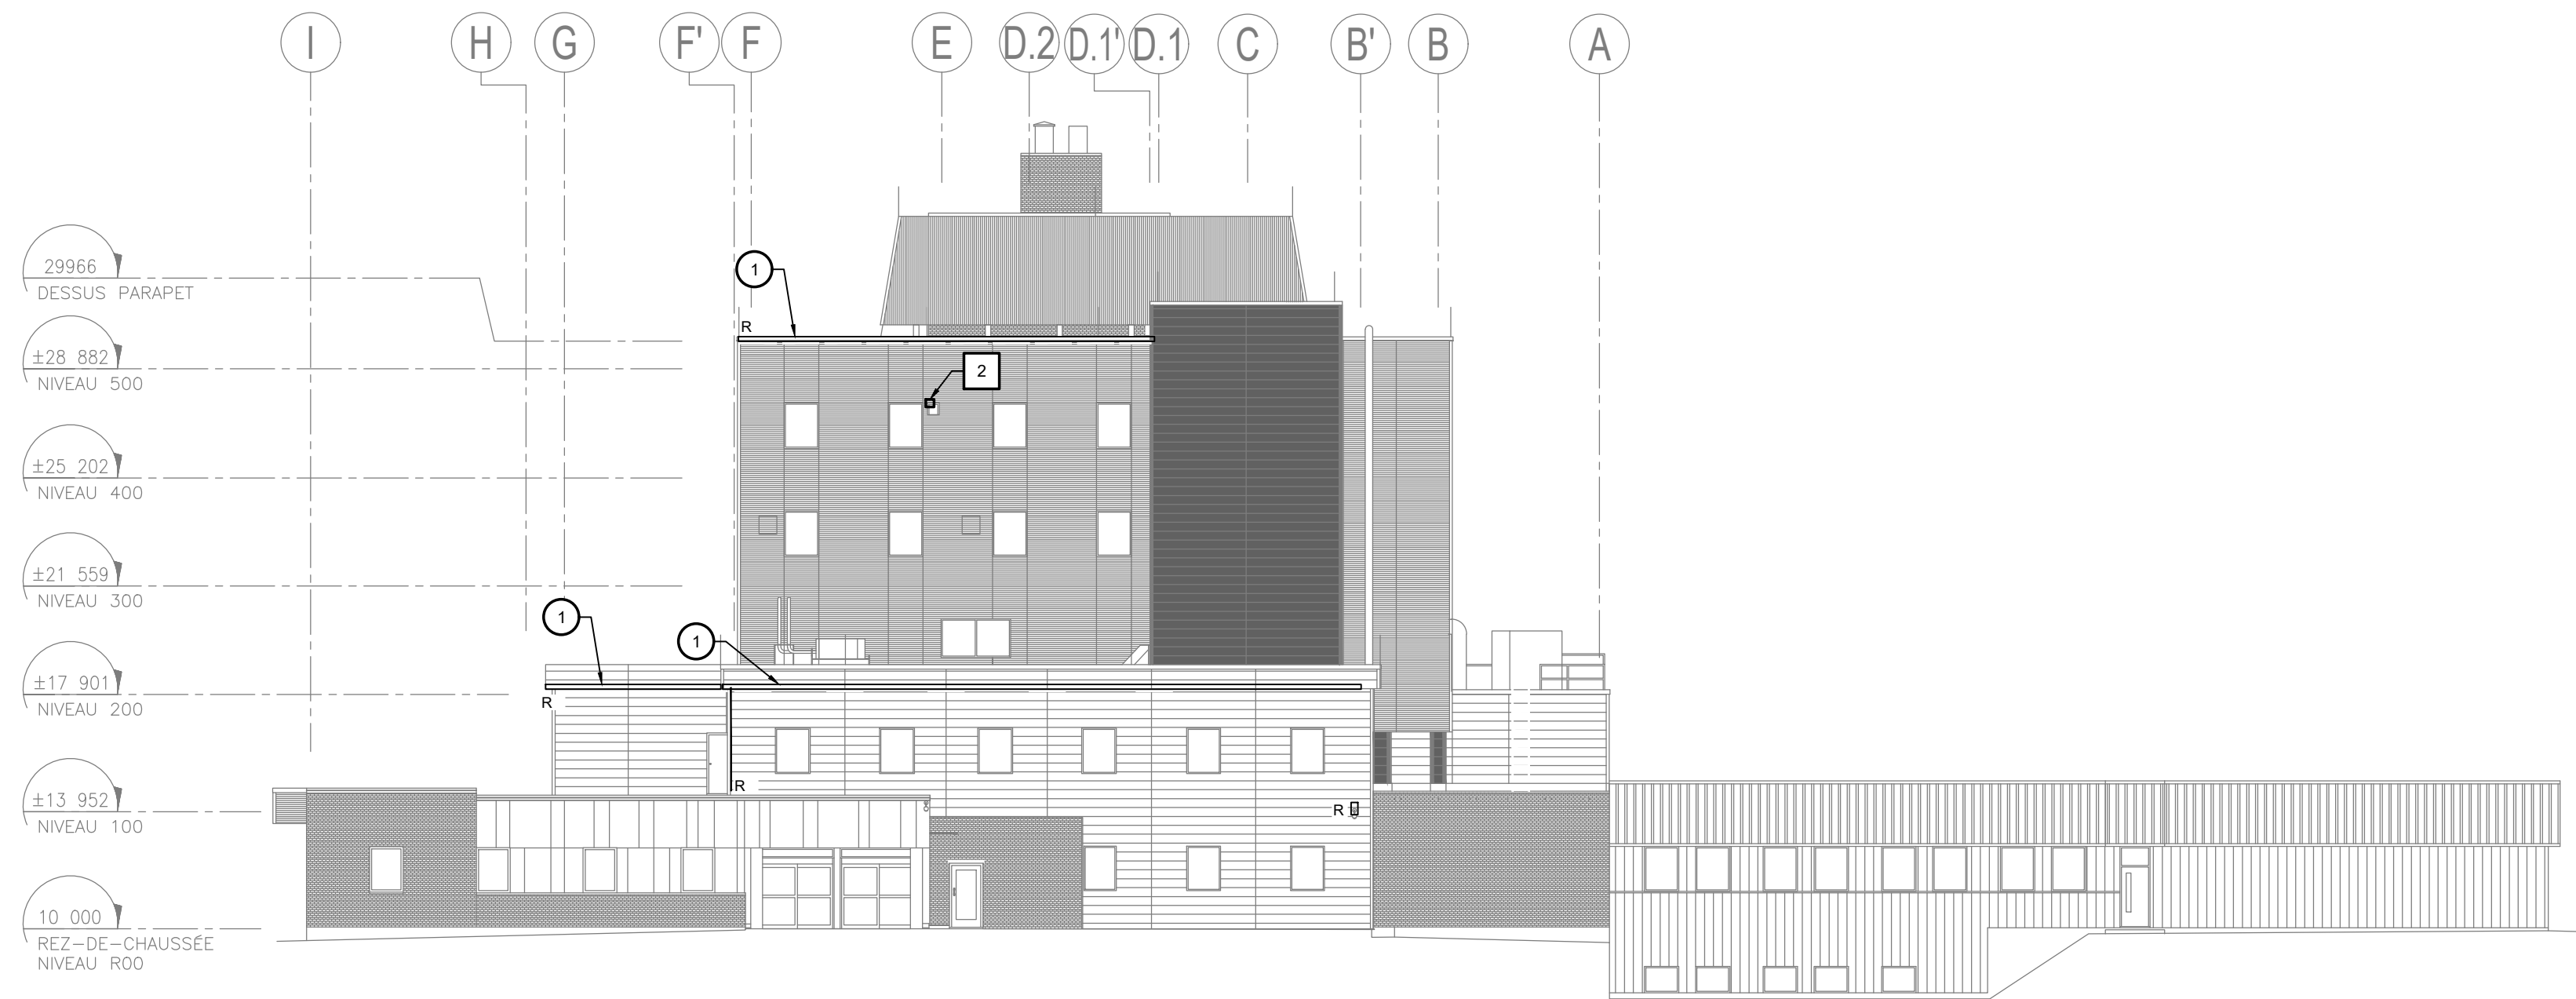

ÉLEVATION EST - CONSTRUCTION

ÉCHELLE: 1:200

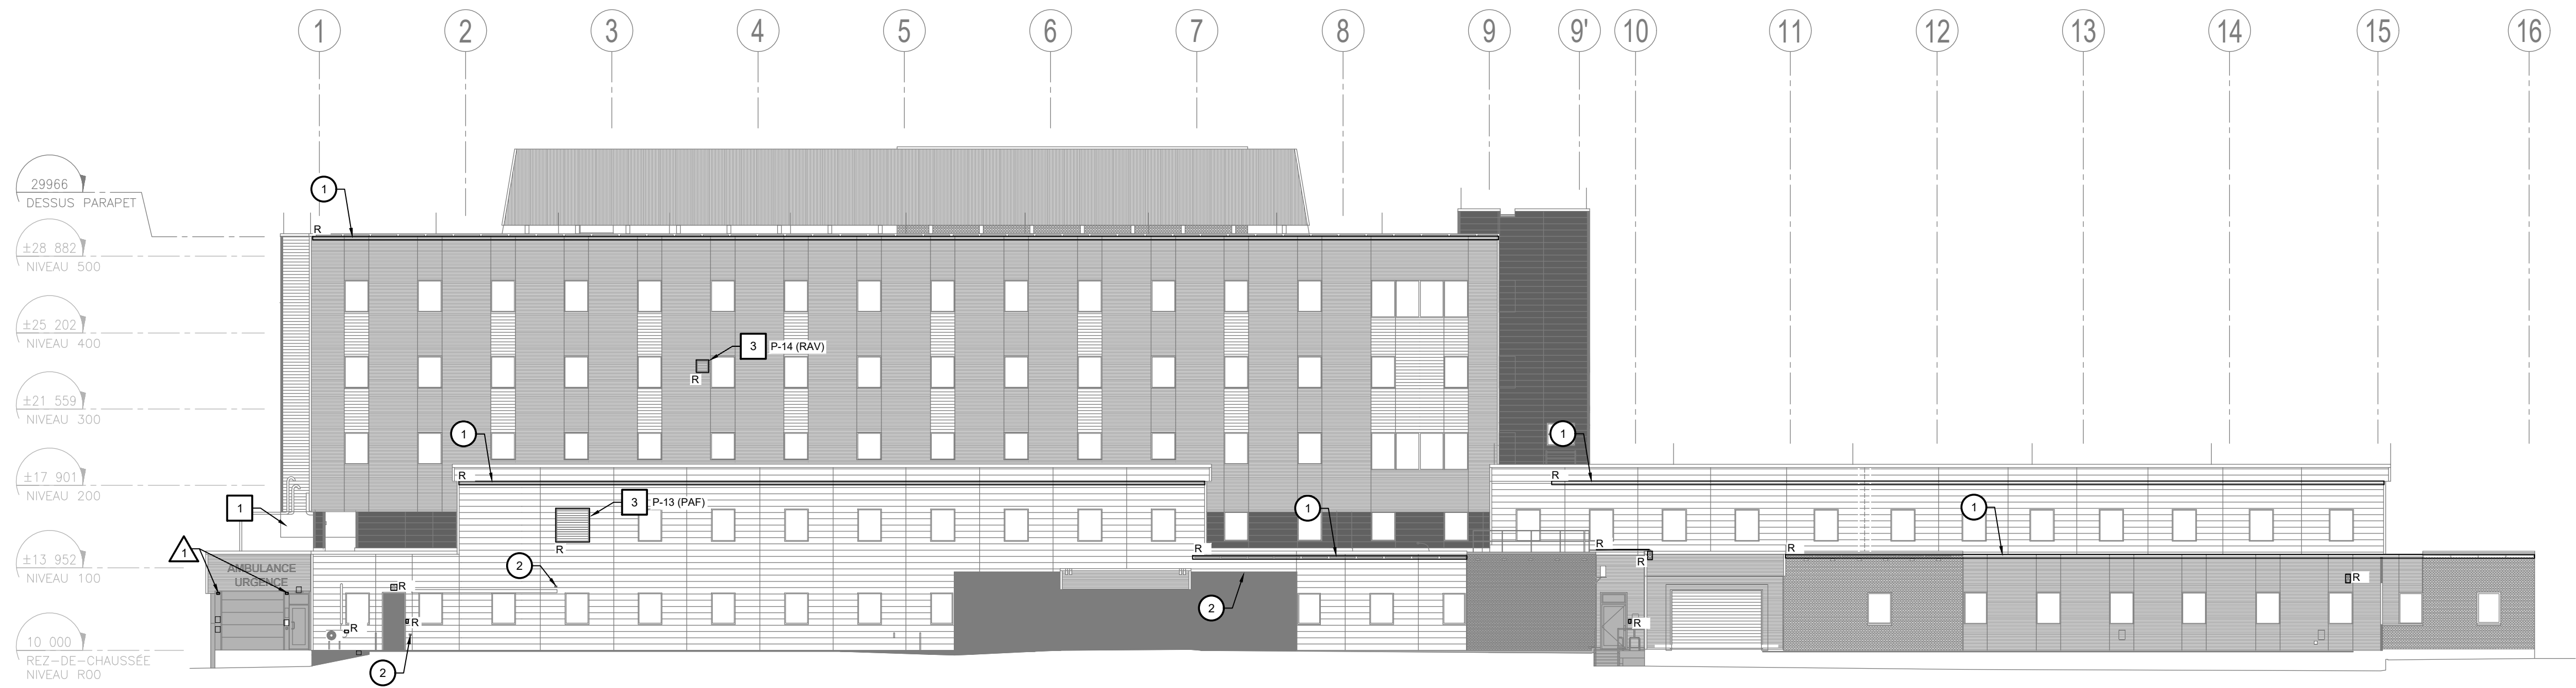

ÉLEVATION SUD - CONSTRUCTION

ÉCHELLE: 1:200

NOTES CONSTRUCTION - VENTILATION

- 1 NOUVEAU CONDUIT DE PRISE D'AIR FRAIS DU BLOC OPÉATOIRE (VOIR VUES AGRANDIES EN PLANS).
- 2 NOUVELLE SORTIE D'AIR MURALE (CAPOTIN) POUR REMPLACER CELLE EXISTANTE. COULEUR AU CHOIX DE L'ARCHITECTE. DIMENSION 250mmØ À VALIDER SUR PLACE AVANT LA COMMANDE, CONDUIT PROLONGÉ.
- 3 PERSIENNE EXISTANTE À RÉINSTALLER APRÈS LES TRAVAUX DE REVÊTEMENT.

NOTES CONSTRUCTION - ÉLECTRICITÉ

- 1 SÉRIE DE LUMINAIRES MURAUX À RÉINSTALLER AU MÊME ENDROIT SUR LE CÔTÉ DU NOUVEAU PARAPET OU SUR LE MUR EXTÉRIEUR (SELON LE CAS) APRÈS LES TRAVAUX DE REVÊTEMENT. CONSERVER L'AJUSTEMENT DE L'ANGLE DES LUMINAIRES.
- 2 NOUVELLE PRISE DDFT AVEC BÔTIER ÉTANCHE EN SURFACE POUR RACCORDEMENT AU CIRCUIT EXISTANT. RÉALISER TOUTES LES MODIFICATIONS REQUISES.

NOTE CONSTRUCTION - GICLEURS

- ⚠ TUYAUTERIES DE GICLEURS EXISTANTES MODIFIÉES (32mmØ / 1 1/4 PO) RÉINSTALLÉES SOUS LE TOIT DE L'ENTRÉE DES AMBULANCES (SUD) AVEC NOUVEAUX GICLEURS, VOIR VUES AGRANDIES EN PLAN.



SANTÉ QUÉBEC GASPÉSIE

RÉF. CLIENT:
PROJET


HÔPITAL DE CHANDLER
(RÉFECTION DE L'ENVELOPPE)


Architecte



CE DOCUMENT NE DOIT PAS SERVIR À
LA CONSTRUCTION

REV	DATE	DESCRIPTION	PAR
RÉVISIONS PARTIELLES			
1	2026/09/04	DÉFINITIFS POUR SOUMISSION	JD/JA
B	2026/08/21	DÉFINITIFS 100% POUR APPROBATION	JD/VS
A	2026/05/14	DÉFINITIFS 60% POUR APPROBATION	JD/VS
REV	DATE	DESCRIPTION	PAR

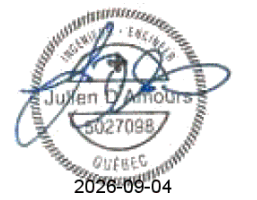
SCEAU:	
 MÉCANIQUE	 ÉLECTRICITÉ
AVERTISSEMENT: DROIT D'AUTEUR: CE DESSIN EST LA PROPRIÉTÉ INTELLECTUELLE DE WSP CANADA INC. AUCUNE RÉVISION, REPRODUCTION OU TOUT AUTRE USAGE NEST PERMIS SANS L'AUTORISATION ÉCRITE DE WSP CANADA INC. L'ENTREPRENEUR DEVRA VÉRIFIER TOUTES LES DIMENSIONS AUX PLANS ET FAIRE LOCALISER TOUS LES SERVICES D'UTILITÉS PUBLIQUES ET RAPPORTER TOUTES ERREURS OU OMISSIONS AVANT DE COMMENCER LES TRAVAUX.	
ÉCHELLE: ORIGINALE: INDIQUÉE DESSINÉ PAR: A. CASTONGUAY & A.HALLÉ PRÉPARÉ SOUS SUPERVISION PAR: J. D'AMOURS ET V. STOCKMEYER, ing. PRÉPARÉ PAR: J. D'AMOURS ET J. ALCINDOR, ing. APPROUVÉ ADMINISTRATIVEMENT PAR: S. LAVOIE	DATE: AVRIL 2026 SI CETTE BARRE NE MESURE PAS 25 mm, AJUSTER VOTRE ÉCHELLE DE TRAPAGE. 25mm
DISCIPLINE: MÉCANIQUE / ÉLECTRIQUE	

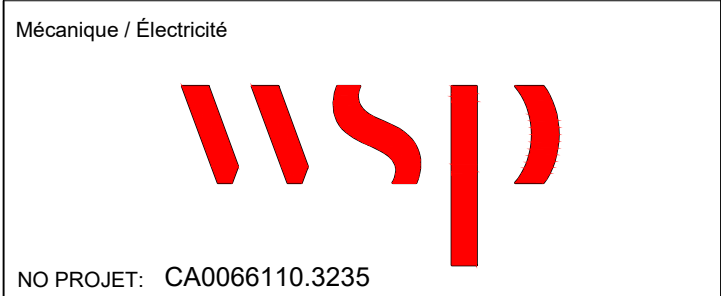

NO PROJET: CA0066110.3235


TITRE:
ÉLEVATIONS SUD / EST CONSTRUCTION
NUMÉRO DU FEUILLET:
ME002

\\corp.pharma.net\cad\daas\cant1\PEP\projets\2026\11\CA0066110\3235\Bâtiment05 TECH04.1 CAO

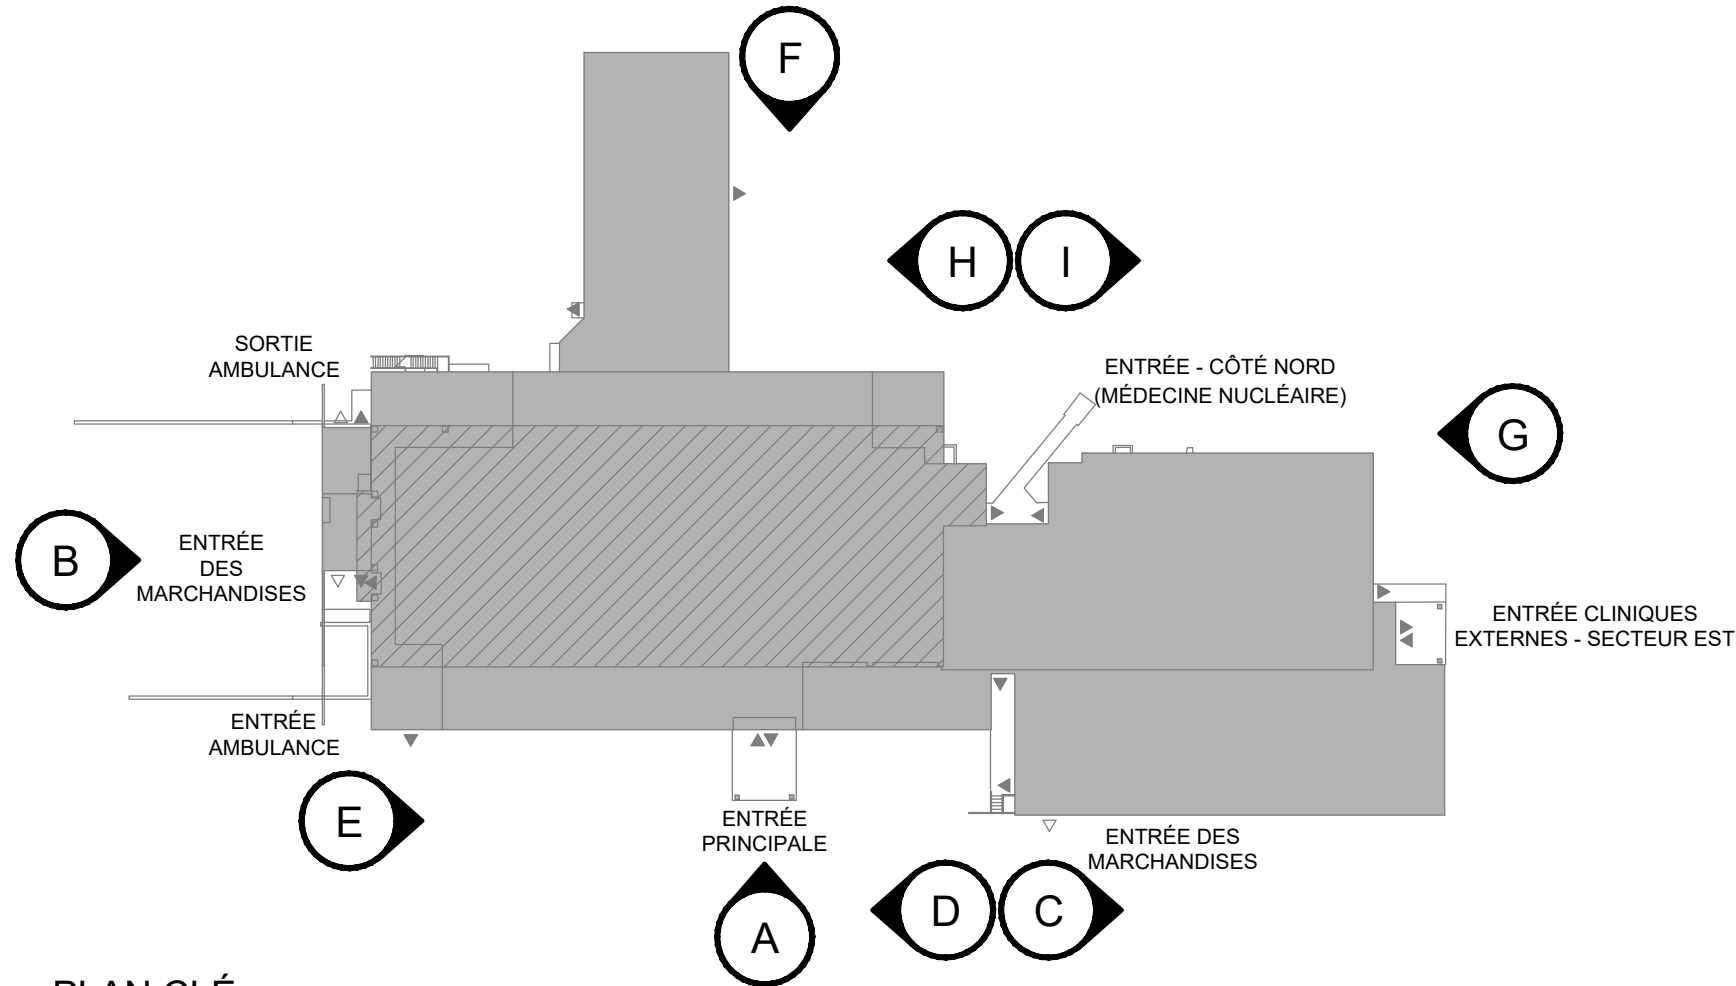


PLAN CLÉ


ÉCHELLE: AUCUNE

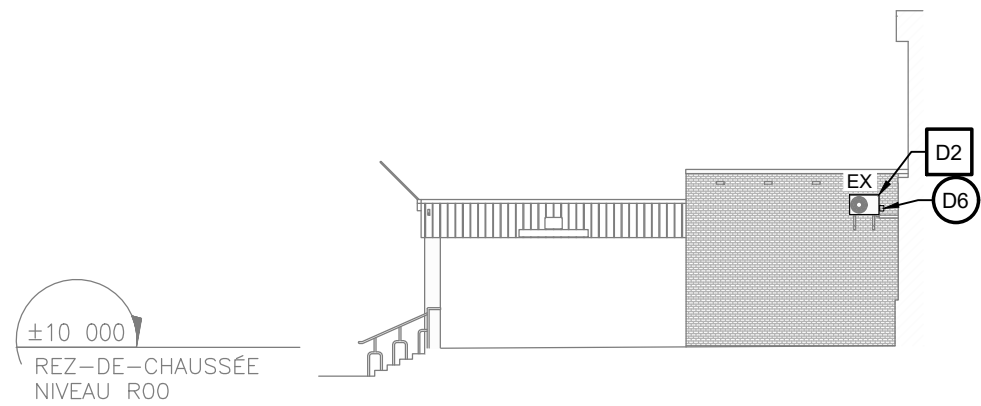


D ÉLÉVATION EST PARTIELLE - DÉMOLITION
ÉCHELLE: 1:200

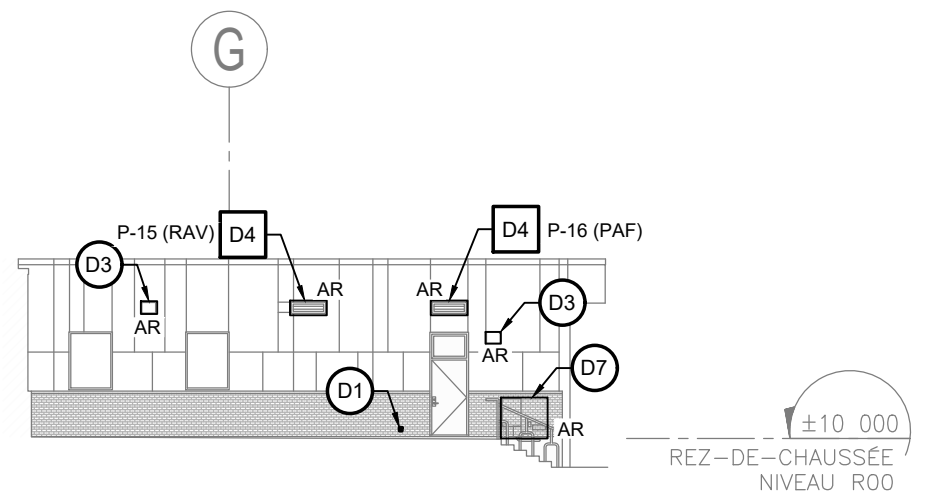


C ÉLÉVATION OUEST PARTIELLE - DÉMOLITION
ÉCHELLE: 1:200

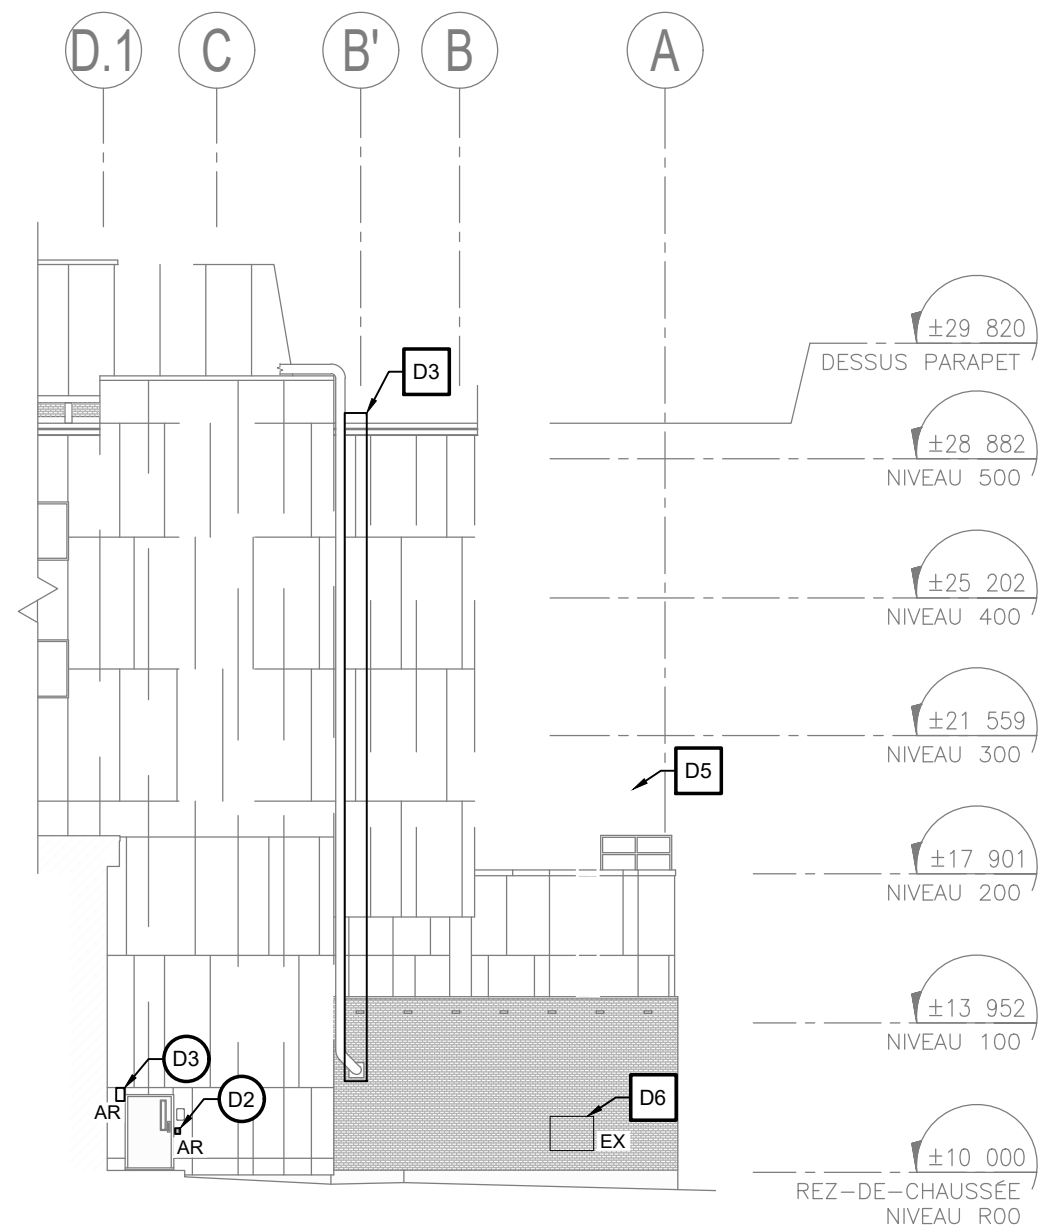

H ÉLÉVATION EST PARTIELLE - DÉMOLITION
ÉCHELLE: 1:200

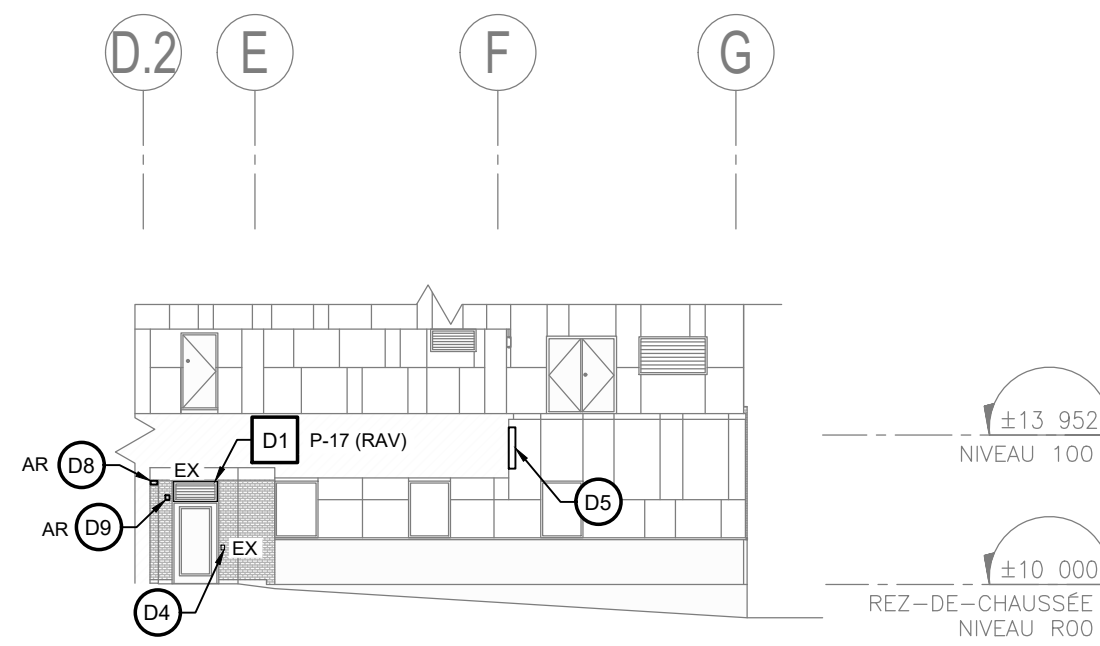

E ÉLÉVATION OUEST PARTIELLE - DÉMOLITION
ÉCHELLE: 1:200

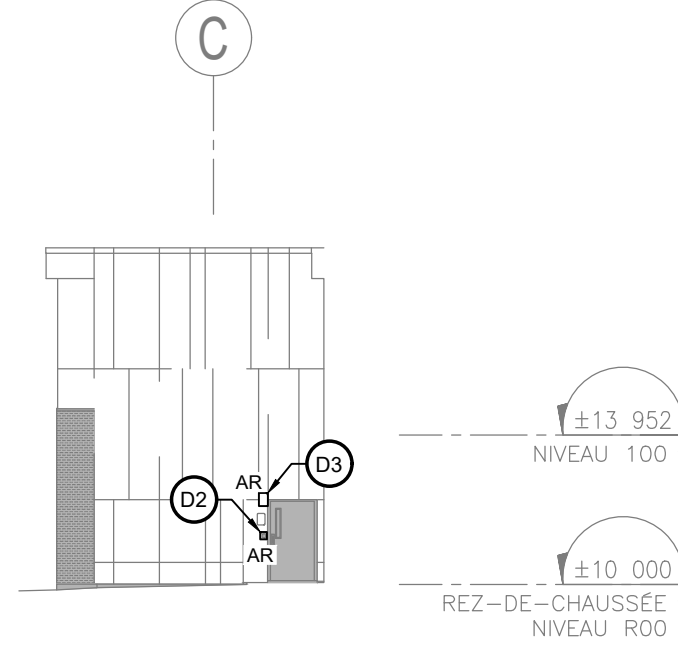

I ÉLÉVATION OUEST PARTIELLE - DÉMOLITION
ÉCHELLE: 1:200

NOTES DÉMOLITION - VENTILATION

- D1** PERSIENNE D'ÉVACUATION D'UNE CHAMBRE À PRESSION NÉGATIVE NON TOUCHÉE PAR LES TRAVAUX. À CONSERVER EN FONCTION DURANT LES TRAVAUX.
- D2** UNITÉ EXTÉRIEURE SYSTÈME BI-BLOC EXISTANTE À CONSERVER. ENLEVER ET RÉINSTALLER LE CACHE-TUYAU. LE NOUVEAU REVÊTEMENT DOIT ÊTRE INSTALLÉ AUTOUR DE LA TUYAUTERIE EXISTANTE.
- D3** CONDUIT D'ÉVACUATION D'UN VENTILATEUR DE LABORATOIRE AU TOIT, DESSERVANT UNE NOTIE EN MÉDECINE NUCLÉAIRE, À MODIFIER POUR RÉINSTALLATION SUR LE NOUVEAU REVÊTEMENT. REMPLACER LES SUPPORTS MURAUX GALVANISÉS.
- D4** PERSIENNE DE L'ÉCHANGEUR D'AIR DU SECTEUR DE LA ROULOTTE D'IRM MOBILE. À ENLEVER TEMPORAIREMENT DURANT LES TRAVAUX ET À RÉINSTALLER APRÈS LES TRAVAUX DE REVÊTEMENT.
- D5** UNITÉ DE VENTILATION AU TOIT EXISTANTE À CONSERVER, DESSERVANT LE SECTEUR D'HÉMODIALYSE ET DU LABORATOIRE. TROIS CONDUITS TRAVERSANT LE PAREMENT À MODIFIER DE FAÇON À GARDER L'UNITÉ EN FONCTION DURANT LES TRAVAUX. STRUCTURE DE PASSERELLE D'ACCÈS EN ALUMINIUM À ENLEVER TEMPORAIREMENT ET À MODIFIER POUR RÉINSTALLATION PAR L'ENTREPRENEUR GÉNÉRAL. UNE INSTALLATION DE CONDUITS TEMPORAIRES D'ALIMENTATION ET DE RETOUR D'AIR FRAIS DOIT ÊTRE MISE EN PLACE AVANT LES TRAVAUX DE DÉMOLITION DE L'ENVELOPPE.
- D6** UNITÉ EXTÉRIEURE SYSTÈME BI-BLOC EXISTANTE À CONSERVER.

NOTES DÉMOLITION - ÉLECTRICITÉ

- D1** PRISE ÉLECTRIQUE EXISTANTE À REMPLACER. CONSERVER LE CIRCUIT.
- D2** LECTEURS DE CARTE À ENLEVER TEMPORAIREMENT LE TEMPS DES TRAVAUX. ENTREPOSER ADEQUATEMENT.
- D3** LUMINAIRES MURAUX À ENLEVER TEMPORAIREMENT LE TEMPS DES TRAVAUX. ENTREPOSER ADEQUATEMENT.
- D4** ÉQUIPEMENT (EX) EXISTANT À CONSERVER.
- D5** ENSEIGNE AMBULANCE URGENCE À DÉBRANCHER PAR L'ÉLECTRICIEN ET À ENLEVER PAR L'ENTREPRENEUR GÉNÉRAL LE TEMPS DES TRAVAUX. VOIR VUES AGRANDIES EN PLAN.
- D6** SECTIONNEUR THERMOPOMPE 208V/1P À ENLEVER TEMPORAIREMENT LE TEMPS DES TRAVAUX.
- D7** COMPOSANTS DE RACCORDEMENT DE LA ROULOTTE MOBILE D'IMAGERIE PAR RÉSONNANCE MAGNÉTIQUE À ENLEVER TEMPORAIREMENT ET À RELOCALISER AU MÊME ENDROIT APRÈS LES TRAVAUX.
- D8** CAMÉRA EXTÉRIEURE POUR URGENCES, LOCALISÉE AU PLAFOND, À ENLEVER TEMPORAIREMENT ET À RELOCALISER AVEC BOÎTE ÉLECTRIQUE EXTÉRIEURE ÉTANCHE EN SURFACE.
- D9** DÉTECTEUR DE MOUVEMENT À ENLEVER TEMPORAIREMENT ET À RELOCALISER AVEC CONDUITS ET CÂBLAGE DISSIMULÉ DANS L'ENTREPLAFOND.



SANTÉ QUÉBEC GASPÉSIE

RÉF. CLIENT:
PROJET

HÔPITAL DE CHANDLER
(RÉFECTION DE L'ENVELOPPE)


Architecte



CE DOCUMENT NE DOIT PAS SERVIR À
LA CONSTRUCTION

REV	DATE	DESCRIPTION	PAR
RÉVISIONS PARTIELLES			
1	2026/09/04	DÉFINITIFS POUR SOUMISSION	JDJA
B	2026/08/21	DÉFINITIFS 100% POUR APPROBATION	JDVS
A	2026/05/14	DÉFINITIFS 60% POUR APPROBATION	JDVS
REV	DATE	DESCRIPTION	PAR


SCEAU:	
MÉCANIQUE	ÉLECTRICITÉ
AVERTISSEMENT: DROIT D'AUTEUR: CE DESSIN EST LA PROPRIÉTÉ INTELLECTUELLE DE WSP CANADA INC. AUCUNE RÉVISION, REPRODUCTION OU TOUT AUTRE USAGE N'EST PERMIS SANS L'AUTORISATION ÉCRITE DE WSP CANADA INC. L'ENTREPRENEUR DEVRA VÉRIFIER TOUTES LES DIMENSIONS AUX PLANS ET FAIRE LOCALISER TOUS LES SERVICES D'UTILITÉS PUBLIQUES ET RAPPORTER TOUTES ERREURS OU OMISSIONS AVANT DE COMMENCER LES TRAVAUX.	
ÉCHELLE: ORIGINALE: INDIQUÉE DESSINÉ PAR: A. CASTONGUAY & A. HALLÉ PRÉPARÉ SOUS SUPERVISION PAR: J. D'AMOURS ET V. STOCKMEYER, ing. PRÉPARÉ PAR: J. D'AMOURS ET J. ALCINDOR, ing. APPROUVÉ ADMINISTRATIVEMENT PAR: S. LAVOIE	DATE: AVRIL 2026 SI CETTE BARRE NE MESURE PAS 25 mm, AJUSTER VOTRE ÉCHELLE DE TRAPAGE. 25mm
DISCIPLINE: MÉCANIQUE / ÉLECTRIQUE	

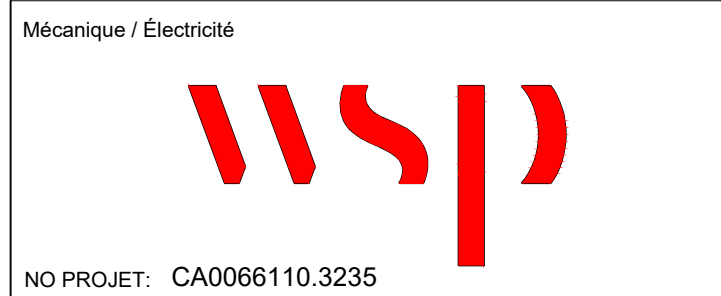

NO PROJET: CA0066110.3235


TITRE:
ÉLÉVATIONS PARTIELLES DÉMOLITION
NUMÉRO DU FEUILLET:
ME003D

\\corp.phsban.net\cadda5\cant11\PEP\projets\2026\11\CA066110\3235\Bâtiment05 - TECH04.1 - CAO

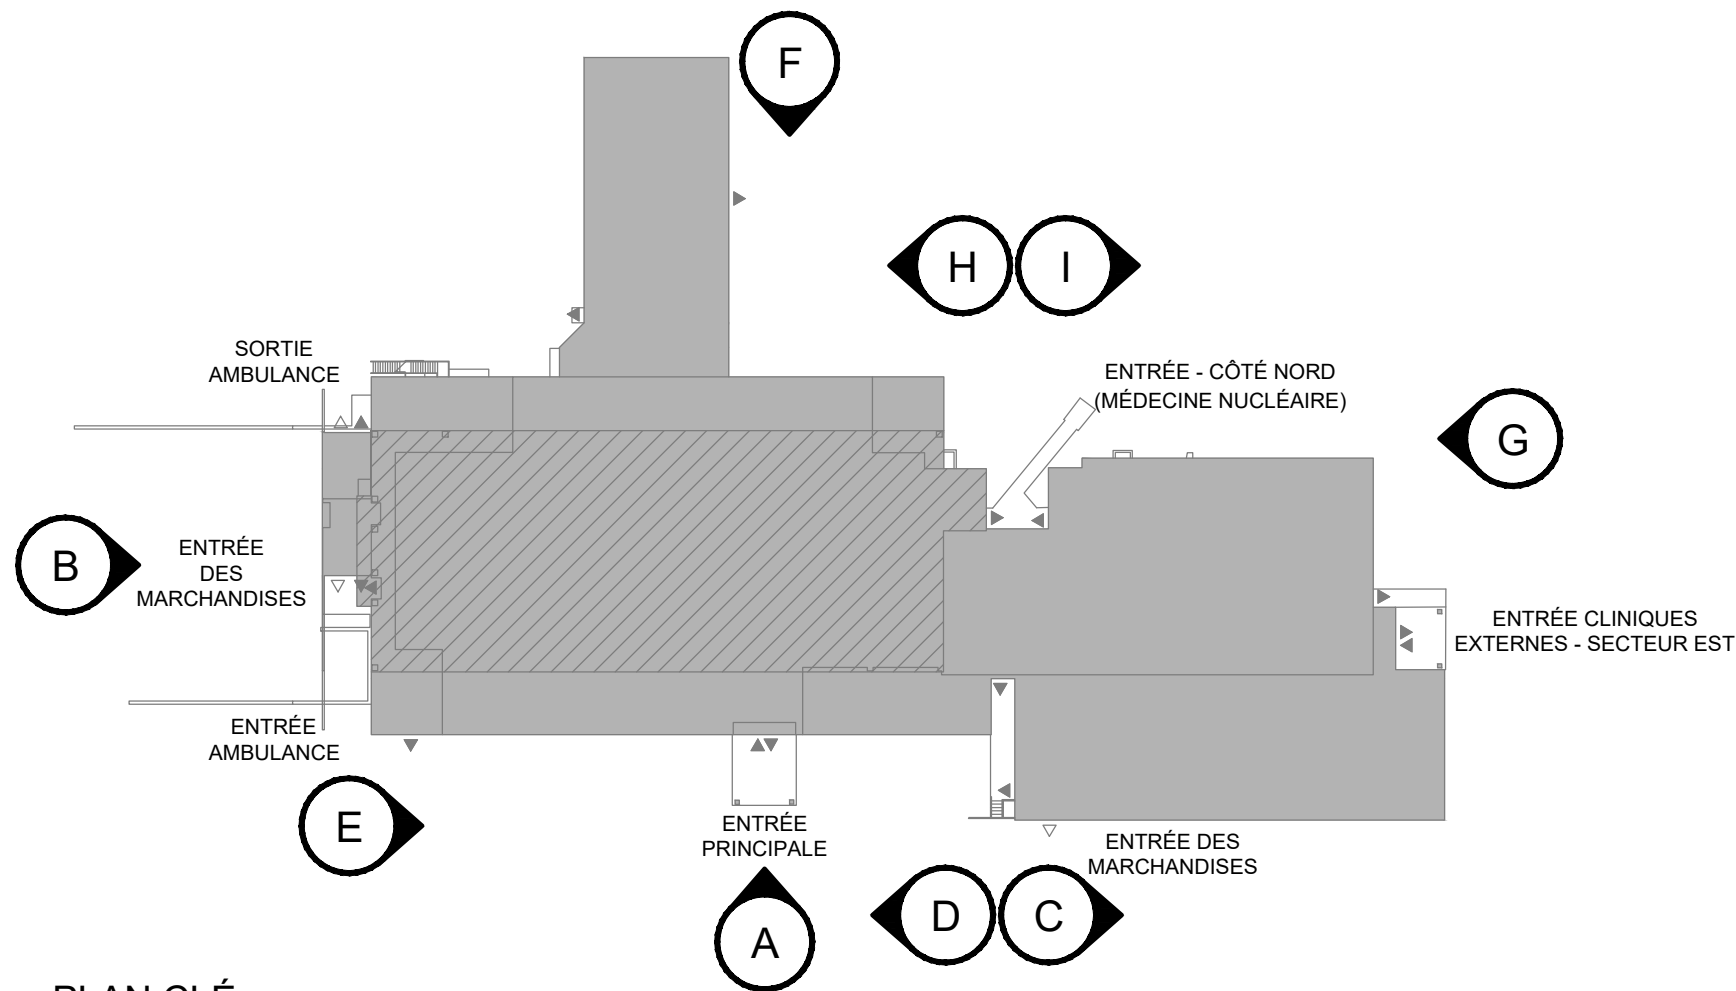


PLAN CLÉ


ÉCHELLE: AUCUNE

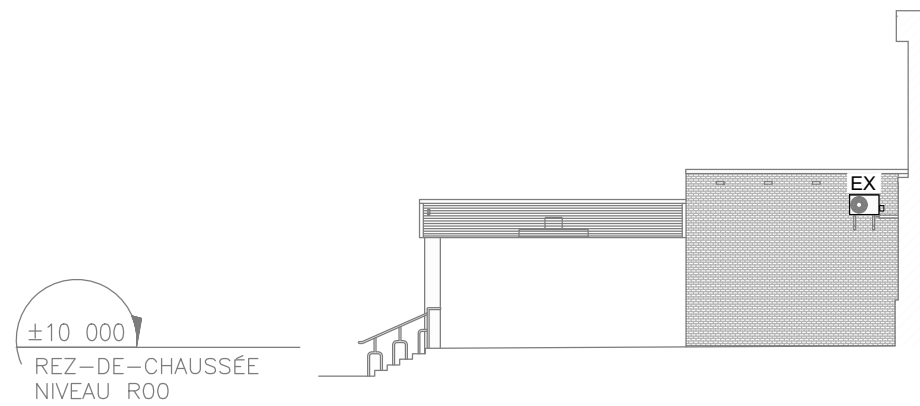


D ÉLÉVATION EST PARTIELLE - CONSTRUCTION
ÉCHELLE: 1:200

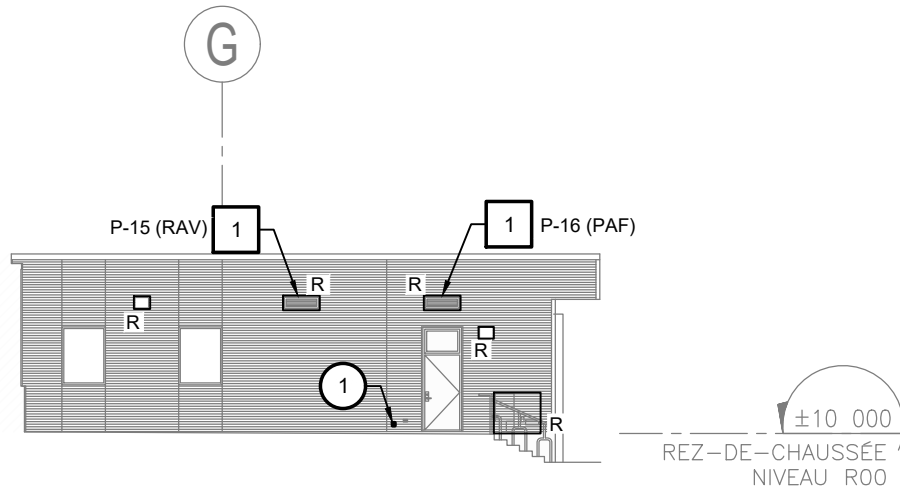


C ÉLÉVATION OUEST PARTIELLE - CONSTRUCTION
ÉCHELLE: 1:200

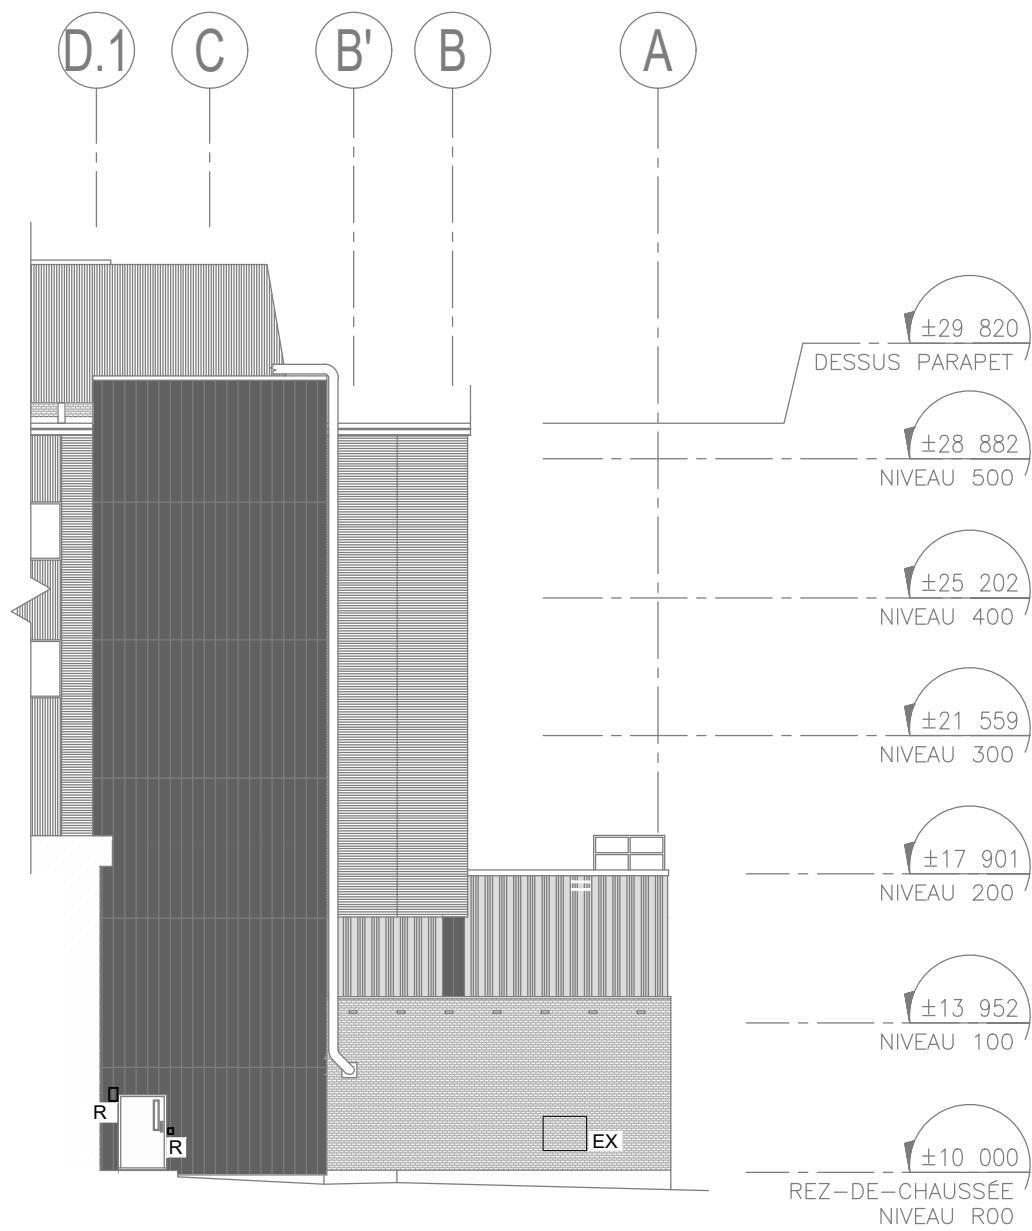

H ÉLÉVATION EST PARTIELLE - CONSTRUCTION
ÉCHELLE: 1:200

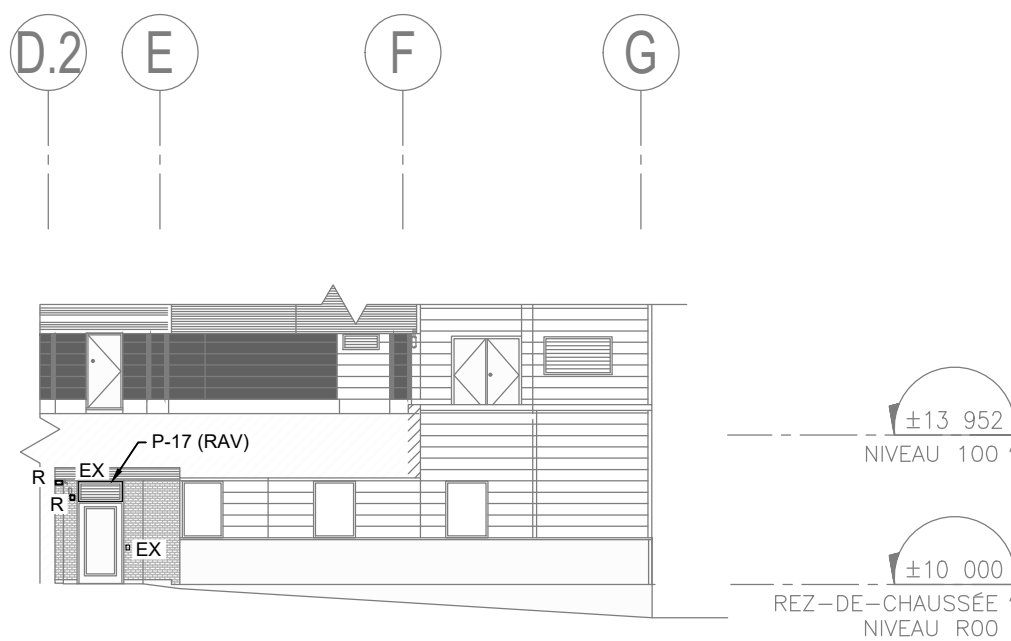

E ÉLÉVATION OUEST PARTIELLE - CONSTRUCTION
ÉCHELLE: 1:200

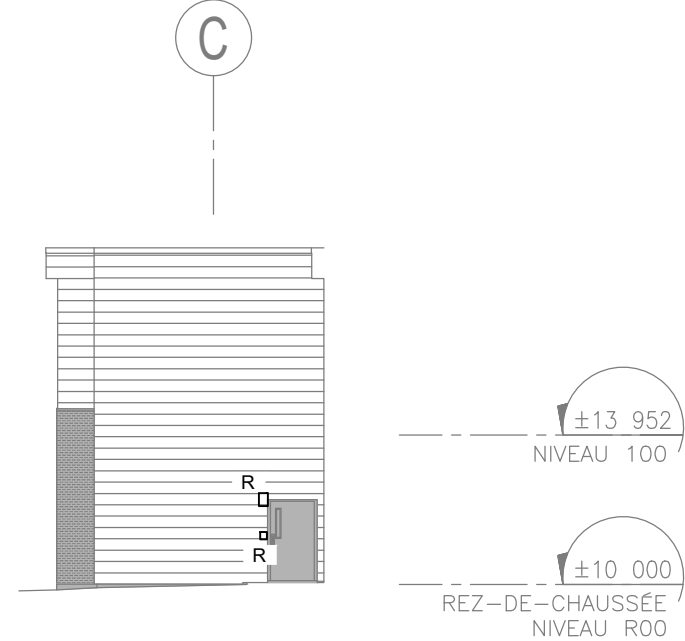

I ÉLÉVATION OUEST PARTIELLE - CONSTRUCTION
ÉCHELLE: 1:200

NOTE CONSTRUCTION - VENTILATION

- 1 PERSIENNE EXISTANTE À RÉINSTALLER APRÈS LES TRAVAUX DE REVÊTEMENT.

NOTE CONSTRUCTION - ÉLECTRICITÉ

- 1 NOUVELLE PRISE DDFT AVEC BOÎTIER ÉTANCHE EN SURFACE POUR RACCORDEMENT AU CIRCUIT EXISTANT. RÉALISER TOUTES LES MODIFICATIONS REQUISES.



SANTÉ QUÉBEC GASPÉSIE

RÉF. CLIENT:

PROJET

HÔPITAL DE CHANDLER
(RÉFECTION DE L'ENVELOPPE)

Architecte



CE DOCUMENT **NE DOIT PAS** SERVIR À
LA CONSTRUCTION

REV	DATE	DESCRIPTION	PAR
-----	------	-------------	-----

RÉVISIONS PARTIELLES

1	2026/09/04	DÉFINITIFS POUR SOUMISSION	JD-JA
B	2026/08/21	DÉFINITIFS 100% POUR APPROBATION	JD-VS
A	2026/05/14	DÉFINITIFS 60% POUR APPROBATION	JD-VS


REV	DATE	DESCRIPTION	PAR
-----	------	-------------	-----

SCEAU:	
MÉCANIQUE	ÉLECTRICITÉ

AVERTISSEMENT: DROIT D'AUTEUR:
CE DESSIN EST LA PROPRIÉTÉ INTELLECTUELLE DE WSP CANADA INC. AUCUNE RÉVISION, REPRODUCTION OU TOUT AUTRE USAGE N'EST PERMIS SANS L'AUTORISATION ÉCRITE DE WSP CANADA INC. L'ENTREPRENEUR DEVRA VÉRIFIER TOUTES LES DIMENSIONS AUX PLANS ET FAIRE LOCALISER TOUTS LES SERVICES D'UTILITÉS PUBLIQUES ET RAPPORTER TOUTES ERREURS OU OMISSIONS AVANT DE COMMENCER LES TRAVAUX.

ÉCHELLE: ORIGINALE: INDIQUÉE DESSINÉ PAR: A. CASTONGUAY & A. HALLÉ PRÉPARÉ SOUS SUPERVISION PAR: J. D'AMOURS ET V. STOCKMEYER, ing. PRÉPARÉ PAR: J. D'AMOURS ET J. ALCINDOR, ing. APPROUVÉ ADMINISTRATIVEMENT PAR: S. L'AVOIE	DATE: AVRIL 2026 SI CETTE BARRE NE MESURE PAS 25 mm: AJUSTER VOTRE ÉCHELLE DE TRAVAIL: 25mm
---	---

DISCIPLINE:
MÉCANIQUE / ÉLECTRIQUE

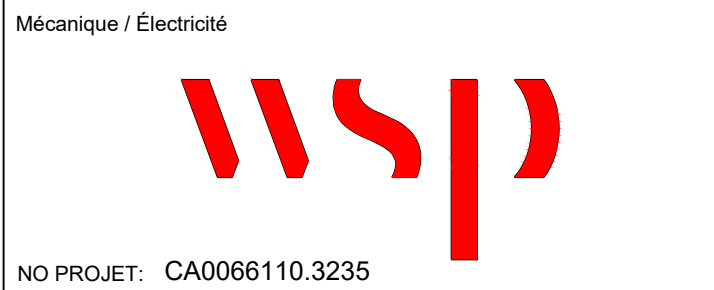


NO PROJET: CA0066110.3235

TITRE:

ÉLÉVATIONS PARTIELLES
CONSTRUCTION

NUMÉRO DU
FEUILLET:

ME003

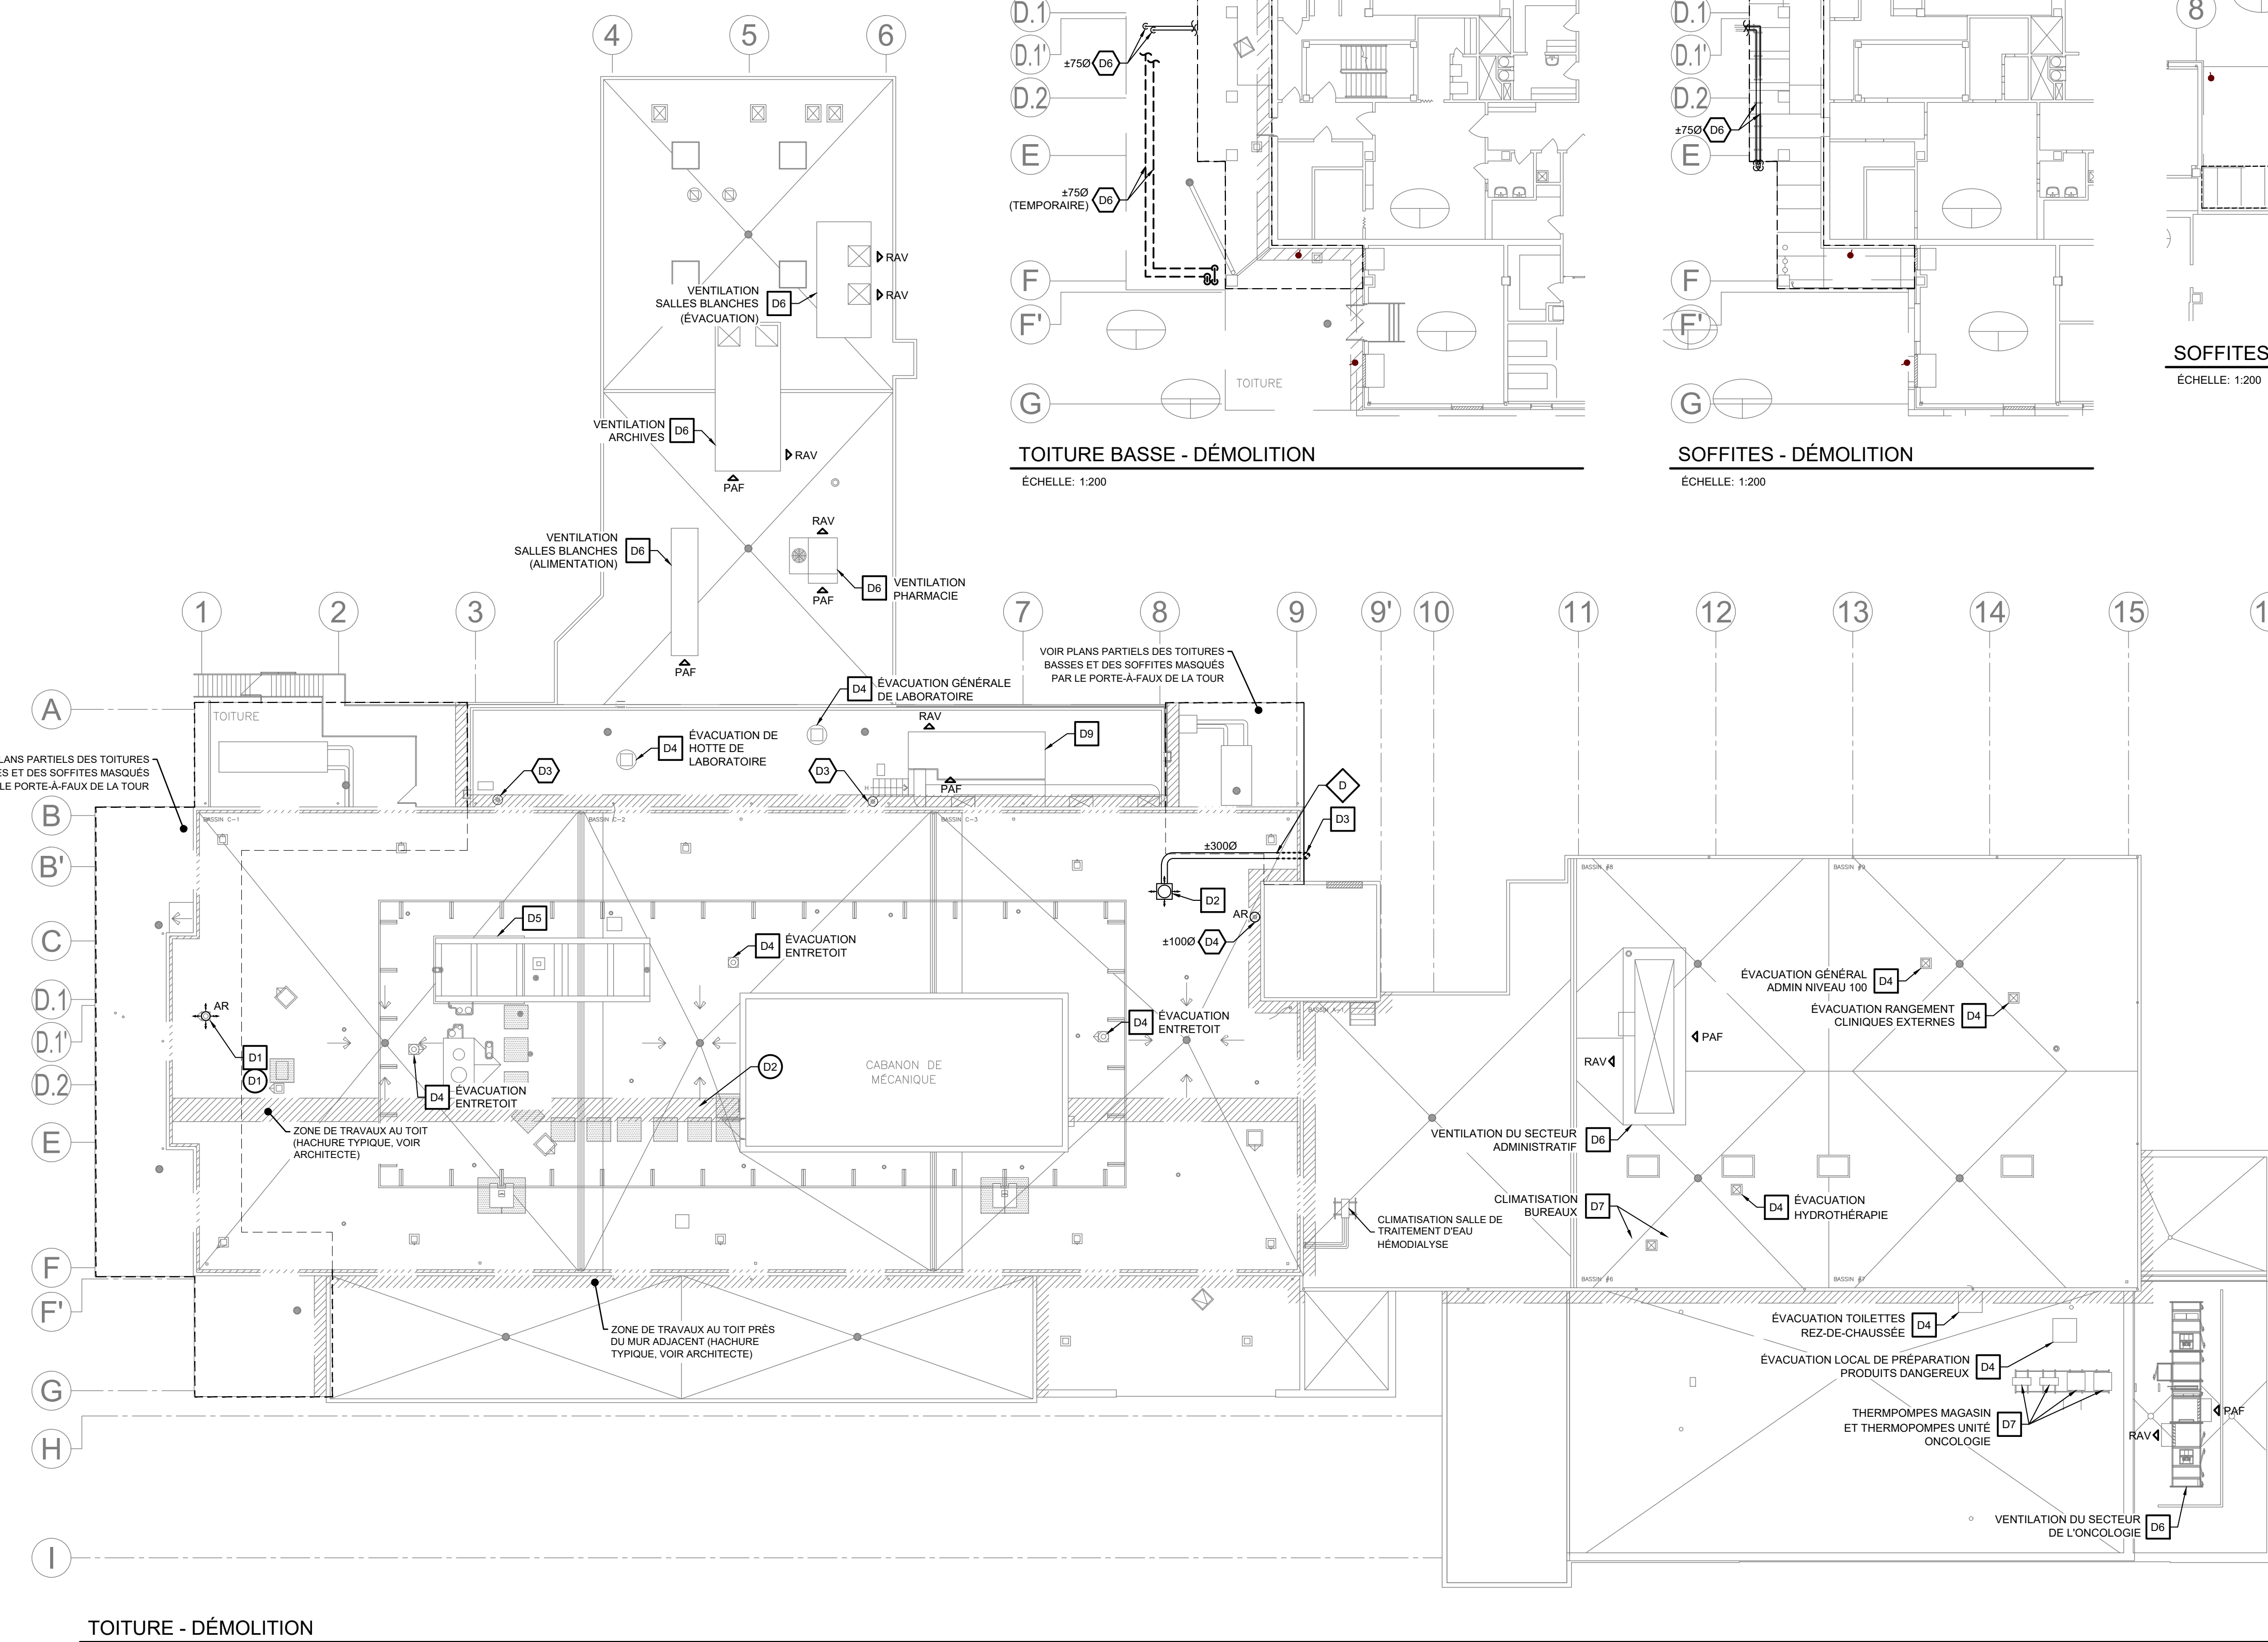

TOITURE - DÉMOLITION

ÉCHELLE: 1:200

NOTES DÉMOLITION - VENTILATION


- | | |
|-----|--|
| D1 | VENTILATEUR D'ÉVACUATION À ENLEVER
TEMPORAIREMENT ET À REINSTALLER APRÈS LES
TRAVAUX EN TOITURE. CONSERVER LE CONDUIT EXISTANT
DANS L'ENTRETOIT ET INSTALLER UN CALORIFUGE DE
TYPE D-2 D'50MM D'ÉPAISSEUR. LE CONDUIT CALORIFUGÉ
SERA CLOISONNÉ DANS L'ENTRETOIT (VOIR ARCHITECTE). |
| D2 | VENTILATEUR D'ÉVACUATION DE LABORATOIRE EXISTANT
À CONSERVER, DESERVANT UNE HOTTE DU SECTEUR DE
MÉDECINE NUCLEAIRE. CONSERVER LES CONDUITS
HORIZONTAUX EN TOITURE SUR SUPPORTS EXISTANTS. |
| D3 | CONDUIT D'ÉVACUATION DE LA HOTTE DE MÉDECINE
NUCLEAIRE À MODIFIER SUR TOUTE LA HAUTEUR DU
TOIT AFIN DE PERMETTRE LES TRAVAUX DE
RÉFÉCTION DES FAÇADES (VOIR VUES EN ÉLEVATION
POUR LES TRAVAUX). |
| D4 | VENTILATEUR EXISTANT À CONSERVER. |
| D5 | TOUR D'EAU EXISTANTE À CONSERVER. |
| D6 | UNITÉ DE VENTILATION EXISTANTE À CONSERVER. |
| D7 | UNITÉ DE CLIMATISATION EXISTANTE À CONSERVER. |
| D8 | TRAPPE D'ACCÈS DANS LE SOFFITE À RELOCALISER PAR
L'ENTREPRENEUR GÉNÉRAL, POUR ACCÈS À LA
MÉCANIQUE DISSIMULÉE SOUTS LE PORTE-A-FAX
(VENTILATEUR, DÉTENTE D'EAU, ÉCLAIRAGE, SÉRIE
REGISTRÉ MOTORISÉ, PURGEURS D'AIR, ETC.). |
| D9 | UNITÉ DE VENTILATION EXISTANTE À CONSERVER.
DESERVANT LE SECTEUR DES LABORATOIRES ET DE
L'HÉMODIALYSE. CONDUITS À MODIFIER ET CONDUITS
TEMPORAIRES À PRÉVOIR (VOIR VUES AGRANDIES). |
| D10 | VENTILATEUR D'ÉVACUATION MURAL EXTERIEUR (CLOCHE)
DESERVANT LA SALLE DE MÉCANIQUE DE STÉRILISATION
(1000CFM, 0.2PSH20). À ENLEVER TEMPORAIREMENT ET À
REINSTALLER APRÈS LES TRAVAUX DE RÉFÉCTION DE
FAÇADE. PROLONGER LE CONDUIT À L'INTÉRIEUR DU MUR
EXTERIEUR. |
| D11 | PERSIENNE D'ÉVACUATION DES LABORATOIRES À ENLEVER
SÉRIEUSEMENT ET À REINSTALLER DANS LE NOUVEAU
SOFFITE. LES SYSTÈMES DOIVANT DEMEURER EN
FONCTION DURANT TOUTE LA DURÉE DES TRAVAUX. |

NOTES DÉMOLITION - ÉLECTRICITÉ

- 01 DÉBRANCHER TEMPORAIREMENT LE SECTIONNEUR ÉLECTRIQUE SUR LE VENTILATEUR D'ÉVACUATION. CONSERVER L'ALIMENTATION ÉLECTRIQUE EXISTANTE VENANT DE L'ENTRETOIT ET RACCORDER LE VENTILATEUR REINSTALLÉ APRÈS LES TRAVAUX EN TOITURE.
- 02 CÂBLE CHAUFFANT À DÉPLACER TEMPORAIREMENT EN DEHORS DES ZONES DE TRAVAUX EN TOITURE ET À REMPLACER APRÈS LES TRAVAUX.
- 03 VENTILATEUR MURAL EXTERIEUR À DÉBRANCHER TEMPORAIREMENT. PROLONGER L'ALIMENTATION ÉLECTRIQUE JUSQU'AU VENTILATEUR RELOCALISÉ SELON L'ÉPAISSEUR DU MUR (120V/160, 0.25HP) À PARTIR D'UNE NOUVELLE BOÎTE DE JONCTION DANS LA SALLE MÉCANIQUE DE STÉRILISATION.

NOTES DÉMOLITION - PLOMBERIE

- | | |
|----|---|
| D1 | REFROIDISSEUR DE LIQUIDES EXISTANT À CONSERVER POUR LE SYSTÈME DE DÉSHUMIDIFICATION DU BLOC OPÉRATEUR. EXISTANT À CONSERVER. TUYAUTERIES DE GLYCOL À RELOCALISER (VOIR VUES AGRANDIES). |
| D2 | REFROIDISSEUR DU TOMODENSITOMÈTRE EXISTANT À CONSERVER. |
| D3 | SORTIE D'ÉVENT SANITAIRE EXISTANTE AU TOIT, À CONSERVER. SOLIN À REMPLACER PAR L'ENTREPRENEUR GÉNÉRAL. LORS DES TRAVAUX AU NIVEAU DU BANDEAU DE TOITURE PRÈS DU MUR EXTÉRIEUR. |
| D4 | SORTIE D'ÉVENT SANITAIRE EXISTANTE AU TOIT, À RELOCALISER PAR L'ENTREPRENEUR EN PLUMBERIE. SOLIN À REMPLACER PAR L'ENTREPRENEUR GÉNÉRAL. LORS DES TRAVAUX AU NIVEAU DU BANDEAU DE TOITURE PRÈS DU MUR EXTÉRIEUR. |
| D5 | SORTIE D'ÉVENT DE LABORATOIRE (MÉDECINE NUCLÉAIRE ET DOUCHE D'URGENCE) EXISTANTE AU TOIT, À RELOCALISER. SOLIN À REMPLACER PAR L'ENTREPRENEUR GÉNÉRAL. LORS DES TRAVAUX AU NIVEAU DU BANDEAU DE TOITURE PRÈS DU MUR EXTÉRIEUR. |
| D6 | SORTIE D'ÉVENT DE VAPEUR DES AUTOCUVES, EN ACIER SOUDÉ, À CONSERVER. LES PROLONGEMENTS DE TUYAUTERIE AU TOIT DOIVENT ÊTRE ENLEVÉS TEMPORAIREMENT AFIN DE PERMETTRE LES TRAVAUX DE RÉVÊTEMENT. |
| D7 | INSTALLER DES TUYAUTERIES TEMPORAIRES POUR ÉLIMINER LES SORTIES DES PRISES D'AIR FRAIS DE TOITURE. INSTALLER LES TUYAUTERIES TEMPORAIRES SUR DES DORMANTS EN BOIS TRAITÉS SUR LA TOITURE ET REHAUSSER LES COLS DE CYGNE À 10-M AU-DESSUS DU TOIT. |
| D8 | TUYAUTERIES DE GLYCOL À RELOCALISER (VOIR VUES AGRANDIES). À ENLEVER TEMPORAIREMENT AFIN DE PERMETTRE LES TRAVAUX DE RÉVÊTEMENT. |
| D9 | TUYAUTERIE DE PRISE D'AIR DE LA CENTRALE D'AIR MÉDICAL DE L'HÔPITAL. À ENLEVER TEMPORAIREMENT AFIN DE PERMETTRE LES TRAVAUX DE RÉVÊTEMENT. UNE PRISE D'AIR TEMPORAIRE DOIT ÊTRE INSTALLÉE PAR L'ENTREPRENEUR DURANT LE CHANTIER. |

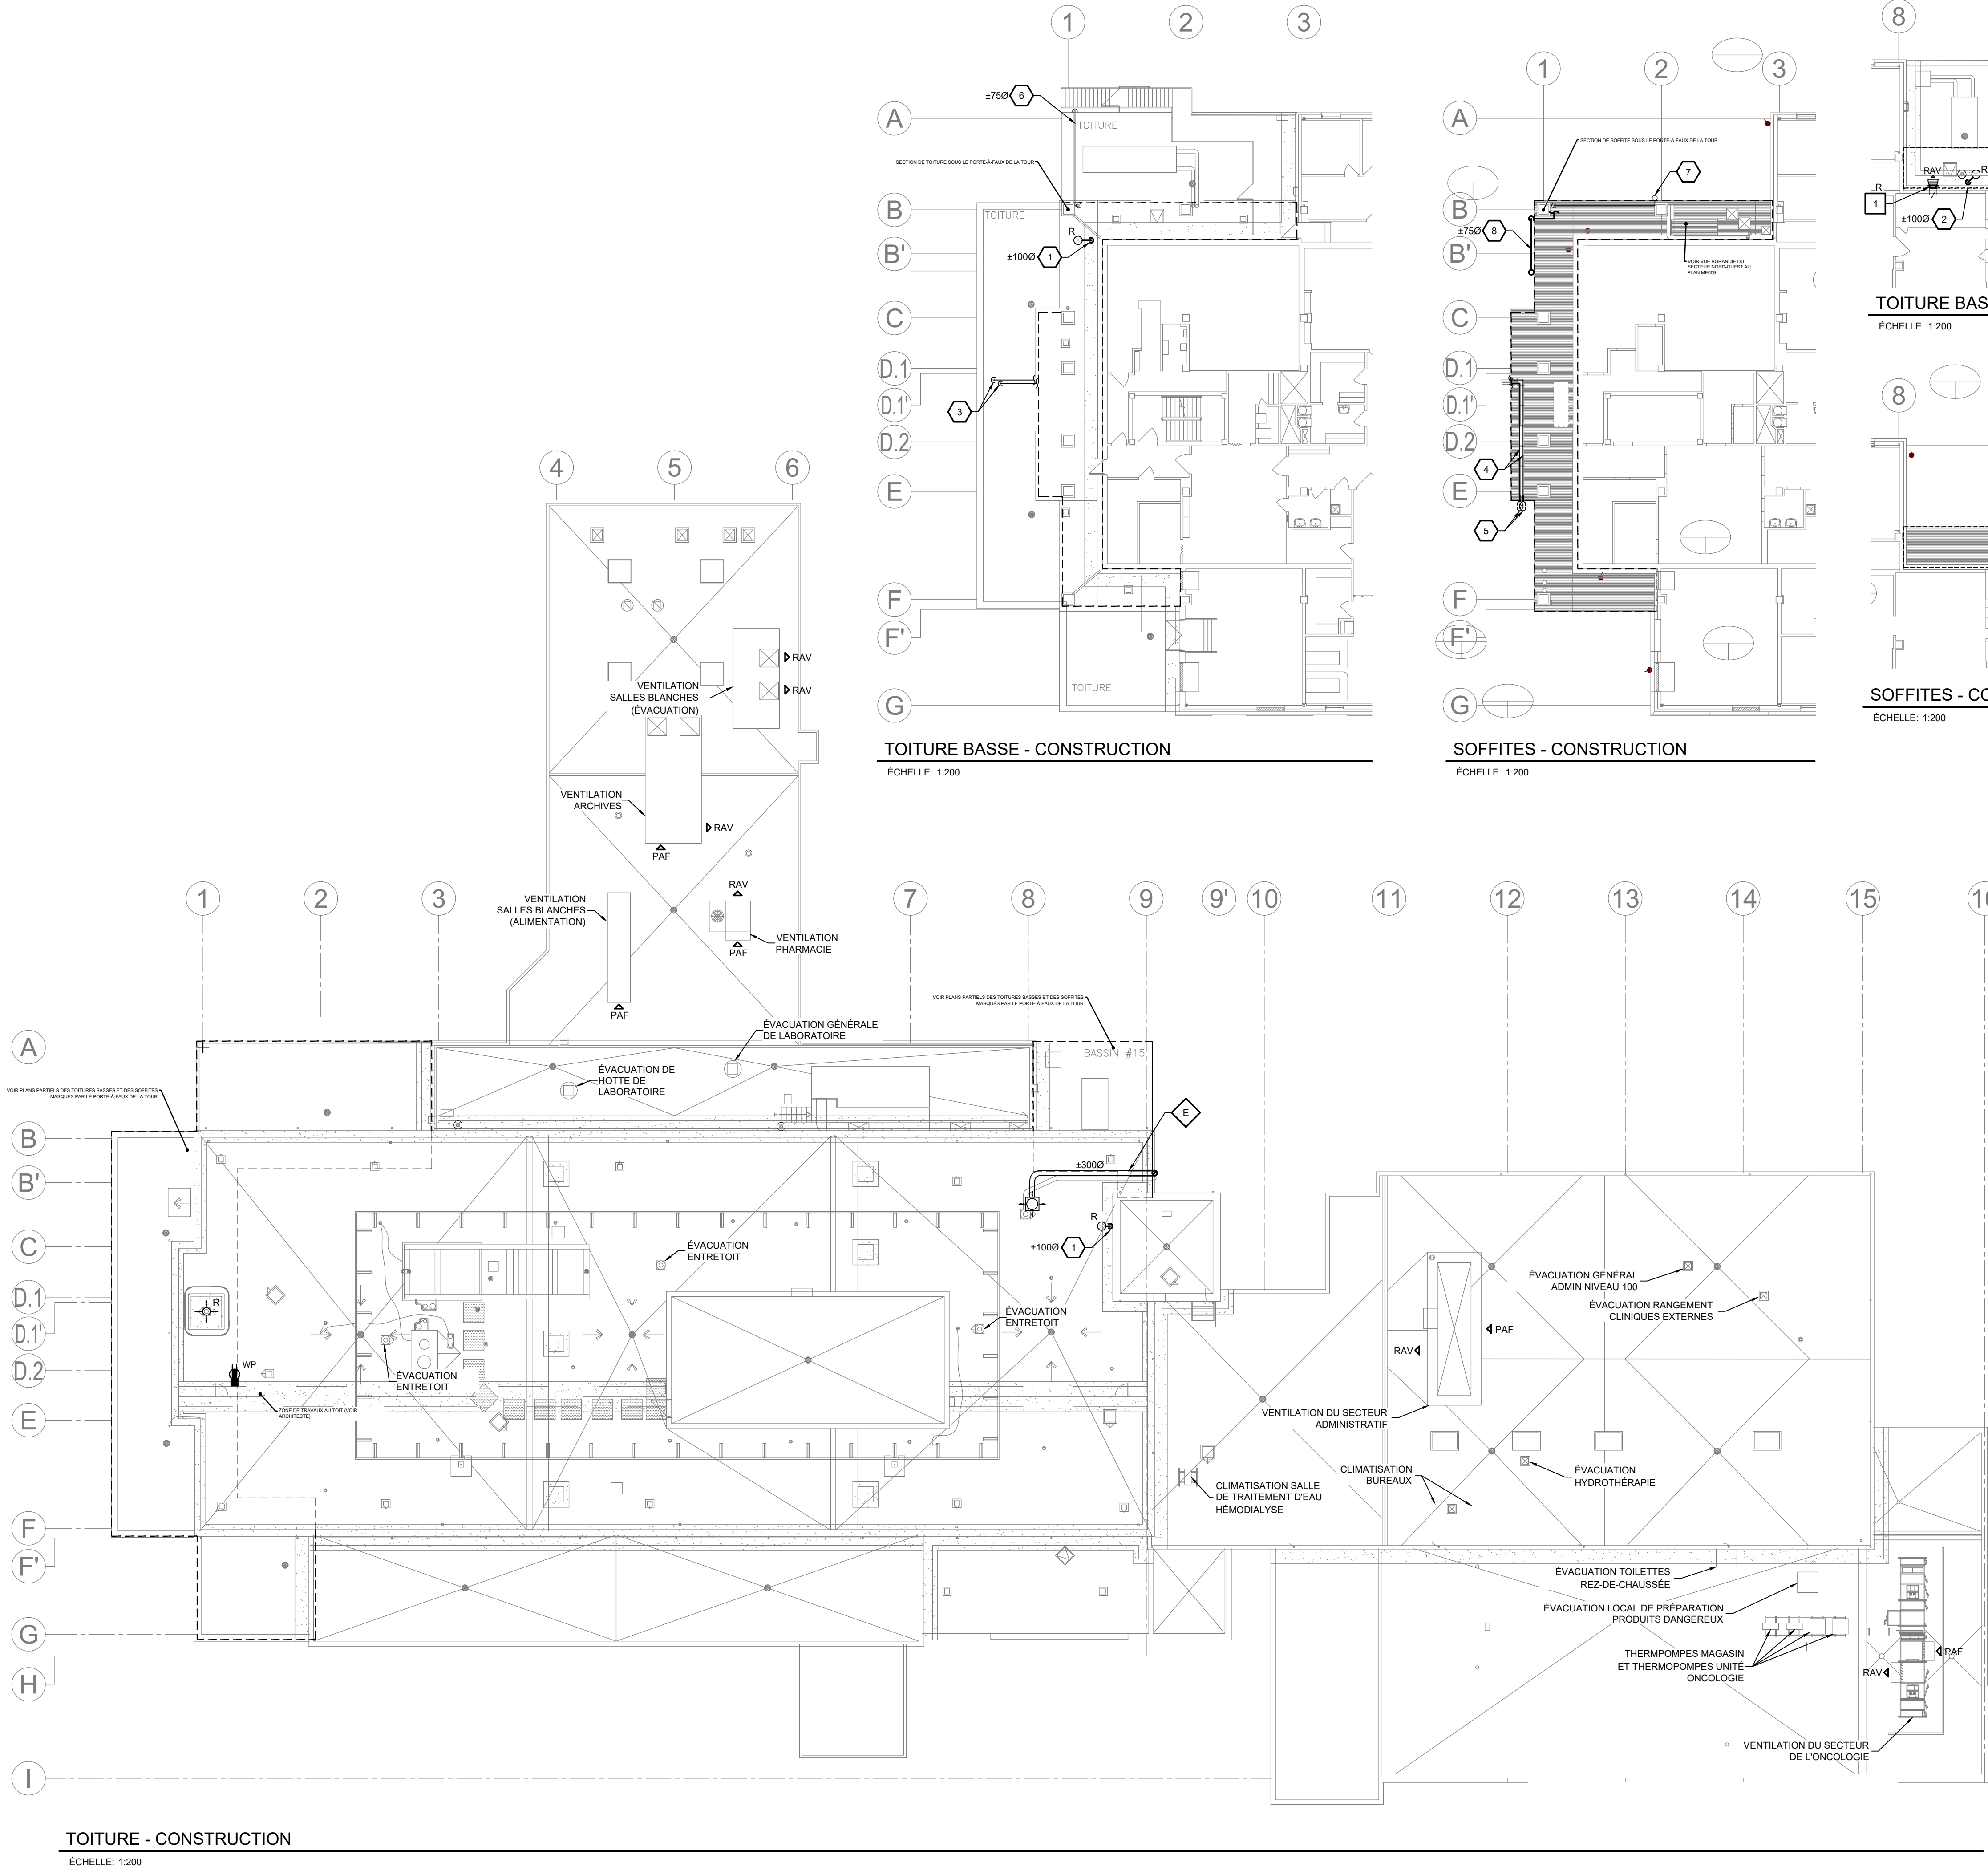

TOITURE - CONSTRUCTION
ÉCHELLE: 1:200

NOTE CONSTRUCTION - VENTILATION

- 1 MESURER LES DIMENSIONS EXACTES DES CONDUITS D'ÉVACUATION POUR LA PROLONGATION DU CONDUIT DU VENTILATEUR RELOCALISÉ.

NOTES CONSTRUCTION - PLOMBERIE

- 1 DÉVIATION DE TUYAUTERIE D'ÉVENT SANITAIRE EN FONTE À INSTALLER DANS L'ENTRETOIT VENTILÉ (HAUTEUR D'ACCÈS ± 450 MM) AFIN DE RELOCALISER LA SORTIE D'ÉVENT À 600MM DU MUR DU BÂTIMENT.
- 2 DÉVIATION DE TUYAUTERIE D'ÉVENT DE LABORATOIRE (MÉDECINE NUCLÉAIRE ET DOUCHE D'URGENCE) EN ACIER INOXYDABLE 304L À INSTALLER DANS L'ENTRETOIT VENTILÉ AFIN DE RELOCALISER LA SORTIE D'ÉVENT À 600MM DU MUR DU BÂTIMENT.
- 3 RÉINSTALLER LES PROLONGEMENTS DE TUYAUTERIES DES SORTIES D'ÉVENT DE VAPEUR DES AUTOCLAVES. AJUSTER LA HAUTEUR DES TUYAUTERIES SELON LE NOUVEAU REVÊTEMENT.
- 4 RÉINSTALLER LES PROLONGEMENTS DE TUYAUTERIES DES SORTIES D'ÉVENT DE VAPEUR DES AUTOCLAVES SUR DE NOUVEAUX SUPPORTS EN ACIER GALVANISÉ SOUS LE NOUVEAU SOFFITE.
- 5 RÉINSTALLER LES COLS DE CYGNE DES SORTIES D'ÉVENT DE VAPEUR DES AUTOCLAVES SUR DE NOUVEAUX SUPPORTS MURAUX EN ACIER GALVANISÉ. PROLONGER LES TUYAUTERIES SOUS LE SOFFITE SELON LA NOUVELLE ÉPAISSEUR DU MUR EXTÉRIEUR.
- 6 RÉINSTALLER LA TUYAUTERIE DE PRISE D'AIR DE LA CENTRALE D'AIR MÉDICAL SUR LES SUPPORTS EXISTANTS DÉPOSÉS EN TOITURE.
- 7 APRÈS LES TRAVAUX DE REVÊTEMENT EXTÉRIEUR DE LA FAÇADE NORD, RÉINSTALLER LA TUYAUTERIE DE PRISE D'AIR DE LA CENTRALE D'AIR MÉDICAL SUR DES NOUVEAUX SUPPORTS MURAUX EN ACIER INOXYDABLE. RÉINSTALLER LE BÔTIER DE FILTRATION D'ENTRÉE D'AIR.
- 8 TUYAUTERIE DE PRISE D'AIR TEMPORAIRE À INSTALLER SUR LA FAÇADE OUEST POUR PERMETTRE LES TRAVAUX DE REVÊTEMENT SUR LA FAÇADE NORD. COORDONNER LE PHASAGE AVEC L'ENTREPRENEUR GÉNÉRAL.

TOITURE BASSE - CONSTRUCTION

ÉCHELLE: 1:200

SOFFITES - CONSTRUCTION

ÉCHELLE: 1:200

SANTÉ QUÉBEC GASPÉSIE

RÉF. CLIENT:
PROJET

HÔPITAL DE CHANDLER
(RÉFECTION DE L'ENVELOPPE)

Architecte

CE DOCUMENT NE DOIT PAS SERVIR À LA CONSTRUCTION

REV	DATE	DESCRIPTION	PAR
RÉVISIONS PARTIELLES			
1	2026/09/04	DÉFINITIFS POUR SOUMISSION	JD-JA
B	2026/08/21	DÉFINITIFS 100% POUR APPROBATION	JD-VS
A	2026/05/14	DÉFINITIFS 60% POUR APPROBATION	JD-VS
REV	DATE	DESCRIPTION	PAR

MÉCANIQUE

ÉLECTRICITÉ

AVERTISSEMENT:
CE Dessin est la propriété intellectuelle de WSP Canada Inc. Aucune réimpression, reproduction ou tout autre usage n'est permis sans l'autorisation écrite de WSP Canada Inc. L'entrepreneur devra vérifier toutes les dimensions aux plans et faire localiser tous les services d'utilités publiques et rapporter toutes erreurs ou omissions avant de commencer les travaux.

SCHEMATA:
INDIQUÉE
A. CASTONGUAY
PRÉPARÉ SOUS SUPERVISION PAR:
J. D'AMOURS ET V. STOCKMEYER, ing.
PRÉPARÉ PAR:
J. D'AMOURS ET J. ALCINDOR, ing.
APPROUVÉ ADMINISTRATIVEMENT PAR:
S. L'AVOIE

DATE:
AVRIL 2026
SI CETTE BARRE NE MESURE PAS 25 mm, AJUSTER VOTRE ÉCHELLE DE TRACÉ:
25mm


DISCIPLINE:
MÉCANIQUE / ÉLECTRICITÉ

Mécanique / Électricité

NO PROJET: CA0066110.3235

TITRE:
TOITURES ET SOFFITES
CONSTRUCTION

NUMÉRO DU FEUILLET:
ME004

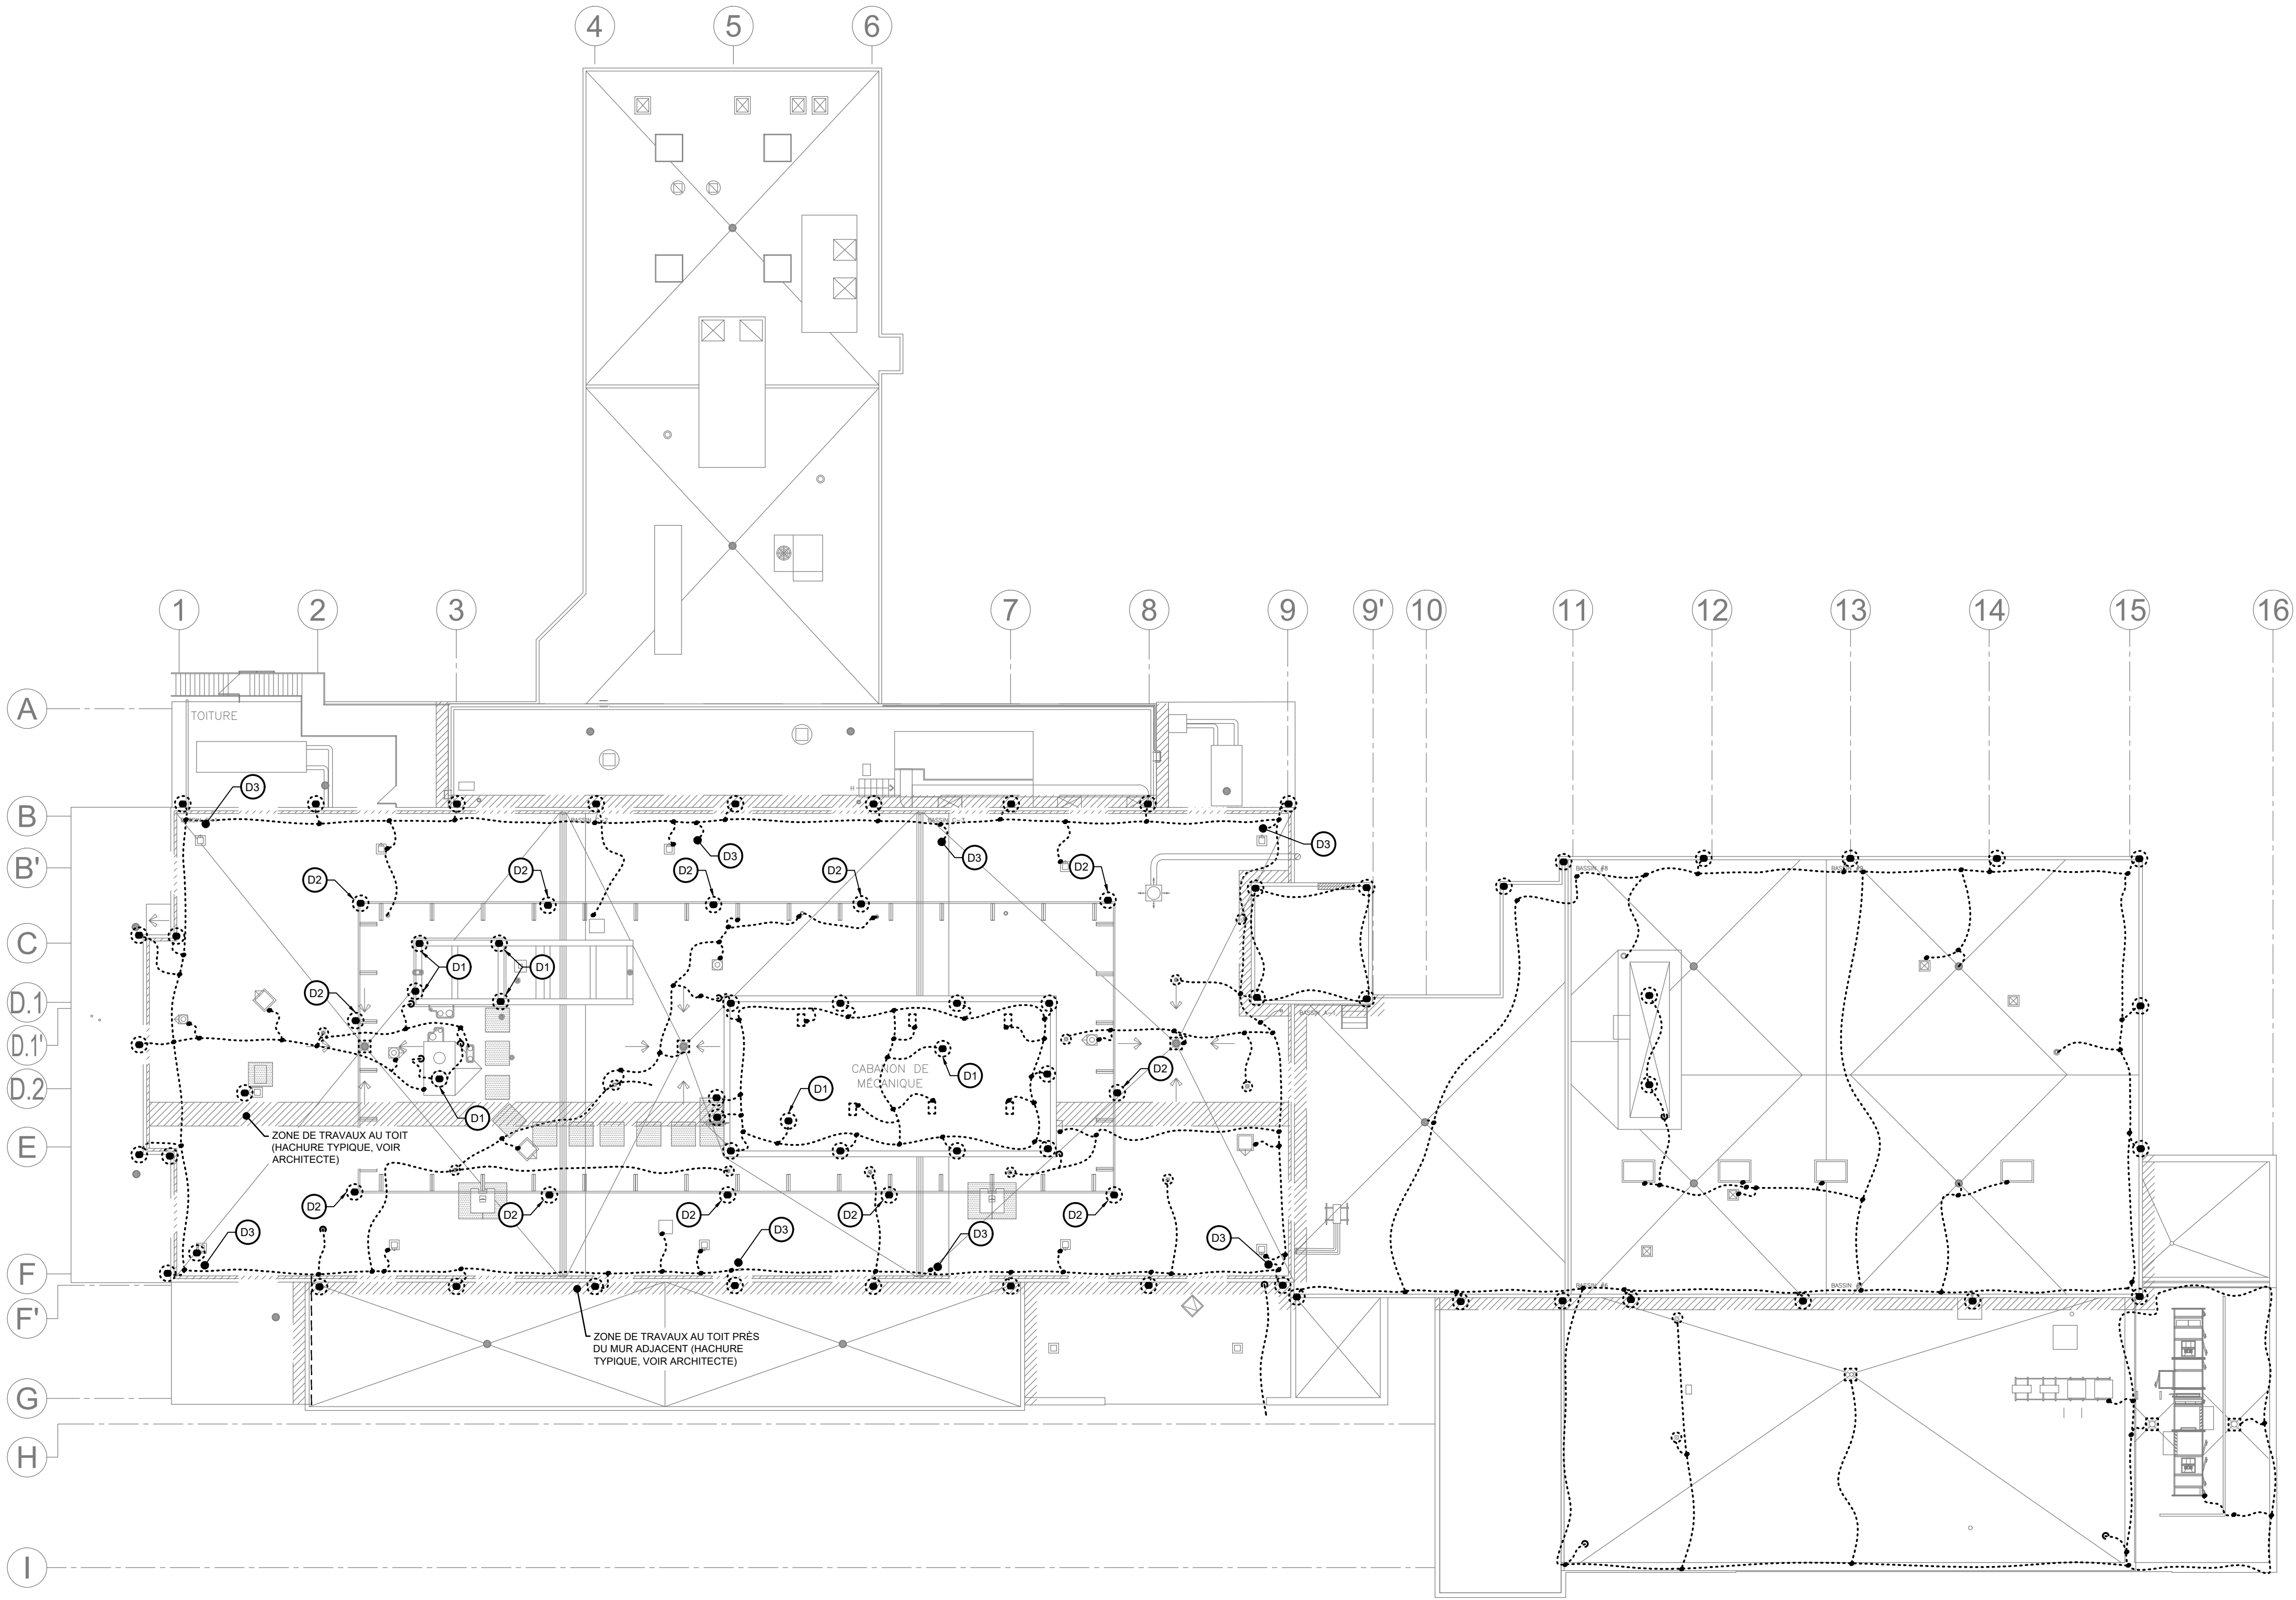

TOITURE - DÉMOLITION
ÉCHELLE: 1:200

LÉGENDE ÉLECTRIQUE

MISE À LA TERRE ET PARATONNERRE

- TIGE DE MISE À LA TERRE
- ⦿ TIGE DE MISE À LA TERRE AVEC Puits d'inspection
- Soudure aluminothermique
- BRANCHEMENT COMPRESSÉ DE STYLE «LUG»

LÉGENDE MÉCANIQUE

- AVALOIR DE TOITURE
- SORTIE D'ÉVENT AU TOIT

NOTES GÉNÉRALES - PORTÉE DE TRAVAUX PARATONNERRE

- L'ENTREPRENEUR SPÉCIALISÉ EN PARATONNERRE DOIT FAIRE LE DÉMONTÉMENT DU SYSTÈME EN PLACE, SANS S'Y LIMITER:
 - TIGES DE CAPTATION
 - RACCORDS SUR LES ÉQUIPEMENTS MÉTALLIQUES
 - CONDUCTEUR APPARENTS
 - DESCENTES SITUÉES À L'INTÉRIEUR DE L'URÉTHANE QUI SERA ENLEVÉ DANS LE CADRE DU PROJET.
- LA DÉMOLITION DES DESCENTES À L'INTÉRIEUR DU BÂTIMENT AINSI QUE LES TIGES DE TERRE SONT EXCLUS DU PRÉSENT MANDANT.
- LORSQUE LA DESCENTE PASSE À TRAVERS UN COL DE CYGNE (POUR EFFECTUER LA DESCENTE À L'INTÉRIEUR DU BÂTIMENT), OBTURER L'OUVERTURE DE FAÇON ÉTANCHE.
- IDENTIFIER LE MATÉRIEL AVANT LE DÉMONTÉMENT. ENTREPOSER, À L'ENDROIT DÉSIGNÉ PAR LE PROPRIÉTAIRE, LE MATÉRIEL DÉMANTÉLÉ.
- INDIQUER LES LIMITES DE DÉMOLITION SUR LES PLANS ANNOTÉS PAR L'ENTREPRENEUR.
- FOURNIR UN RAPPORT PHOTOGRAPHIQUE DES INSTALLATIONS.
- LE PLAN EST À TITRE INDICATIF SEULEMENT. LE NOMBRE DE COMPOSANTE PEUT VARIER.

NOTES DÉMOLITION - PARATONNERRE

- D1 TIGE DE CAPTATION INSTALLÉ SUR L'ANTENNE OU UNE ÉCHELLE OU UN ÉQUIPEMENT MÉCANIQUE OU UNE CHEMINÉE À DÉMANTÉLER.
- D2 TIGE DE CAPTATION INSTALLÉ SUR LE MUR-ÉCRAN À DÉMANTÉLER.
- D3 COL DE CYGNE C/A UNE DESCENTE INTÉRIEURE.



SANTÉ QUÉBEC GASPÉSIE

RÉF. CLIENT:
PROJET

HÔPITAL DE CHANDLER
(RÉFECTION DE L'ENVELOPPE)

Architecte




CE DOCUMENT NE DOIT PAS SERVIR À
LA CONSTRUCTION

REV	DATE	DESCRIPTION	PAR
RÉVISIONS PARTIELLES			
1	2026/09/04	DÉFINITIFS POUR SOUMISSION	JD-JA
B	2026/08/21	DÉFINITIFS 100% POUR APPROBATION	JD-VS
A	2026/05/14	DÉFINITIFS 60% POUR APPROBATION	JD-VS
REV	DATE	DESCRIPTION	PAR


SCEAU:	
AVERTISSEMENT: DROIT D'AUTEUR: CE DESSIN EST LA PROPRIÉTÉ INTELLECTUELLE DE WSP CANADA INC. AUCUNE RÉVISION, REPRODUCTION OU TOUT AUTRE USAGE N'EST PERMIS SANS L'AUTORISATION ÉCRITE DE WSP CANADA INC. L'ENTREPRENEUR DEVRA VÉRIFIER TOUTES LES DIMENSIONS AUX PLANS ET FAIRE LOCALISER TOUS LES SERVICES D'UTILITÉS PUBLIQUES ET RAPPORTER TOUTES ERREURS OU OMISSIONS AVANT DE COMMENCER LES TRAVAUX.	
ÉCHELLE: ORIGINALE: INDIQUÉE DESSINÉ PAR: A. CASTONGUAY PRÉPARÉ SOUS SUPERVISION PAR: J. D'AMOURS ET V. STOCKMEYER, ing. PRÉPARÉ PAR: J. D'AMOURS ET J. ALCINDOR, ing. APPROUVÉ ADMINISTRATIVEMENT PAR: S. L'AVOIE	DATE: AVRIL 2026 SI CETTE BARRE NE MESURE PAS 25 mm, AJUSTER VOTRE ÉCHELLE DE TRAVAIL: 25mm
DISCIPLINE: MÉCANIQUE / ÉLECTRIQUE	

Mécanique / Électricité
NO PROJET: CA0066110.3235
TITRE: TOITURE - PARATONNERRE DÉMOLITION
NUMÉRO DU FEUILLET: ME005D

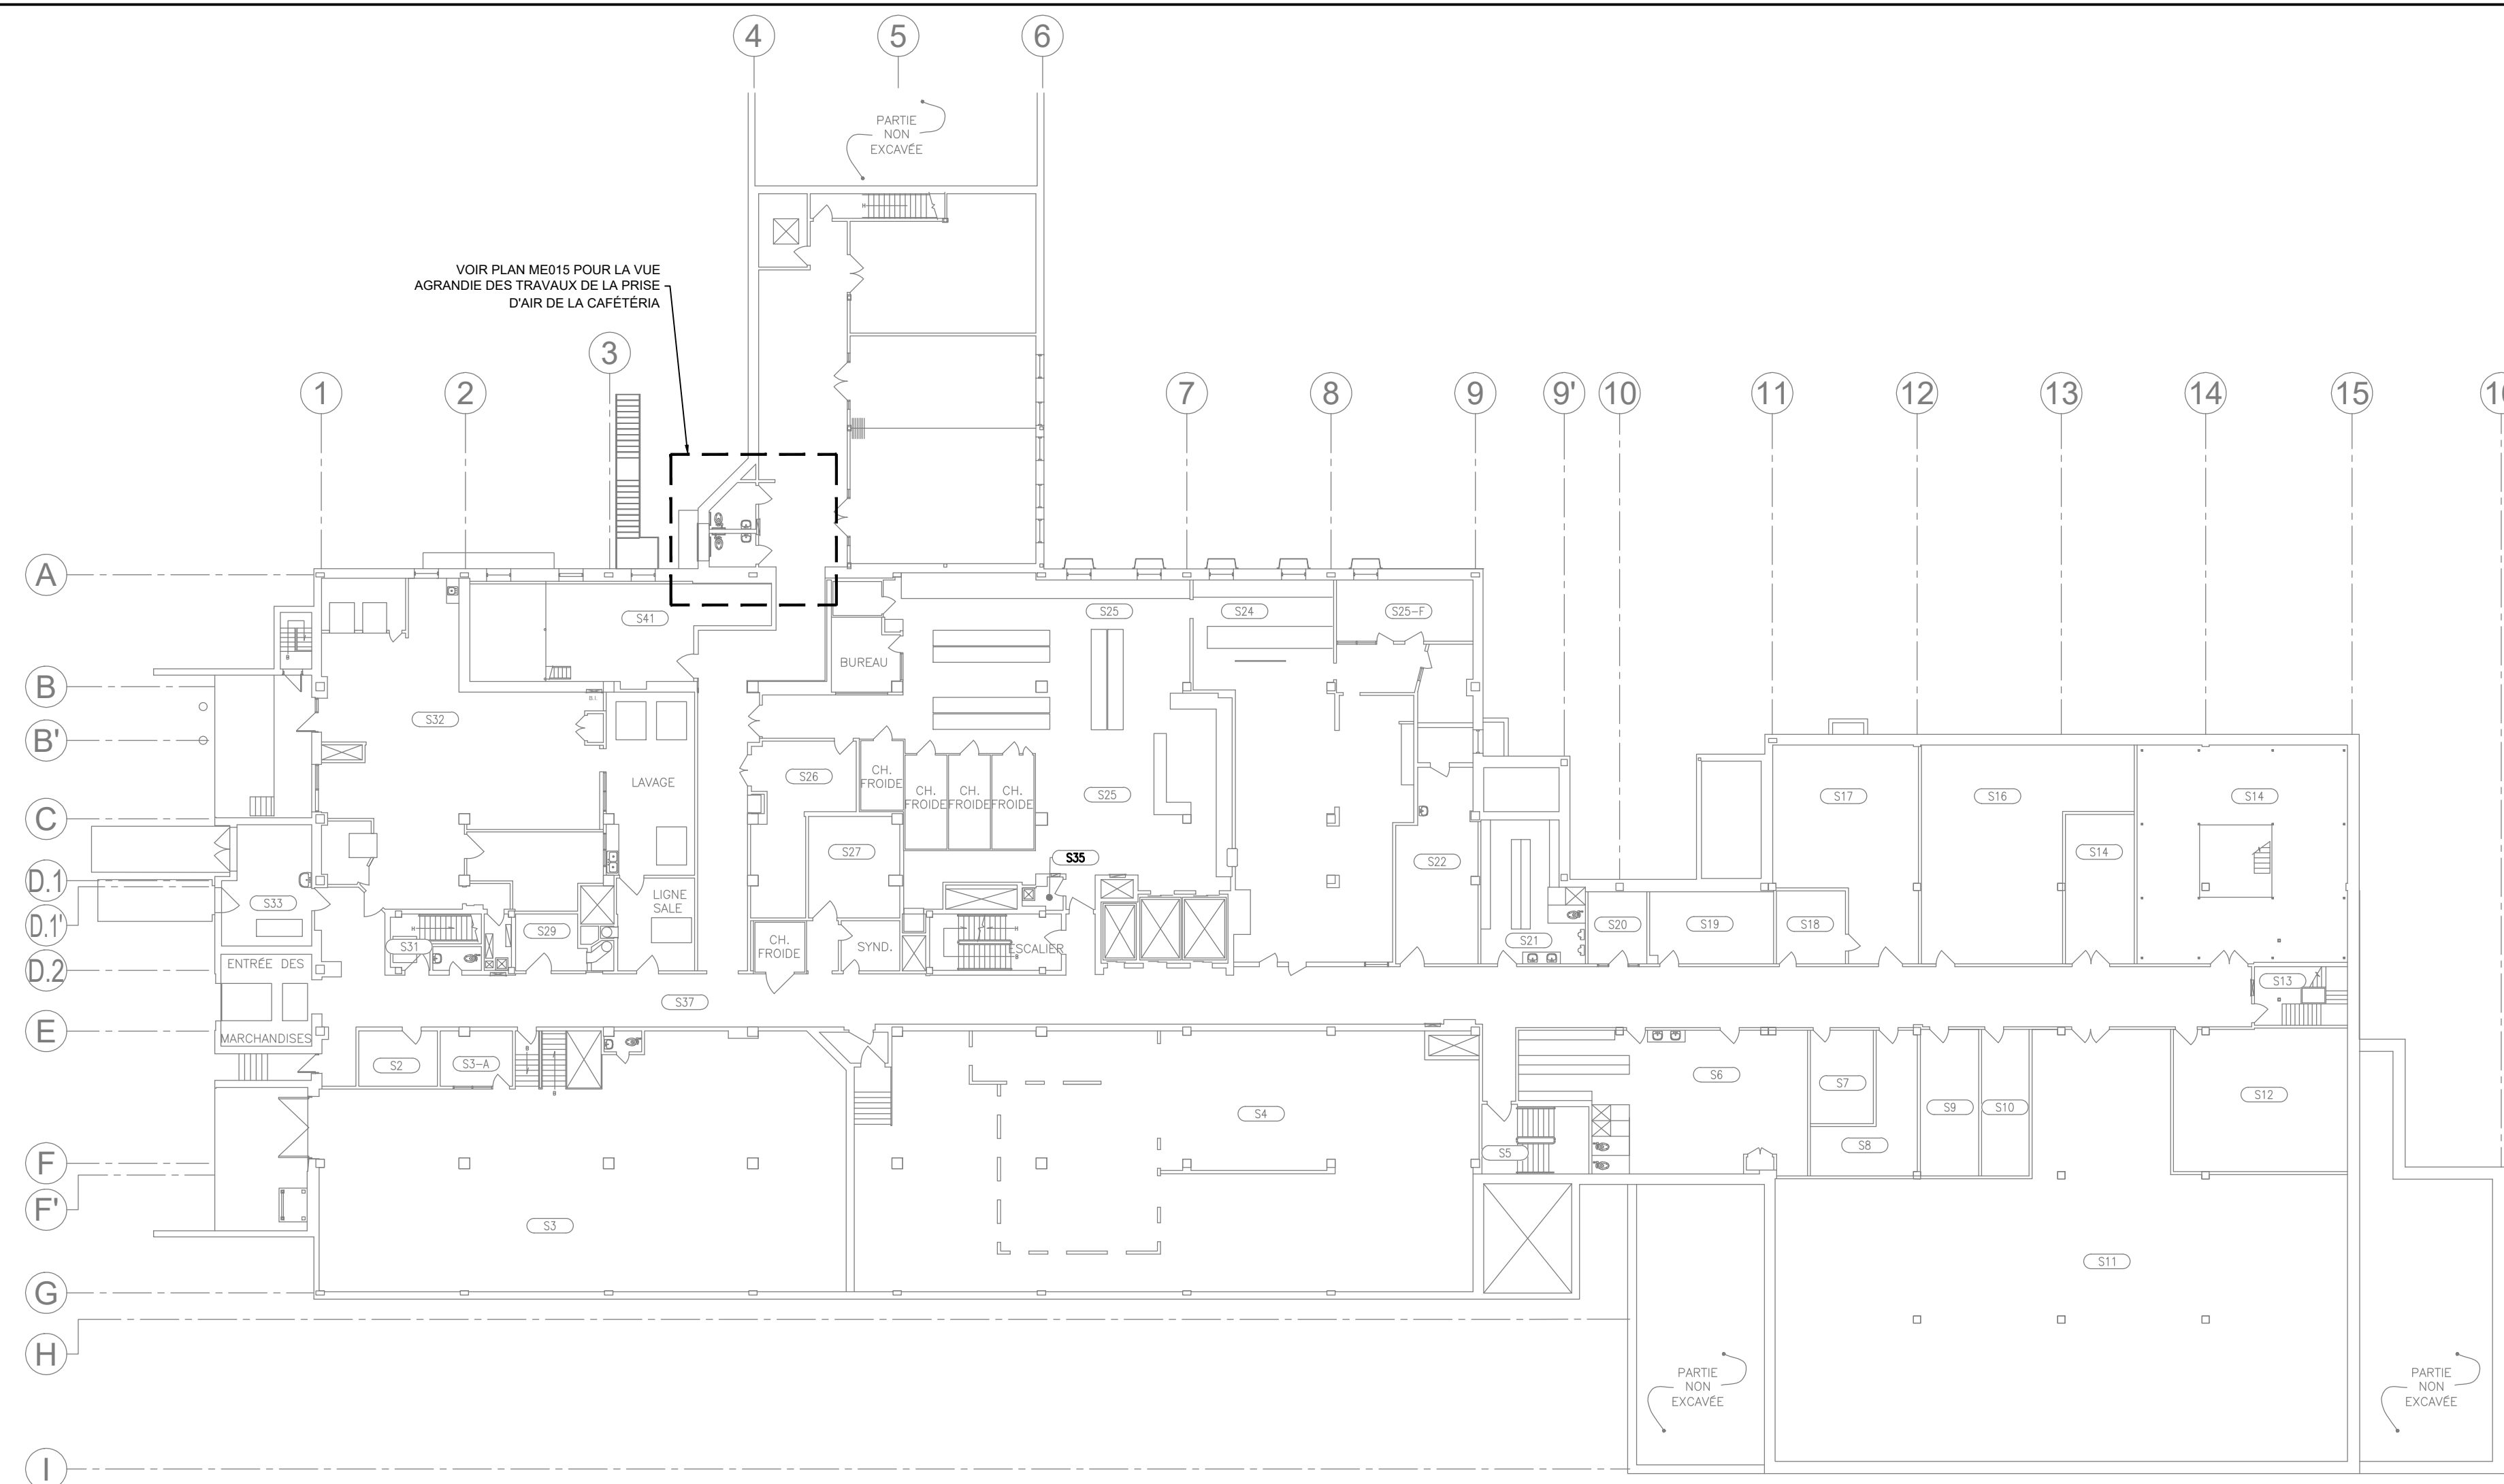

SOUS-SOL - EXISTANT - LOCALISATION DES TRAVAUX INTÉRIEURS

ÉCHELLE: 1:200

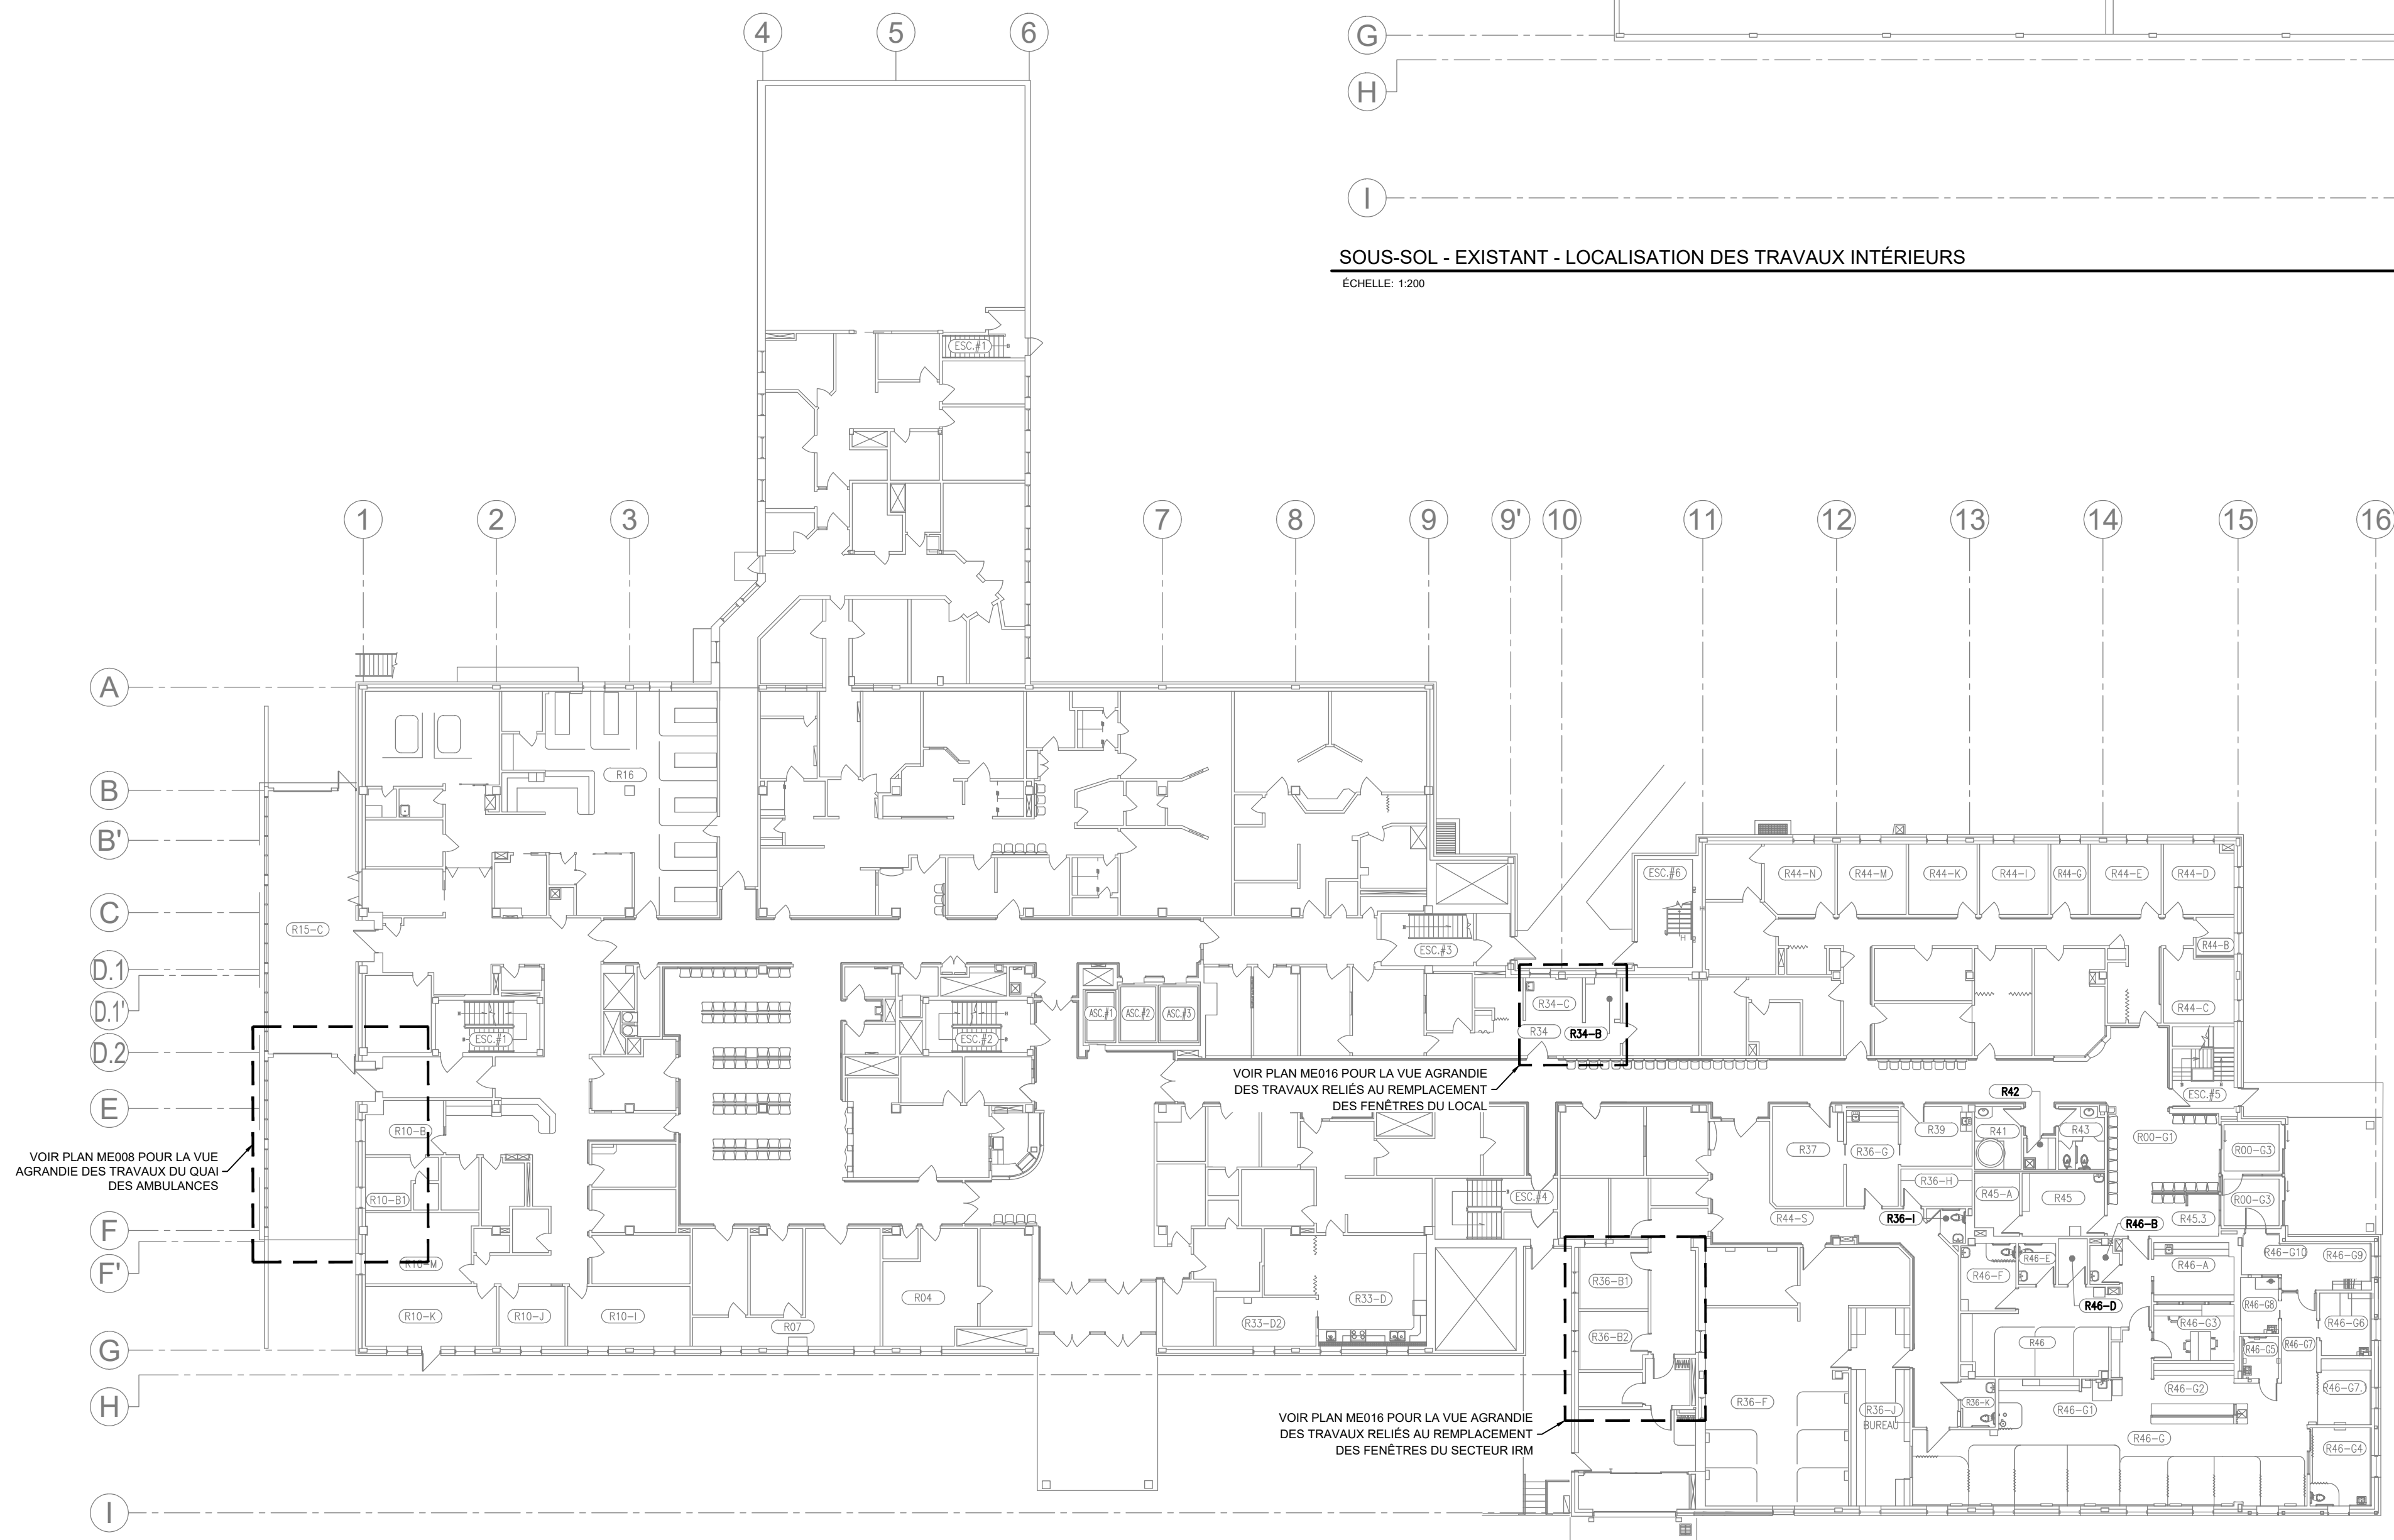


REZ-DE-CHAUSSÉE - EXISTANT - LOCALISATION DES TRAVAUX INTÉRIEURS

ÉCHELLE: 1:200

CE DOCUMENT **NE DOIT PAS** SERVIR À
LA CONSTRUCTION

REV	DATE	DESCRIPTION	PAR
RÉVISIONS PARTIELLES			
1	2026/09/04	DÉFINITIFS POUR SOUMISSION	JDJA
B	2026/08/21	DÉFINITIFS 100% POUR APPROBATION	JDDVS
A	2026/05/14	DÉFINITIFS 60% POUR APPROBATION	JDDVS
REV	DATE	DESCRIPTION	PAR

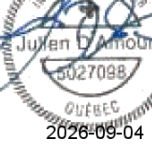SCÉAU :  2020-05-04	 2020-09-04
MÉCANIQUE	ÉLECTRICITÉ
AVERTISSEMENT : LE BRESSIN EST LA PROPRIÉTÉ INTELLECTUELLE DE WSP CANADA INC. AUCUNE RÉVISION, RÉPRODUCTION OU TOUT AUTRE USAGE N'EST PERMIS SANS L'AUTORISATION ÉCRITE DU BRESSIN. IL EST INTERDIT DE REPRODUIRE, DE VÉRIFIER TOUTES LES DIMENSIONS AUX PLANS ET FAIRE LOCALISER TOUTES LES SERVICES DOUTILES PARQUOI LE BRESSIN RAPORTE TOUTES ERREURS OU OMISSIONS AVANT DE COMMENCER LES TRAVAUX.	
ÉCHELLE ORIGINALE : INDIQUÉE Dessiné PAR : A. CASTONGUAY INFORMÉ SOUS SUPERVISION PAR : J. D'AMOURS ET V. STOCKMEYER, ing. PRÉPARÉ PAR : J. D'AMOURS ET J. ALCINDOR, ing. APPROUVE ADMINISTRATIVEMENT PAR : G. LAVOIE	DATE : AVRIL 2026 SI CETTE BARRE NE MESURE PAS 25 mm, AJUSTER VOTRE ÉCHELLE DE TRAÇAGE.  25mm
DISCIPLINE : MÉCANIQUE / ÉLECTRICITÉ	


Mécanique / Électricité

WSP


NO PROJ: CA0066110.3235

TITRE:	
SOUS-SOL ET REZ-DE-CHAUSSÉE LOCALISATION DES TRAVAUX INTÉRIEURS	
NUMÉRO DU FEUILLET:	ME006


ÉCHELLE: 1:250

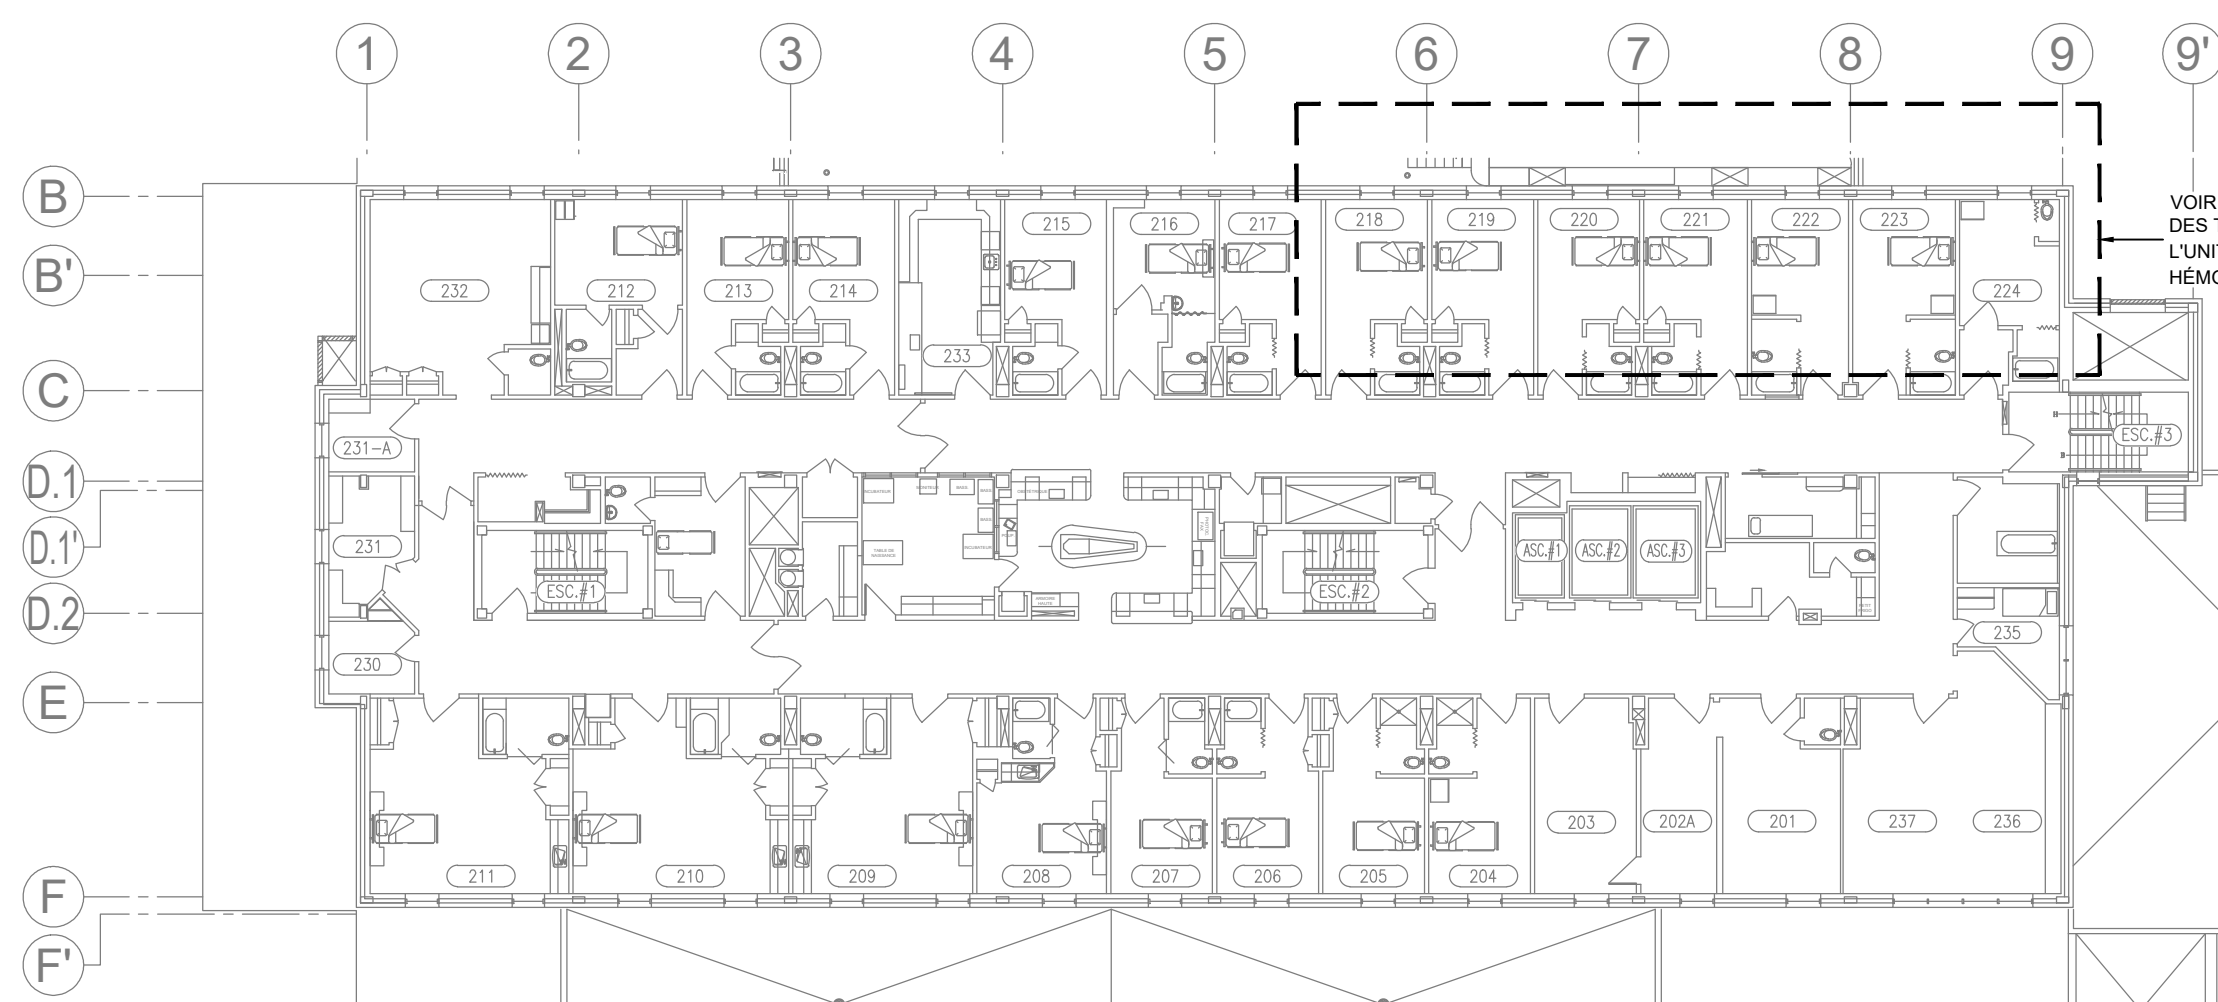

ÉCHELLE: 1:250

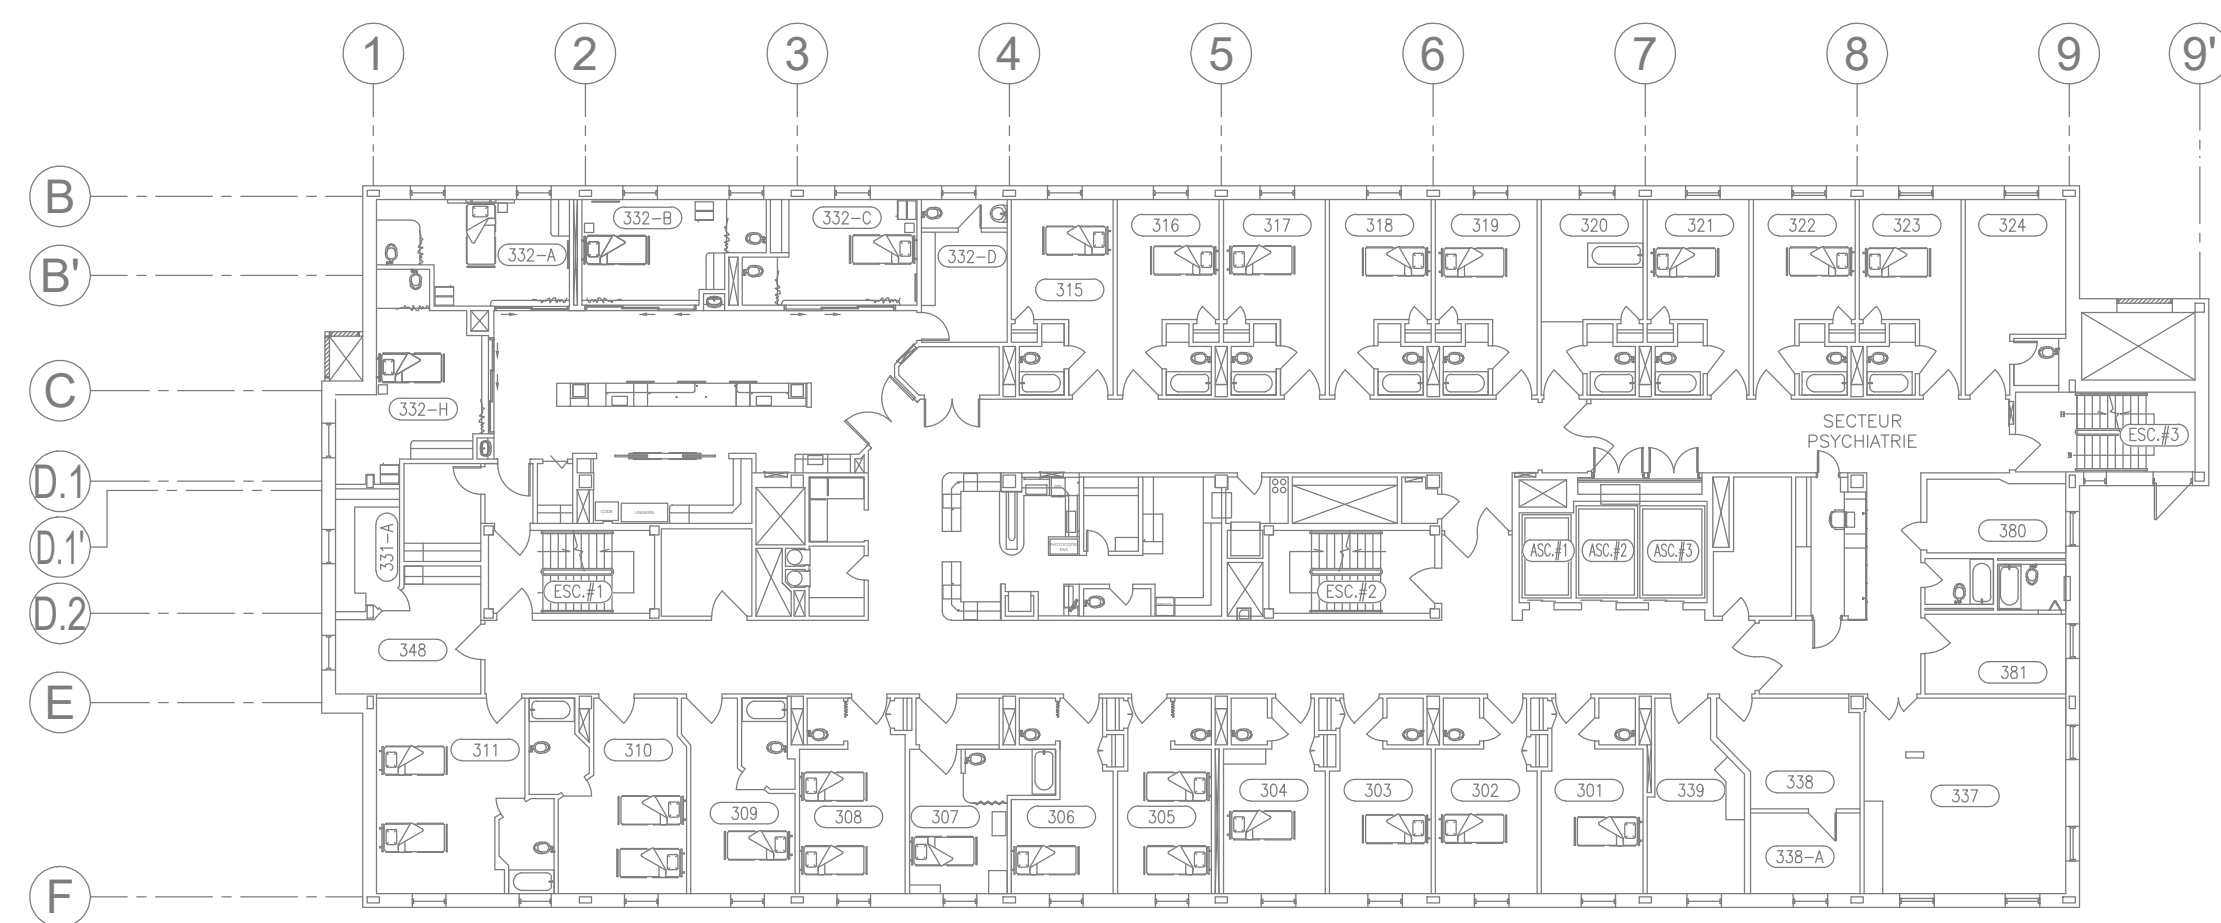

ÉCHELLE: 1:250

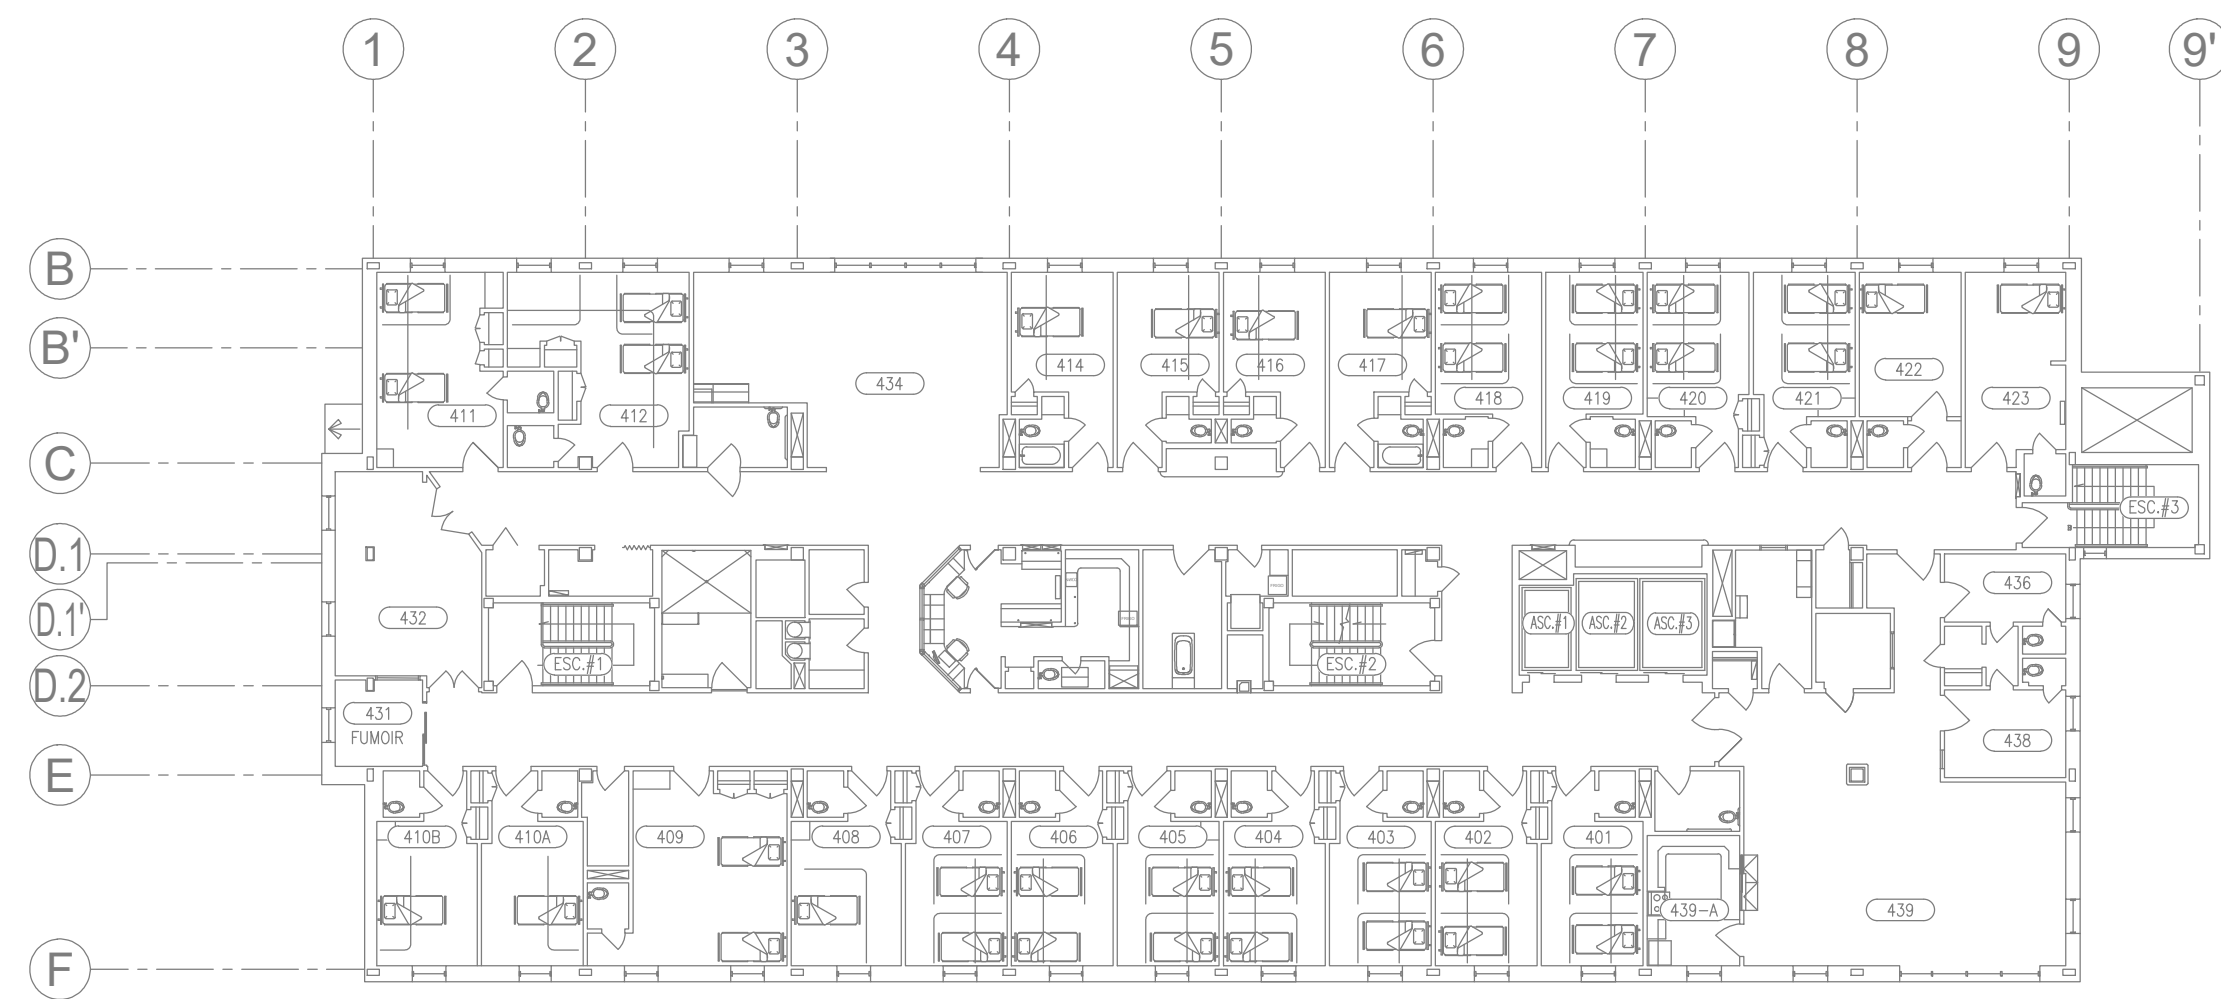

ÉCHELLE: 1:250

CE DOCUMENT **NE DOIT PAS** SERVIR À
LA CONSTRUCTION


[illegible]

RÉVISIONS PARTIELLES			
----------------------	--	--	--

1	2026/09/04	DÉFINITIFS POUR SOUMISSION	JD-JA
B	2026/08/21	DÉFINITIFS 100% POUR APPROBATION	JD-VS
A	2026/05/14	DÉFINITIFS 60% POUR APPROBATION	JD-VS

REV	DATE	DESCRIPTION	PAR
-----	------	-------------	-----

SCEAU:

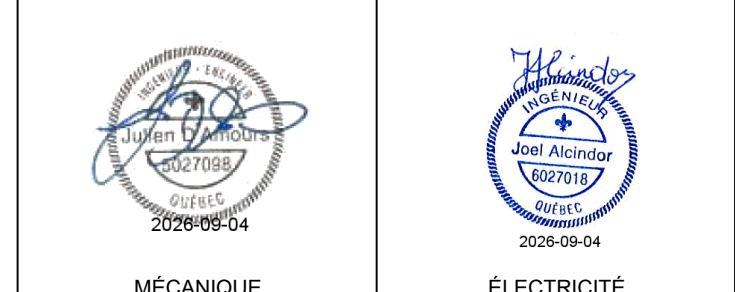

AVERTISSEMENT:	DROIT D'AUTEUR:
----------------	-----------------

CE DESSIN EST LA PROPRIÉTÉ INTELLECTUELLE DE WSP CANADA INC. AUCUNE RÉVISION, REPRODUCTION OU TOUT AUTRE USAGE N'EST PERMIS SANS L'AUTORISATION ÉCRITE DE WSP CANADA INC. L'ENTREPRENEUR DEVRA VÉRIFIER TOUTES LES DIMENSIONS AUX PLANS ET FAIRE LOCALISER TOUS LES SERVICES D'UTILITÉS PUBLIQUES ET RAPPORTER TOUTES ERREURS OU OMISSIONS AVANT DE COMMENCER LES TRAVAUX.

ECHELLE ORIGINALE: INDIQUÉE DESSINE PAR : A. CASTONGUAY & A. HALLÉ PRÉPARE SOUS SUPERVISION PAR : J. D'AMOURS ET V. STOCKMEYER, ing. PRÉPARE PAR : J. D'AMOURS ET J. ALCINDOR, ing. APPROUVE ADMINISTRATIVEMENT PAR : G. LAVOIE	DATE : AVRIL 2026 SI CETTE BARRE NE MESURE PAS 25 mm, AJUSTER VOTRE ECHELLE DE TRAÇAGE.
---	---


DISCIPLINE: MÉCANIQUE / ÉLECTRIQUE

Mécanique / Électricité

NO PROJET: CA0066110.3235


NIVEAUX 100, 200, 300 ET 400
LOCALISATION DES TRAVAUX
INTÉRIEURS

NUMÉRO DU
FEUILLET: ME007

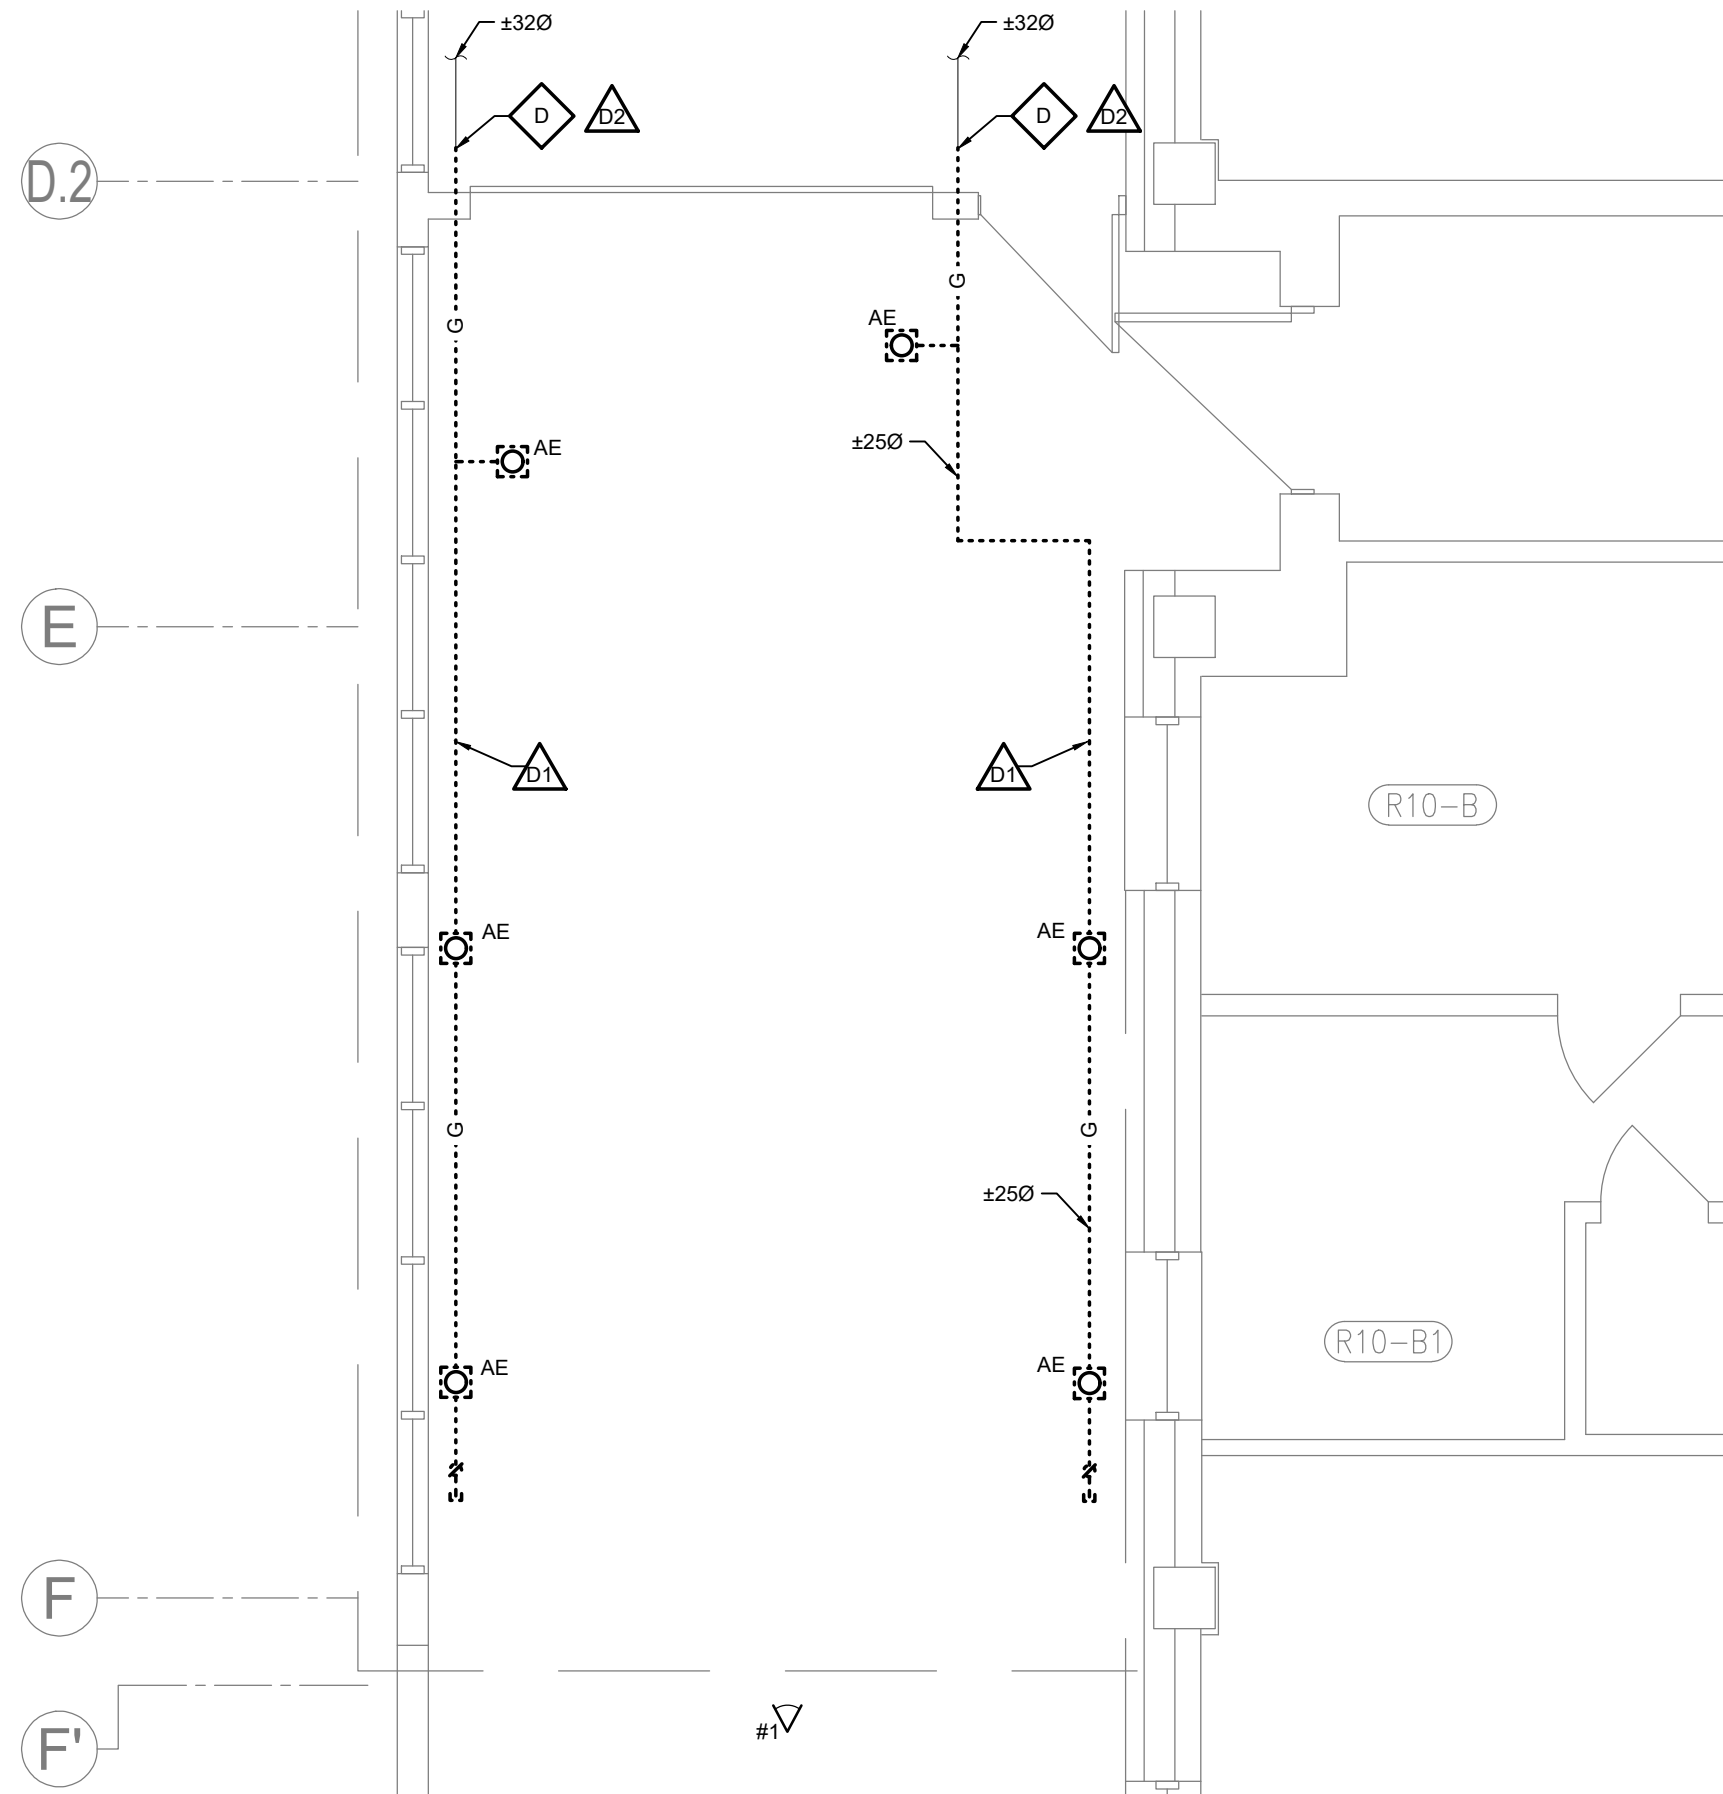


VUE AGRANDIE - QUAI DES AMBULANCES - PROTECTION-INCENDIE - DÉMOLITION

ÉCHELLE: 1:50

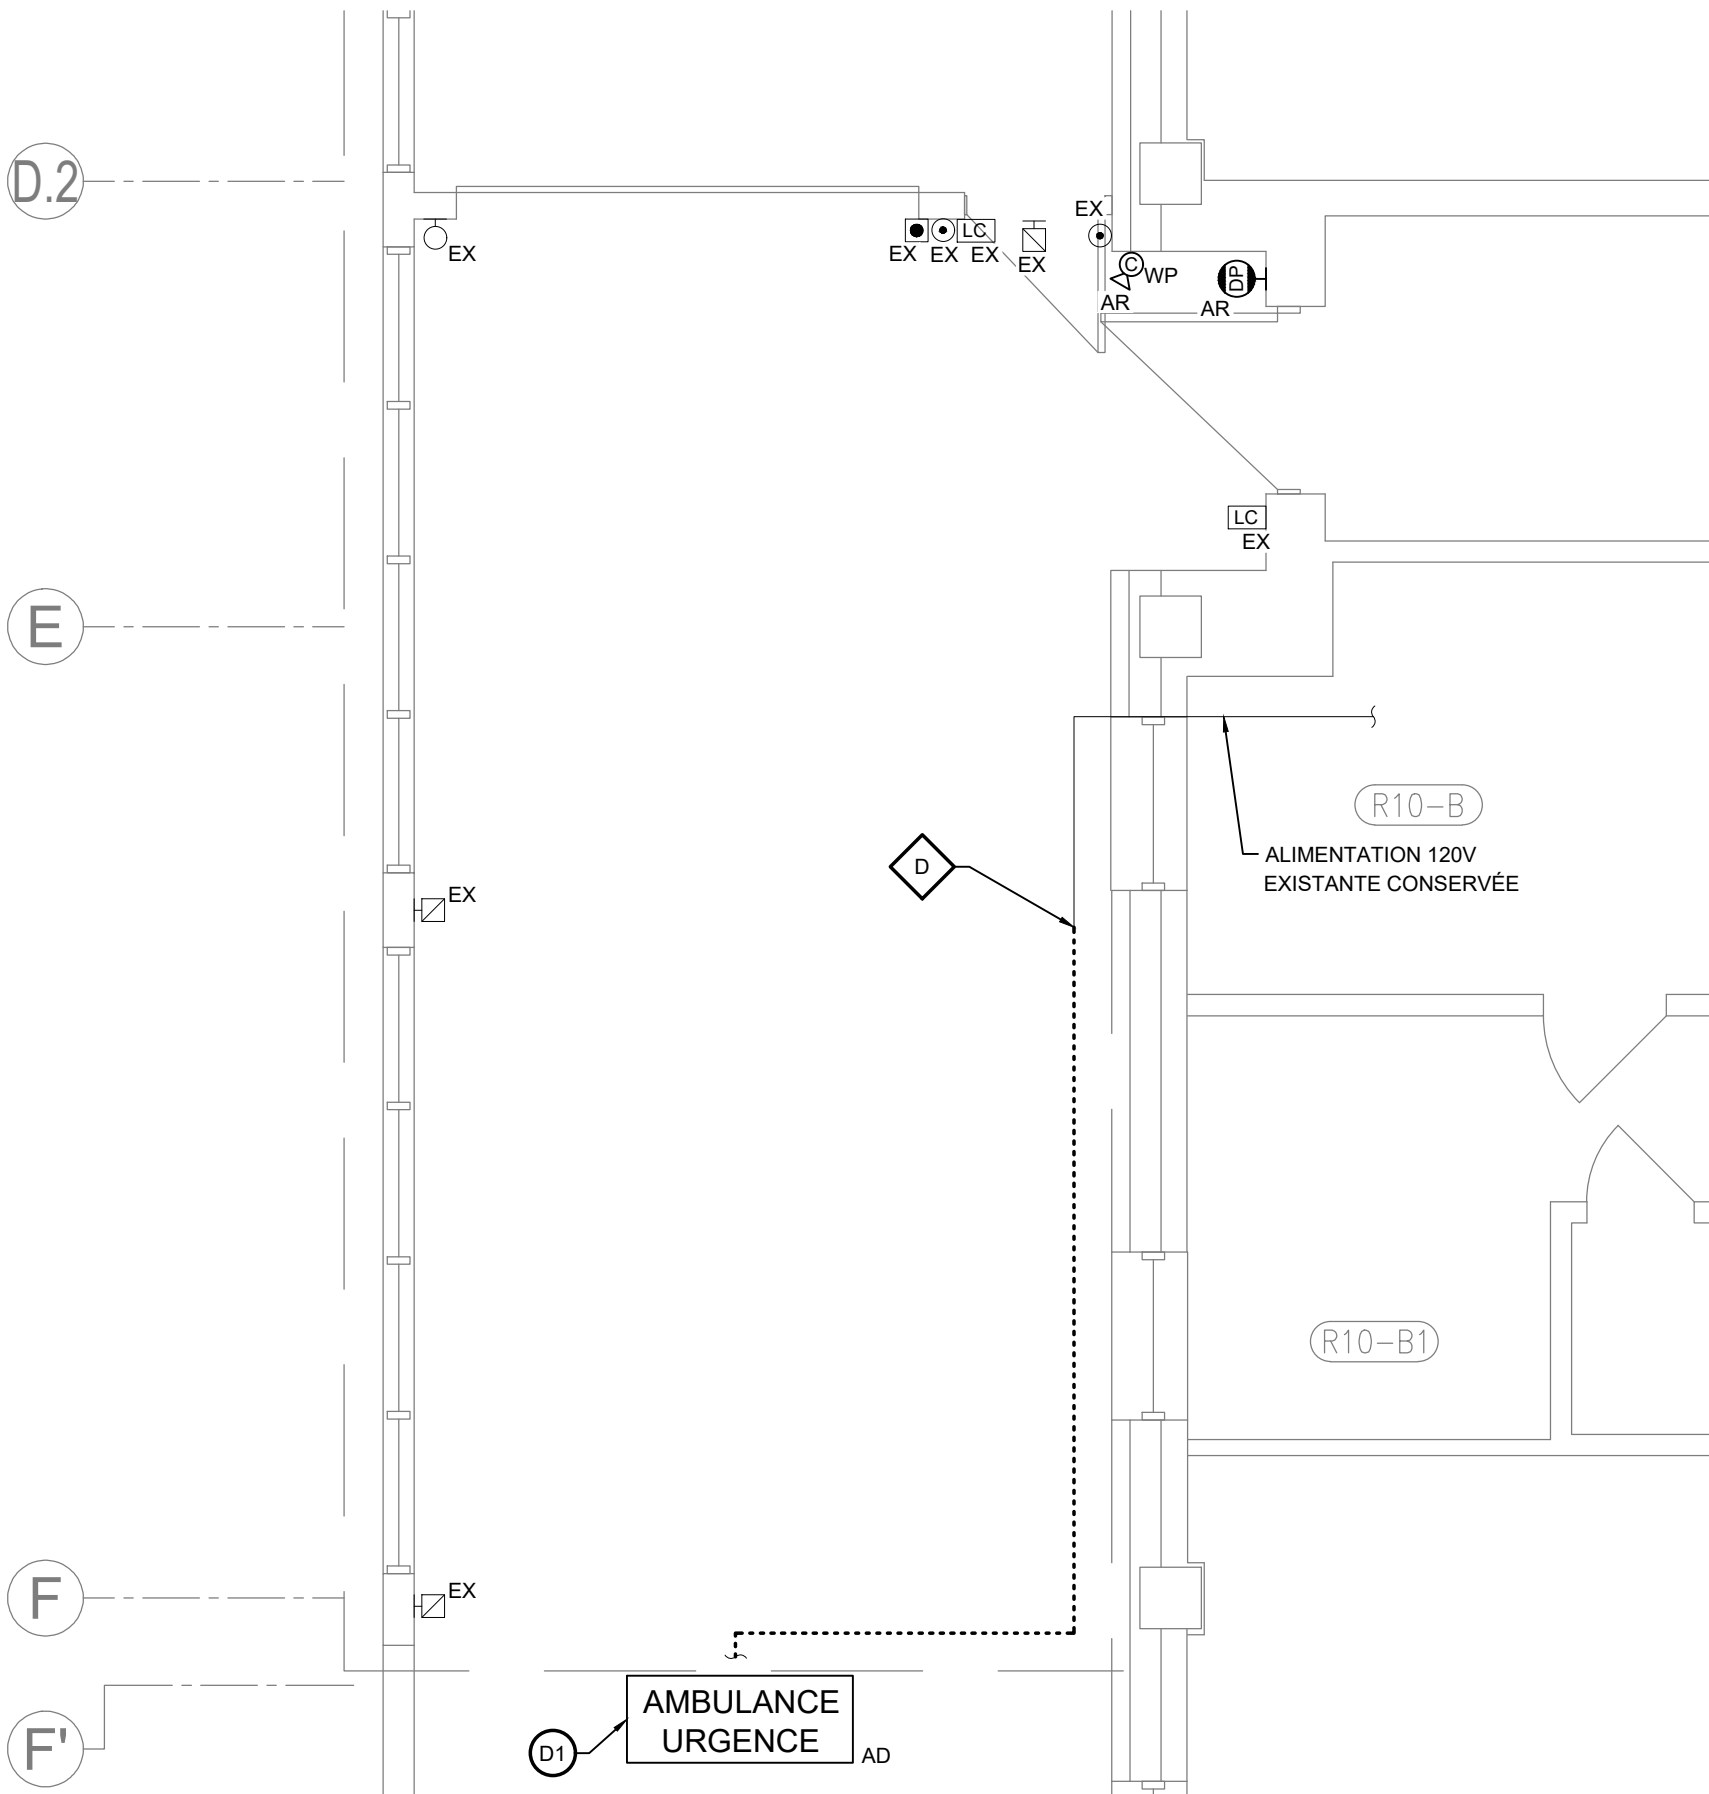


VUE AGRANDIE - QUAI DES AMBULANCES - ÉLECTRICITÉ - DÉMOLITION

ÉCHELLE: 1:50

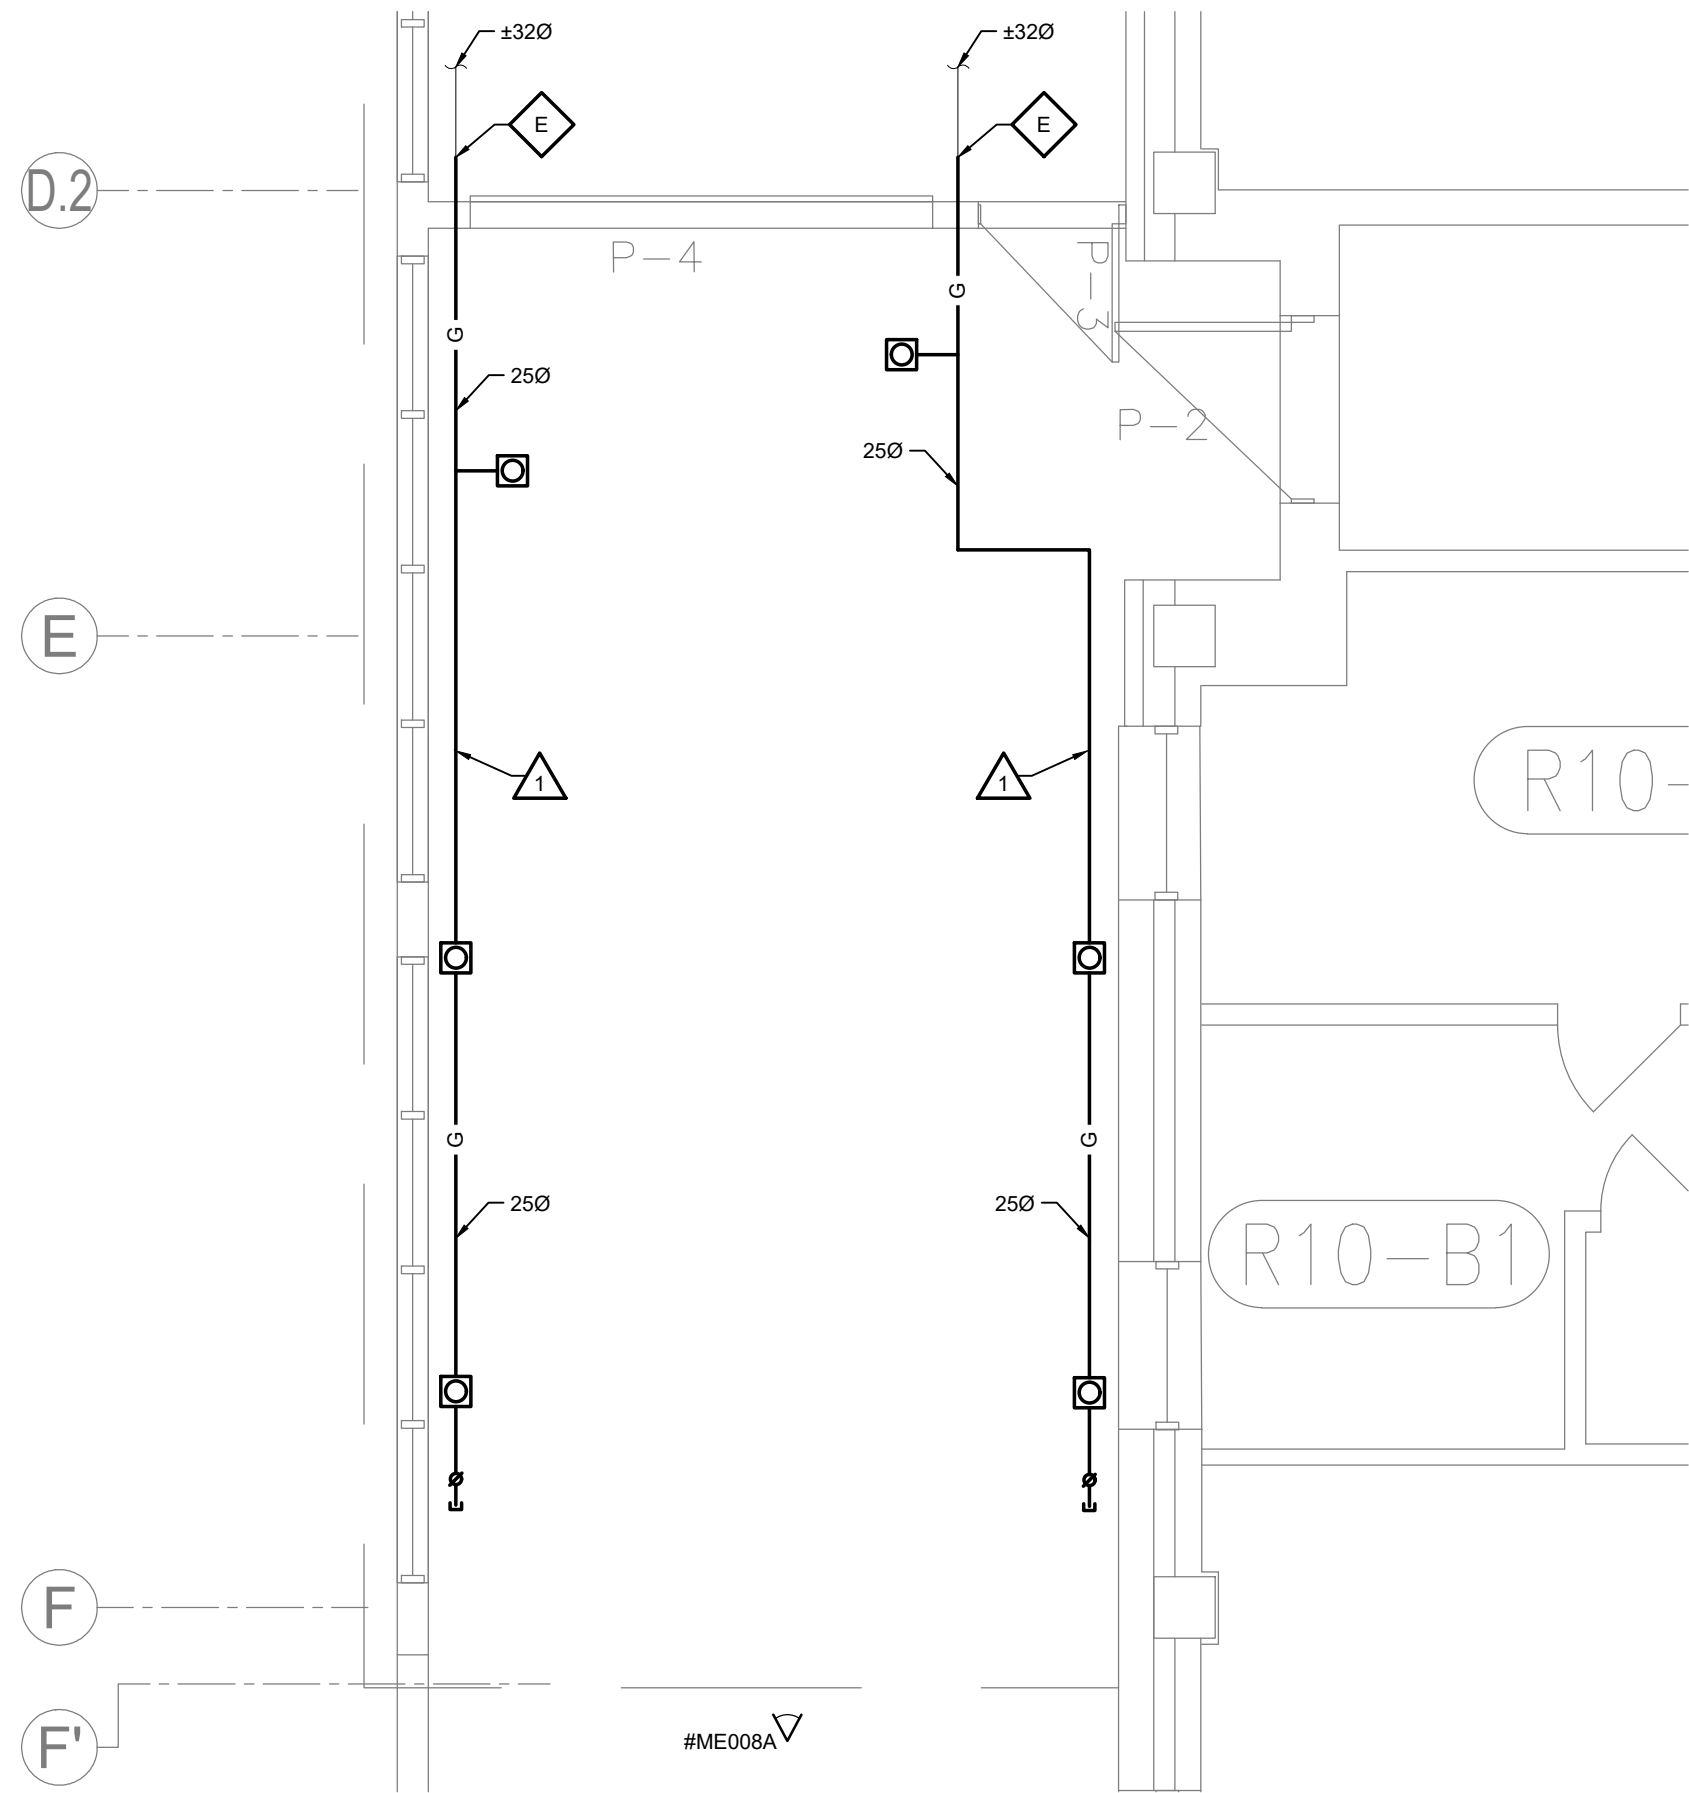

VUE AGRANDIE - QUAI DES AMBULANCES - PROTECTION-INCENDIE - CONSTRUCTION

ÉCHELLE: 1:50

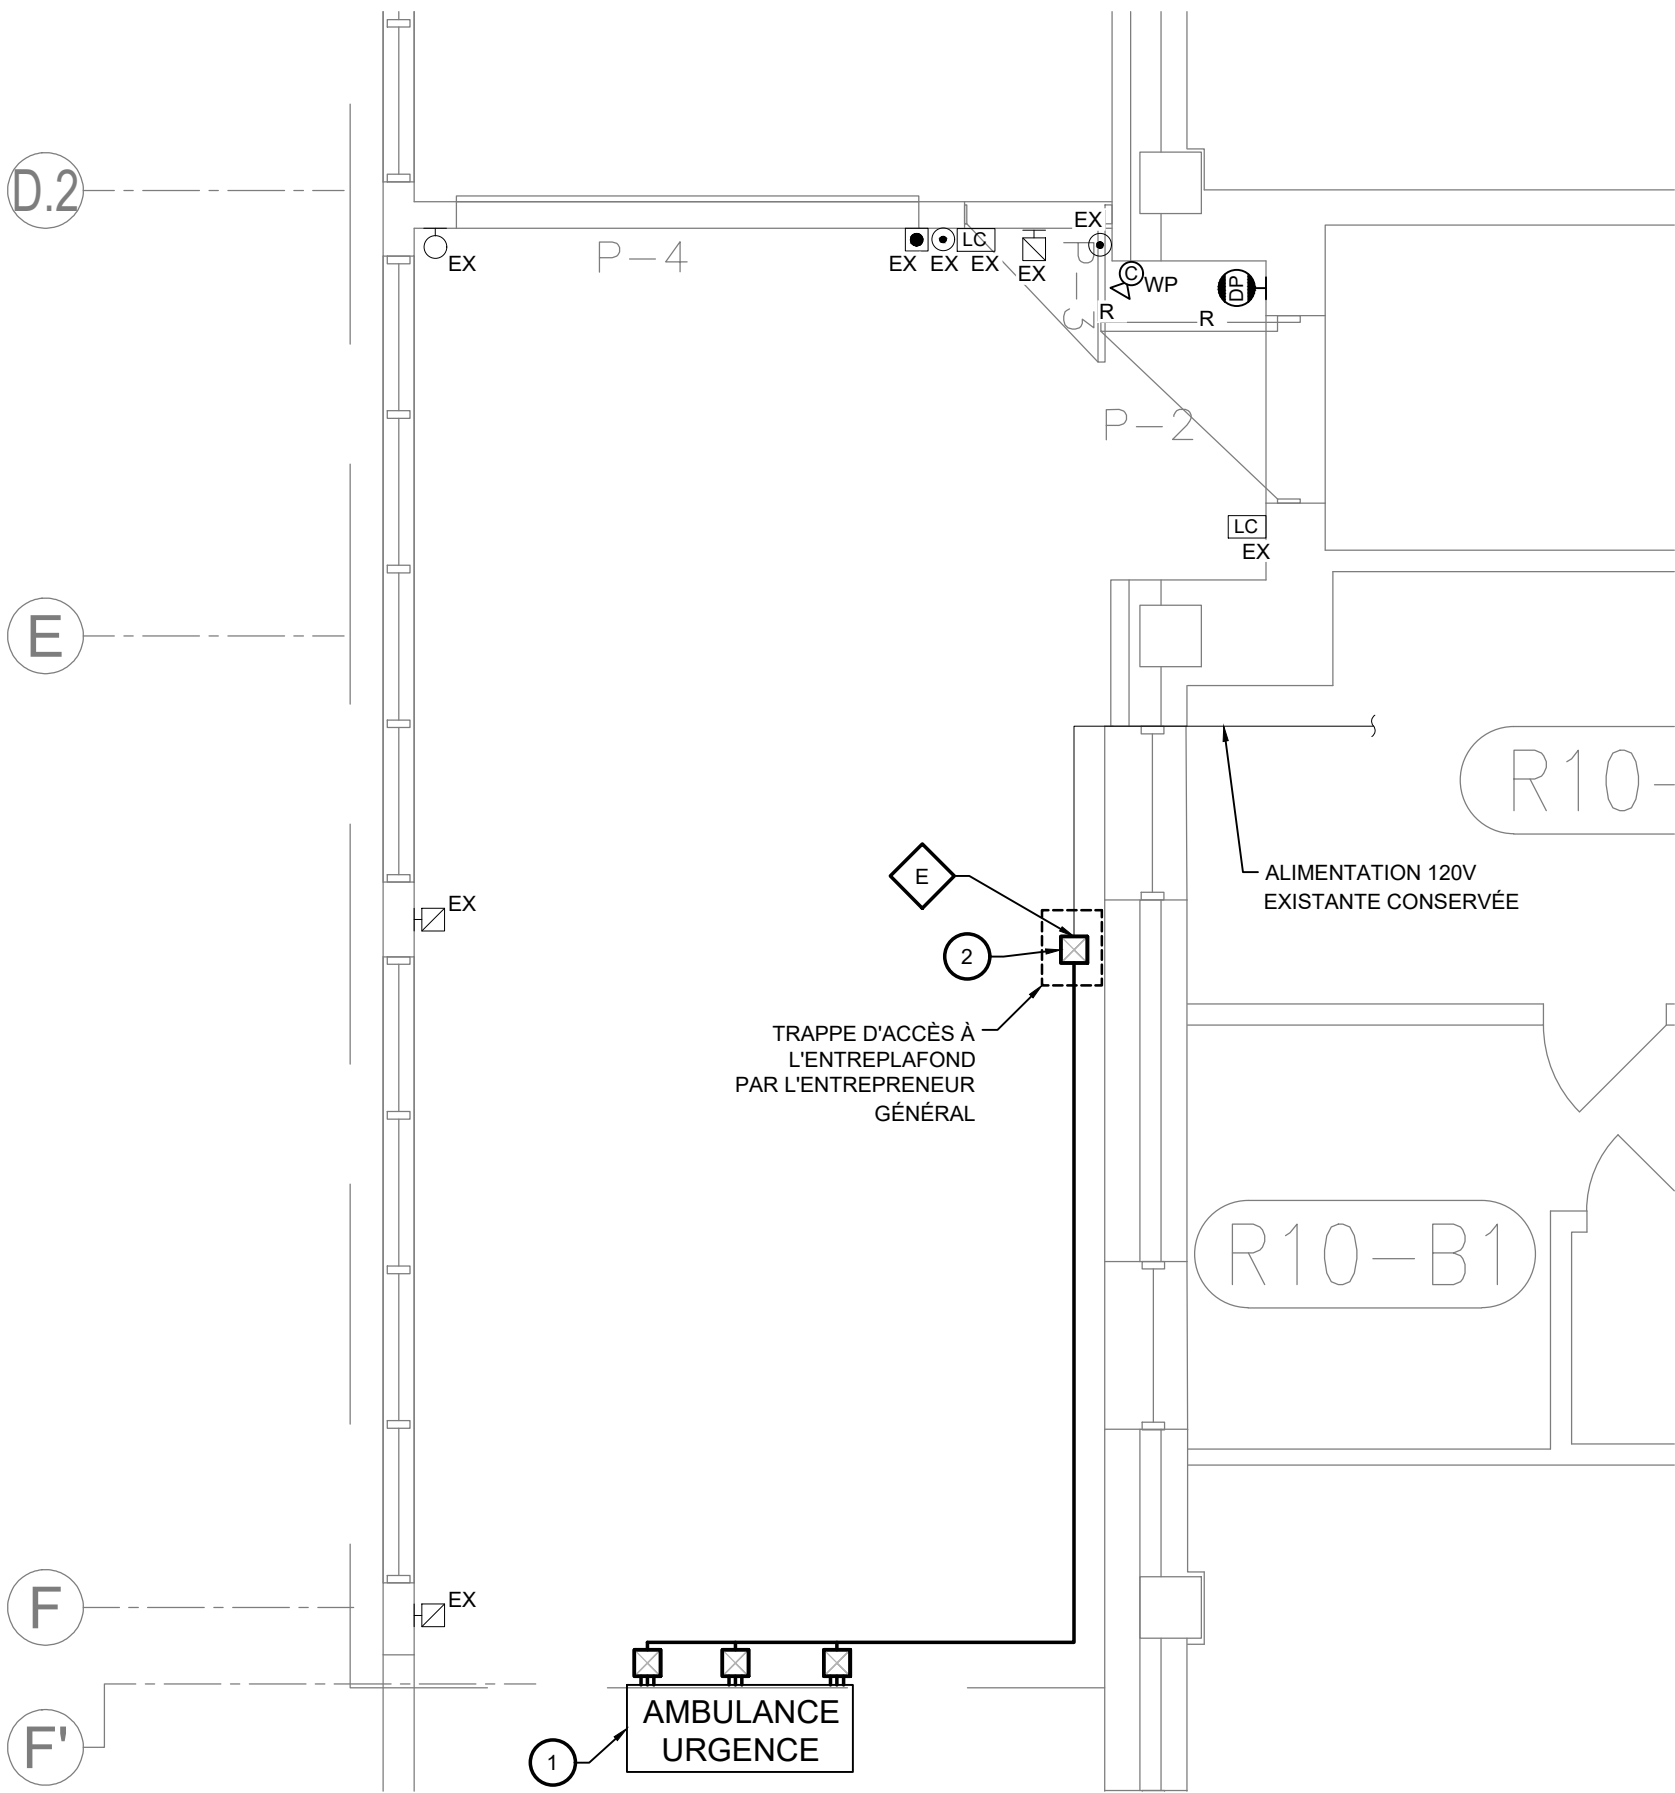

VUE AGRANDIE - QUAI DES AMBULANCES - ÉLECTRICITÉ - CONSTRUCTION

ÉCHELLE: 1:50

NOTE GÉNÉRALE

- LA DURÉE DES TRAVAUX DEVANT LES PORTES DE GARAGE DES AMBULANCES EST LIMITÉE (VOIR DOCUMENTS DE PHASAGE EN ARCHITECTURE). LES APPAREILS À RELOCALISER OU REMPLACER DOIVENT ÊTRE ENLEVÉS SEULEMENT LORSQUE LE SECTEUR EST EN TRAVAUX ET REINSTALLÉS AUSSIÔT QUE LES TRAVAUX SONT TERMINÉS DEVANT LA PORTE DE GARAGE.

NOTES DÉMOLITION - ÉLECTRICITÉ

- ENSEIGNE LUMINEUSE À DÉBRANCHER PAR L'ÉLECTRICIEN JUSQU'À L'INTÉRIEUR DU PLAFOND EXTÉRIEUR DEVANT L'ENTRÉE DES AMBULANCE (SUD). CÂBLAGE À MODIFIER.

NOTES DÉMOLITION - GICLEURS

- GICLEURS EXISTANTS ET TUYAUTERIE ASSOCIÉE EXISTANTE (Ø 32 MM / 1 1/4 PO) SITUÉE SOUS LE TOIT DE L'ENTRÉE DES AMBULANCES (SUD), À DÉMANTELER TEMPORAIREMENT. PRÉVOIR LA MISE HORS-SERVICE DE CETTE ZONE DU SYSTÈME DE PROTECTION INCENDIE ET L'OBTURATION TEMPORAIRE DE LA TUYAUTERIE. PRÉVOIR LA RÉCUPÉRATION DU GLYCOL. LA TUYAUTERIE ET LES SUPPORTS SONT À RÉCUPÉRER ET MODIFIER. REMPLACER LES GICLEURS TEL QUE L'EXISTANT.
- POINT LIMITE DE DÉMOLITION AU PREMIER RACCORD PRÈS DU MUR À L'INTÉRIEUR DU BÂTIMENT. LE SYSTÈME DE REMPLISSAGE ET LES ROBINETS D'ARRÊT DU RÉSEAU GLYCOL SONT LOCALISÉES À L'INTÉRIEUR DU BÂTIMENT PRÈS DE L'ENTRÉE DU GARAGE.

NOTES CONSTRUCTION - ÉLECTRICITÉ

- ENSEIGNE LUMINEUSE À RACCORDER PAR L'ÉLECTRICIEN. CHAQUE LETTRE DE L'ENSEIGNE EST RACCORDÉE INDÉPENDEMMENT JUSQU'À LA BOÎTE DE JONCTION DE L'ALIMENTATION PRINCIPALE DE L'ENSEIGNE.
- INTERCEPTER L'ALIMENTATION EXISTANTE DE L'ENSEIGNE ET INSTALLER UNE NOUVELLE BOÎTE DE JONCTION 300X300X200MM À L'INTÉRIEUR DU PLAFOND EXTÉRIEUR DEVANT L'ENTRÉE DES AMBULANCE (SUD) POUR L'INSTALLATION DU BOÎTIER D'ALIMENTATION. NOUVEAU CÂBLAGE À DISSIMULER AVEC CONDUITS DE PVC DANS L'ENVELOPPE DU BÂTIMENT JUSQU'À L'ENSEIGNE. RACCORDER SELON LES RECOMMANDATIONS DU MANUFACTURIER ET DIMENSIONNER LES CONDUITS PVC SELON LA QUANTITÉ DE CÂBLAGE.

NOTE CONSTRUCTION - GICLEURS

- TUYAUTERIES DE GICLEURS EXISTANTES MODIFIÉES (32mmØ / 1 1/4 PO) REINSTALLÉES SOUS LE TOIT DE L'ENTRÉE DES AMBULANCES (SUD) AVEC NOUVEAUX GICLEURS DROITS À RÉPONSE RAPIDE ANTI-CORROSION POUR L'EXTÉRIEUR, TEL QUE CEUX EXISTANTS.



PHOTO #ME008A

ÉCHELLE: AUCUNE

CLIENT

Santé Québec

SANTÉ QUÉBEC GASPÉSIE

RÉF. CLIENT: PROJET

HÔPITAL DE CHANDLER
(RÉFECTION DE L'ENVELOPPE)

Architecte

GRC RM **P. H. PROULX-SAVARD ARCHITECTES**

CE DOCUMENT NE DOIT PAS SERVIR À LA CONSTRUCTION

REV	DATE	DESCRIPTION	PAR
RÉVISIONS PARTIELLES			
1	2026/09/04	DÉFINITIFS POUR SOUMISSION	JD-JA
B	2026/08/21	DÉFINITIFS 100% POUR APPROBATION	JD-VS
A	2026/05/14	DÉFINITIFS 60% POUR APPROBATION	JD-VS
REV	DATE	DESCRIPTION	PAR

SCEAU:

MÉCANIQUE ÉLECTRICITÉ

AVERTISSEMENT: DROIT D'AUTEUR: CE DESSIN EST LA PROPRIÉTÉ INTELLECTUELLE DE WSP CANADA INC. AUCUNE RÉVISION, REPRODUCTION OU TOUT AUTRE USAGE N'EST PERMIS SANS L'AUTORISATION ÉCRITE DE WSP CANADA INC. L'ENTREPRENEUR DEVRA VÉRIFIER TOUTES LES DIMENSIONS AUX PLANS ET FAIRE LOCALISER TOUS LES SERVICES D'UTILITÉS PUBLIQUES ET RAPPORTER TOUTES ERREURS OU OMISSIONS AVANT DE COMMENCER LES TRAVAUX.

ÉCHELLE: ORIGINALE: INDICUÉE

DATE: AVRIL 2026

SI CETTE BARRE NE MESURE PAS 25 mm, AJUSTER VOTRE ÉCHELLE DE TRAPAGE.

DISCIPLINE: MÉCANIQUE / ÉLECTRIQUE


Mécanique / Électricité

wsp

NO PROJET: CA0066110.3235


TITRE: VUES AGRANDIES ET DÉTAILS QUAI DES AMBULANCES

NUMÉRO DU FEUILLET: ME008

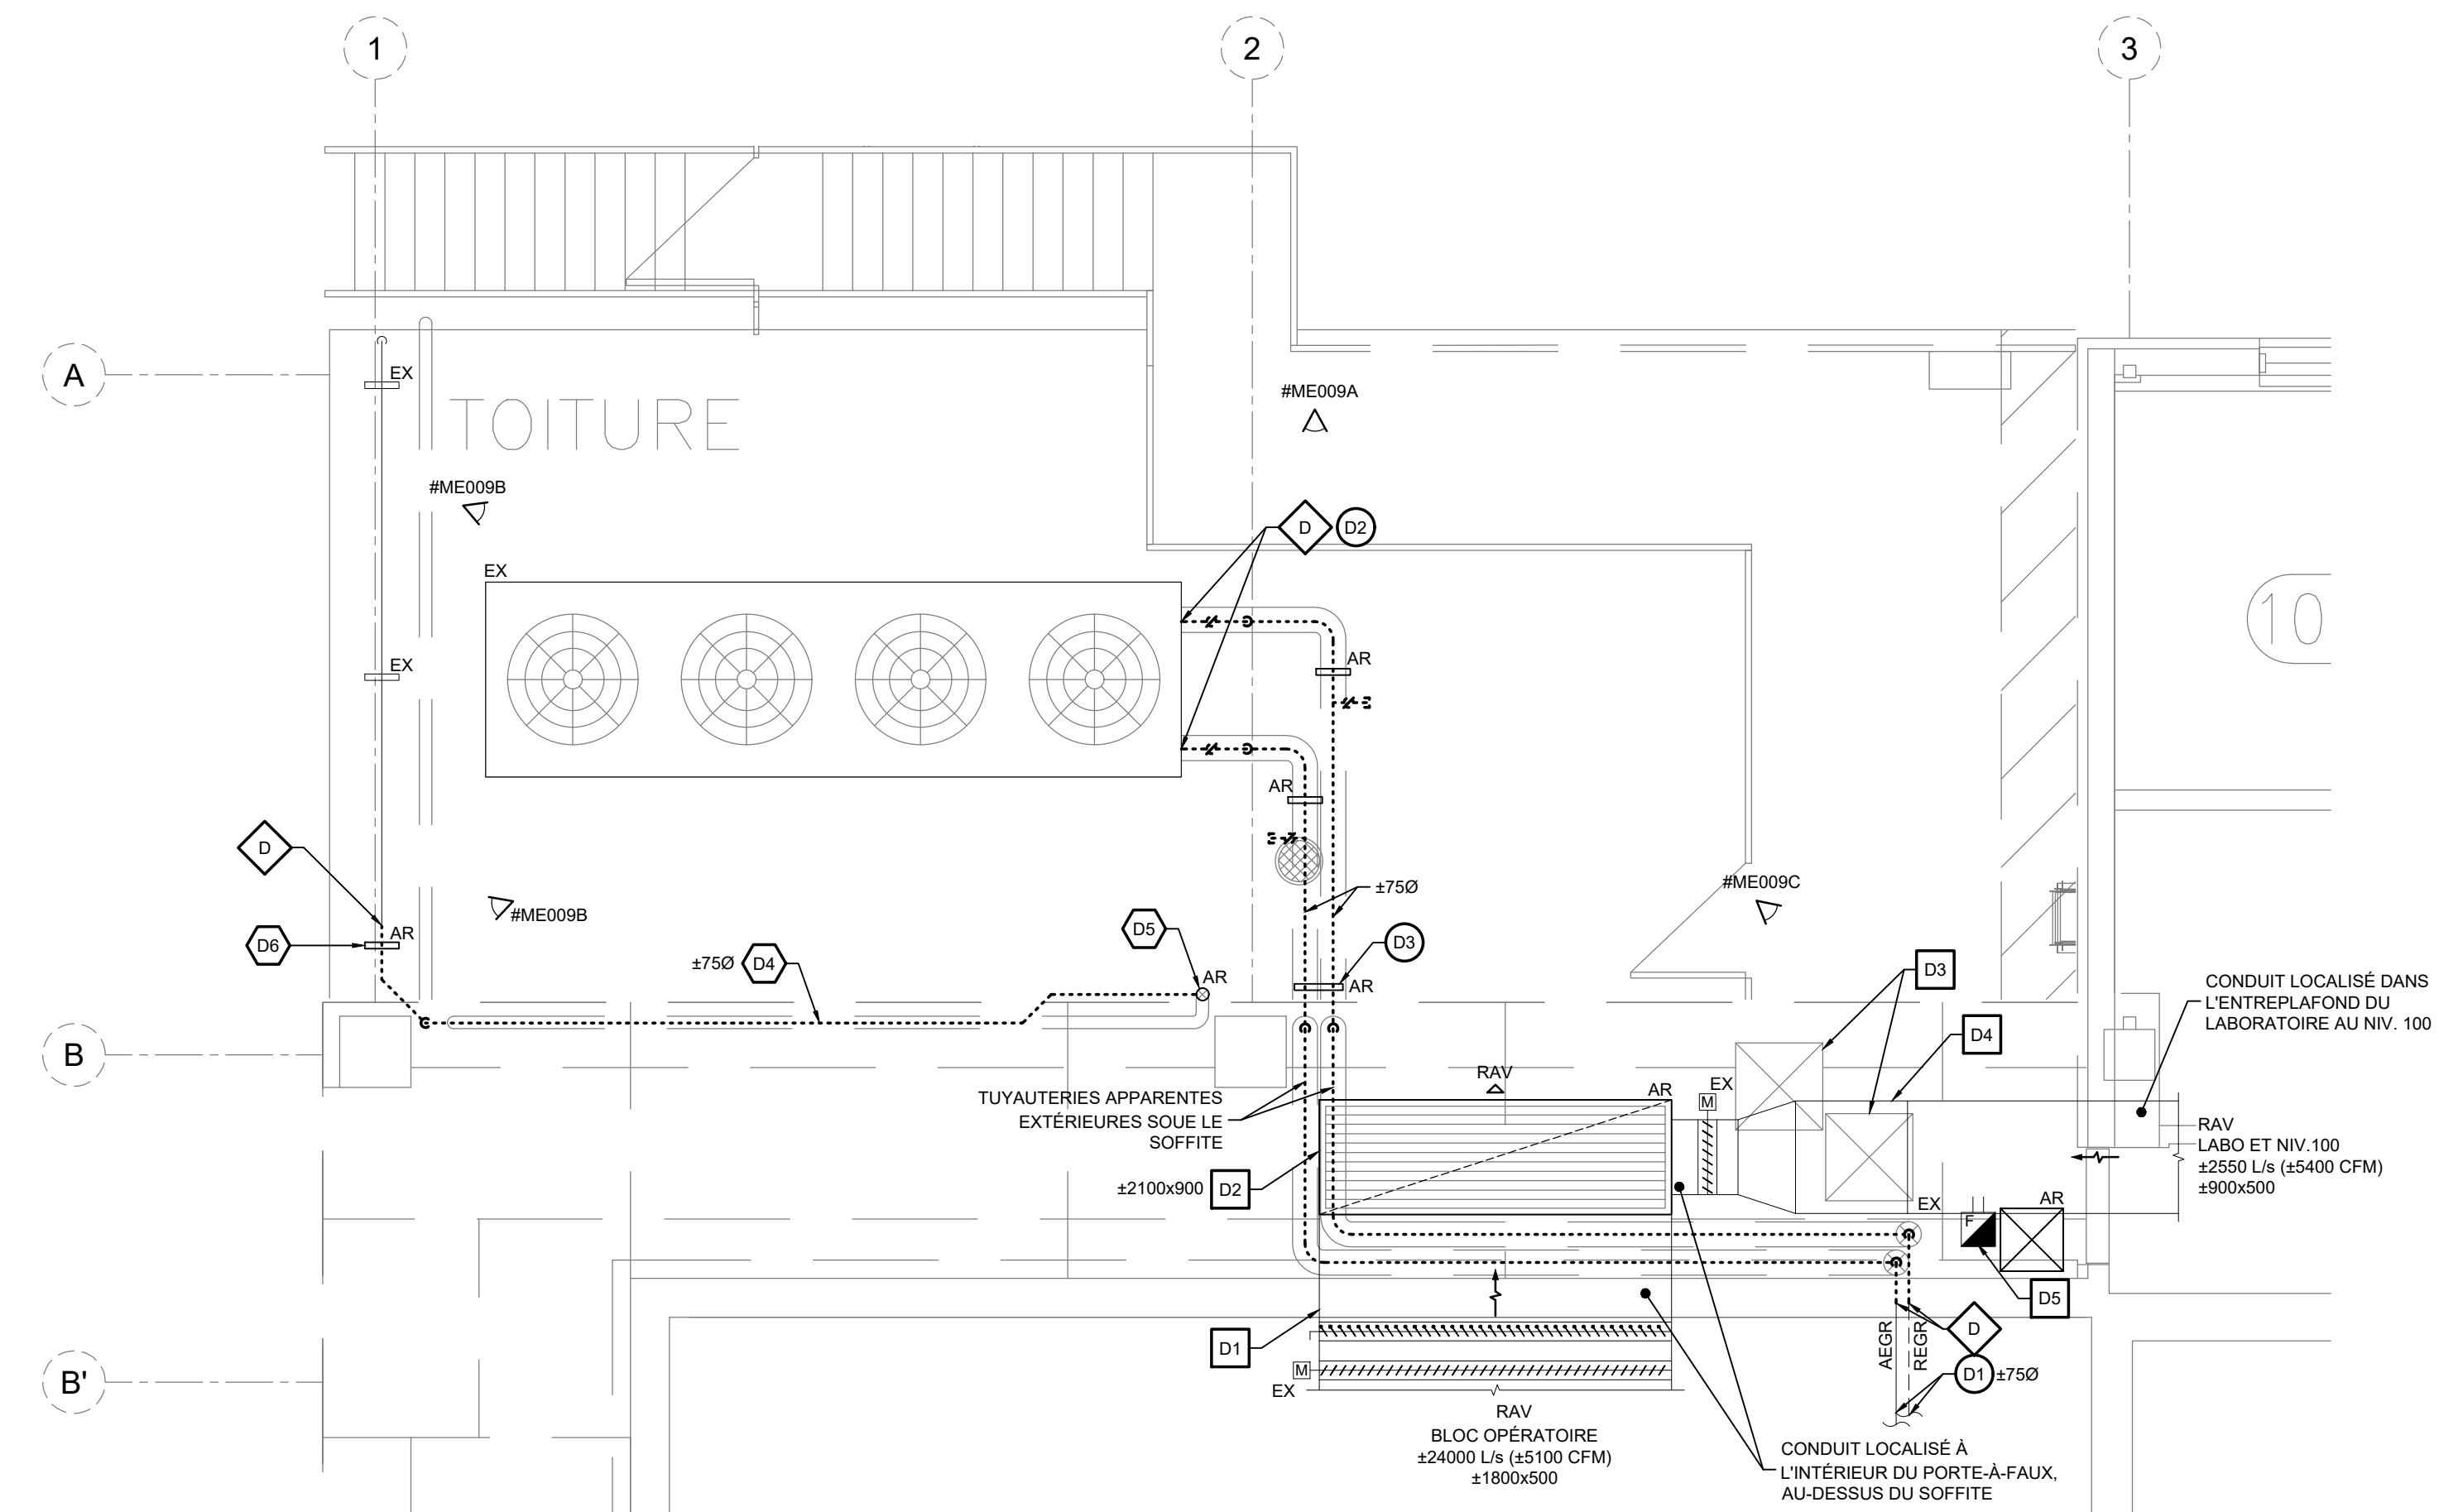

VUE AGRANDIE - TOITURE COIN NORD-OUEST - DÉMOLITION

ÉCHELLE: 1:50

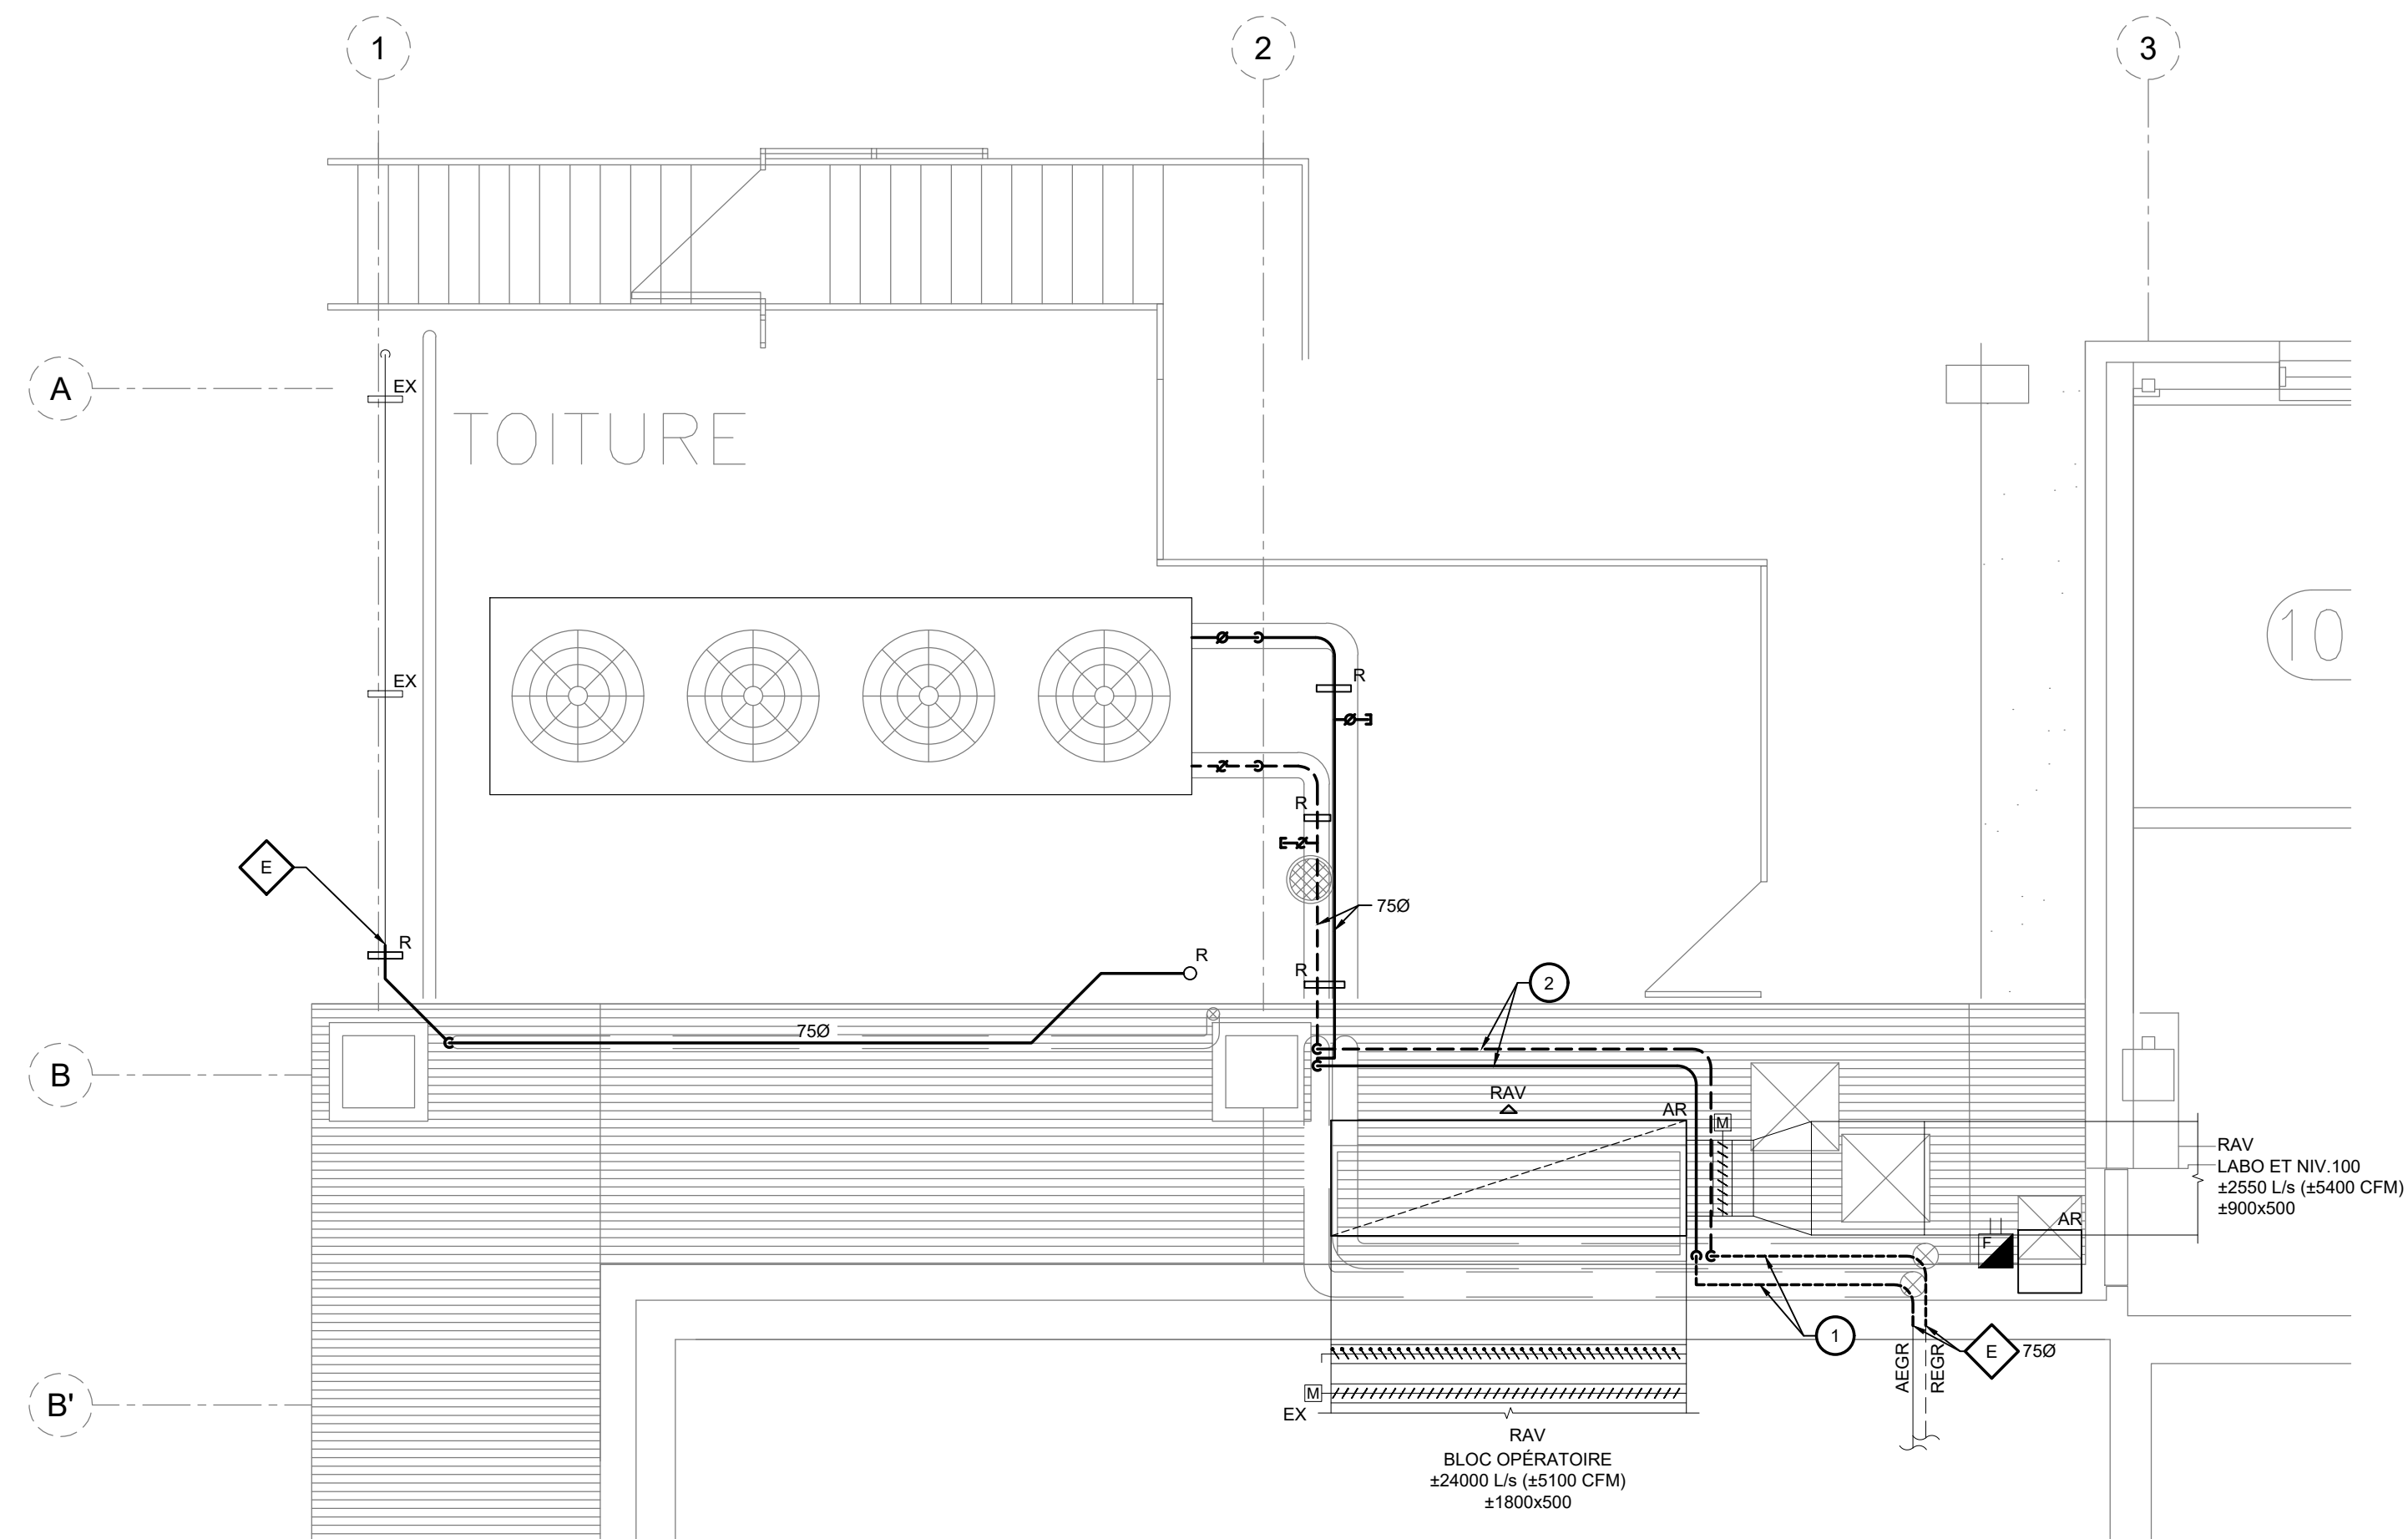

VUE AGRANDIE - TOITURE COIN NORD-OUEST - CONSTRUCTION

ÉCHELLE: 1:50



PHOTO #ME009A

ÉCHELLE: AUCUNE

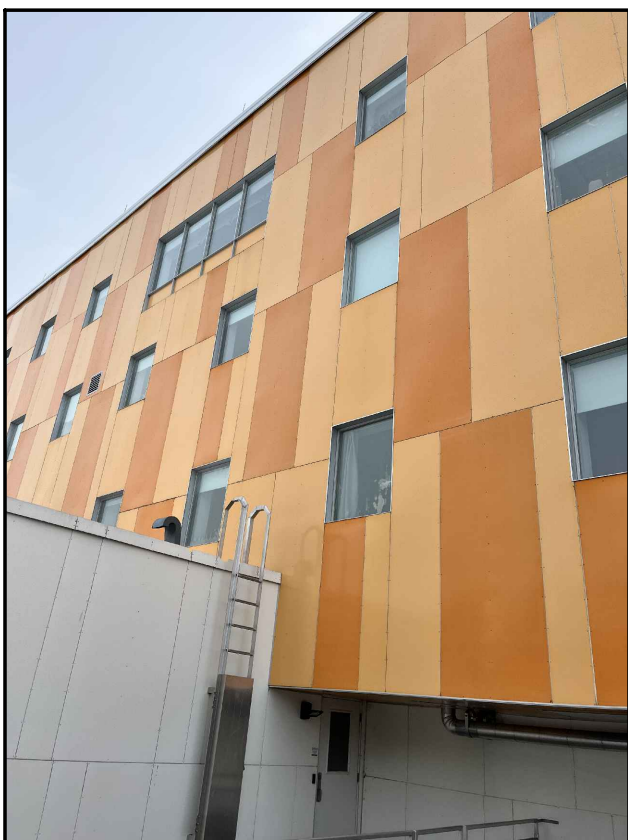


PHOTO #ME009B

ÉCHELLE: AUCUNE



PHOTO #ME009C

ÉCHELLE: AUCUNE



PHOTO #ME009D

ÉCHELLE: AUCUNE

NOTES DÉMOLITION - VENTILATION


- | | |
|----|---|
| D1 | CONDUIT D'ÉVACUATION DE L'UNITÉ DE VENTILATION DU BLOC OPÉRATEUR À CONSERVER ET À GARDER EN FONCTION DURANT LE CHANTIER. |
| D2 | PERSIENNE DURANT LE BLOC OPÉRATEUR DE DIVERS SECTEUR DU NIVEAU 10 LOCALISÉE DANS LE SOUTERRAIN, À ENLEVER TEMPORAIREMENT ET À REINSTALLER APRÈS LES TRAVAUX DE MODIFICATION DE L'ENVELOPPE GÉNÉRALE, À PROLONGER LE PLUS JUSQU'À LA FIN DE L'OPÉRATION, À ENLEVER LE PLUS JUSQU'À LA FIN DE L'OPÉRATION SELON L'ÉPAISSEUR DE L'ENVELOPPE. |
| D3 | TRAPPES D'ACCÈS REQUISES POUR LES APPAREILS DE MÉCANIQUE DANS LE SOUTERRAIN, À REMPLACER PAR L'ENTREPRENEUR GÉNÉRAL (VOIR ARCHITECTURE). |
| D4 | VENTILATEUR D'ÉVACUATION AVEC EN LIGNE DESERVANT PLUSIEURS SECTEURS DU NIVEAU 100 À CONSERVER ET À GARDER EN FONCTION DURANT LE CHANTIER. |
| D5 | DÉTECTEUR DE FUMÉE DE GAINE EXISTANT À CONSERVER |

NOTES DÉMOLITION - PLOMBERIE


- D1** TUYAURIER EXISTANTES À L'INTÉRIEUR DU PORTE-À-FAUX AU-DESSUS DU SOFFITE, VERS LA SALLE DE MÉCANIQUE DU BLOC OPÉRATEUR, À CONSERVER. TUYAUVES SPIRITUELLES EN ALUMINIUM PUR VUE LA TRAPPE D'ACCÈS EXTÉRIEUR, ÉTHYLÈNE GLYCOL, 50% TUYAUVIER D'ACIER, CALORIFIQUE DE FAÇON DE VERRRE 38mm.
 - D2** REFRÉDROISANT DE LIQUIDE EXISTANT À CONSERVER, SERVANT AU SYSTÈME DE DÉSHUMIDIFICATION DU BLOC OPÉRATEUR. TUYAURIERES EXTERIEURES A REMPLACER POUR S'ADAPTER A LA NOUVELLE ENVELOPPE EXTERIEUR DU BATIMENT. CHEMISAGE D'ALUMINIUM SUR LES TUYAURIERES EXTERIEURES.
 - D3** SUPPORTS DÉPOSÉS EN TOITURE À RELOCALISER, INCLINANT LE CONDUIT ENT VIDE 25mm SERVANT À ATTACHER LE CÂBLAGE TECH EXTERIEUR.
 - D4** TUYAURIER EXTERIEURE DE PRISE D'AIR DU SYSTÈME D'AIR MÉDICAL DE L'HÔPITAL. EN ACIER INOXYDABLE SOUDE, DIAMÈTRE 475mm/50, À MODIFIER POUR S'ADAPTER A LA NOUVELLE ENVELOPPE EXTERIEUR DU BATIMENT. TUYAUVIER D'AIR TEMPORAIRE DOIT ÊTRE INSTALLÉ SUR LA FAÇADE OUEST DURANT LES TRAVAUX DE LA FAÇADE NORD.
 - D5** BÔÎTIER DE FILTRATION HEPA POUR PRISE D'AIR DU SYSTÈME D'AIR MÉDICAL DE L'HÔPITAL. À RELOCALISER POUR S'ADAPTER A LA NOUVELLE ENVELOPPE EXTERIEUR DU BATIMENT. LE BÔÎTIER DOIT ÊTRE INSTALLÉ SUR LA FAÇADE OUEST DURANT LES TRAVAUX DE LA FAÇADE NORD AFIN DE GARDER LE SYSTÈME D'AIR MÉDICAL EN FONCTION.
 - D6** SUPPORTS DÉPOSÉS EN TOITURE À RELOCALISER AFIN DE DÉGAGER LE NOUVEAU REVÊTEMENT DE LA COLONNE À L'INTÉRIEUR DU BÂTIMENT (AXE B1). MODIFIER LES CONTREVENTEMENTS EXISTANTS D'ALUMINIUM SELON LA NOUVELLE LOCALISATION DU SUPPORT RELOCALISÉ.

NOTES CONSTRUCTION - PLOMBERIE


- | | |
|----|--|
| D1 | NOUVELLES TUYAUTERIES À L'INTÉRIEUR DU PORTE-À-FAUX AU-DESSUS DU SOFFITE, VERS LA SALLE D'OPÉRATION, À L'INTÉRIEUR DU BLOC OPÉATOIRE, AVEC NOUVEAUX PURGEURS D'AIR PRÈS DE LA TRAPPE D'ACCÈS EXTÉRIEURE. ÉTHYLÈNE GLYCOL 50%, TUYAUTERIE D'ACIER, CALORIFUGE DE FIBRE DE VERRE 38mm. |
| D2 | NOUVELLES TUYAUTERIES APPARENTES EXTÉRIEURES EN-DESSOUS DU SOFFITE. AJOUTER UN CHEMISAGE D'ALUMINIUM SUR LE CALORIFUGAGE APPARENT EXTERIEUR (VOIR DEVIS). |

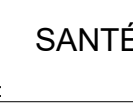CLIENT	 Santé Québec SANTÉ QUÉBEC GASPÉSIE
# RÉF. CLIENT:	
PROJET	
HÔPITAL DE CHANDLER (RÉFECTION DE L'ENVELOPPE)	
Architecte	 
CE DOCUMENT NE DOIT PAS SERVIR À LA CONSTRUCTION	

REV	DATE	DESCRIPTION	PAR
		RÉVISIONS PARTIELLES	
1	2026/09/04	DÉFINITIFS POUR SOUMISSION	JD-JA
B	2026/08/21	DÉFINITIFS 100% POUR APPROBATION	JDV-S
A	2026/05/14	DÉFINITIFS 60% POUR APPROBATION	JDV-S
REV	DATE	DESCRIPTION	PAR

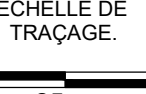
SEAU:  MÉCANIQUE	 ÉLECTRICITÉ
AVERTISSEMENT: DROIT D'AUTEUR: CE DESSIN EST LA PROPRIÉTÉ INTELLECTUELLE DE WSP CANADA INC. AUCUNE RÉVISION, REPRODUCTION OU TOUT AUTRE USAGE N'EST PERMIS SANS L'AUTORISATION ÉCRITE DE WSP CANADA INC. L'ENTREPRENEUR DOIT VÉRIFIER TOUTES LES DIMENSIONS AUX PLANS ET FAIRE LOUALISER TOUTS LES SERVICES D'UTILITÉS PUBLIQUES ET RAPPORTER TOUTES ERREURS OU OMISSIONS AVANT DE COMMENCER LES TRAVAUX.	
ECHELLE ORIGINALE: INDIQUÉE DESSIN PAR : A. HALLÉ PRÉPARE SOUS SUPERVISION PAR : J. DAMOURS ET Y. STOCKMEYER, ing. PRÉPARE PAR : J. DAMOURS ET J. ALCINDOR, ing. APPROUVE ADMINISTRATIVEMENT PAR : G. LAVOIE	DATE: AVRIL 2026 SI CETTE BARRE NE MESURE PAS 25 mm, AJUSTER VOTRE ECHELLE DE TRAÇAGE. 
DISCIPLINE: MÉCANIQUE / ÉLECTRICITÉ	

Mécanique / Electricité	
	
NO PROJET: CA0066110.3235	
TITRE:	
VUES AGRANDIES ET DÉTAILS TOITURE COIN NORD-OUEST	
NUMERO DU FEUILLET:	
ME009	

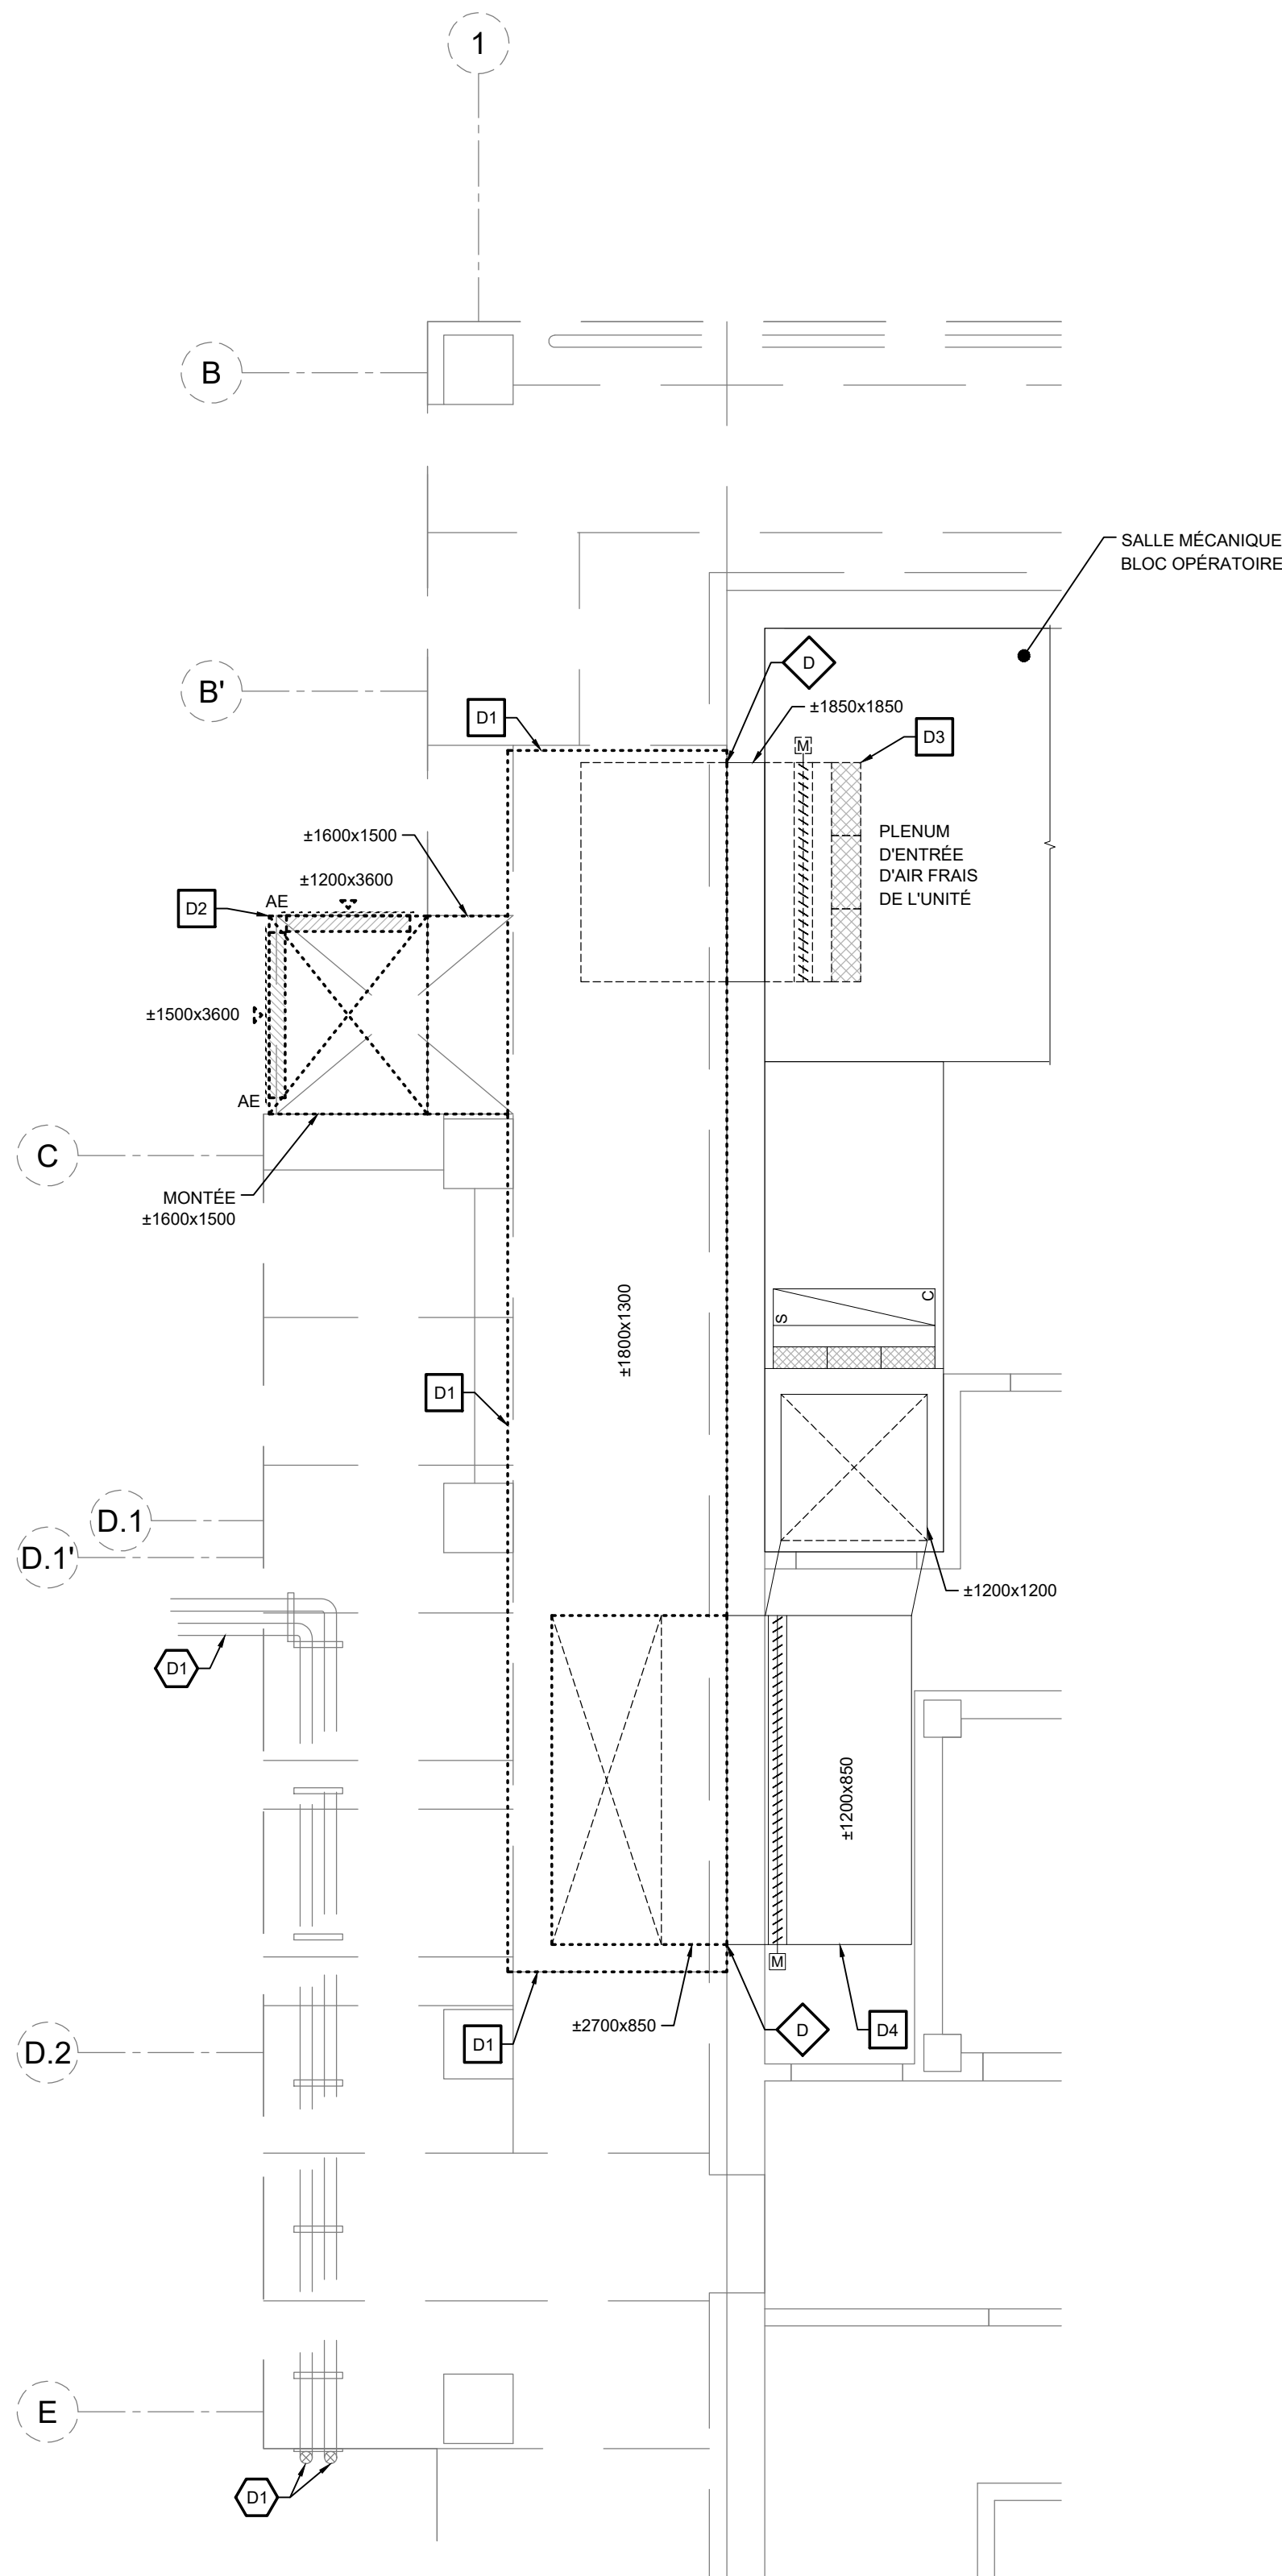

VUE AGRANDIE - TOITURE OUEST - PRISE D'AIR FRAIS BLOC OPÉRAIRE - DÉMOLITION

ÉCHELLE: 1:50

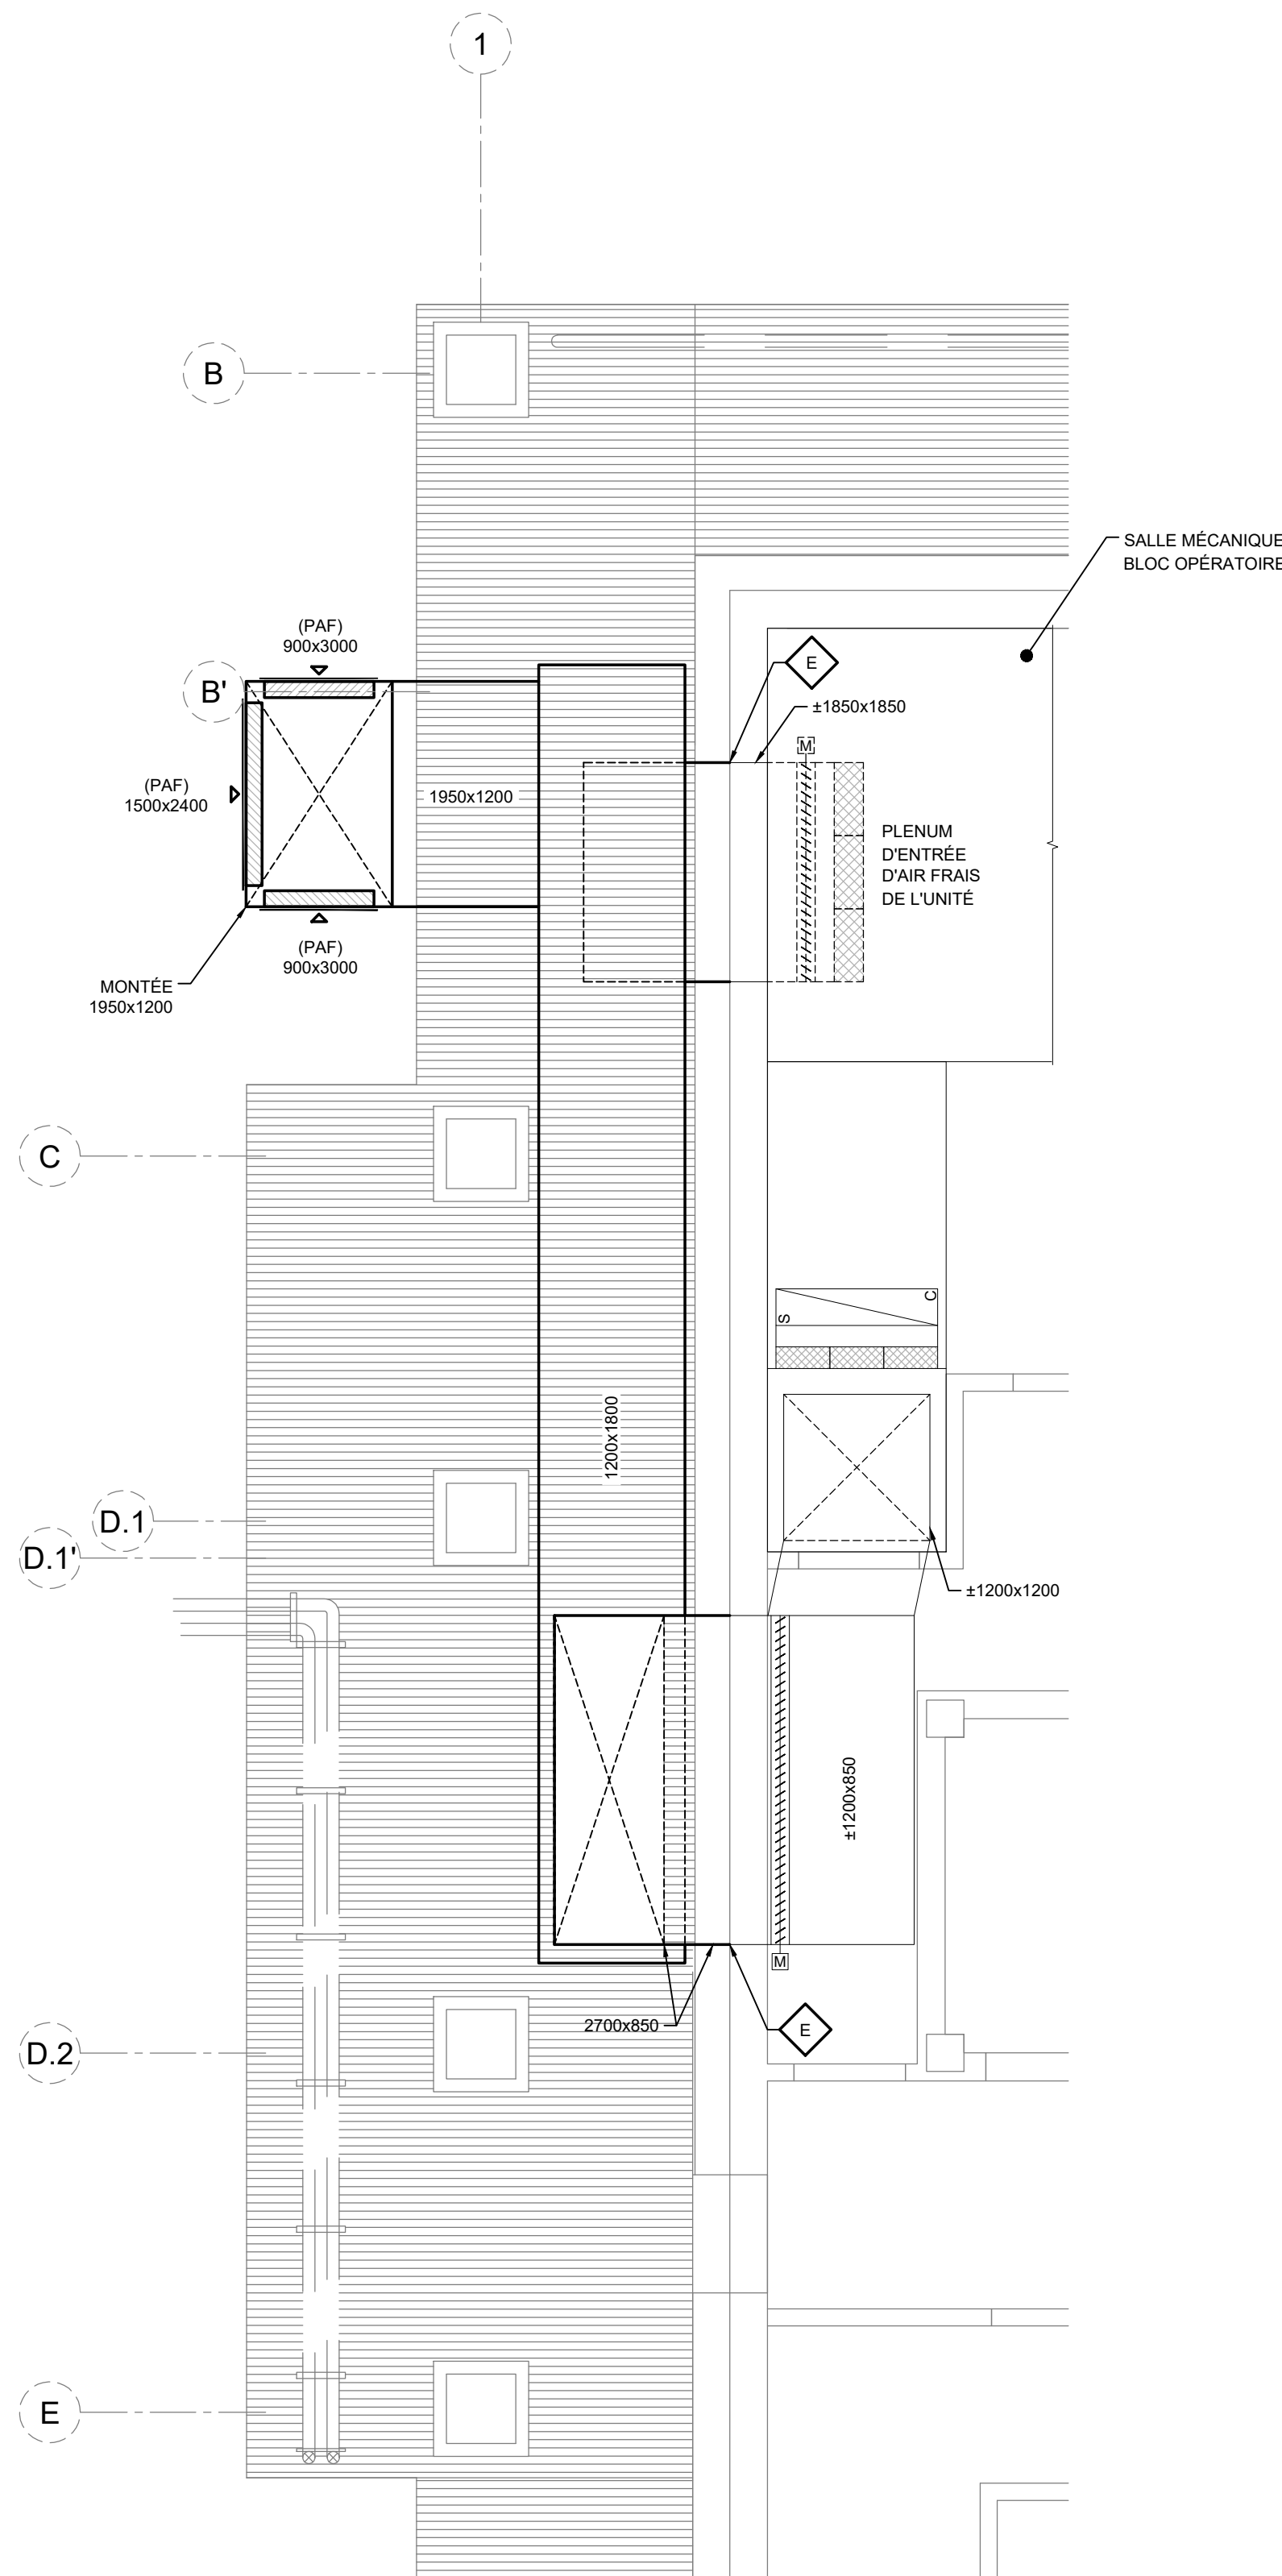

VUE AGRANDIE - TOITURE OUEST - PRISE D'AIR FRAIS BLOC OPÉRATOIRE - CONSTRUCTION

ÉCHELLE: 1:50

NOTES DÉMOLITION - VENTILATION

- | | |
|----|--|
| D1 | CONDUIT DE PRISE D'AIR FRAIS EN SURFACE À L'EXTÉRIEUR DU BÂTIMENT, DESSERVANT LA VENTILATION DU BLOC OPÉRATEUR. À GARDER EN FONCTION DURANT TOUTE LA DURÉE DES TRAVAUX AFIN DE RÉALISER LES TRAVAUX DE RÉNOUVELLEMENT DE FACILITATION DE L'AIR FRAIS EXISTANT. UNE INSTALLATION DE CONDUITS TEMPORAIRES D'AIR FRAIS DOIT ÊTRE MISE EN PLACE PAR L'ENTREPRENEUR EN PARALLÈLE DU CONDUIT EXISTANT ET DES TRAVAUX EN PLUSIEURS ÉTAPES SONT À PLANIFIER. VOIR VOIES AGRANDIES EN PLUS. VOIR PLAN DES ÉTAPES TEMPORAIRES. |
| D2 | MONTÉE DU CONDUIT DE PRISE D'AIR FRAIS LONG DU MUR EXTÉRIEUR. À DÉMANTÉLER INCLUANT LES PERNES SUR DEUX FACES. |
| D3 | ENTRÉE D'AIR SECONDAIRE NON CHAUFFÉE (FONCTIONNEMENT EN ÉTÉ OU EN MODE REFRIGÉRATION GRATUIT SEULEMENT) VERS LE PLENUM D'ENTRÉE D'AIR DE L'UNITÉ DE VENTILATION DANS LA SALLE DE MÉCANIQUE DU BLOC OPÉRATEUR. CONDUIT À PROLONGER DANS LE MUR VERS LE NOUVEAU CONDUIT EXTÉRIEUR. |
| D4 | ENTRÉE D'AIR PRINCIPALE CHAUFFÉE VERS LE PLENUM D'ENTRÉE D'AIR DE L'UNITÉ DE VENTILATION DANS LA SALLE DE MÉCANIQUE DU BLOC OPÉRATEUR. CONDUIT À PROLONGER DANS LE MUR VERS LE NOUVEAU CONDUIT EXTÉRIEUR. |

NOTES DÉMOLITION - PLOMBERIE

- D1** ÉVÉNEMENTS DE VAPEUR POUR AUTOCLAVE LOCALISÉ AU SOUS-SOL, À RELOCALISER AVANT LE DÉBUT DES TRAVAUX DE LA FAÇADE OUEST. PROLONGER LA TUYAUTERIE EXTÉRIEURE SUR DES SUPPORTS TEMPORAIRES DÉPOSÉS EN TOITURE JUSQU'AU COIN SUD-OUEST DU BÂTIMENT. VOIR VUES AGRANDIES EN PLAN.



SANTÉ QUÉBEC GASPÉSIE

RÉF. CLIENT
PROJET

HÔPITAL DE CHANDLER
(RÉFECTION DE L'ENVELOPPE)

Architecte




CE DOCUMENT **NE DOIT PAS** SERVIR À
LA CONSTRUCTION

[illegible]

REV	DATE	DESCRIPTION	PAR
REVISIONS PARTIELLES			
1	2026/09/04	DÉFINITIFS POUR SOUMISSION	JD-JA
B	2026/08/21	DÉFINITIFS 100% POUR APPROBATION	JD-VS
A	2026/05/14	DÉFINITIFS 60% POUR APPROBATION	JD-VS
REV	DATE	DESCRIPTION	PAR

SCEAU:

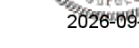

2026-09-04

MÉCANIQUE



2026-09-04

ÉLECTRICITÉ

AVERTISSEMENT:	DROIT D'AUTEUR:
CE DESSIN EST LA PROPRIÉTÉ INTELLECTUELLE DE WSP CANADA INC. AUCUNE REVISION, REPRODUCTION OU TOUT AUTRE USAGE N'EST PERMIS SANS L'AUTORISATION ÉCrite DE WSP CANADA INC. L'ENTREPRENEUR DEVRA VÉRIFIER TOUTES LES DIMENSIONS AUX PLANS ET FAIRE LOCALISER TOUTS LES SERVICES D'UTILITÉS PUBLIQUES ET RAPPORTER TOUTES ERREURS OU OMISSIONS AVANT DE COMMENCER LES TRAVAUX.	

ECHELLE ORIGINALE: INDIQUÉE DESSINÉ PAR : A. CASTONGUAY PRÉPARÉ SOUS SUPERVISION PAR : J. D'AMOURS ET V. STOCKMEYER, ing. PRÉPARÉ PAR : J. D'AMOURS ET J. ALCINDOR, ing. APPROUVÉ ADMINISTRATIVEMENT PAR : G. LAVOIE	DATE: AVRIL 2026 SI CETTE BARRE NE MESURE PAS 25 mm, AJUSTER VOTRE ECHELLE DE TRAÇAGE.  25mm
--	--

DISCIPLINE: MÉCANIQUE / ÉLECTRIQUE

Mécanique / Électricité



NO PROJET: CA0066110.3235


TITRE:

VUES AGRANDIES ET DÉTAILS
TOITURE OUEST
PRISE D'AIR FRAIS
BLOC OPÉRATOIRE

NUMÉRO D'FEUILLET:


ME010

\\corp.phban.net\cad\data\cant1\PEP\projets\2026\11\CA066110\3235\Bâtiment05 - TECH04.1 - CAO

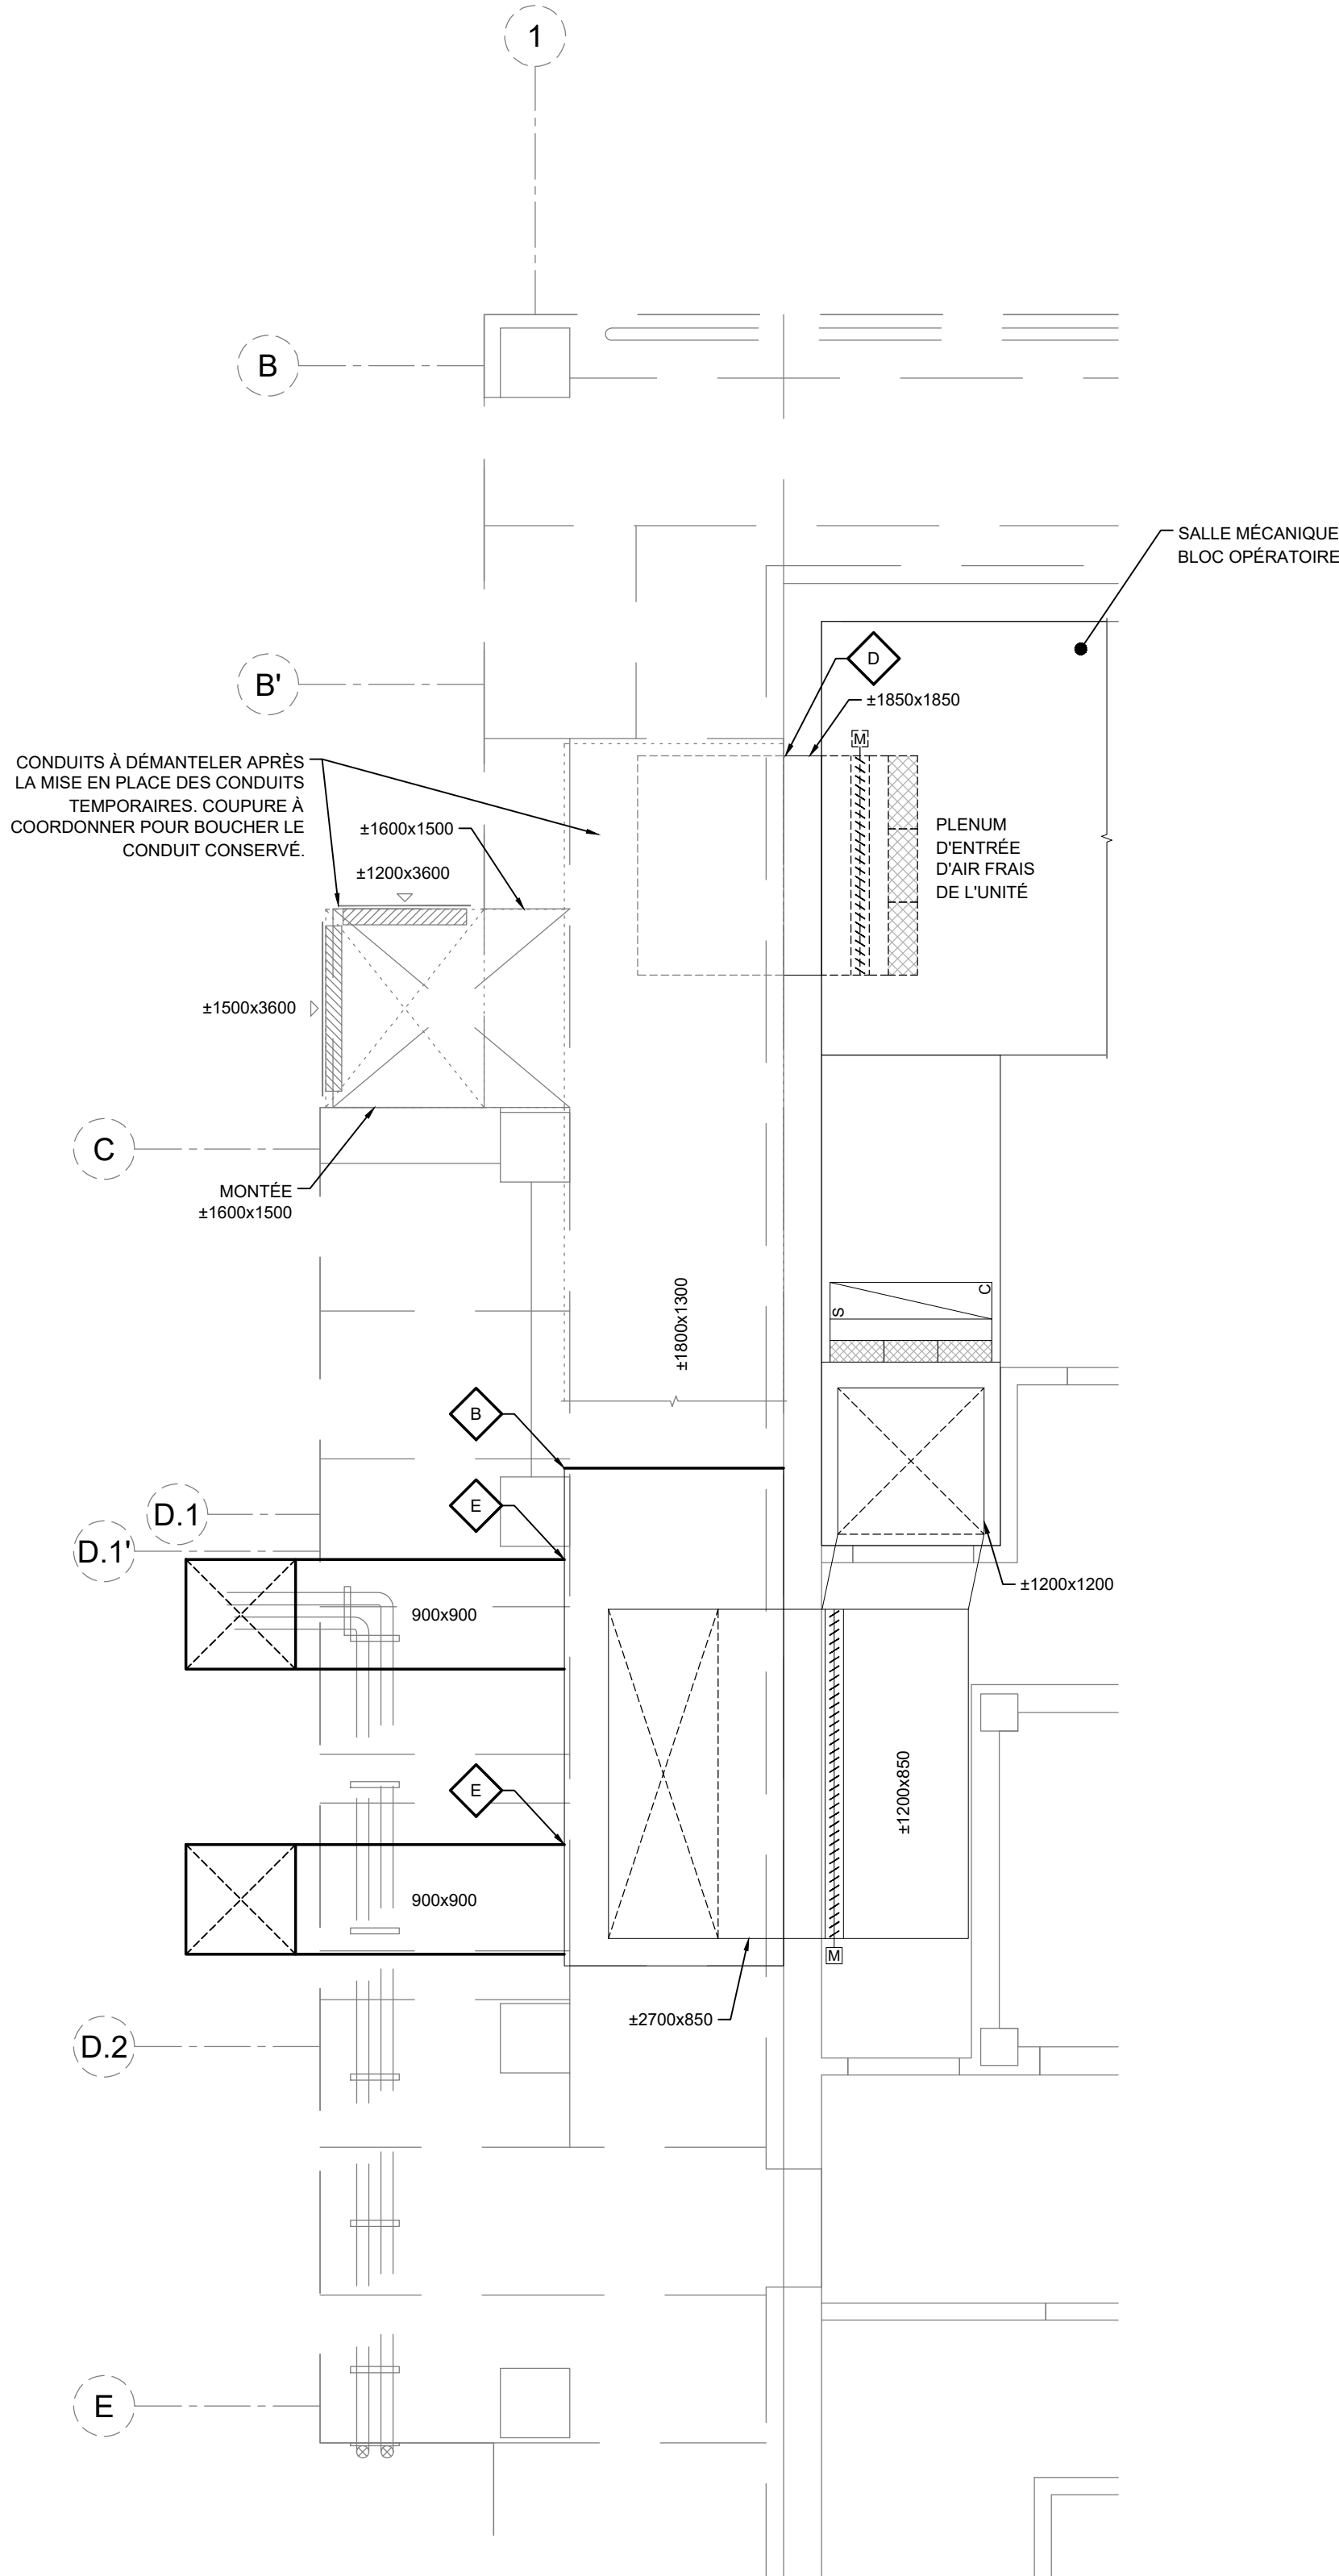

VUE AGRANDIE - TOITURE OUEST - PRISE D'AIR FRAIS BLOC OPÉRATEIRE - TEMPORAIRE #1

ÉCHELLE: 1:50

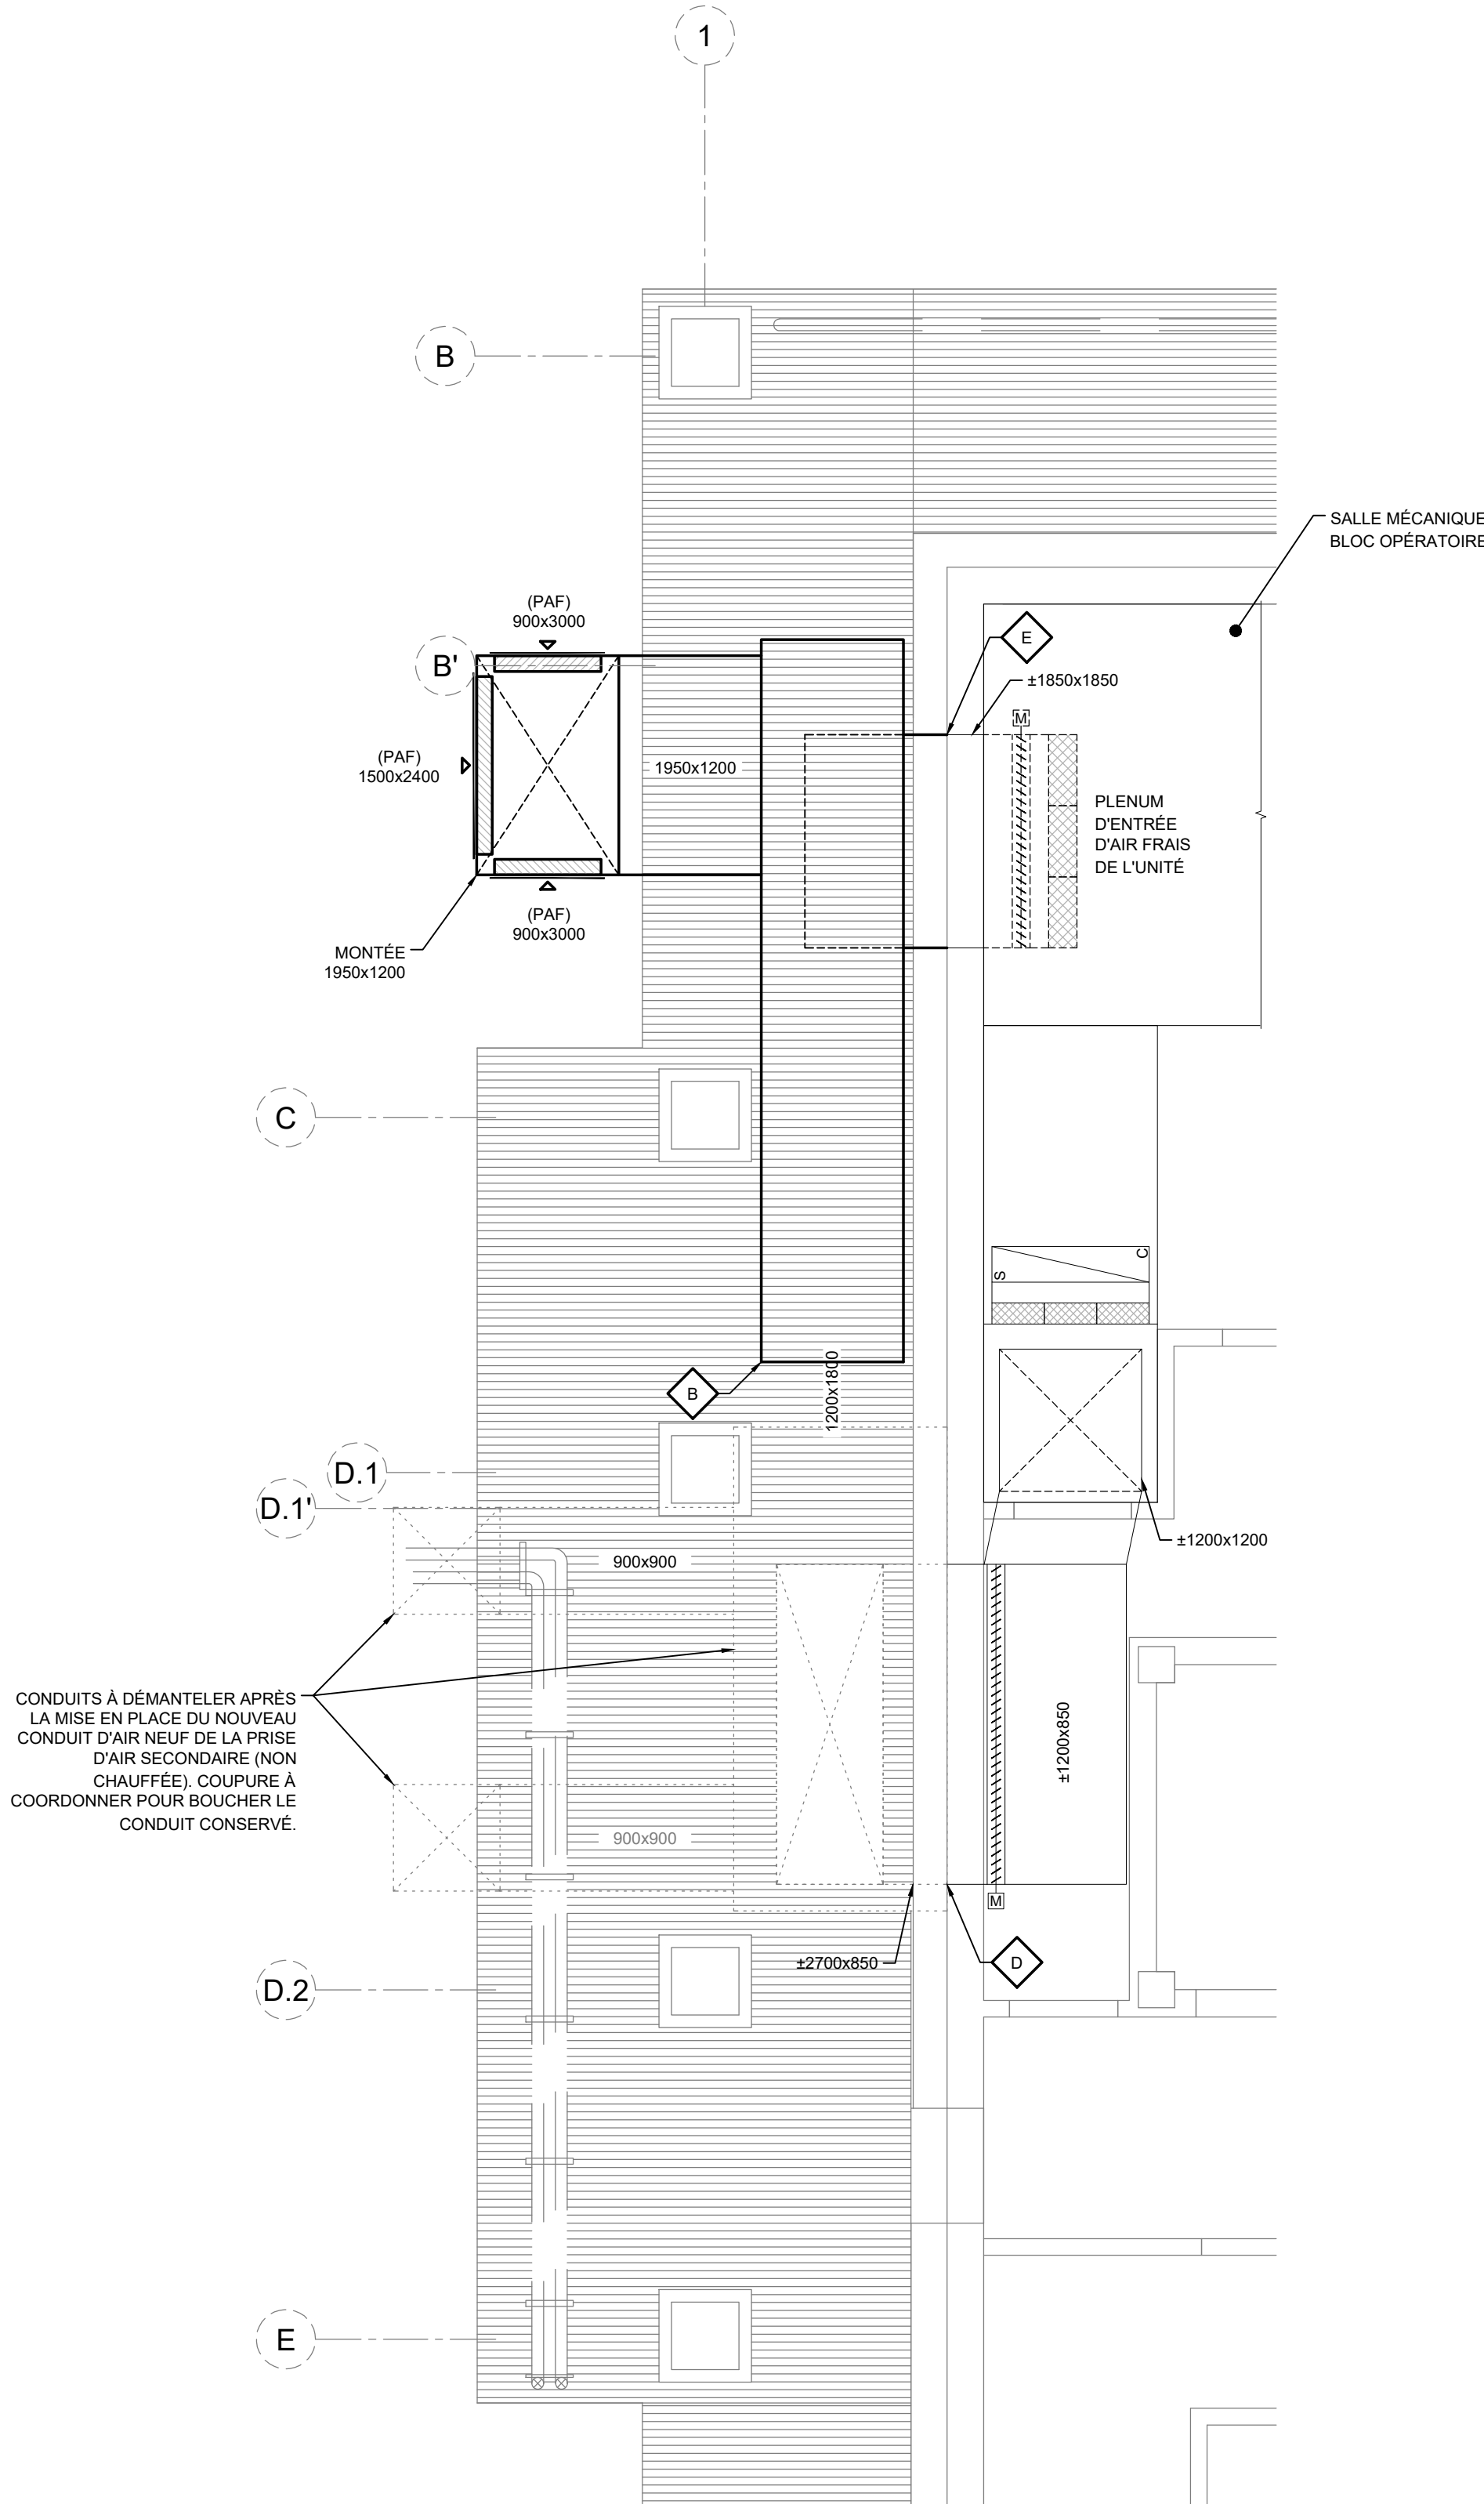

VUE AGRANDIE - TOITURE OUEST - PRISE D'AIR FRAIS BLOC OPÉRATEIRE - TEMPORAIRE #2

ÉCHELLE: 1:50

CLIENT

 **Santé Québec**

SANTÉ QUÉBEC GASPÉSIE

RÉF. CLIENT:

PROJET

HÔPITAL DE CHANDLER
(RÉFECTION DE L'ENVELOPPE)

Architecte

CE DOCUMENT NE DOIT PAS SERVIR À LA CONSTRUCTION

REV	DATE	DESCRIPTION	PAR
RÉVISIONS PARTIELLES			
1	2026/09/04	DÉFINITIFS POUR SOUMISSION	JD-JA
B	2026/08/21	DÉFINITIFS 100% POUR APPROBATION	JD-VS
A	2026/05/14	DÉFINITIFS 60% POUR APPROBATION	JD-VS
REV	DATE	DESCRIPTION	PAR

SCEAU:

MÉCANIQUE ÉLECTRICITÉ

AVERTISSEMENT: DROIT D'AUTEUR:

CE DESSIN EST LA PROPRIÉTÉ INTELLECTUELLE DE WSP CANADA INC. AUCUNE RÉVISION, REPRODUCTION OU TOUT AUTRE USAGE N'EST PERMIS SANS L'AUTORISATION ÉCRITE DE WSP CANADA INC. L'ENTREPRENEUR DEVRA VÉRIFIER TOUTES LES DIMENSIONS AUX PLANS ET FAIRE LOCALISER TOUS LES SERVICES D'UTILITÉS PUBLIQUES ET RAPPORTER TOUTES ERREURS OU OMISSIONS AVANT DE COMMENCER LES TRAVAUX.

ÉCHELLE: ORIGINALE: DATE: AVRIL 2026

INDIQUÉE

DESSINÉ PAR: A. CASTONGUAY

PRÉPARÉ SOUS SUPERVISION PAR: J. D'AMOURS ET V. STOCKMEYER, ing.

PRÉPARÉ PAR: J. D'AMOURS ET J. ALCINDOR, ing.

APPROUVÉ ADMINISTRATIVEMENT PAR: S. L'AVOIE

SI CETTE BARRE NE MESURE PAS 25 mm, AJUSTER VOTRE ÉCHELLE DE TRAPAGE.

25mm

DISCIPLINE: MÉCANIQUE / ÉLECTRIQUE

Mécanique / Électricité



NO PROJET: CA0066110.3235


TITRE:

VUES AGRANDIES ET DÉTAILS
TOITURE OUEST
PRISE D'AIR FRAIS
BLOC OPÉRATEIRE

NUMÉRO DU FEUILLET:


ME011

\\corp.phon.net\cad\as5\cant1\PEP\projets\2026\11CA066110.3235Bailment05 TECH04.1 CAD

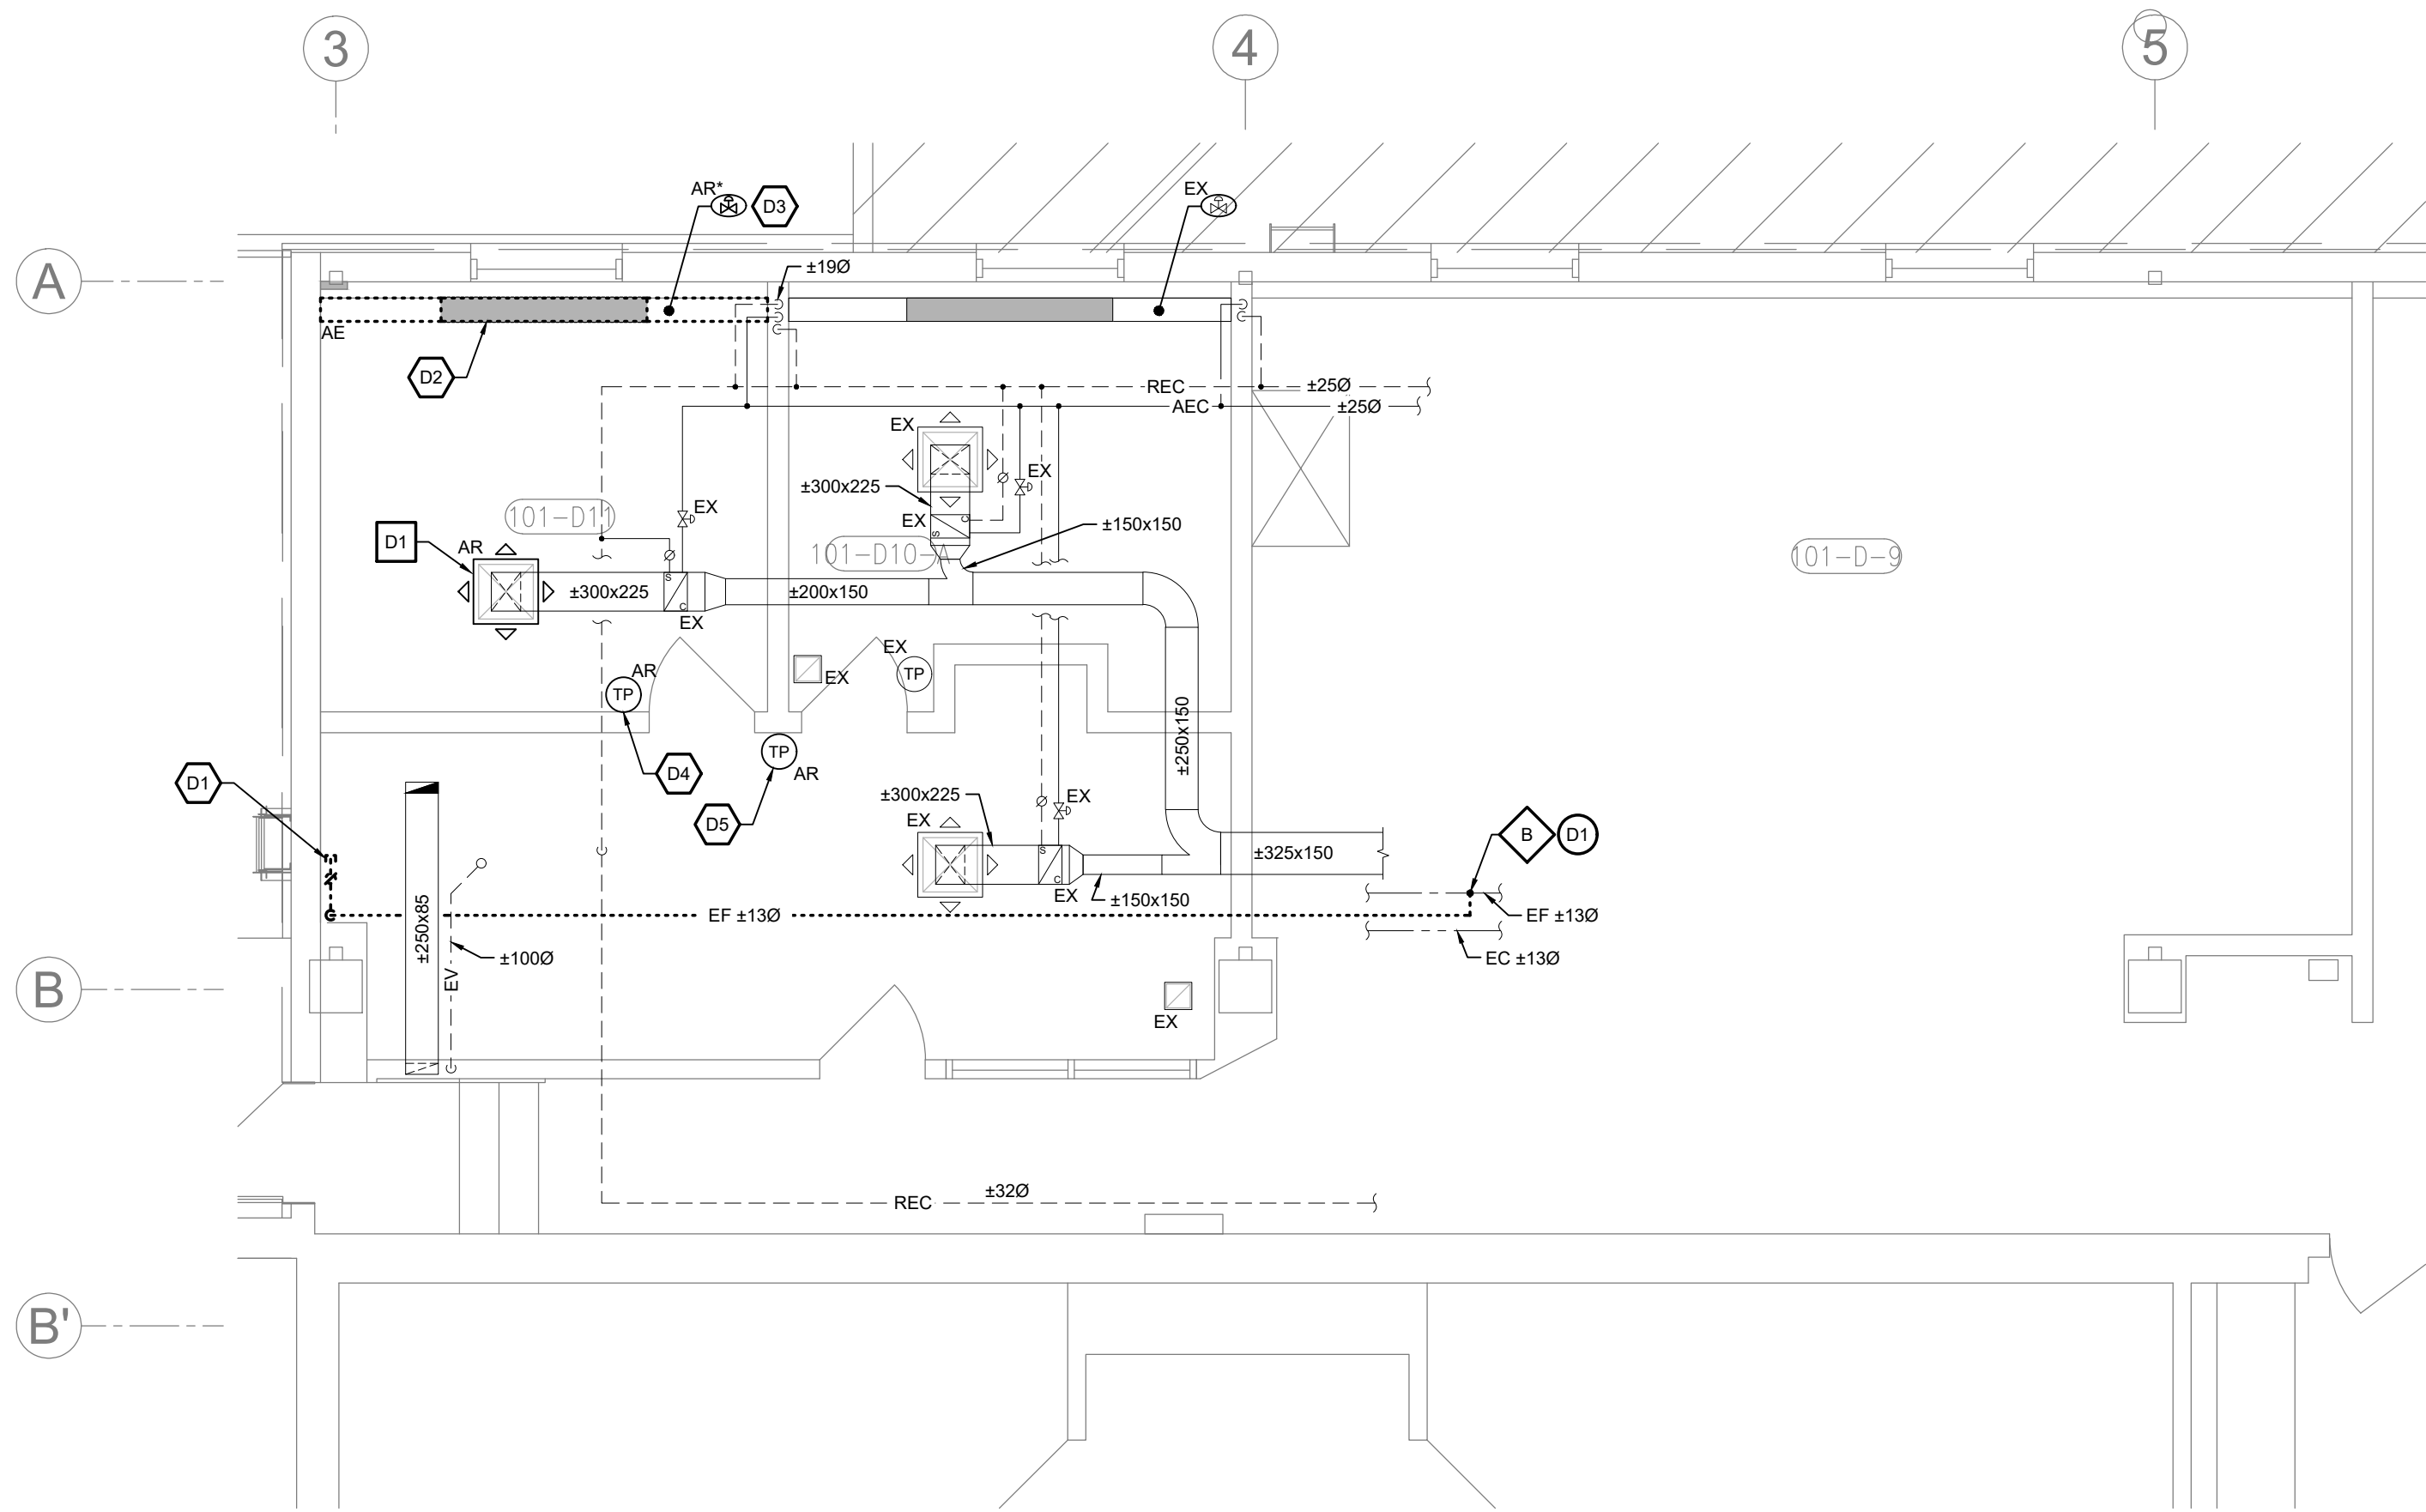

VUE AGRANDIE - AJOUT ISSUE LABORATOIRE - MÉCANIQUE - DÉMOLITION

ÉCHELLE: 1:50

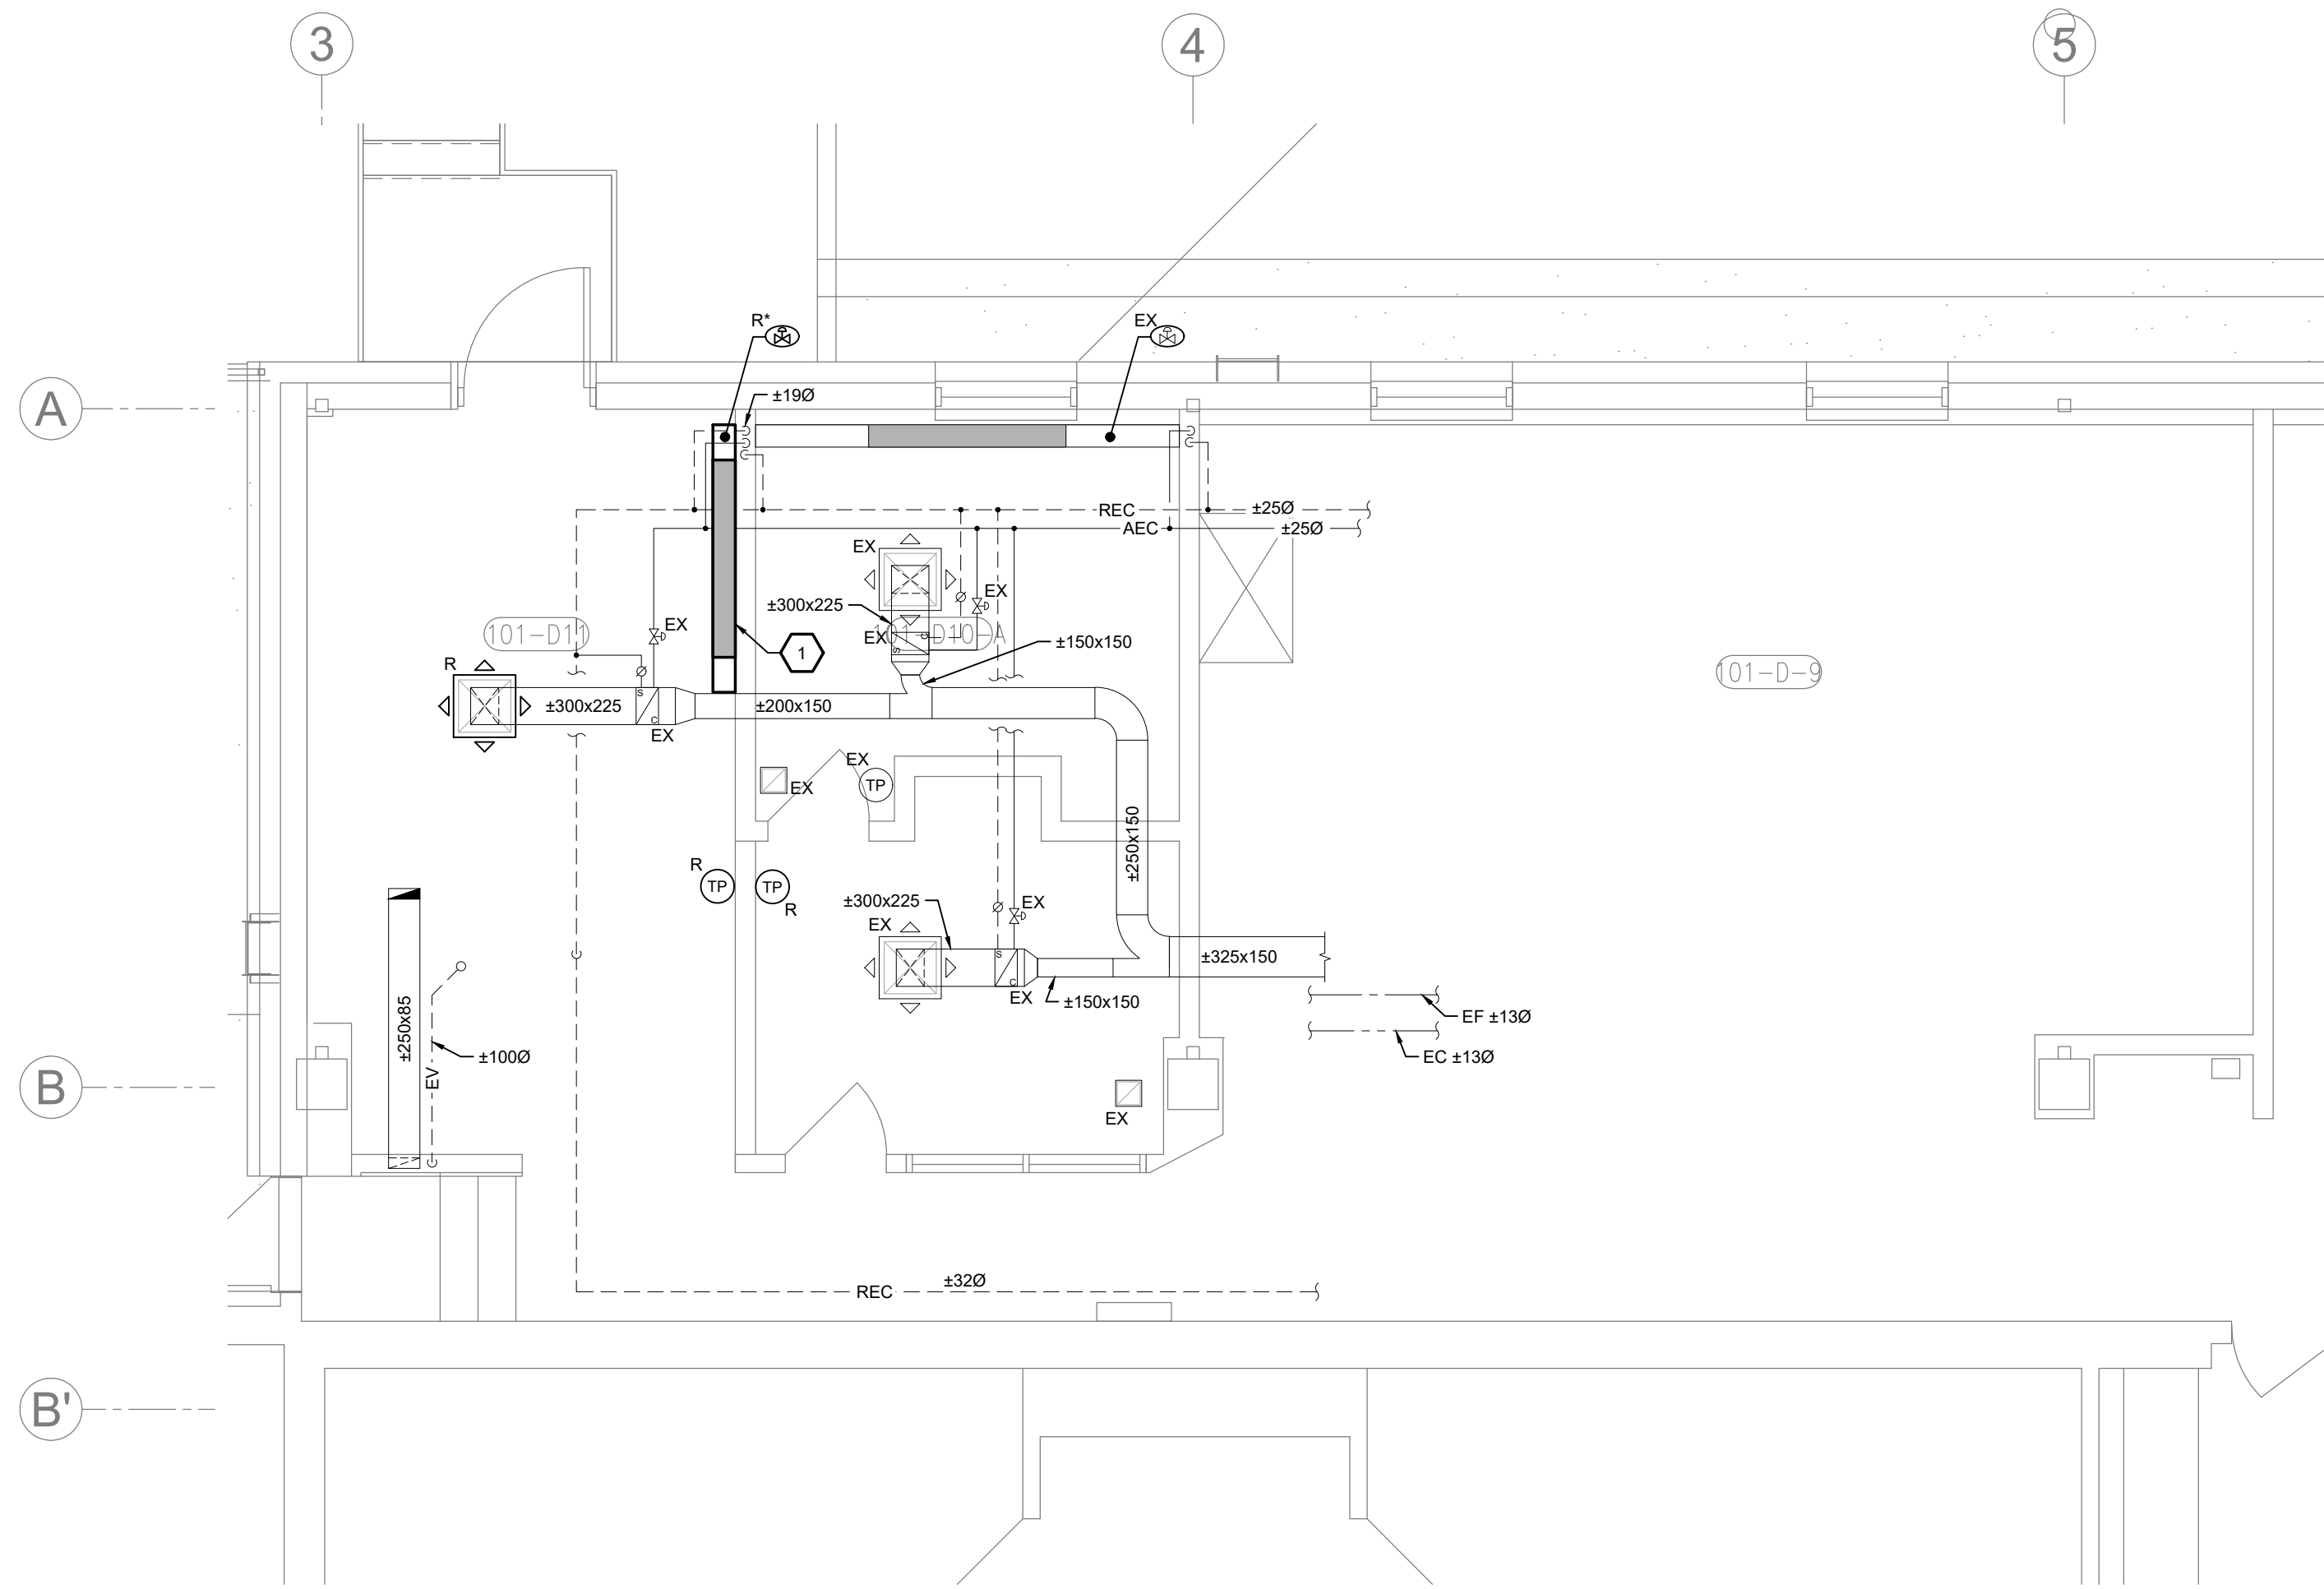

VUE AGRANDIE - AJOUT ISSUE LABORATOIRE - MÉCANIQUE - CONSTRUCTION

ÉCHELLE: 1:50

NOTE DÉMOLITION - VENTILATION

D1 DIFFUSEUR EXISTANT À ENLEVER TEMPORAIREMENT DURANT LES TRAVAUX AU PLAFOND ET À REINSTALLER.

NOTES DÉMOLITION - PLOMBERIE

- D1 SORTIE D'EAU FROIDE POUR MACHINE À CAFÉ, INSTALLÉE EN SURFACE AU MUR. À DÉMANTELER JUSQU'AU TUYAU D'EAU FROIDE CONSERVÉ.
- D2 CABINET DE CHAUFFAGE HYDRONIQUE EXISTANT À DÉMANTELER.
- D3 SOUPAPE DE CONTRÔLE PNEUMATIQUE EXISTANTE À RELOCALISER DANS LE NOUVEAU CABINET. MODIFIER LA TUYAUTERIE PNEUMATIQUE EXISTANTE DU THERMOSTAT.
- D4 THERMOSTAT PNEUMATIQUE EXISTANT À RELOCALISER PAR L'ENTREPRENEUR EN PLOMBERIE/CHAUFFAGE. MODIFIER LA TUYAUTERIE EXISTANTE JUSQU'aux SOUPAPES DE CONTRÔLE DU LOCAL (CABINET ET SERPENTIN) ET LA TUYAUTERIE D'ALIMENTATION D'AIR EN AMONT DU THERMOSTAT.

NOTE CONSTRUCTION - PLOMBERIE

- 1 NOUVEAU CABINET DE CHAUFFAGE HYDRONIQUE À RACCORDER À LA TUYAUTERIE EXISTANTE CONSERVÉE DE L'ANCIEN CABINET. INSTALLER LA SOUPAPE PNEUMATIQUE EXISTANTE. UN NOUVEAU ROBINET D'ARRÊT ET UN NOUVEAU ROBINET DE VIDANGE DANS LE CABINET.



SANTÉ QUÉBEC GASPÉSIE

RÉF. CLIENT:
PROJET

HÔPITAL DE CHANDLER
(RÉFECTION DE L'ENVELOPPE)

Architecte



CE DOCUMENT NE DOIT PAS SERVIR À
LA CONSTRUCTION

REV	DATE	DESCRIPTION	PAR
RÉVISIONS PARTIELLES			
1	2026/09/04	DÉFINITIFS POUR SOUMISSION	JD-JA
B	2026/08/21	DÉFINITIFS 100% POUR APPROBATION	JD-VS
A	2026/05/14	DÉFINITIFS 60% POUR APPROBATION	JD-VS
REV	DATE	DESCRIPTION	PAR

SCEAU:	
	
MÉCANIQUE	ÉLECTRICITÉ
AVERTISSEMENT: DROIT D'AUTEUR: CE DESSIN EST LA PROPRIÉTÉ INTELLECTUELLE DE WSP CANADA INC. AUCUNE RÉVISION, REPRODUCTION OU TOUT AUTRE USAGE N'EST PERMIS SANS L'AUTORISATION ÉCRITE DE WSP CANADA INC. L'ENTREPRENEUR DEVRA VÉRIFIER TOUTES LES DIMENSIONS AUX PLANS ET FAIRE LOCALISER TOUS LES SERVICES D'UTILITÉS PUBLIQUES ET RAPPORTER TOUTES ERREURS OU OMISSIONS AVANT DE COMMENCER LES TRAVAUX.	
ÉCHELLE: ORIGINALE: INDIQUÉE DESSINÉ PAR: A. CASTONGUAY & A. HALLÉ PRÉPARÉ SOUS SUPERVISION PAR: J. D'AMOURS ET V. STOCKMEYER, ing. PRÉPARÉ PAR: J. D'AMOURS ET J. ALCINDOR, ing. APPROUVÉ ADMINISTRATIVEMENT PAR: S. L'AVOIE	DATE: AVRIL 2026 SI CETTE BARRE NE MESURE PAS 25 mm, AJUSTER VOTRE ÉCHELLE DE TRAPAGE. 25mm
DISCIPLINE: MÉCANIQUE / ÉLECTRICITÉ	

Mécanique / Électricité



NO PROJET: CA0066110.3235

TITRE:

VUES AGRANDIES ET DÉTAILS
AJOUT ISSUE LABORATOIRE
MÉCANIQUE

NUMÉRO DU
FEUILLET:

ME012

\\corp.phonon.net\caddas\carr\1191\projets\2026\11\CA00661\10-32356\Bailment05 TECH04.1 CAO

TABLEAU DES APPAREILS D'ÉCLAIRAGE													
-COORDONNER L'EMPLACEMENT EXACT DES LUMINAIRES SUR LES LIEUX.													
TYPE	APPAREIL	COMPAGNIE	No. CATALOGUE	VOLTS	WATTS	LAMPES	MONTAGE				HAUTEUR DE MONTAGE	REMARQUES	
							SURFACE		ENCASTRÉ				SUSPENDU
							MUR	PLAFOND	MUR	PLAFOND			
L1	LUMINAIRE MURAL C/A PHOTOCELLULE	LITHONIA	WDGE2 LED P4 40K 80CRI T4M MVOLT SRM PE DBLXD	120	47	LED	X				±3050mm	B	
X1	INDICATEUR DE SORTIE UNIVERSEL À PICTOGRAMME	EMERGI-LITE	EA1WU	120/24	-	LED		X				A	
REMARQUES :													
A. CONFORME À LA NORME ISO 31364-1 ET 7010.													
B. VALIDER LA COULEUR AVEC L'ARCHITECTE AVANT LA COMMANDE.													

NOTES CONSTRUCTION - ME013


- MODULE À RELAIS SERVANT À RELÂCHER LA PORTE SUR ALARME INCENDIE.
- ÉQUIPEMENT ET FILERIE À INSTALLER EN SURFACE.


NOTES GÉNÉRALES - ME013

- LE SYSTÈME DE CONTRÔLE D'ACCÈS EST DE MARQUE KANTECH.
- FOURNIR, INSTALLER ET RACCORDER TOUS LES ÉQUIPEMENTS NÉCESSAIRES AU BON FONCTIONNEMENT DE LA PORTE, EN INCLUANT, SANS SY LIMITER, UN CONTRÔLEUR KT-1.
- RACCORDER LE NOUVEAU CONTRÔLEUR KT-1 AU CONTRÔLEUR EXISTANT À PROXIMITÉ.
- FOURNIR TOUS LES ACCESSOIRES REQUIS AINSI QUE LA PROGRAMMATION NÉCESSAIRE.

NOTES GÉNÉRALES - ALARME INCENDIE


- LE SYSTÈME D'ALARME INCENDIE EXISTANT EST DE MARQUE NOTIFIER MODÈLE NFS2-3030-FR DE TYPE ADRESSABLE À DEUX ÉTAPES. CONTACTER LE MANUFACTURIER POUR COORDONNER LE TRAVAIL À EFFECTUER AU SYSTÈME (DÉNUMÉRER LES APPAREILS À AJOUTER ET COORDONNER LA FAISABILITÉ). TOUT LE MATÉRIEL REQUIS DOIT ÊTRE FOURNI PAR LE MANUFACTURIER DU SYSTÈME D'ALARME INCENDIE.
- RACCORDER LES APPAREILS DE DÉTECTION SUR LA BOUCLE DE DÉTECTION EXISTANTE.
- L'INSTALLATION DOIT ÊTRE CONFORME À LA NORME CANULC-524, DERNIÈRE ÉDITION.
- SUITE AUX TRAVAUX, LE MANUFACTURIER DOIT FAIRE UNE VÉRIFICATION COMPLÈTE DE TOUS LES SYSTÈMES AINSI QUE CHAQUE DE SES COMPOSANTES. EN PLUS, IL DOIT VÉRIFIER TOUS LES RACCORDEMENTS AFIN DE S'ASSURER :
 - QUE LE SYSTÈME EST INSTALLÉ SUIVANT LES PLANS ET DEVIS.
 - QUE LE SYSTÈME EST INSTALLÉ SUIVANT LES RECOMMANDATIONS DU MANUFACTURIER ET FONCTIONNE PARFAITEMENT;
 - QUE TOUS LES DISPOSITIFS SONT VÉRIFIÉS AU POINT DE VUE FONCTIONNEMENT.
- LORSQUE LA VÉRIFICATION EST TERMINÉE, REMETTRE UN CERTIFICAT ATTESTANT QUE LES TRAVAUX ONT ÉTÉ RÉALISÉS CONFORMEMENT AUX NORMES.
- LE SYSTÈME D'ALARME INCENDIE EXISTANT DOIT DEMEURER FONCTIONNEL DURANT TOUTE LA DURÉE DES TRAVAUX, INCLUANT LES INTERRUPTIONS DE COURANT.
- TOUS LES TRAVAUX À L'INTÉRIEUR DU PANNEAU D'ALARME INCENDIE DOIVENT ÊTRE RÉALISÉS PAR UN TECHNICIEN DU MANUFACTURIER DU SYSTÈME.
- L'INSPECTION ET LA MISE À L'ESSAI DOIVENT ÊTRE CONFORMES À LA NORME ULC-S536, DERNIÈRE ÉDITION.
- INCLURE TOUS LES COÛTS DU MANUFACTURIER RELATIFS À LA PROGRAMMATION NÉCESSAIRES SUITE AUX PRÉSENTS TRAVAUX.
- LES CONDUCTEURS DU RÉSEAU D'ALARME-INCENDIE DOIVENT ÊTRE DU TYPE SECUREX SOUS GAINÉ MÉTALLIQUE SOUPLE (TYPE BX) DE COULEUR ROUGE OU SOUS CONDUIT EMT DE COULEUR ROUGE ET FAIT SELON LES EXIGENCES DU MANUFACTURIER DU SYSTÈME D'ALARME INCENDIE.

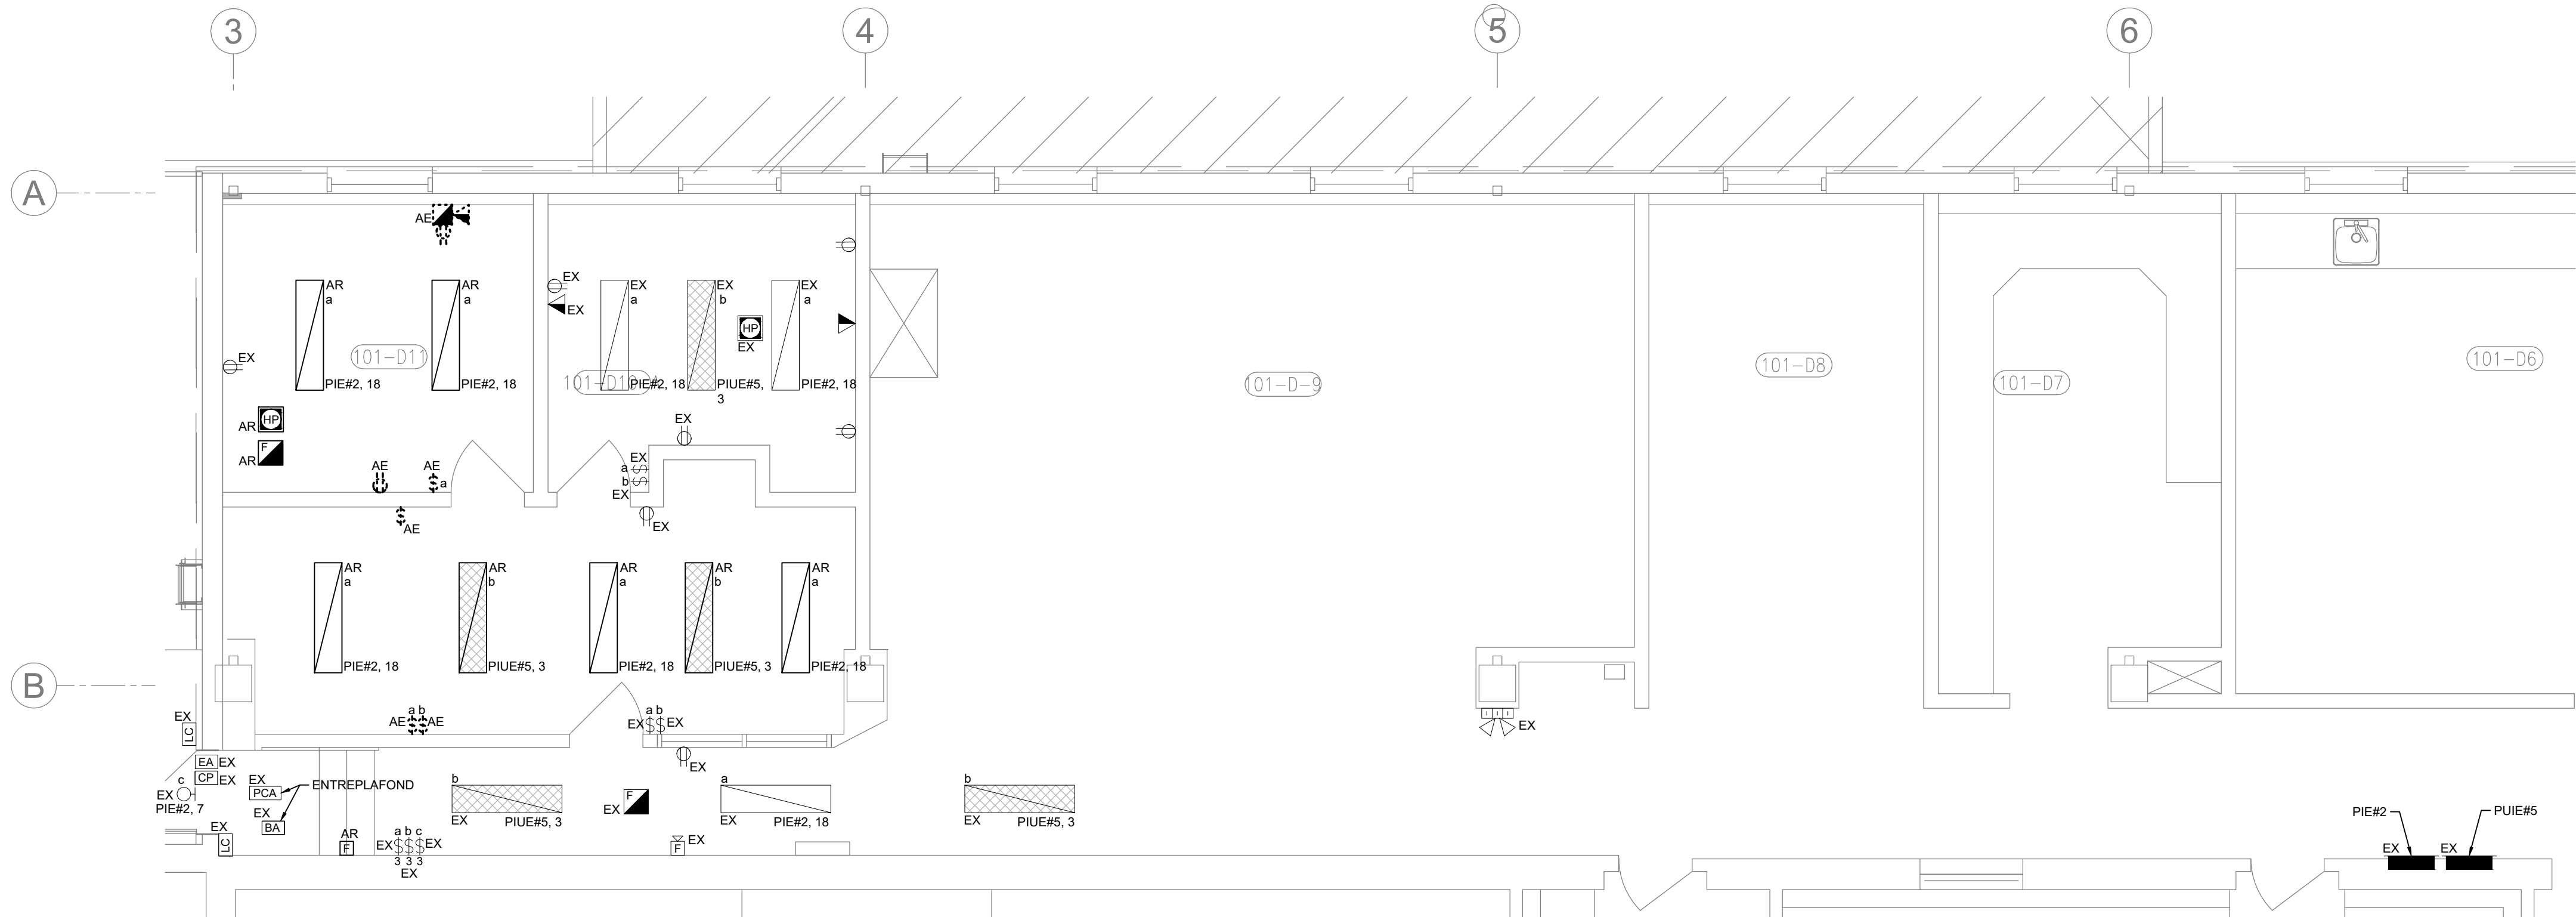

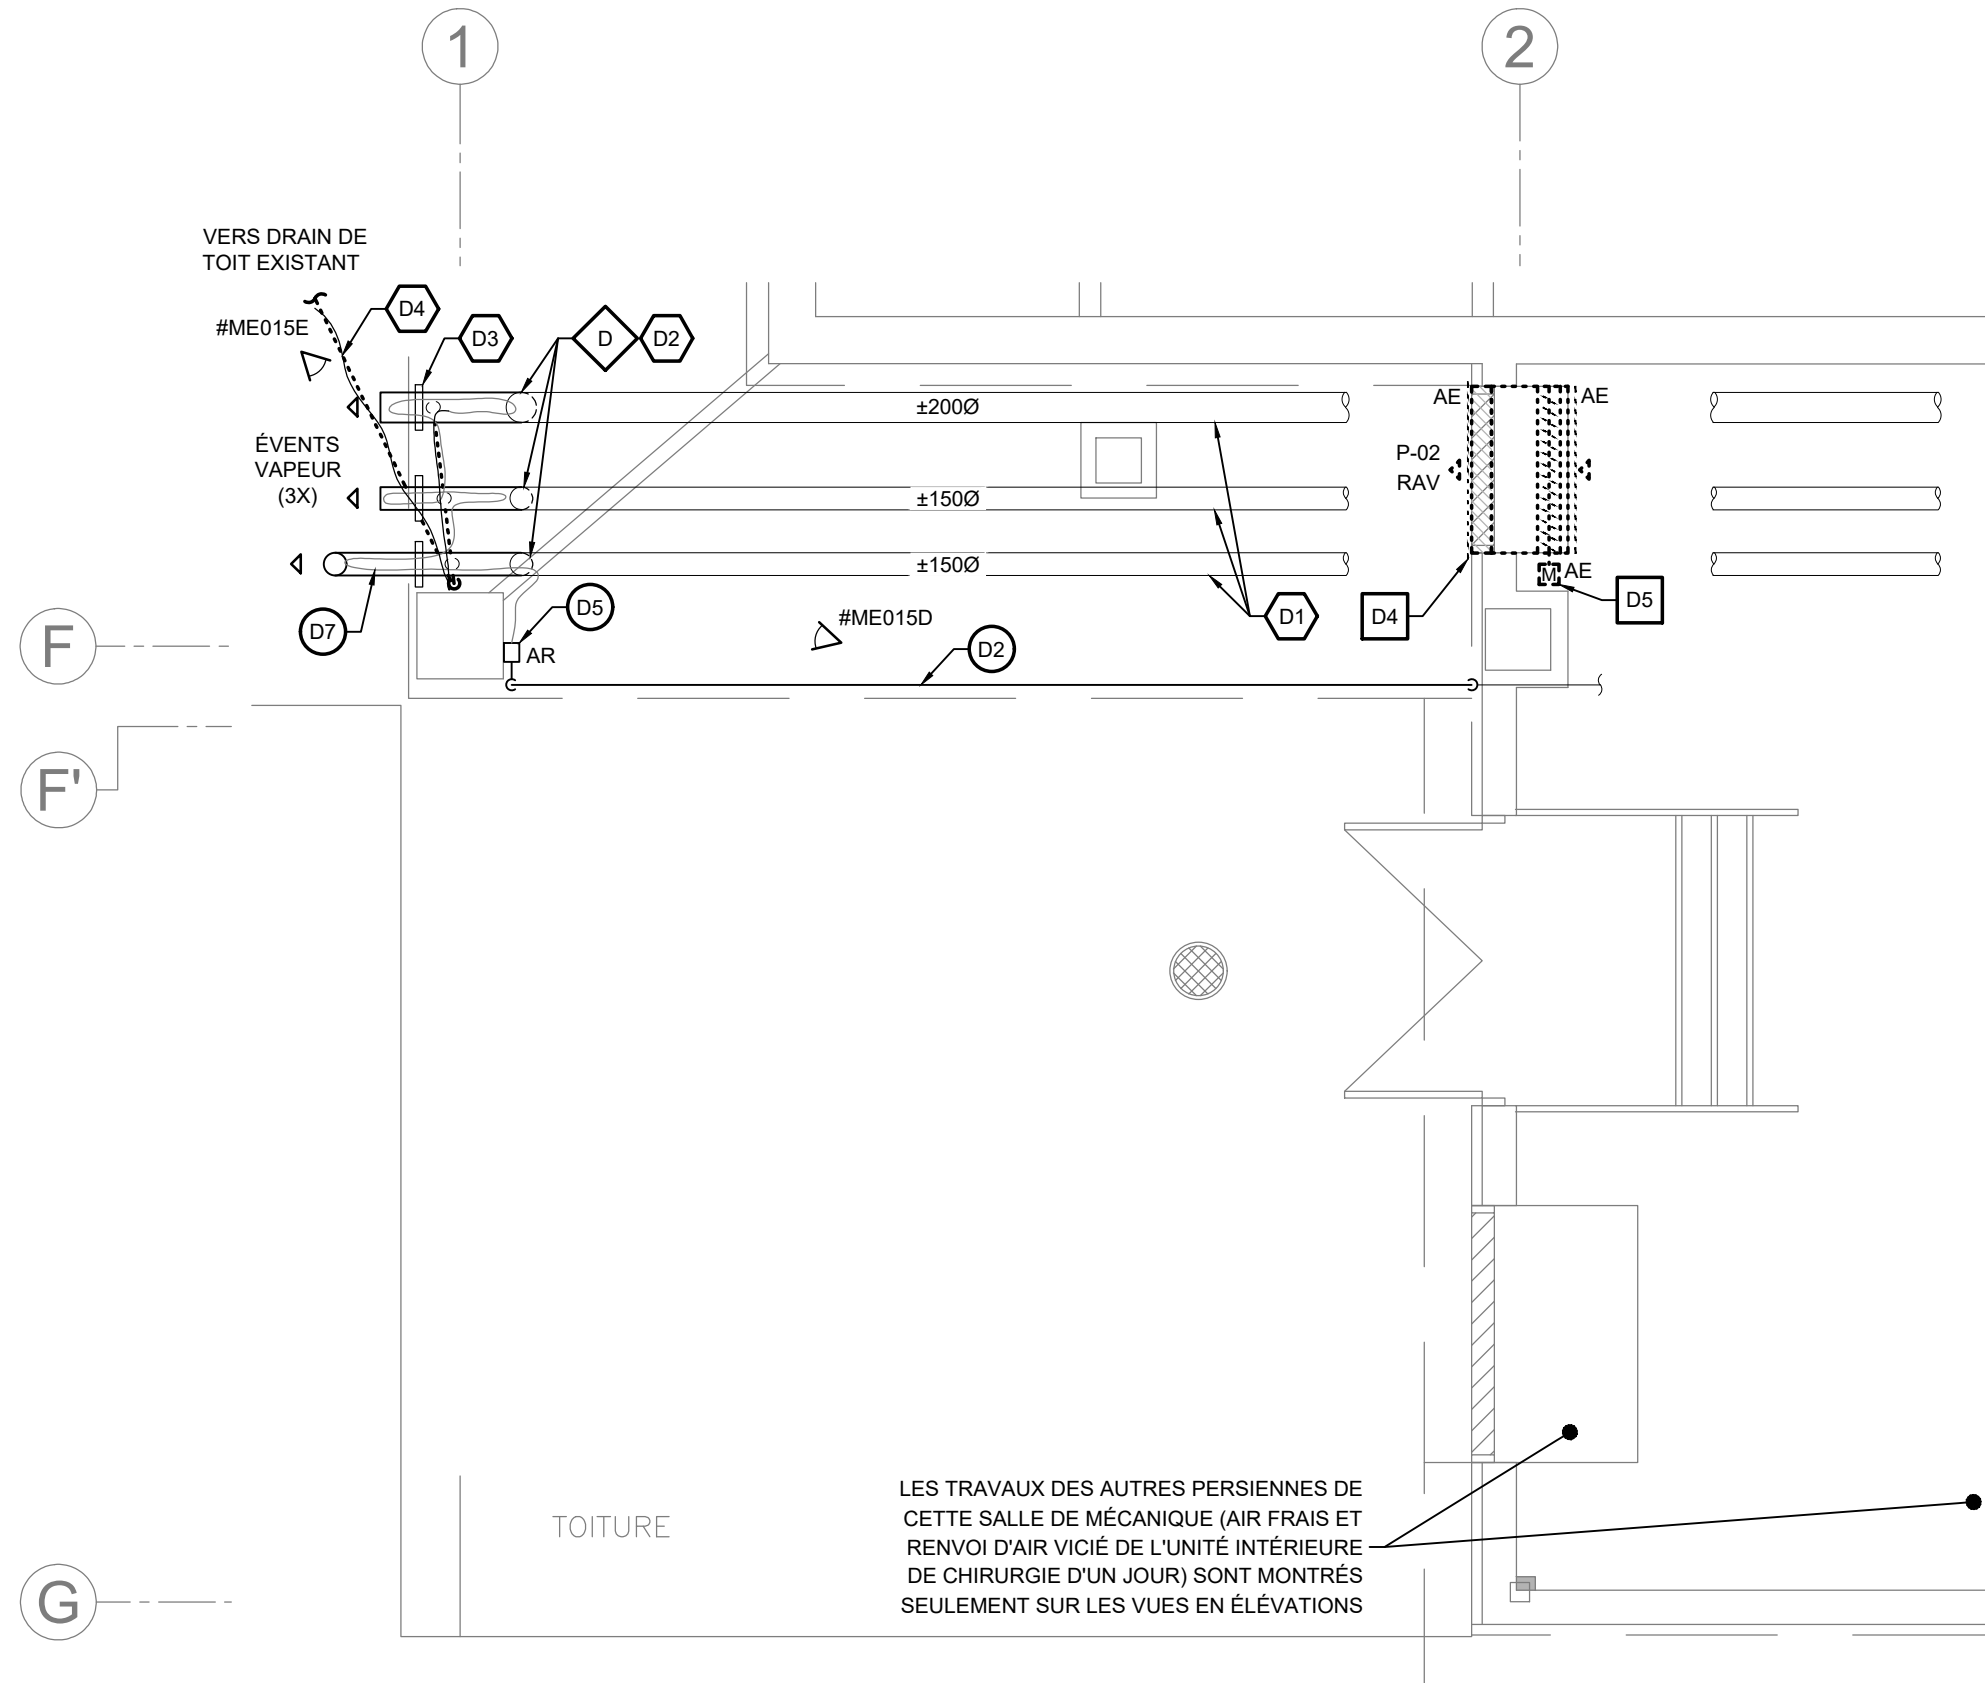


VUE AGRANDIE - SALLE MÉCANIQUE CHIRURGIE D'UN JOUR - DÉMOLITION

ÉCHELLE: 1:50

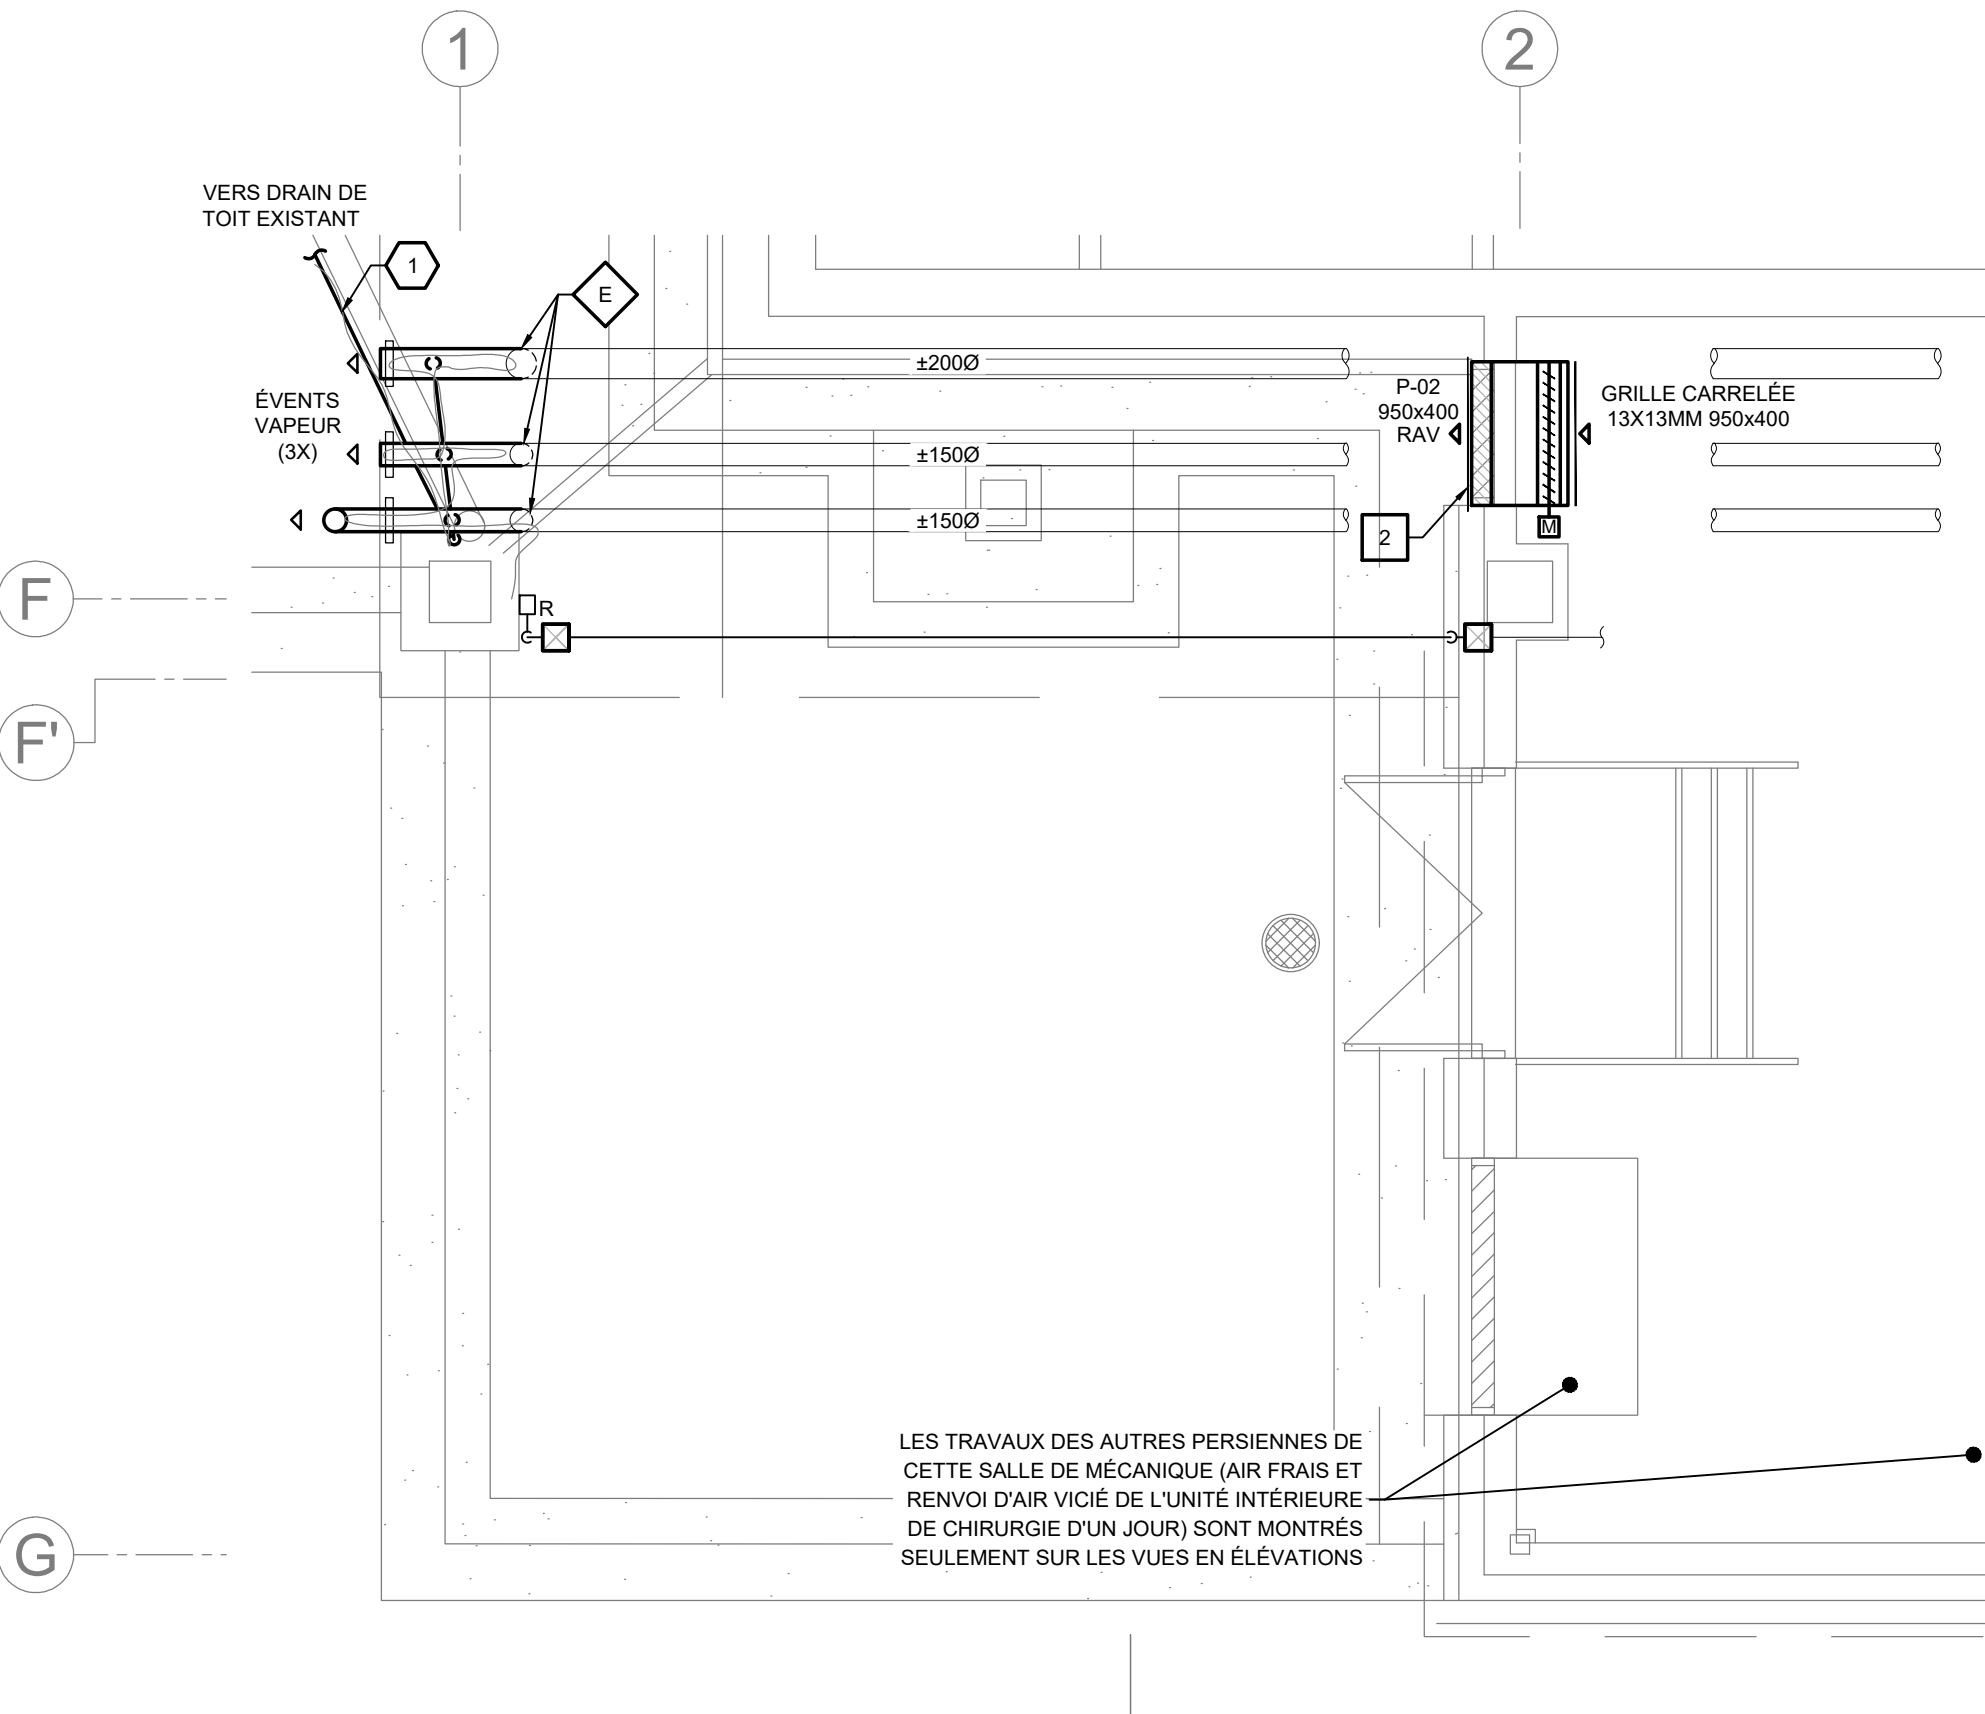


VUE AGRANDIE - SALLE MÉCANIQUE CHIRURGIE D'UN JOUR - CONSTRUCTION

ÉCHELLE: 1:50

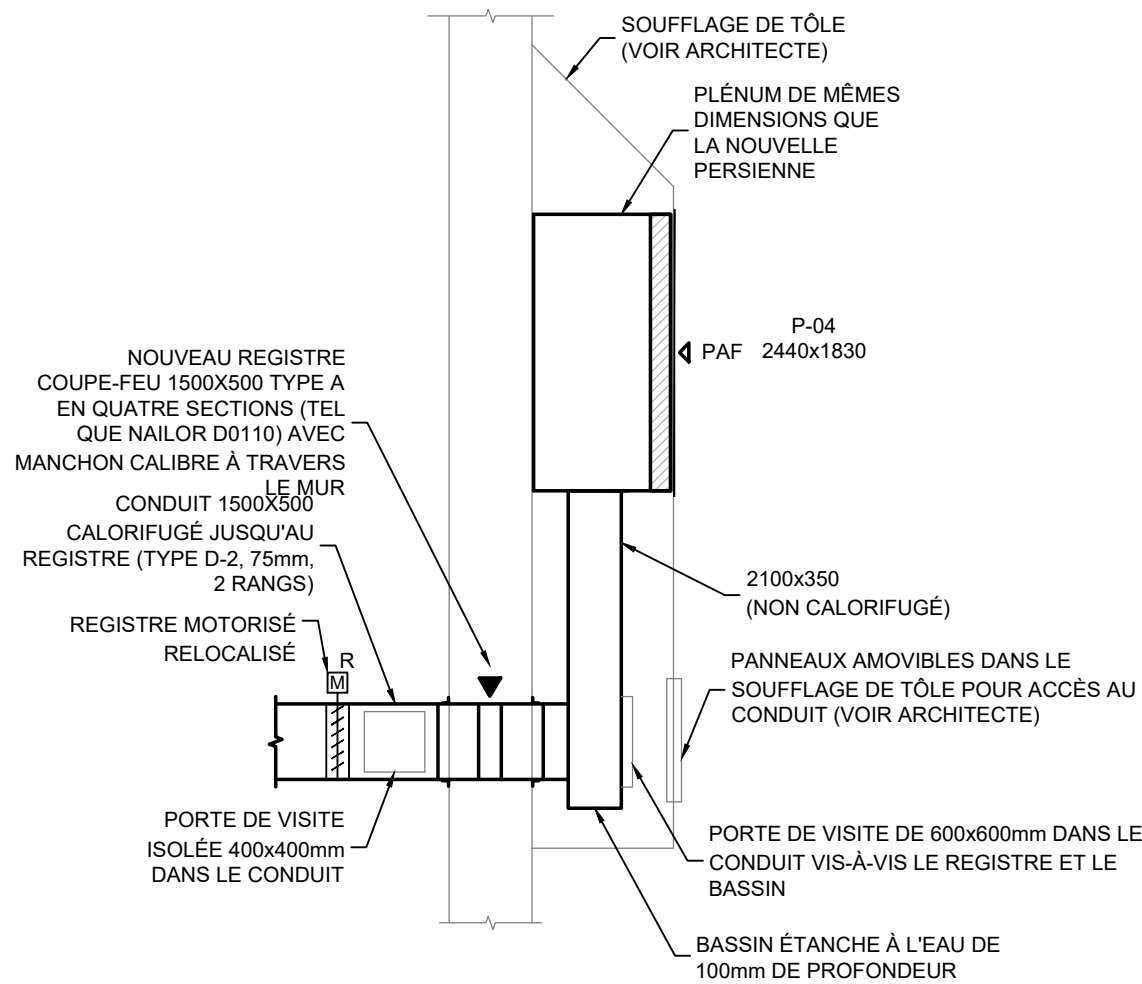


1 COUPE SCHEMATIQUE DU CONDUIT EXTERIEUR

ME015 ÉCHELLE: 1:50

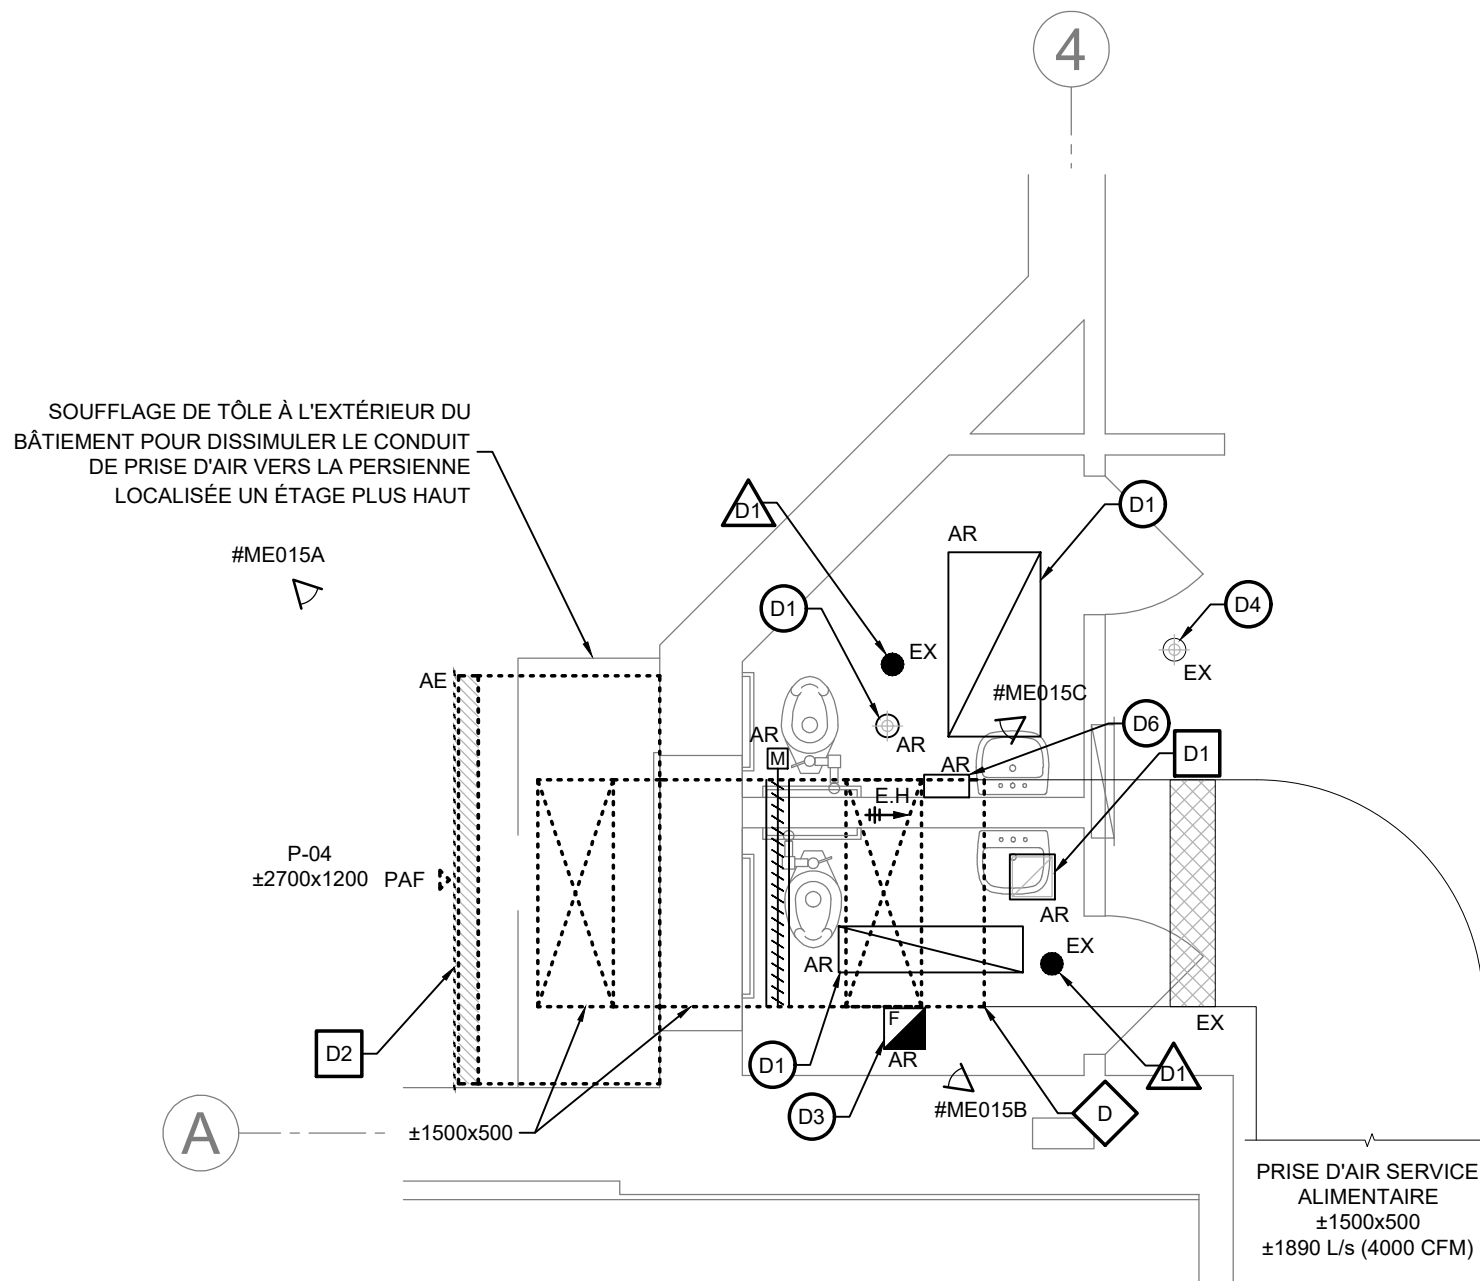

VUE AGRANDIE - PRISE D'AIR SERVICE ALIMENTAIRE - DÉMOLITION

ÉCHELLE: 1:50

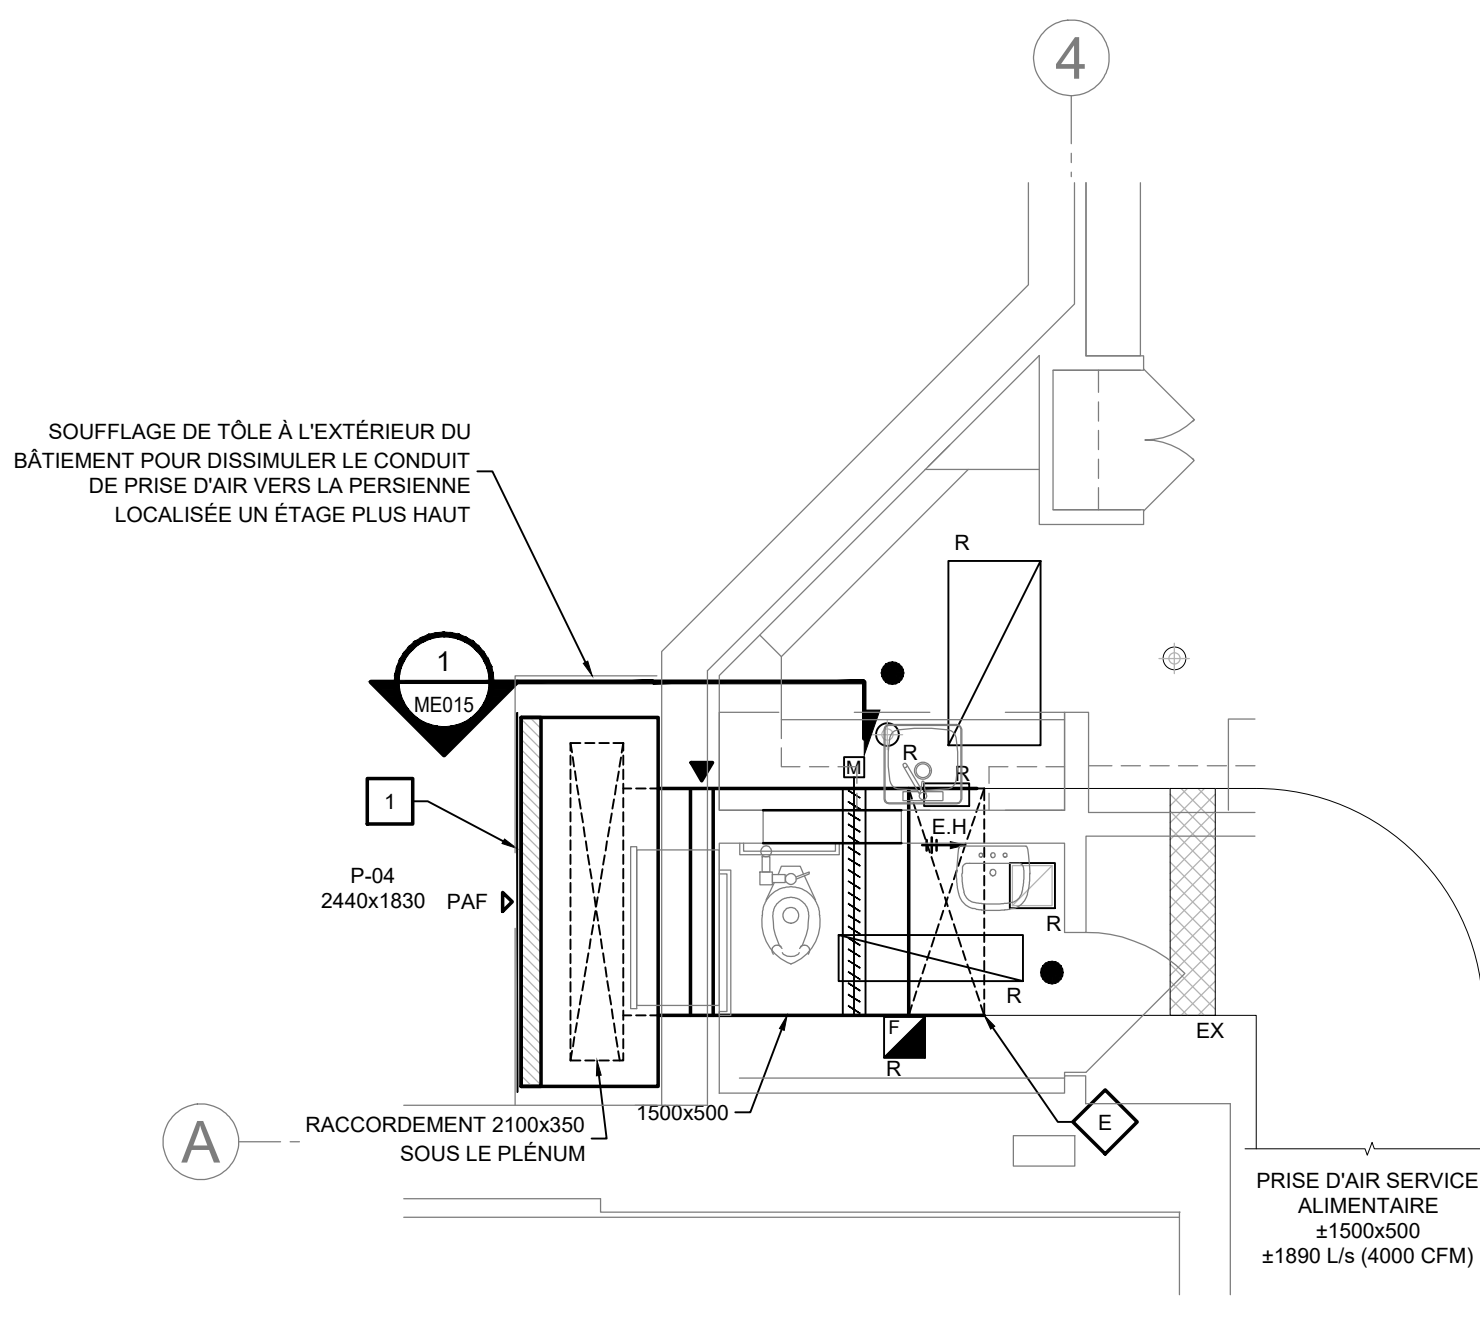

VUE AGRANDIE - PRISE D'AIR SERVICE ALIMENTAIRE - CONSTRUCTION

ÉCHELLE: 1:50

NOTE DÉMOLITION - PLOMBERIE - ME015

- D1 TUYAUTERIE D'ÉVENT DE VAPEUR PROVENANT DE LA CHAUFFERIE, DISSIMULÉES À L'INTÉRIEUR DU PORTE-A-FAUX (AU-DESSUS DU SOFFITE), À CONSERVER EN FONCTION DURANT TOUTE LA DURÉE DES TRAVAUX.
- D2 DÉVIATION DE TUYAUTERIE VERS LE BAS SORTANT SOUS LE SOFFITE, À PROLONGER AFIN D'ABAISSE LES ÉVÉNEMENTS DE VAPEUR EN-DESSOUS DU NOUVEAU SOFFITE. ADAPTER LA LONGUEUR DE TUYAUTERIE SELON LES NOUVELLES ÉPAISSEURS D'ENVELOPPE EXTERIEURE DU BÂTIMENT (VOIR ARCHITECTE).
- D3 SUPPORT DE TYPE "COLIER POUR COLONNE MONTANTE" EN ACIER INOXYDABLE À REMPLACER.
- D4 TUYAUTERIE DE DRAINAGE DE CONDENSATS DES ÉVÉNEMENTS DE VAPEUR À REMPLACER EN CUIVRE DWV 380 AVEC CALORIFUGE DE TYPE P-1 ET CHEMISAGE EN ALUMINIUM. CONSERVER LE RACCORD SUR LES ÉVÉNEMENTS D'ACIER INOXYDABLE ET REFAIRE LA TUYAUTERIE TEL QUE L'EXISTANTE EN S'ADAPTANT SELON LES NOUVELLES ÉPAISSEURS D'ENVELOPPE EXTERIEURE DU BÂTIMENT (VOIR ARCHITECTE). COORDONNER LA RÉINSTALLATION DU CÂBLE CHAUFFANT AUTOUR DE LA TUYAUTERIE DE DRAINAGE (SOUS L'ISOLANT) ET À L'INTÉRIEUR DES TROIS ÉVÉNEMENTS DE VAPEUR, TEL QUE L'EXISTANT.

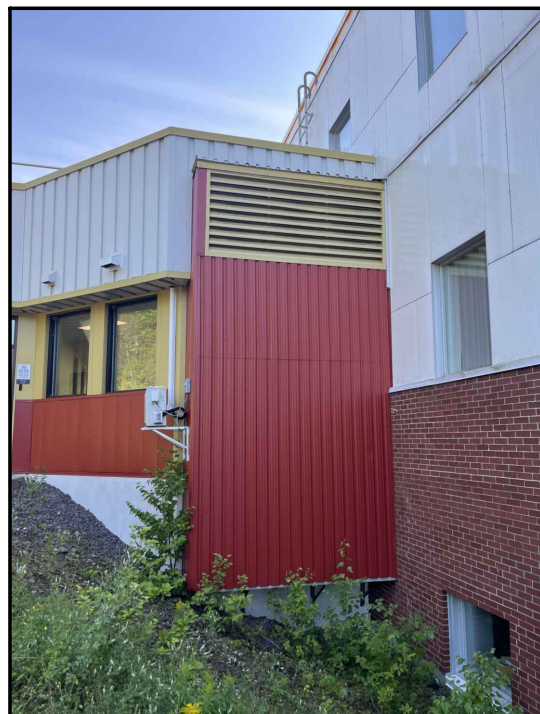


PHOTO #ME015A

ÉCHELLE: AUCUNE

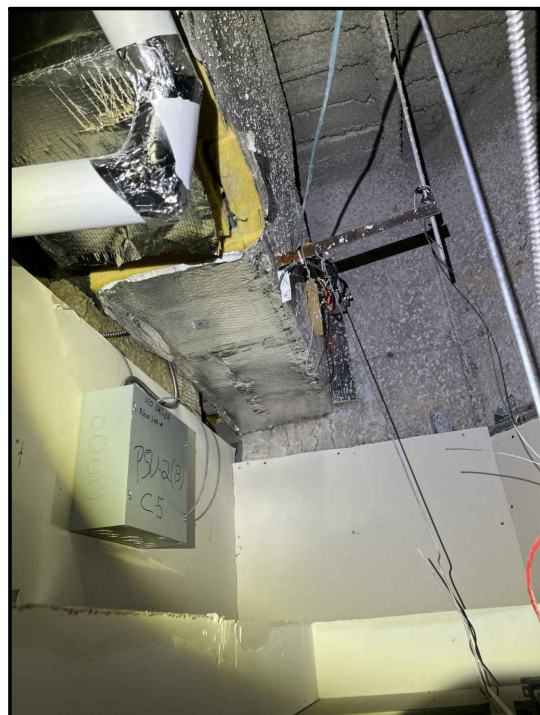


PHOTO #ME015C

ÉCHELLE: AUCUNE



PHOTO #ME015D

ÉCHELLE: AUCUNE



PHOTO #ME015B

ÉCHELLE: AUCUNE

NOTES DÉMOLITION VENTILATION - ME015

- D1 GRILLE / DIFFUSEUR À ENLEVER TEMPORAIREMENT AFIN DE PERMETTRE LES TRAVAUX DANS L'ENTREPLAFOND ET À RELOCALISER DANS LE PLAFOND AU MÊME ENDROIT.
- D2 PERSIENNE DE PRISE D'AIR FRAIS DU SERVICE ALIMENTAIRE À REMPLACER DANS LE SOUFFLAGE DE TÔLE ARCHITECTURAL À L'EXTÉRIEUR DU BÂTIMENT.
- D3 REGISTRE MOTORISÉ EXISTANT AVEC ACTUATEUR BÉLIMO À RELOCALISER AFIN DE PERMETTRE L'AJOUT DU REGISTRE COUPE-FEU. LE CONDUIT INTÉRIEUR À MODIFIER EST CALORIFUGÉ AVEC PANNEAUX RIGIDES DISSOLANT DE FIBRE DE VERRE 75MM EN DEUX RANGS À JOINTS CHEVAUCHÉS ET PARE-VAPEUR INTÉGRÉ (TYPE D-2, VOIR DEVIS).
- D4 PERSIENNE DE RENVOI D'AIR VICIÉ DE LA SALLE DE MÉCANIQUE DE CHIRURGIE D'UN JOUR, À DÉMANTÉLER INCLINANT LE PLENUM. REGISTRE MOTORISÉ ET GRILLE INTÉRIEURE LA NOUVELLE PERSIENNE SERA PLUS PETITE QUE CELLE EXISTANTE. OBTURATION DE L'OUVERTURE EXCÉDENTAIRE PAR L'ENTREPRENEUR GÉNÉRAL.
- D5 ACTUATEUR DE REGISTRE MOTORISÉ HONEYWELL EXISTANT À REMPLACER PAR L'ENTREPRENEUR EN RÉGULATION. POINT DE CONTRÔLE À CONSERVER POUR RÉALISER LES TRAVAUX.

NOTES DÉMOLITION - ÉLECTRICITÉ - ME015

- D1 LUMINAIRE EXISTANT À ENLEVER TEMPORAIREMENT AFIN DE PERMETTRE LES TRAVAUX DANS L'ENTREPLAFOND ET À RELOCALISER DANS LE PLAFOND AU MÊME ENDROIT.
- D2 CONDUIT EMT C/A FILAGE APPARENT SOUS LE SOFFITE À MODIFIER AFIN DE S'ADAPTER À L'ÉPAISSEUR DE LA NOUVELLE ENVELOPPE DU BÂTIMENT. FOURNIR TOUS LES ACCESSOIRES REQUIS INCLINANT, SANS S'Y LIMITER, BOÎTES DE JONCTION, FILAGE, CONDUITS, COUDES, ETC.
- D3 DÉTECTEUR DE FUMÉE EXISTANT À ENLEVER TEMPORAIREMENT AFIN DE PERMETTRE LES TRAVAUX DANS L'ENTREPLAFOND ET À RELOCALISER DANS LE PLAFOND AU MÊME ENDROIT. INCLURE LA VÉRIFICATION DE FONCTIONNEMENT DE CETTE COMPOSANTE DANS LE RAPPORT DE VÉRIFICATION D'ALARME-INCENDIE DU PROJET.
- D4 LUMINAIRE EXISTANT À CONSERVER ET À PROTÉGER DURANT LES TRAVAUX AU PLAFOND.
- D5 THERMOSTAT POUR CÂBLES CHAUFFANTS DE MARQUE PYROTENAX À ENLEVER TEMPORAIREMENT LE TEMPS DES TRAVAUX ET À RÉINSTALLER SUR LA COLONNE APRÈS LES TRAVAUX DE REVÊTEMENT.
- D6 BOÎTIER POUR "DRIVER" D'ÉCLAIRAGE LED DU LOCAL S44 À RELOCALISER TEMPORAIREMENT POUR EFFECTUER LES TRAVAUX SUR LA CLOISON DANS L'ENTREPLAFOND.
- D7 CÂBLE CHAUFFANT EXISTANT À ENLEVER TEMPORAIREMENT ET À RÉINSTALLER LE LONG DES TUYAUTERIES DE DRAINAGE DE CONDENSATS ET D'ÉVENT DE VAPEUR (À COORDONNER AVEC L'ENTREPRENEUR EN PLOMBERIE).

NOTE DÉMOLITION - GICLEURS - ME015

- Δ GICLEUR EXISTANT SEMI-ENCASTRÉ À CONSERVER ET À PROTÉGER DURANT LES TRAVAUX AU PLAFOND. ENLEVER LA ROSACE AFIN DE PERMETTRE LE DÉMANTÈLEMENT ET LE REMPLACEMENT COMPLET DU PLAFOND SUSPENDU DANS CE LOCAL.

NOTE CONSTRUCTION VENTILATION - ME015

- 1 NOUVELLE PERSIENNE DE PRISE D'AIR FRAIS (VOIR TABLEAU) À INSTALLER DANS LE SOUFFLAGE DE TÔLE À L'EXTÉRIEUR DU BÂTIMENT. LE CONDUIT DE PRISE D'AIR NEUF DOIT ÊTRE REMPLACÉ JUSQU'AU POINT INDiqué AFIN DE FAIRE L'AJOUT D'UN REGISTRE COUPE-FEU VIS-À-VIS LE MUR EXTERIEUR.
- 2 NOUVELLE PERSIENNE DE RENVOI D'AIR VICIÉ (VOIR TABLEAU), NOUVEAU REGISTRE MOTORISÉ ET NOUVELLE GRILLE D'ÉVACUATION CARELÉE TEL QUE NALOR S/EC. DIMENSIONS DE 950X400. ACTUATEUR PAR L'ENTREPRENEUR EN RÉGULATION.

NOTE CONSTRUCTION - PLOMBERIE - ME015

- 1 NOUVELLE TUYAUTERIE DE DRAINAGE DE CONDENSATS DES ÉVÉNEMENTS DE VAPEUR, APPARENT EN SURFACE DE LA TOITURE ET DU REVÊTEMENT EXTERIEUR, EN CUIVRE DWV 380 AVEC CALORIFUGE DE TYPE P-1 ET CHEMISAGE EN ALUMINIUM. FOURNIR ET INSTALLER TROIS NOUVEAUX SUPPORTS DURABLES DE 10 POUR ACHÉMINER LA TUYAUTERIE DIRECTEMENT AU-DESSUS DU DRAIN DE TOIT.



PHOTO #ME015E

ÉCHELLE: AUCUNE

SANTÉ QUÉBEC GASPÉSIE

RÉF. CLIENT:
PROJET

HÔPITAL DE CHANDLER
(RÉFECTION DE L'ENVELOPPE)

Architecte

CE DOCUMENT NE DOIT PAS SERVIR À LA CONSTRUCTION

REV	DATE	DESCRIPTION	PAR
RÉVISIONS PARTIELLES			
1	2026/09/04	DÉFINITIFS POUR SOUMISSION	JDJA
B	2026/08/21	DÉFINITIFS 100% POUR APPROBATION	JDVS
A	2026/05/14	DÉFINITIFS 60% POUR APPROBATION	JDVS
REV	DATE	DESCRIPTION	PAR

SCEAU:

MÉCANIQUE

ÉLECTRICITÉ

AVERTISSEMENT: DROIT D'AUTEUR:
CE DESSIN EST LA PROPRIÉTÉ INTELLECTUELLE DE WSP CANADA INC. AUCUNE RÉVISION, REPRODUCTION OU TOUT AUTRE USAGE N'EST PERMIS SANS L'AUTORISATION ÉCRITE DE WSP CANADA INC. L'ENTREPRENEUR DEVRA VÉRIFIER TOUTES LES DIMENSIONS AUX PLANS ET FAIRE LOCALISER TOUS LES SERVICES D'UTILITÉS PUBLIQUES ET RAPPORTER TOUTES ERREURS OU OMISSIONS AVANT DE COMMENCER LES TRAVAUX.

ÉCHELLE: ORIGINALE:
INDIQUÉE
A. HALLÉ
PRÉPARÉ SOUS SUPERVISION PAR:
J. D'AMOURS ET V. STOCKMEYER, ing.
PRÉPARÉ PAR:
J. D'AMOURS ET J. ALCINDOR, ing.
APPROUVÉ ADMINISTRATIVEMENT PAR:
G. LAVOIE

DATE:
AVRIL 2026
SI CETTE BARRE NE MESURE PAS 25 mm, AJUSTER VOTRE ÉCHELLE DE TRAPAGE.
25mm

DISCIPLINE:
MÉCANIQUE / ÉLECTRIQUE

Mécanique / Électricité

NO PROJET: CA0066110.3235

TITRE:
VUES AGRANDIES ET DÉTAILS
SALLE MÉCANIQUE CHIRURGIE D'UN JOUR ET PRISE D'AIR SERVICE ALIMENTAIRE

NUMÉRO DU FEUILLET:
ME015

FORMAT D+ (36" x 24")

