



PHOTOS DE L'EXISTANT



- NOTES

- 1 ÉCHELLE EXISTANTE À DÉMONTÉ ET À PROTÉGER
PENDANT LES TRAVAUX POUR RÉINSTALLATION APRÈS
MODIFICATION DE L'ÉCHELLE.
- 2 SECTION DES LONGERONS DE L'ÉCHELLE EXISTANTE À
COUPER. MEULER LES ARRETES DE LA COUPE.
- 3 BRACKETES DE L'ÉCHELLE EXISTANTE À COUPER.
- 4 CONSERVER UNE LONGUEUR DE LONGERON D'AU MOINS
300mm AU-DESSUS DU DERNIER ECHELLONN.
- 5 GARDE-CORPS EXISTANT À DÉMONTÉ ET À PROTÉGER
PENDANT LES TRAVAUX POUR RÉINSTALLATION APRÈS
MODIFICATION DU GARDE-CORPS.
- 6 SECTION DU GRADE-CORPS EXISTANT À COUPER.
- 7 PORTILLON EXISTANT À DÉMONTÉ ET À PROTÉGER
PENDANT LES TRAVAUX POUR RÉINSTALLATION APRÈS
LES MODIFICATIONS AU FENÊTRES.
- 8 ÉCHELLE EXISTANTE RÉINSTALLÉE APRÈS LES TRAVAUX
D'AJUSTEMENT DE L'ÉCHELLE, VOIR ÉLEVATIONS POUR
FENÊTRES EXISTANTES. RÉINSTALLATION DE L'ÉCHELLE
- 9 POTEAUX ET PLAQUES DE FIXATION EN STRUCTURE
D'ACIER. VOIR DOCUMENTS D'INGÉNIEURIE.
- 10 PAIRE DE PLAQUES PLEES AJUSTABLES EN ALUMINIUM
75mm DE LARGEUR, 6mm ép. FIXER LA PREMIÈRE
PLAQUE PLEUE À L'ARRIÈRE DES ECHELLONN EXISTANTS
DE L'ÉCHELLE. FIXER LA DEUXIÈME PLAQUE PLEUE SUR LA
PLAQUE DE FIXATION DE STRUCTURE. INSTALLER UN
SÉPARATEUR DIÉLECTRIQUE ENTRE LA PLAQUE PLEUE ET
LA PLAQUE DE FIXATION EN ACIER DE STRUCTURE.
- 11 PAIRE DE PLAQUES PLEES AJUSTABLES EN ALUMINIUM
75mm DE LARGEUR, 6mm ép. FIXER LA PREMIÈRE
PLAQUE PLEUE À L'ARRIÈRE DES ECHELLONN EXISTANTS
DE L'ÉCHELLE. FIXER LA DEUXIÈME PLAQUE PLEUE SUR LA
PLAQUE DE RIVE EN ACIER. INSTALLER UN BRIS
THERMIQUE D'UNE ÉPAISSEUR DE 13mm ENTRE LA
PLAQUE PLEUE ET LA POUTRE EXISTANTE.
- 12 PAIRE DE PLAQUES PLEES AJUSTABLES EN ALUMINIUM
75mm DE LARGEUR, 6mm ép. FIXER LA PREMIÈRE
PLAQUE SUR LE CÔTÉ EXTÉRIEUR DES ECHELLONN
EXISTANTS DE L'ÉCHELLE. FIXER LA DEUXIÈME PLAQUE
PLEUE SUR LA PLAQUE DE FIXATION DE STRUCTURE.
INSTALLER UN SÉPARATEUR DIÉLECTRIQUE ENTRE LA
PLAQUE PLEUE ET LA PLAQUE DE FIXATION DE
STRUCTURE.
- 13 PAIRE DE PLAQUES PLEES AJUSTABLES EN ALUMINIUM
75mm DE LARGEUR, 6mm ép. FIXER LA PREMIÈRE
PLAQUE SUR LE CÔTÉ EXTÉRIEUR DES ECHELLONN
EXISTANTS DE L'ÉCHELLE. FIXER LA DEUXIÈME PLAQUE
PLEUE SUR LA POUTRE DE RIVE EN ACIER. INSTALLER UN
BRIS THERMIQUE D'UNE ÉPAISSEUR DE 13mm
ENTRE LA PLAQUE PLEUE ET LA POUTRE.
- 14 PALIER EN CALLEBOTIS D'ALUMINIUM SUR UNE
STRUCUTURE EN ALUMINIUM 50x50mm, 6mm ép.
FIXER AVEC CORNIÈRE DE RENFORT À MIS-PORTÉE.
- 15 CORNIÈRE DE RENFORT EN ALUMINIUM 50x50mm, 6mm
ép. FIXER SUR L'ARRIÈRE DES LONGERONS DE
L'ÉCHELLE EXISTANTE ET SUR LES CORNIÈRES DU
PALIER.
- 16 FIXER MÉCANIQUEMENT LA STRUCTURE DU PALIER À
L'ARRIÈRE DES LONGERONS DE L'ÉCHELLE EXISTANTE.
- 17 CORNIÈRE EN ALUMINIUM DE DIMENSIONS REQUISES
POUR FIXER LE CÔTÉ EXTÉRIEUR DES ECHELLONN
EXISTANTS DE L'ÉCHELLE. INSTALLER UN
SÉPARATEUR DIÉLECTRIQUE ENTRE LA CORNIÈRE ET LE
FER "C".
- 18 FER "C" EN ACIER GALVANISÉ C200x17, INSTALLÉ SUR
LE DESSUS DU PARAPET.
- 19 NOUVEAU PARAPET POUR ASSISSE DU NOUVEAU PALIER
DE L'ÉCHELLE.
- 20 GARDE-CORPS COMPOSÉ DE HSS EN ALUMINIUM DE
38x38mm, 6mm ép. LE GARDE-CORPS DOIT ÊTRE FIXÉ
MÉCANIQUEMENT À LA STRUCTURE DU PALIER.
- 21 CORNIÈRE EN ALUMINIUM 50x50mm, 6mm ép. DE
200mm DE LONGUEUR, FIXÉE MÉCANIQUEMENT SUR LE
CÔTÉ EXTÉRIEUR DES LONGERONS DE L'ÉCHELLE
EXISTANTE.
- 22 FIXER MÉCANIQUEMENT LA STRUCTURE DU PALIER À
L'ARRIÈRE DES NOUVELLES CORNIÈRES INSTALLÉES SUR
LE CÔTÉ DES LONGERONS DE L'ÉCHELLE EXISTANTE.
- 23 CORNIÈRE DE RENFORT EN ALUMINIUM 50x50mm, 6mm
ép. FIXER SUR L'ARRIÈRE DES NOUVELLES CORNIÈRES
INSTALLÉES SUR LE CÔTÉ DES LONGERONS DE
L'ÉCHELLE EXISTANTE, ET SUR LES CORNIÈRES DU
PALIER.
- 24 TÔLE EN ACIER GALVANISÉ, 1.994mm ép. INSTALLÉE EN
SURFACE DE PARAPET AVANT L'INSTALLATION DES
NOUVELLES MEMBRANES DU PARAPET.
- 25 CORNIÈRE EN ALUMINIUM CONTINUE 150x100mm, 9mm
ép. FIXÉE DANS LA NOUVELLE TÔLE DANS LE PARAPET.
GARDE-CORPS EXISTANT RÉINSTALLÉ.
- 26 COUPER LES CHARNIÈRES DU PORTION EXISTANT ET
RETIRER LA PLAQUE MURALE.
- 27 POTEAUX EN ACIER GALVANISÉ 38x38mm AVEC PLAQUE
DE FIXATION AU SOL. UTILISER DES ANCRAGES
CHIMIQUES POUR LA FIXATION DU POTEAU DANS LA
DALLE DE BÉTON EXISTANTE.
- 28 INSTALLER DE NOUVELLES CHARNIÈRES SUR LE PORTION
EXISTANT ET LE NOUVEAU POTEAU EN ACIER.
- 29 SYSTÈME ANTI-CHÛTE POUR ÉCHELLE.
- 30 PORTILLON EXISTANT RÉINSTALLÉ.
- 31 SYSTÈME DE LOQUET EXISTANT CONSERVÉ.
- 32 MEULER LES SURFACES DU GARDE-CORPS QUI ONT ÉTÉ
COUPÉ ET FAIRE DES RETOUCHES DE GALVANISATION À
FROID AVANT LA RÉINSTALLATION DU GARDE-CORPS.
- 33 BRACKETE DE FIXATION EN ACIER EXISTANTE À
DÉMOUR.
- 34 UNITÉ DE MÉCANIQUE ET SON SUPPORT EXISTANTS À
DÉMONTÉLER TEMPORAIREMENT, VOIR DOCUMENTS
D'INGÉNIEURIE.
- 35 MÉCANISME DE BOUCHER DE FAÇON ÉTANCHE TOUS LES
PERÇEMENTS DU SYSTÈME DE TOITURE EXISTANT APRÈS
LE RETRAIT DU GARDE-CORPS.
- 36 UNITÉ DE MÉCANIQUE ET SON SUPPORT EXISTANTS
RÉINSTALLÉS, VOIR DOCUMENTS D'INGÉNIEURIE.
- 37 RETENUE DE PORTE EXISTANTE À DÉMONTÉLER ET
RETRANSPORTER PENDANT LES TRAVAUX POUR
RÉINSTALLATION FUTURE.
- 38 RETENUE DE PORTE EXISTANTE RÉINSTALLÉE SUR LE
NOUVEAU POTEAU.
- 39 CORNIÈRE EN ACIER GALVANISÉ CONTINUE 150x100mm,
9mm ép. FIXÉE DANS LA NOUVELLE TÔLE DANS LE
PARAPET.


NE DOIT PAS SERVIR À L'EXÉCUTION

Le présent document est émis pour la seule fin identifiée. Son contenu est protégé par les droits d'auteur et toute reproduction ou modification, partielle ou totale, est interdite sans l'autorisation écrite de gagnon, letellier, cyr, ricard, mathieu, proulx, savard consortium d'architectes.

PROJET	HÔPITAL DE CHANDLER, Chandler (Réfection de l'enveloppe)	DESIGNATEUR (S)	DESIGNER No. J.L.	24-108 / 1857-24
		ÉCHELLE INDIQUÉE	DATE	SEPTEMBRE 2026
PROPRIÉTAIRE	HÔPITAL DE CHANDLER, Chandler (Réfection de l'enveloppe)	05	2024-09-04	DÉFINITIVES POUR SOUMISSION
		04	2024-08-21	DÉFINITIVES 100% POUR APPROBATION
		03	2024-08-03	DÉFINITIVES 80% POUR APPROBATION
		02	2024-05-14	DÉFINITIVES 60% POUR APPROBATION
		01	2024-02-27	PRÉLIMINAIRES 30% POUR APPROBATION
No	DATE	RÉVISIONS		





PHOTOS DE L'EXISTANT

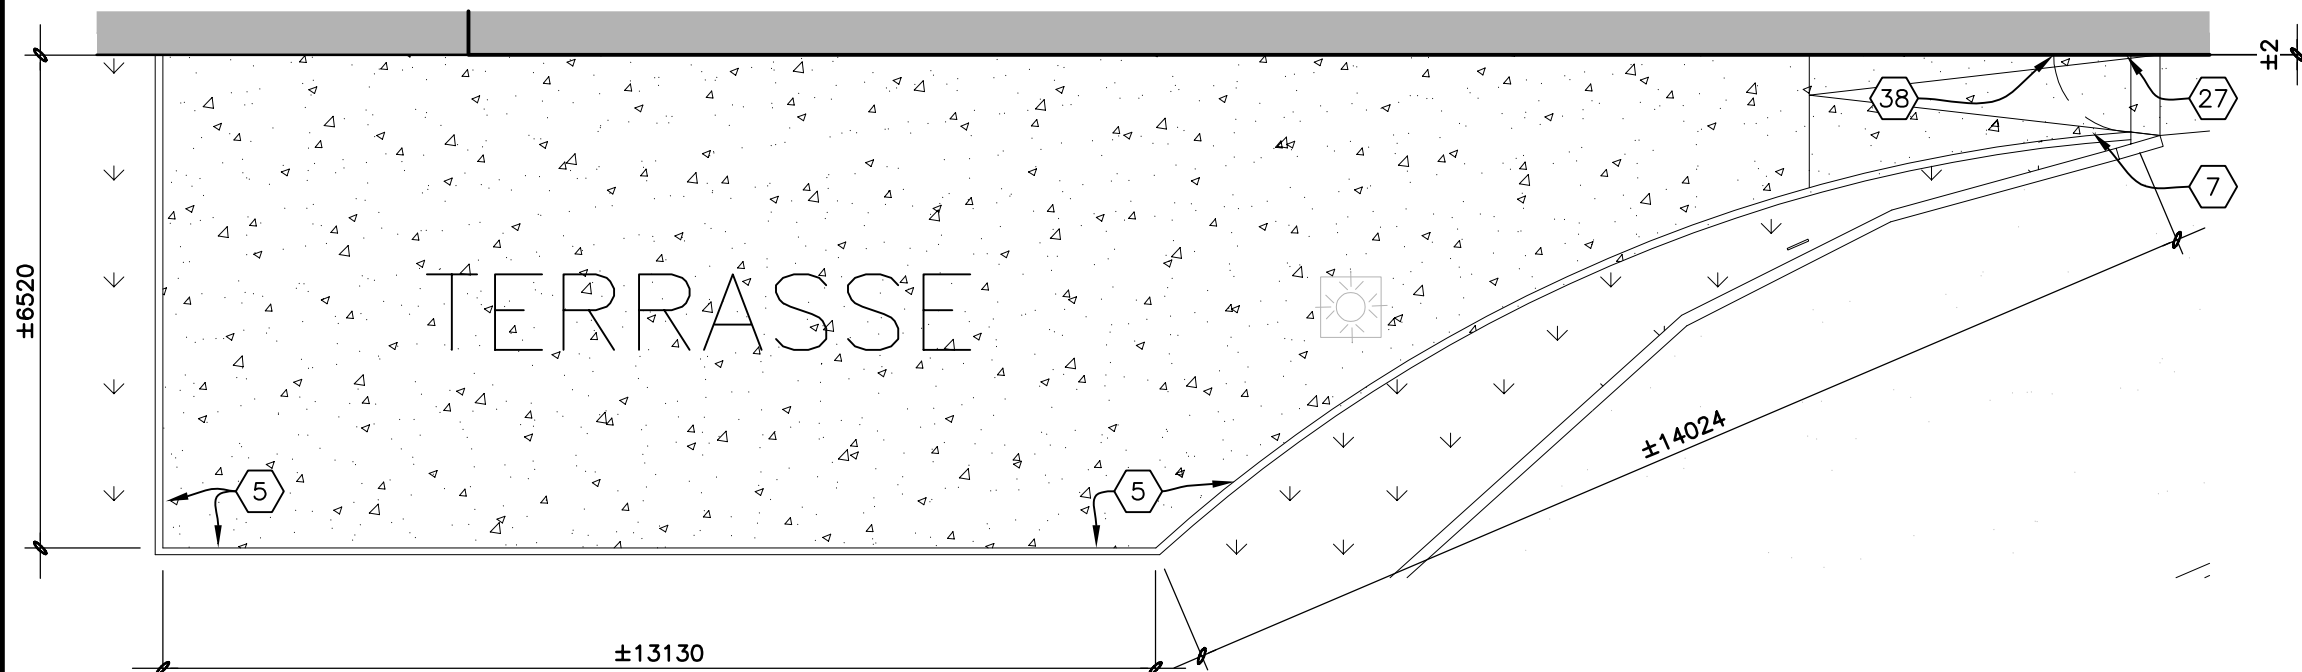


PLAN DE L'EXISTANT

1:100

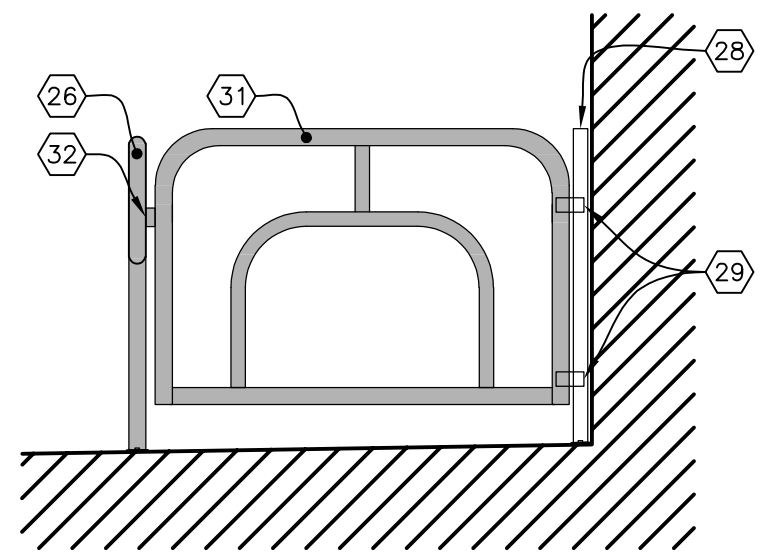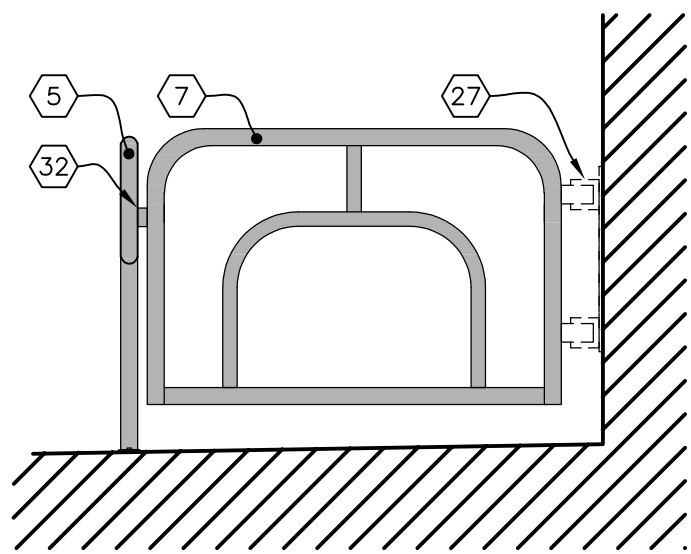


DÉMOLITION PORTILLON

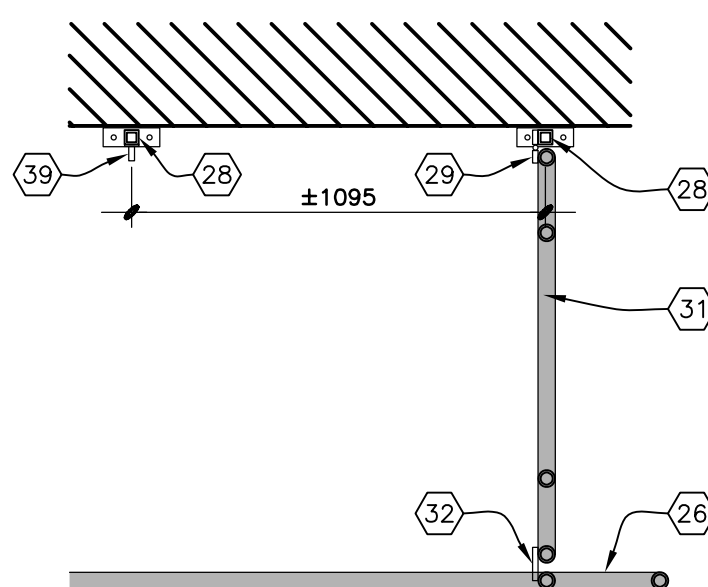


VUE EN PLAN PORTILLON CONSTRUCTION




PHOTOS DE L'EXISTANT

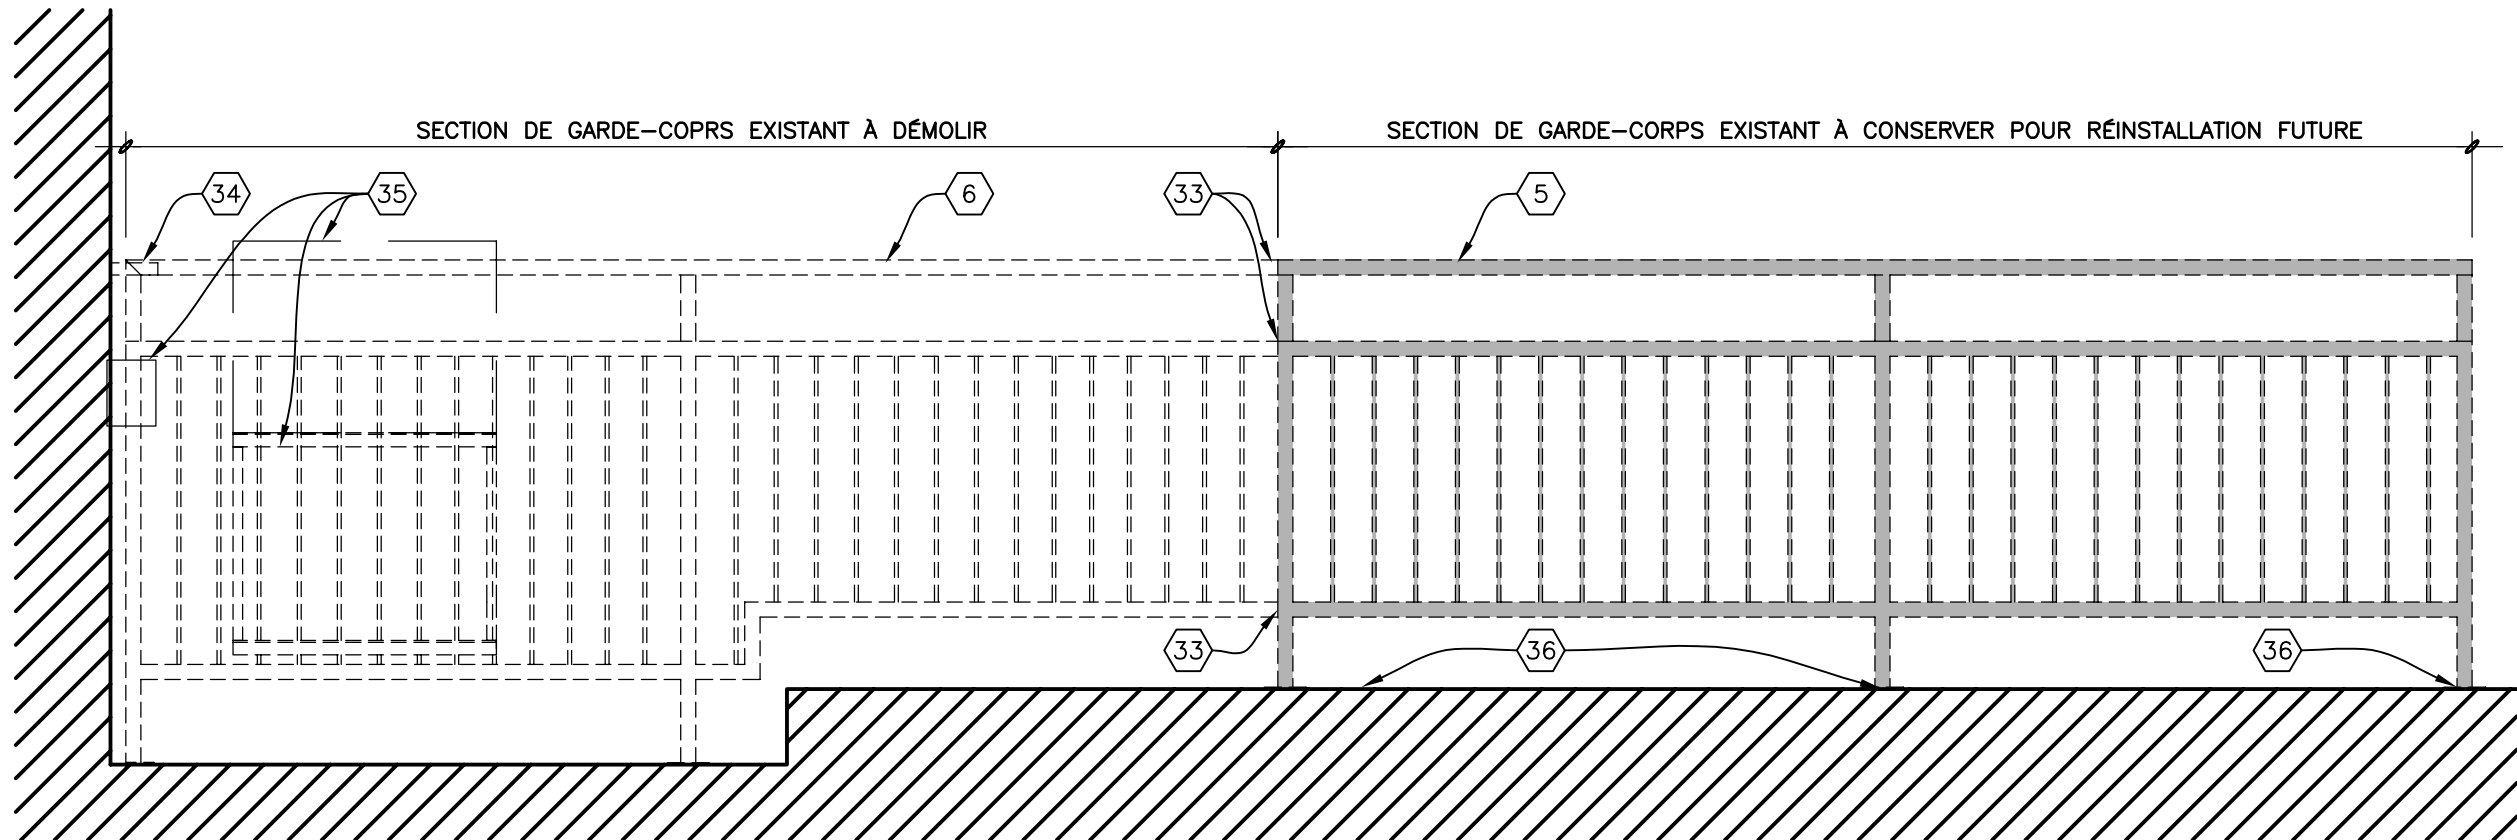

ÉLÉVATION DÉMOLITION

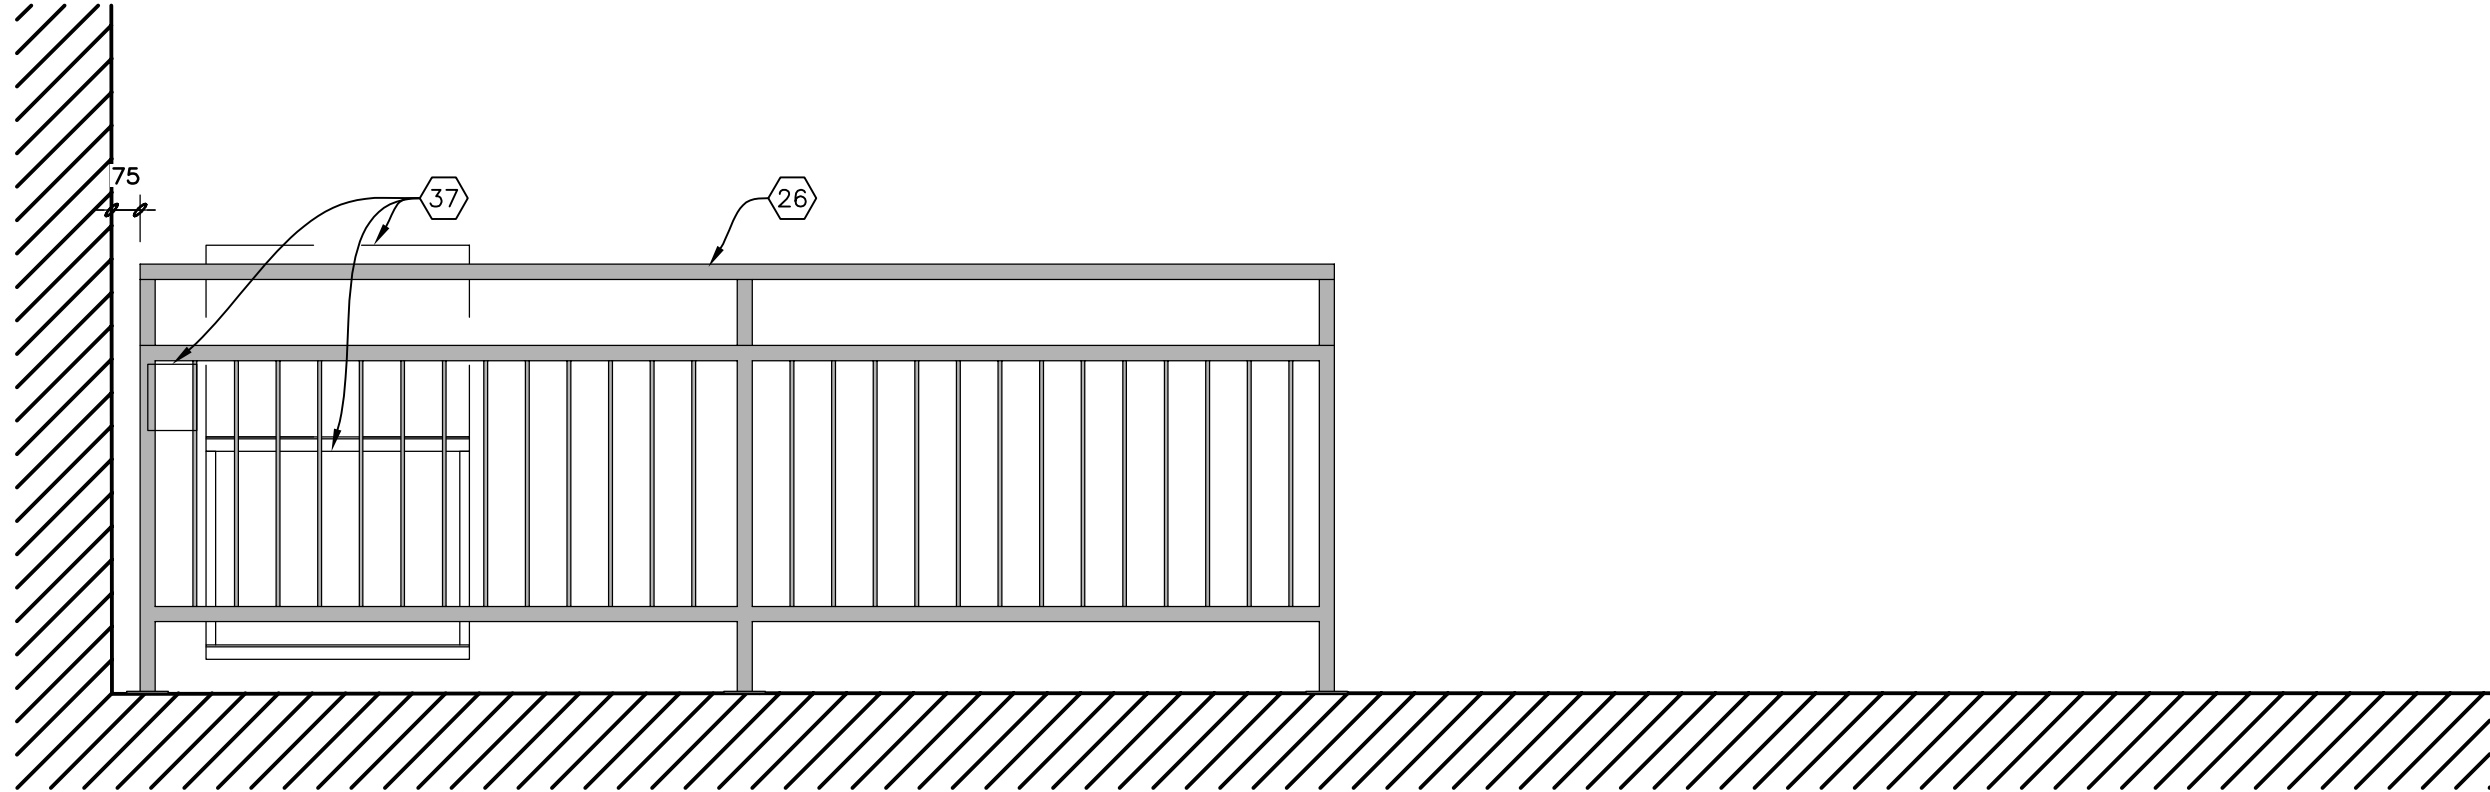

ÉLÉVATION CONSTRUCTION

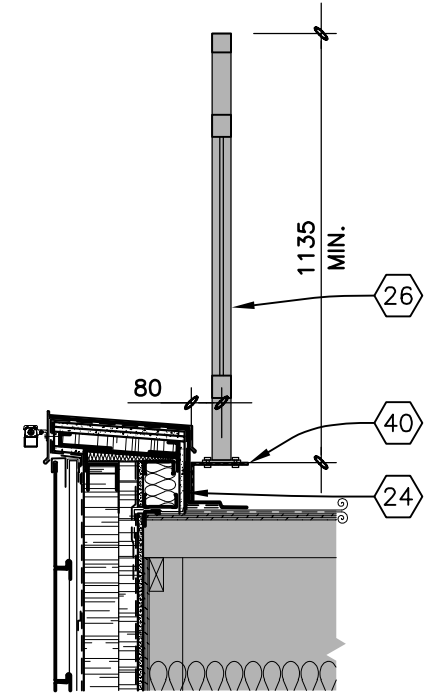

DÉTAIL EN COUPE



NOTES

- 1 L'ÉCHELLE EXISTANTE À DÉMONTÉ ET À PROTÉGER PENDANT LES TRAVAUX POUR RÉINSTALLATION APRÈS MODIFICATION DE L'ÉCHELLE.
- 2 SECTION DES LONGERONS DE L'ÉCHELLE EXISTANTE À COUPER, MEULER LES ARÊTES DE LA COUPE.
- 3 BRACKETTES DE L'ÉCHELLE EXISTANTE À COUPER.
- 4 CONSERVER UNE LONGUEUR DE LONGERON D'AU MOINS 500mm AU-DESSUS DU DERNIER ÉCHELON.
- 5 GARDE-CORPS EXISTANT À DÉMONTÉ ET À PROTÉGER PENDANT LES TRAVAUX POUR RÉINSTALLATION APRÈS MODIFICATION DU GARDE-CORPS.
- 6 SECTION DU GARDE-CORPS EXISTANT À COUPER.
- 7 PORTILLON EXISTANT À DÉMONTÉ ET À PROTÉGER PENDANT LES TRAVAUX POUR RÉINSTALLATION APRÈS LES MODIFICATIONS AU PENTURE.
- 8 L'ÉCHELLE EXISTANTE RÉINSTALLÉE APRÈS LES TRAVAUX DE DÉMONTAGE, LEFÈRE, LES ÉLEVATIONS POUR LOCALISATION EXACTE DE LA RÉINSTALLATION DE L'ÉCHELLE.
- 9 POTEAU ET PLAQUE DE FIXATION EN STRUCTURE D'ACIER, VOIR DOCUMENTS D'INGÉNIEURIE.
- 10 PAIRE DE PLAQUES PLUÉES AJUSTABLES EN ALUMINIUM 75mm DE LARGEUR, 6mm ép. FIXER LA PREMIÈRE PLAQUE PLUÉE À L'ARRIÈRE DES ÉCHELLONS EXISTANTS DE L'ÉCHELLE. FIXER LA DEUXIÈME PLAQUE PLUÉE SUR LA PLAQUE DE FIXATION DE STRUCTURE. INSTALLER UN SÉPARATEUR ÉLECTRIQUE ENTRE LA PLAQUE PLUÉE ET LA PLAQUE DE FIXATION EN ACIER DE STRUCTURE.
- 11 PAIRE DE PLAQUES PLUÉES AJUSTABLES EN ALUMINIUM 75mm DE LARGEUR, 6mm ép. FIXER LA PREMIÈRE PLAQUE PLUÉE À L'ARRIÈRE DES ÉCHELLONS EXISTANTS DE L'ÉCHELLE. FIXER LA DEUXIÈME PLAQUE PLUÉE SUR LA POUTRE DE RIVE EN ACIER. INSTALLER UN BRIS THERMIQUE D'UNE ÉPAISSEUR DE 13mm ENTRE LA PLAQUE PLUÉE ET LA POUTRE EXISTANTE.
- 12 PAIRE DE PLAQUES PLUÉES AJUSTABLES EN ALUMINIUM 75mm DE LARGEUR, 6mm ép. FIXER LA PREMIÈRE PLAQUE SUR LE CÔTÉ EXTÉRIEUR DES ÉCHELLONS EXISTANTS DE L'ÉCHELLE. FIXER LA DEUXIÈME PLAQUE SUR LA POUTRE DE RIVE EN ACIER. INSTALLER UN SÉPARATEUR ÉLECTRIQUE ENTRE LA PLAQUE PLUÉE ET LA PLAQUE DE FIXATION DE STRUCTURE.
- 13 PAIRE DE PLAQUES PLUÉES AJUSTABLES EN ALUMINIUM 75mm DE LARGEUR, 6mm ép. FIXER LA PREMIÈRE PLAQUE SUR LE CÔTÉ EXTÉRIEUR DES ÉCHELLONS EXISTANTS DE L'ÉCHELLE. FIXER LA DEUXIÈME PLAQUE PLUÉE SUR LA POUTRE DE RIVE EN ACIER. INSTALLER UN BRIS THERMIQUE D'UNE ÉPAISSEUR DE 13mm ENTRE LA PLAQUE PLUÉE ET LA POUTRE.
- 14 PALIER EN CALLEBOTS D'ALUMINIUM SUR UNE STRUCTURE EN CORNIÈRES D'ALUMIUM DE 50X50mm, 6mm ép. AVEC CORNIÈRE DE RENFORT À MIS-PORTÉE.
- 15 CORNIÈRE DE RENFORT EN ALUMINIUM 50X50mm, 6mm ép. FIXÉE SUR L'ARRIÈRE DES LONGERONS DE L'ÉCHELLE EXISTANTE ET SUR LES CORNIÈRES DU PALIER.
- 16 FIXER MÉCANIQUEMENT LA STRUCTURE DU PALIER À L'ARRIÈRE DES LONGERONS DE L'ÉCHELLE EXISTANTE.
- 17 CORNIÈRE EN ALUMINIUM DE DIMENSIONS REQUISES POUR FIXATION DU PALIER AU FER "C". INSTALLER UN SÉPARATEUR ÉLECTRIQUE ENTRE LA CORNIÈRE ET LE FER "C".
- 18 FER "C" EN ACIER GALVANISÉ C200X17, INSTALLÉ SUR LE DESSUS DU PARAPET.
- 19 NOUVEAU PARAPET POUR ASSISE DU NOUVEAU PALIER DE L'ÉCHELLE.
- 20 GARDE-CORPS COMPOSÉ DE HSS EN ALUMINIUM DE 38X38mm, 6mm ép. LE GARDE-CORPS DOIT ÊTRE FIXÉ MÉCANIQUEMENT À LA STRUCTURE DU PALIER.
- 21 CORNIÈRE EN ALUMINIUM 50X50mm, 6mm ép. DE SOUTÈNIR LE PARAPET. FIXER MÉCANIQUEMENT SUR LE CÔTÉ EXTÉRIEUR DES LONGERONS DE L'ÉCHELLE EXISTANTE.
- 22 FIXER MÉCANIQUEMENT LA STRUCTURE DU PALIER À L'ARRIÈRE DES NOUVELLES CORNIÈRES INSTALLÉES SUR LE CÔTÉ DES LONGERONS DE L'ÉCHELLE EXISTANTE.
- 23 CORNIÈRE DE RENFORT EN ALUMINIUM 50X50mm, 6mm ép. FIXÉE SUR L'ARRIÈRE DES NOUVELLES CORNIÈRES INSTALLÉES SUR LE CÔTÉ DES LONGERONS DE L'ÉCHELLE EXISTANTE, ET SUR LES CORNIÈRES DU PALIER.
- 24 TÔLE EN ACIER GALVANISÉ 1,994mm ép. INSTALLÉE EN SOUTÈNIR LE PARAPET. FIXER MÉCANIQUEMENT LES NOUVELLES MEMBRANES DU PARAPET.
- 25 CORNIÈRE EN ALUMINIUM CONTINUE 150X100mm, 9mm ép. FIXÉE DANS LA NOUVELLE TÔLE DANS LE PARAPET.
- 26 GARDE-CORPS EXISTANT REINSTALLÉ.
- 27 COUPER LES CHARNIÈRES DU PORTION EXISTANT ET RETENIR LA PLAQUE MURALE.
- 28 POTEAU EN ACIER GALVANISÉ 38X38mm AVEC PLAQUE DE FIXATION AU SOL. UTILISER DES ANCRAGES POUR FOURRIR LA POUTRE EN POTEAU DANS LA DALLE DE BÉTON EXISTANTE.
- 29 INSTALLER DE NOUVELLES CHARNIÈRES SUR LE PORTION EXISTANT ET LE NOUVEAU POTEAU EN ACIER.
- 30 SYSTÈME ANTI-CHÛTE POUR ÉCHELLE.
- 31 PORTILLON EXISTANT RÉINSTALLÉ.
- 32 SYSTÈME DE LOQUET EXISTANT CONSERVÉ.
- 33 MEULER LES SURFACES DU GARDE-CORPS QUI ONT ÉTÉ COUPÉ ET FAIRE DES RETOUCHES DE GALVANISATION À FROID AVANT LA RÉINSTALLATION DU GARDE-CORPS.
- 34 BRACKETTE DE FIXATION EN ACIER EXISTANTE À DÉMÔLER.
- 35 UNITÉ DE MÉCANIQUE ET SON SUPPORT EXISTANTS À DÉMÔLER TEMPORAIREMENT, VOIR DOCUMENTS D'INGÉNIEURIE.
- 36 DÉMÔLER LE BOUCHER DE FAÇON ÉTANCHE TOUS LES PERCEMENTS DU SYSTÈME DE TOITURE EXISTANT APRÈS LE RETRAIT DU GARDE-CORPS.
- 37 UNITÉ DE MÉCANIQUE ET SON SUPPORT EXISTANTS RÉINSTALLÉS, VOIR DOCUMENTS D'INGÉNIEURIE.
- 38 RETENUE DE PORTE EXISTANTE À DÉMÔLER ET ENTREPOSER PENDANT LES TRAVAUX POUR RÉINSTALLATION FUTURE.
- 39 RETENUE DE PORTE EXISTANTE RÉINSTALLÉE SUR LE NOUVEAU POTEAU.
- 40 CORNIÈRE EN ACIER GALVANISÉ CONTINUE 150X100mm, 9mm ép. FIXÉE DANS LA NOUVELLE TÔLE DANS LE PARAPET.

NE DOIT PAS SERVIR À L'EXÉCUTION

Le présent document est émis pour la seule fin identifiée. Son contenu est protégé par les droits d'auteur et toute reproduction ou modification, partielle ou totale, est interdite sans l'autorisation écrite de gagnon, letellier, cyr, ricard, mathieu, proulx, savard consortium d'architectes.

GLCRM:
128, Avenue de la Cathédrale,
Bureau 201
Rimouski, QC, G5L 5H7
(418) 722-7655



2406, Ch. des Quatres-Bourgeois,
Bureau 100
Québec, QC, G1V 1W5
(418) 647-1700

Proulx Savard Architectes:
75, boul. Arthur-Buies Ouest,
Rimouski QC G5L 5C2
(418) 722 5542

ARCHITECTURE



CONSULTANTS

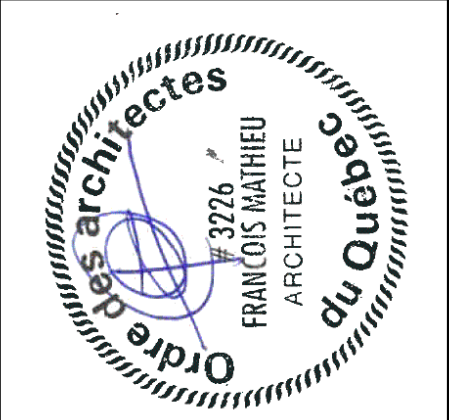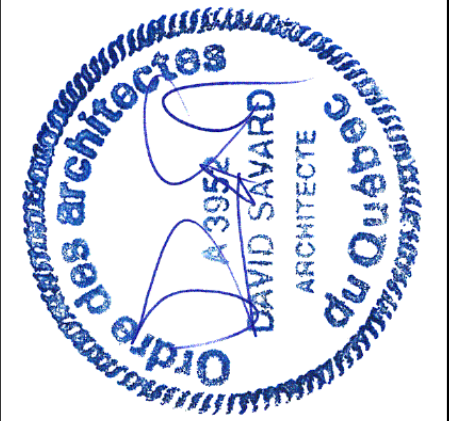

DESINATEUR (S)	J.L.	ÉCHELLE INDIQUÉE	DATE INDIQUÉE	DOSSIER No. 24-108 / R657-24	SEPTEMBRE 2026				
	05		2024-09-04		DÉFINITIFS POUR SOUMISSION				
	04		2024-08-21		DÉFINITIFS 100% POUR APPROBATION				
	03		2024-08-03		DÉFINITIFS 80% POUR APPROBATION				
	02		2024-05-14		DÉFINITIFS 60% POUR APPROBATION				
	01		2024-02-27		PRÉLIMINAIRES 30% POUR APPROBATION				
No			DATE		RÉVISIONS				


PROJET
HÔPITAL DE CHANDLER,
DÉMOLITION ET CONSTRUCTION
Région de l'enveloppe

PROPRIÉTAIRE

 Santé
Québec




PHOTO DE L'EXISTANT

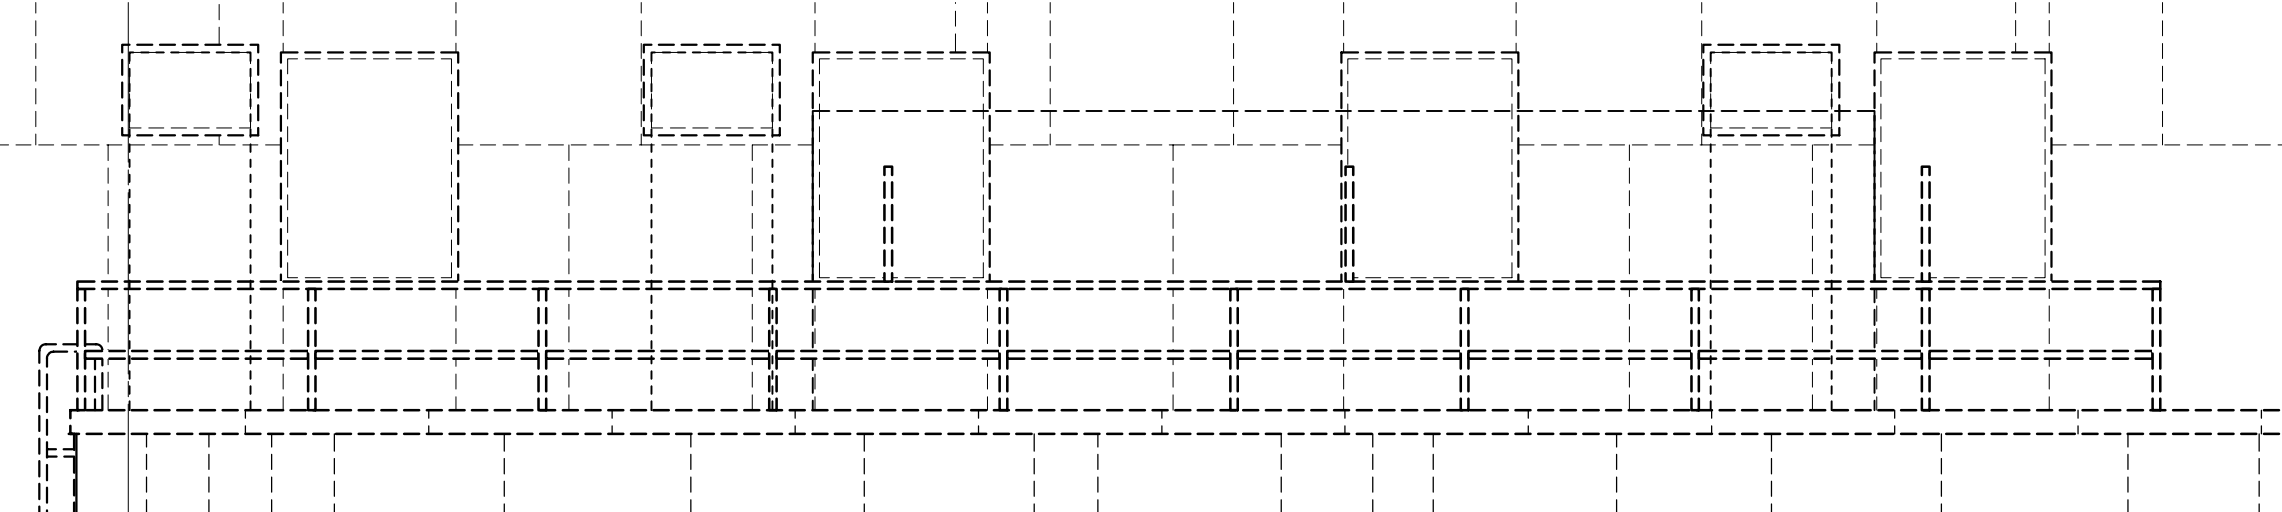


ÉLEVATION NORD DÉMOLITION

1:50

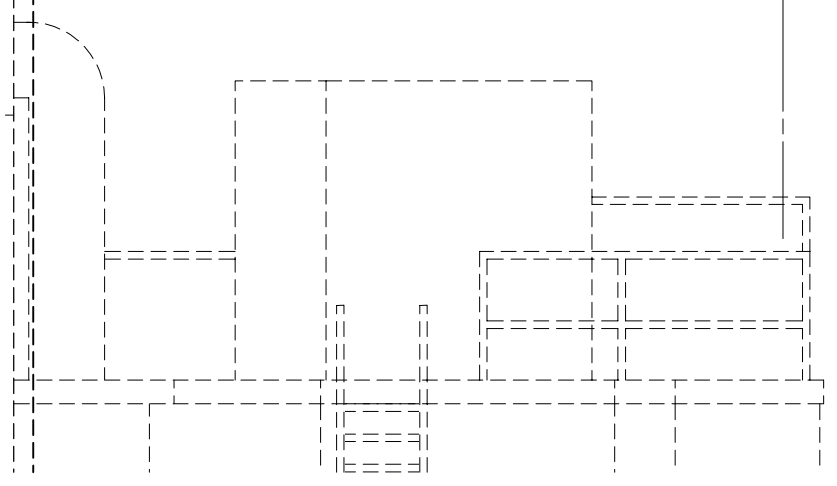

ÉLEVATION EST DÉMOLITION

1:50

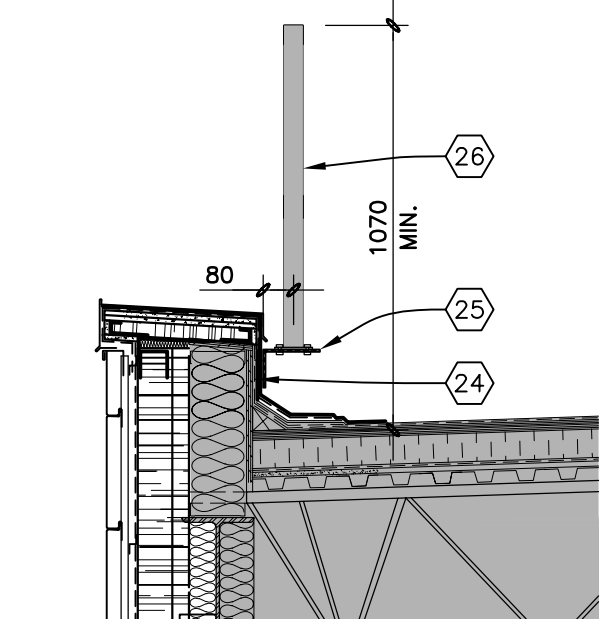


COUPE CONSTRUCTION


7
201,203 704

GARDE-CORPS G-03


1:20mm

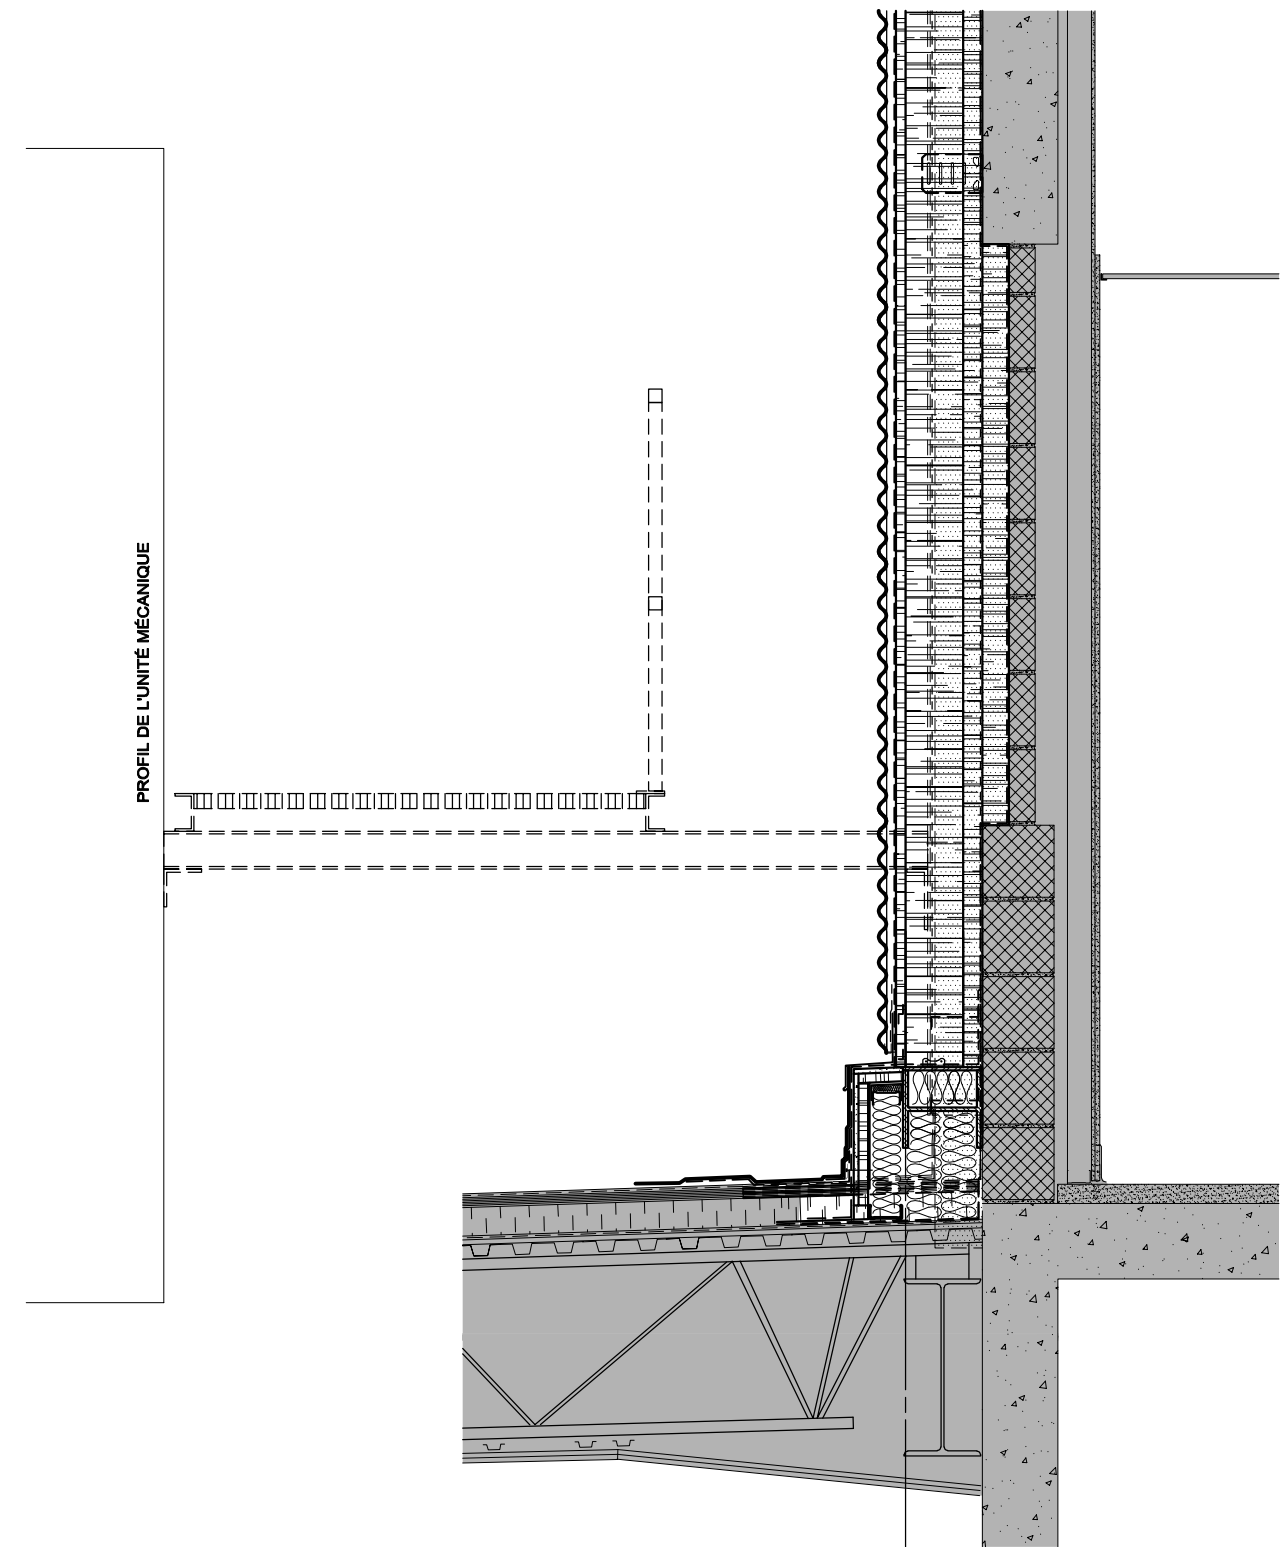


DÉMOLITION

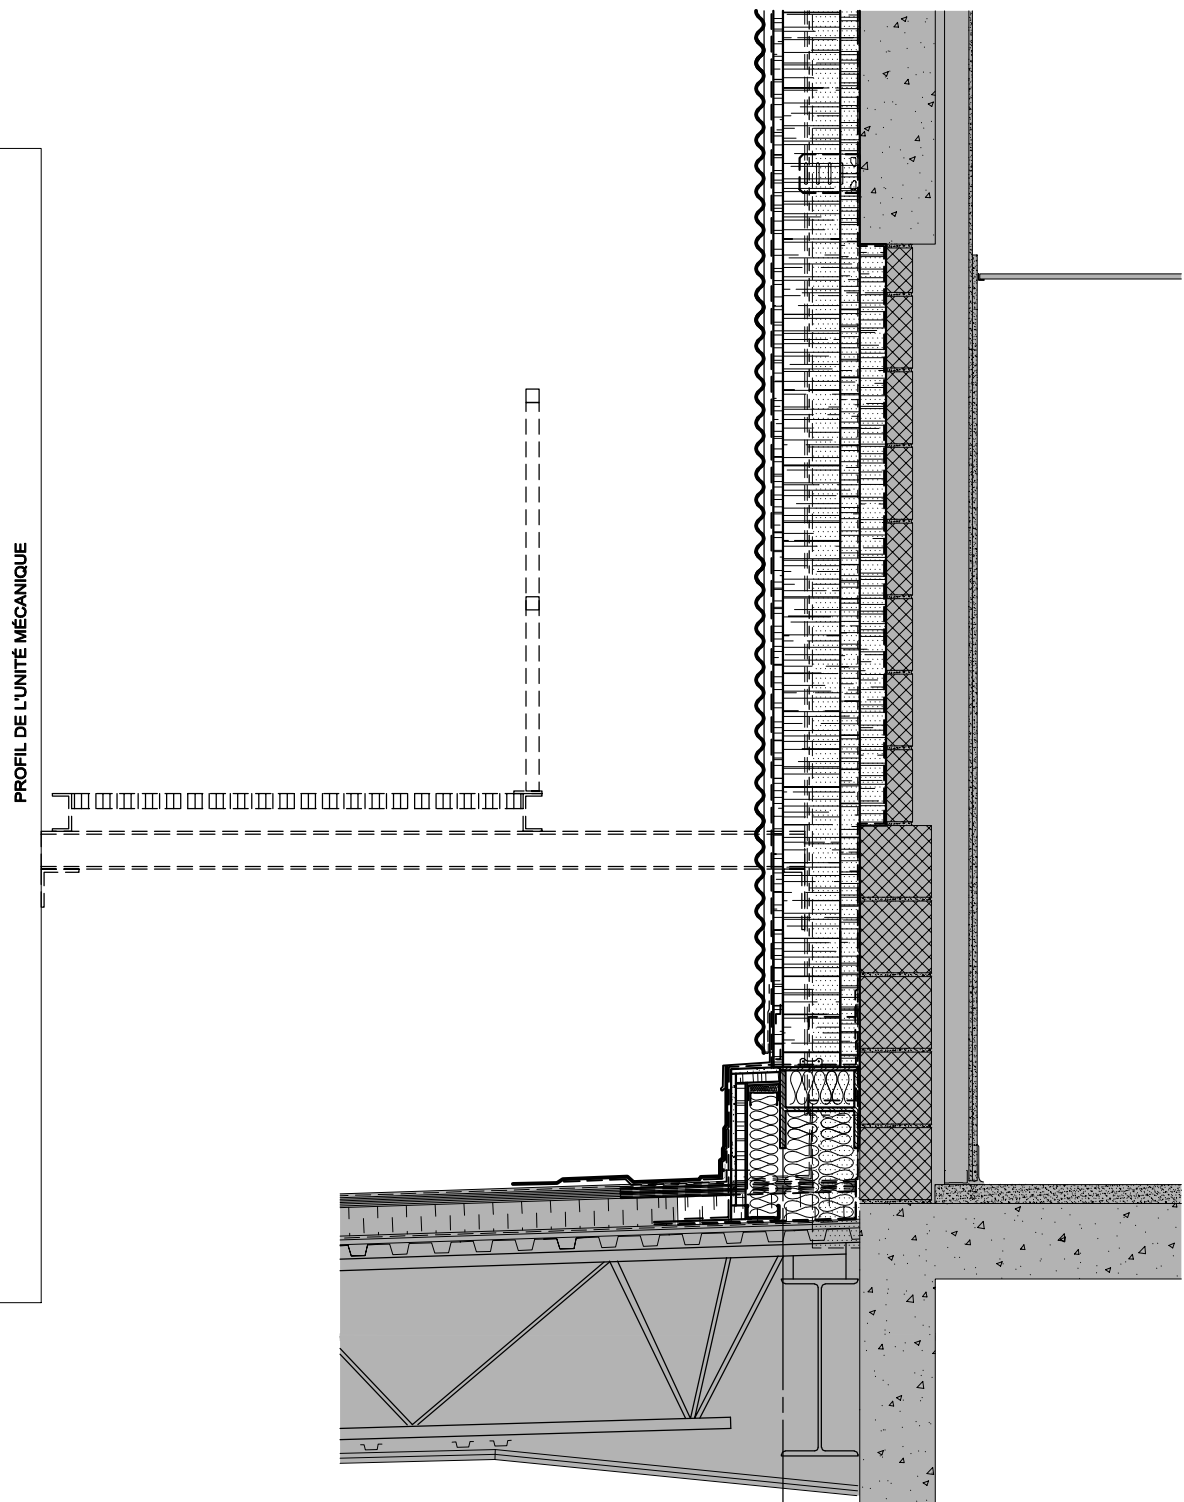

CONSTRUCTION

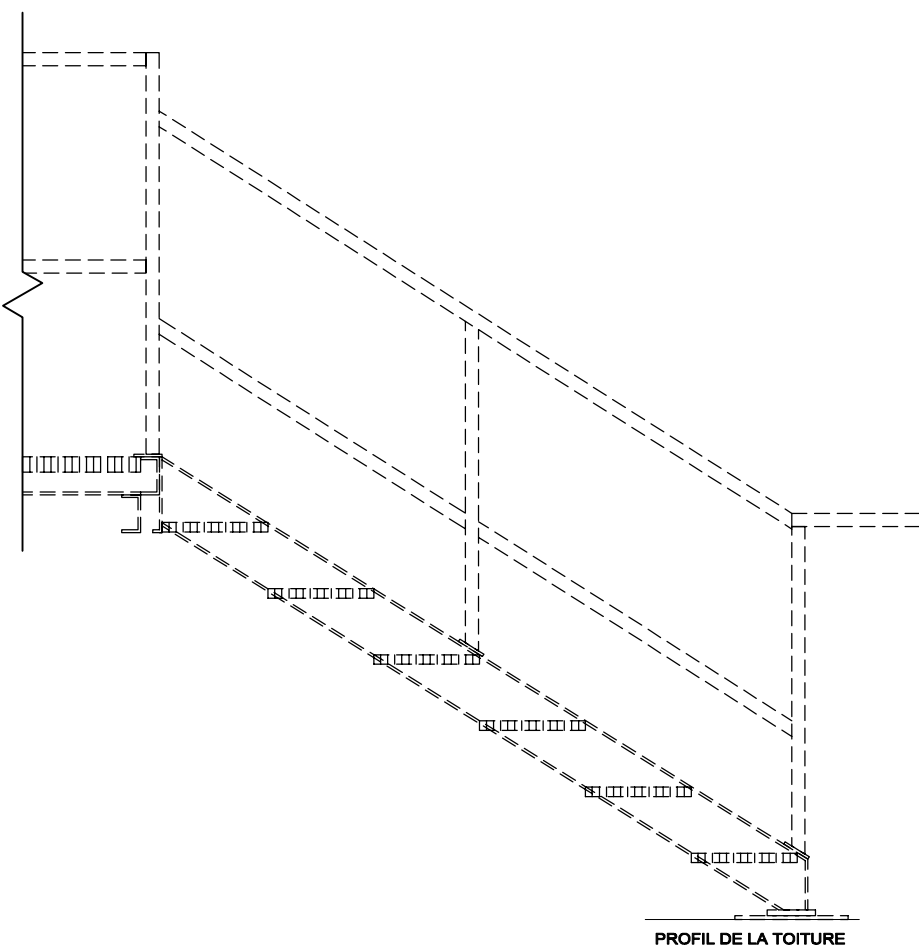

DÉMOLITION

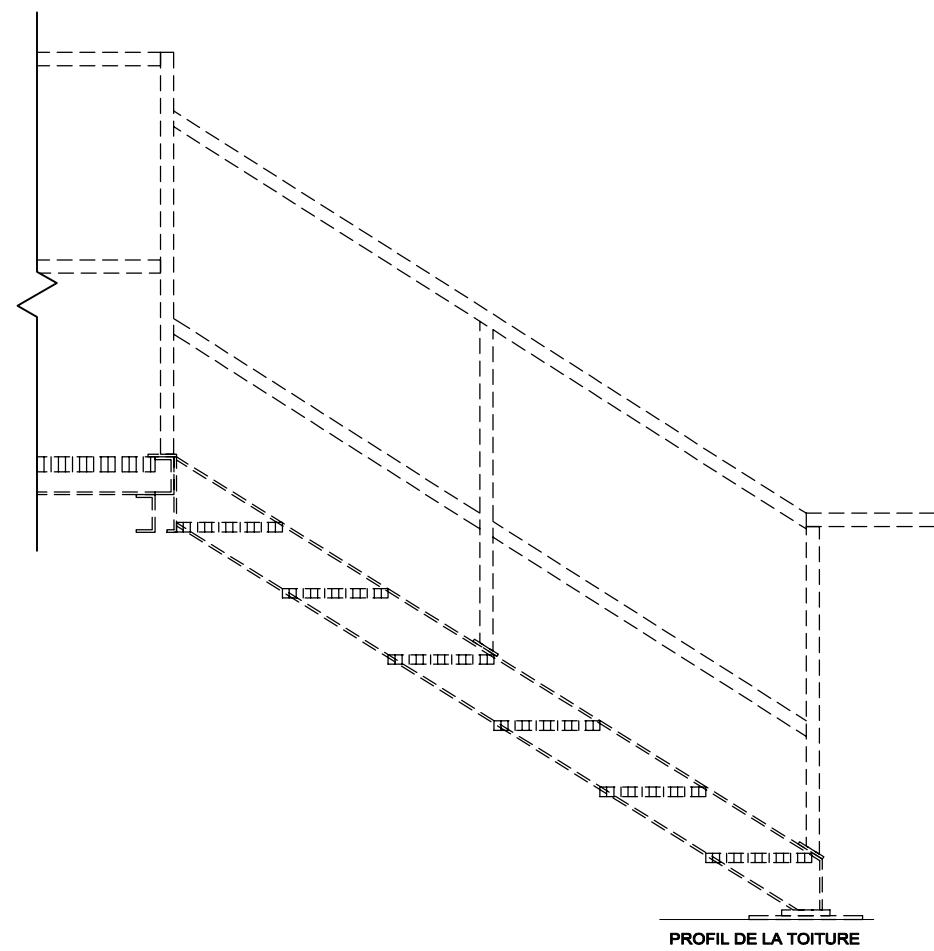

CONSTRUCTION

8
201,203 704

ESCALIER ET PASSERELLE TECHNIQUE P-01

1:20mm

NOTES

- ÉCHELLE EXISTANTE À DÉMONTER ET À PROTÉGER PENDANT LES TRAVAUX POUR RÉINSTALLATION APRÈS MODIFICATION DE L'ÉCHELLE.
- SECTION DES LONGERONS DE L'ÉCHELLE EXISTANTE À COUPER. MEULER LES ARRÊTES DE LA COUPE.
- BRAQUETTES DE L'ÉCHELLE EXISTANTE À COUPER.
- CONSERVER UNE LONGUEUR DE LONGERON D'AU MOINS 300mm AU-DESSUS DU DERNIER ÉCHELON.
- GARDE-CORPS EXISTANT À DÉMONTER ET À PROTÉGER PENDANT LES TRAVAUX POUR RÉINSTALLATION APRÈS LES MODIFICATIONS AU PENTE.
- SECTION DU GARDE-CORPS EXISTANT À COUPER.
- PORTILLON EXISTANT À DÉMONTER ET À PROTÉGER PENDANT LES TRAVAUX POUR RÉINSTALLATION APRÈS LES MODIFICATIONS AU PENTE.
- ÉCHELLE EXISTANTE RÉINSTALLÉE APRÈS LES TRAVAUX D'AJUSTEMENT DE L'ÉCHELLE, VOIR ÉLEVATIONS POUR LOCALISATION EXACTE DE RÉINSTALLATION DE L'ÉCHELLE.
- POTEAUX ET PLAQUE DE FIXATION EN STRUCTURE D'ACIER, VOIR DOCUMENTS D'INGÉNIERIE.
- PAIRE DE PLAQUES PUIÉES AJUSTABLES EN ALUMINIUM 75mm DE LARGEUR, 6mm ép. FIXER LA PREMIÈRE PLAQUE PUIÉE À L'ARRIÈRE DES ÉCHELLONS EXISTANTS DE L'ÉCHELLE. FIXER LA DEUXIÈME PLAQUE PUIÉE SUR LA PLAQUE DE FIXATION DE STRUCTURE. INSTALLER UN SÉPARATEUR DIELECTRIQUE ENTRE LA PLAQUE PUIÉE ET LA PLAQUE DE FIXATION EN ACIER DE STRUCTURE.
- PAIRE DE PLAQUES PUIÉES AJUSTABLES EN ALUMINIUM 75mm DE LARGEUR, 6mm ép. FIXER LA PREMIÈRE PLAQUE PUIÉE À L'ARRIÈRE DES ÉCHELLONS EXISTANTS DE L'ÉCHELLE. FIXER LA DEUXIÈME PLAQUE PUIÉE SUR LA POUTRE DE RIVE EN ACIER. INSTALLER UN BRIS THERMIQUE D'UNE ÉPAISSEUR DE 13mm ENTRE LA PLAQUE PUIÉE ET LA POUTRE EXISTANTE.
- PAIRE DE PLAQUES PUIÉES AJUSTABLES EN ALUMINIUM 75mm DE LARGEUR, 6mm ép. FIXER LA PREMIÈRE PLAQUE SUR LE CÔTÉ EXTÉRIEUR DES ÉCHELLONS EXISTANTS DE L'ÉCHELLE. FIXER LA DEUXIÈME PLAQUE PUIÉE SUR LA PLAQUE DE FIXATION DE STRUCTURE. INSTALLER UN SÉPARATEUR DIELECTRIQUE ENTRE LA PLAQUE PUIÉE ET LA PLAQUE DE FIXATION DE STRUCTURE.
- PAIRE DE PLAQUES PUIÉES AJUSTABLES EN ALUMINIUM 75mm DE LARGEUR, 6mm ép. FIXER LA PREMIÈRE PLAQUE SUR LE CÔTÉ EXTÉRIEUR DES ÉCHELLONS EXISTANTS DE L'ÉCHELLE. FIXER LA DEUXIÈME PLAQUE PUIÉE SUR LA POUTRE DE RIVE EN ACIER. INSTALLER UN BRIS THERMIQUE D'UNE ÉPAISSEUR DE 13mm ENTRE LA PLAQUE PUIÉE ET LA POUTRE.
- PALIER EN CAILLEBOTIS D'ALUMINIUM SUR UNE STRUCTURE EN CORNIÈRES D'ALUMINIUM DE 50X50mm, 6mm ép. AVEC CORNIÈRE DE RENFORT À MIS-PORTÉE.
- CORNIÈRE DE RENFORT EN ALUMINIUM 50X50mm, 6mm ép. FIXÉE SUR L'ARRIÈRE DES LONGERONS DE L'ÉCHELLE EXISTANTE ET SUR LES CORNIÈRES DU PALIER.
- FIXER MÉCANIQUEMENT LA STRUCTURE DU PALIER À L'ARRIÈRE DES LONGERONS DE L'ÉCHELLE EXISTANTE.
- CORNIÈRE EN ALUMINIUM DE DIMENSIONS REQUISES POUR FIXATION DU PALIER AU FER "C". INSTALLER UN SÉPARATEUR DIELECTRIQUE ENTRE LA CORNIÈRE ET LE FER "C".
- FER "C" EN ACIER GALVANISÉ C200X17, INSTALLÉ SUR LE DESSUS DU PARAPET.
- NOUVEAU PARAPET POUR ASSISSE DU NOUVEAU PALIER DE L'ÉCHELLE.
- GARDE-CORPS COMPOSÉ DE HSS EN ALUMINIUM DE 38X38mm, 6mm ép. LE GARDE-CORPS DOIT ÊTRE FIXÉ MÉCANIQUEMENT À LA STRUCTURE DU PALIER.
- CORNIÈRE EN ALUMINIUM 50X50mm, 6mm ép. DE 200mm DE LONGUEUR, FIXÉE MÉCANIQUEMENT SUR LE CÔTÉ EXTÉRIEUR DES LONGERONS DE L'ÉCHELLE EXISTANTE.
- FIXER MÉCANIQUEMENT LA STRUCTURE DU PALIER À L'ARRIÈRE DES NOUVELLES CORNIÈRES INSTALLÉES SUR LE CÔTÉ DES LONGERONS DE L'ÉCHELLE EXISTANTE.
- CORNIÈRE DE RENFORT EN ALUMINIUM 50X50mm, 6mm ép. FIXÉE SUR L'ARRIÈRE DES NOUVELLES CORNIÈRES INSTALLÉES SUR LE CÔTÉ DES LONGERONS DE L'ÉCHELLE EXISTANTE. ET SUR LES CORNIÈRES DU PALIER.
- TÔLE EN ACIER GALVANISÉ 1,994mm ép. INSTALLÉE EN SURFACE DU PARAPET AVANT L'INSTALLATION DES NOUVELLES MEMBRANES DU PARAPET.
- CORNIÈRE EN ALUMINIUM CONTINUE 150X100mm, 9mm ép. FIXÉE DANS LA NOUVELLE TÔLE DANS LE PARAPET.
- GARDE-CORPS EXISTANT RÉINSTALLÉ.
- COUPER LES CHARNIÈRES DU PORTION EXISTANT ET RETIRER LA PLAQUE MURALE.
- POTEAUX EN ACIER GALVANISÉ 38X38mm AVEC PLAQUE DE FIXATION AU SOL UTILISER DES ANCRAGES CHIMIQUES POUR LA FIXATION DU POTEAU DANS LA DALLE DE BÉTON EXISTANTE.
- INSTALLER DE NOUVELLES CHARNIÈRES SUR LE PORTION EXISTANT ET LE NOUVEAU POTEAU EN ACIER.
- SYSTÈME ANTI-CHUTE POUR ÉCHELLE.
- PORTILLON EXISTANT RÉINSTALLÉ.
- SYSTÈME DE LOQUET EXISTANT CONSERVÉ.
- MEULER LES SURFACES DU GARDE-CORPS QUI ONT ÉTÉ COUPER ET FAIRE DES RETOUCHES DE GALVANISATION À FROID AVANT LA RÉINSTALLATION DU GARDE-CORPS.
- BRAQUETTE DE FIXATION EN ACIER EXISTANTE À DÉMOLIR.
- UNITÉ DE MÉCANIQUE ET SON SUPPORT EXISTANTS À DÉMONTÉLER TEMPORAIREMENT, VOIR DOCUMENTS D'INGÉNIERIE.
- PRÉVOIR DE BOUCHER DE FAÇON ÉTANCHE TOUS LES PERCEMENTS DU SYSTÈME DE TOITURE EXISTANT APRÈS LE RETRAIT DU GARDE-CORPS.
- UNITÉ DE MÉCANIQUE ET SON SUPPORT EXISTANTS RÉINSTALLÉS, VOIR DOCUMENTS D'INGÉNIERIE.
- RETENUE DE PORTE EXISTANTE À DÉMONTÉLER ET ENTREPOSER PENDANT LES TRAVAUX POUR RÉINSTALLATION FUTURE.
- RETENUE DE PORTE EXISTANTE RÉINSTALLÉE SUR LE NOUVEAU POTEAU.
- CORNIÈRE EN ACIER GALVANISÉ CONTINUE 150X100mm, 9mm ép. FIXÉE DANS LA NOUVELLE TÔLE DANS LE PARAPET.

NE DOIT PAS SERVIR À L'EXÉCUTION

Le présent document est émis pour la seule fin identifiée. Son contenu est protégé par les droits d'auteur et toute reproduction ou modification, partielle ou totale, est interdite sans l'autorisation écrite de gagnon, letellier, cyr, ricard, mathieu, proulx, savard consortium d'architectes.




GLCRM | Proulx Savard |

GLCRM:
128, Avenue de la Cathédrale,
Bureau 201
Rimouski, QC, G5L 5H7
(418) 722-7655

2406, Ch. des Quatre-Bourgeois,
Bureau 100
Québec, QC G1V 1W5
(418) 647-1700

Proulx Savard Architectes:
75, boul. Arthur-Buies Ouest,
Rimouski QC G5L 5C2
(418) 723-5543

ARCHITECTURE

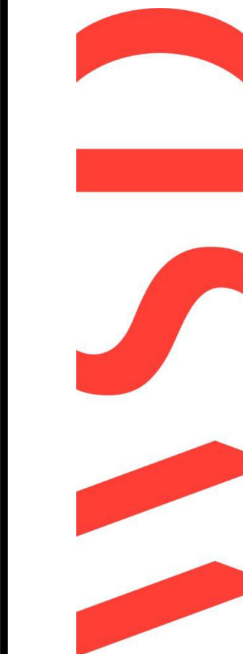

CONSULTANTS



DOSSIER N°:	DATE	DATE	DATE	DATE	DATE
24-107 / 1657-24	2024-09-04	2024-08-21	2024-08-03	2024-05-14	2024-02-27
DESSINATEUR (S)	J.L.	ÉCHELLE	INDIQUÉE	DATE	REVISIONS
					No

DESSIN	PROJET	PROPRIÉTAIRE
METALL-OUVRÉS DÉMOLITION ET CONSTRUCTION	HÔPITAL DE CHANDLER, Chandler (Réfection de l'enveloppe)	Santé Québec

704



- 1 PIEUX VISÉ, VOIR DOCUMENTS D'INGÉNIERIE.
- 2 DALLE DE BÉTON SUR SOL, VOIR DOCUMENTS D'INGÉNIERIE.
- 3 POTEAUX HSS EN ACIER GALVANISÉ 76x76mm de 6.4mm d'ÉPAISSEUR AVEC CONTREVENTEMENT EN «X» CORRÉLÉ À LA COURBURE EN ACIER GALVANISÉ 52x52mm de 6.4mm d'ÉPAISSEUR.
- 4 LIMON EN ACIER GALVANISÉ C310x31 CONTINU ENTRE LA VOLÉE ET LE PALIER AU-DESSUS.
- 5 MARCHÉ PRÉFABRIQUÉ EN ACIER GALVANISÉ DE TYPE SAFETY TREAD (AMICO).
- 6 CONTRAMARCHÉ EN PLAQUE D'ACIER GALVANISÉ PLIÉE 2mm d'ÉPAISSEUR, FIXÉE MÉCANIQUEMENT AUX MARCHES.
- 7 PALIER COMPOSÉ DE PLANCHES PRÉFABRIQUÉES EN ACIER GALVANISÉ DE TYPE SAFETY TREAD (AMICO).
- 8 TRAVERSE EN ACIER GALVANISÉ C200x17.
- 9 CONTREVENTEMENT HORIZONTAL ENTRE LES LIMONS, COMPOSÉ DE CORNIÈRES 52x52mm DE 6.4mm d'ÉPAISSEUR.
- 10 GARDE-CORPS EN ACIER GALVANISÉ, VOIR DÉTAIL 9B.
- 11 MAIN-COURANTE EN ACIER GALVANISÉ EN PROFIL HSR 32mm², CONTINUE SUR TOUTE LA LONGUEUR DE L'ESCALIER. POURSUIVRE HORIZONTALEMENT LA MAIN-COURANTE AU BAS ET AU HAUT DES VOLÉES.
- 12 POUTRE SUR LAQUELLE LES MAINS-COURANTES, VOIR PROFILS EN PLAN, FIXATION DE LA MAIN-COURANTE SUR LES POTEAUX VERTICAUX DU GARDE-CORPS À L'AIDE DE TIGES PLIÉES EN ACIER GALVANISÉ 10mm d'ÉPAISSEUR.
- 13 MEMBRURE HORIZONTALE EN ACIER GALVANISÉ EN PROFIL HSS 38x38mm.
- 14 POTEAUX VERTICAUX EN ACIER GALVANISÉ EN PROFIL HSS 38x38mm. POUR FIXER UN POTEAU À CHAQUE EXTREMITÉ DU GARDE-CORPS ET À CHAQUE CHANGEMENT D'INCLINAISON, INSTALLER LES POTEAUX À DES DISTANCES C/C ÉGALES, SANS ÊTRE SUPÉRIEUR À 1220mm SUR UNE MÊME VOLÉE D'ESCALIER.
- 15 BARROTINS VERTICAUX EN TIGE CARRÉE D'ACIER GALVANISÉ DE 10x100mm. INSTALLER LES BARROTINS À DES DISTANCES C/C ÉGALES SUR UNE MÊME VOLÉE D'ESCALIER SANS QUE L'ESPACE LIBRE ENTRE CEUX-CI NE SOIT ÉGAL OU SUPÉRIEUR À 100mm.
- 16 PALIER EN ACIER GALVANISÉ DE 38x38mm, 4.8mm d'ÉPAISSEUR SOUDÉE AU LIMON, POUR FIXATION DES MARCHES OU DES PLANCHES DES PALIERS.
- 17 CORNIÈRE EN ACIER GALVANISÉ DE 76x75mm, 6mm d'ÉPAISSEUR, 1500mm DE LONGUEUR, SOUDÉE AU LIMON, POUR FIXATION MÉCANIQUE DES LIMONS AUX PLAQUES DE TÊTE DES PIEUX VISÉS.
- 18 CORNIÈRE EN ACIER GALVANISÉ DE 76x75mm, 6mm d'ÉPAISSEUR, 1500mm DE LONGUEUR, SOUDÉE AU LIMON, POUR FIXATION MÉCANIQUE DES LIMONS.
- 19 PLAQUE EN ACIER GALVANISÉ 150x100mm, 6mm d'ÉPAISSEUR SOUDÉE À LA TÊTE DES POTEAUX POUR FIXATION MÉCANIQUE DES LIMONS.
- 20 PLAQUE EN ACIER GALVANISÉ 150x150mm, 6mm d'ÉPAISSEUR SOUDÉE À LA BASE DES POTEAUX POUR FIXATION MÉCANIQUE DES POTEAUX AUX PIEUX VISÉS.

705

Le présent document est émis pour la seule fin identifiée. Son contenu est protégé par les droits d'auteur et toute reproduction ou modification, partielle ou totale, est interdite sans l'autorisation écrite de gagnon, letellier, cyr, ricard, mathieu, proulx, savard consortium d'architectes.

705