



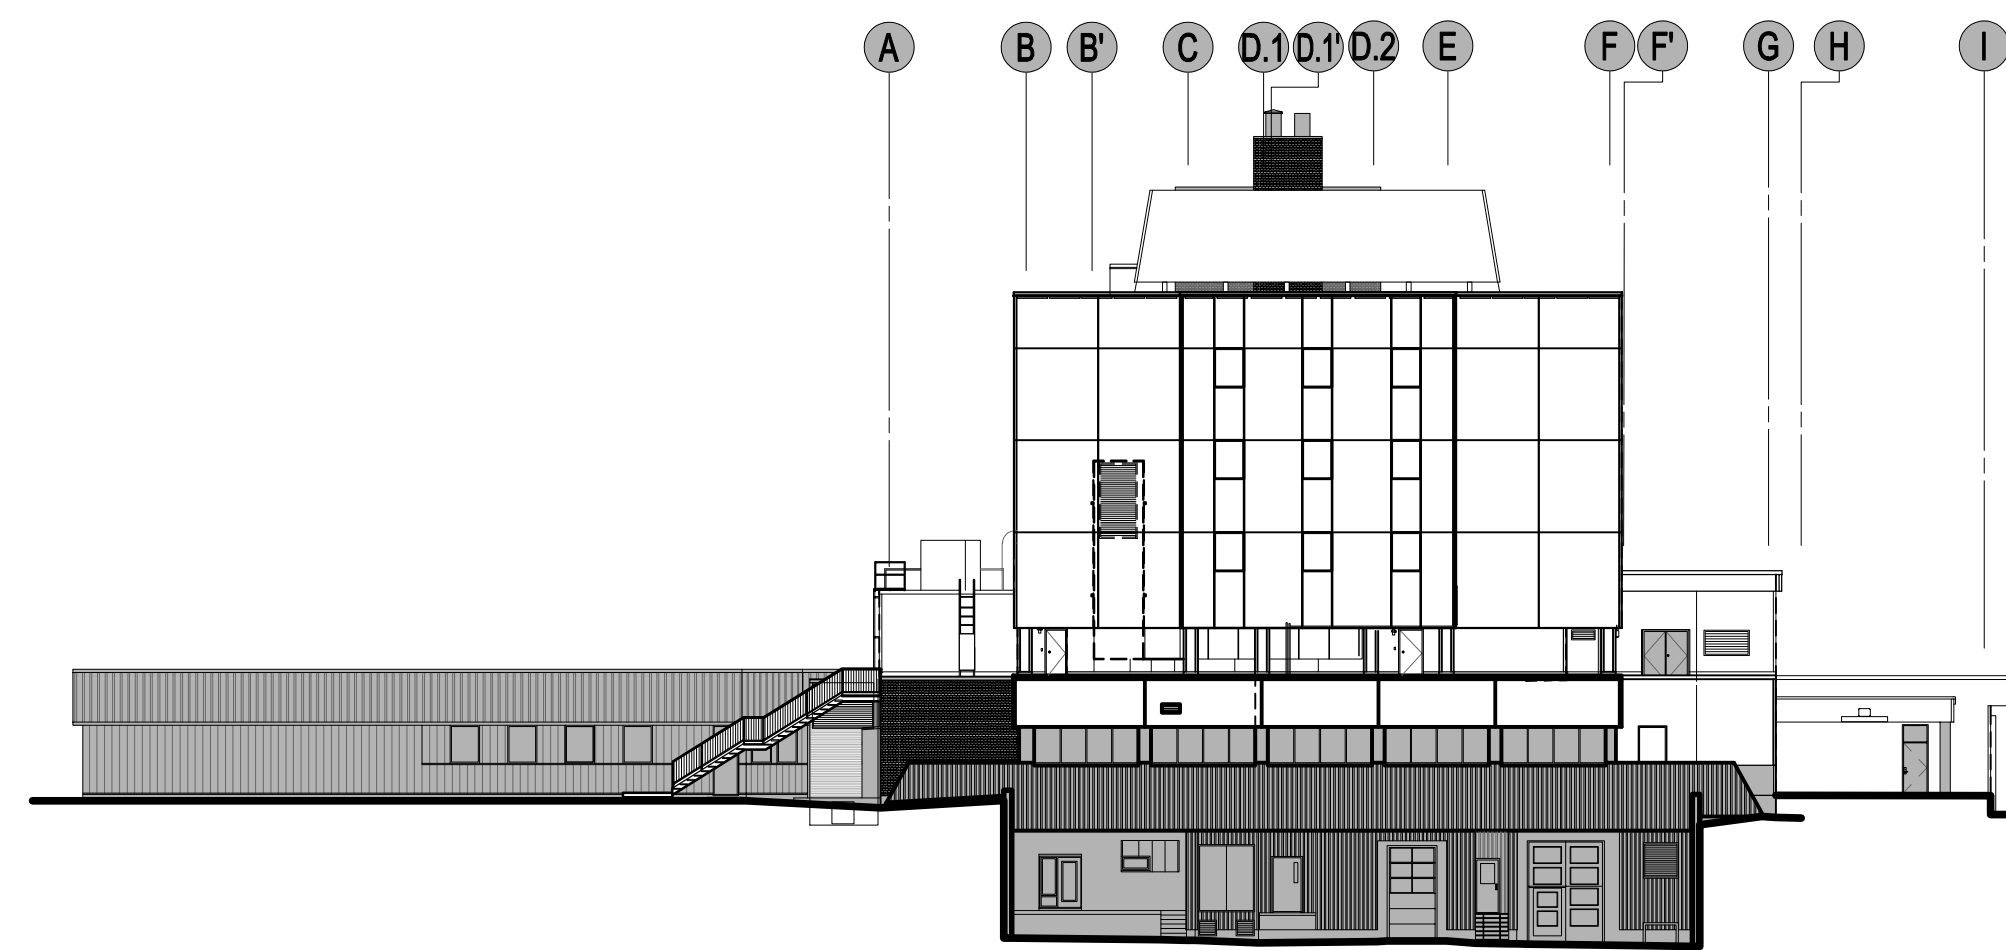



B ÉLÉVATION OUEST
1:300mm



A detailed architectural section drawing of the building, showing the internal structure and levels. The drawing is oriented horizontally, with the ground level at the bottom. The building has a complex, multi-level design. The section shows the internal walls, floors, and roof structure. The levels are labeled D.2, E, F, and G, with vertical lines indicating their positions. The drawing is a black and white line drawing, showing the internal structure and levels of the building.

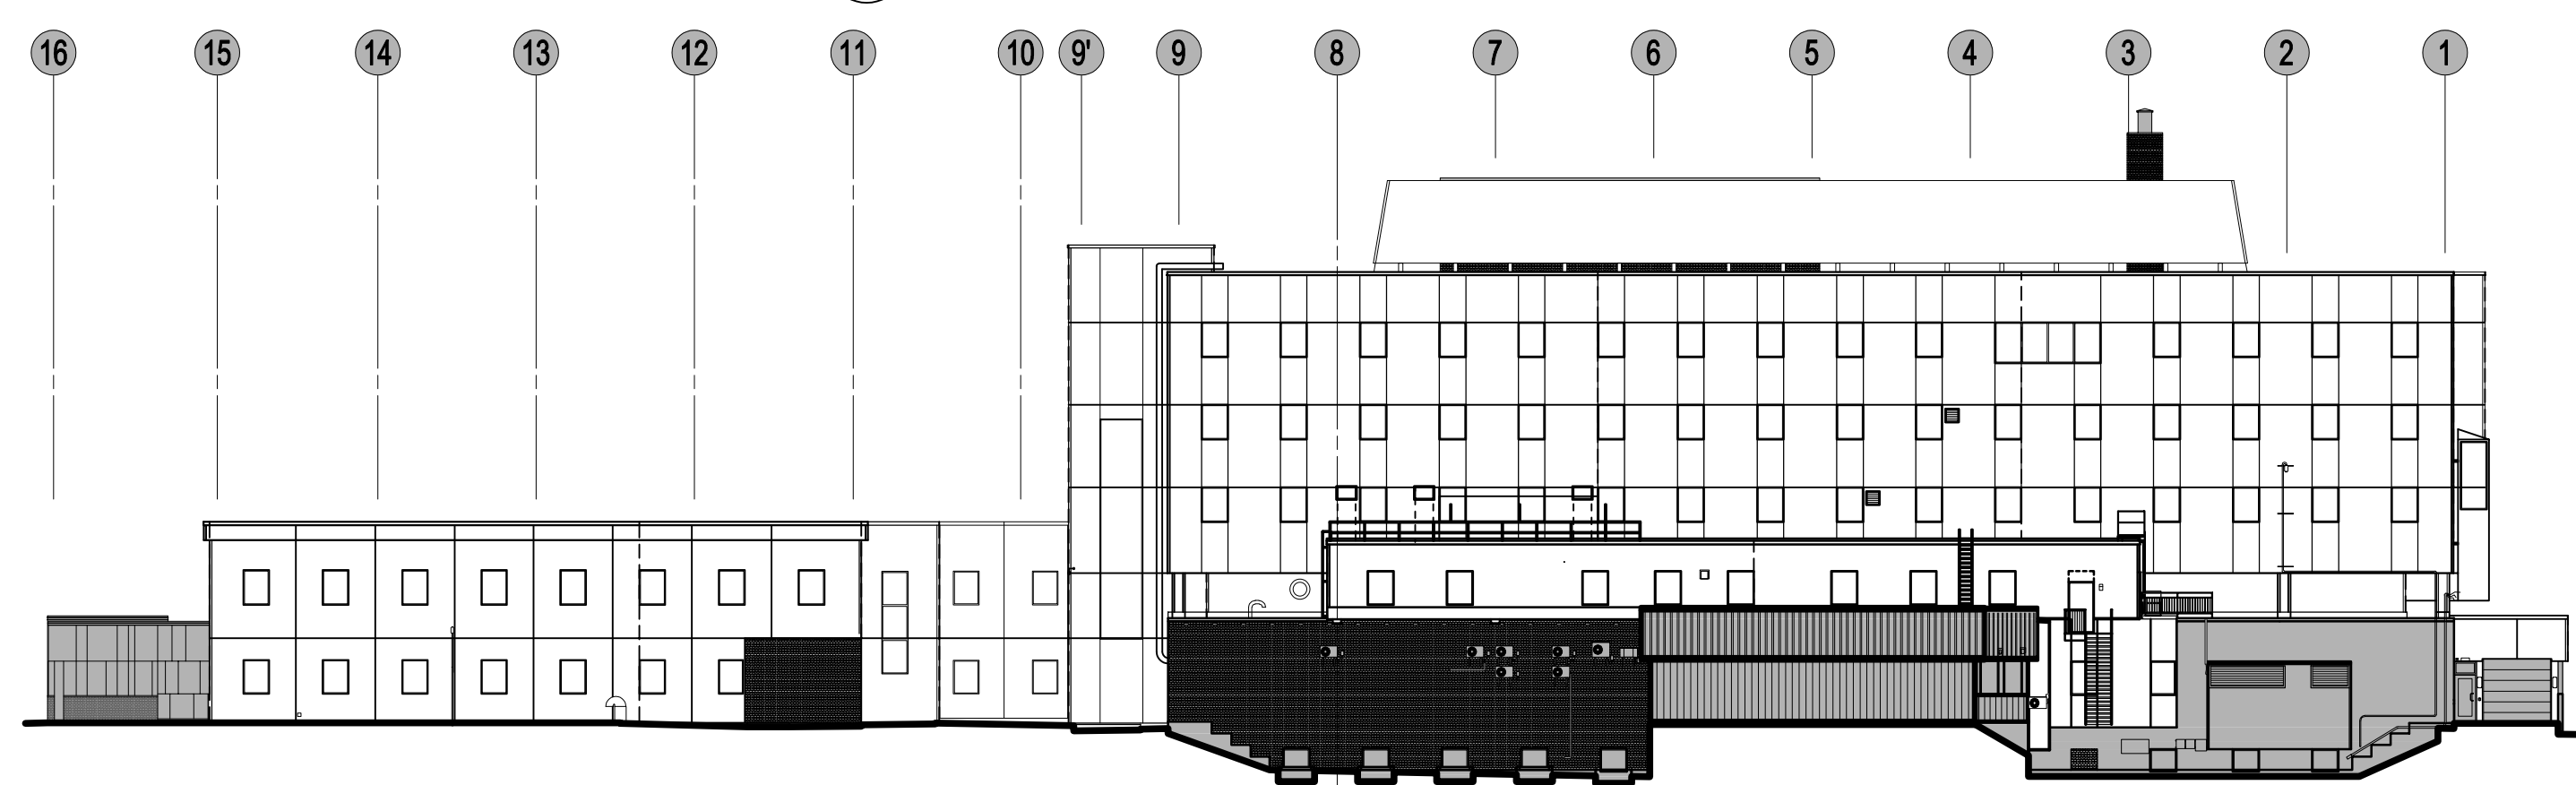

ÉLÉVATION OUEST PARTIELLE

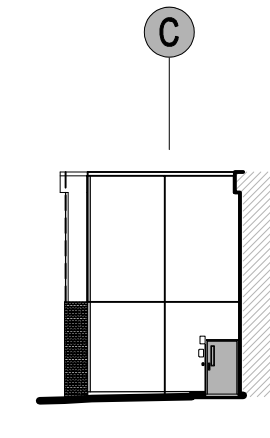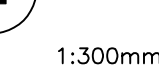

ÉLEVATION OUEST PARTIELLE



Le présent document est émis pour la seule fin identifiée. Son contenu est protégé par les droits d'auteur et toute reproduction ou modification, partielle ou totale, est interdite sans l'autorisation écrite de gagnon, letellier, cyr, ricard, mathieu, proulx, savard consortium d'architectes.

LISTE DES LOCAUX

S2	DÉCHETS BIO-MÉDICAUX
S3	CENTRALE THERMIQUE
S3-A	BUREAU
S4	VENTILATION
S5	ESCAUER
S6	VESTIAIRE
S7	CHEF DE SERVICE
S8	ARCHIVE
S9	CONSEILLÈRE DST
S10	DÉPÔT
S11	MAGASIN
S12	ARCHIVES
S13	ESCAUER
S14	DÉPÔT
S15	DÉPÔT
S16	MENUISERIE
S17	GBM
S18	BUREAU
S19	CHEF DE SERVICE
S20	PRÉVENTIONNISTE
S21	VESTIAIRE HOMMES
S22	SALLE DE PAUSE
S23/24	CAFÉTÉRIA/ NUTRITIONNISTE
S25	CUISINE
S26	RÉSERVE
S27	ENTRETIEN MÉNAGER
S29	CHUTE À DÉCHETS
S31	ESCAUER
S32	BUANDERIE
S33	BIO-MÉDICAUX DÉCHETS
S35	CONCIERGERIE
S37	CORRIDOR
S41	ARCHIVES MORTES



PLAN DU SOUS-SOL - DÉMOLITION
1:200mm

NOTES

- CONTENEUR À RECYCLAGE EXISTANT À CONSERVER.
- CONTENEUR À DÉCHET EXISTANT À CONSERVER.
- PROFIL DE L'ÉTAGE.
- BOLLARD EXISTANT À CONSERVER.
- OUVERTURE À RÉALISER DANS LE HAUT DE LA CLOISON DE GYPSE AU-DESSUS DES PLAFONDS SUSPENDUS POUR LES TRAVAUX DE MÉCANIQUE, VOIR DOCUMENTS D'INGÉNÉRIE.
- TUILES ET SUSPENSION DE PLAFOND SUSPENDU À DÉMOLIR DANS L'ENTRÉE DU LOCAL. POUR LES ÉLÉMENTS ÉLECTROMÉCANIQUES INSTALLÉS DANS LE PLAFOND SUSPENDU, VOIR LES DOCUMENTS D'INGÉNÉRIE.
- TUILES DE PLAFOND SUSPENDU SUR LE LONG DE LA CLOISON À ENLEVER TEMPORAIREMENT POUR LES TRAVAUX DE MÉCANIQUE, VOIR DOCUMENTS D'INGÉNÉRIE.
- PROFIL DU CAPOTIN DE VENTILATION EXISTANT AU-DESSUS À CONSERVER ET PROTÉGER PENDANT LES TRAVAUX.
- SOUFFLAGE ET PERSIENNE EXISTANTS À DÉMOLIR, VOIR DÉTAIL 61 DE LA FEUILLE 422.

LÉGENDE

- (X) NOTE DESCRIPTIVE.
- (X) AXE EXISTANT.
- (NS) NOUVEL AXE.
- (XXX) NUMÉRO DE LOCAUX.
- EXISTANT À CONSERVER.
- MUR OU CLOISON À DÉMOLIR.
- TRAVAUX DE DÉMOLITION SUR LE MUR EXISTANT, VOIR LES COMPOSITIONS, COUPES DE MUR TYPES ET DÉTAILS TYPES POUR LES COMPOSANTES À DÉMOLIR.
- (X) COUPE DE MUR.
- (X) DÉTAIL TYPE.
- PORTE EXISTANTE À CONSERVER.
- PORTE EXISTANTE À DÉMOLIR.
- FENÊTRE EXISTANTE OU MUR-RIDEAU À CONSERVER.
- FENÊTRE EXISTANTE OU MUR-RIDEAU À DÉMOLIR, VOIR LES COUPES DE MURS ET DÉTAILS TYPES DE FENÊTRE POUR LA SÉQUENCE DE TRAVAUX.
- ZONE DE DÉMOLITION DE TOITURE.
- NOUVEAU MUR OU NOUVELLE CLOISON À CONSTRUIRE.
- NOUVELLES COMPOSANTES DE MUR À CONSTRUIRE, DÉTAILS TYPES.
- NOUVELLE PORTE.
- NOUVELLE FENÊTRE OU NOUVEAU MUR-RIDEAU, VOIR COUPES DEMUR, DÉTAILS TYPES ET ÉLEVATIONS TYPE DE FENÊTRES.
- ZONE DE RECONSTRUCTION DE TOITURE.
- NOUVELLE TOILE SOLAIRE
- NOUVELLE TOILE SOLAIRE
- LIMITE DES TRAVAUX D'ENVELOPPE, VOIR NOTES SPÉCIFIQUES. LA NOTE SPÉCIFIQUE EST APPLICABLE À PARTIR DE CETTE LIMITE JUSQU'À LA PROCHAÎNE LIMITE SUR LE PÉRIMÈTRE DE L'ÉTAGE.
- TYPE DE VENTILATEUR D'ENTRETOIT
- TYPE A: CABANON DE VENTILATION 813x813
- TYPE B: CABANON DE VENTILATION 660x660
- TYPE C: VENTILATEUR 450x450
- TYPE D: VENTILATION EXISTANT

NE DOIT PAS SERVIR À L'EXÉCUTION

Le présent document est émis pour la seule fin identifiée. Son contenu est protégé par les droits d'auteur et toute reproduction ou modification, partielle ou totale, est interdite sans l'autorisation écrite de gagnon, letellier, cyr, ricard, mathieu, proulx, savard consortium d'architectes.




GLCRM | Proulx Savard |

GLCRM:
128, Avenue de la Cathédrale,
Bureau 201
Québec, QC, G5L 5H7
(418) 722-7655


2406, Ch. des Quatres-Bourgeois,
Bureau 100
Québec, QC, G1V 1W5
(418) 647-1700

Proulx Savard Architectes:
75, boul. Arthur-Buies Ouest,
Rimouski QC G5L 5C2
(418) 723-5543

ARCHITECTURE

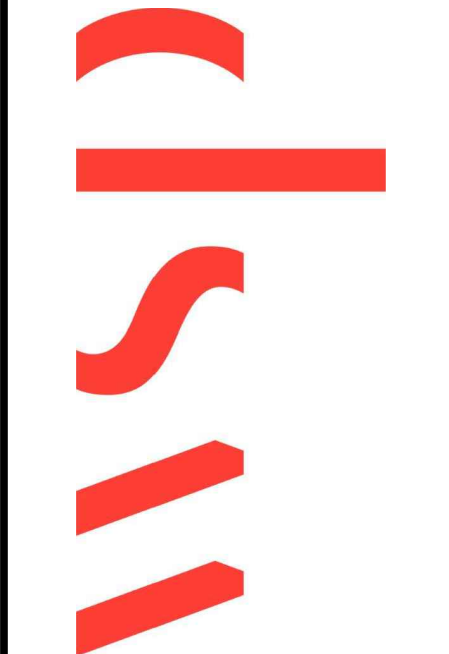

CONSULTANTS

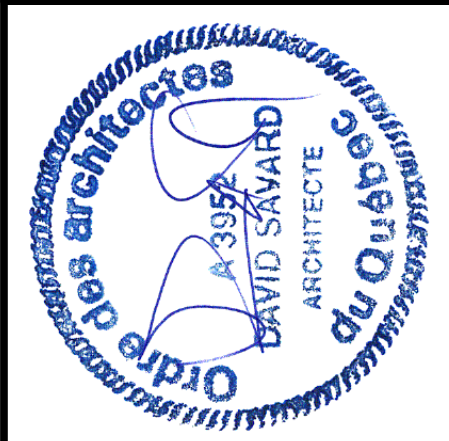

DESIGNATEUR(S) D.B. I.A.C.	DOSSIER No. 24-187 / 8487-24	DATE SEPTEMBRE 2024	ÉCHELLE INDIQUÉE	No	DATE	RÉVISIONS
PROJET HÔPITAL DE CHAUDIER, Chaudier (Réfection de l'enveloppe)	05	2024-09-04	DÉFINITIVES POUR SOUMISSION	PROPRIÉTAIRE Santé Québec		
	06	2024-08-21	DÉFINITIVES 100% POUR APPROBATION			
	03	2024-08-03	DÉFINITIVES 80% POUR APPROBATION			
	02	2024-05-14	DÉFINITIVES 40% POUR APPROBATION			
PROJET HÔPITAL DE CHAUDIER, Chaudier (Réfection de l'enveloppe)	01	2024-02-27	PRÉLIMINAIRES 20% POUR APPROBATION	PROPRIÉTAIRE Santé Québec		

PLAN DU SOUS-SOL - DÉMOLITION

050

PLAN DU REZ-DE-CHAUSSÉE - DÉMOLITION

PLA
1:200mm

NOTES

- 51 CONDUIT ET PERSIENNE EXISTANTS, VOIR DOCUMENTS D'INGÉNIERIE.
- 52 REVÊTEMENT DE PLANCHER DE VINYLE ET PLINTHE DE VINYLE À DEMOUR.
- 53 SECTION DU SYSTÈME DE TOITURE EXISTANT À DEMOURIR POUR L'INSTALLATION DES VENTILATEURS D'ENTRETIOT, DIMENSIONS SELON LE TYPE, VOIR PLAN DE CONSTRUCTION À LA PAGE 302. PRÉVOIR DE DÉCASSULER LA MEMBRANE DE 4,355mm, VOIR DÉTAIL TYPE 2 DE LA FEUILLE 305.
- 54 PROFIL DU CAPOTIN DE VENTILATION.
- 55 REVÊTEMENT DE PLANCHER EXISTANT À CONSERVER ET À PROTÉGER PENDANT LES TRAVAUX.
- 56 TUILES DE PLAFOND SUSPENDU À ENLEVER TEMPORAIREMENT POUR LES TRAVAUX DE MÉCANIQUE.
- 57 TUILES DE PLAFOND SUSPENDU ET SUSPENSION À ENLEVER TEMPORAIREMENT SUR UNE LARGEUR DE 2 TUILES POUR LES TRAVAUX DE MÉCANIQUE.

NOTES

- 33 APPAREIL DE CHAUFFAGE EXISTANT À DÉMOLIR, VOIR DOCUMENTS D'INGÉNIERIE.
- 34 SECTION DE MUR À DÉMOLIR SOUS LA FENÊTRE JUSQU'À LA DALLE DE PLANCHER.
- 35 PORTE ET CADRE EXISTANTS À DÉMOLIR.
- 36 CLOISON EXISTANTE À DÉMOLIR JUSQU'À LA HAUTEUR DU CADRE DE PORTE EXISTANT.
- 37 ZONE DE TOITURE À DÉMOLIR POUR LES TRAVAUX DES ECHELLES, VOIR DÉTAIL 4 SUR LA FEUILLE 306.
- 38 PERSIENNE EXISTANTE À MODIFIER POUR NE PAS ÊTRE EN CONFLIT AVEC LE NOUVEAU REVÊTEMENT.
- 39 PAREMENT DE TÔLE EXISTANT À DÉMOLIR.
- 40 TOILE AMOVIBLE EXISTANTE À DÉMONTÉ ET ENTREPOSER POUR REINSTALLATION FUTURE.
- 41 GARDE-CORPS EXISTANT À CONSERVER ET À PROTÉGER PENDANT LES TRAVAUX.

NOTES

- 1 APPAREIL D'ÉLECTRO-MÉCANIQUE ET SUPPORT EXISTANT, VOIR DOCUMENTS D'INGÉNIEURIE.
- 2 CONDUIT EXISTANT, VOIR DOCUMENTS D'INGÉNIEURIE.
- 3 PERSIENNE À DÉMONTÉLER ET ENTREPOSER PENDANT LES TRAVAUX POUR REINSTALLATION FUTURE, VOIR DOCUMENTS D'INGÉNIEURIE.
- 4 GARDE-CORPS EXISTANT À DÉMONTÉLER ET ENTREPOSER POUR REINSTALLATION FUTURE.
- 5 ÉCHELLE EXISTANTE À DÉMONTÉLER ET ENTREPOSER POUR REINSTALLATION FUTURE, VOIR LA SÉRIE DE FEUILLE 700 POUR LES INTERVENTIONS À FAIRE SUR LES ÉCHELLES AVANT LEUR REINSTALLATION.
- 6 COUSSIN GONFLABLE D'ÉTANCHÉITE POUR QUAI D'EMBARQUEMENT À DÉMONTÉLER ET ENTREPOSER POUR REINSTALLATION FUTURE.
- 7 SORTIE OU ENTRÉE DE VENTILATION EXISTANTE, VOIR DOCUMENTS D'INGÉNIEURIE.
- 8 ESCALIER EN ACIER EXISTANT À DÉPLACER ET ENTREPOSER POUR REINSTALLATION FUTURE.

GLCRM | Proulx Savard |

106, Ch. des Quatres-Bourgeois,
Bureau 100
Montréal, QC, G1V 1W5
Tél. (514) 647-1700

roulx Savard Architectes:
5, boul. Arthur-Buies Ouest,
Lamoussi QC G5L 5C2

ARCHITECTURE



051

LISTE DES LOCAUX	
101-D4	BUREAU
101-D5	PROLÈVEMENT
101-D6	PRÉPARATION ET ENVOI
101-D7	BANQUE DE SANG
101-D8	HÉMATOLOGIE
101-D9	BIOCHIMIE
101-D10	CHEF DE SERVICE
101-D11	BUREAU
104-A1	VESTIAIRE HOMME?
104-A2	VESTIAIRE FEMME?
104-C	SALON
104-F	CHIRURGIE 1 JOUR
104-G	SALLE DE RÉVÊL
105-B	1 TECHNICIEN
105-C	DÉPOT
105-D	1 TECHNICIEN
105-E	DIR. SERVICES TECHNIQUE
107-C	COMITÉ DES USAGERS
109	SALLE DES SERVEURS
110-A	CHEF DE SERVICE
110-B	CONSEILLÈRE
110-C	SALLE CONFÉRENCE DSP
112-B	SALON MÉDECIN
112-C	SALON MÉDECIN
113-A	CHEF DE SERVICE
113-B	DIR. RESS. INFORMATIONNELLES
116-A	LISTE DE RAPPEL
121-A	AVOCATE
122-A	CHEF DE SERVICE
122-B	CONSEILLÈRE RH
122-C	TECH. RH
122-D	TECH. RH
124	ADJOINT DSI
123-A	TECH. DSI
123-B	CONSEILLÈRE DSI
123-D	INFIRMIÈRE PCI
123-E	CONSEILLÈRE DSI
123-G	CHEF DE L'APPRO.
123-H	LABO INF.
124-A	ADJOINT DSI
124-B	TECH. DSI

NOTES

58 OUVERTURE À RÉALISER DANS LE MUR EXISTANT DANS L'ENTREPLAFOND POUR ACCÉDER AUX BASES DES COLONNES D'ACIER POUR LES TRAVAUX DE STRUCTURE. VOIR PHOTO DE RÉFÉRENCE #1 SUR LA FEUILLE 051.

59 RANGEMENT EN ÉBÉNISTERIE À RETIRER ET REMETTRE AU PROPRIÉTAIRE.

60 DISTRIBUTEUR DE VERRE DE CARTON À RETIRER ET REMETTRE AU PROPRIÉTAIRE.

NOTES

51 CONDUIT ET PERSIENNE EXISTANTS, VOIR DOCUMENTS D'INGÉNIERIE.

52 REVÊTEMENT DE PLANCHER DE VINYLE ET PLINTHE DE VINYLE À DÉMOLIR.

53 SECTION DU SYSTÈME DE TOITURE EXISTANT À DÉMOLIR POUR L'INSTALLATION DES VENTILATEURS D'ENTRETOIT, DIMENSIONS SELON LE TYPE, VOIR PLAN DE CONSTRUCTION À LA PAGE 302. PRÉVOIR DE DÉGRANULER LA MEMBRANE DE ±305mm, VOIR DÉTAIL TYPE 2 DE LA FEUILLE 305.

54 PROFIL DU CAPOTIN DE VENTILATION.

55 REVÊTEMENT DE PLANCHER EXISTANT À CONSERVER ET À PROTÉGER PENDANT LES TRAVAUX.

56 TUILES DE PLAFOND SUSPENDU À ENLEVER TEMPORAIREMENT POUR LES TRAVAUX DE MÉCANIQUE.

57 TUILES DE PLAFOND SUSPENDU ET SUSPENSION À ENLEVER TEMPORAIREMENT SUR UNE LARGEUR DE 2 TUILES POUR LES TRAVAUX DE MÉCANIQUE.

NOTES

42 PRISE D'AIR EXTÉRIEURE EXISTANTE À CONSERVER ET À PROTÉGER PENDANT LES TRAVAUX.

43 MUR EN REVÊTEMENT MÉTALLIQUE EXISTANT À CONSERVER ET À PROTÉGER PENDANT LES TRAVAUX.

44 MUR DE MAÇONNERIE EXISTANT À CONSERVER ET À PROTÉGER PENDANT LES TRAVAUX. À MOINS D'INDICATIONS CONTRAIRES DANS LES ÉLEVATIONS ET LES COUPES DE MUR.

45 TRAVAUX DE DÉMOLITION DU MUR, VOIR LES COUPES DE MUR TYPES ET LES DÉTAILS TYPES.

46 TRAPPE D'ACCÈS DE L'ENTRETOIT EXISTANTE À CONSERVER.

47 FENÊTRE INTÉRIEURE À DÉMOLIR, VOIR DÉTAIL #1 DE LA FEUILLE 502.

48 SOLIN À COUPER, VOIR DÉTAILS EN COUPES TYPES DE LA SÉRIE DE FEUILLES 400.

49 ÉVENT EXISTANT À DÉPLACER, VOIR DOCUMENTS D'INGÉNIERIE.

50 PORTE ET CADRE EXISTANTS À DÉMOLIR.

NOTES

33 APPAREIL DE CHAUFFAGE EXISTANT À DÉMOLIR, VOIR DOCUMENTS D'INGÉNIERIE.

34 SECTION DE MUR À DÉMOLIR SOUS LA FENÊTRE JUSQU'À LA DALLE DE PLANCHER.

35 PORTE ET CADRE EXISTANTS À DÉMOLIR.

36 CLOISON EXISTANTE À DÉMOLIR JUSQU'À LA HAUTEUR DU CADRE DE PORTE EXISTANT.

37 ZONE DE TOITURE À DÉMOLIR POUR LES TRAVAUX DES ÉCHELLES, VOIR DÉTAIL 4 SUR LA FEUILLE 306.

38 PERSIENNE EXISTANTE À MODIFIER POUR NE PAS ÊTRE EN CONFLIT AVEC LE NOUVEAU REVÊTEMENT.

39 PAREMENT DE TÔLE EXISTANT À DÉMOLIR.

40 TOILE AMOVIBLE EXISTANTE À DÉMOLIR ET ENTREPOSER POUR RÉINSTALLATION FUTURE.

41 GARDE-CORPS EXISTANT À CONSERVER ET À PROTÉGER PENDANT LES TRAVAUX.

NOTES

24 GARGOUILLE EXISTANTE À NETTOYER.

25 MURET PARAPET EXISTANT À CONSERVER ET PROTÉGER PENDANT LES TRAVAUX.

26 SECTION DE MURET PARAPET EXISTANT À DÉMOLIR. DANS LA LIMITE DE L'OUVERTURE DE LA TOITURE POUR LES TRAVAUX DE STRUCTURE.

27 PARAPET EXISTANT À DÉMOLIR, VOIR DÉTAILS DE LA SÉRIE DE FEUILLES 400.

28 ESCALIER EXISTANT À DÉMOLIR.

29 GARDE-CORPS EXISTANT À DÉMOLIR.

30 ZONE DE TOITURE À DÉMOLIR. VOIR DÉTAILS DE LA SÉRIE DE FEUILLES 300.

31 SOLIN ET MEMBRANES SUR LE PARAPET À DÉMOLIR. CONSERVER LE BATI DU PARAPET, VOIR DÉTAILS DE LA SÉRIE 400.

32 AÉRATEUR D'ENTRETOIT EXISTANT À ENLEVER TEMPORAIREMENT ET RELOCALISER, VOIR DÉTAIL 1 SUR LA FEUILLE 306.

NOTES

1 APPAREIL D'ÉLECTRO-MÉCANIQUE ET SUPPORT EXISTANT, VOIR DOCUMENTS D'INGÉNIERIE.

2 CONDUIT EXISTANT, VOIR DOCUMENTS D'INGÉNIERIE.

3 PERSIENNE À DÉMONTÉLER ET ENTREPOSER PENDANT LES TRAVAUX POUR RÉINSTALLATION FUTURE, VOIR DOCUMENTS D'INGÉNIERIE.

4 GARDE-CORPS EXISTANT À DÉMONTÉLER ET ENTREPOSER POUR RÉINSTALLATION FUTURE.

5 ÉCHELLE EXISTANTE À DÉMONTÉLER ET ENTREPOSER POUR RÉINSTALLATION FUTURE, VOIR LA SÉRIE DE FEUILLE 700 POUR LES INTERVENTIONS À FAIRE SUR LES ÉCHELLES AVANT LEUR RÉINSTALLATION.

6 COUSSIN GONFLABLE D'ÉTANCHÉITÉ POUR QUAI D'EMBARQUEMENT À DÉMONTÉLER ET ENTREPOSER POUR RÉINSTALLATION FUTURE.

7 SORTIE OU ENTRÉE DE VENTILATION EXISTANTE, VOIR DOCUMENTS D'INGÉNIERIE.

8 ESCALIER EN ACIER EXISTANT À DÉPLACER ET ENTREPOSER POUR RÉINSTALLATION FUTURE.

9 SECTION DE GARDE-CORPS À COUPER ET DÉMONTÉLER. ENTREPOSER POUR RÉINSTALLATION FUTURE, VOIR DÉTAILS DE LA SÉRIE DE FEUILLES 700.

10 CONDUIT DE VENTILATION EXISTANT, VOIR DOCUMENTS D'INGÉNIERIE.

11 PLATEFORME ET GARDE-CORPS EN ACIER EXISTANT À DÉMONTÉLER ET ENTREPOSER POUR RÉINSTALLATION FUTURE.

12 ZONE DE TOITURE À DÉMOLIR POUR LES TRAVAUX DE STRUCTURE, SUR ±610mm DE LARGEUR LE LONG DU MUR EXTÉRIEUR, VOIR DÉTAILS DE LA SÉRIE DE FEUILLES 400.

13 PROFIL DU PORTE-A-FAUX EXISTANT AU-DESSUS.

14 PROFIL DU DÉBORD DE TOIT EXISTANT AU-DESSUS.

15 ÉVENT EXISTANT, VOIR DOCUMENTS D'INGÉNIERIE.

16 AÉRATEUR D'ENTRETOIT EXISTANT À CONSERVER.

17 TRAPPE D'ACCÈS À L'ENTRETOIT EXISTANTE À DÉMOLIR.

18 DRAIN DE TOITURE EXISTANT, VOIR DOCUMENTS D'INGÉNIERIE.

19 BASE MEMBRANÉE EN TOITURE EXISTANTE POUR ANCRAGE DES GARDE-CORPS À DÉMOLIR.

20 BASE MEMBRANÉE EN TOITURE EXISTANTE POUR SORTIE DE CONDUITS À CONSERVER ET PROTÉGER PENDANT LES TRAVAUX.

21 BASE MEMBRANÉE EN TOITURE EXISTANTE À CONSERVER ET À PROTÉGER PENDANT LES TRAVAUX.

22 TRAPPE D'ACCÈS AU TOIT EXISTANTE À CONSERVER ET PROTÉGER PENDANT LES TRAVAUX.

23 COL. DE CYGNE EXISTANT, VOIR DOCUMENTS D'INGÉNIERIE.

LÉGENDE

- (X) NOTE DESCRIPTIVE.
- (X) AXE EXISTANT.
- (NS) NOUVEL AXE.
- (XXX) NUMÉRO DE LOCAUX.
- () EXISTANT À CONSERVER.
- (---) MUR OU CLOISON À DÉMOLIR.
- (---) TRAVAUX DE DÉMOLITION SUR LE MUR EXISTANT, VOIR LES COMPOSITIONS, COUPES DE MUR TYPES ET DÉTAILS TYPES POUR LES COMPOSANTES À DÉMOLIR.
- (X/XXX/XXX) COUPE DE MUR.
- (X/XXX/XXX) DÉTAIL TYPE.
- () PORTE EXISTANTE À CONSERVER.
- () PORTE EXISTANTE À DÉMOLIR.
- () FENÊTRE EXISTANTE OU MUR-RIDEAU À CONSERVER.
- () FENÊTRE EXISTANTE OU MUR-RIDEAU À DÉMOLIR, VOIR LES COUPES DE MURS ET DÉTAILS TYPES DE FENÊTRE POUR LA SÉQUENCE DE TRAVAU.
- (---) ZONE DE DÉMOLITION DE TOITURE.
- (---) NOUVEAU MUR OU NOUVELLE CLOISON À CONSTRUIRE.
- (---) NOUVELLES COMPOSANTES DE MUR À CONSTRUIRE, DÉTAILS TYPES.
- () NOUVELLE PORTE.
- () NOUVELLE FENÊTRE OU NOUVEAU MUR-RIDEAU, VOIR COUPES DEMUR, DÉTAILS TYPES ET ÉLEVATIONS TYPE DE FENÊTRES.
- (---) ZONE DE RECONSTRUCTION DE TOITURE.
- (ST1) NOUVELLE TOILE SOLAIRE.
- (ST2) NOUVELLE TOILE SOLAIRE.
- (X/X) LIMITE DES TRAVAUX D'ENVELOPPE, VOIR NOTES SPÉCIFIQUES. LA NOTE SPÉCIFIQUE EST APPLICABLE À PARTIR DE CETTE LIMITE JUSQU'À LA PROCHAÎNE LIMITE SUR LE PÉRIMÈTRE DE L'ÉTAGE.

TYPE DE VENTILATEUR D'ENTRETOIT

TYPE A: CABANON DE VENTILATION 813x813

TYPE B: CABANON DE VENTILATION 660x660

TYPE C: VENTILATEUR 450x450

TYPE D: VENTILATION EXISTANT

NE DOIT PAS SERVIR À L'EXÉCUTION

Le présent document est émis par la seule fin identifiée. Son contenu est protégé par les droits d'auteur et toute reproduction ou modification, partielle ou totale, est interdite sans l'autorisation écrite de gagnon, letellier, cyr, ricard, mathieu, proulx, savard consortium d'architectes.




GLCRM | Proulx Savard |

GLCRM:
128, Avenue de la Cathédrale,
Bureau 201
Rimouski, QC, G5L 5H7
14181 722-7655

2406, Ch. des Quatres-Bourgeois,
Bureau 100
Québec, QC, G1V 1W5
14181 647-1700

Proulx Savard Architectes:
75, boul. Arthur-Buies Ouest,
Rimouski QC G5L 5C2
14181 723-5543

ARCHITECTURE

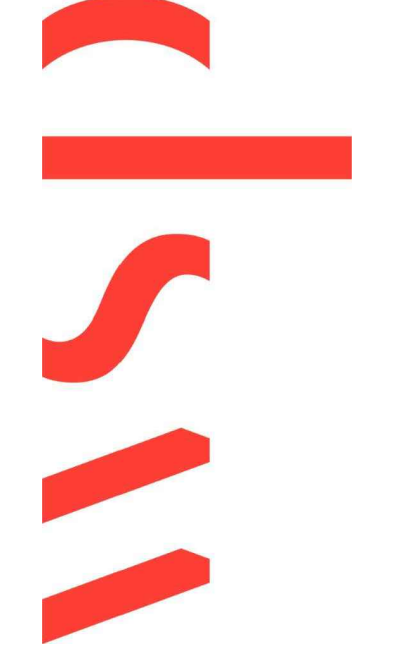

CONSULTANTS



DOSSIER No.		DATE		RÉVISIONS	
24-1087 / 8487-24		SEPTEMBRE 2024			
DESIGNATEUR (S)	DATE	ÉCHELLE	INDICÉE	DATE	No
D.B. A.C.	05	2024-09-04	DÉFINITIVES POUR SOUMISSION		
	06	2024-08-21	DÉFINITIVES 100% POUR APPROBATION		
	03	2024-08-03	DÉFINITIVES 80% POUR APPROBATION		
	02	2024-05-14	DÉFINITIVES 40% POUR APPROBATION		
D.B. A.C.	01	2024-05-14	PRÉLIMINAIRES 50% POUR APPROBATION		
	01	2024-02-27			

PROJET
HÔPITAL DE CHANDLER,
Chandler
(Réfection de l'enveloppe)

PROPRIÉTAIRE
Santé Québec

LISTE DES LOCAUX	
202	SALLE D'ATTENTE HÉMODIALYSE
202A	TRAITEMENT D'EAU
203	TRAITEMENT D'EAU
204	CHAMBRE 1 LIT
205	CHAMBRE 1 LIT
206	CHAMBRE 1 LIT
207	CHAMBRE NAÏSS.
208	CHAMBRE NAÏSS.
209	CHAMBRE NAÏSS.
210	CHAMBRE NAÏSS.
211	CHAMBRE NAÏSS.
212	CHAMBRE ISOLEMENT #1
213	CHAMBRE 1 LIT
214	CHAMBRE OBSERV.
215	CHAMBRE 1 LIT
216	CHAMBRE A PRESSION NEGATIVE
217	CHAMBRE 1 LIT
218	CHAMBRE 1 LIT
219	CHAMBRE 1 LIT
220	CHAMBRE 1 LIT
221	CHAMBRE 1 LIT
222	CHAMBRE 1 LIT
223	CHAMBRE 1 LIT
224	CHAMBRE 1 LIT
230	NON-STRESS-TEST
231	UTILITE PROPRE
232	S. SEJOUR PED.
233	PHARMACIE
234	DEPOT HEMO.
235	ISOLEMENT HEMO.
236	TRAITEMENT HEMO.

NOTES

- (58) OUVERTURE À RÉALISER DANS LE MUR EXISTANT DANS L'ENTREPLAFOND POUR ACCÉDER AUX BASES DES COLONNES D'ACIER POUR LES TRAVAUX DE STRUCTURE. VOIR PHOTO DE RÉFÉRENCE #1 SUR LA FEUILLE 051.
- (59) RANGEMENT EN ÉBÉNISTERIE À RETIRER ET REMETTRE AU PROPRIÉTAIRE.
- (60) DISTRIBUTEUR DE VERRE DE CARTON À RETIRER ET REMETTRE AU PROPRIÉTAIRE.

NOTES

- 51) CONDUIT ET PERSIENNE EXISTANTS, VOIR DOCUMENTS D'INGENIERIE.
- 52) REVÊTEMENT DE PLANCHER DE VINYLE ET PLINTHE DE VINYLE À DÉMOLIR.
- 53) SECTION DU SYSTÈME DE TOITURE EXISTANT À DÉMOLIR POUR L'INSTALLATION DES VENTILATEURS D'ENTRETOIT, DIMENSIONS SELON LE TYPE, VOIR PLAN DE CONSTRUCTION À LA PAGE 302. PRÉVOIR DE DÉGRADULER LA MEMBRANE DE ±305mm, VOIR DÉTAIL TYPE 2 DE LA FEUILLE 305.
- 54) PROFIL DU CAPOTIN DE VENTILATION.
- 55) REVÊTEMENT DE PLANCHER EXISTANT À CONSERVER ET À PROTÉGER PENDANT LES TRAVAUX.
- 56) TULES DE PLAFOND SUSPENDU À ENLEVER TEMPORAIREMENT POUR LES TRAVAUX DE MÉCANIQUE.
- 57) TULES DE PLAFOND SUSPENDU ET SUSPENSION À ENLEVER TEMPORAIREMENT SUR UNE LARGEUR DE 2 TULES POUR LES TRAVAUX DE MÉCANIQUE.

NOTES

- (42) PRISE D'AIR EXTÉRIEURE EXISTANTE À CONSERVER ET À PROTÉGER PENDANT LES TRAVAUX.
- (43) MUR EN REVÊTEMENT MÉTALLIQUE EXISTANT À CONSERVER ET À PROTÉGER PENDANT LES TRAVAUX.
- (44) MUR DE MAÇONNERIE EXISTANT À CONSERVER ET À PROTÉGER PENDANT LES TRAVAUX. À MOINS D'INDICATIONS CONTRAIRES DANS LES ÉLEVATIONS ET LES COUPES DE MUR.
- (45) TRAVAUX DE DÉMOLITION DU MUR, VOIR LES COUPES DE MUR TYPES ET LES DÉTAILS TYPES.
- (46) TRAPPE D'ACCÈS DE L'ENTRETOIT EXISTANTE À CONSERVER.
- (47) FENÊTRE INTÉRIEURE À DÉMOLIR, VOIR DÉTAIL #1 DE LA FEUILLE 502.
- (48) SOLIN À COUPER. VOIR DÉTAILS EN COUPES TYPES DE LA SÉRIE DE FEUILLES 400.
- (49) ÉVENT EXISTANT À DÉPLACER, VOIR DOCUMENTS D'INGÉNIERIE.
- (50) PORTE ET CADRE EXISTANTS À DÉMOLIR.

NOTES

- (33) APPAREIL DE CHAUFFAGE EXISTANT À DÉMOLIR, VOIR DOCUMENTS D'INGÉNIEURIE.
- (34) SECTION DE MUR À DÉMOLIR SOUS LA FENÊTRE JUSQU'À LA DALLE DE PLANCHER.
- (35) PORTE ET CADRE EXISTANTS À DÉMOLIR.
- (36) CLOISON EXISTANTE À DÉMOLIR JUSQU'À LA HAUTEUR DU CADRE DE PORTE EXISTANT.
- (37) ZONE DE TOITURE À DÉMOLIR POUR LES TRAVAUX DES ECHELLES, VOIR DÉTAIL 4 SUR LA FEUILLE 306.
- (38) PERSIENNE EXISTANTE À MODIFIER POUR NE PAS ÊTRE EN CONFLIT AVEC LE NOUVEAU REVÊTEMENT.
- (39) PAREMENT DE TOLE EXISTANT À DÉMOLIR.
- (40) TOILE AMOVIBLE EXISTANTE À DÉMONTÉ ET ENTREPOSER POUR REINSTALLATION FUTURE.
- (41) GARDE-CORPS EXISTANT À CONSERVER ET À PROTÉGER PENDANT LES TRAVAUX.

NOTES

- (24) GARGOUILLE EXISTANTE À NETTOYER.
- (25) MURET PARAPET EXISTANT À CONSERVER ET PROTÉGER PENDANT LES TRAVAUX.
- (26) SECTION DE MURET PARAPET EXISTANT À DÉMOURIR. LA LIMITE DE L'OUVRETURE DE LA TOITURE POUR LES TRAVAUX DE STRUCTURE.
- (27) PARAPET EXISTANT À DÉMOURIR, VOIR DÉTAILS DE LA SÉRIE DE FEUILLES 400.
- (28) ESCALIER EXISTANT À DÉMOURIR.
- (29) GARDE-CORPS EXISTANT À DÉMOURIR.
- (30) ZONE DE TOITURE À DÉMOURIR. VOIR DÉTAILS DE LA SÉRIE DE FEUILLES 300.
- (31) SOLIN ET MEMBRANES SUR LE PARAPET À DÉMOURIR. CONSERVER LE BÂTI DU PARAPET, VOIR DÉTAILS DE LA SÉRIE 400.
- (32) AÉRATEUR D'ENTRETOIT EXISTANT À ENLEVER TEMPORAIREMENT ET RELOCALISÉ, VOIR DÉTAIL 1 SUR LA FEUILLE 306.

NOTES

- 1 APPAREIL D'ÉLECTRO-MÉCANIQUE ET SUPPORT EXISTANT, VOIR DOCUMENTS D'INGÉNIEURIE.
- 2 CONDUIT EXISTANT, VOIR DOCUMENTS D'INGÉNIEURIE.
- 3 PERSIENNE À DÉMONTÉLER ET ENTREPOSER PENDANT LES TRAVAUX POUR REINSTALLATION FUTURE, VOIR DOCUMENTS D'INGÉNIEURIE.
- 4 GARDE-CORPS EXISTANT À DÉMONTÉLER ET ENTREPOSER POUR REINSTALLATION FUTURE.
- 5 ECHELLE EXISTANTE À DÉMONTÉLER ET ENTREPOSER POUR REINSTALLATION FUTURE, VOIR LA SÉRIE DE FEUILLE 700 POUR LES INTERVENTIONS À FAIRE SUR LES ECHELLES AVANT LEUR REINSTALLATION.
- 6 COUSSIN GONFLABLE D'ÉTANCHÉITÉ POUR QUAI D'EMBARQUEMENT À DÉMONTÉLER ET ENTREPOSER POUR REINSTALLATION FUTURE.
- 7 SORTIE OU ENTRÉE DE VENTILATION EXISTANTE, VOIR DOCUMENTS D'INGÉNIEURIE.
- 8 ESCALIER EN ACIER EXISTANT À DÉPLACER ET ENTREPOSER POUR REINSTALLATION FUTURE.




GLCRM | Proulx Savard |

GLCRM:
128, Avenue de la Cathédrale,
Bureau 201
Rimouski, QC, G5L 5H7
(418) 722-7655


2406, Ch. des Quatres-Bourgeois,
Bureau 100
Québec, QC, G1V 1W5
(418) 647-1700

Proulx Savard Architectes:
75, boul. Arthur-Buies Ouest

ARCHITECTURE

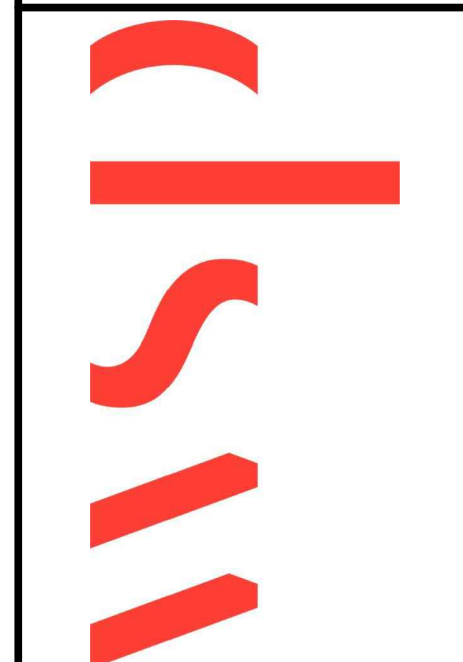


CONSULTANTS

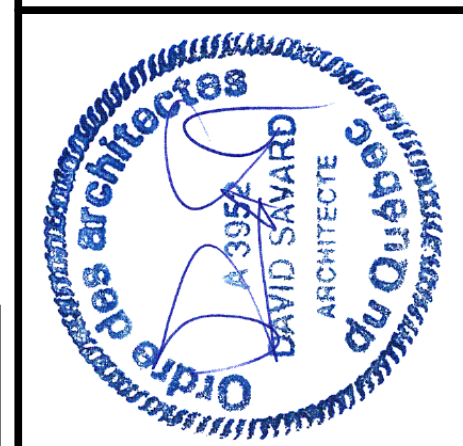

DESSINATEUR (S)	DOSSIER No.
D.B., A.C.	D-2-108 / R457-24
ECHELLE	DATE
INDOULÉE	SEPTEMBRE 2026
05	2024-09-04
04	2024-08-21
03	2024-08-03
02	2024-05-14
01	2024-02-27
	DEFINITIFS POUR SOUMISSION
	DEFINITIFS 100% POUR APPROBATION
	DEFINITIFS 80% POUR APPROBATION
	DEFINITIFS 40% POUR APPROBATION
	PRELIMINAIRES 30% POUR APPROBATION
	REVISIONS

PROJET	PLAN DU NIVEAU 200 DEMOLITION
PROJET	HÔPITAL DE CHANDLER, Chandler (Réfection de l'enveloppe)
PROPRIÉTAIRE	 Santé Québec

053

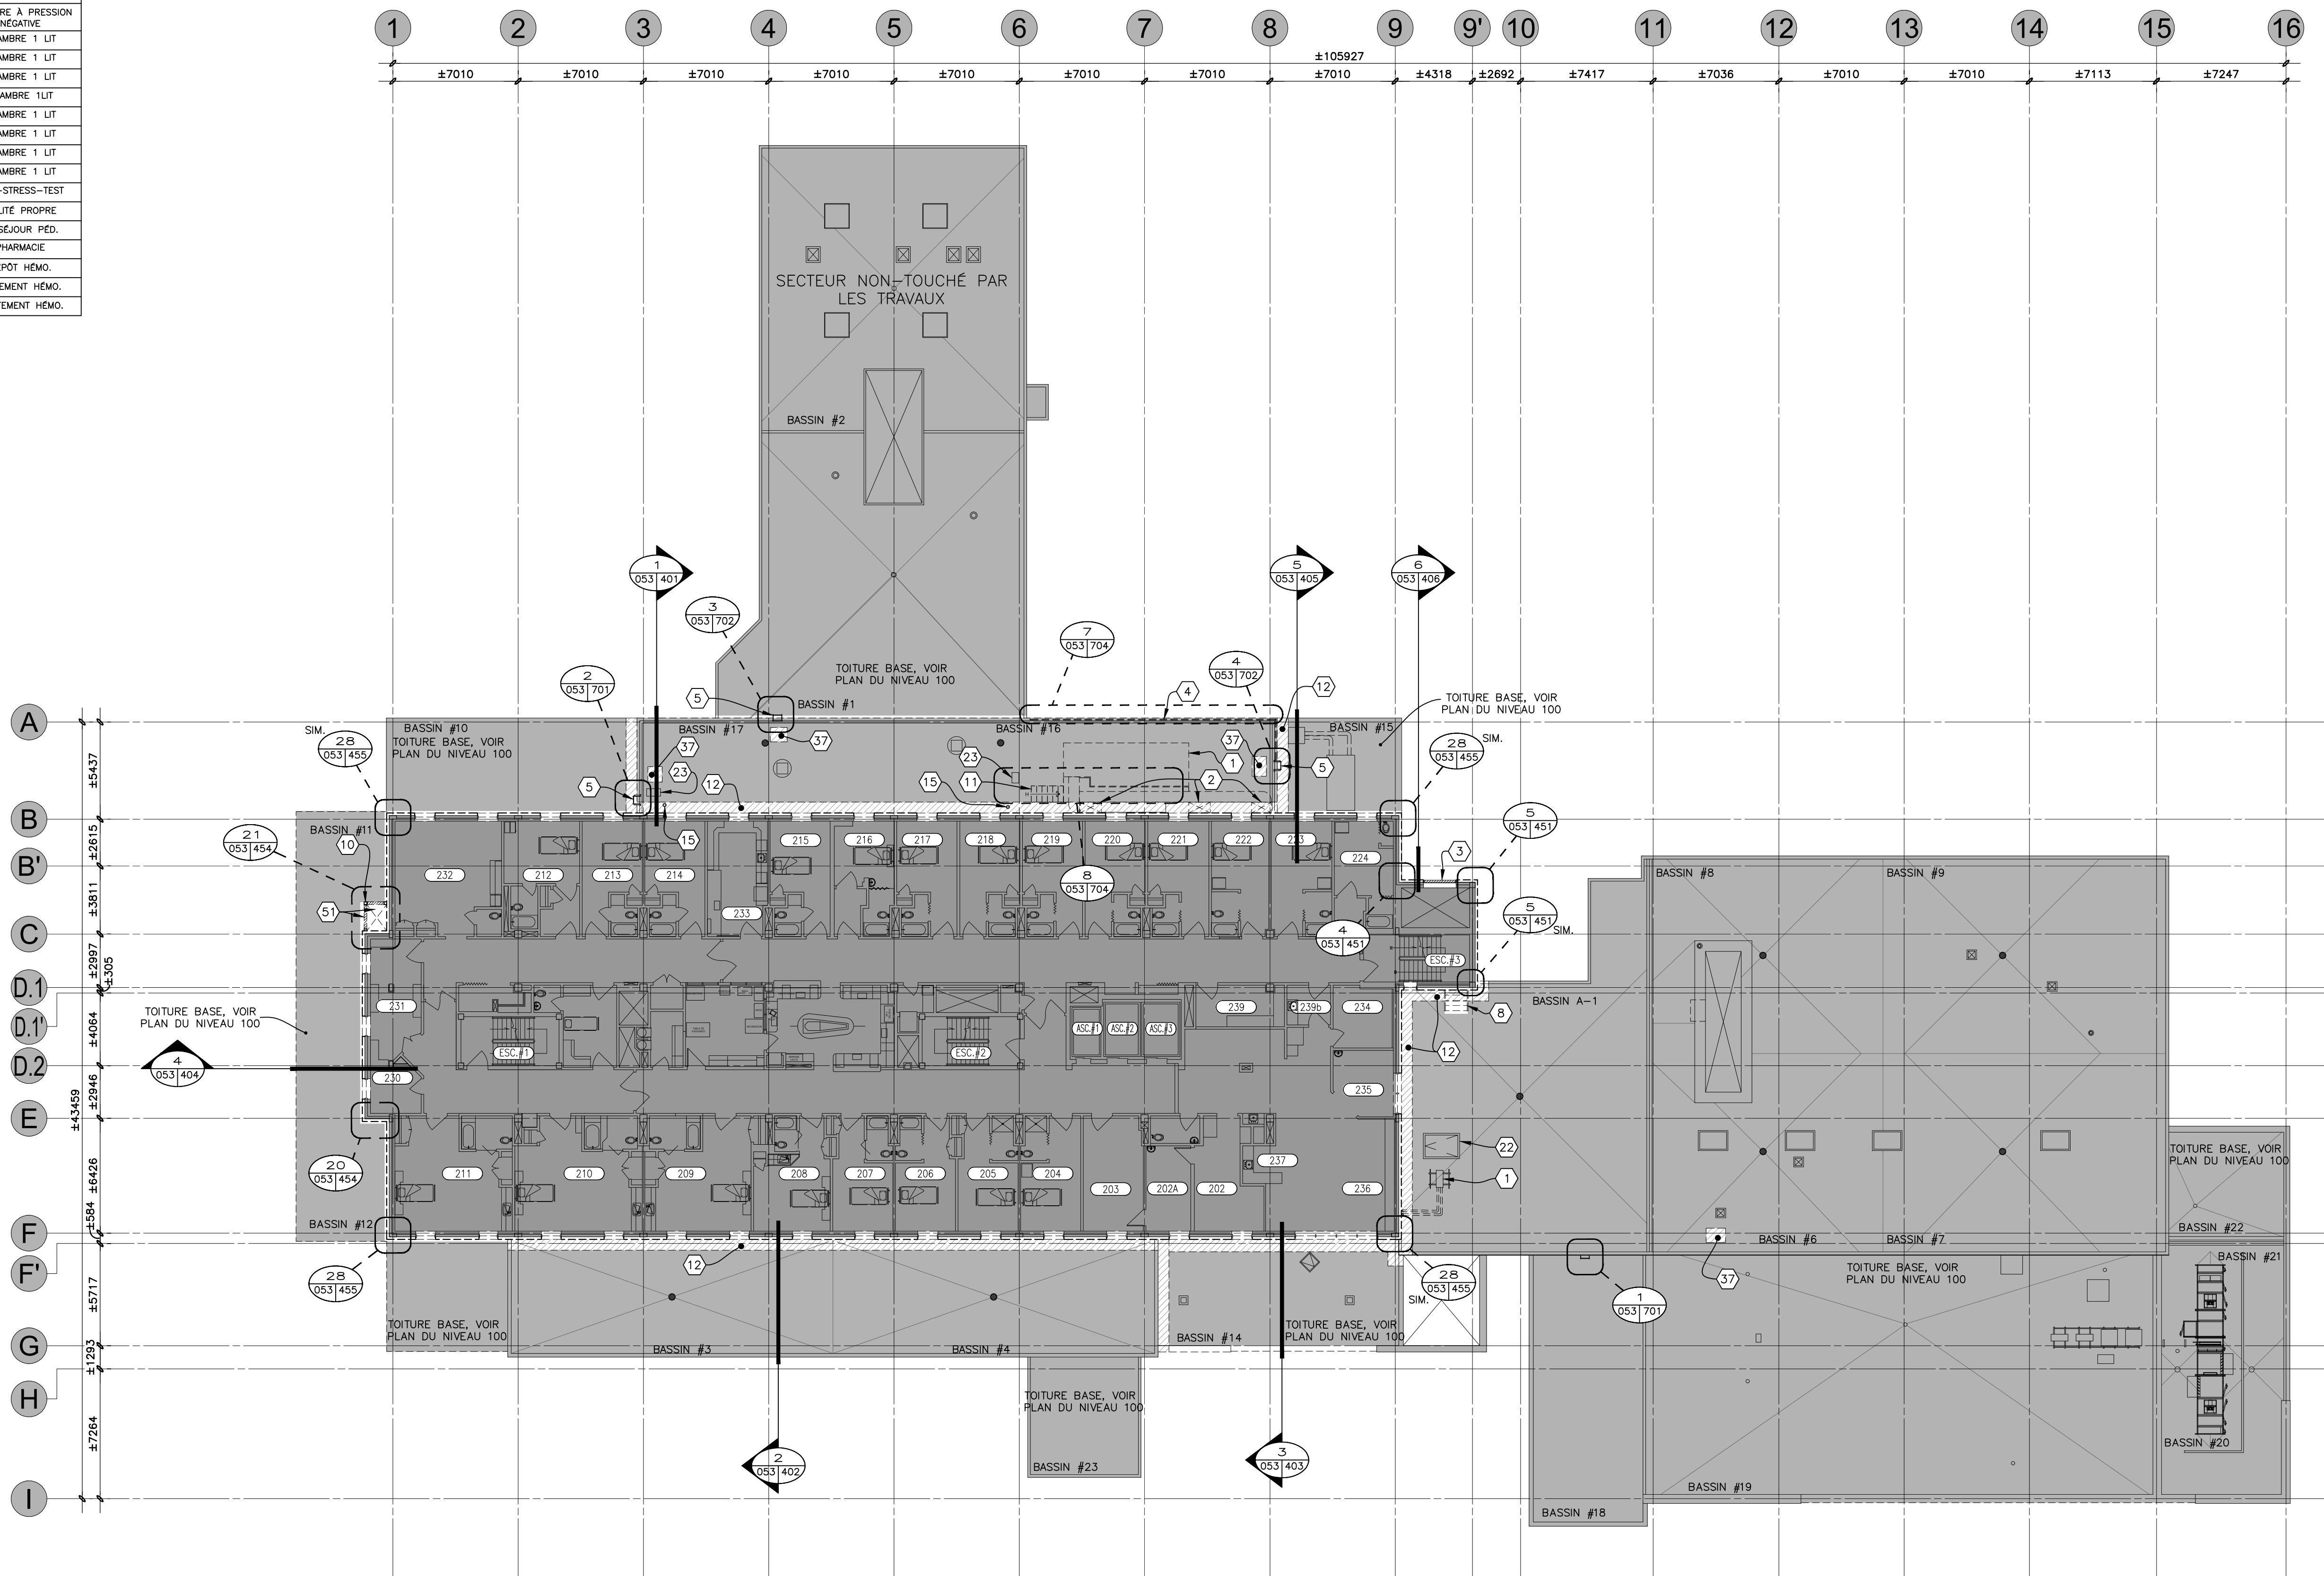

PLAN DU NIVEAU 200 - DÉMOLITION

—LÉGENDE

- | | |
|---|---|
|  | NOTE DESCRIPTIVE. |
|  | AXE EXISTANT. |
|  | NOUVEL AXE. |
|  | NUMÉRO DE LOCAUX. |
|  | EXISTANT À CONSERVER. |
|  | MUR OU CLOISON À DÉMOLIR. |
|  | TRAVAUX DE DÉMOLITION SUR LE MUR EXISTANT, VOIR LES COMPOSITIONS, COUPES DE MUR TYPES ET DÉTAILS TYPES POUR LES COMPOSANTES À DÉMOLIR. |
|  | COUPE DE MUR. |
|  | DÉTAIL TYPE. |
|  | PORTE EXISTANTE À CONSERVER. |
|  | PORTE EXISTANTE À DÉMOLIR. |
|  | FENÊTRE EXISTANTE OU MUR-RIDEAU À CONSERVER. |
|  | FENÊTRE EXISTANTE OU MUR-RIDEAU À DÉMOLIR, VOIR LES COUPES DE MURS ET DÉTAILS TYPES DE FENÊTRE POUR LA SÉQUENCE DE TRAVAU. |
|  | ZONE DE DÉMOLITION DE TOITURE. |
|  | NOUVEAU MUR OU NOUVELLE CLOISON À CONSTRUIRE. |
|  | NOUVELLES COMPOSANTES DE MUR À CONSTRUIRE, DÉTAILS TYPES. |
|  | NOUVELLE PORTE. |
|  | NOUVELLE FENÊTRE OU NOUVEAU MUR-RIDEAU, VOIR COUPES DEMUR, DÉTAILS TYPES ET ÉLÉVATIONS TYPE DE FENÊTRES. |
|  | ZONE DE RECONSTRUCTION DE TOITURE. |
|  | NOUVELLE TOILE SOLAIRE |
|  | NOUVELLE TOILE SOLAIRE |
|  | LIMITÉ DES TRAVAUX D'ENVELOPPE, VOIR NOTES SPÉCIFIQUES. LA NOTE SPÉCIFIQUE EST APPLICABLE À PARTIR DE CETTE LIMITE JUSQU'À LA PROCHAINE LIMITE SUR LE PÉRIMÈTRE DE L'ÉTAGE. |
| <u>TYPE DE VENTILATEUR D'ENTRETOIT</u> | |
| TYPE A: CABANON DE VENTILATION 813x813 | |
| TYPE B: CABANON DE VENTILATION 660x660 | |
| TYPE C: VENTILATEUR 450x450 | |
| TYPE D: VENTILATEUR EXISTANT | |

NE DOIT PAS SERVIR À L'EXÉCUTION

Le présent document est émis pour la seule fin identifiée. Son contenu est protégé par les droits d'auteur et toute reproduction ou modification, partielle ou totale, est interdite sans l'autorisation écrite de gagnon, letellier, cyr, ricard, mathieu, proulx, savard consortium d'architectes.